जयपुर विकास प्राधिकरण, जयपुर।

ज.वि.प्रा./स.स./बी.पी.सी.(बीपी)/2015/डी–1270 दिनांकः– 26/5/2015

श्री कपिल राय सिंघानी,
अधिकृत हस्ताक्षरकर्ता,
महिमा रियल एस्टेट प्रा.लि.,
एफ–1, गोविन्द मार्ग, राजापार्क,
जयपुर।

विषय :– खसरा नम्बर 4760/3345, 4777/3346, 4776/3345 एवं 4775/3345, ग्रुप हाउसिंग, ग्राम–खो नागोरियान, तहसील–सांगानेर, जयपुर के प्रस्तावित अपार्टमेन्ट के भवन मानचित्र अनुमोदन बाबत्।

महोदय,

आपका प्रार्थना पत्र दिनांक 25.06.2014 के संदर्भ में जो प्रस्ताव खसरा नम्बर 4760/3345, 4777/3346, 4776/3345 एवं 4775/3345, ग्रुप हाउसिंग, ग्राम–खो नागोरियान, तहसील–सांगानेर, जयपुर में स्थित भूखण्ड (9503.00 वर्गमीटर क्षेत्रफल) पर 40 मीटर ऊँचाई के (बेसमेन्ट + स्टिल्ट + 12 तल) के आवासीय अपार्टमेन्ट के भवन मानचित्र अनुमोदन के लिए प्रस्तुत किये गये थे उनकी स्वीकृति भवन मानचित्र समिति (बी.पी.) में दिनांक 12.09.2014 को निम्न शर्तों के साथ दी गयी है:–

1. यह भवन अनुज्ञा माह (भारतीय विमानपत्तन प्राधिकरण की अनापत्ति क्रमांक AAI//RHQ/NR/ATM/NOC/2014/346/7852-55 दिनांक 11.09.2014 के अनुसार) दिनांक 10.09.2019 तक प्रभावी है।
2. भवन निर्माण स्वीकृत मानचित्र के अनुसार ही किया जावेगा तथा किसी भी प्रकार का उल्लंघन (डेवियेशन) नहीं किया जायेगा।
3. भूखण्ड के स्वामी एवं मानचित्र तैयार करने वाले तकनीकीविज्ञ का कर्तव्य होगा कि वो यह सुनिश्चित कर ले कि स्वीकृति मानचित्र प्रचलित मास्टर प्लान/जोनल प्लान/भवन विनियमों के अनुरूप है। यदि कोई उल्लंघन प्राधिकरण की जानकारी में आया तो प्राधिकरण को भवन मानचित्रों की दी गयी अनुज्ञा रद्द करने का अधिकार होगा तथा प्राधिकरण से प्रार्थी को किसी भी प्रकार की क्षतिपूर्ति का हक नहीं होगा।
4. निर्माण कार्य प्रारम्भ करने से पूर्व स्वामी प्राधिकरण को निर्धारित प्रपत्र में सूचना प्रस्तुत करेगा।
5. भवन निर्माणकर्ता द्वारा प्लिन्थ लेवल तक का निर्माण पूर्ण होने की सूचना निर्धारित प्रपत्र में आवश्यक रूप से संबंधित उपायुक्त जोन को दी जानी होगी, यदि इसकी अनुपालना भवन निर्माता द्वारा नहीं की जाती है तो जारी अनुज्ञा को वापस ले लिया जावेगा।
6. उक्त स्वीकृति के कारण यदि जयपुर विकास प्राधिकरण को किसी न्यायालय, सक्षम अधिकारी तथा नगर भूमि (अधिकतम सीमा एवं विनियम) अधिनियम के तहत नियुक्त अधिकारी के समक्ष किसी कार्यवाही में कोई भी खर्च, नुकसान, मुआवजा देना पडे या देने योग्य हो तो प्रार्थी उनकी इस क्षति को पूर्ण करने के लिए बाध्य होगा।
7. दरवाजे एवं खिडकियाँ इस प्रकार लगाए जायेगें कि वो सडक की ओर निकले हुए नहीं हों।
8. स्वामी प्रत्येक मंजिल के लिए स्वीकृत आवासीय ईकाई से अधिक का निर्माण नहीं करेगा।
9. ऊपर वर्णित शर्तों एवं अन्य कोई संबंधित शर्त का पालन नहीं होने पर भवन अनुज्ञा रद्द मानी जायेगी।
10. स्वामी भवन के परिसर को स्वीकृत उपयोग के अनुसार ही उपयोग में लेगा।
11. तकनीकीविज्ञ के निरीक्षण में स्वामी निर्माण कार्य करवायेगा जिसके संबंध में सूचना प्राधिकरण को पूर्व में देनी होगी। यदि तकनीकीविज्ञ को बदला जाता है तो इसकी सूचना 48 घन्टे के अन्दर यथोचित प्रमाण–पत्र में प्राधिकरण को देनी होगी।
12. स्वीकृत मानचित्र को प्राप्ति दिनांक से राज्य स्तर के समाचार–पत्र में एक सप्ताह में प्रकाशित करने होगें तथा इसकी सूचना संबंधित उपायुक्त जोन को देगा।
13. आवेदक द्वारा पार्किंग क्षेत्र की पालना भवन विनियम 2011 के विनियम 10.1.8 के अनुसार सुनिश्चित की जानी होगी।

14. भवन परिसर में ही आगुन्तकों की पार्किंग करवाई जावे तथा आगन्तुकों हेतु निःशुल्क वाहन पार्किंग का बोर्ड लगवाया जावें।

15. भवन विनियम की धारा 16.5 की अनुपालना में भवन में भूकम्परोधी प्रावधान रखा जाना सुनिश्चित किया जावे।

16. अग्निशमन दृष्टि से सक्षम अधिकारी द्वारा दिये गये अनापत्ति प्रमाण पत्र की शर्तों की पालना सुनिश्चित की जानी आवश्यक होगी तथा भवन की आवश्यकतानुसार अग्निशमन यंत्र (Fire Extinguisher) रखें जावें तथा इनको संचालित करने के लिये प्रशिक्षित व्यक्ति ऐसे भवन में हर समय उपलब्ध रहें।

17. निर्माण स्थल पर स्वीकृति का विवरण अर्थात अनुमोदित मानचित्र, उपलब्ध पार्किंग की सूचना एवं भवन में सुरक्षा एवं निकास प्लान (Escape Plan) का नक्शा भी प्रदर्शित (Display) उपयुक्त स्थान पर प्रदर्शित किया जावें।

18. अधिवास प्रमाण पत्र भवन निर्मित होने के उपरान्त आवश्यक रूप से लिया जाना होगा।

19. भवन का उपयोग प्रांरभ होने पर एक केयर टेकर की नियुक्ति की जावें जिसके पास भवन का मानचित्र, सुरक्षा एवं निकास प्लान (Escape Plan) उपलब्ध रहें। इस प्रकार नियुक्त केयर टेकर के मोबाईल नंबर एवं Land Line Number भी लिये जाकर पुलिस आयुक्त जयपुर महानगर व अधोहस्ताक्षरकर्ता को सूचना उपलब्ध करवाई जावें ताकि किसी भी दुर्घटना की स्थिति में बचाव कार्य प्रभावी रूप से किये जा सकें।

20. भवन विनियम 2010 की धारा 17.3 की अनुपालना में "गलत तथ्यों पर प्राप्त की गई अथवा तथ्यों को छुपाकर प्राप्त की गई स्वीकृति स्वत निरस्त मानी जायेगी एवं ऐसी निर्माण स्वीकृति प्राप्त करने के लिए आवेदनकर्ता को दोषी माना जायेगा।"

21. राज्य सरकार के आदेश दिनांक 02.05.2012 के बिन्दु संख्या 1.5 अनुसार EWS/LIG की स्वीकृति जारी होने के तीन माह की अवधि में निर्माण कार्य प्रारम्भ करना आवश्यक होगा तथा इन EWS/LIG इकाईयों के निर्माण कार्य के लिए 2 वर्ष की अधिकतम सीमा होगी।

22. उक्त आदेश के बिन्दु संख्या 1.6 के अनुसार यदि अधिकतम 3 माह के अन्दर EWS/LIG इकाईयों के निर्माण कार्य प्रारम्भ नहीं किया जाता है तो निम्नानुसार शास्ति देय होगीः–

प्रथम माह –	25/रूपये– Per sq. ft (EWS/LIG के क्षेत्रफल पर)
द्वितीय माह–	50/रूपये– Per sq. ft (EWS/LIG के क्षेत्रफल पर)
तृतीय माह–	100/रूपये– Per sq. ft (EWS/LIG के क्षेत्रफल पर)

यदि छः माह में भी EWS/LIG इकाईयों का निर्माण प्रारम्भ नहीं किया जाता है तो मुख्य भवन के निर्माण कार्य को रूकवा दिया जावेगा तथा उसे अनाधिकृत निर्माण की श्रेणी में मानते हुए ध्वस्त भी किया जा सकेगा।"

23. पर्यावरण प्रदूषण विभाग द्वारा जारी अनापत्ति प्रमाण पत्र की अनुपालना आप द्वारा सुनिश्चित की जानी होगी।

भवदीय

25/5/15

(मुकेश मित्तल)
वरिष्ठ नगर नियोजक एवं
सदस्य सचिव
भवन मानचित्र समिति (बी.पी.)
जयपुर विकास प्राधिकरण, जयपुर।

प्रतिलिपिः– सूचनार्थ एवं आवश्यक कार्यवाही हेतु।

1. मुख्य नियन्त्रक (प्रवर्तन), जयपुर विकास प्राधिकरण, जयपुर।
2. उपायुक्त, जोन–10ए, जयपुर विकास प्राधिकरण, जयपुर।
3. उप नगर नियोजक/सहायक नगर नियोजक जोन–10ए, जविप्रा को सूचनार्थ भेजकर लेख है कि कृपया अनुमोदित भवन मानचित्र की प्रति उपायुक्त जोन से प्राप्त करें।
4. अधिशाषी अभियन्ता, बीपीसी–द्वितीय, जविप्रा, जयपुर को साईट निरीक्षण पत्रावली हेतु।
5. अध्यक्ष एवं प्रबन्ध निदेशक, राजस्थान राज्य विद्युत वितरण निगम लि0 विद्युत भवन जनपथ, जयपुर।
6. मुख्य अभियन्ता, मुख्यालय जन स्वाथ्य अभियांत्रिकी विभाग हसनपुरा रोड, रेल्वे हॉस्पीटल के पास, जयपुर।

(मुकेश मित्तल)
वरिष्ठ नगर नियोजक एवं
सदस्य सचिव
भवन मानचित्र समिति (बी.पी.)
जयपुर विकास प्राधिकरण, जयपुर।

E:\New Folder\bpc-2\bpc\Section letter\19 Point Section Letter-2.doc

जयपुर विकास प्राधिकरण
समस्त बहुमंजिली इमारतों एवं विवाह [illegible] [illegible] [illegible] प्रकार्य एवं साथ ही अग्निशमन केन्द्र [illegible] [illegible] [illegible] अनापत्ति प्रमाण पत्र [illegible] आवश्यक है।
100 वर्ग मीटर से बड़े व्यावसायिक/संस्थानिक भूखण्डों में मौके पर भवन निर्माणकर्ता द्वारा [illegible] स्वीकृत मानचित्र [illegible] [illegible] [illegible] [illegible] स्वीकृत मानचित्र प्राप्त होने की तिथि से एक वर्ष में [illegible] अनिवार्य होगा।

[illegible] मानचित्र का अनुमोदन किसी भी प्रकार [illegible] भूमि/भूखण्ड के प्रति स्वामित्व [illegible] [illegible] [illegible] [illegible] (STRUCTURE) का दायित्व [illegible] का होगा"।

जयपुर विकास प्राधिकरण (जयपुर [illegible] [illegible] अधिनियम 2000 की धारा 17 [illegible] [illegible] [illegible]

जयपुर विकास प्राधिकरण (जयपुर [illegible] अधिनियम [illegible] की धारा 8.15 के [illegible] [illegible] [illegible] की जावेगी।

Applicant should get the construction checked at plinth level before proceeding for further construction.

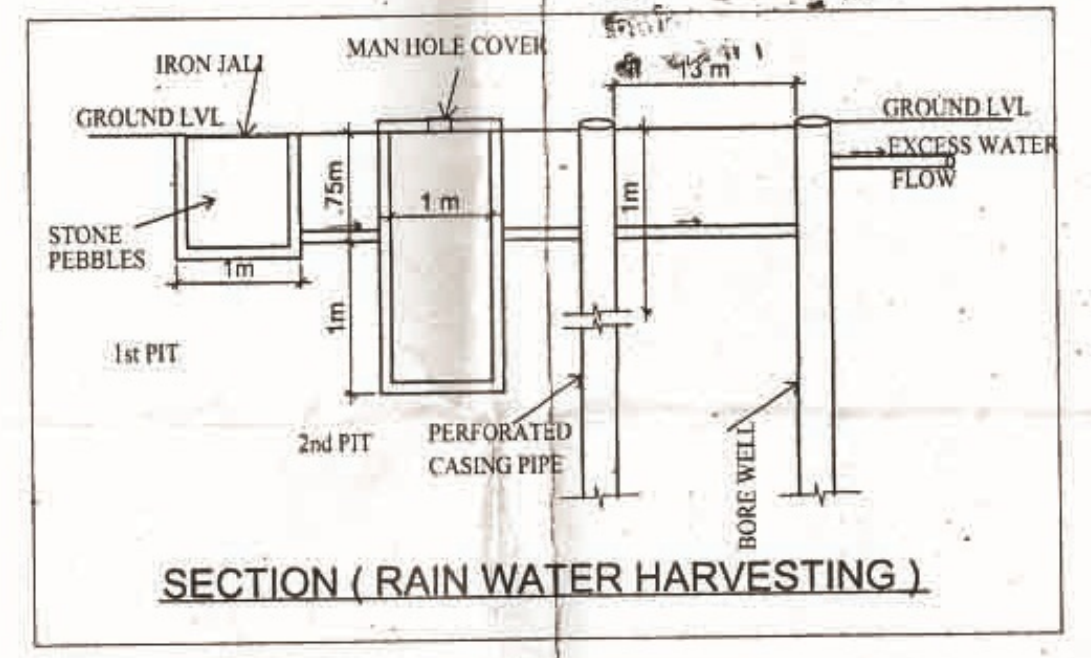
IRON JALI
MAN HOLE COVER
GROUND LVL
GROUND LVL
EXCESS WATER FLOW
STONE PEBBLES
.75m
1 m
1m
1m
1m
.13m
1st PIT
2nd PIT
PERFORATED CASING PIPE
BORE WELL

SECTION (RAIN WATER HARVESTING)

AREA STATEMENT

S. NO.	FLOOR NAME	B.U.A. SQ.MT.	F.A.R.	GROSS B.U.A.	service area	Balcony area	CORRIDOR
1.	STILT FLOOR	2191.96	21.42	2224.13	187.11		71.73
2.	FIRST FLOOR	1973.91	1599.98	2037.81	22.65	112.07	148.20
3.	SECOND FLOOR	1973.91	1599.98	2037.81	22.65	112.07	148.20
4.	THIRD FLOOR	1973.91	1599.98	2037.81	22.65	112.07	148.20
5.	FOURTH FLOOR	1973.91	1599.98	2037.81	22.65	112.07	148.20
6.	FIFTH FLOOR	1973.91	1599.98	2037.81	22.65	112.07	148.20
7.	SIXTH FLOOR	1973.91	1599.98	2037.81	22.65	112.07	148.20
8.	SEVENTH FLOOR	1973.91	1599.98	2037.81	22.65	112.07	148.20
9.	EIGHTH FLOOR	1973.91	1599.98	2037.81	22.65	112.07	148.20
10.	NINTH FLOOR	1973.91	1599.98	2037.81	22.65	112.07	148.20
11.	10 TH FLOOR	1973.91	1599.98	2037.81	22.65	112.07	148.20
12.	11 TH FLOOR	1973.91	1599.98	2037.81	22.65	112.07	148.20
13.	12 TH FLOOR	1973.91	1599.98	2037.81	22.65	112.07	148.20
14.	TERRACE FLOOR	240.00	NIL	240.00			
8.	TOTAL	26118.88	19221.18	26917.85	458.91	1344.84	1850.13

1. PLOT AREA = 9503.00 SQ.MT.
2. PERMISSIBLE F.A.R. = 2.25
=PLOT AREA X2.25 = 9503.00 X 2.25 = 21381.75 SQ.MT.
2. ACHIEVED F.A.R. AREA
= 19221.18 (+2160.57) SQ.MT.
PENDING
3. PERMISSIBLE FREE F.A.R. AREA
(A). STORE AREA 3% OF ACHIEVED F.A.R. = 576.63 SQ.MT.
(B). CLUB AREA 5% OF ACHIEVED FAR AREA = 961.05SQ.MT.
(C). SERVICES AREA 7% OF ACHIEVED F.A.R. = 1345.48SQ.MT.
(D).CIRCULATION AREA 15% OF ACHIEVED F.A.R. =2883.17 SQ.MT.
4. ACHIEVED FREE F.A.R. AREA
(A). STORE AREA = 000.00 SQ.MT.
(B). CLUB AREA = 609.72 SQ.MT.
(C). SERVICES AREA = 458.91 SQ.MT.
(D).CORRIDOR CIRCULATION AREA = 1850.13 SQ.MT.
5. MANDATORY GREEN AREA 10% =950.30 SQ.MT.
(A). ACHIEVED GREEN AREA = 963.23 SQ.MT.
6. PERMISSIBLE HEIGHT = 40.00 M.
(A). ACHIEVED HEIGHT = 39.8 M.
7. PERMISSIBLE GROUND COVERAGE = 35%
(A). ACHIEVED GROUND COVERAGE =22.55 % (2231.11 SQ.MT.)

REQUIRED PARKING CALCULATION

1.. REQUIRED E.C.U.=ACHIVED F.A.R. /75=19221.18 / 75
=256.28 E.C.U.=say 257 E.C.U.

2.. 25% VISITORS PARKING EXTRA
=257.32 X 25% =64.33 E.C.U.SAY 64 E.C.U.

3.. TOTAL PARKING REQUIRED = 64+ 257 = 321 E.C.U.

PARKING

PARKING IN	PERMISSIBLE PARKING	REQUIRED PARKING	SURFACE CARS	TWO WHEELERS	TOTAL E.C.U.
STILT FLOOR	51		50	69 (23 e.c.u.)	73 E.C.U.
OPEN GROUND	273		210	117(39 e.c.u.)	249 E.C.U.
TOTAL E.C.U.	324	321	260	186 (62 e.c.u.)	322 E.C.U.

SHEET NO.1

TITLE :- SITE PLAN

भवन मानचित्र समिति (बी.पी.) की ...164....वीं
बैठक दिनांक ...12/9/2014 में लिये गये निर्णय
की अनुपालना में भवन मानचित्र पत्रांक जविप्रा/
स.स./बीपीसी (बीपी)/डी-1270 दिनांक.......
..24/5/2015 द्वारा अनुमोदित कर जारी किये गये।
अनुमोदित

21/5/15
उप नगर नियोजक (बी0 पी0 सी0)
जयपुर विकास प्राधिकरण
जयपुर

सदस्य सचिव (बी0 पी0 सी0)
जयपुर विकास प्राधिकरण
जयपुर

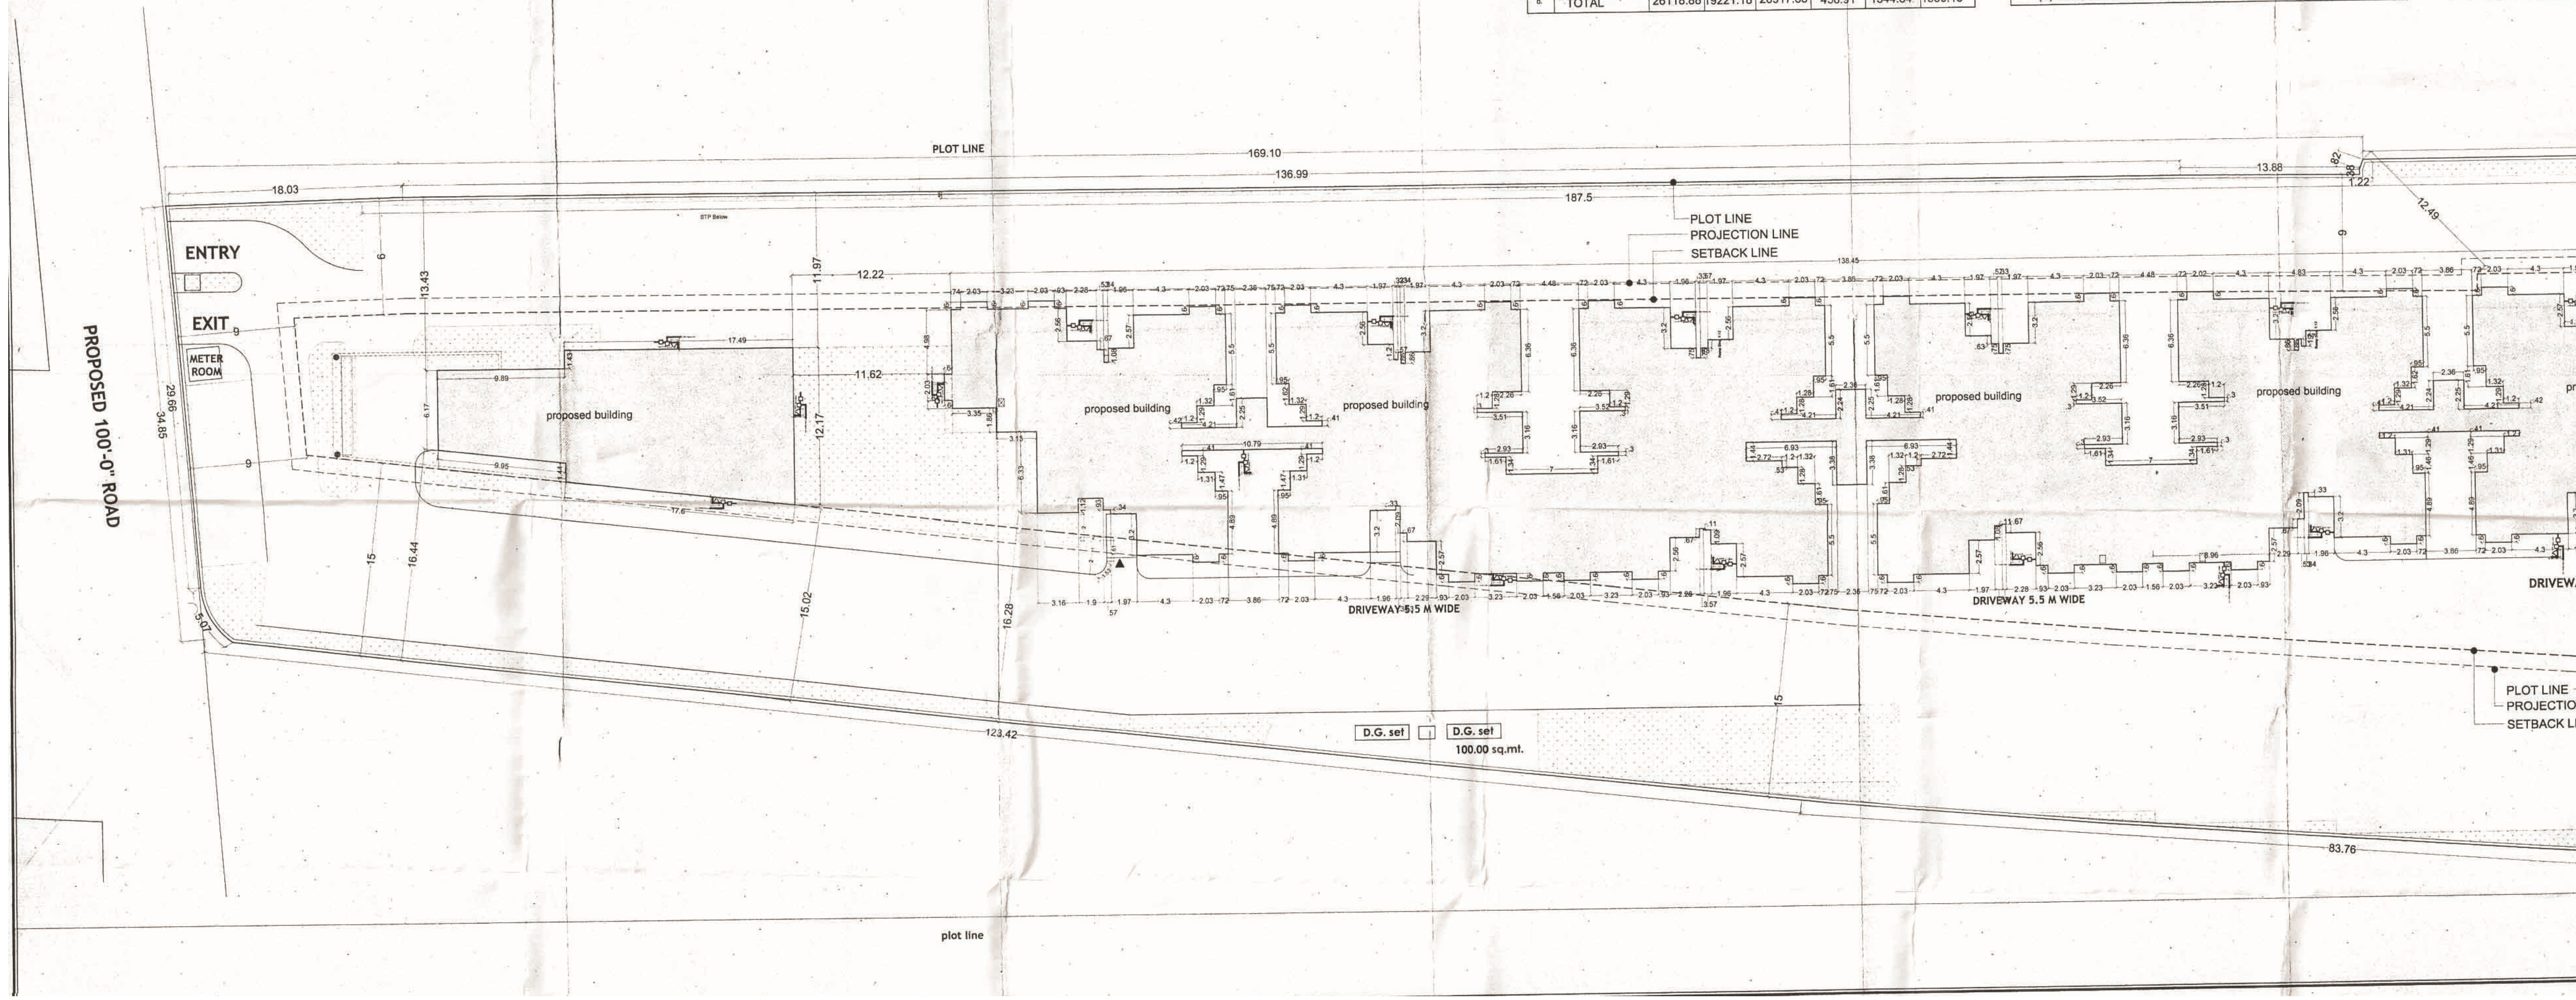
PLOT LINE
169.10
136.99
187.5
13.88
38.48
18.03
1.22
12.49
PLOT LINE
PROJECTION LINE
SETBACK LINE
138.45
STP Below
UG WATER TANK Below
ENTRY
EXIT
METER ROOM
PROPOSED 100'-0" ROAD
29.66
34.85
5.07
13.43
11.97
12.22
17.49
11.62
12.17
9.89
9.95
6.17
17.6
15
16.44
15.02
16.28
proposed building
proposed building
proposed building
proposed building
proposed building
proposed building
DRIVEWAY 5.5 M WIDE
DRIVEWAY 5.5 M WIDE
DRIVEWAY 5.5 M WIDE
DRIVEWAY 3.6 M WIDE
D.G. set
D.G. set
100.00 sq.mt.
123.42
83.76
55.81
PLOT LINE
PROJECTION LINE
SETBACK LINE
plot line

TITLE:- SUBMISSION DRAWINGS
SITE PLAN

SCALE:- 1= 200
DATE : 10-06-2014
NORTH

PROJECT:- MAHIMA BELLEVUE
PROPOSED APARTMENTS
AT KHASARA NO.- 4760/3345,4776/3346,
4775/3345,4777/3346
REVENUE VILLAGE,KHO-NAGORIYAN,
TEH. SANGANER
JAIPUR (RAJ.)

ARCHITECTS:-
m|a| architects pvt. ltd.
Jaipur - Bangalore - Hyderabad
Plot No. -1, greenwood, Lal Kothi Scheme
Sahkar Marg Jaipur-302001
Tel : 91-141- 4299999
email- studio@maarchitects.in web- www.maarchitects.in

OWNER

For MAHIMA REAL ESTATE PVT LTD
Auth. Signatory

ARCHITECTS

Ar. Puneet Dua
B. Arch
CA/2005/355

जयपुर विकास प्राधिकरण [illegible]

इस मानचित्र का अनुमोदन किसी भी व्यक्ति [illegible] (STRUCTURE) का दायित्व [illegible] का होगा"।

[illegible] धारा 8 15 [illegible]

Applicant should get the construction checked at plinth level before proceeding for further construction.

SHEET NO.2

TITLE :- STILT FLOOR PLAN

भवन मानचित्र समिति (बी.पी.) की ...164... बैठक दिनांक 12/9/2014 में लिये गये निर्णय की अनुपालना में भवन मानचित्र पत्रांक [illegible] स.स./बीपीसी (बीपी)/डी-12.70. दिनांक....... 26/5/2015 द्वारा अनुमोदित कर जारी किये गये।

अनुमोदित

2/5/15
उप नगर नियोजक (बी0 पी0 सी0)
जयपुर विकास प्राधिकरण
जयपुर

सदस्य सचिव (बी0 पी0 सी0)
जयपुर विकास प्राधिकरण
जयपुर

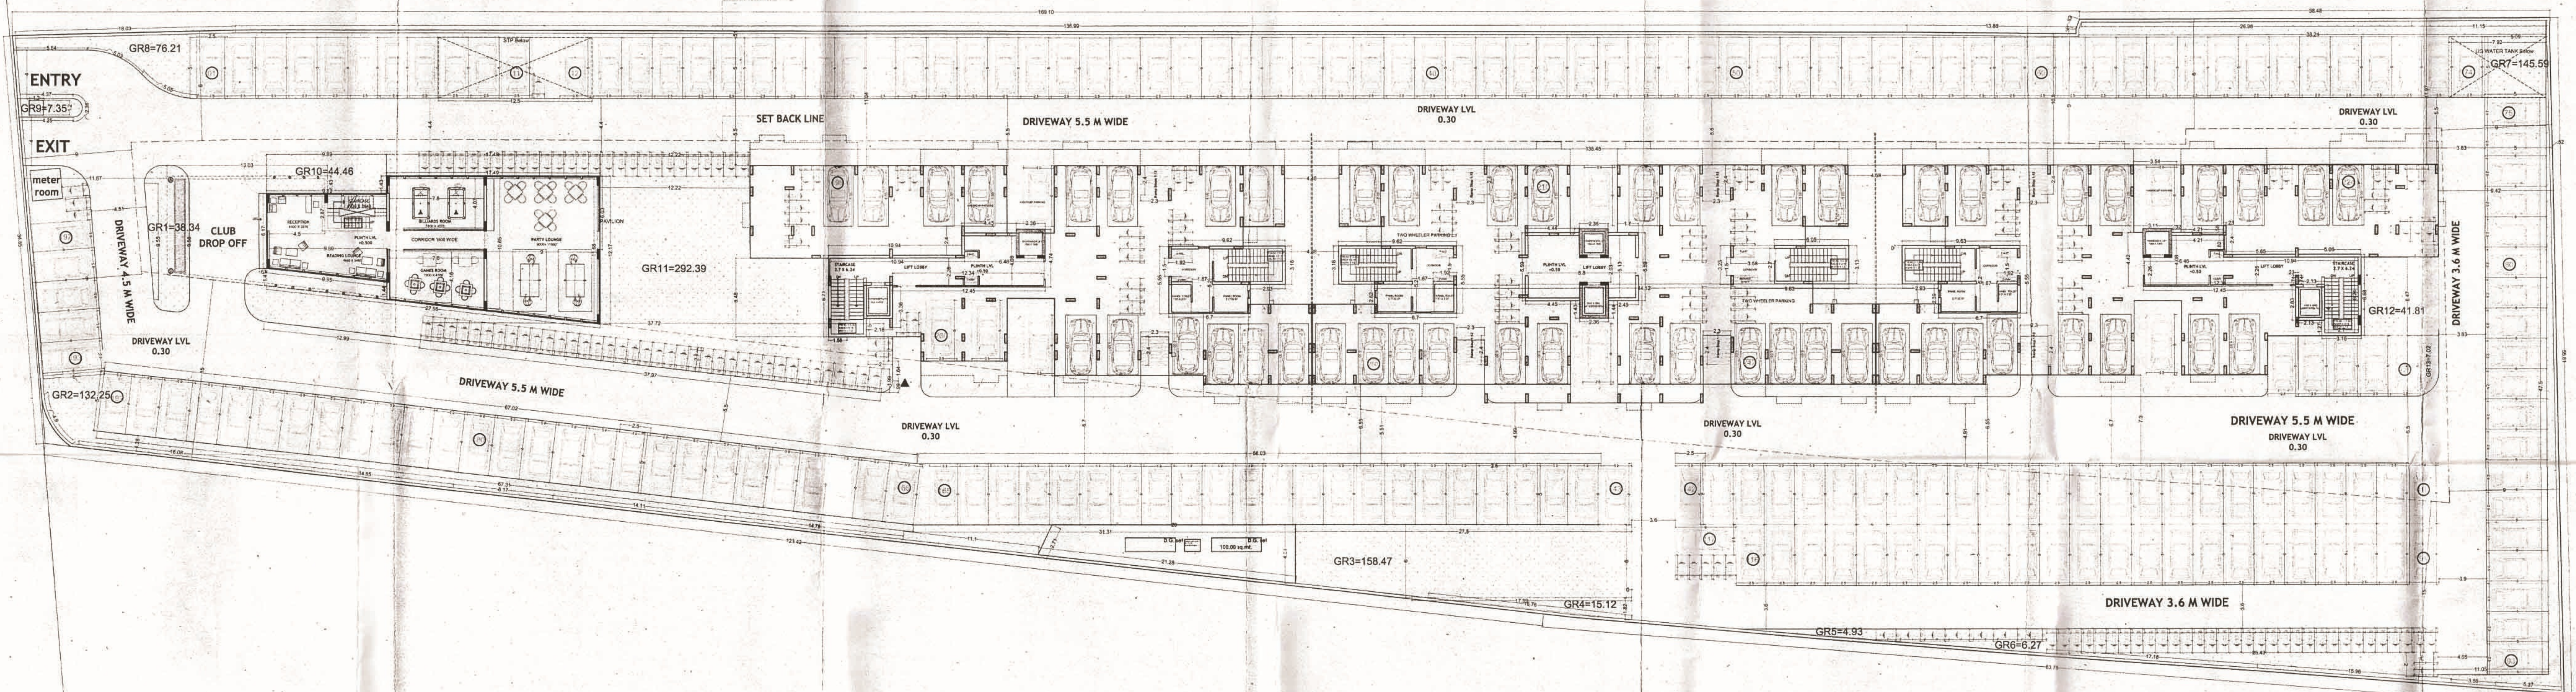

PLOT LINE
GR8=76.21
STP Below
ENTRY
GR9=7.35
EXIT
meter room
GR10=44.46
GR1=38.34
CLUB DROP OFF
DRIVEWAY 4.5 M WIDE
RECEPTION
BILLIARDS ROOM
PARTY LOUNGE
PAVILION
CORRIDOR 1500 WIDE
READING LOUNGE
GAMES ROOM
PLINTH LVL +0.500
GR11=292.39
SET BACK LINE
DRIVEWAY 5.5 M WIDE
DRIVEWAY LVL 0.30
STAIRCASE
LIFT LOBBY
PLINTH LVL
TWO WHEELER PARKING
PROPOSED 100'-0" ROAD
ROAD LVL 0.00
GR2=132.25
DRIVEWAY LVL 0.30
DRIVEWAY 5.5 M WIDE
D.G. set
D.G. set
100.00 sq.mt.
GR3=158.47
GR4=15.12
GR5=4.93
GR6=6.27
DRIVEWAY LVL 0.30
DRIVEWAY LVL 0.30
DRIVEWAY 5.5 M WIDE
DRIVEWAY LVL 0.30
DRIVEWAY 3.6 M WIDE
UG WATER TANK Below
GR7=145.59
DRIVEWAY LVL 0.30
GR12=41.81
GR13=7.02
DRIVEWAY 3.6 M WIDE

TITLE:- SUBMISSION DRAWINGS
STILT FLOOR PLAN

SCALE:- 1= 200
DATE : 10-06-2014
NORTH : N W E S

PROJECT:- MAHIMA BELLEVUE
PROPOSED APARTMENTS
AT KHASARA NO.- 4760/3345,4776/3346,
4775/3345,4777/3346
REVENUE VILLAGE,KHO-NAGORIYAN,
TEH. SANGANER
JAIPUR (RAJ.)

ARCHITECTS:-
m|a| architects pvt. ltd.
Jaipur - Bangalore - Hyderabad
Plot No. -1, greenwood, Lal Kothi Scheme
Sahkar Marg Jaipur-302001
Tel : 91-141- 4299999
email- studio@maarchitects.in web- www.maarchitects.in

OWNER	ARCHITECTS
For MAHIMA REAL ESTATE PVT LTD Auth. Signatory	Ar. Puneet Dua B. Arch CA/2005/35530

applicant should get his construction checked at plinth level before proceeding for further construction.

"Structural ... जिम्मेदारी ... होगा"।

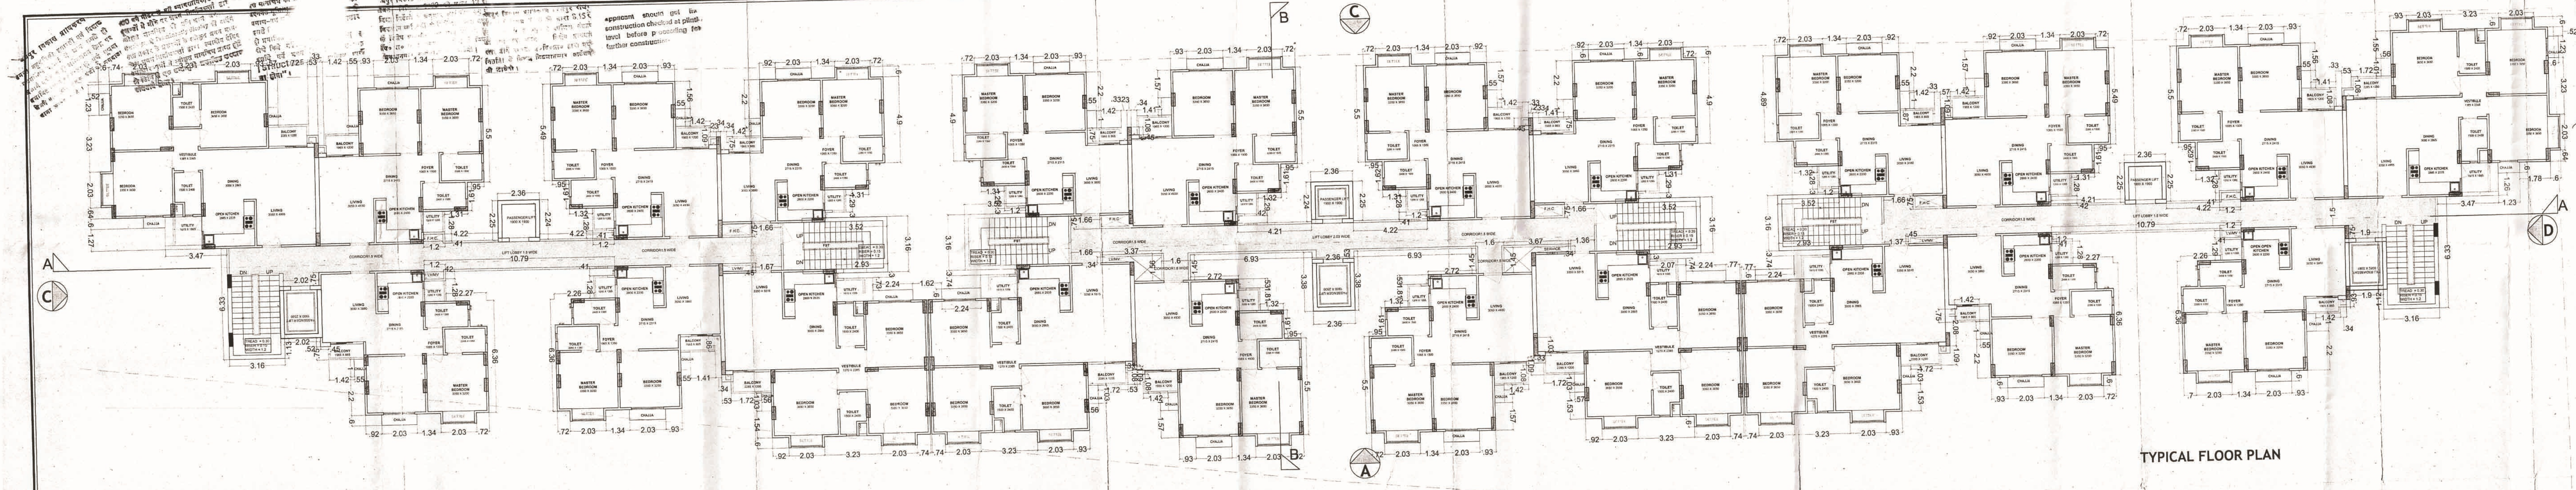

B
C
A
D
BEDROOM
MASTER BEDROOM
TOILET
FOYER
DINING
LIVING
OPEN KITCHEN
UTILITY
BALCONY
CHAJJA
SETTEE
VESTIBULE
F.H.C.
LV/MV
PASSENGER LIFT 1900 X 1900
PASSENGER LIFT 1900 X 2500
LIFT LOBBY 1.5 WIDE
LIFT LOBBY 2.03 WIDE
CORRIDOR1.5 WIDE
CORRIDOR1.6 WIDE
SERVICE
FST
UP
DN
TREAD = 0.30
RISER = 0.15
WIDTH = 1.2
10.79
6.93
3.47
3.16
6.33

TYPICAL FLOOR PLAN

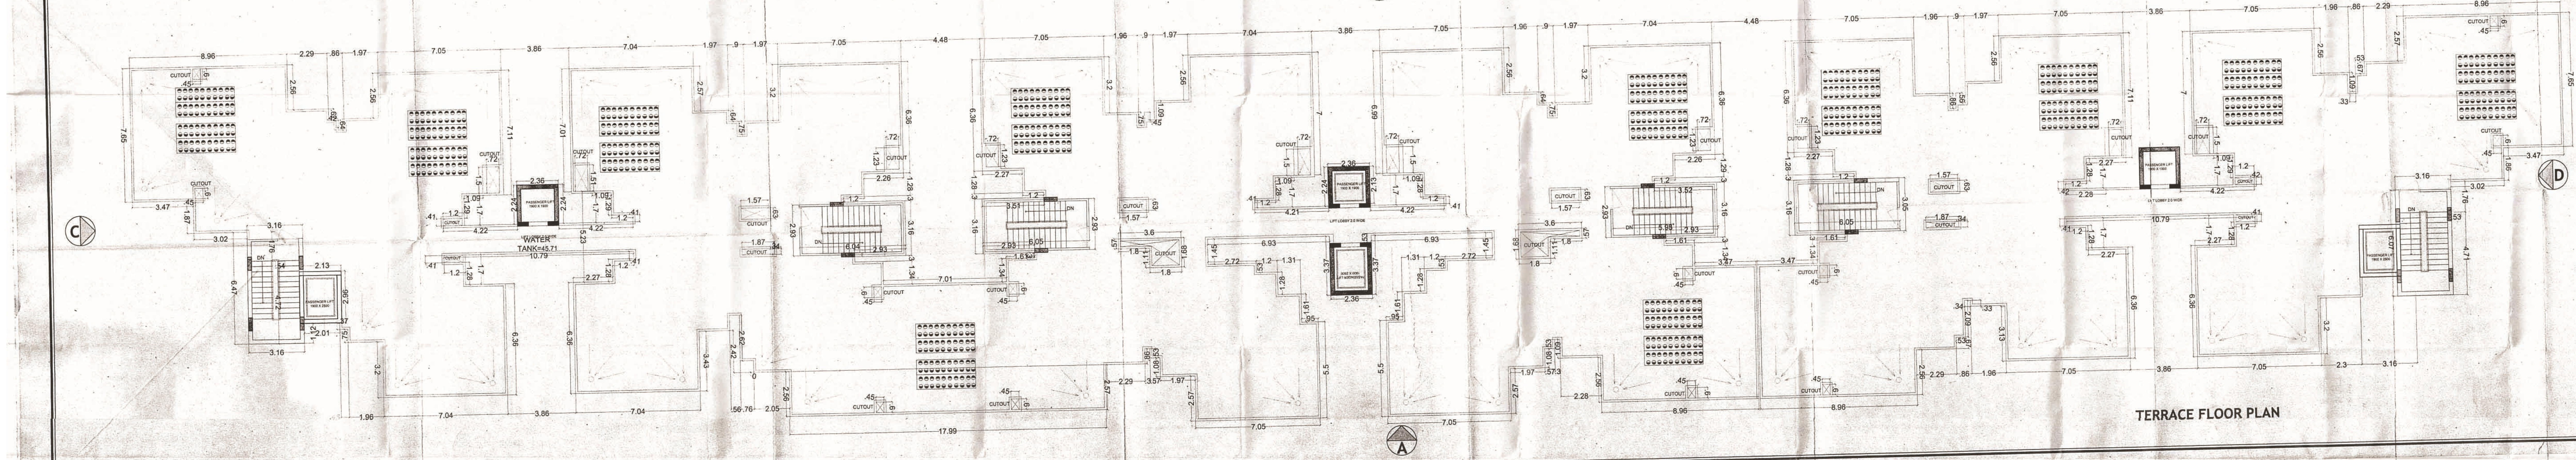

C
A
D
CUTOUT
PASSENGER LIFT 1900 X 1900
PASSENGER LIFT 1900 X 2500
LIFT LOBBY 2.0 WIDE
WATER TANK=45.71
UP
DN
8.96
7.05
7.04
3.86
4.48
17.99
10.79

TERRACE FLOOR PLAN

SHEET NO.3

TITLE :- TYPICAL FLOOR PLAN
TERRACE FLOOR PLAN

भवन मानचित्र समिति (बी.पी.) की 164 वीं
बैठक दिनांक 12/9/14 में लिये गये निर्णय
की अनुपालना में भवन मानचित्र पत्रांक जविप्रा/
स.रा./बीपीसी (बीपी)/डी-1270 दिनांक
26/5/2015 द्वारा अनुमोदित कर जारी किये गये।

अनुमोदित

21/5/15
उप नगर नियोजक (बी0 पी0 सी0)
जयपुर विकास प्राधिकरण
जयपुर

सदस्य सचिव (बी0पी0सी0)
जयपुर विकास प्राधिकरण
जयपुर

TITLE:- SUBMISSION DRAWINGS
TYPICAL FLOOR PLAN
TERRACE FLOOR PLAN

SCALE:- 1= 100

DATE : 10-06-2014

NORTH :
N
W
E
S

PROJECT:- MAHIMA BELLEVUE
PROPOSED APARTMENTS
AT KHASARA NO.- 4760/3345,4776/3346,
4775/3345,4777/3346
REVENUE VILLAGE,KHO-NAGORIYAN,
TEH. SANGANER
JAIPUR (RAJ.)

ARCHITECTS:-

ma architects pvt. ltd.
Jaipur - Bangalore - Hyderabad
Plot No. -1, greenwood, Lal Kothi Scheme
Sahkar Marg Jaipur-302001
Tel : 91-141- 4299999
email- studio@maarchitects.in web- www.maarchitects.in

OWNER	ARCHITECTS
For MAHIMA REAL ESTATE PVT LTD Auth. Signatory	Ar. Puneet Dua B. Arch. CA/2005/35530 Ar. Puneet Dua B. Arch. C

जयपुर विकास प्राधिकरण
[illegible]

100 वर्ग मीटर से बड़े व्यावसायिक/आवासीय भूखण्डों में मौके पर भवन निर्माणकर्ता द्वारा स्वीकृत मानचित्र [illegible] होगा।

इस मानचित्र का अनुमोदन किसी भी भाँति सम्बन्धित भूमि/भूखण्ड के प्रति स्वामित्व का प्रमाण-पत्र नहीं [illegible] इससे किसी के स्वामित्व सम्बन्धी अधिकार ही प्रभावित होंगे।
नीचे किये गये अनुमोदित मानचित्रों की [illegible] भवन निर्माण का संरचना (STRUCTURE) का दायित्व [illegible] का होगा"।

जयपुर विकास प्राधिकरण (जयपुर [illegible]) [illegible] 2000 की धारा 12 [illegible]
[illegible]

जयपुर विकास प्राधिकरण (जयपुर [illegible]) [illegible] की धारा 8.13 [illegible]
[illegible]

Applicant should get the construction checked at plinth level before proceeding further construction.

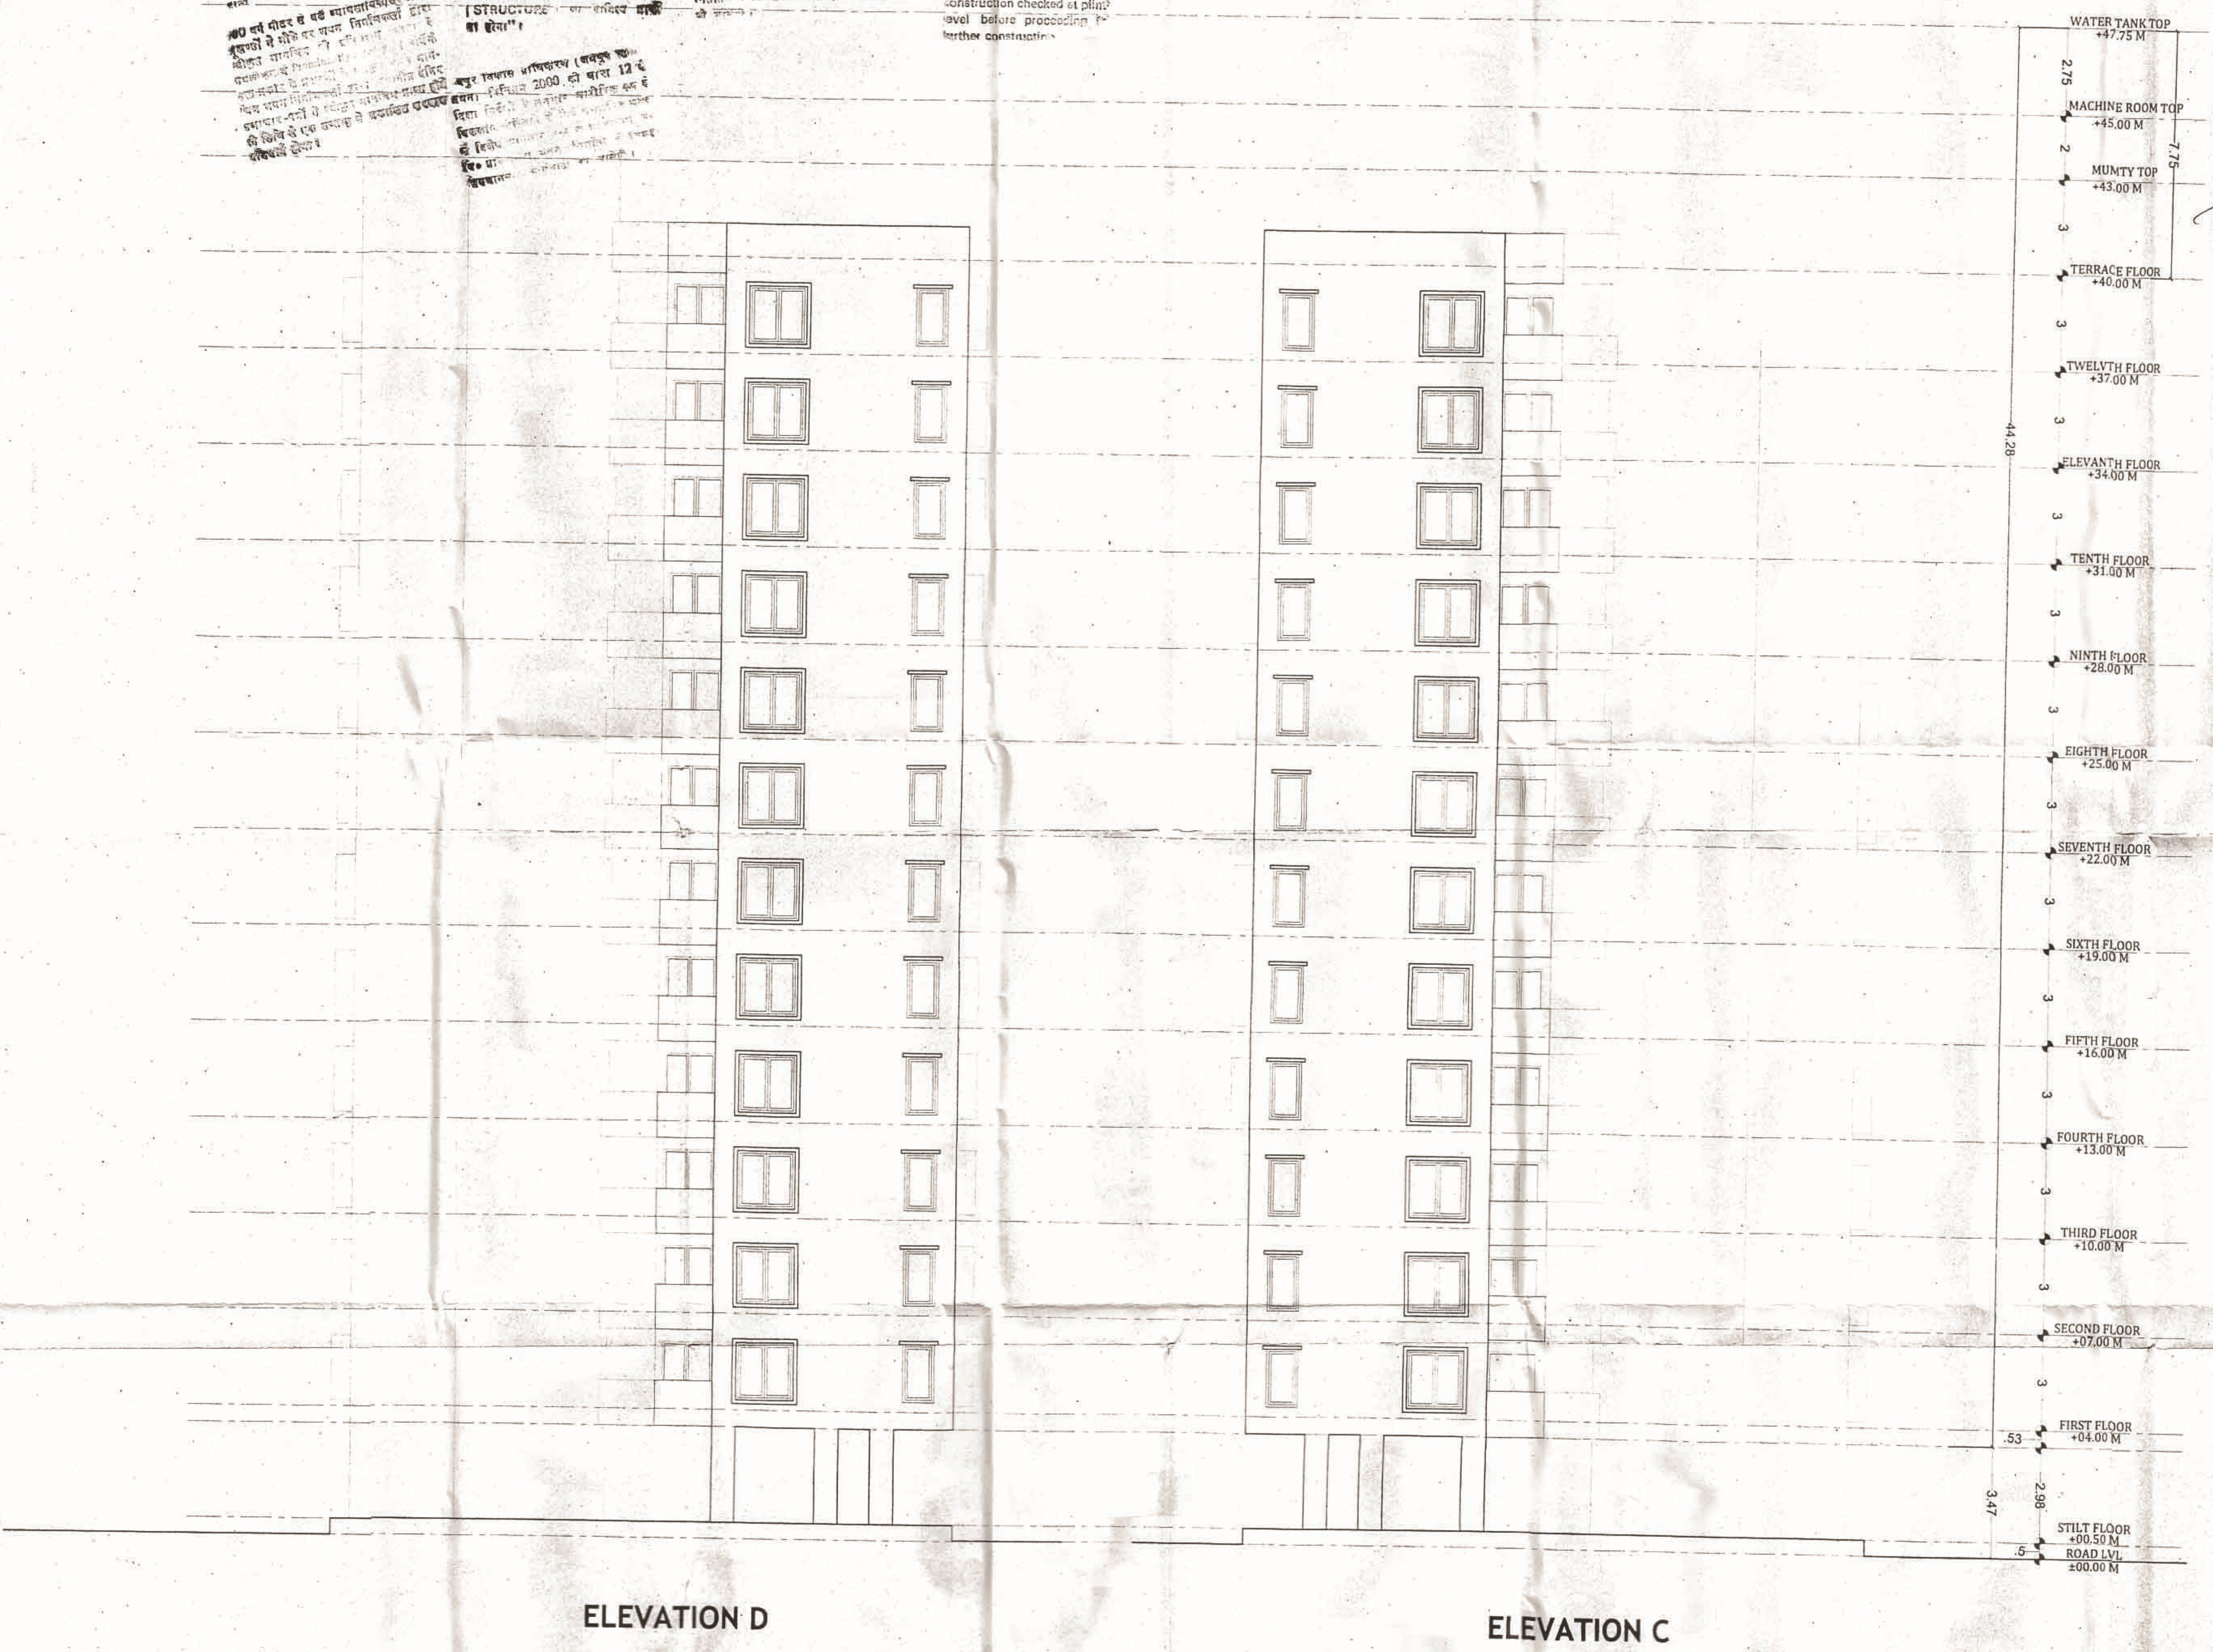

WATER TANK TOP +47.75 M
2.75
MACHINE ROOM TOP +45.00 M
2
7.75
MUMTY TOP +43.00 M
3
TERRACE FLOOR +40.00 M
3
TWELVTH FLOOR +37.00 M
3
44.28
ELEVANTH FLOOR +34.00 M
3
TENTH FLOOR +31.00 M
3
NINTH FLOOR +28.00 M
3
EIGHTH FLOOR +25.00 M
3
SEVENTH FLOOR +22.00 M
3
SIXTH FLOOR +19.00 M
3
FIFTH FLOOR +16.00 M
3
FOURTH FLOOR +13.00 M
3
THIRD FLOOR +10.00 M
3
SECOND FLOOR +07.00 M
3
.53
FIRST FLOOR +04.00 M
3.47
2.98
STILT FLOOR +00.50 M
.5
ROAD LVL ±00.00 M

ELEVATION D

ELEVATION C

SHEET NO.4

TITLE :- ELEVATIONS
C & D

भवन मानचित्र समिति (बी.पी.) की 164वीं
बैठक दिनांक 2/9/2014 में लिये गये निर्णय
की अनुपालना में भवन मानचित्र पत्रांक जविप्रा/
स.स./बीपीसी (बीपी)/डी-1270 दिनांक
26/5/2015 द्वारा अनुमोदित कर जारी किये गये।
अनुमोदित

21/5/15
उप नगर नियोजक (बी0 पी0 सी0)
जयपुर विकास प्राधिकरण
जयपुर

सदस्य सचिव (बी0 पी0 सी0)
जयपुर विकास प्राधिकरण
जयपुर
[illegible]/5/15

TITLE:- SUBMISSION DRAWINGS
ELEVATION A & ELEVATION B

SCALE:- 1= 100
DATE : 10-06-2014
NORTH :
N
W
E
S

PROJECT:- MAHIMA BELLEVUE
PROPOSED APARTMENTS
AT KHASARA NO.- 4760/3345,4776/3346,
4775/3345,4777/3346
REVENUE VILLAGE,KHO-NAGORIYAN,
TEH. SANGANER
JAIPUR (RAJ.)

ARCHITECTS:-
m|a| architects pvt. ltd.
Jaipur - Bangalore - Hyderabad
Plot No. -1, greenwood, Lal Kothi Scheme
Sahkar Marg Jaipur-302001
Tel : 91-141- 4299999
email- studio@maarchitects.in web- www.maarchitects.in

OWNER	ARCHITECTS
For MAHIMA REAL ESTATE [illegible] LTD Auth. Signatory	Ar. Puneet Dua B. Arch. CA/2005/35530

जयपुर विकास प्राधिकरण
समस्त [illegible]
[illegible]

[illegible] वर्ग मीटर से बड़े [illegible] द्वारा [illegible]
[illegible] स्वीकृत मानचित्र [illegible]
[illegible] होगा।

[illegible] किसी भी [illegible]
[illegible]
[illegible] (STRUCTURE) [illegible] उत्तरदायित्व [illegible] का होगा"।

[illegible] विकास प्राधिकरण (जयपुर [illegible]
भवन) विनियम 2000 की धारा 12 के
[illegible]
[illegible] के लिये
[illegible] की जायेगी।

जयपुर विकास प्राधिकरण (जयपुर क्षेत्र
भवन) विनियम [illegible] की धारा 8.15 के
[illegible]
की जायेगी।

applicant should get the construction checked at plinth level before proceeding for further construction

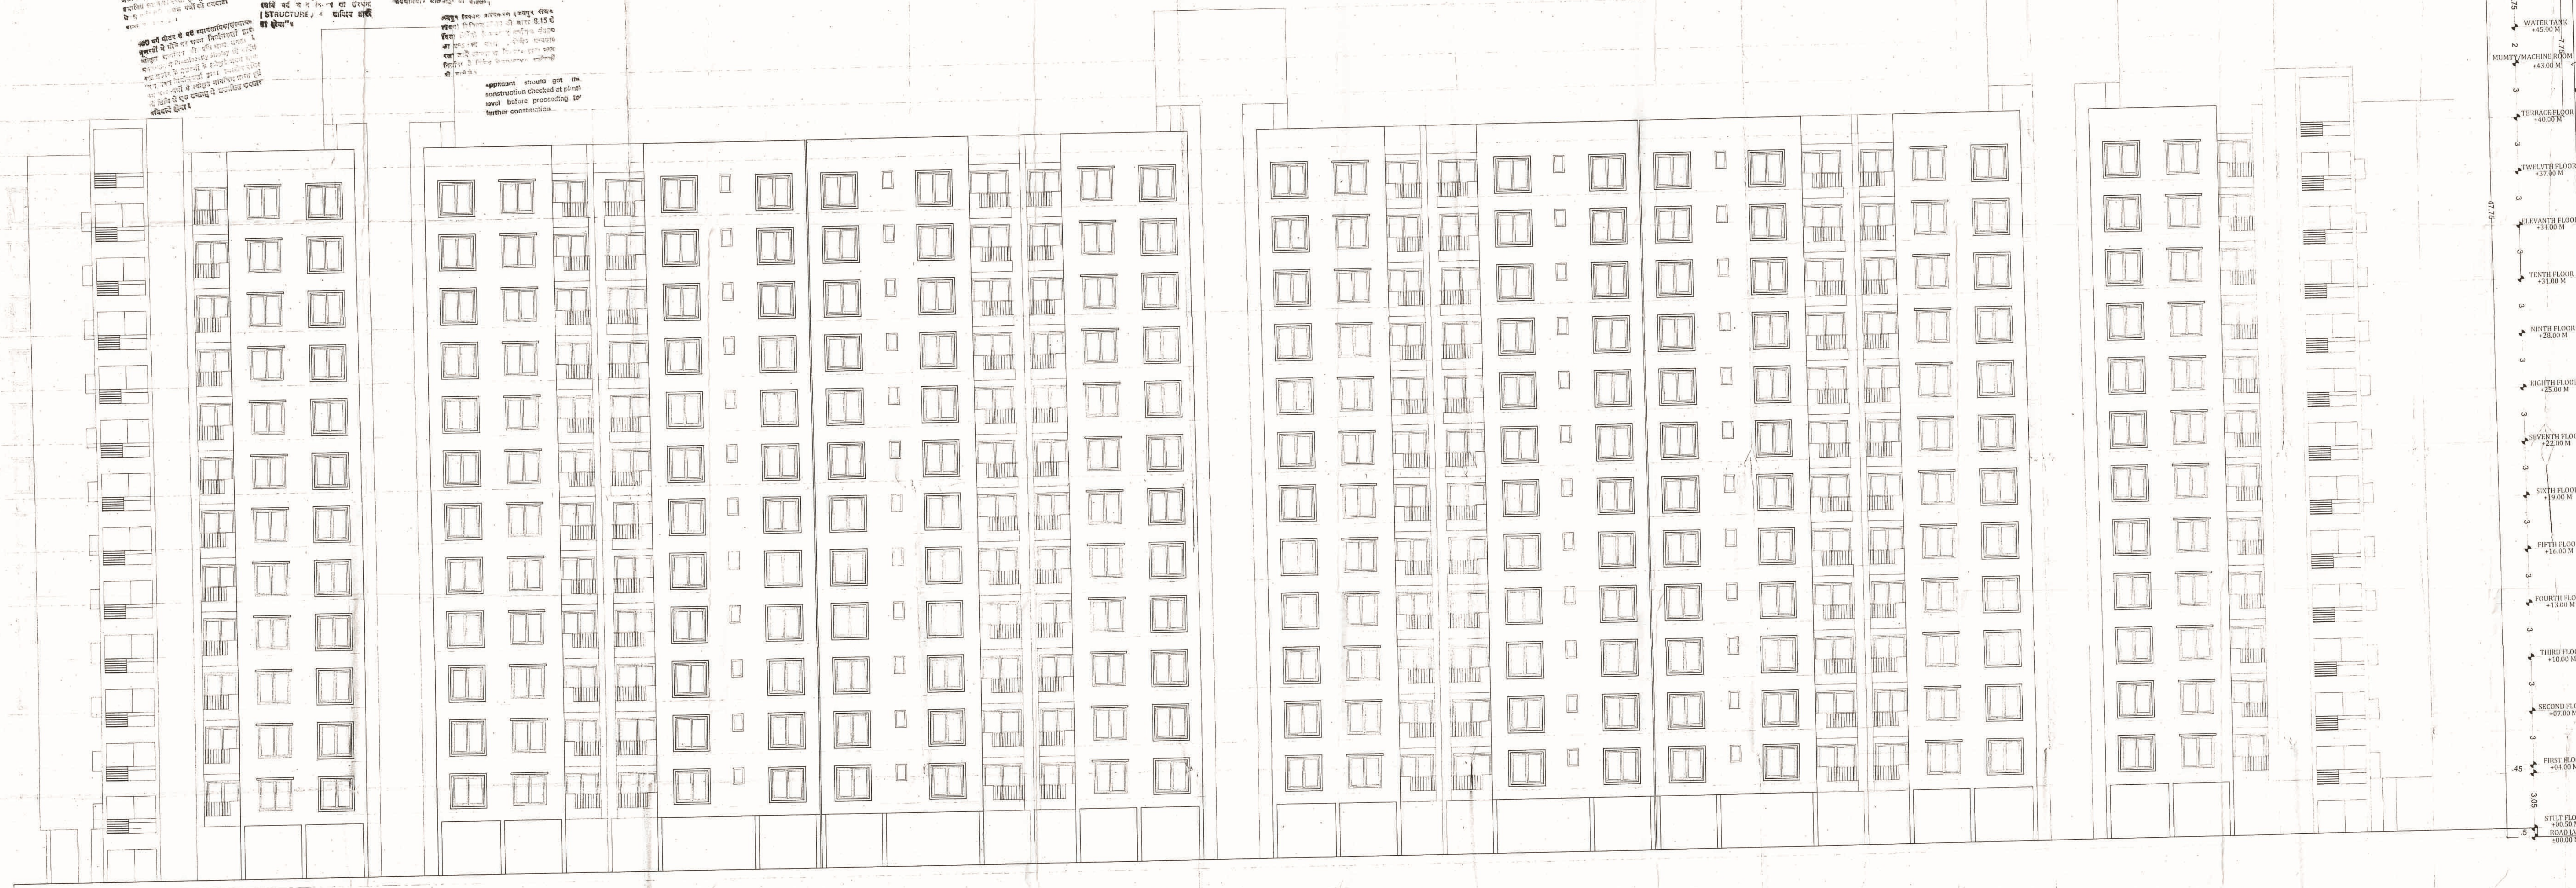

+47.75 M
2.75
WATER TANK +45.00 M
2
7.75
MUMTY/MACHINE ROOM +43.00 M
3
TERRACE FLOOR +40.00 M
3
TWELVTH FLOOR +37.00 M
3
47.75
ELEVANTH FLOOR +34.00 M
3
TENTH FLOOR +31.00 M
3
NINTH FLOOR +28.00 M
3
EIGHTH FLOOR +25.00 M
3
SEVENTH FLOOR +22.00 M
3
SIXTH FLOOR +19.00 M
3
FIFTH FLOOR +16.00 M
3
FOURTH FLOOR +13.00 M
3
THIRD FLOOR +10.00 M
3
SECOND FLOOR +07.00 M
3
.45
FIRST FLOOR +04.00 M
3.05
STILT FLOOR +00.50 M
.5
ROAD LVL ±00.00 M

ELEVATION A

SHEET NO.5

TITLE :- ELEVATION A

भवन मानचित्र समिति (बी.पी.) की 164... बैठक दिनांक 12/9/2014 में लिये गये की अनुपालना में भवन मानचित्र पत्रांक व स.स./बीपीसी (बीपी)/डी-1270 दिनांक 26/5/2015 द्वारा अनुमोदित कर जारी कि...

अनुमोदित

उप नगर नियोजक (बी0 पी0 सी0)
जयपुर विकास प्राधिकरण
जयपुर

[illegible] (बी0 पी0 सी0)
जयपुर विकास प्राधिकरण
जयपुर

TITLE:- SUBMISSION DRAWINGS
ELEVATION A

SCALE:- 1= 100

NORTH :

DATE :- 10-06-2014

PROJECT:- MAHIMA BELLEVUE
PROPOSED APARTMENTS
AT KHASARA NO.- 4760/3345,4776/3346,
4775/3345,4777/3346
REVENUE VILLAGE,KHO-NAGORIYAN,
TEH. SANGANER
JAIPUR (RAJ.)

ARCHITECTS:-
m|a| architects pvt. ltd.
Jaipur - Bangalore - Hyderabad
Plot No. -1, greenwood, Lal Kothi Scheme
Sahkar Marg Jaipur-302001
Tel : 91-141- 4299999
email- studio@maarchitects.in web- www.maarchitects.in

OWNER	ARCHITECTS
For MAHIMA REAL ESTATE PVT. LTD. Auth. Signatory	Ar. Puneet Dua B. Arch. CA/2005/35530

जयपुर विकास प्राधिकरण
समस्त बहुमंजिली इमारतों एवं विकास [illegible] यंत्रों की व्यवस्था [illegible] जाना आवश्यक है।

इस मानचित्र का अनुमोदन किसी भी व्यक्ति [illegible] STRUCTURE) का दायित्व [illegible] का होगा"।

500 वर्ग मीटर से बड़े व्यावसायिक/संस्थानिक [illegible] भवन निर्माणकर्ता [illegible]

जयपुर विकास प्राधिकरण (जयपुर [illegible]) [illegible] 12 [illegible]

जयपुर विकास प्राधिकरण (जयपुर [illegible]) [illegible] 8.15 [illegible]

Applicant should get the construction checked at plinth level before proceeding for further construction.

+47.75 M
2.75
WATER TANK
+45.00 M
2
7.75
MUMTY/MACHINE ROOM
+43.00 M
3
TERRACE FLOOR
+40.00 M
3
TWELVTH FLOOR
+37.00 M
3
47.75
ELEVANTH FLOOR
+34.00 M
3
TENTH FLOOR
+31.00 M
3
NINTH FLOOR
+28.00 M
3
EIGHTH FLOOR
+25.00 M
3
SEVENTH FLOOR
+22.00 M
3
SIXTH FLOOR
+19.00 M
3
FIFTH FLOOR
+16.00 M
3
FOURTH FLOOR
+13.00 M
3
THIRD FLOOR
+10.00 M
3
SECOND FLOOR
+07.00 M
3
FIRST FLOOR
+04.00 M
.45
3.05
STILT FLOOR
+00.50 M
.5
ROAD LVL.
±00.00 M

ELEVATION B

SHEET NO.6

TITLE :- ELEVATION B

भवन मानचित्र समिति (बी.पी.) की ..164.....वीं बैठक दिनांक 12/9/2014 में लिये गये निर्णय की अनुपालना में भवन मानचित्र पत्रांक जविप्रा/ स.स./बीपीसी (बीपी)/डी-1270 दिनांक....... 26/5/2015 द्वारा अनुमोदित कर जारी किये गये।

अनुमोदित

उप नगर नियोजक (बी0 पी0 सी0)
जयपुर विकास प्राधिकरण
जयपुर
21/5/15

सदस्य सचिव (बी0 पी0 सी0)
जयपुर विकास प्राधिकरण
जयपुर
26/5/15

TITLE:- SUBMISSION DRAWINGS
ELEVATION B

SCALE:- 1= 100
DATE :- 10-06-2014
NORTH

PROJECT:- MAHIMA BELLEVUE
PROPOSED APARTMENTS
AT KHASARA NO.- 4760/3345,4776/3346,
4775/3345,4777/3346
REVENUE VILLAGE,KHO-NAGORIYAN,
TEH. SANGANER
JAIPUR (RAJ.)

ARCHITECTS:-
m|a| architects pvt. ltd.
Jaipur - Bangalore - Hyderabad
Plot No. -J, greenwood, Lal Kothi Scheme
Sahkar Marg Jaipur-302001
Tel : 91-141- 4299999
email- studio@maarchitects.in web- www.maarchitects.in

OWNER	ARCHITECTS
For MAHIMA REAL ESTATE PVT LTD Auth. Signatory	Ar. Puneet Dua B. Arch. CA/2005/35530

जयपुर विकास प्राधिकरण
समस्त [illegible] हो
[illegible] दूसरा
[illegible] की उपधारा
[illegible]

इस मानचित्र का अनुमोदन किसी भी भौतिक [illegible] भूमि/भूखण्ड के प्रति स्वामित्व [illegible]
[illegible] अधिकार
इससे [illegible]
ही प्रमाणित होंगे।
[illegible] STRUCTURE [illegible] होगा"।

[illegible] वर्ग मीटर से बड़े व्यावसायिक/संस्थानिक [illegible]
[illegible] निर्माणकर्ता [illegible]
[illegible] होगा।

जयपुर विकास प्राधिकरण (जयपुर [illegible]) 2000 की धारा 12 [illegible]
[illegible]

जयपुर विकास [illegible] धारा 8.15 [illegible]
[illegible]

Applicant should get the construction checked at plinth level before proceeding for further construction.

WATER TANK
MACHINE ROOM
WATER TANK
MACHINE ROOM
WATER TANK
MACHINE ROOM
TREAD = 0.30
RISER = 0.15
WIDTH = 1.2
+47.75 M
2.75
WATER TANK
+45.00 M
2
7.75
MUMTY/MACHINE ROOM
+43.00 M
3
TERRACE FLOOR
+40.00 M
3
TWELVTH FLOOR
+37.00 M
3
47.75
ELEVANTH FLOOR
+34.00 M
3
TENTH FLOOR
+31.00 M
3
NINTH FLOOR
+28.00 M
3
EIGHTH FLOOR
+25.00 M
3
SEVENTH FLOOR
+22.00 M
3
SIXTH FLOOR
+19.00 M
3
FIFTH FLOOR
+16.00 M
3
FOURTH FLOOR
+13.00 M
3
THIRD FLOOR
+10.00 M
3
SECOND FLOOR
+07.00 M
3
.45
FIRST FLOOR
+04.00 M
3.05
STILT FLOOR
+00.50 M
.5
ROAD LEVEL
±00.00 M

SECTION AT AA

SHEET NO.7

TITLE :- SECTION AT AA

भवन मानचित्र समिति (बी.पी.) की 164 वीं बैठक दिनांक 12/5/2015 में लिये गये निर्णय की अनुपालना में भवन मानचित्र पत्रांक जविप्रा/ स.स./बीपीसी (बीपी)/डी-1270 दिनांक 26/5/2015 द्वारा अनुमोदित कर जारी किये गये।

अनुमोदित

21/5/15
उप नगर नियोजक (बी0 पी0 सी0)
जयपुर विकास प्राधिकरण
जयपुर

सदस्य सचिव (बी0 पी0 सी0)
जयपुर विकास प्राधिकरण
जयपुर

TITLE:- SUBMISSION DRAWINGS
SECTION AT AA

SCALE:- 1= 100
DATE :- 10-06-2014
NORTH :

PROJECT:- MAHIMA BELLEVUE
PROPOSED APARTMENTS
AT KHASARA NO.- 4760/3345,4776/3346,
4775/3345,4777/3346
REVENUE VILLAGE,KHO-NAGORIYAN,
TEH. SANGANER
JAIPUR (RAJ.)

ARCHITECTS:-
m|a| architects pvt. ltd.
Jaipur - Bangalore - Hyderabad
Plot No. -1, greenwood, Lal Kothi Scheme
Sahkar Marg Jaipur-302001
Tel : 91-141- 4299999
email- studio@maarchitects.in web- www.maarchitects.in

OWNER	ARCHITECTS
For MAHIMA REAL ESTATE PVT. LTD Auth. Signatory	Ar. Puneet Dua B. Arch. CA/2005/35530

जयपुर विकास प्राधिकरण

समस्त बहुमंजिली इमारतों एवं विशाल [illegible] व्यावसायिक [illegible] अलार्म एवं [illegible] प्रदर्शित स्थान पर [illegible] किसी भांति [illegible] जाना [illegible]

500 वर्ग मीटर से बड़े व्यावसायिक/संस्थानिक भूखण्डों से मौके पर भवन निर्माणकर्ता द्वारा स्वीकृत [illegible] (Prominently display) [illegible] की तिथि से एक सप्ताह में प्रदर्शित करना अनिवार्य होगा।

इस मानचित्र का अनुमोदन किसी भी प्रकार से सम्बन्धित भूमि/भूखण्ड के प्रति स्वामित्व [illegible] संरचना (STRUCTURE) का दायित्व [illegible] का होगा।

जयपुर विकास प्राधिकरण (जयपुर [illegible]) अधिनियम 2000 की धारा 12 [illegible]

Applicant [illegible] construction checked at plinth level before processing for further construction.

जयपुर विकास प्राधिकरण (जयपुर [illegible]) [illegible] 8.15 [illegible]

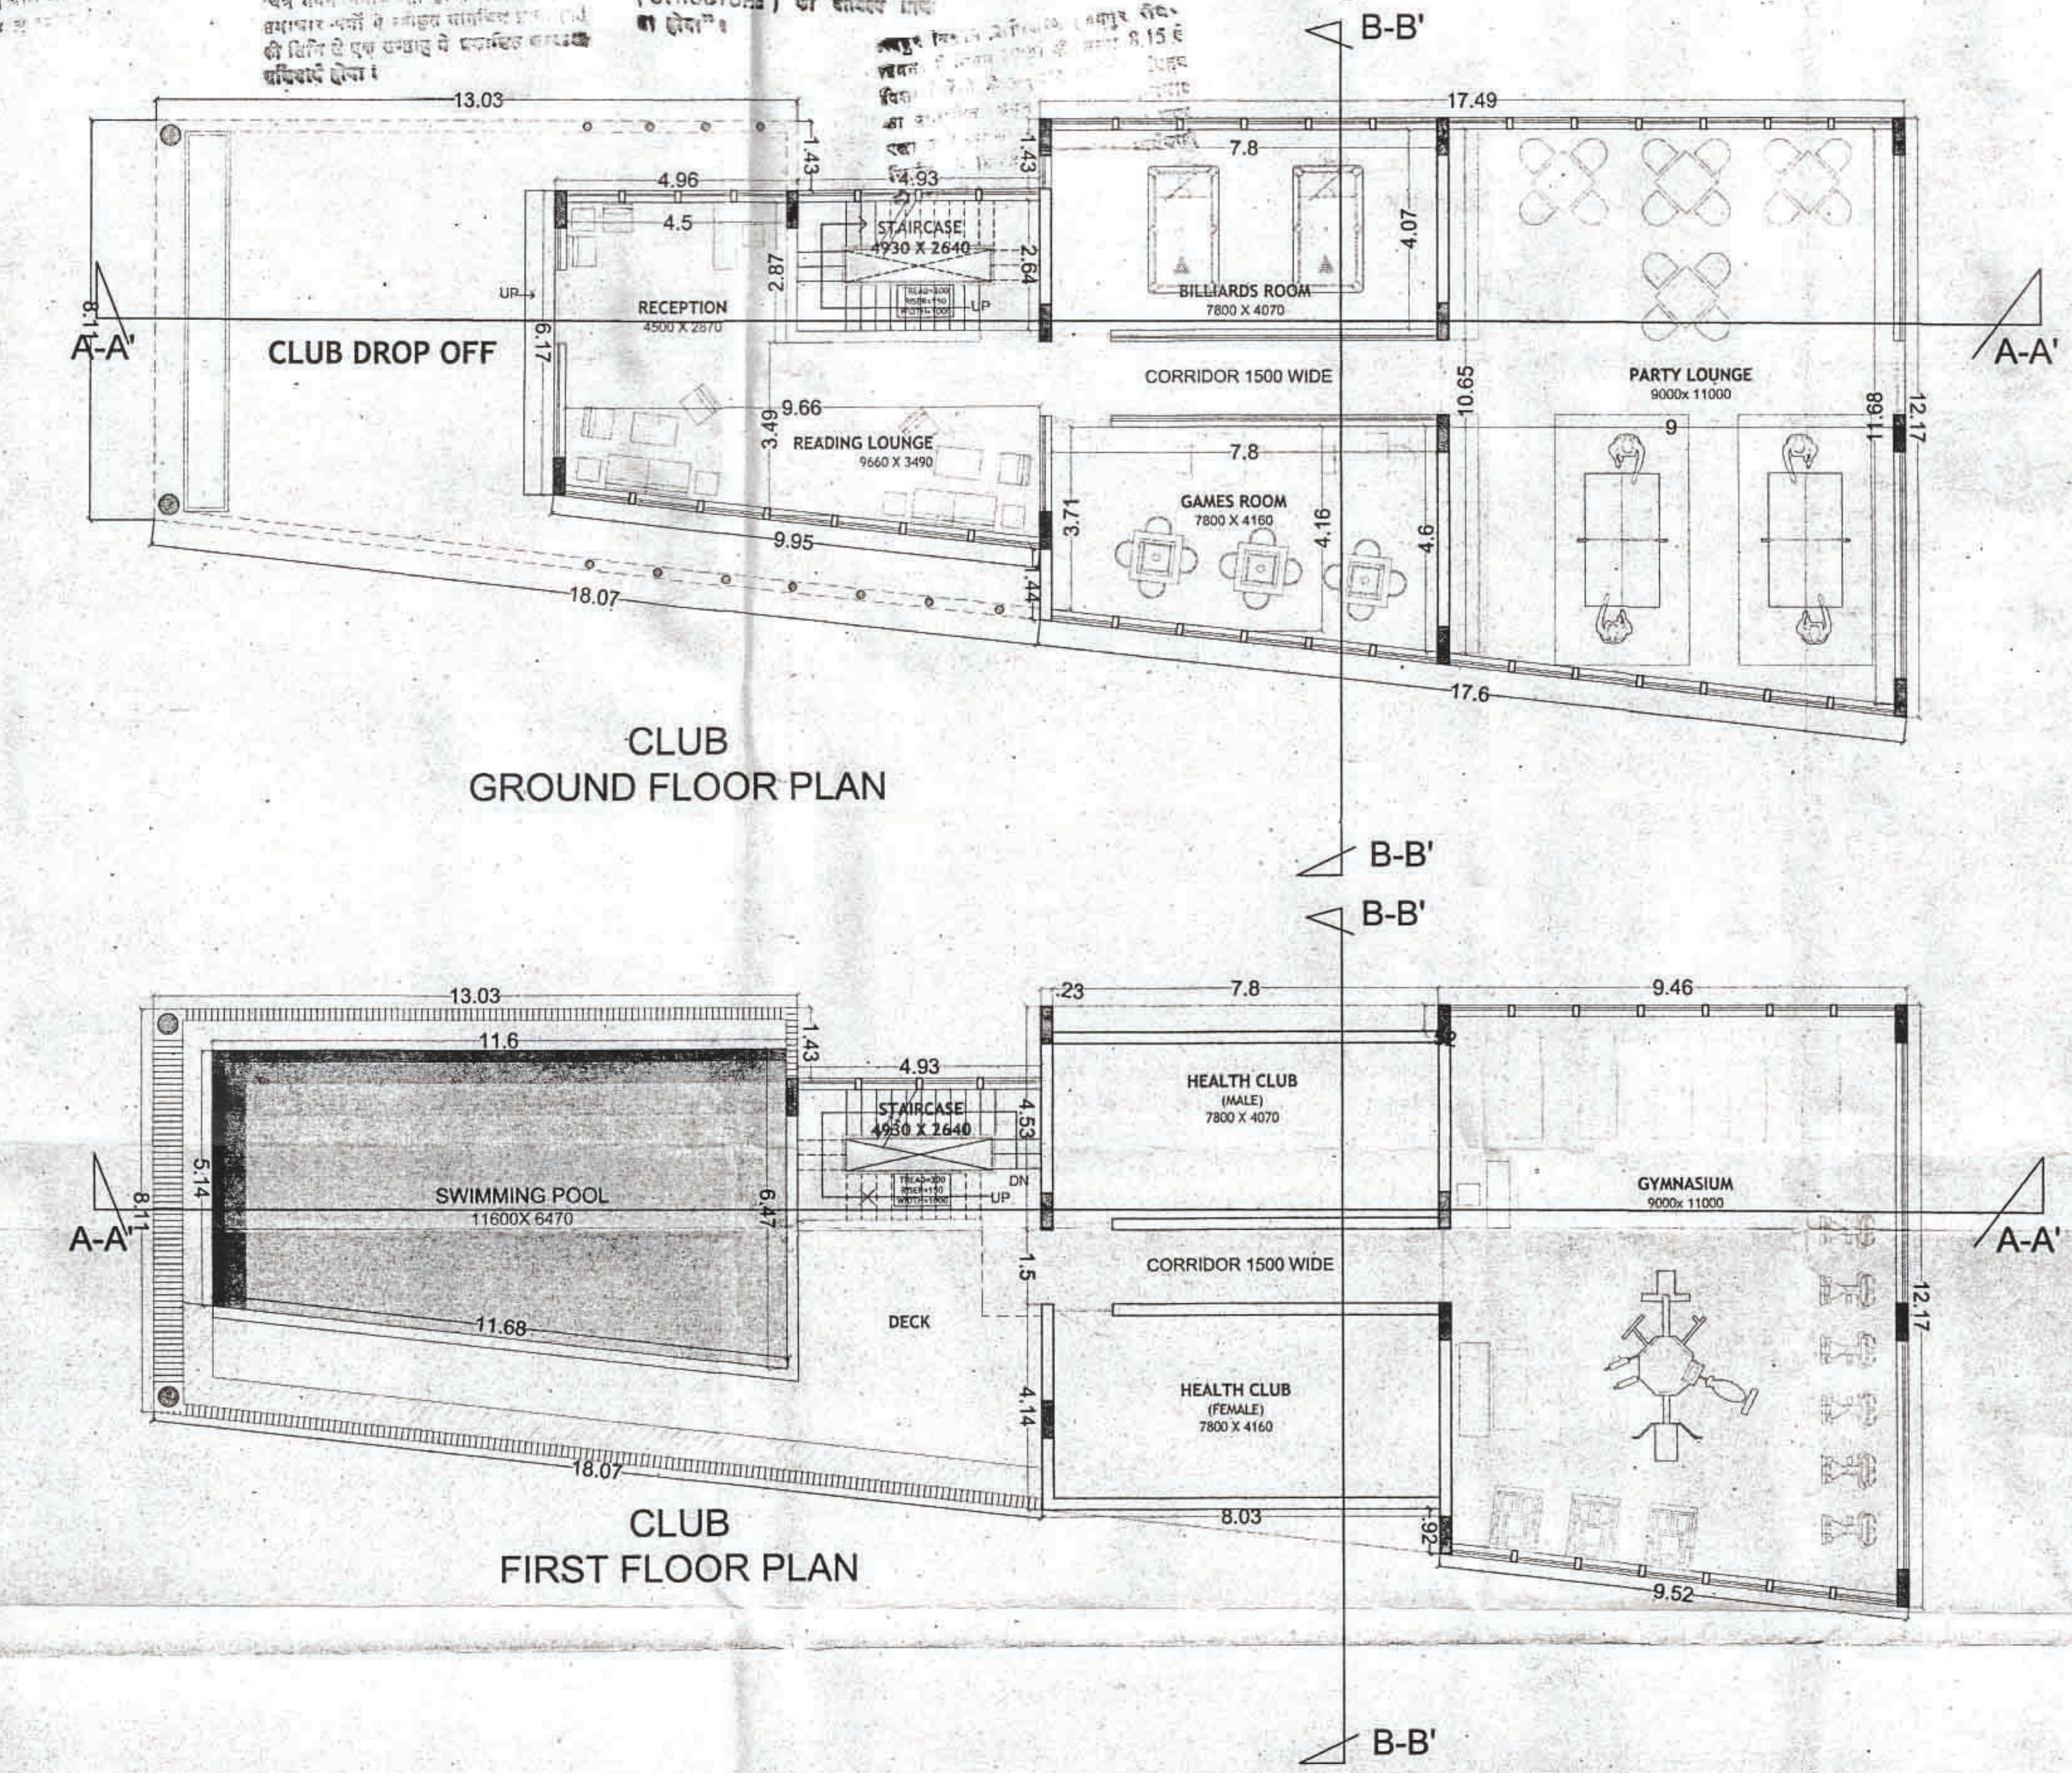
B-B'
13.03
17.49
1.43
4.96
4.93
4.5
7.8
STAIRCASE
4930 X 2640
2.87
2.64
4.07
UP
RECEPTION
4500 X 2870
BILLIARDS ROOM
7800 X 4070
A-A'
8.1
6.17
CLUB DROP OFF
CORRIDOR 1500 WIDE
10.65
PARTY LOUNGE
9000x 11000
11.68
12.17
9
9.66
3.49
READING LOUNGE
9660 X 3490
GAMES ROOM
7800 X 4160
3.71
4.16
4.6
9.95
1.44
18.07
17.6
CLUB
GROUND FLOOR PLAN
B-B'
B-B'
13.03
.23
7.8
9.46
11.6
1.43
4.93
HEALTH CLUB
(MALE)
7800 X 4070
STAIRCASE
4930 X 2640
4.53
DN
UP
5.14
8.11
SWIMMING POOL
11600X 6470
6.47
GYMNASIUM
9000x 11000
A-A'
A-A'
1.5
CORRIDOR 1500 WIDE
11.68
DECK
12.17
HEALTH CLUB
(FEMALE)
7800 X 4160
4.14
18.07
8.03
.92
9.52
CLUB
FIRST FLOOR PLAN
B-B'

SHEET NO.8

TITLE :-
GROUND, FIRST &TERRACE FLOOR PLAN

भवन मानचित्र समिति (बी.पी.) की 164 वीं बैठक दिनांक 12/9/2014 में लिये गये निर्णय की अनुपालना में भवन मानचित्र पत्रांक ज.वि.प्रा./बीपीसी (बीपी)/डी. 1270 दिनांक 26/5/2015 द्वारा अनुमोदित कर जारी किये गये।

अनुमोदित

उप नगर नियोजक बी.पी. सेल
जयपुर विकास प्राधिकरण
जयपुर

सदस्य सचिव (बी.पी.सी. सेल)
जयपुर विकास प्राधिकरण
जयपुर

TITLE:- SUBMISSION DRAWINGS
CLUB HOUSE GROUND FLOOR PLAN
FIRST FLOOR PLAN & TERRACE FLOOR PLAN

SCALE:- 1= 100
DATE : 10-06-2014

NORTH :
N
W E
S

PROJECT:- MAHIMA BELLEVUE
PROPOSED APARTMENTS
AT KHASARA NO.- 4760/3345,4776/3346,
4775/3345,4777/3346
REVENUE VILLAGE,KHO-NAGORIYAN,
TEH. SANGANER
JAIPUR (RAJ.)

ARCHITECTS:-
m|a| architects pvt. ltd.
Jaipur - Bangalore - Hyderabad
Plot No. -1, greenwood, Lal Kothi Scheme
Sahkar Marg Jaipur-302001
Tel : 91-141- 4299999
email- studio@maarchitects.in web- www.maarchitects.in

OWNER
ARCHITECTS

For MAHIMA REAL ESTATE PVT LTD
Auth. Signatory

Ar. Puneet Dua
B. Arch.
CA/2005/35530

जयपुर विकास प्राधिकरण
समस्त बहुमंजिले [illegible] एवं विशाल
व्यवसायिक [illegible]
[illegible]
[illegible]
[illegible] वर्षों की अवधि

उक्त मानचित्र का अनुमोदन [illegible] की
[illegible] भूमि/[illegible] के प्रति [illegible]
प्रमाण-पत्र [illegible]
[illegible]
[illegible]
[illegible]
[illegible]
STRUCTURE [illegible] का दायित्व [illegible]
का होगा"।

400 वर्ग मीटर से बड़े व्यावसायिक/संस्थानिक
भूखण्डों से मौके पर भवन निर्माणकर्ता द्वारा
स्वीकृत [illegible]
[illegible] conspicuously display की [illegible]
[illegible]
[illegible] भवन निर्माणकर्ता द्वारा [illegible]
[illegible] से स्वीकृत मानचित्र [illegible]
की तिथि से एक सप्ताह में [illegible]
अनिवार्य होगा।

जयपुर विकास प्राधिकरण (जयपुर [illegible]
[illegible] 2000 की धारा 12 [illegible]
[illegible]

जयपुर [illegible] (जयपुर [illegible]
[illegible] की धारा 8 15 [illegible]
[illegible]

applicant should get [illegible] construction checked at plinth level before proceeding for further construction

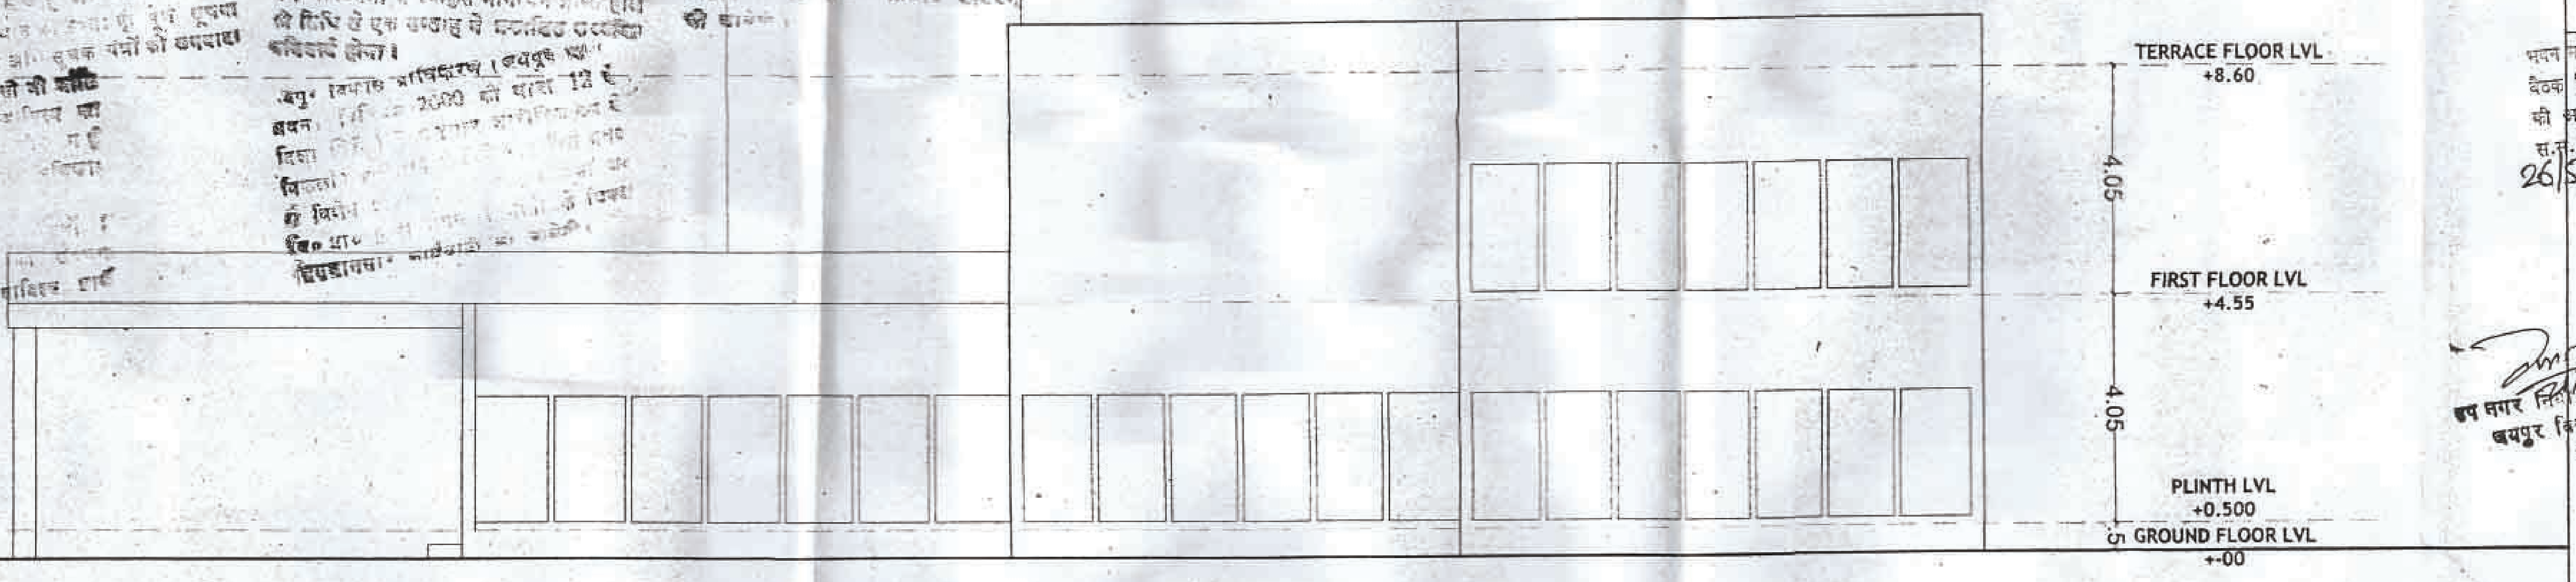
MUMTY LVL
+11.00
TERRACE FLOOR LVL
+8.60
4.05
FIRST FLOOR LVL
+4.55
4.05
PLINTH LVL
+0.500
.5
GROUND FLOOR LVL
+-00

FRONT ELEVATION

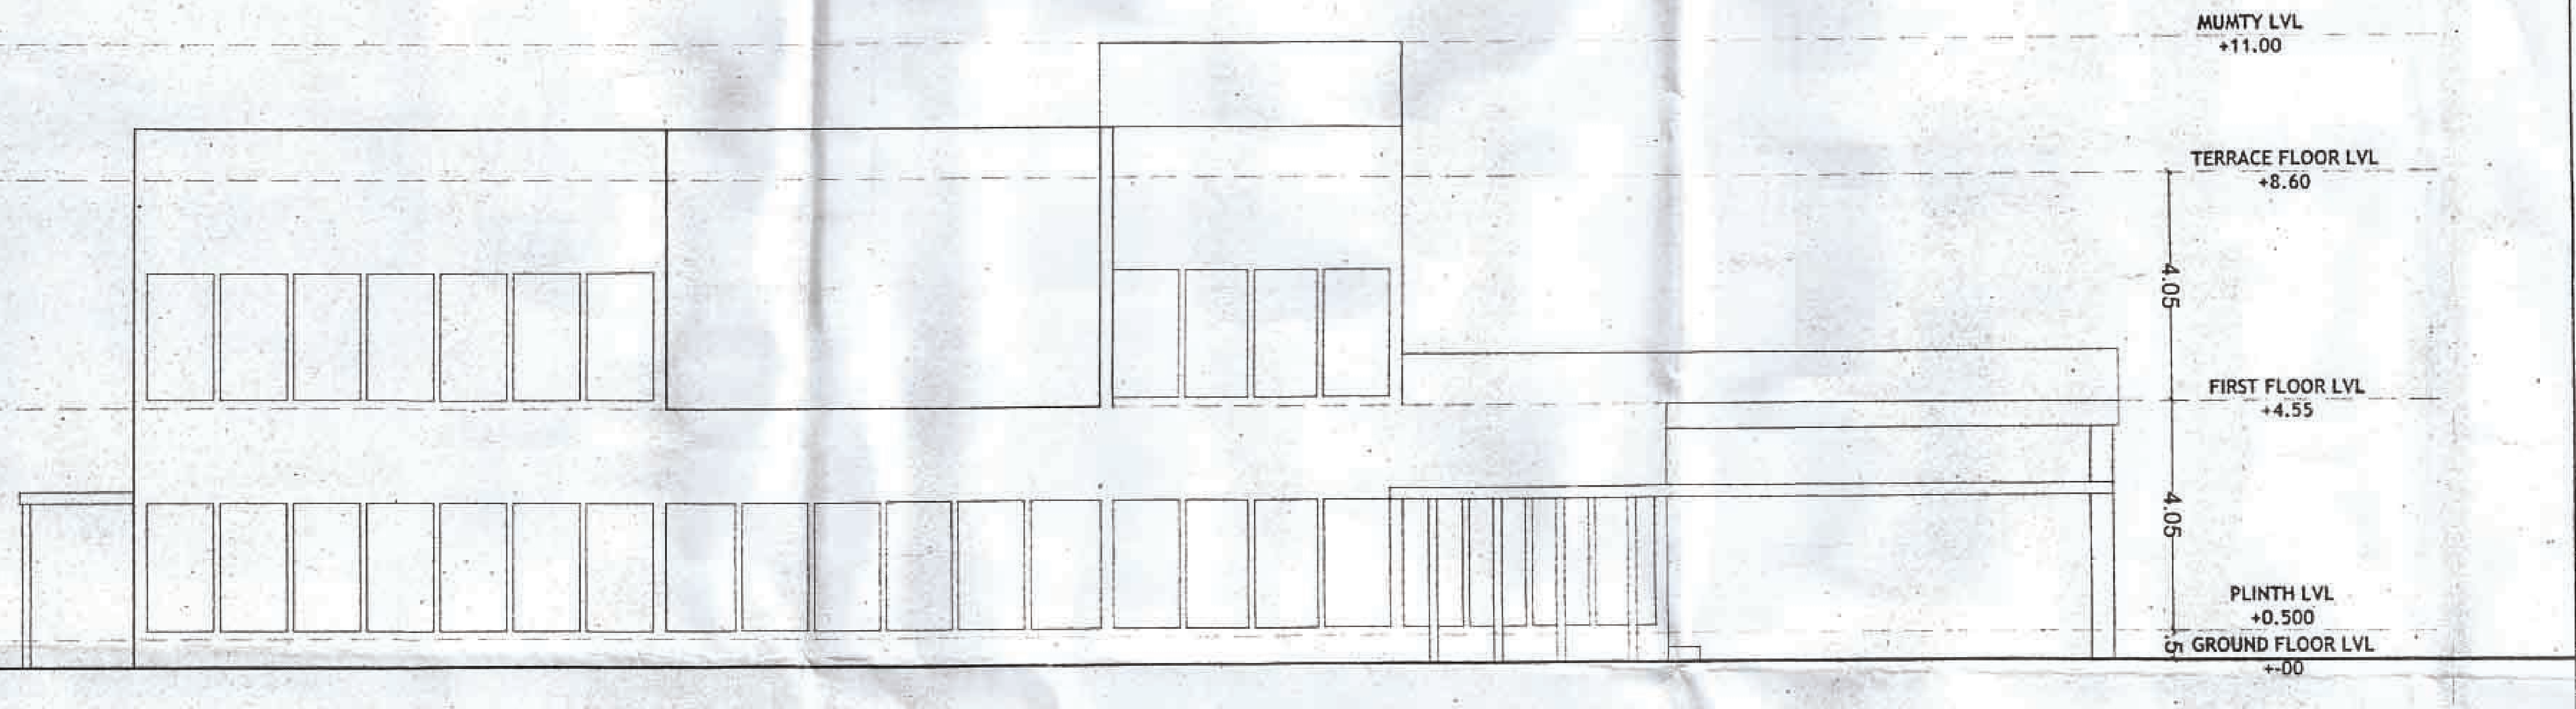
MUMTY LVL
+11.00
TERRACE FLOOR LVL
+8.60
4.05
FIRST FLOOR LVL
+4.55
4.05
PLINTH LVL
+0.500
.5
GROUND FLOOR LVL
+-00

REAR ELEVATION

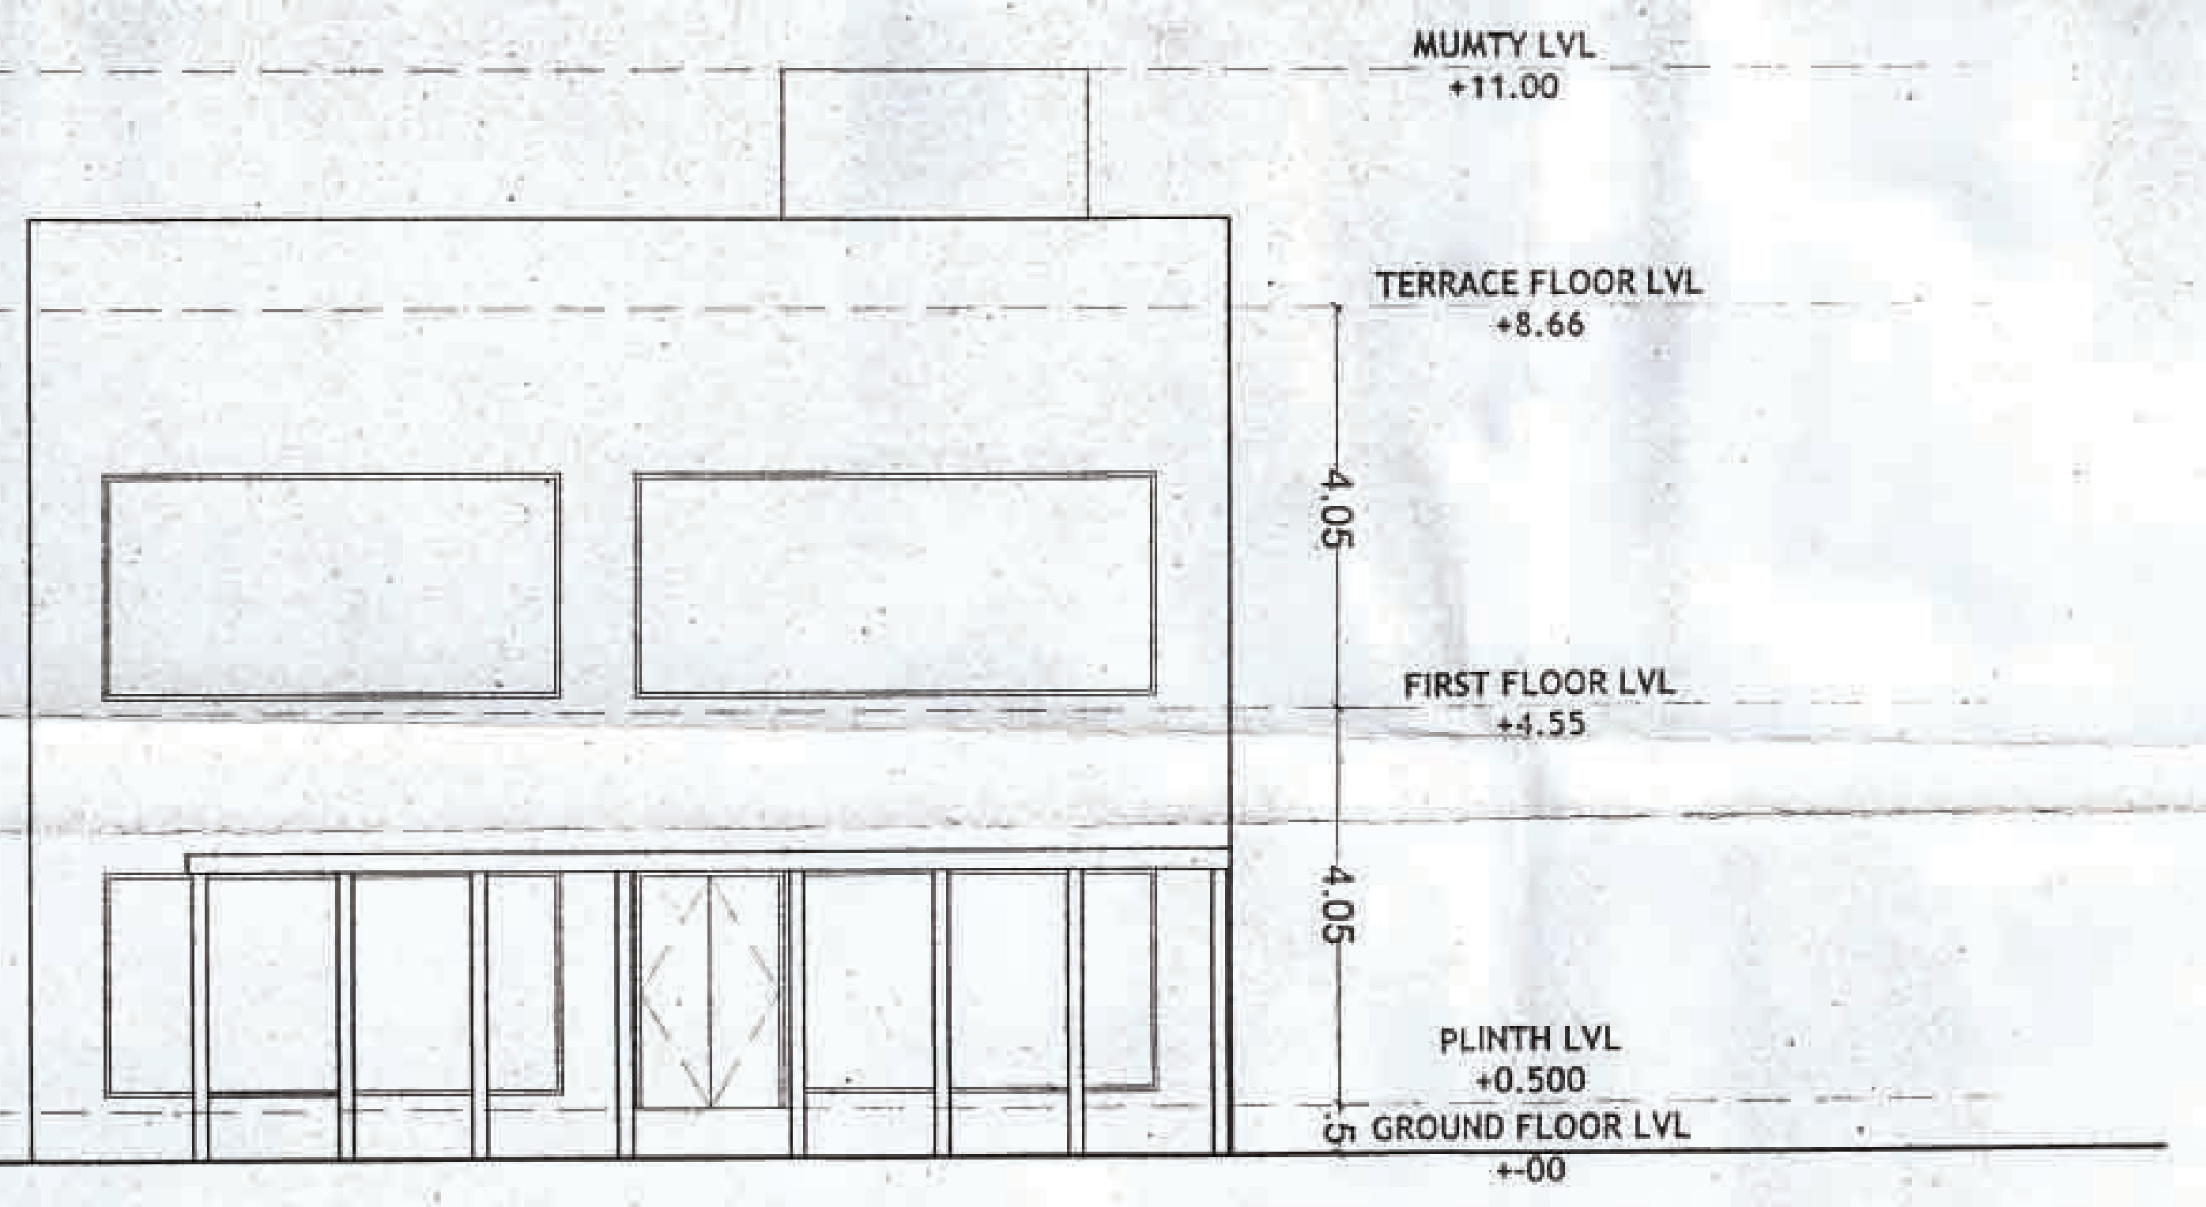
MUMTY LVL
+11.00
TERRACE FLOOR LVL
+8.66
4.05
FIRST FLOOR LVL
+4.55
4.05
PLINTH LVL
+0.500
.5
GROUND FLOOR LVL
+-00

EAST SIDE ELEVATION

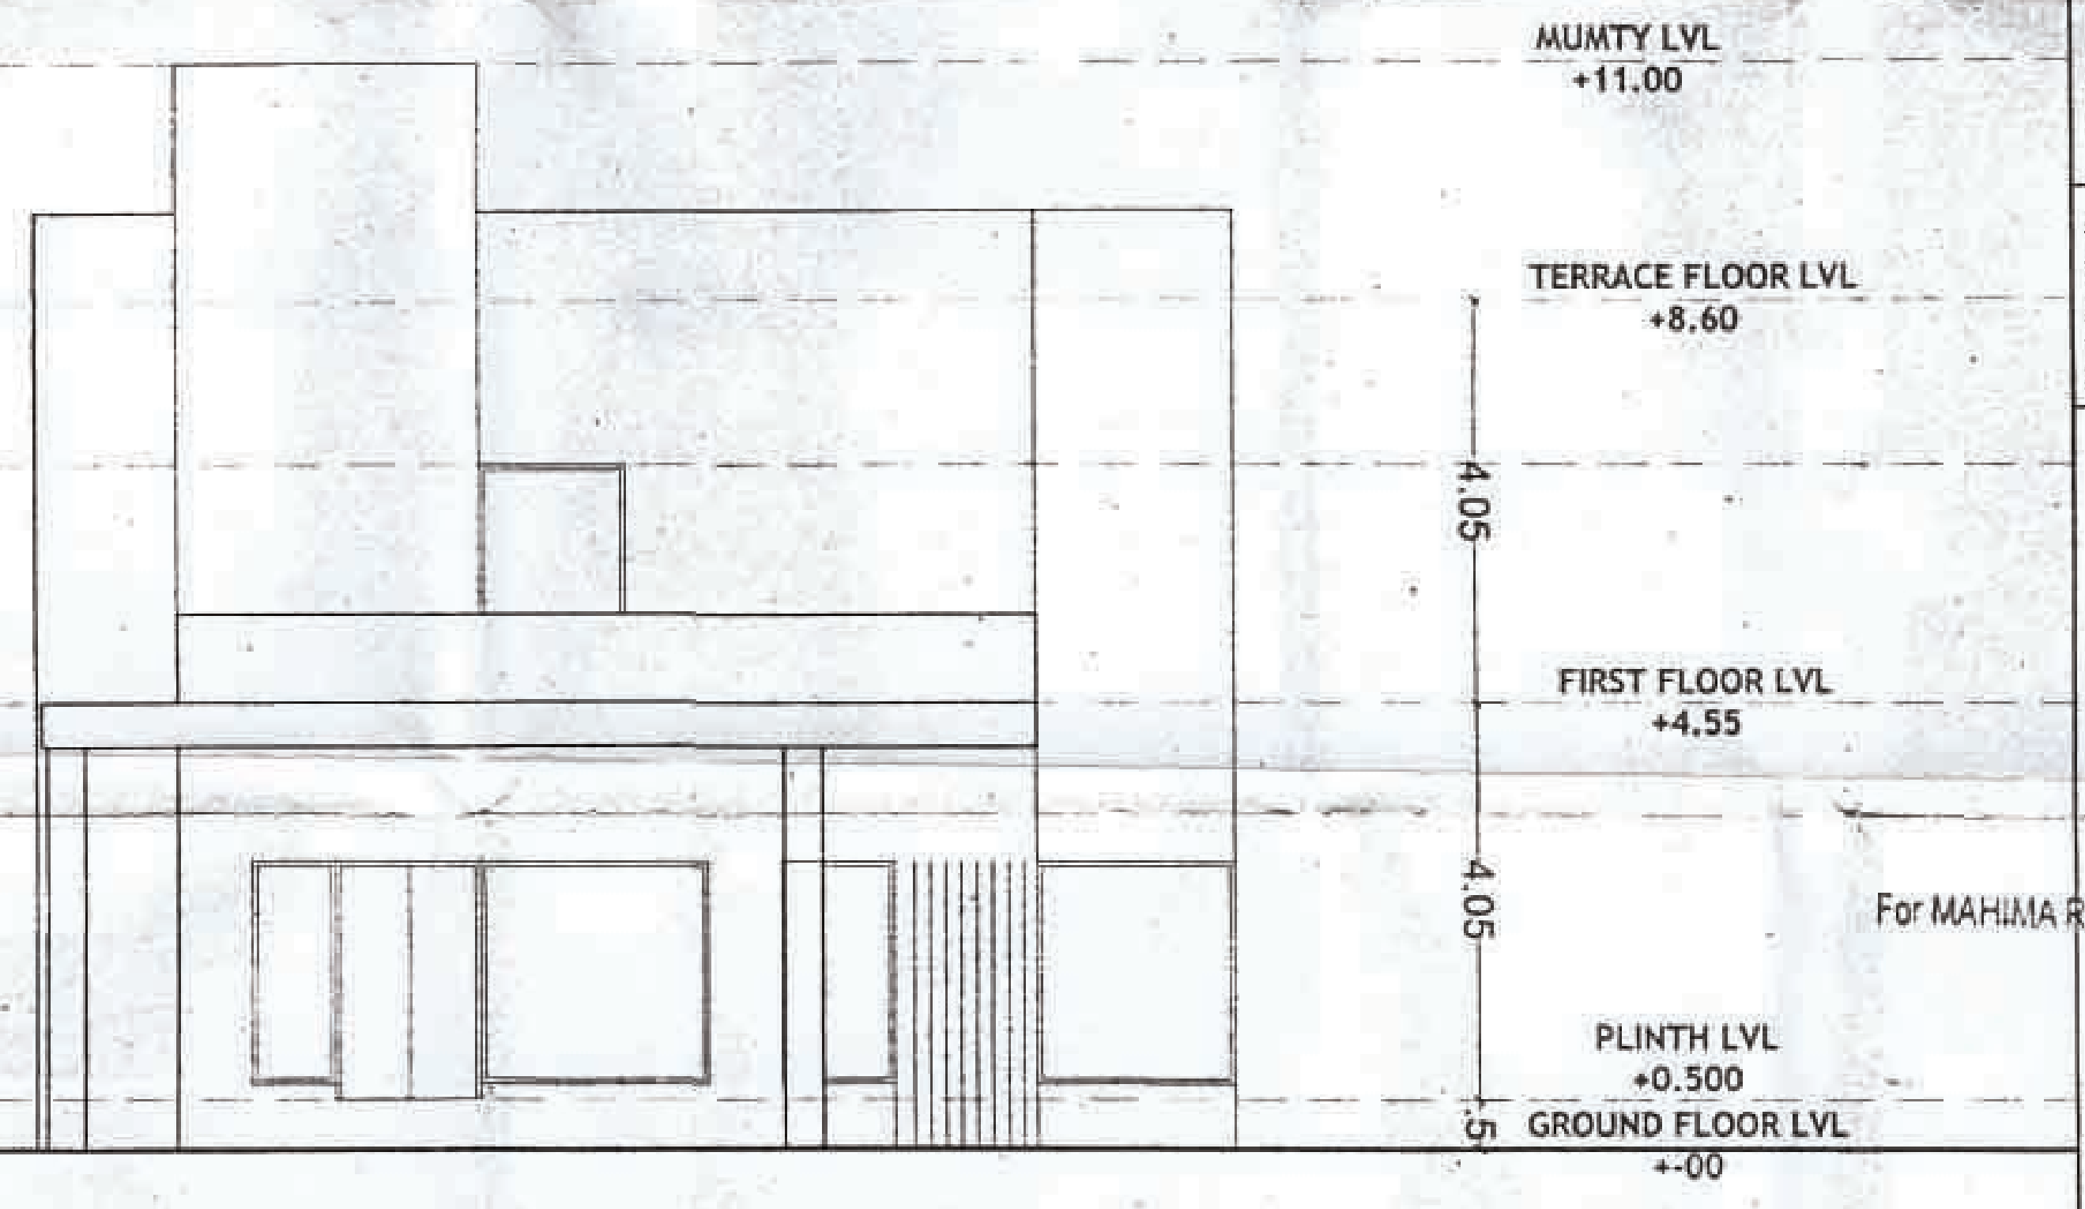
MUMTY LVL
+11.00
TERRACE FLOOR LVL
+8.60
4.05
FIRST FLOOR LVL
+4.55
4.05
PLINTH LVL
+0.500
.5
GROUND FLOOR LVL
+-00

WEST SIDE ELEVATION

SHEET NO.9

TITLE :-
CLUB HOUSE ELEVATIONS

भवन मानचित्र समिति (बी.पी.) की 164 वीं बैठक दिनांक 12/9/2014 में लिये गये निर्णय की अनुपालना में भवन मानचित्र पत्रावली/ स.स./बीपीसी (बीपी)/डी-1270 दिनांक 26/5/2015 द्वारा अनुमोदित कर जारी किये गये।

अनुमोदित

उप नगर नियोजक बी0 पी0 सी0
जयपुर विकास प्राधिकरण
जयपुर

सदस्य सचिव (बी0पी0सी0)
जयपुर विकास प्राधिकरण
जयपुर

TITLE :- SUBMISSION DRAWINGS
CLUB HOUSE ELEVATIONS

SCALE :- 1= 100
DATE : 10-06-2014
NORTH :

PROJECT :- MAHIMA BELLEVUE
PROPOSED APARTMENTS
AT KHASARA NO.- 4760/3345,4776/3346,
4775/3345,4777/3346
REVENUE VILLAGE,KHO-NAGORIYAN,
TEH. SANGANER
JAIPUR (RAJ.)

ARCHITECTS:-
m|a|architects pvt. ltd.
Jaipur - Bangalore - Hyderabad
Plot No. -1, greenwood, Lal Kothi Scheme
Sahkar Marg Jaipur-302001
Tel : 91-141- 4299999
email- [illegible] web- www.maarchitects.in

OWNER
ARCHITECTS

For MAHIMA REAL ESTATE PVT LTD
Auth Signatory

Ar. Puneet Dua
B. Arch.
CA/2005/35530

जयपुर विकास प्राधिकरण
समस्त बहुमंजिले भवनों एवं विशाल व्यवसायिक भवनों में आग लगने की [illegible] एवं [illegible] अग्निशमन [illegible] प्रवाहित स्थान [illegible] बिजली वाले अग्निसूचक यंत्रों को लगाया जाना आवश्यक है।

[illegible] मानचित्र का अनुमोदन किसी भी सीमा [illegible] भूमि/भूखण्ड के प्रति स्वामित्व का प्रमाण-पत्र नहीं माना जायेगा और [illegible] [illegible] प्रमाणित होंगे। [illegible] किये गये अनुमोदित मानचित्रों [illegible] पर्यं भवन निर्माण का [illegible] (STRUCTURE) का दायित्व [illegible] का होगा।

[illegible] से बड़े व्यावसायिक/[illegible] [illegible] निर्माणकर्ता द्वारा [illegible] मानचित्र [illegible] [illegible] प्रकार के [illegible] भवन निर्माणकर्ता [illegible] [illegible] की तिथि से [illegible] अनिवार्य होगा।

जयपुर विकास प्राधिकरण (जयपुर [illegible]) [illegible] 2000 की धारा 12 [illegible] [illegible] कार्यवाही की जायेगी।

जयपुर विकास प्राधिकरण [illegible] [illegible] 2000 की धारा 8.15 [illegible] [illegible] कार्यवाही [illegible]

Applicant should get the construction checked at plinth level before proceeding for further construction.

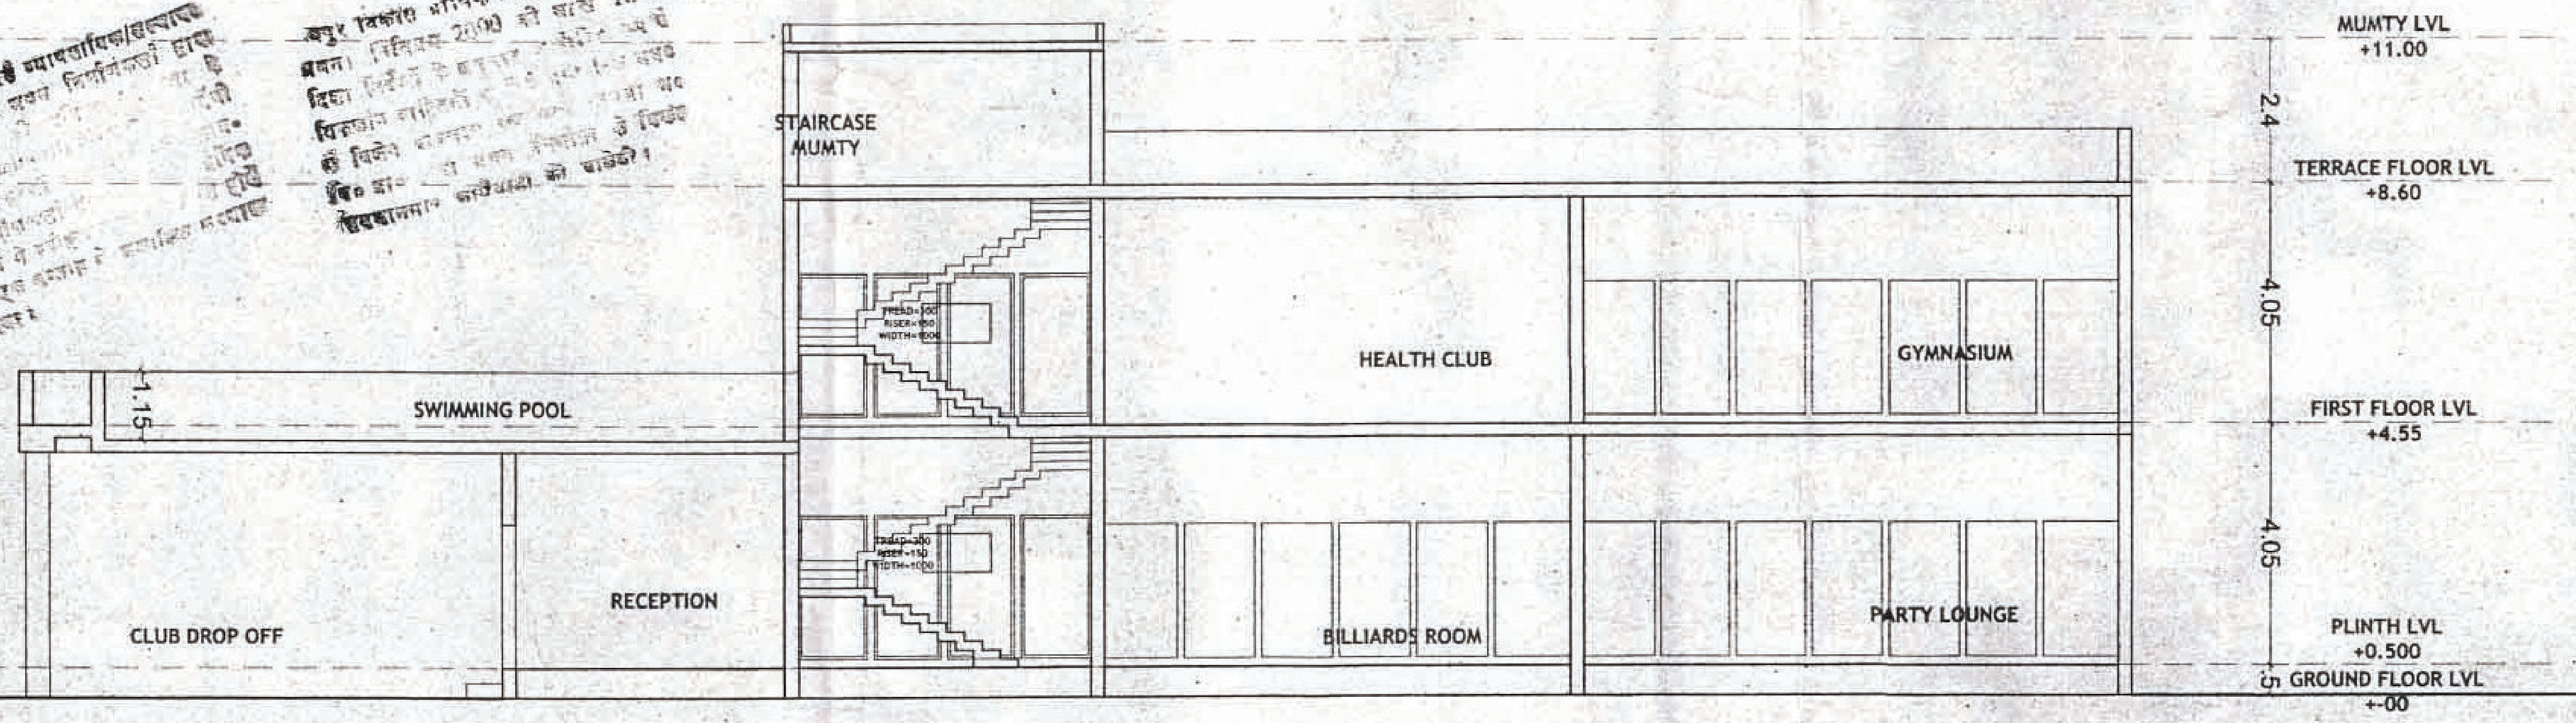
STAIRCASE MUMTY
TREAD=300
RISER=150
WIDTH=1000
SWIMMING POOL
1.15
HEALTH CLUB
GYMNASIUM
CLUB DROP OFF
RECEPTION
BILLIARDS ROOM
PARTY LOUNGE
MUMTY LVL
+11.00
2.4
TERRACE FLOOR LVL
+8.60
4.05
FIRST FLOOR LVL
+4.55
4.05
PLINTH LVL
+0.500
.5
GROUND FLOOR LVL
+-00

SECTION AA'

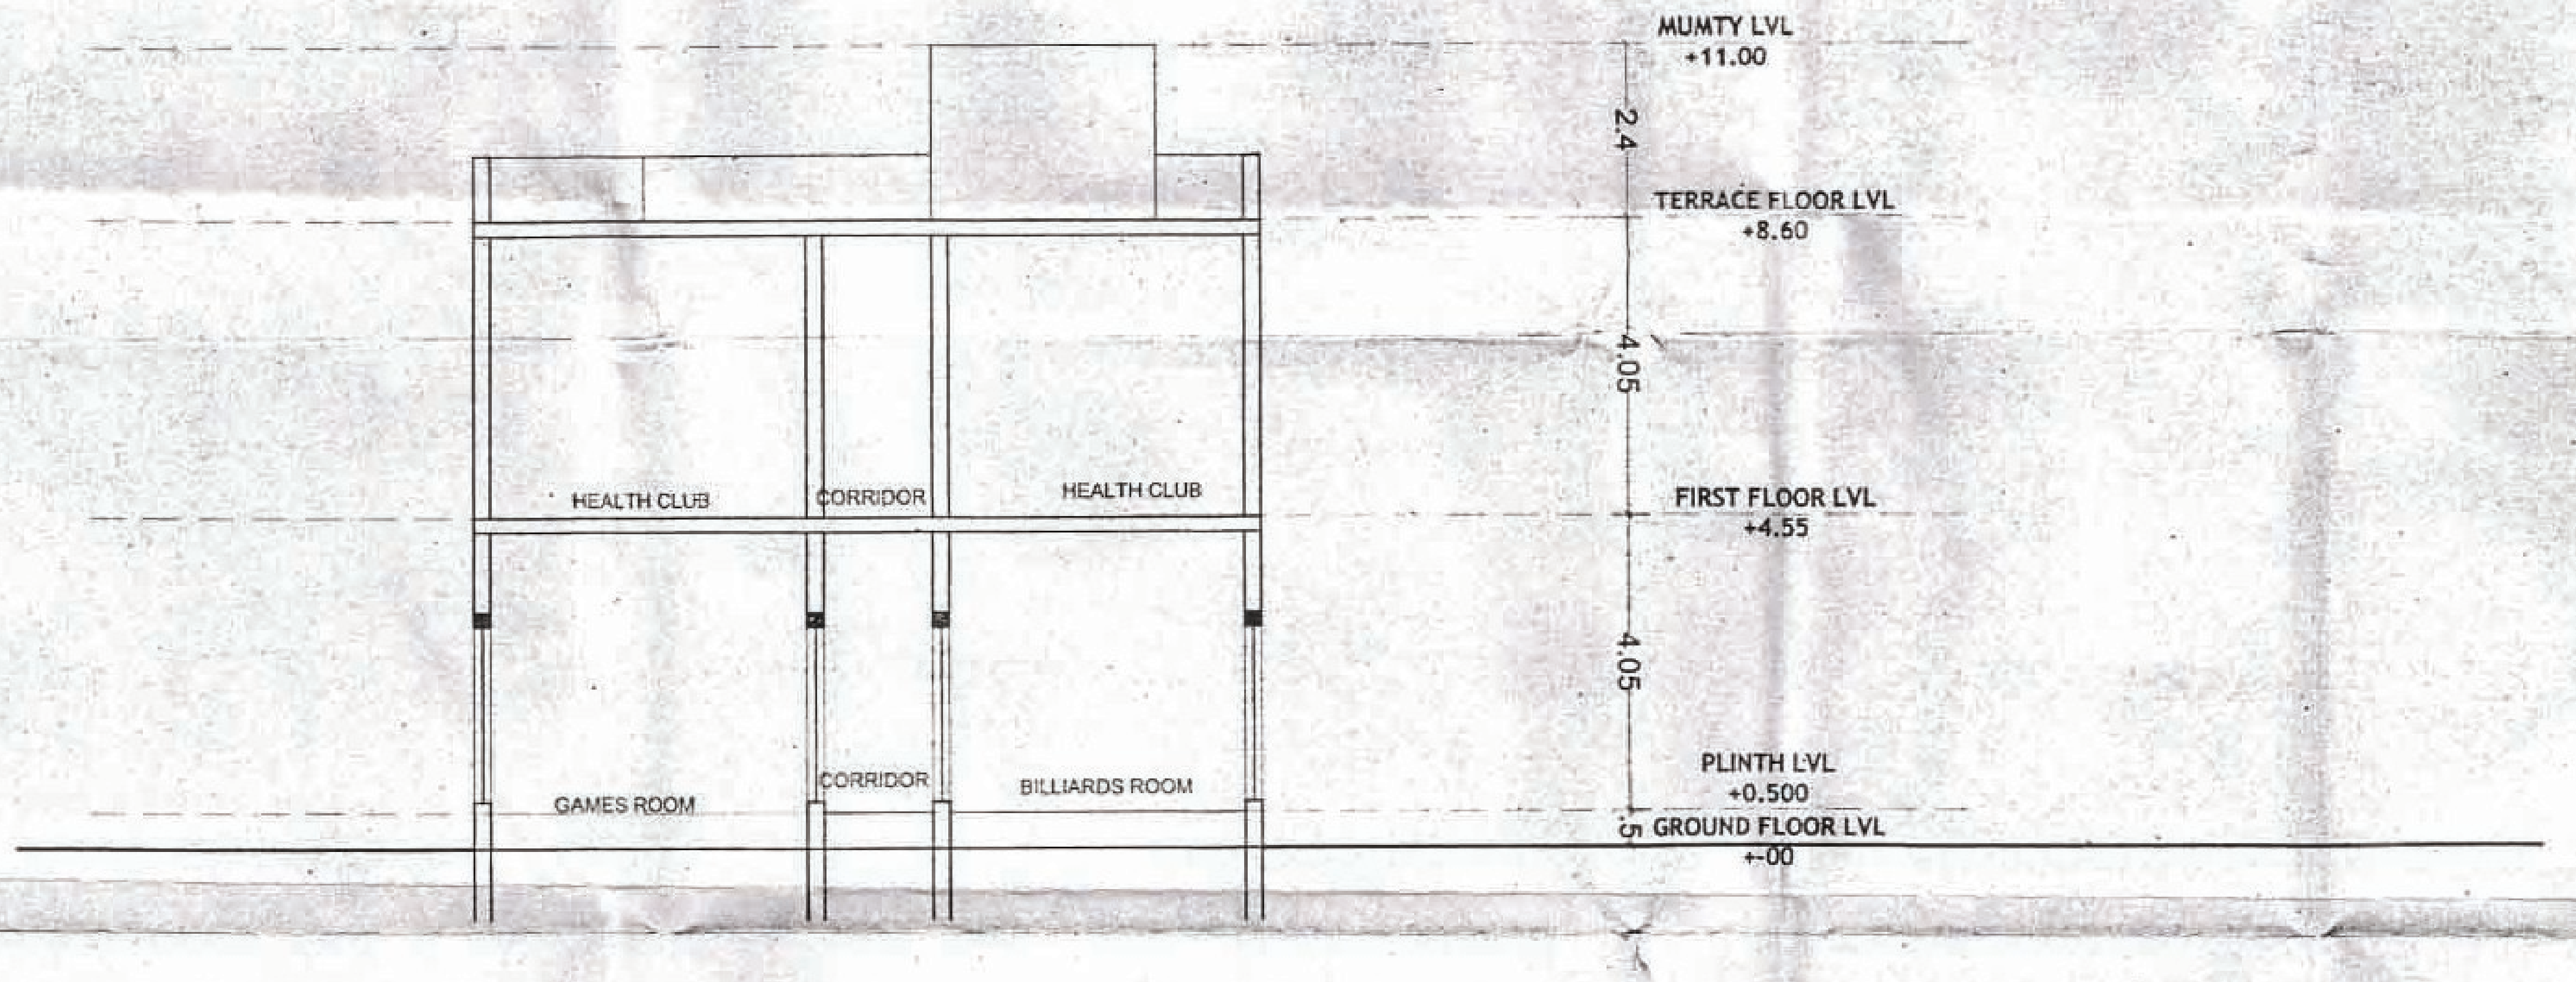
MUMTY LVL
+11.00
2.4
TERRACE FLOOR LVL
+8.60
4.05
HEALTH CLUB
CORRIDOR
HEALTH CLUB
FIRST FLOOR LVL
+4.55
4.05
GAMES ROOM
CORRIDOR
BILLIARDS ROOM
PLINTH LVL
+0.500
.5
GROUND FLOOR LVL
+-00

SECTION BB'

SHEET NO.10

TITLE:-
CLUB HOUSE SECTIONS

भवन मानचित्र समिति (बी.पी.) की 164 वीं बैठक दिनांक 12/9/2014 में लिये गये निर्णय की अनुपालना में भवन मानचित्र पत्रांक [illegible]/ स.स./[illegible] (बीपी)/डी-1270 दिनांक 26/5/2015 द्वारा अनुमोदित कर जारी किये गये।

अनुमोदित

21/5/15
[illegible] नगर नियोजक
जयपुर विकास प्राधिकरण
जयपुर

[illegible] सदस्य सचिव [illegible] बी0 पी0 सी0
जयपुर विकास प्राधिकरण
जयपुर
[illegible]5/15

TITLE:-
SUBMISSION DRAWINGS
CLUB HOUSE SECTIONS

SCALE:- 1= 100
DATE : 10-06-2014

NORTH :
N W E S

PROJECT:- MAHIMA BELLEVUE
PROPOSED APARTMENTS
AT KHASARA NO.- 4760/3345,4776/3346,
4775/3345,4777/3346
REVENUE VILLAGE,KHO-NAGORIYAN,
TEH. SANGANER
JAIPUR (RAJ.)

ARCHITECTS:-
m|a| architects pvt. ltd.
Jaipur - Bangalore - Hyderabad
Plot No. -1, greenwood, Lal Kothi Scheme
Sahkar Marg Jaipur-302001
Tel : 91-141-4299999
email- studio@maarchitects.in web- www.maarchitects.in

OWNER
ARCHITECTS

For MAHIMA REAL ESTATE PVT LTD
Auth. Signatory

Ar. Puneet Dua
B. Arch.
CA/2005/35530