



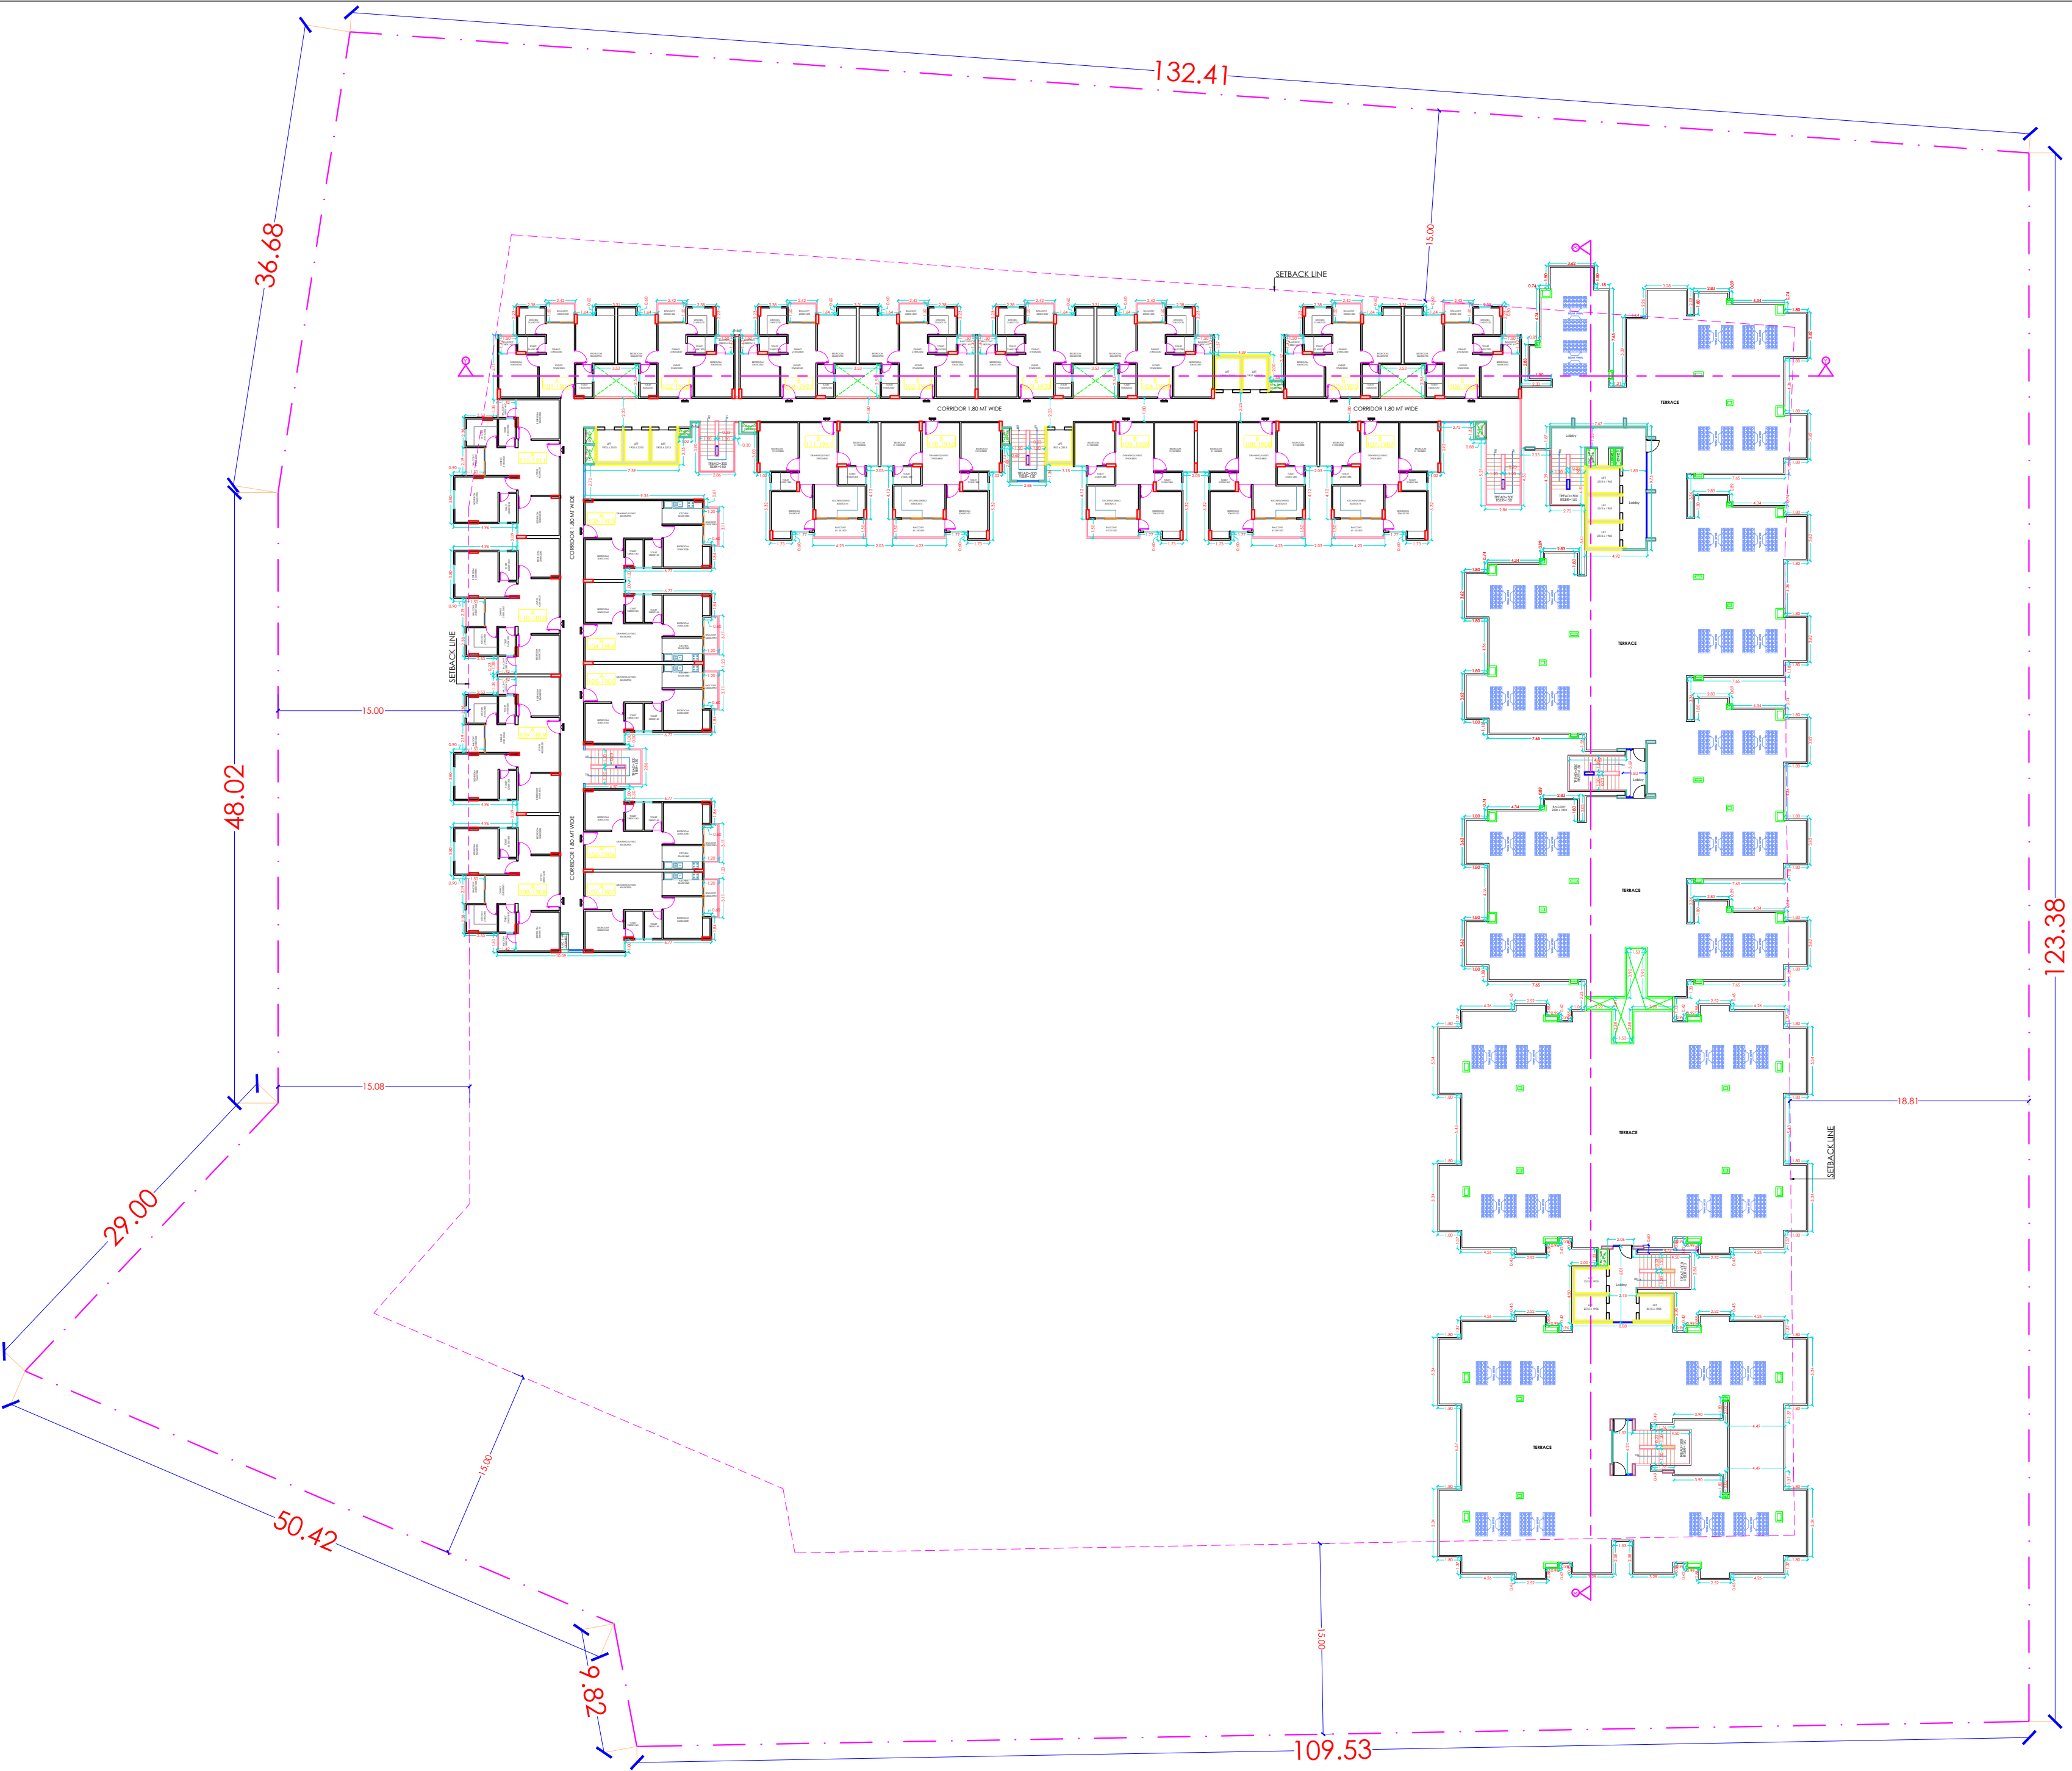


|   |                   |
|---|-------------------|
| SHEET NO. - 06   |                   |
| DRAWING TITLE -   |                   |
| 15th FLOOR PLAN   |                   |
| PROJECT TITLE -   |                   |
| PROPOSED GROUP HOUSING<br>KHASRA NO. 240,241,246<br>AT VILLAGE SUKHIYA<br>TEH.-SANGANER, JAIPUR   |                   |
| FOR ABHINANDAN PROJECTS PVT. LTD.   |                   |
| ARCHITECT:-   |                   |
| ricky mathur & associates<br>architects interior designers planners<br>33, Dhulestwar Garden,<br>Jaipur, (RAJ.) India, 302 001<br>Tel: 91-141-2362688, 5125444<br>Fax: 91-141-4008700<br>e-mail: ricky@rickymathur.com |                   |
| DRAWING TITLE:-   |                   |
| 15th FLOOR PLAN   |                   |
| SCALE 1:150   | DATE AUG_22_2016  |
| DEALT BY.....   | STATUS SUBMISSION |
| CLIENT'S SIGN.   | ARCHITECT'S SIGN. |
| SHEET NO. - 06   | NORTH -           |

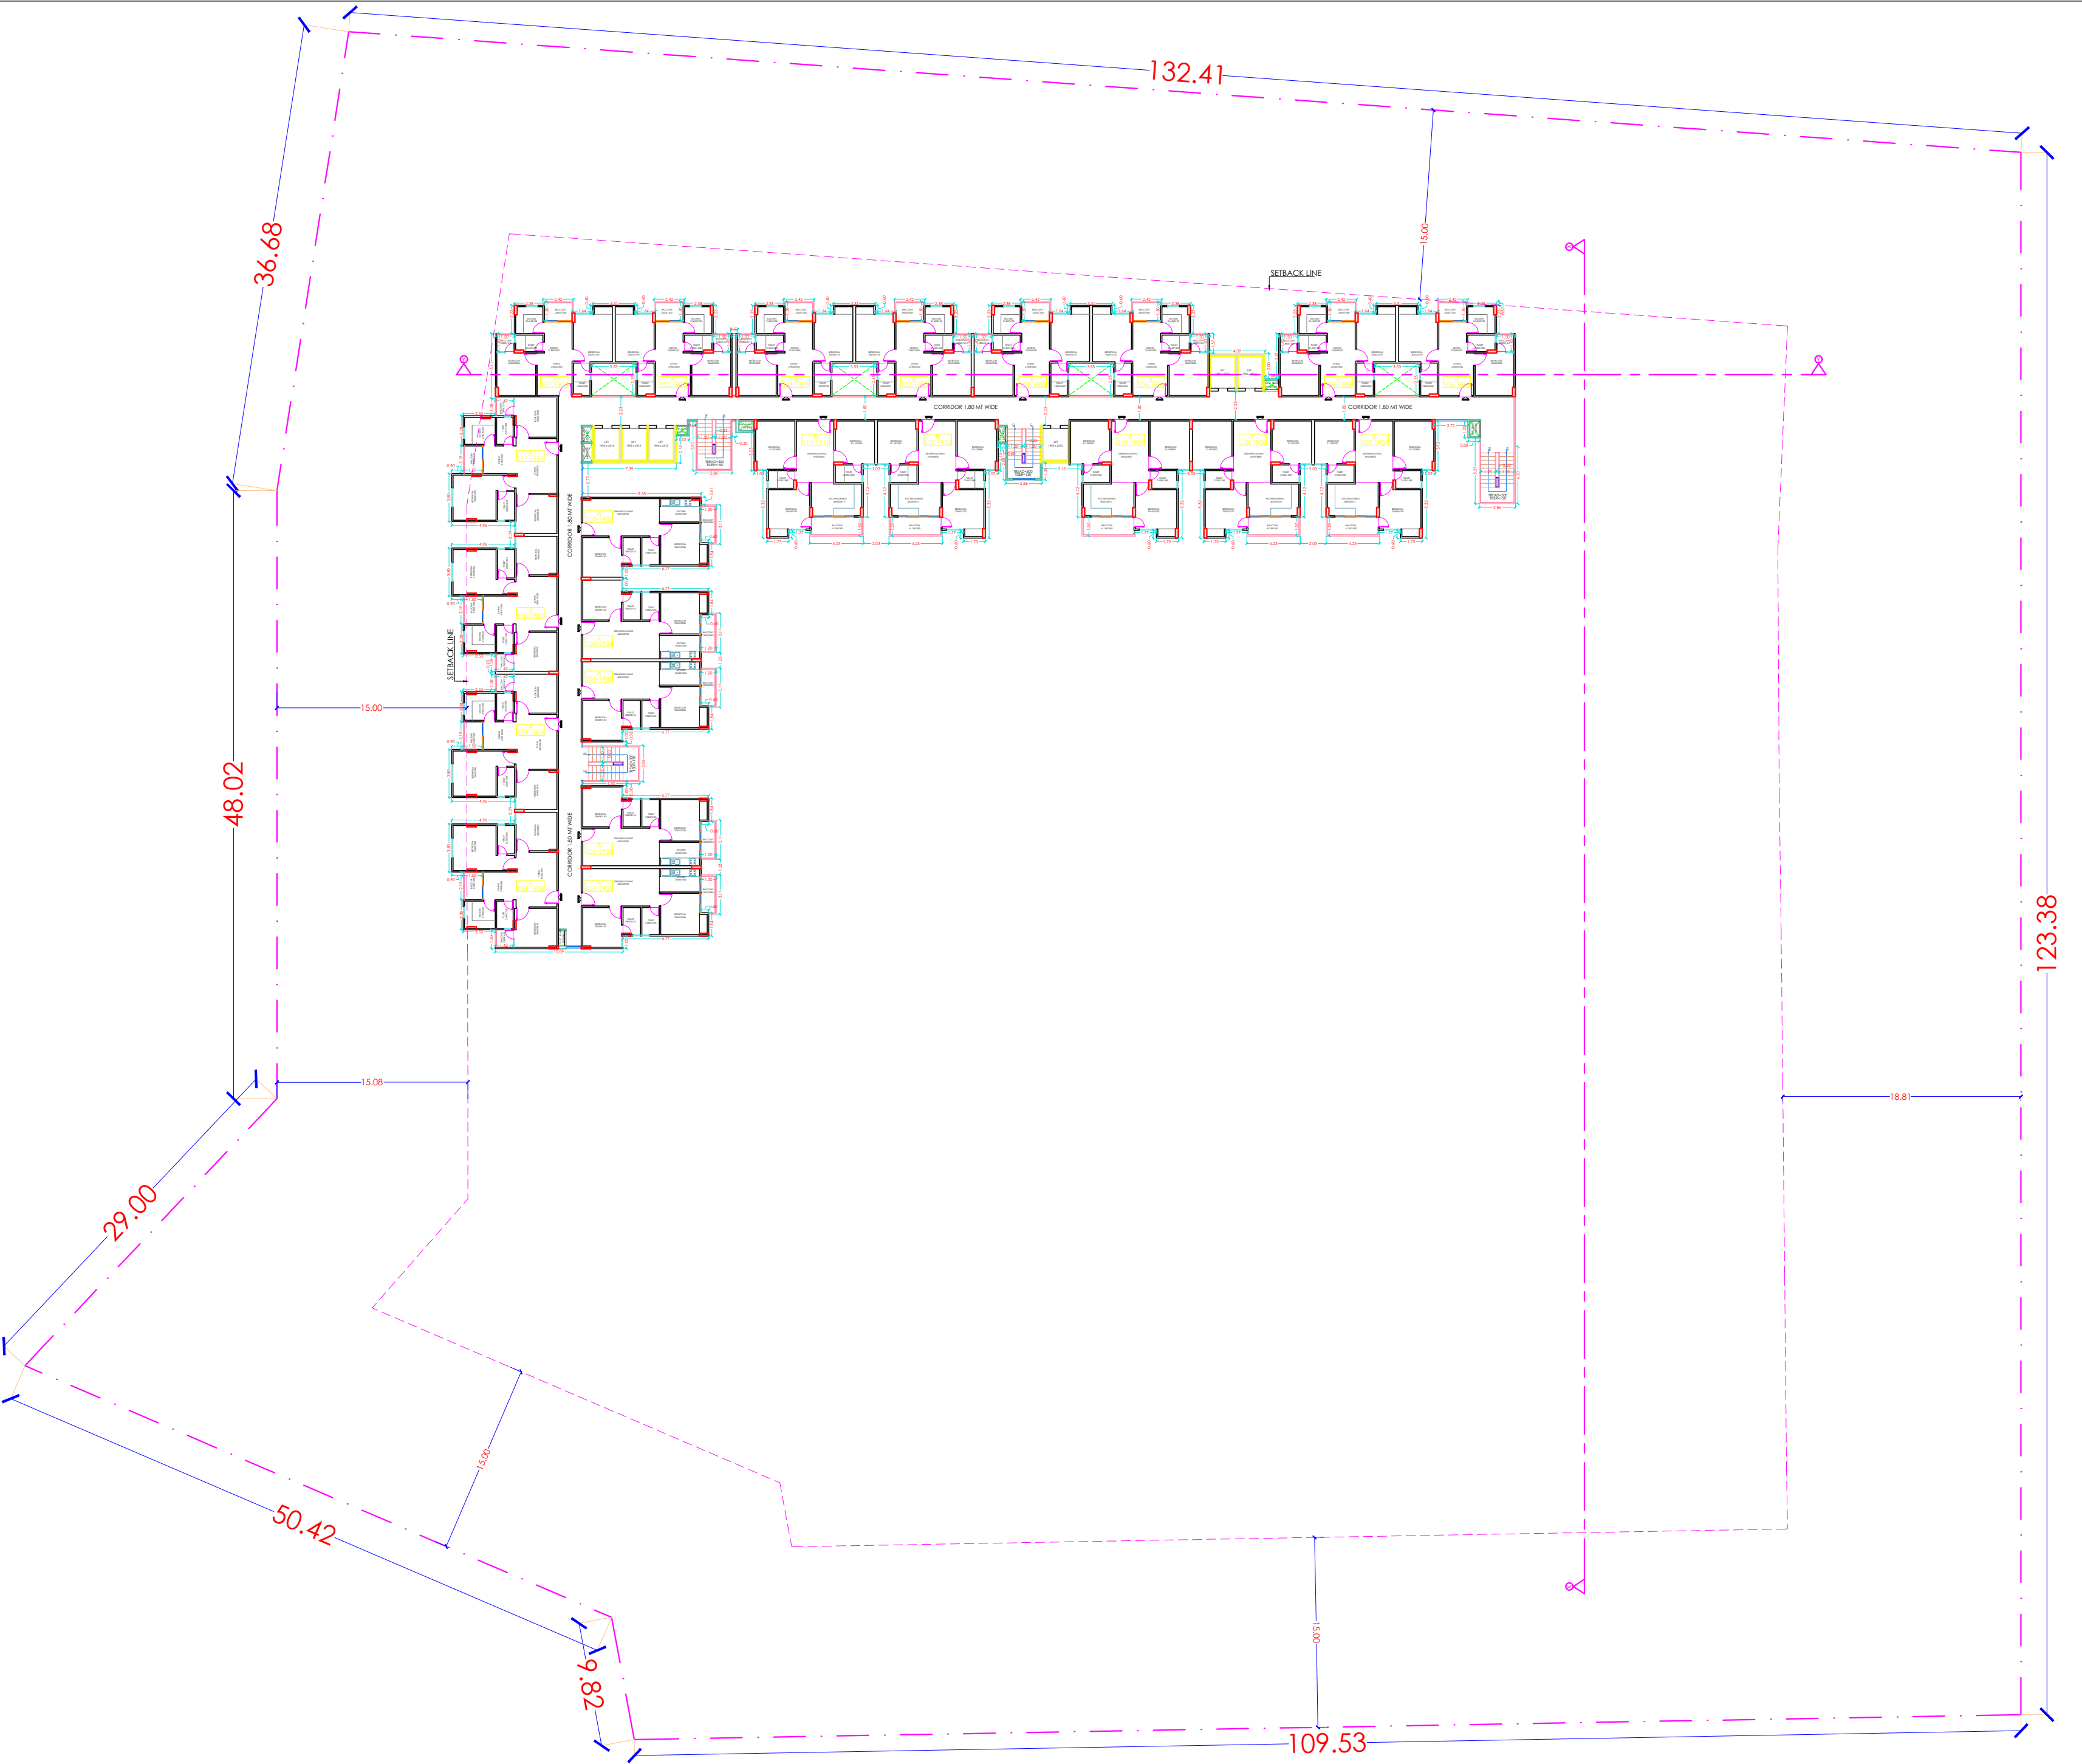

|   |                   |
|---|-------------------|
| SHEET NO. - 07   |                   |
| DRAWING TITLE -   |                   |
| 16th to 18th FLOOR PLAN   |                   |
| PROJECT TITLE -   |                   |
| PROPOSED GROUP HOUSING<br>KHASRA NO. 240,241,246<br>AT VILLAGE SUKHIYA<br>TEH.-SANGANER, JAIPUR   |                   |
| ARCHITECT -   |                   |
| ricky mathur & associates<br>architects interior designers planners<br>33, Dhulestwar Garden,<br>Jaipur, (RAJ.) India, 302 001<br>Tel: 91-141-2362688, 5125444<br>Fax: 91-141-4008700<br>e-mail: ricky@rickymathur.com |                   |
| DRAWING TITLE -   |                   |
| 16th to 18th FLOOR PLAN   |                   |
| SCALE 1:150   | DATE AUG_22_2016  |
| DEALT BY.....   | STATUS SUBMISSION |
| CLIENT'S SIGN.   | ARCHITECT'S SIGN. |
| SHEET NO. - 07   | NORTH -           |





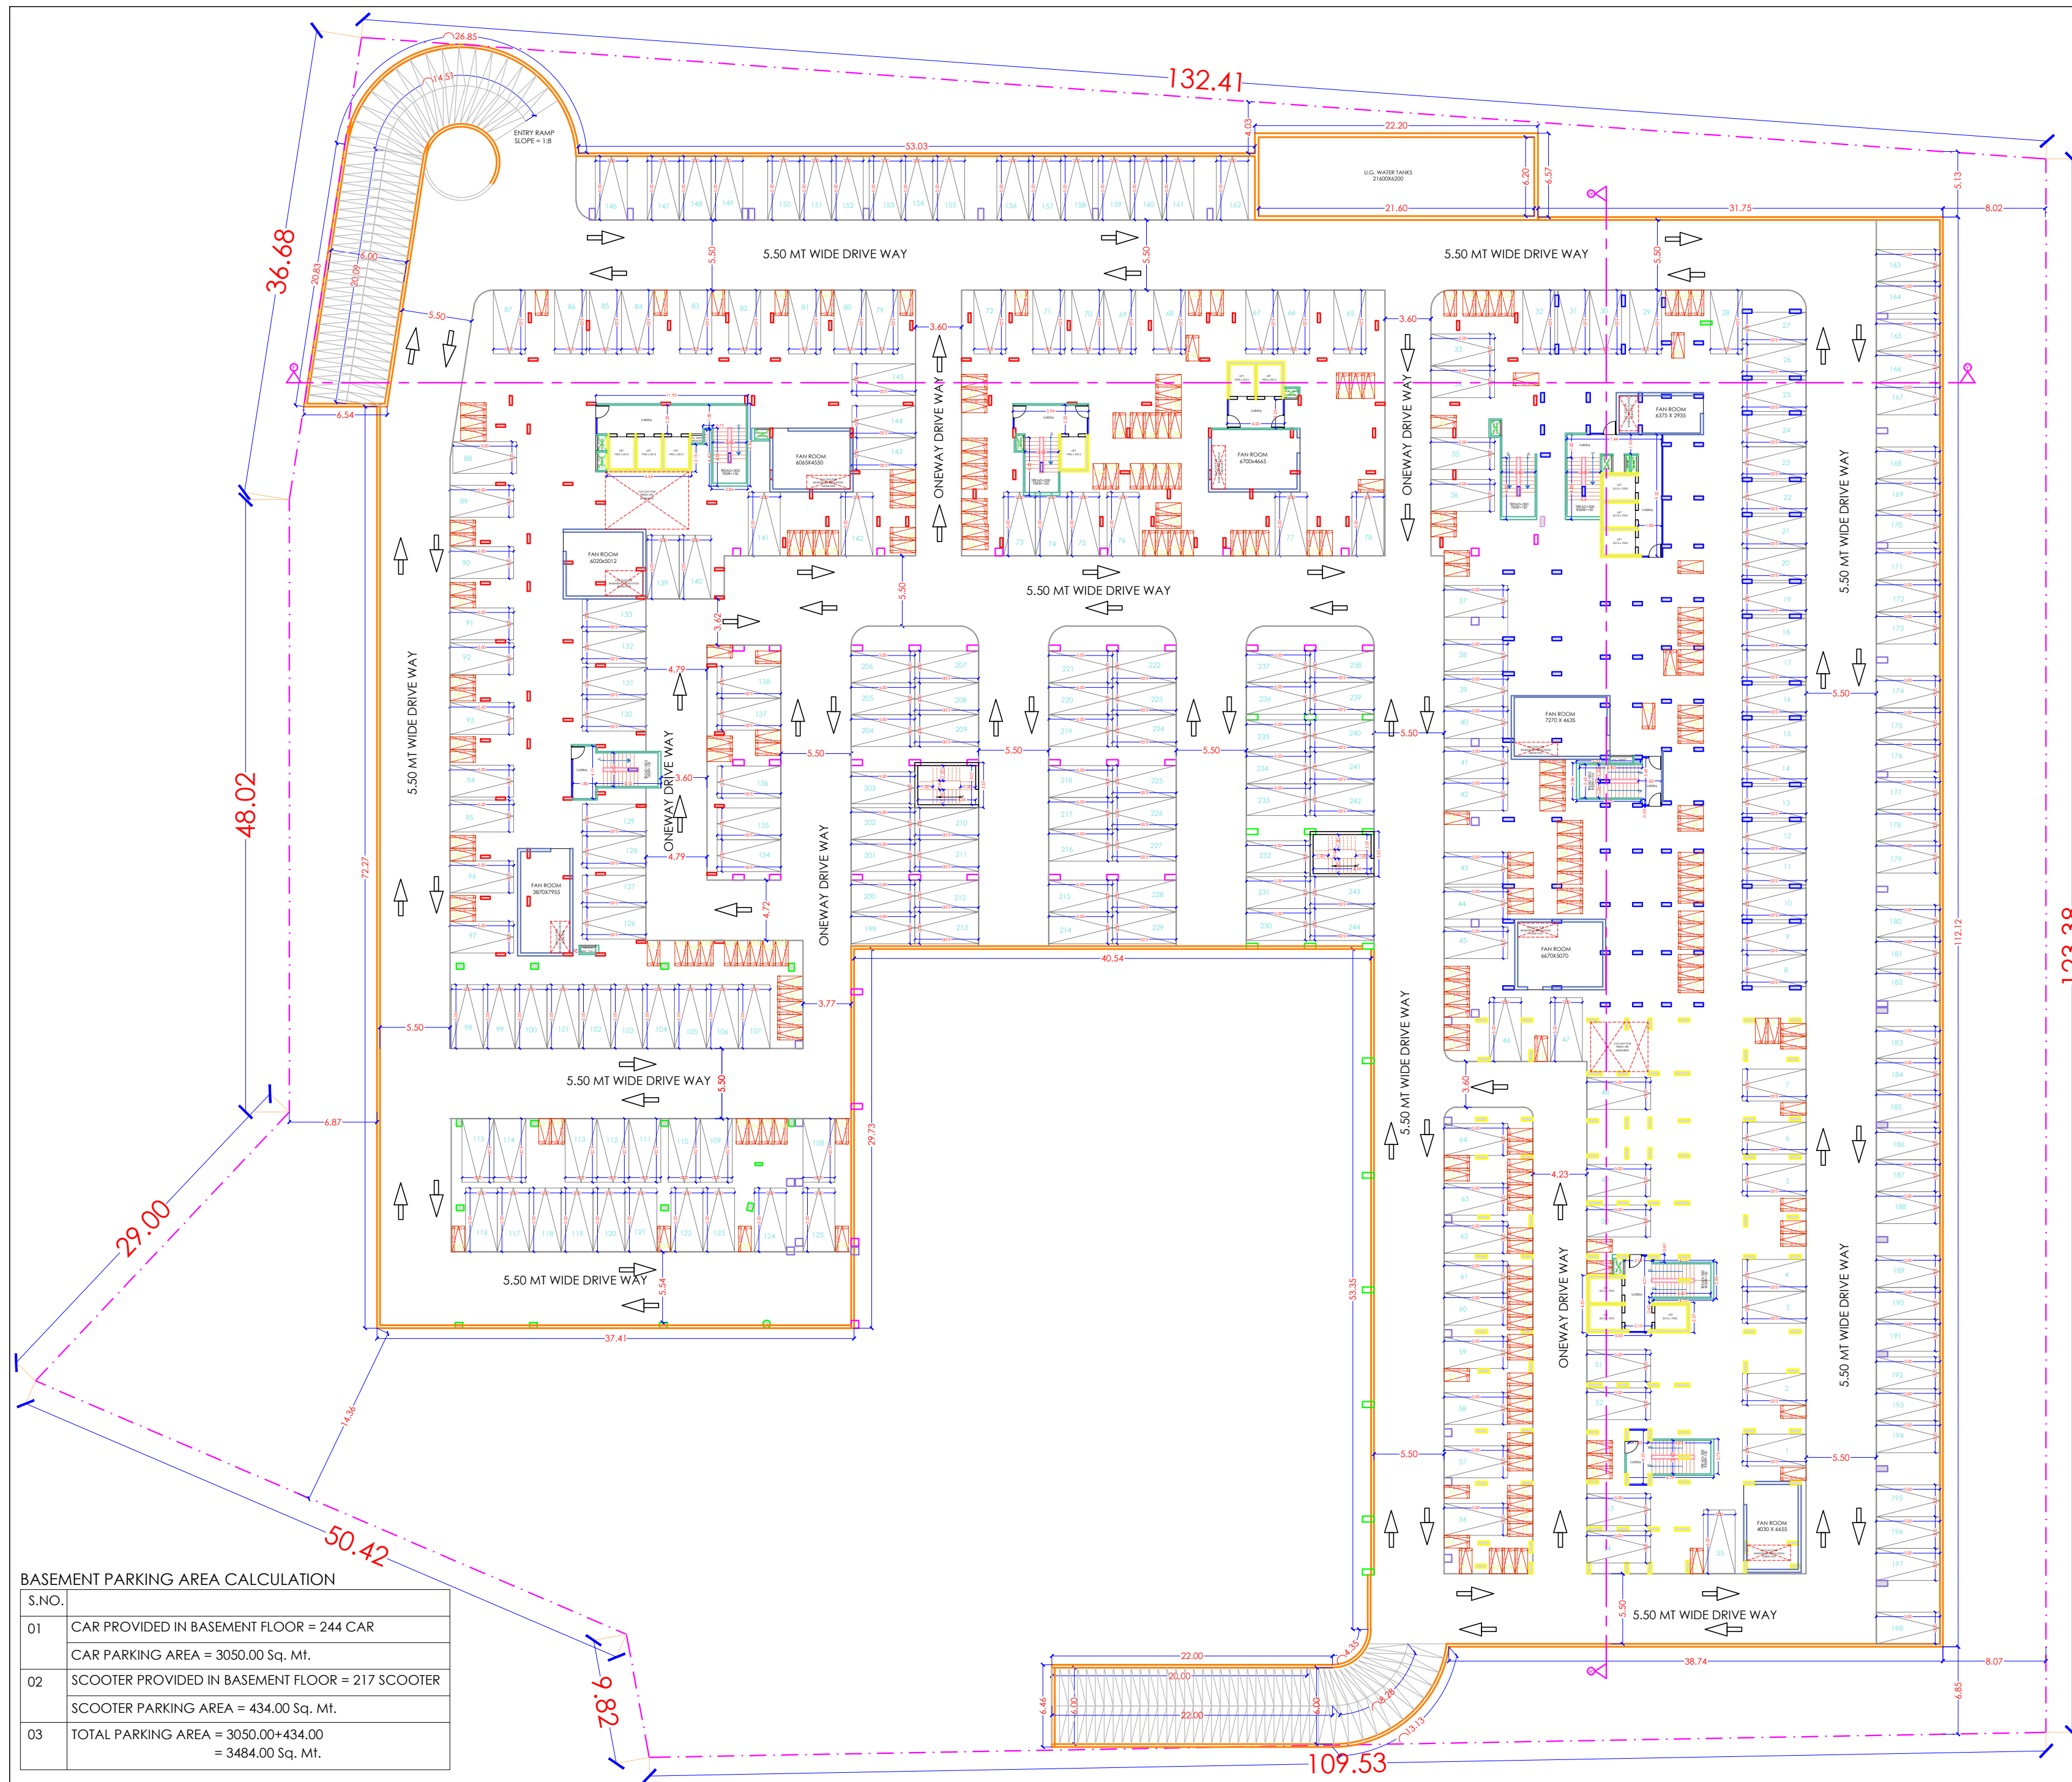

| BASEMENT PARKING AREA CALCULATION |                                                                                           |
|-----------------------------------|-------------------------------------------------------------------------------------------|
| S.NO.                             |                                                                                           |
| 01                                | CAR PROVIDED IN BASEMENT FLOOR = 244 CAR<br>CAR PARKING AREA = 3050.00 Sq. Mt.            |
| 02                                | SCOOTER PROVIDED IN BASEMENT FLOOR = 217 SCOOTER<br>SCOOTER PARKING AREA = 434.00 Sq. Mt. |
| 03                                | TOTAL PARKING AREA = 3050.00+434.00<br>= 3484.00 Sq. Mt.                                  |

SHEET NO. - 03

DRAWING TITLE -

BASEMENT FLOOR PLAN

PROJECT TITLE :

PROPOSED GROUP HOUSING  
KHASRA NO. 240,241,246  
AT VILLAGE SUKHIYA,  
TEH.-SANGANER, JAIPUR

FOR ABHINANDAN PROJECTS PVT. LTD.

ARCHITECT:-

**ricky mathur & associates**  
architects interior designers planners  
33, Dhuleshwar Garden,  
Jaipur, (RAJ.) India. 302 001  
Tel: 91-141-2362688, 5125444  
Fax: 91-141-4008700  
e-mail: ricky@rickymathur.com

DRAWING TITLE :-

BASEMENT FLOOR PLAN

SCALE 1 : 150

DATE AUG\_22\_2016

DEALT BY.....

STATUS SUBMISSION







CLIENT'S SIGN.

ARCHITECT'S SIGN.

SHEET NO. - 03

NORTH -



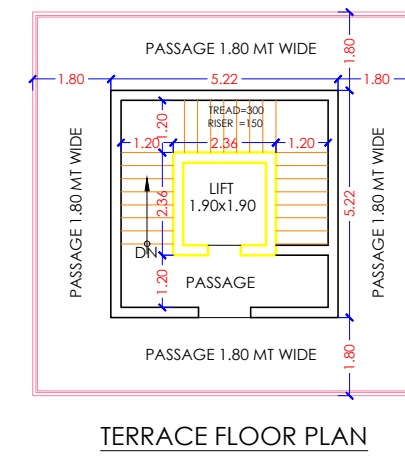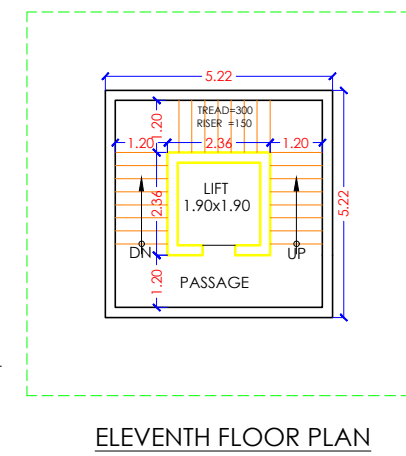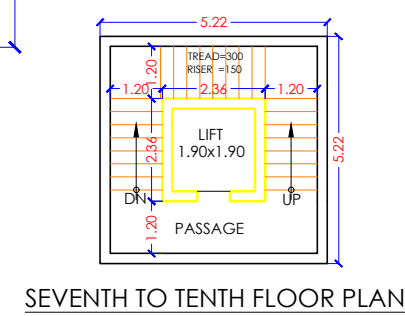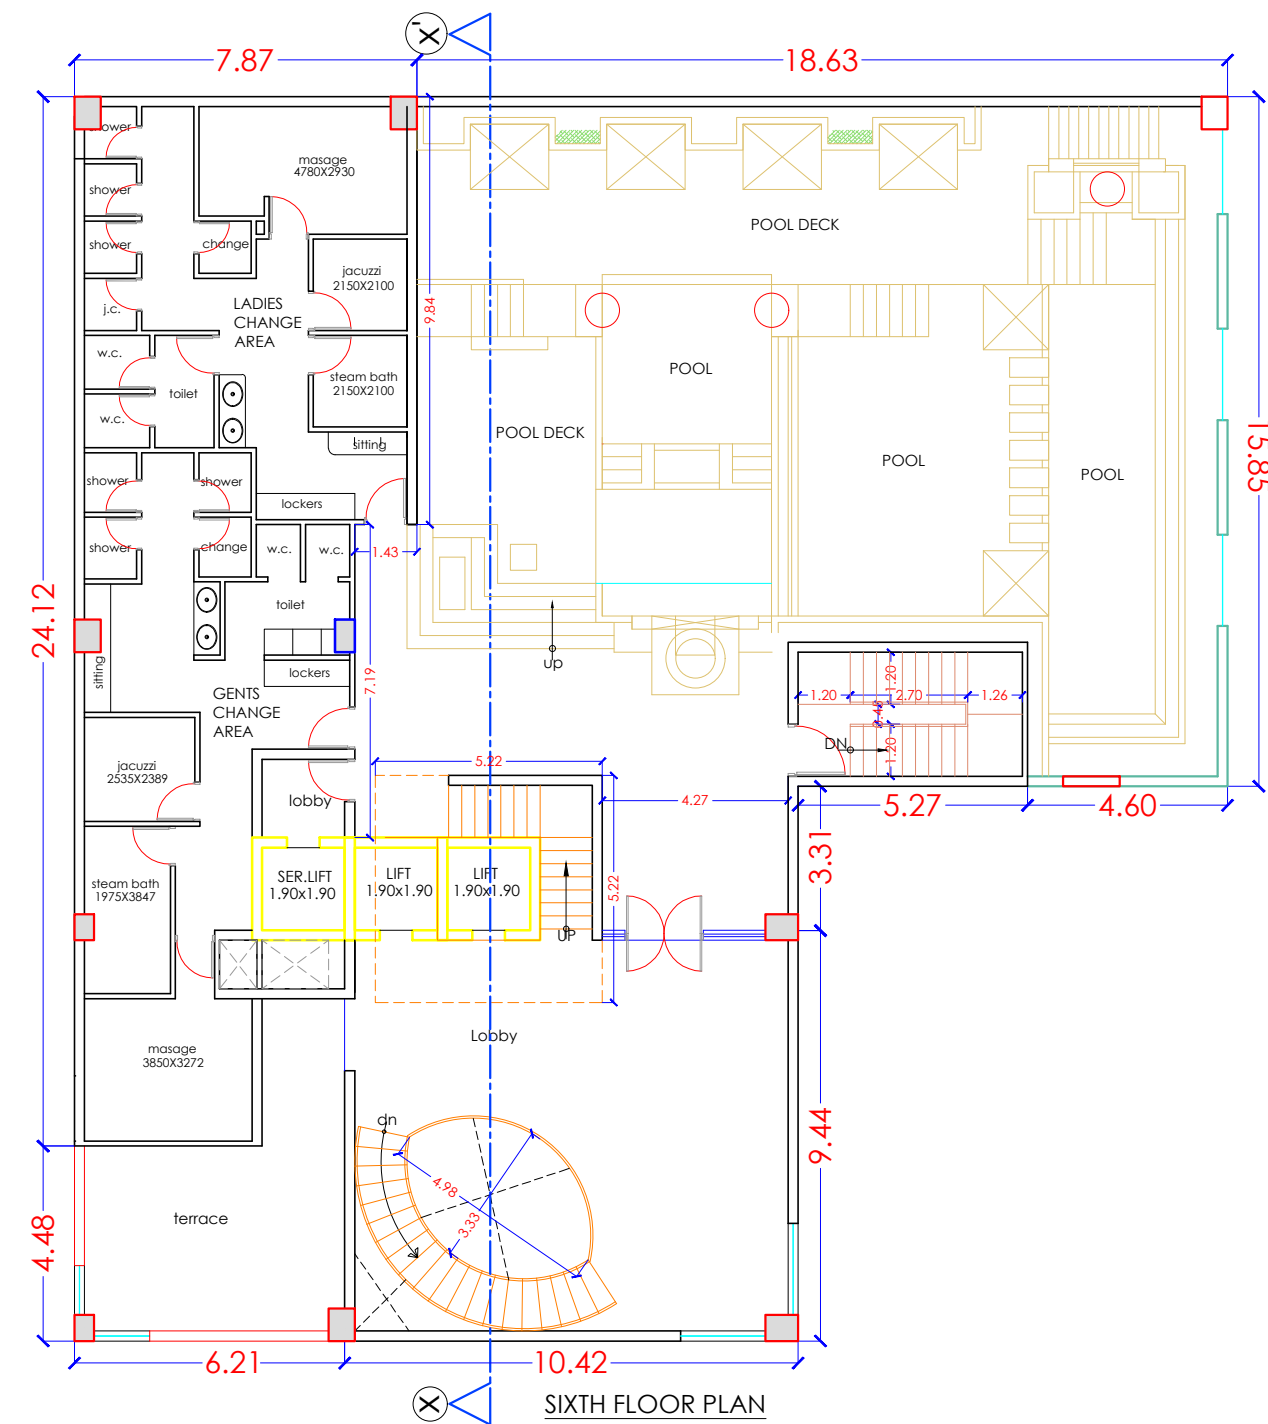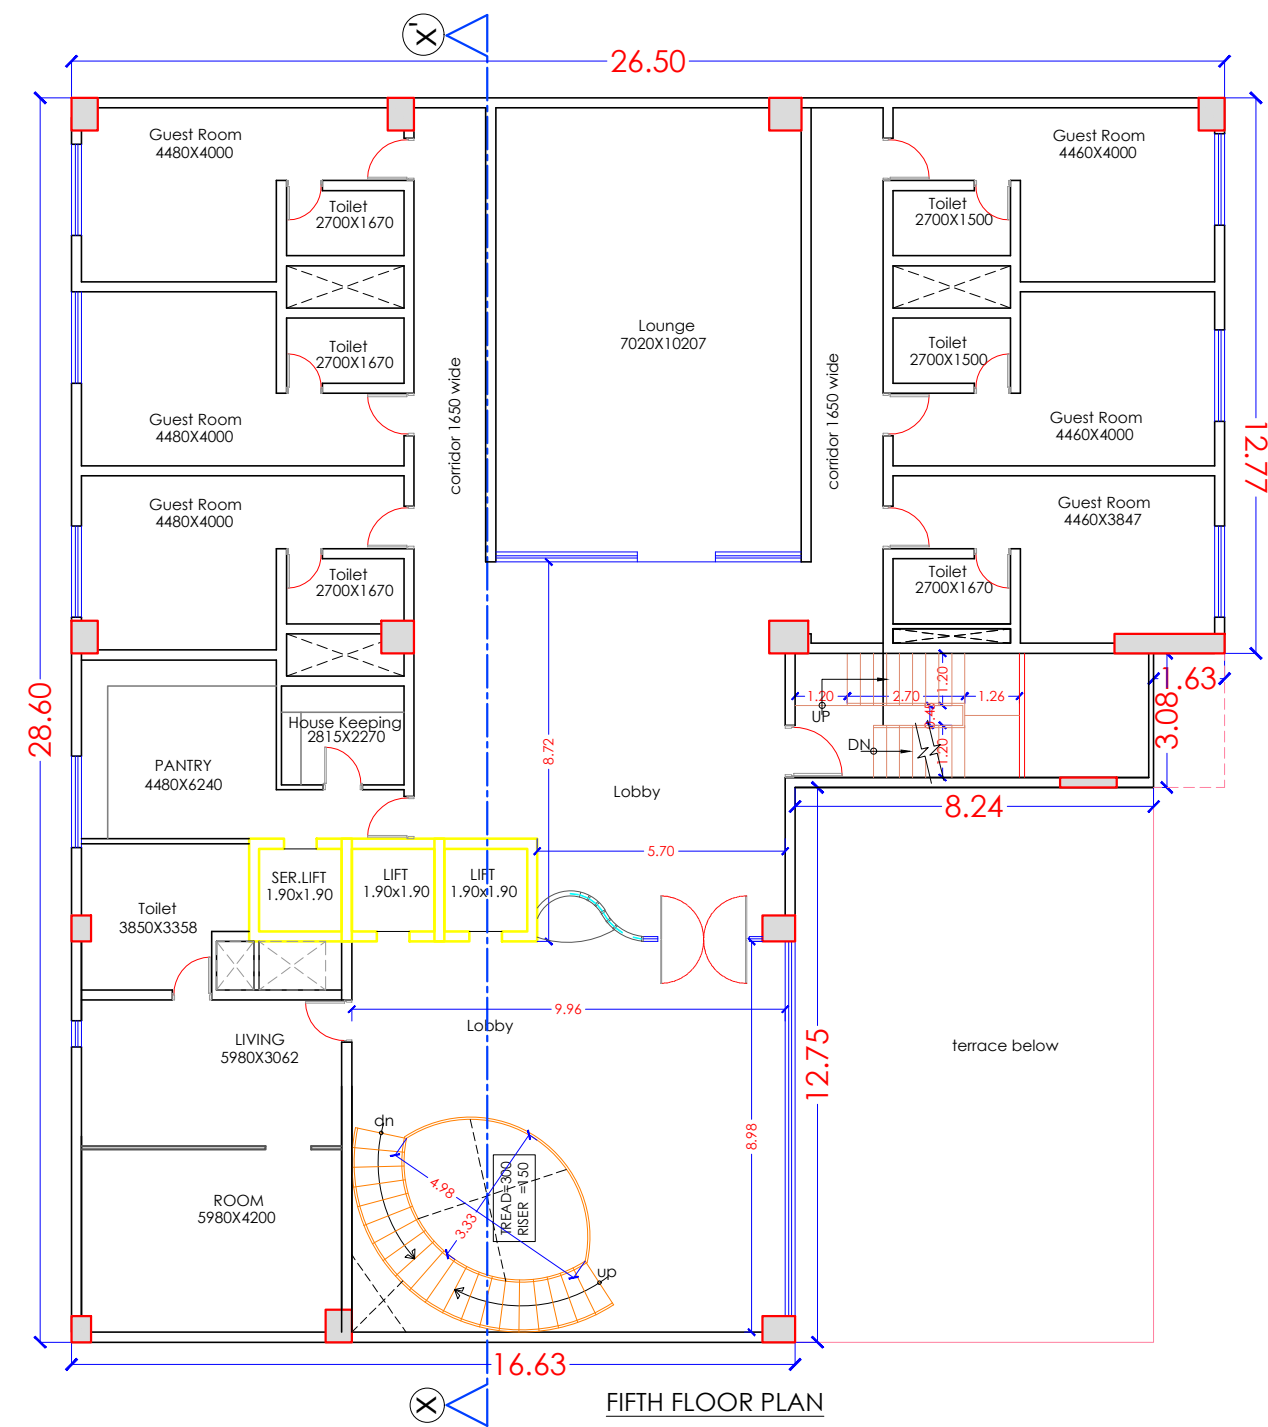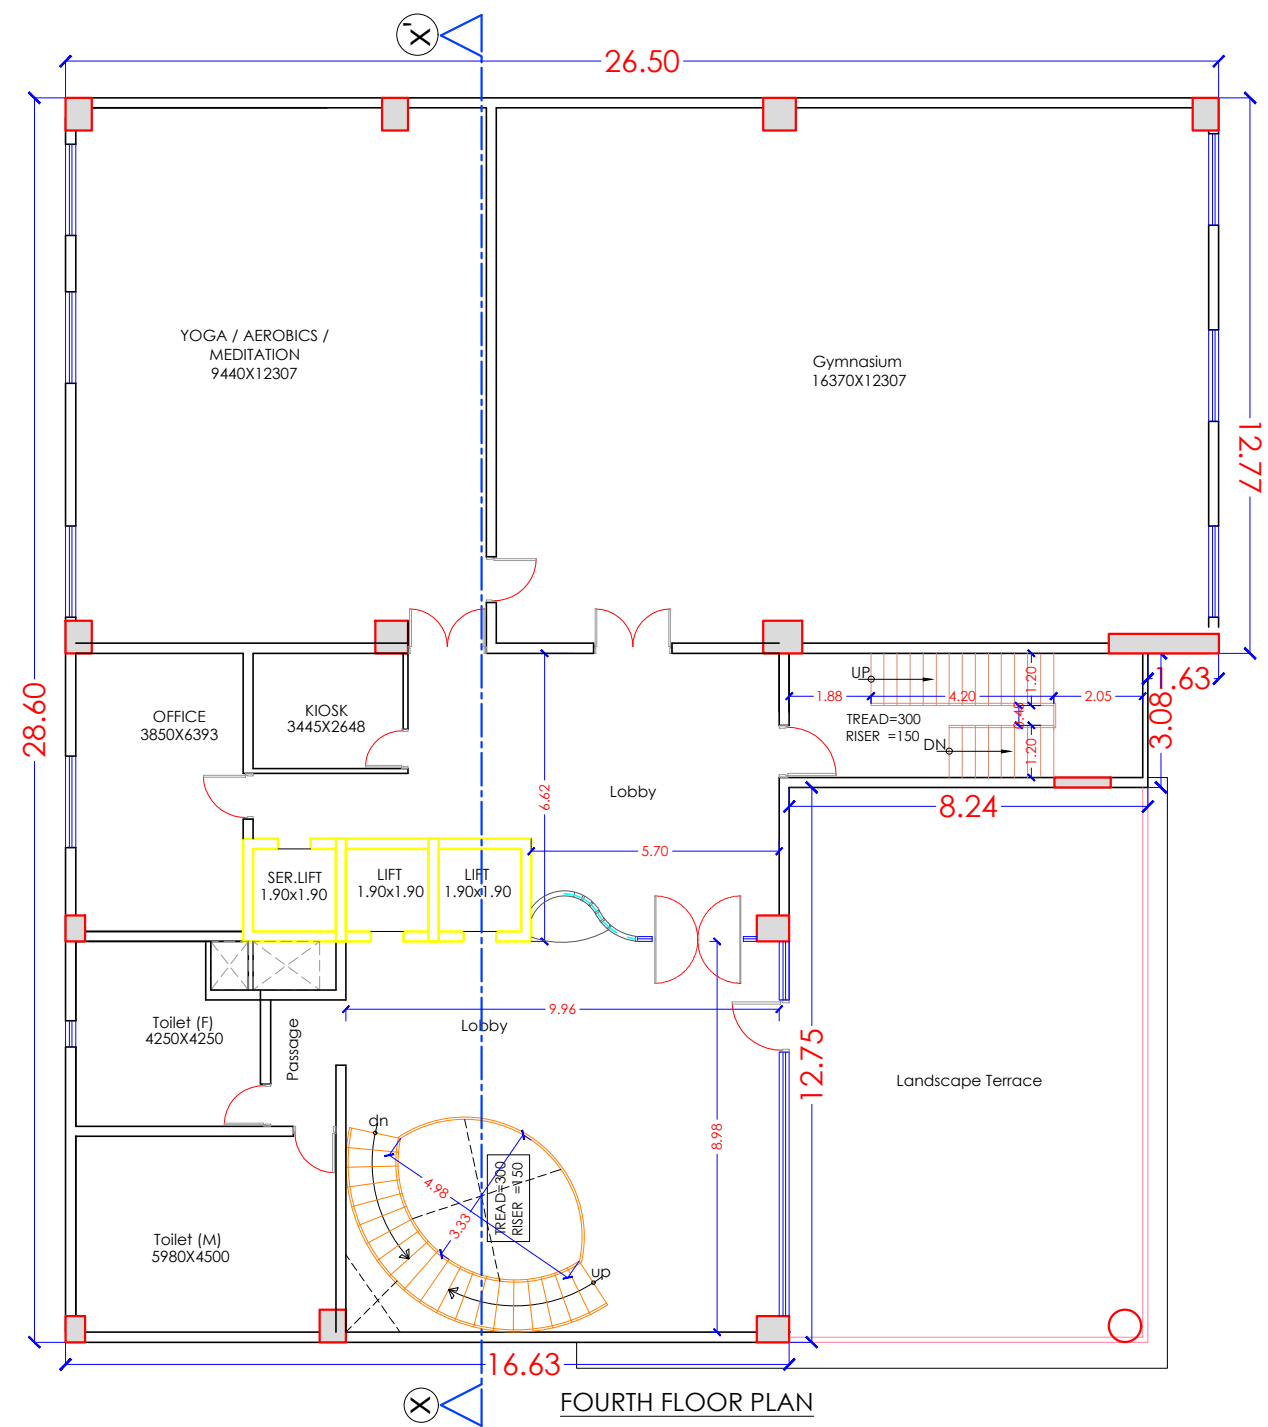

| CLUB AREA CALCULATION |               |                    |                      |
|-----------------------|---------------|--------------------|----------------------|
| S.No.                 | FLOOR         | B.U.A.<br>(SQ.MT.) | G.B.U.A.<br>(SQ.MT.) |
| 1                     | GROUND FLR.   | 276.03             | 276.03               |
| 2                     | FIRST FLR.    | 686.72             | 686.72               |
| 3                     | SECOND FLR.   | 721.63             | 721.63               |
| 4                     | THIRD FLR.    | 621.79             | 621.79               |
| 5                     | FOURTH FLR.   | 615.07             | 615.07               |
| 6                     | FIFTH FLR.    | 615.07             | 615.07               |
| 7                     | SIXTH FLR.    | 281.6              | 281.6                |
| 8                     | SEVENTH FLR.  | 27.24              | 27.24                |
| 9                     | EIGHT FLR.    | 27.24              | 27.24                |
| 10                    | NINTH FLR.    | 27.24              | 27.24                |
| 11                    | TENTH FLR.    | 27.24              | 27.24                |
| 12                    | ELEVENTH FLR. | 77.79              | 77.79                |
| 13                    | TERRACE FLR.  | 77.79              | 77.79                |
| 14                    | TOTAL         | 4082.45            | 4082.45              |

SHEET NO. - 16

DRAWING TITLE -

CLUB HOUSE FLOOR PLANS  
(FOURTH TO TERR. FLOOR)

PROJECT TITLE :

PROPOSED GROUP HOUSING  
KHASRA NO. 240,241,246  
AT VILLAGE SUKHIYA,  
TEH.-SANGANER, JAIPUR

FOR ABHINANDAN PROJECTS PVT. LTD.

ARCHITECT:-

ricky mathur & associates

architects interior designers planners

33, Dhuleshwar Garden,  
Jaipur, (RAJ.) India. 302 001  
Tel: 91-141-2362688, 5125444  
Fax: 91-141-4008700  
e-mail: ricky@rickymathur.com

DRAWING TITLE :-

CLUB HOUSE FLOOR PLANS  
(FOURTH TO TERR. FLOOR)

SCALE 1 : 100

DATE AUG\_22\_2016

DEALT BY.....





STATUS SUBMISSION

CIENT'S SIGN.

ARCHITECT'S SIGN.

SHEET NO. - 16

NORTH -

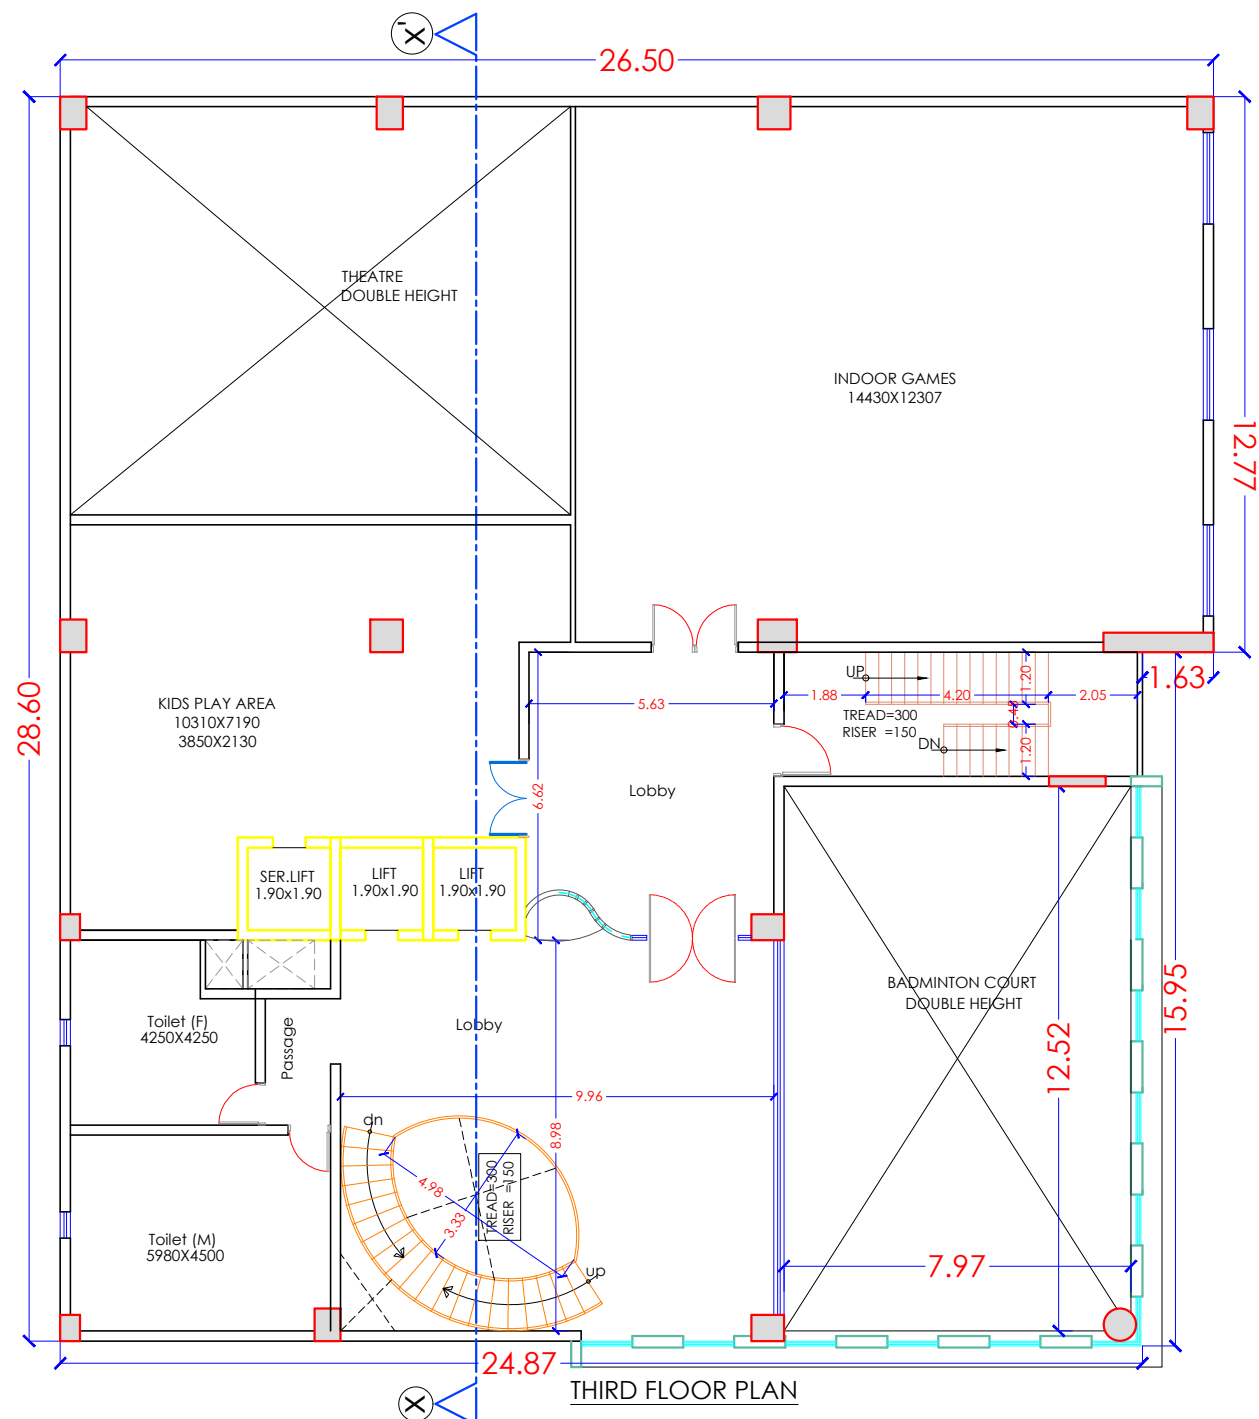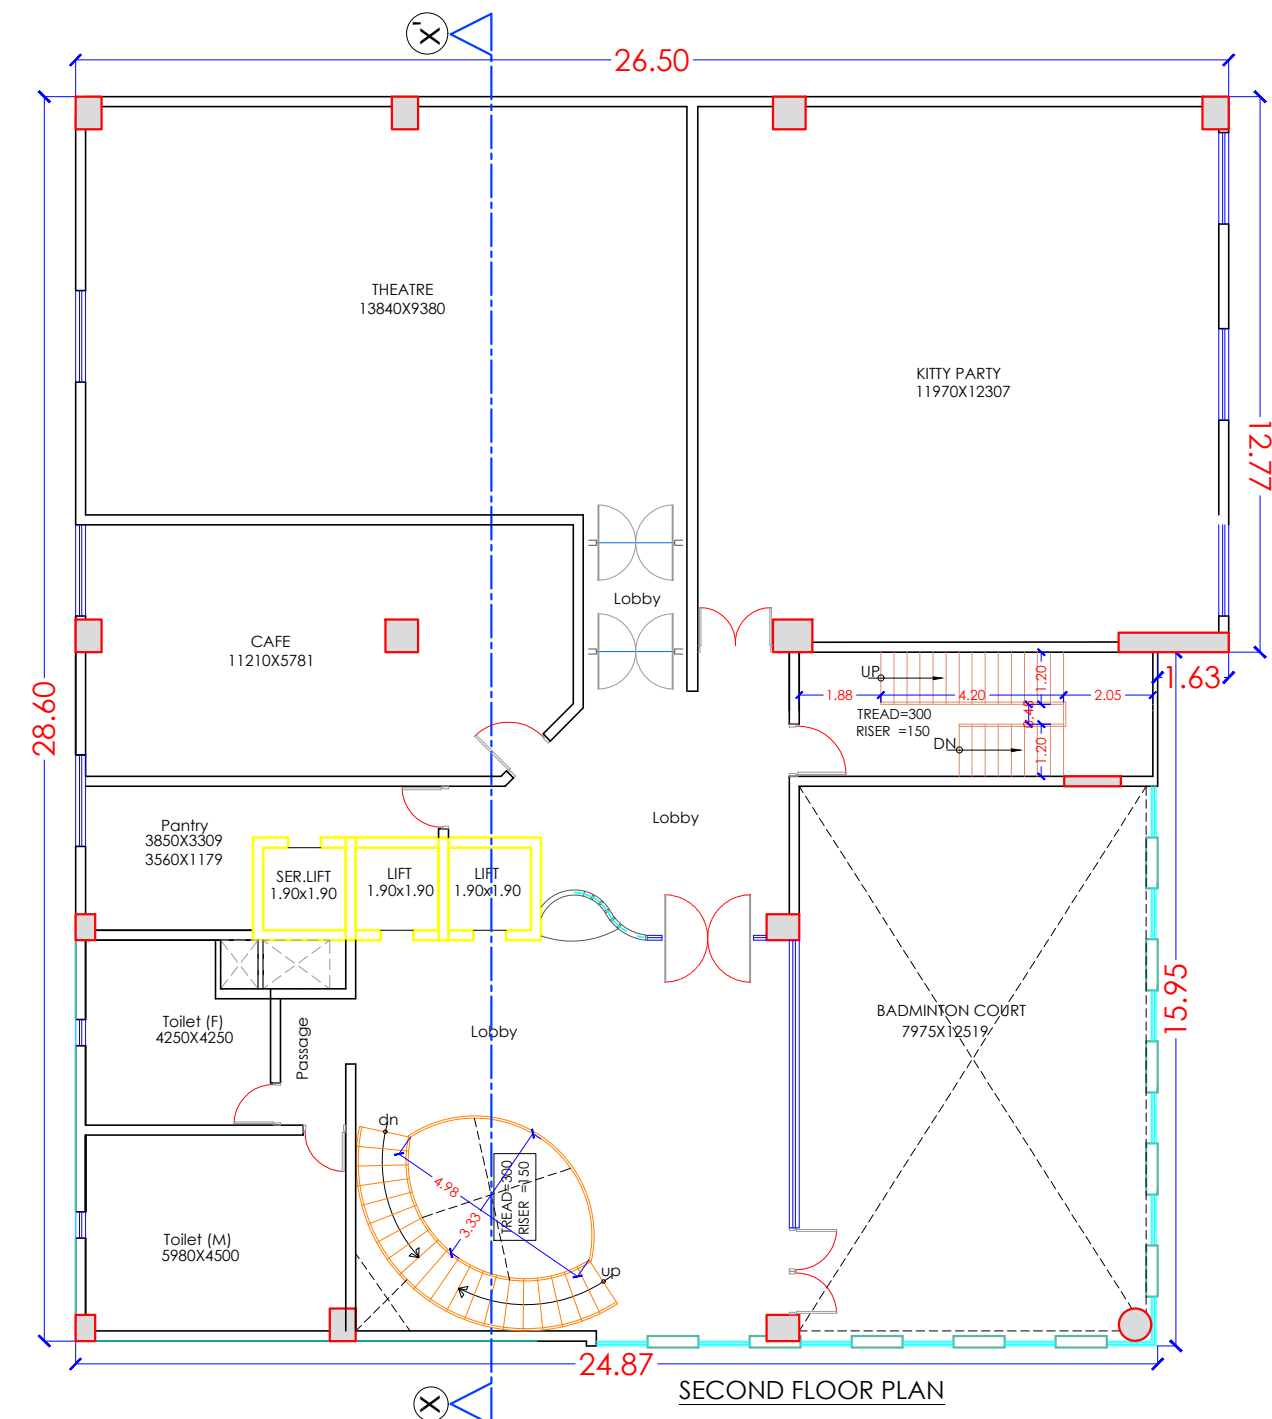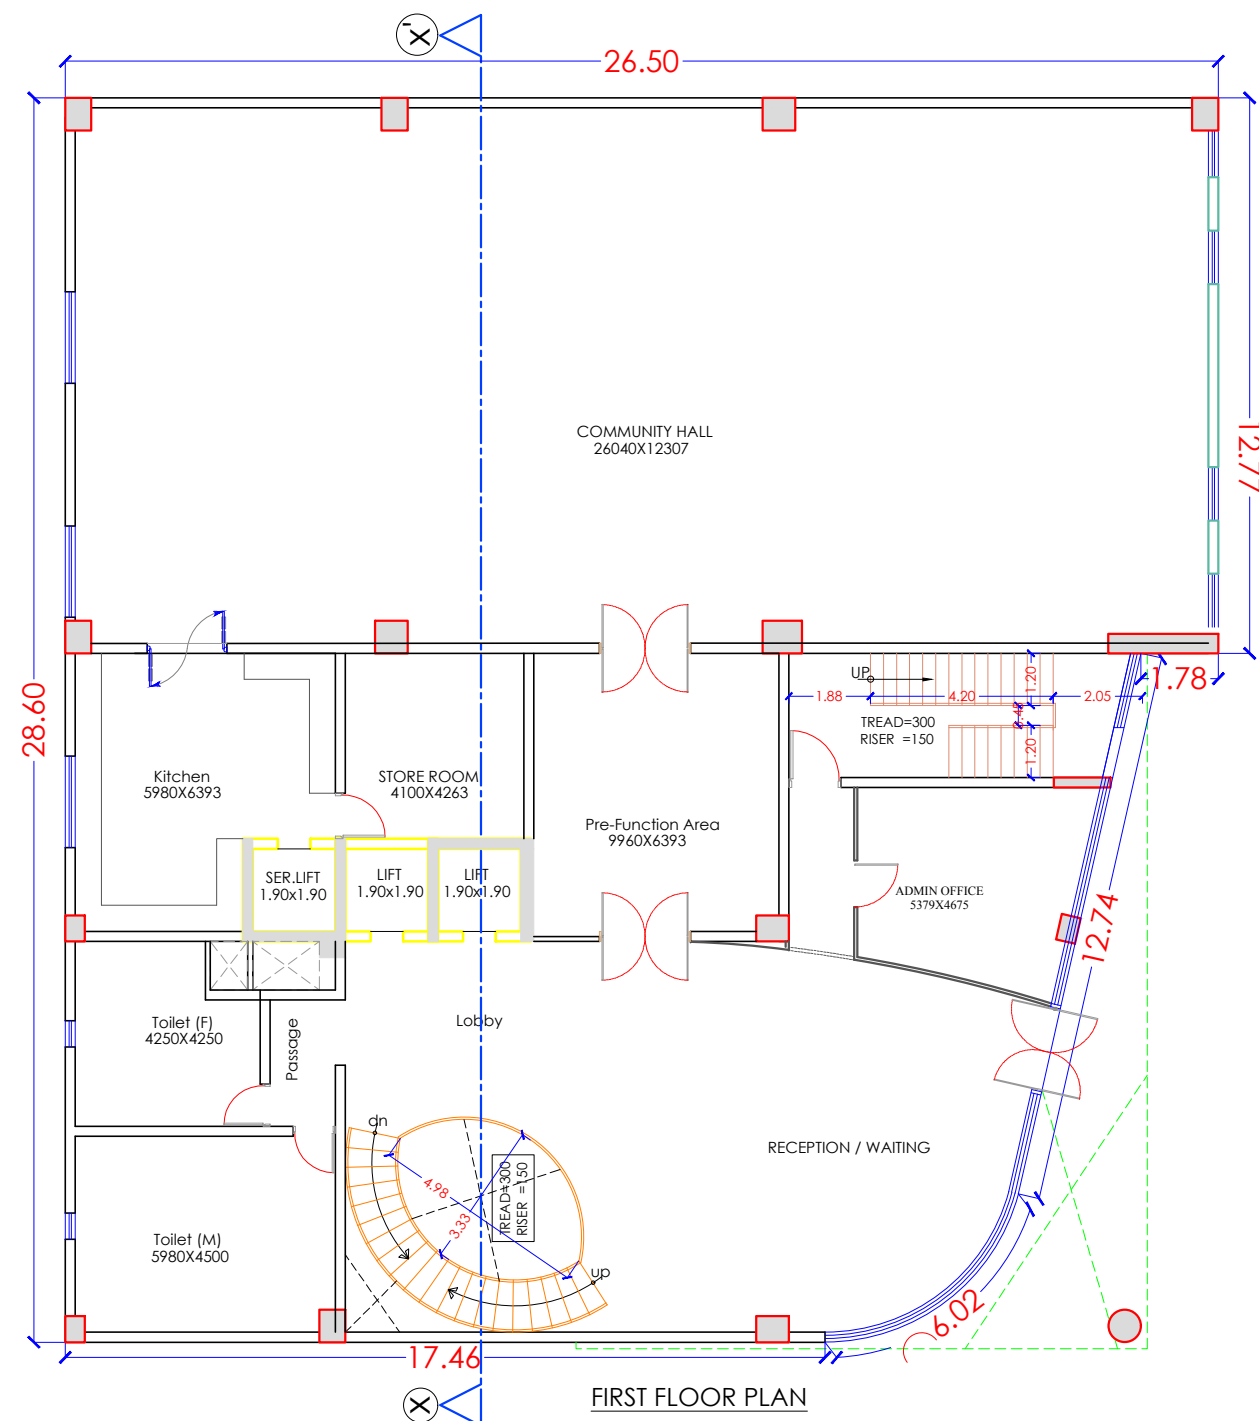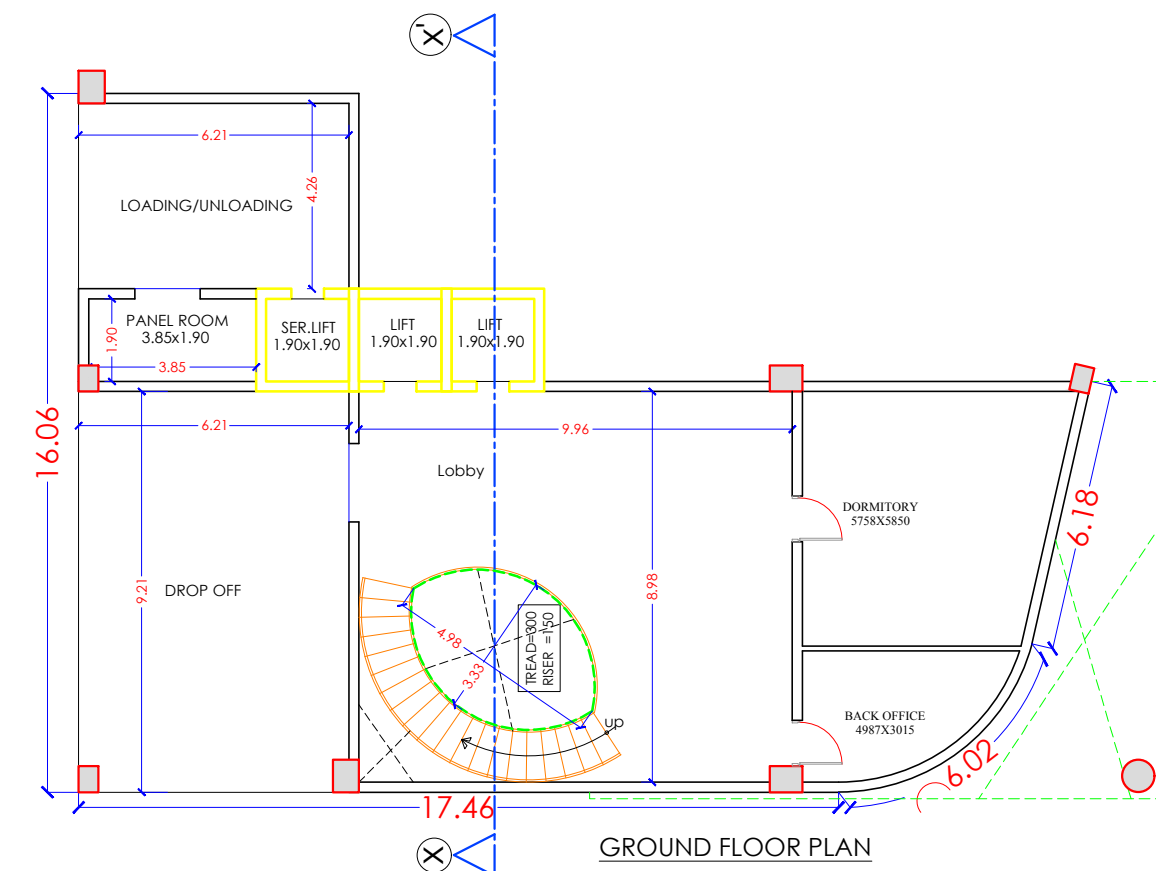

| CLUB AREA CALCULATION |              |          |          |
|-----------------------|--------------|----------|----------|
| S.No.                 | FLOOR        | B.U.A.   | G.B.U.A. |
|                       | (SQ.MT.)     | (SQ.MT.) | (SQ.MT.) |
| 1                     | GROUND FLR.  | 276.03   | 276.03   |
| 2                     | FIRST FLR.   | 686.72   | 686.72   |
| 3                     | SECOND FLR.  | 721.63   | 721.63   |
| 4                     | THIRD FLR.   | 621.79   | 621.79   |
| 5                     | FOURTH FLR.  | 615.07   | 615.07   |
| 6                     | FIFTH FLR.   | 615.07   | 615.07   |
| 7                     | SIXTH FLR.   | 281.6    | 281.6    |
| 8                     | SEVENTH FLR. | 27.24    | 27.24    |
| 9                     | EIGHT FLR.   | 27.24    | 27.24    |
| 10                    | NINTH FLR.   | 27.24    | 27.24    |
| 11                    | TENTH FLR.   | 27.24    | 27.24    |
| 12                    | ELEVETH FLR. | 77.79    | 77.79    |
| 13                    | TERRACE FLR. | 77.79    | 77.79    |
| 14                    | TOTAL        | 4082.45  | 4082.45  |

SHEET NO. - 15

DRAWING TITLE -

CLUB HOUSE FLOOR PLANS  
(GROUND TO THIRD FLOOR)

PROJECT TITLE :

PROPOSED GROUP HOUSING  
KHASRA NO. 240,241,246  
AT VILLAGE SUKHIYA,  
TEH.-SANGANER, JAIPUR

FOR ABHINANDAN PROJECTS PVT. LTD.  
ARCHITECT:-

**ricky mathur & associates**  
architects interior designers planners  
33, Dhuleshwar Garden,  
Jaipur, (RAJ.) India. 302 001  
Tel: 91-141-2362688, 5125444  
Fax: 91-141-4008700  
e-mail: ricky@rickymathur.com

DRAWING TITLE :-

CLUB HOUSE FLOOR PLANS  
(GROUND TO THIRD FLOOR)

SCALE 1 : 100

DATE AUG\_22\_2016

DEALT BY.....

STATUS SUBMISSION



CLIENT'S SIGN.

ARCHITECT'S SIGN.

SHEET NO. - 15


NORTH -



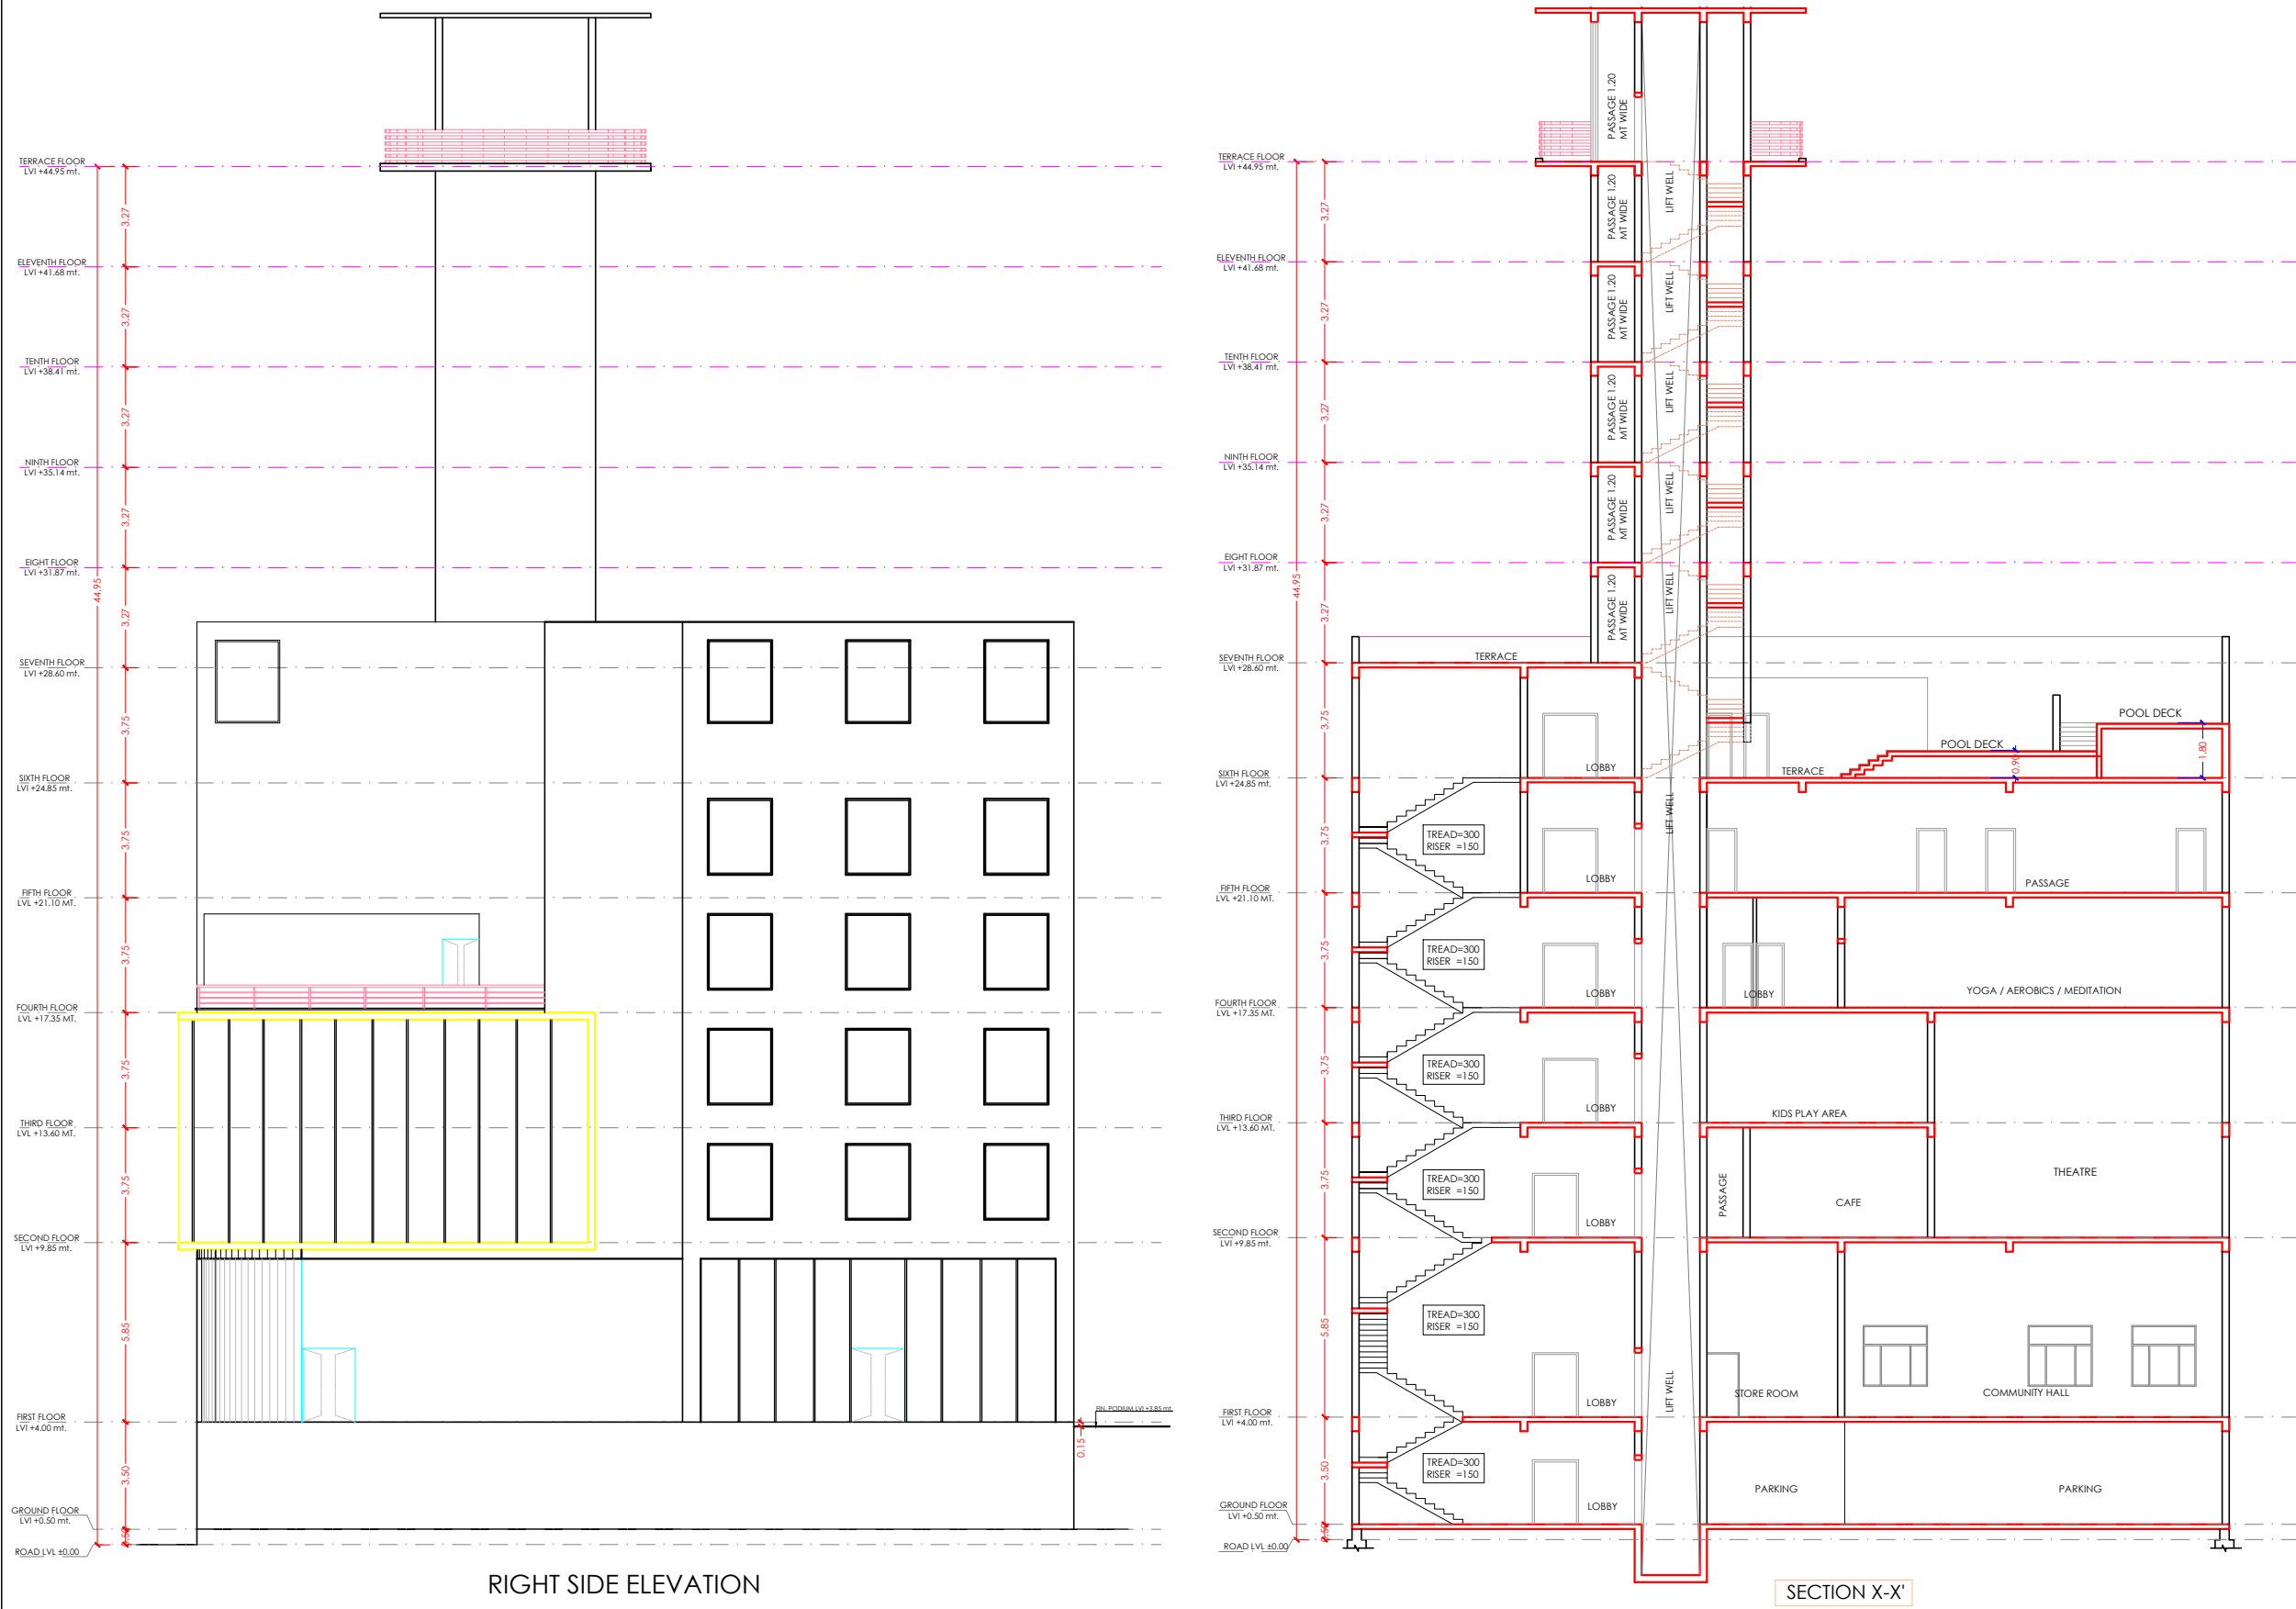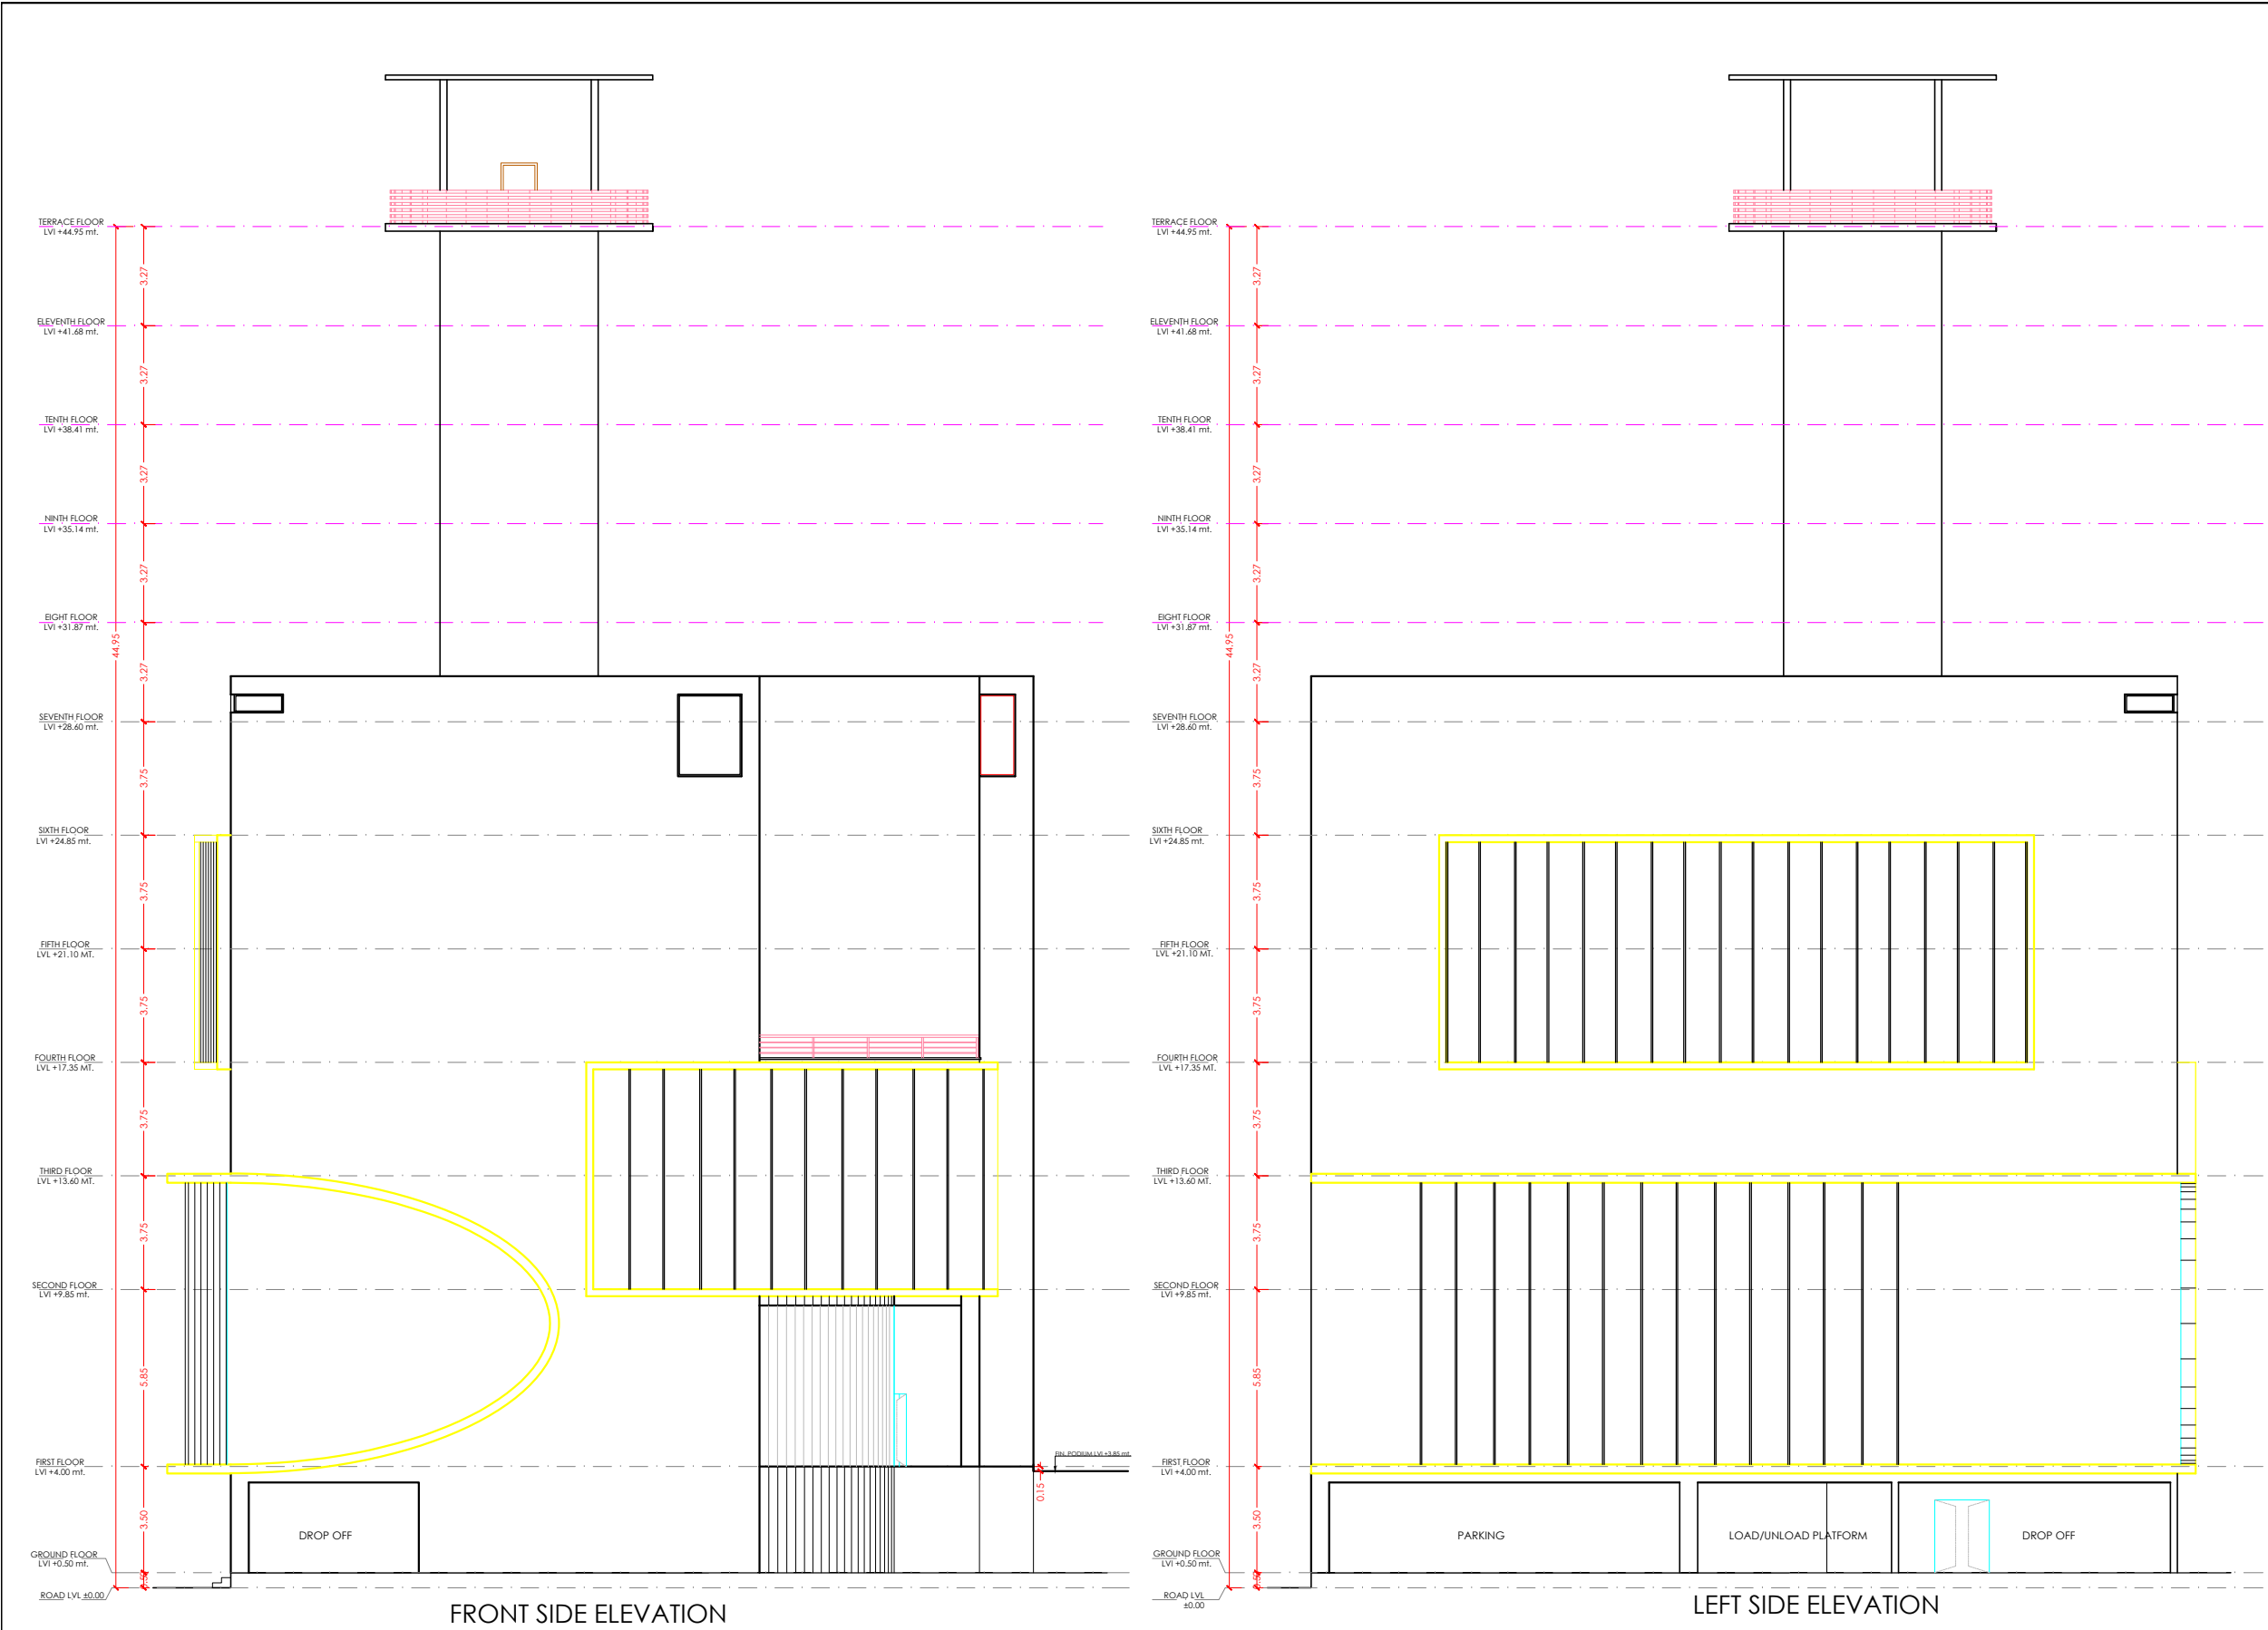


|   |                   |
|---|-------------------|
| SHEET NO. - 17   |                   |
| DRAWING TITLE -   |                   |
| CLUB HOUSE ELEVATIONS & SECTIONS   |                   |
| PROJECT TITLE :-   |                   |
| PROPOSED GROUP HOUSING<br>KHASRA NO. 240,241,246<br>AT VILLAGE SUKHIYA,<br>TEH.-SANGANER, JAIPUR   |                   |
| FOR ABHINANDAN PROJECTS PVT. LTD.   |                   |
| ARCHITECT:-   |                   |
| ricky mathur & associates<br>architects interior designers planners<br>33, Dhuleshwar Garden,<br>Jaipur, (RAJ.) India, 302 001<br>Tel: 91-141-2362688, 5125444<br>Fax: 91-141-4008700<br>e-mail: ricky@rickymathur.com |                   |
| DRAWING TITLE :-   |                   |
| CLUB HOUSE ELEVATIONS & SECTIONS   |                   |
| SCALE 1 : 100   | DATE AUG_22_2016  |
| DEALT BY.....   | STATUS SUBMISSION |
| CLIENT'S SIGN.   |                   |
| ARCHITECT'S SIGN.   |                   |
| SHEET NO. - 17   | NORTH -           |



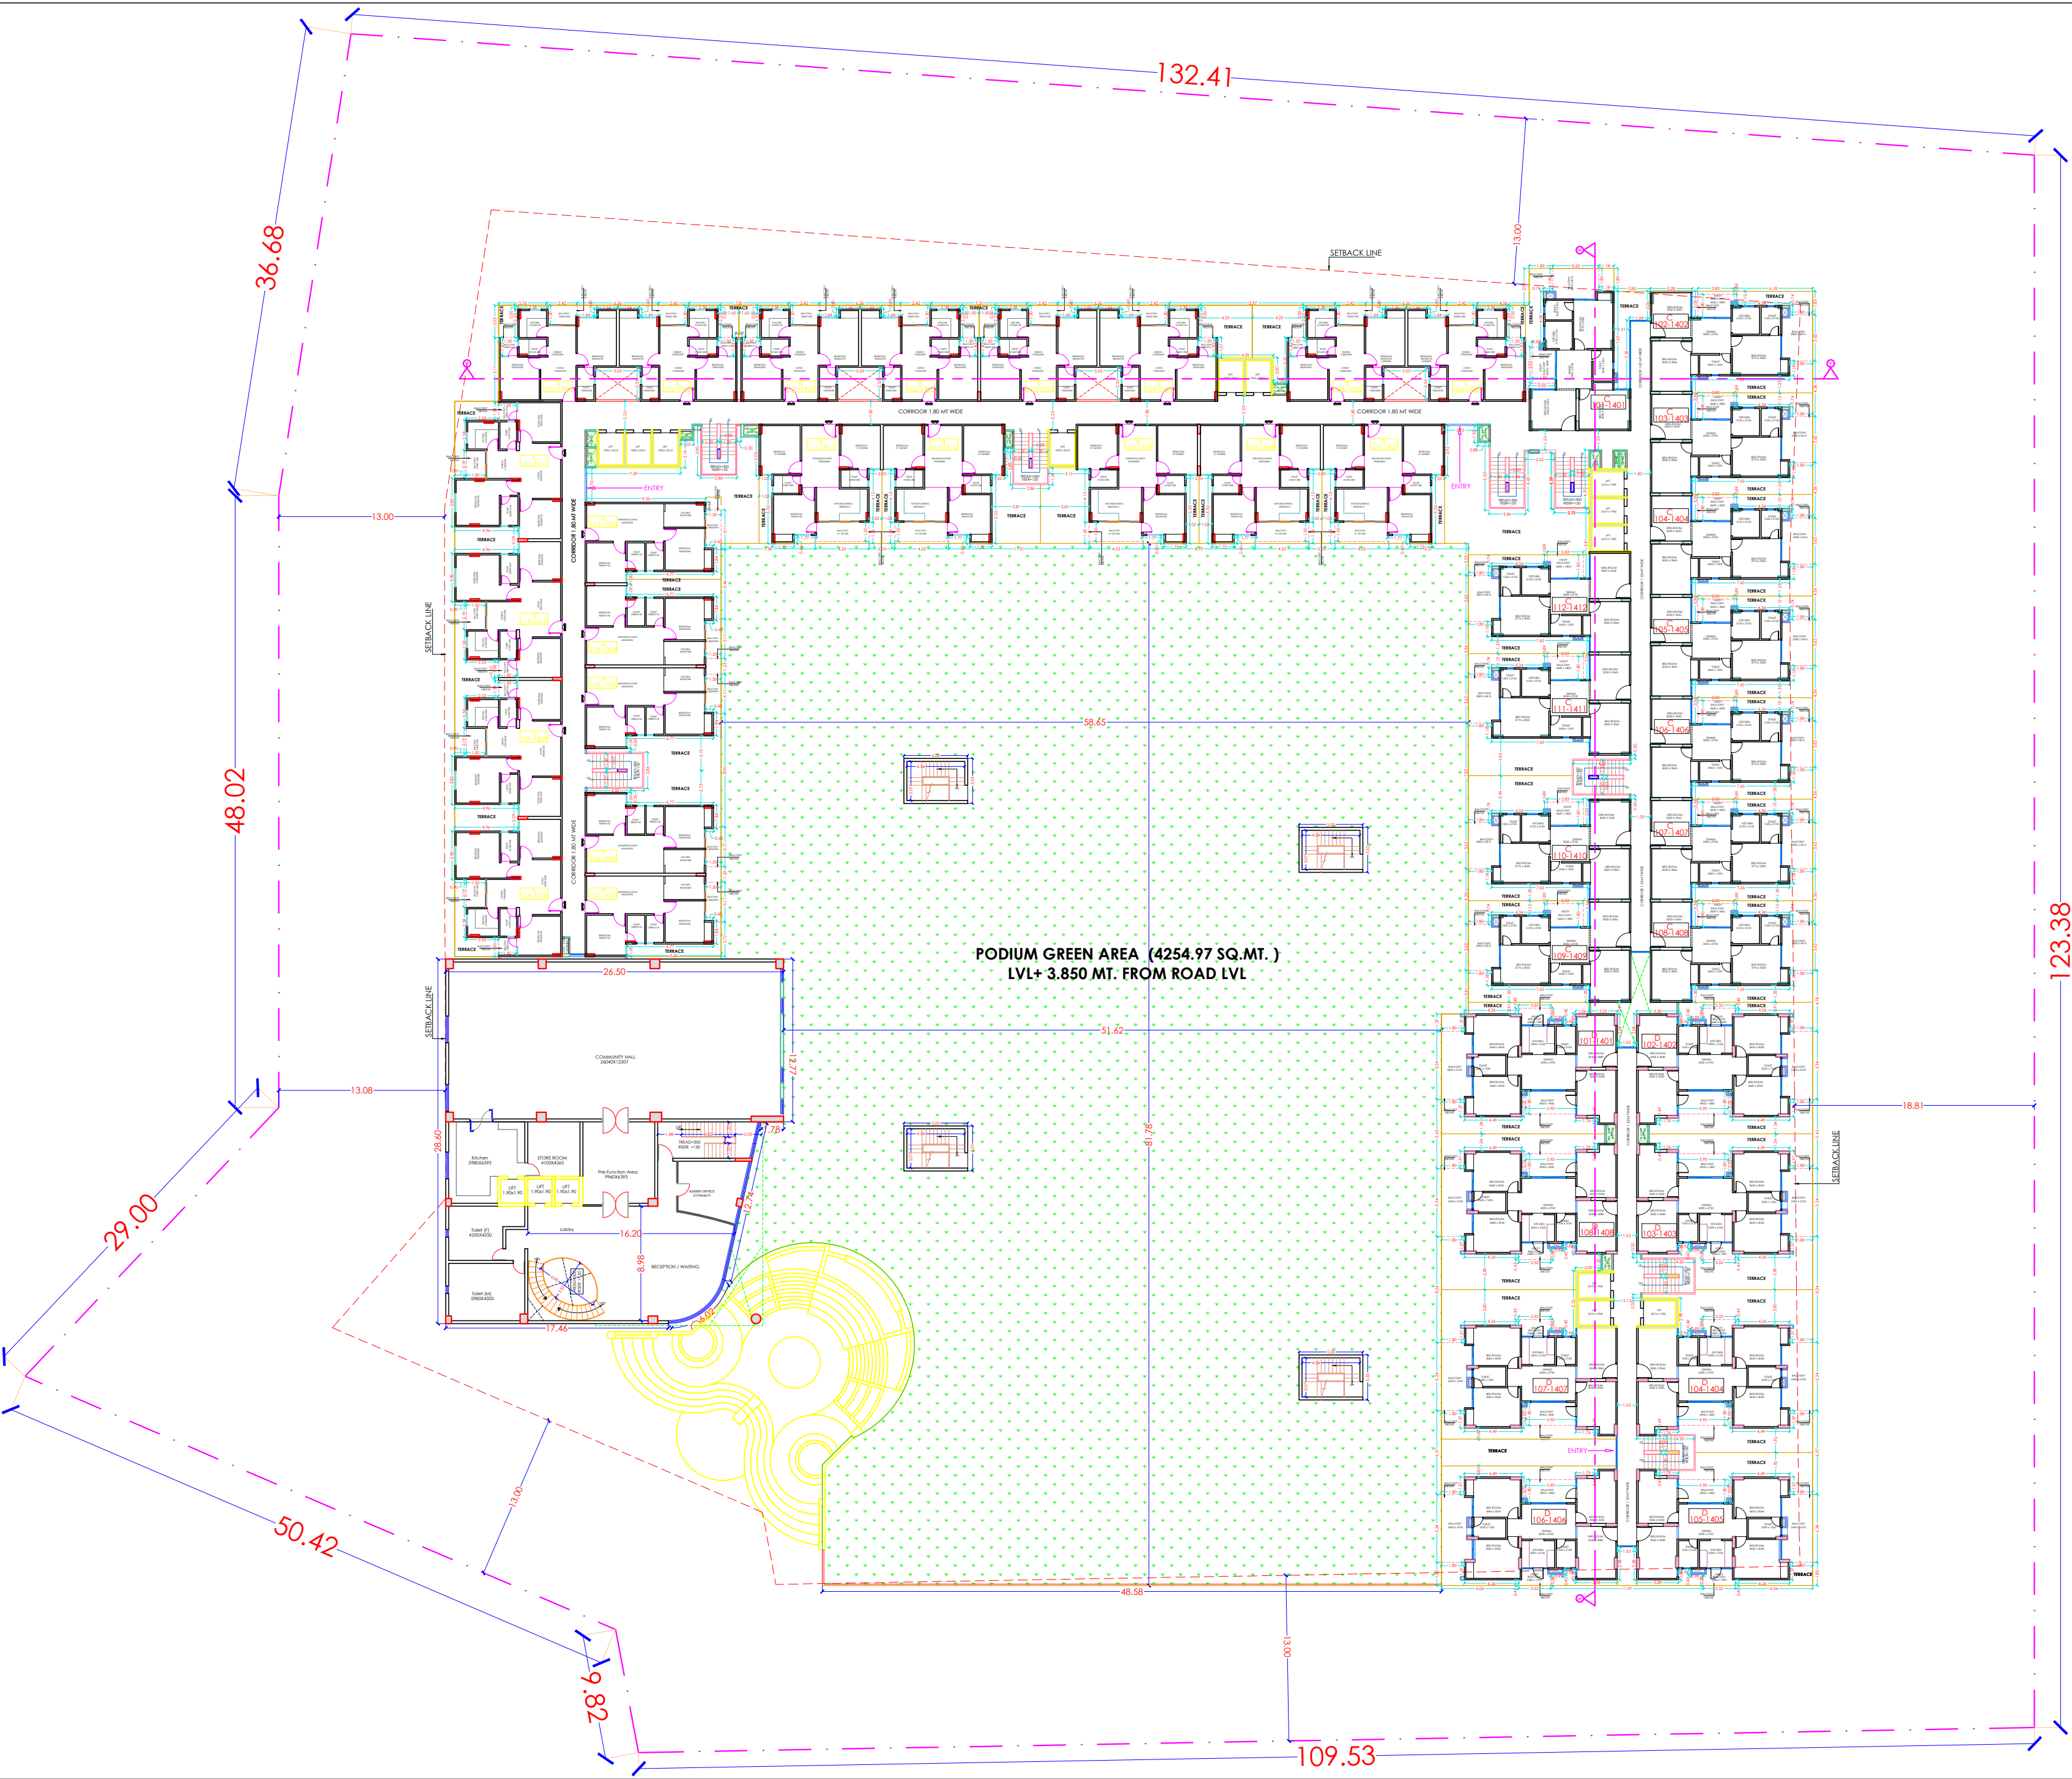

|   |                   |
|---|-------------------|
| SHEET NO. - 04   |                   |
| DRAWING TITLE -   |                   |
| FIRST FLOOR PLAN   |                   |
| PROJECT TITLE -   |                   |
| PROPOSED GROUP HOUSING<br>KHASRA NO. 240,241,246<br>AT VILLAGE SUKHIYA<br>TEH.-SANGANER, JAIPUR   |                   |
| FOR ABHINANDAN PROJECTS PVT. LTD.   |                   |
| ARCHITECT -   |                   |
| ricky mathur & associates<br>architects interior designers planners<br>33, Dhulestwar Garden,<br>Jaipur, (RAJ.) India, 302 001<br>Tel: 91-141-2362688, 5125444<br>Fax: 91-141-4008700<br>e-mail: ricky@rickymathur.com |                   |
| DRAWING TITLE -   |                   |
| FIRST FLOOR PLAN   |                   |
| SCALE 1:150   | DATE AUG_22_2016  |
| DEALT BY.....   | STATUS SUBMISSION |
| CLIENT'S SIGN.   | ARCHITECT'S SIGN. |
| SHEET NO. - 04   | NORTH -           |



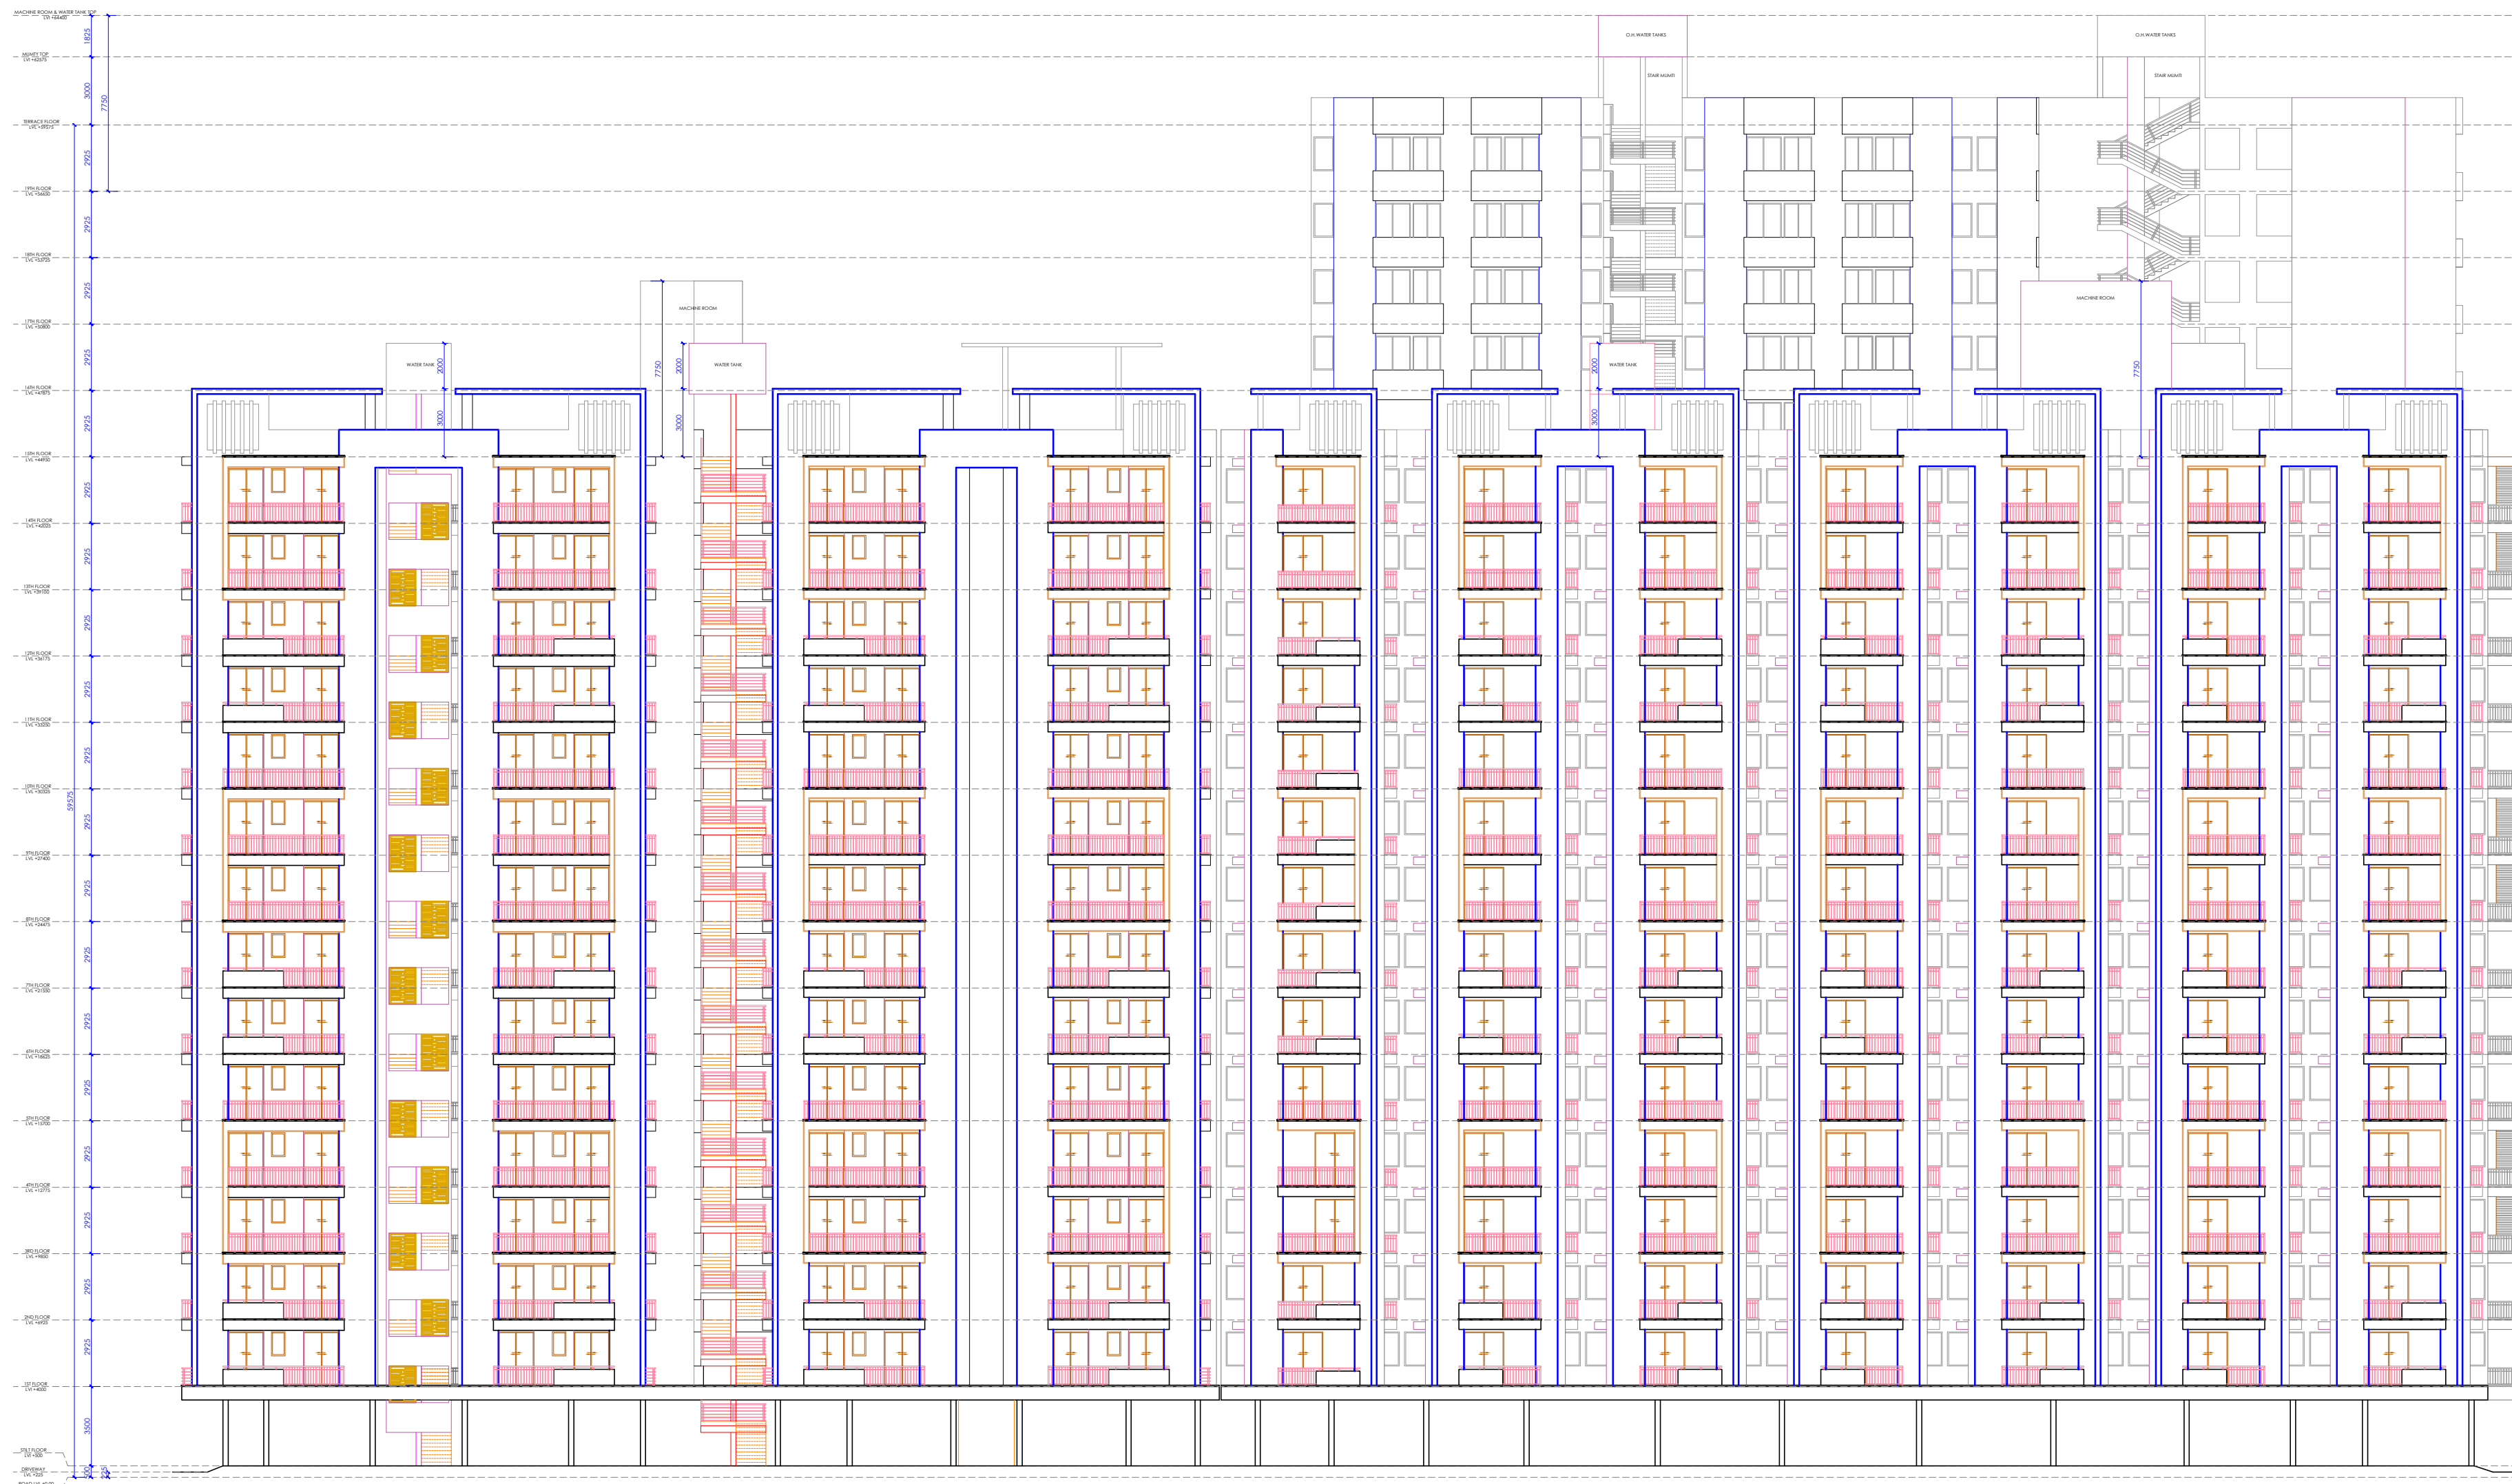

### FRONT SIDE ELEVATION

PROJECT TITLE :

**PROPOSED GROUP HOUSING  
KHASRA NO. 240,241,246  
AT VILLAGE SUKHIYA,  
TEH.-SANGANER, JAIPUR**

FOR ABHINANDAN PROJECTS PVT. LTD.

ARCHITECT-

ricky mathur &amp; associates

**Ricky Mathur & Associates**  
architects interior designers planners  
33, Dhuleshwar Garden,  
Jaipur. (RAJ.) India. 302 001  
Tel: 91-141-2362688, 5125444  
Fax: 91-141-4008700  
e-mail: ricky@rickymathur.com



DRAWING TITLE :-

FRONT SIDE ELEVATION

SCALE 1 : 100

|      |             |
|------|-------------|
| DATE | AUG_22_2018 |
|------|-------------|

DEALT BY.....


| .... | STATUS | SUBMISSION |
|------|--------|------------|
|------|--------|------------|

CLIENT'S SIGN.

ARCHITECT'S SIGN.

SHEET NO. - 09

NORTH -

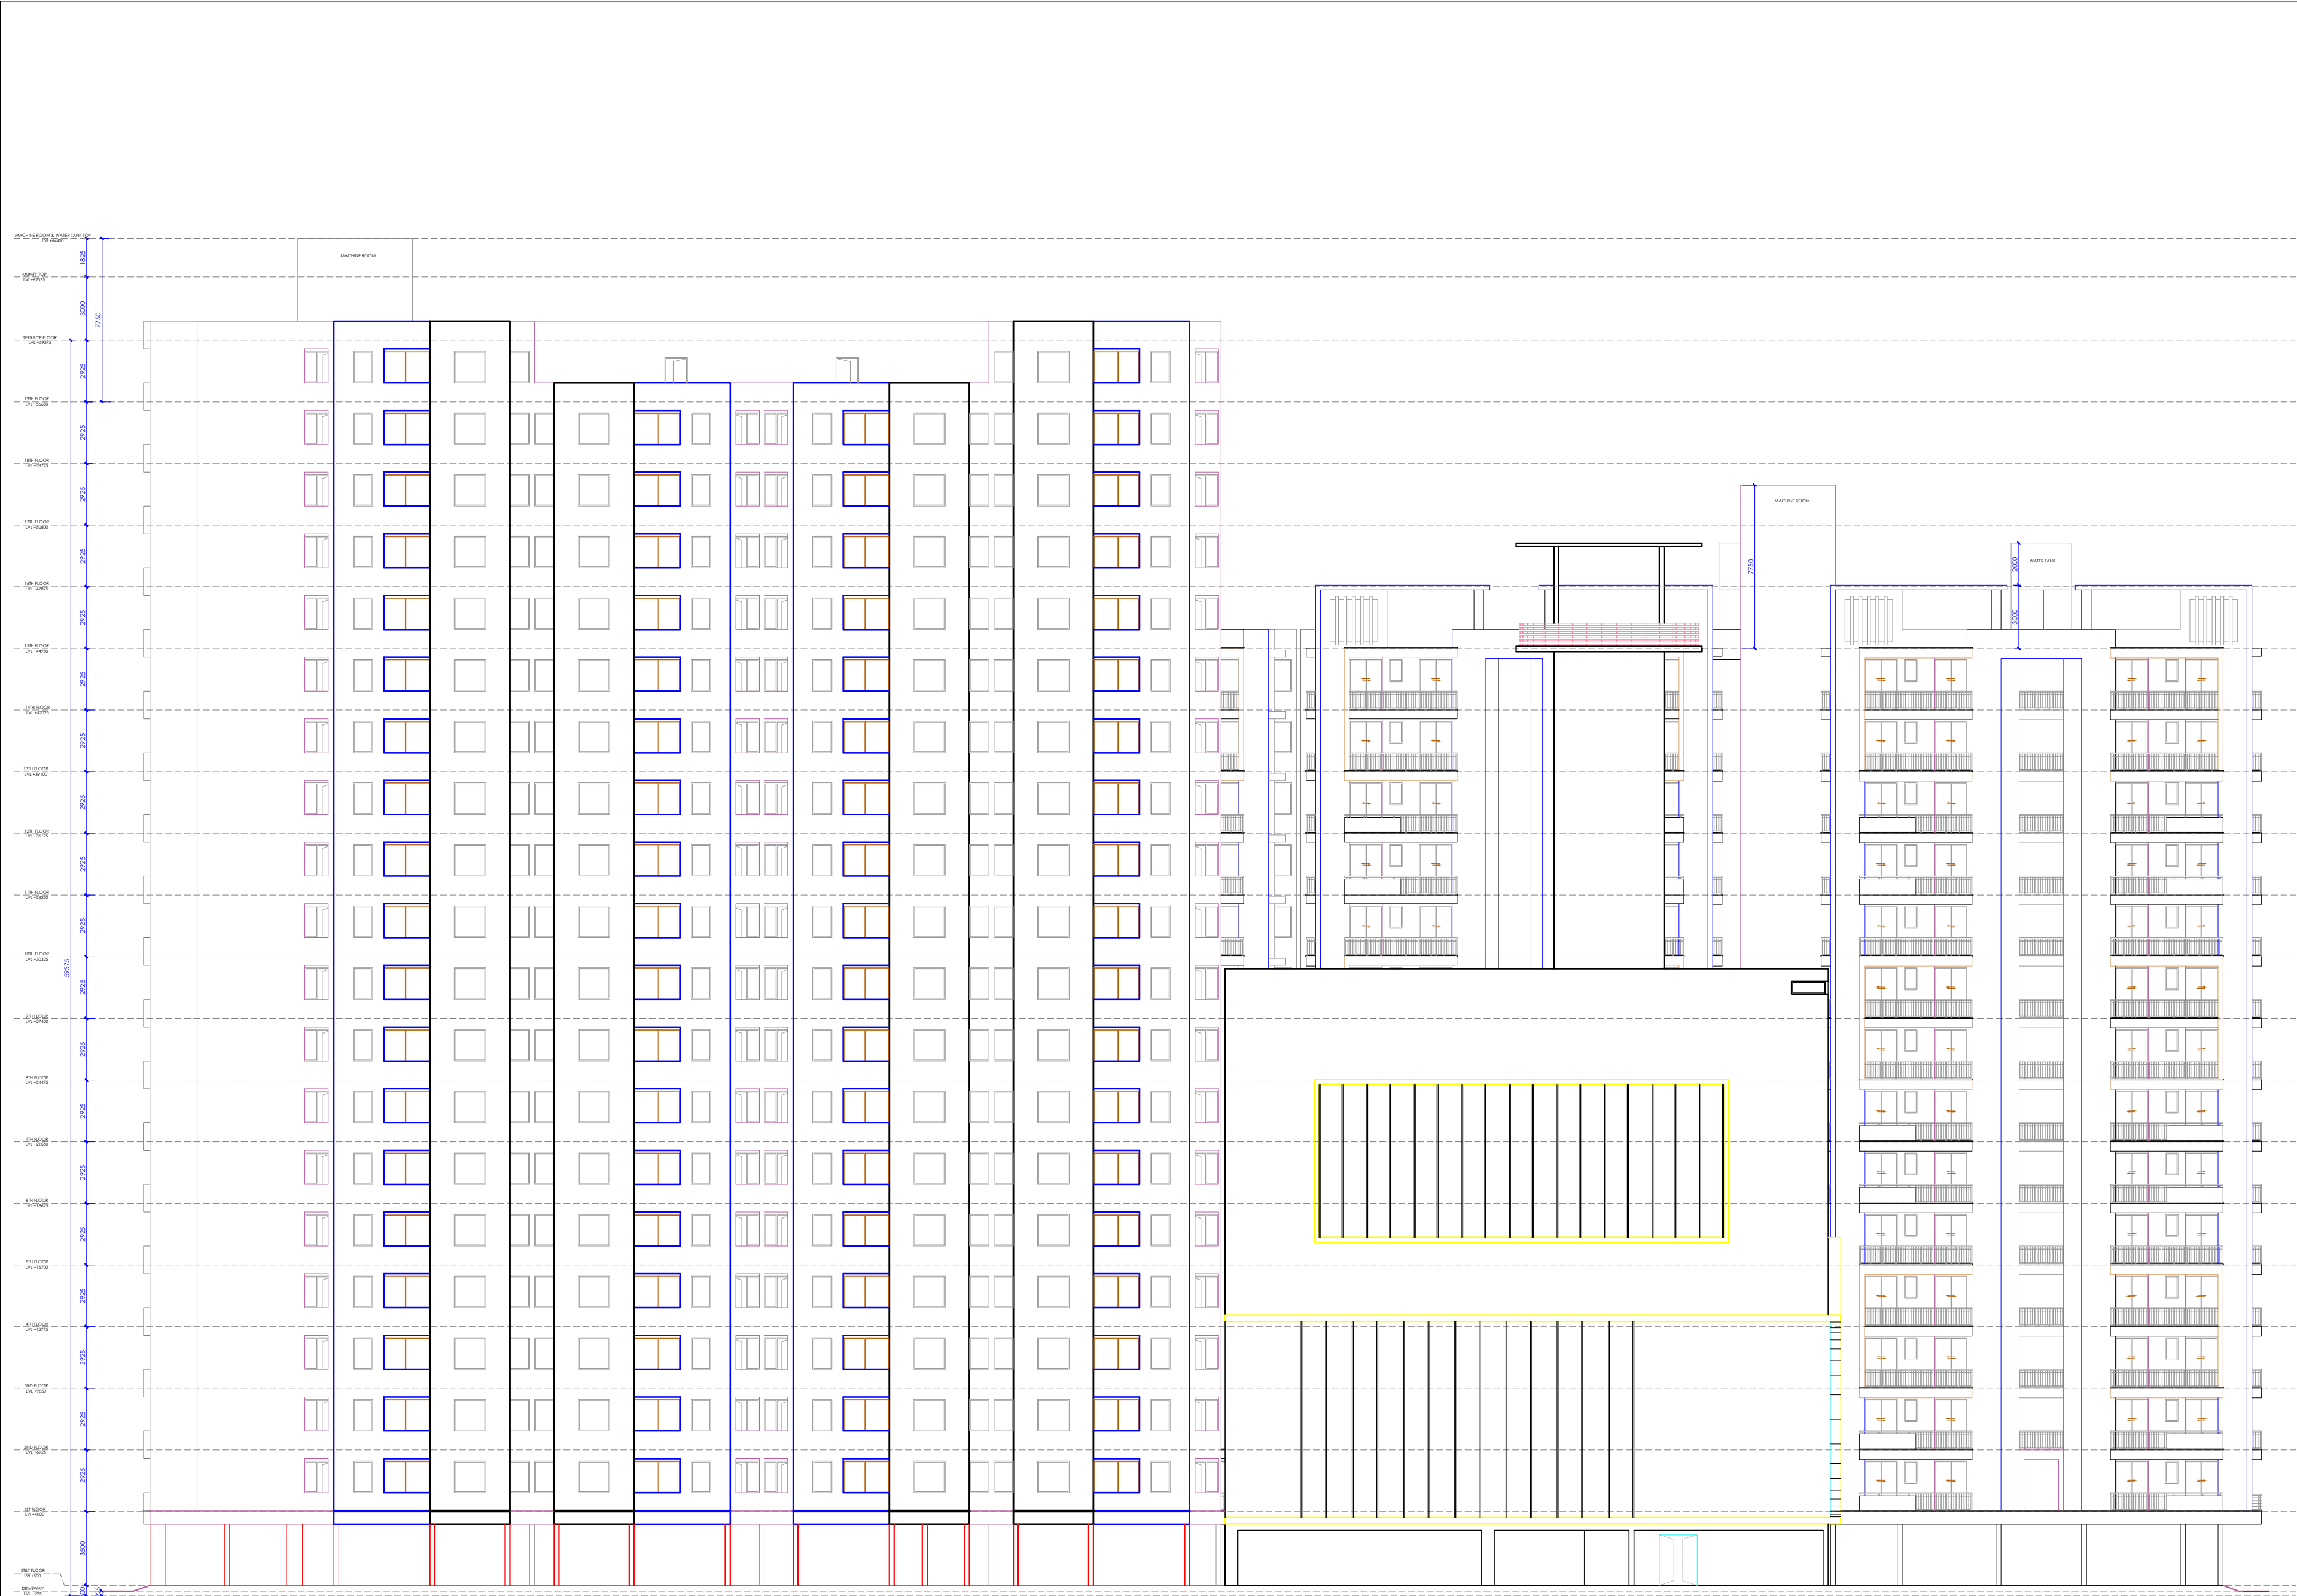

(REAR SIDE ELEVATION)

SHEET NO. - 10

DRAWING TITLE :-

REAR SIDE ELEVATION

PROJECT TITLE :-

PROPOSED GROUP HOUSING  
KHASRA NO. 240,241,246  
AT VILLAGE SUKHIYA,  
TEH.-SANGANER, JAIPUR

FOR ABHINANDAN PROJECTS PVT. LTD.

ARCHITECT:-

**ricky mathur & associates**  
architects interior designers planners  
33, Dhuleshwar Garden,  
Jaipur, (RAJ.) India, 302 001  
Tel: 91-141-2362688, 5125444  
Fax: 91-141-4008700  
e-mail: ricky@rickymathur.com

DRAWING TITLE :-

REAR SIDE ELEVATION

SCALE 1 : 100

DATE AUG\_22\_2016

DEALT BY.....

STATUS SUBMISSION

CLIENT'S SIGN.

ARCHITECT'S SIGN.

SHEET NO. - 10

NORTH -

SHEET NO. - 11

DRAWING TITLE :-

LEFT SIDE ELEVATION

PROJECT TITLE :

PROPOSED GROUP HOUSING  
KHASRA NO. 240,241,246  
AT VILLAGE SUKHIYA,  
TEH.-SANGANER, JAIPUR

FOR ABHINANDAN PROJECTS PVT. LTD.

ARCHITECT:-

ricky mathur & associates

architects interior designers planners

33, Dhuleshwar Garden,  
Jaipur, (RAJ.) India. 302 001

Tel: 91-141-2362688, 5125444

Fax: 91-141-4008700

e-mail: ricky@rickymathur.com

DRAWING TITLE :-

LEFT SIDE ELEVATION

SCALE 1:100

DATE AUG.22, 2016

DEALT BY.....

STATUS SUBMISSION

CLIENT'S SIGN.

ARCHITECT'S SIGN.


SHEET NO. - 11


NORTH -



LEFT SIDE ELEVATION



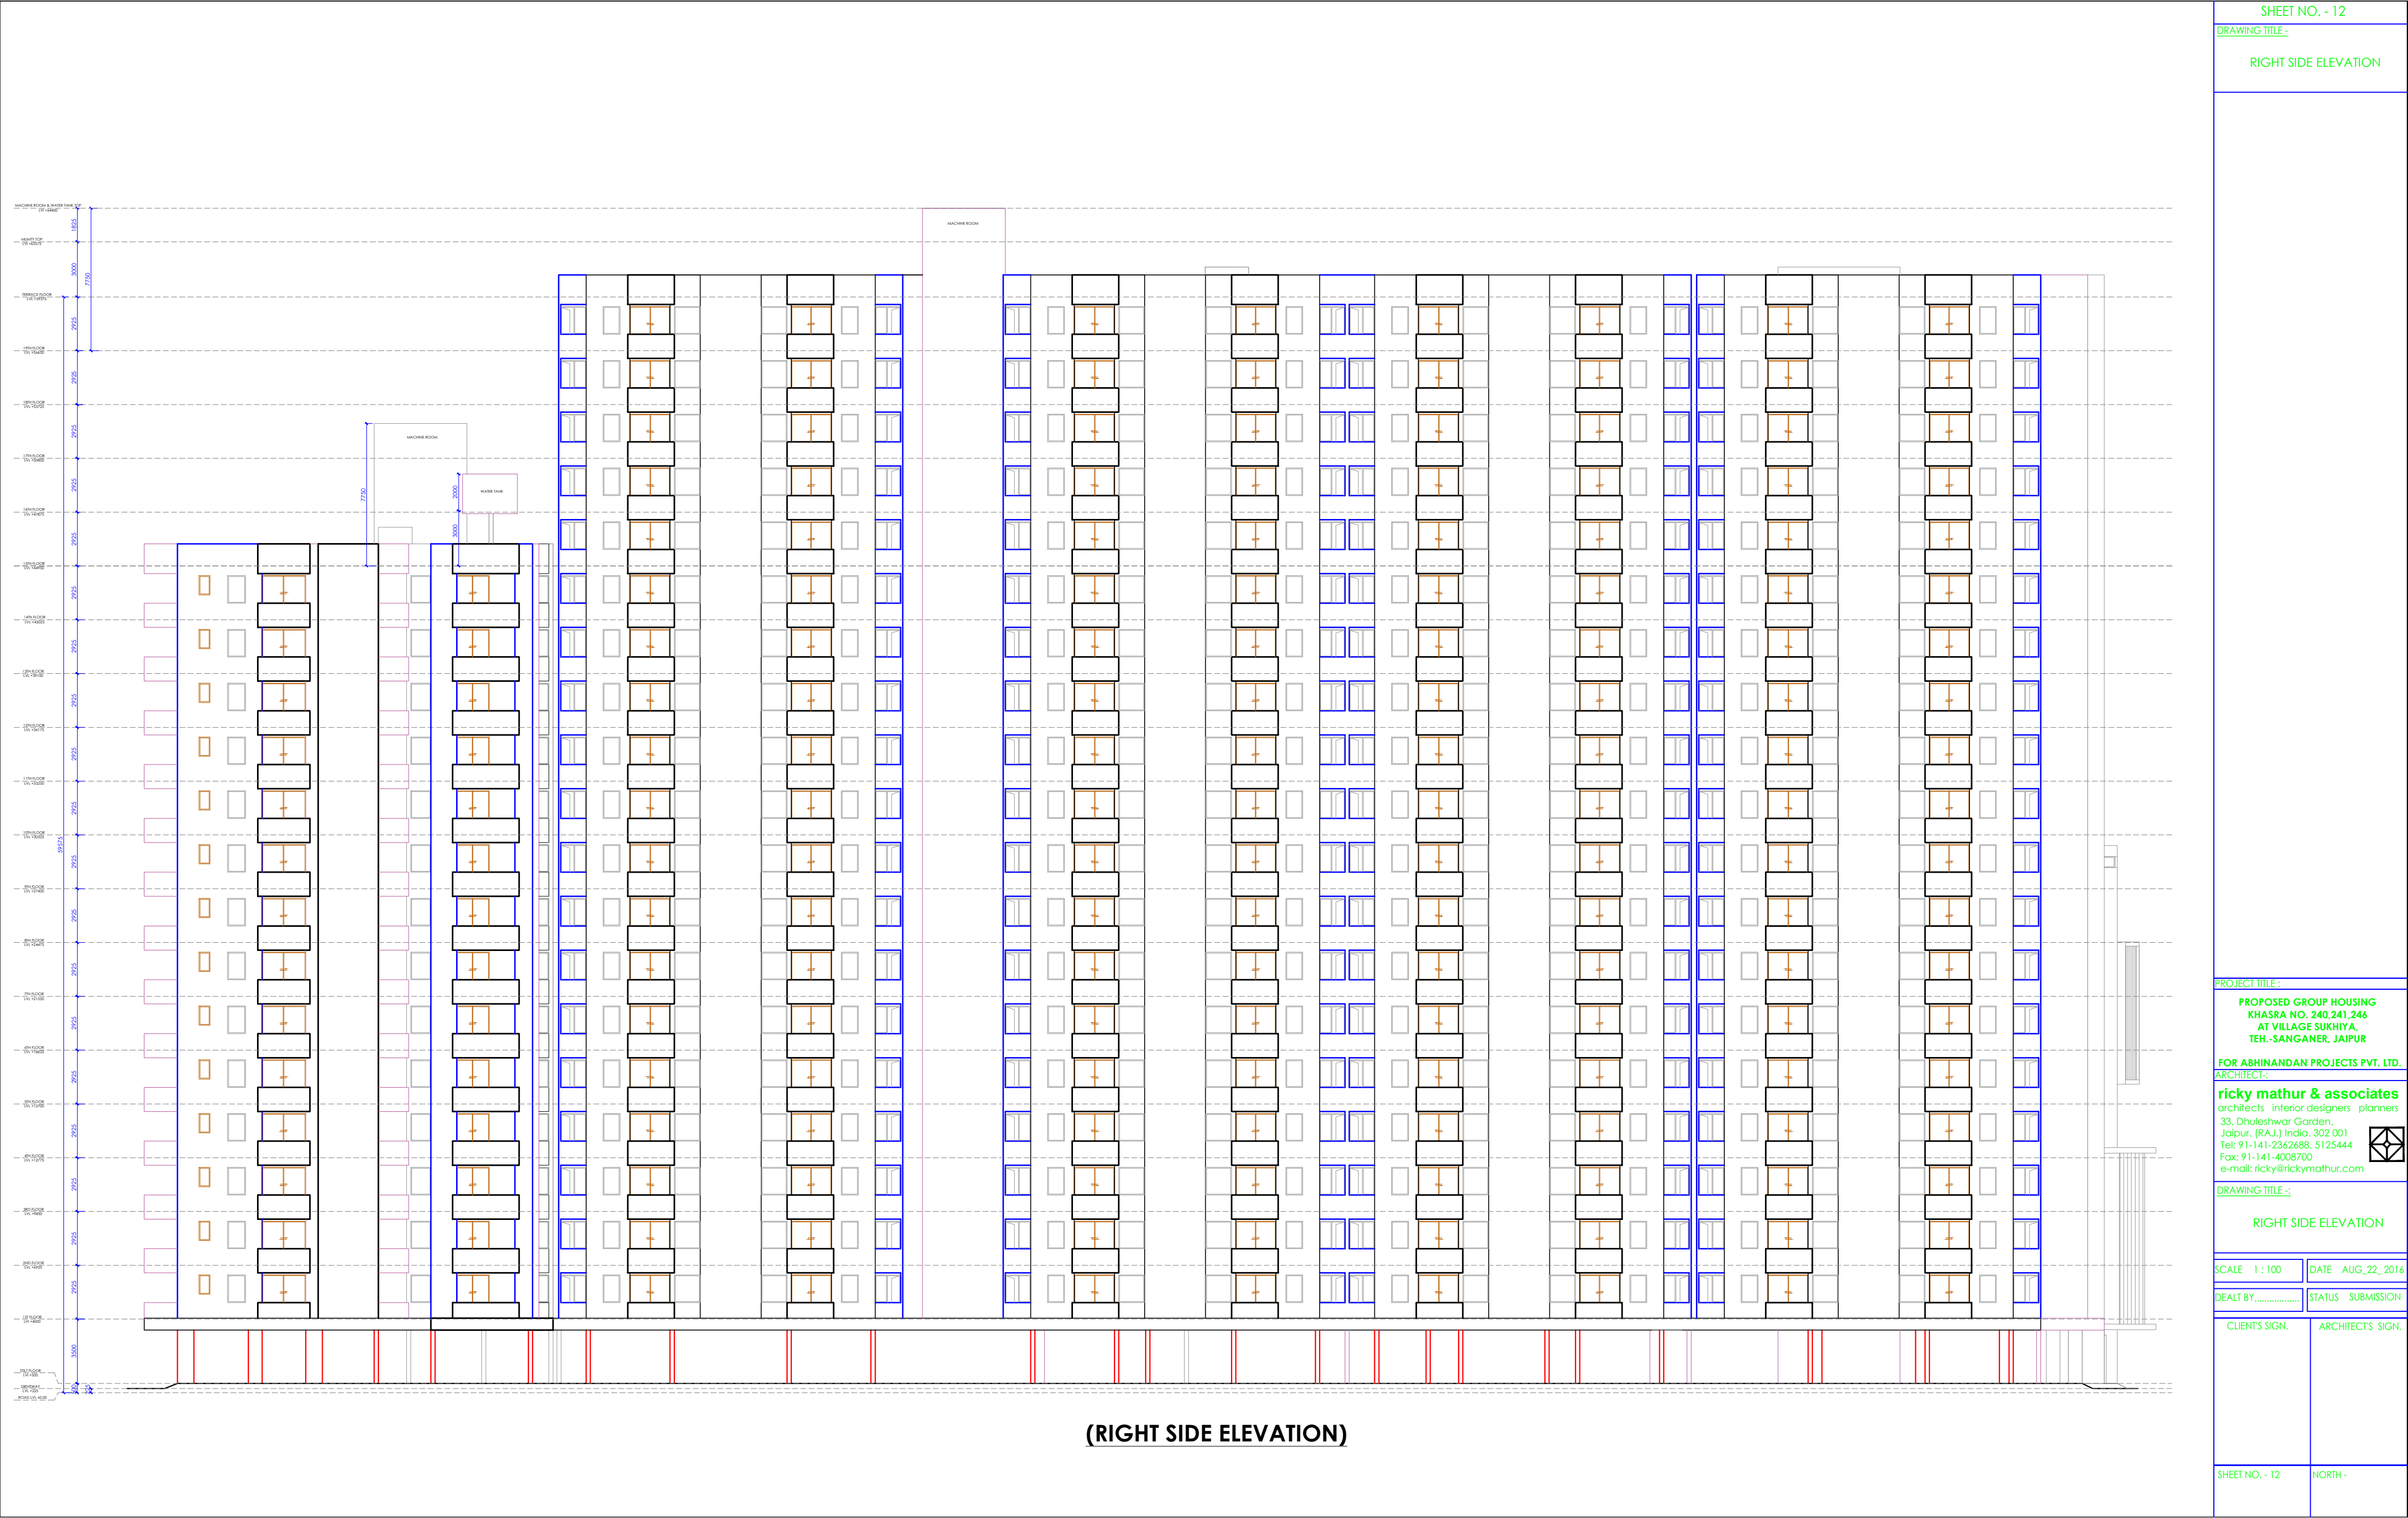

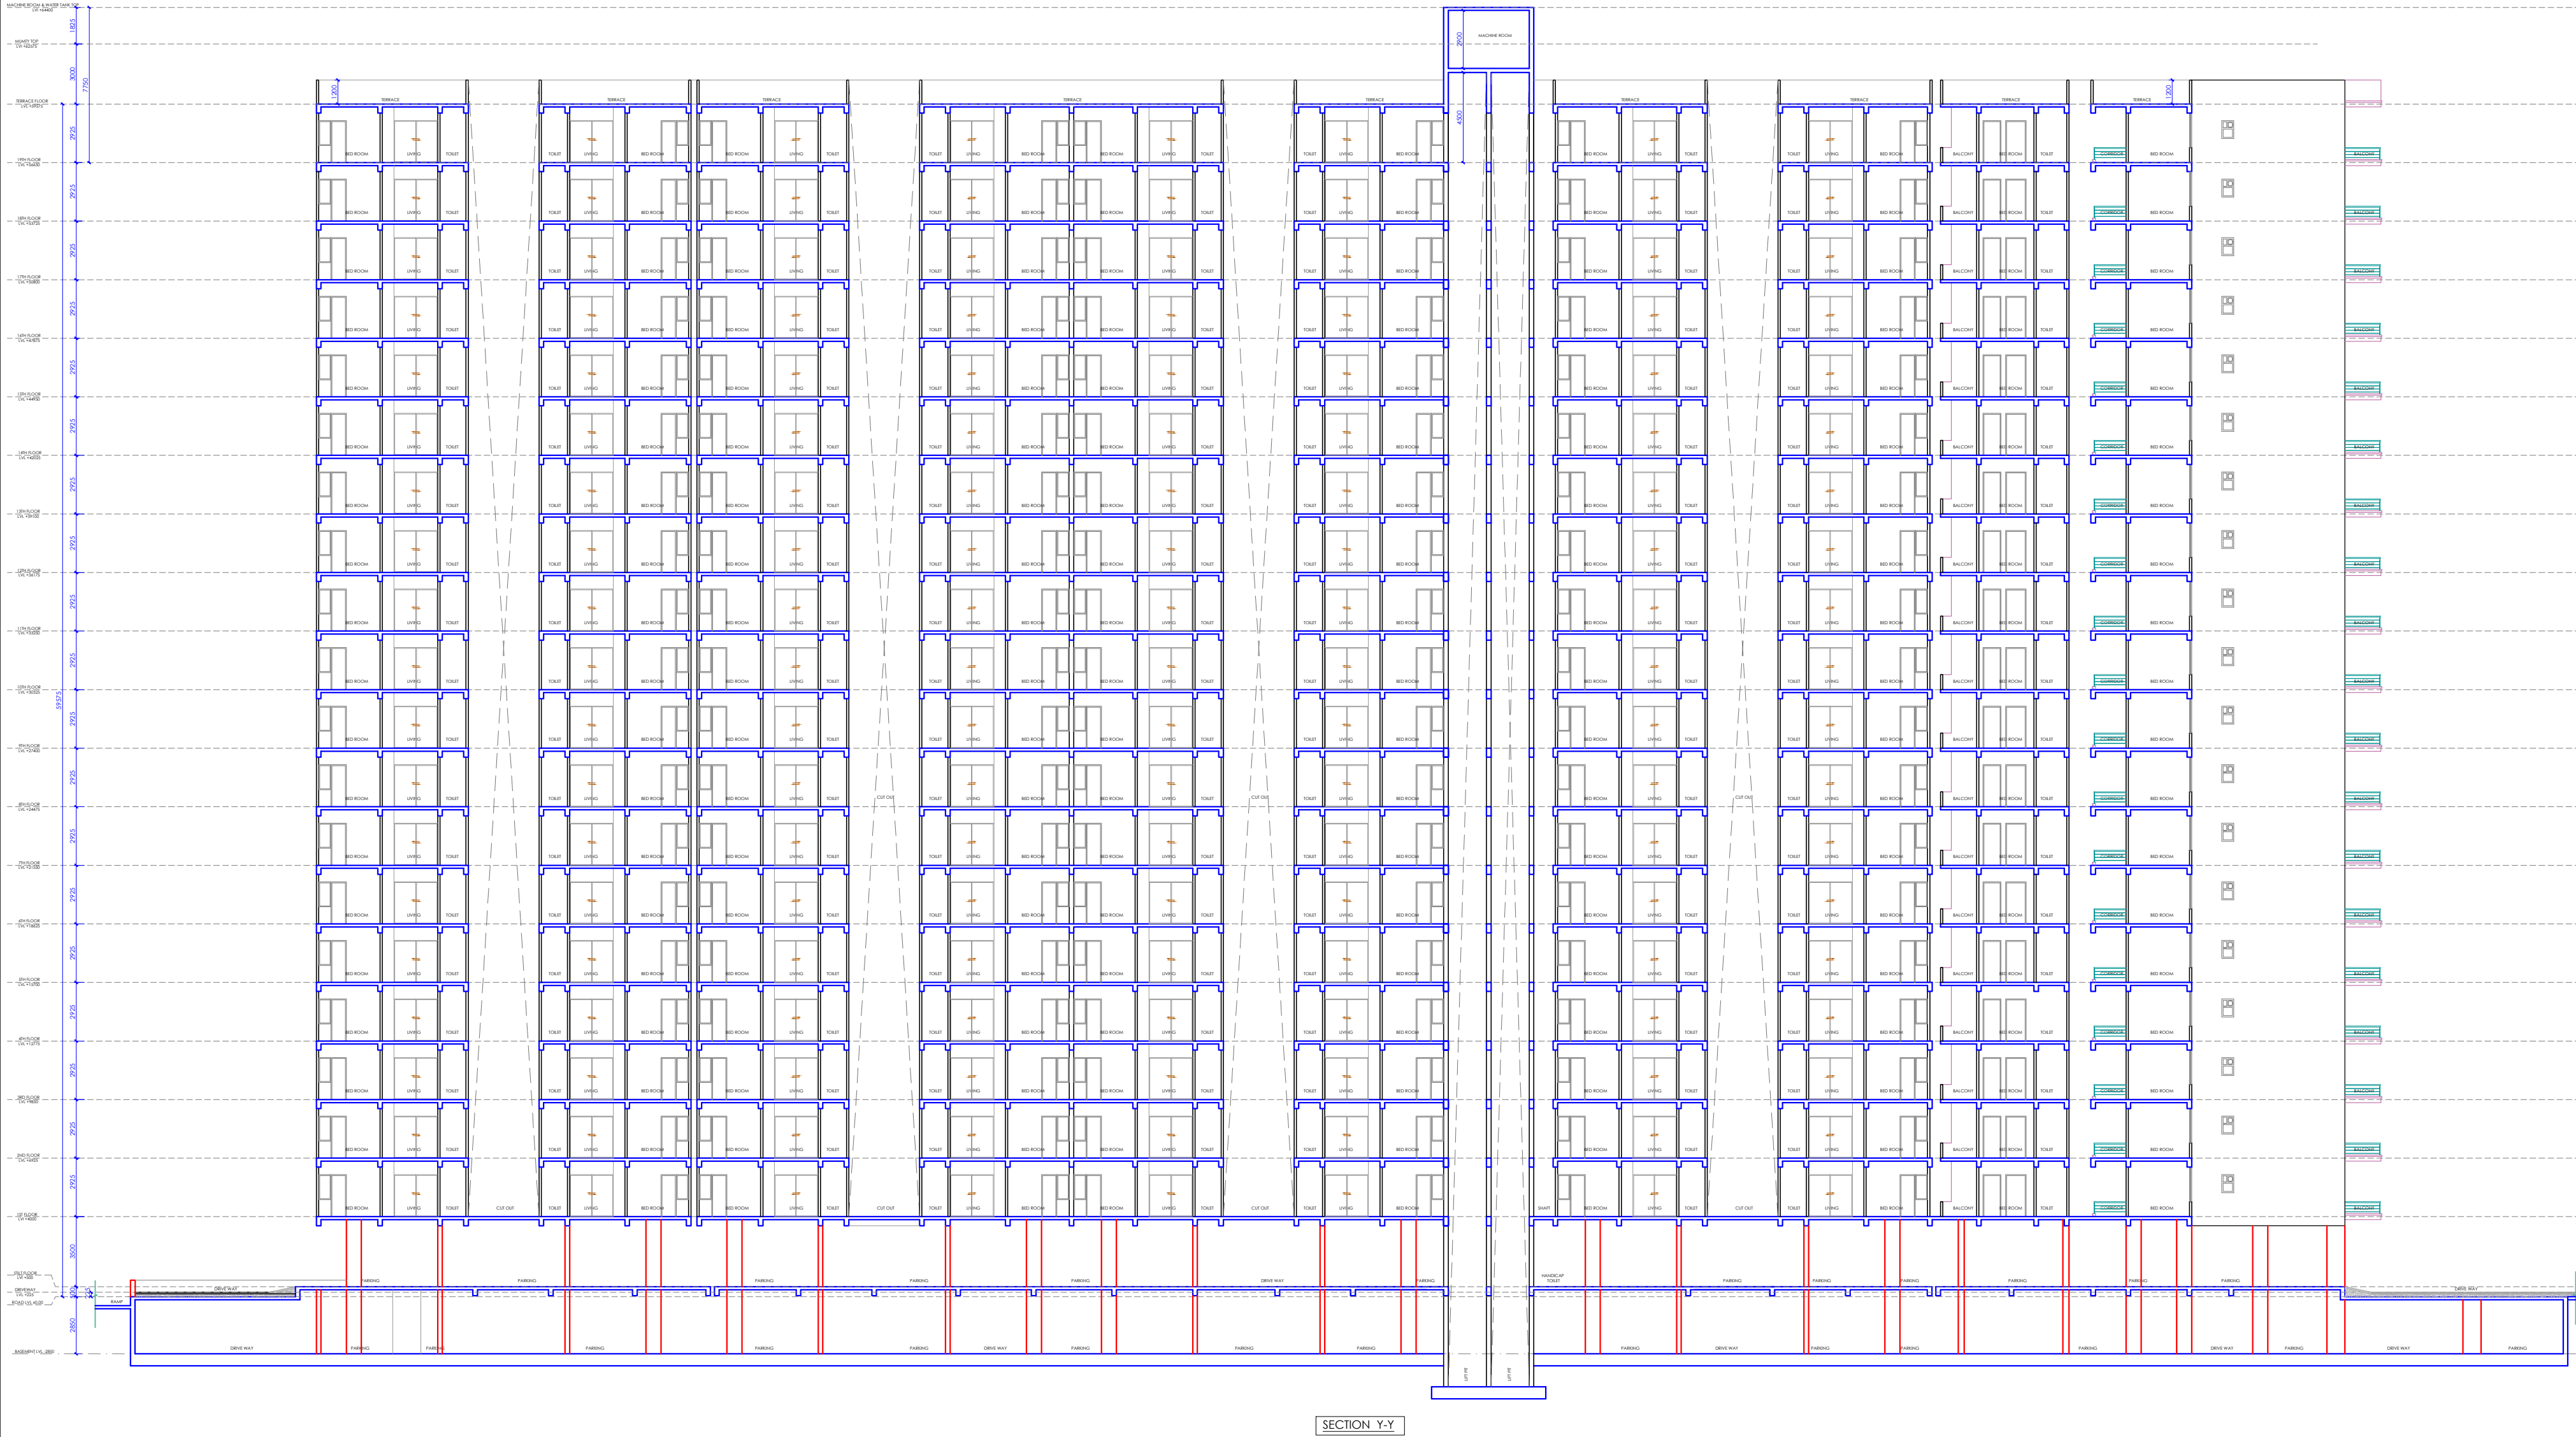

PROJECT TITLE:

PROPOSED GROUP HOUSING  
KHASRA NO. 240.241.246  
AT VILLAGE SUKHIYA,  
TEH.-SANGANER, JAIPUR

FOR ABHINANDAN PROJECTS PVT. LTD.

ARCHITECT:

**ricky mathur & associates**  
architects interior designers planners  
33, Dhuleshwar Garden,  
Jaipur, (RAJ.) India. 302 001  
Tel: 91-141-2362688, 5125444  
Fax: 91-141-4008700  
e-mail: ricky@rickymathur.com

DRAWING TITLE -

SECTION AT (Y-Y)

SCALE 1 : 100

DATE AUG\_22\_2016

DEALT BY.....


STATUS SUBMISSION

CLIENT'S SIGN.

ARCHITECT'S SIGN.

SHEET NO. - 14

NORTH -

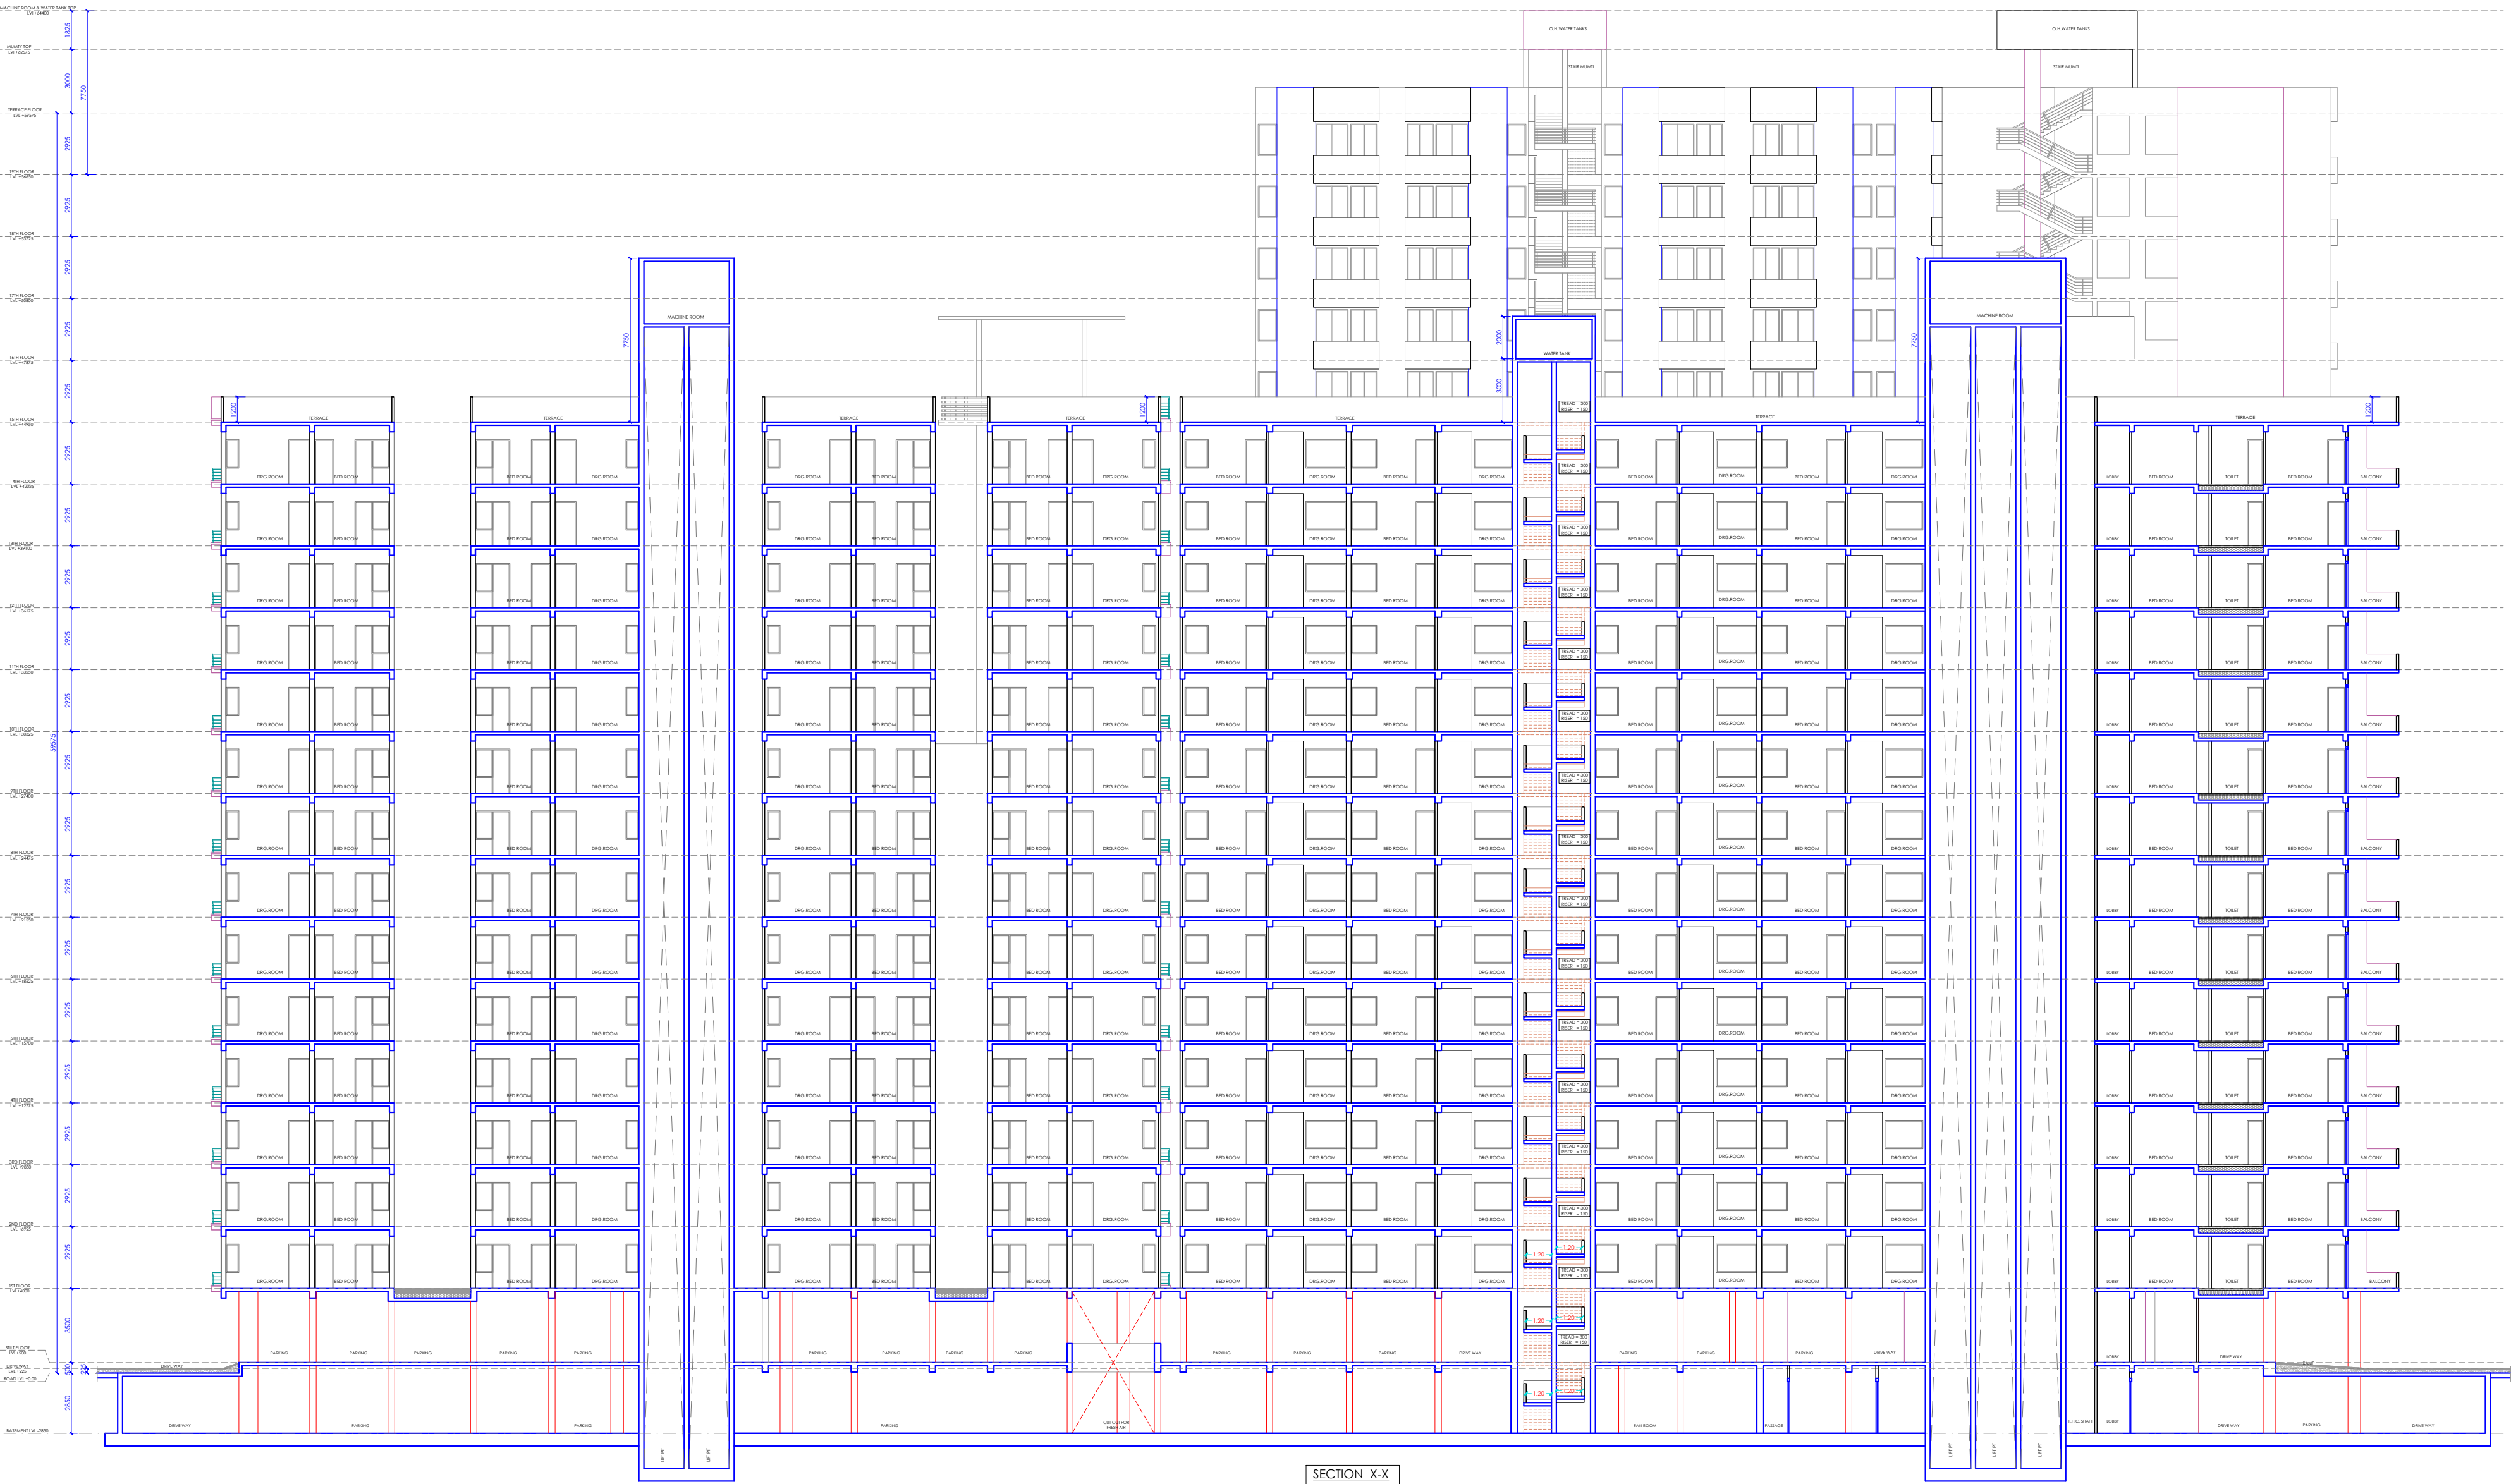

PROJECT TITLE :

PROPOSED GROUP HOUSING  
KHASRA NO. 240,241,246  
AT VILLAGE SUKHIYA,  
TEH.-SANGANER, JAIPUR

FOR ABHINANDAN PROJECTS PVT. LTD.  
ARCHITECT:-

**ricky mathur & associates**  
architects interior designers planners  
33, Dhuleshwar Garden,  
Jaipur, (RAJ.) India. 302 001  
Tel: 91-141-2362688, 5125444  
Fax: 91-141-4008700  
e-mail: ricky@rickymathur.com

DRAWING TITLE :-

SECTION AT (X-X)

SCALE 1 : 100

DATE AUG\_22\_2016

DEALT BY.....

STATUS SUBMISSION

CLIENT'S SIGN.

ARCHITECT'S SIGN.

SHEET NO. - 13

NORTH -



| S.N.                                                                                 | FLOOR                  | F.A.R.  | AREA CALCULATION |             |          |             |         | CORRIDORS | SERVICES |
|--------------------------------------------------------------------------------------|------------------------|---------|------------------|-------------|----------|-------------|---------|-----------|----------|
|                                                                                      |                        |         | CLUB AREA        | BLOCK C & A | TOTAL    | G.B.U. AREA |         |           |          |
| 1                                                                                    | BASEMENT R/L           | 417.82  | 0                | 10934.37    | 10934.37 | 11412.96    | 0       | 642.49    |          |
| 1                                                                                    | 1 <sup>st</sup> FLTR   | 258.78  | 276.03           | 9713.57     | 9989.60  | 10110.24    | 0       | 426.49    |          |
| 2                                                                                    | 2 <sup>nd</sup> FLTR   | 258.78  | 258.78           | 9358.88     | 9617.66  | 9888.62     | 0       | 388.62    |          |
| 3                                                                                    | 2 <sup>nd</sup> FLTR   | 258.78  | 721.63           | 3331.43     | 4053.06  | 4511.02     | 0       | 388.62    |          |
| 4                                                                                    | 2 <sup>nd</sup> FLTR   | 258.78  | 721.63           | 3331.43     | 4053.06  | 4511.02     | 0       | 388.62    |          |
| 5                                                                                    | 4 <sup>th</sup> FLTR   | 258.78  | 615.07           | 3331.43     | 3946.50  | 4404.46     | 0       | 388.62    |          |
| 6                                                                                    | 5 <sup>th</sup> FLTR   | 258.78  | 615.07           | 3331.43     | 3946.50  | 4404.46     | 0       | 388.62    |          |
| 7                                                                                    | 6 <sup>th</sup> FLTR   | 258.78  | 615.07           | 3331.43     | 3946.50  | 4404.46     | 0       | 388.62    |          |
| 8                                                                                    | 7 <sup>th</sup> FLTR   | 258.78  | 274              | 3331.43     | 3558.67  | 3813.63     | 0       | 388.62    |          |
| 9                                                                                    | 8 <sup>th</sup> FLTR   | 258.78  | 274              | 3331.43     | 3558.67  | 3813.63     | 0       | 388.62    |          |
| 10                                                                                   | 9 <sup>th</sup> FLTR   | 258.78  | 274              | 3331.43     | 3558.67  | 3813.63     | 0       | 388.62    |          |
| 11                                                                                   | 10 <sup>th</sup> FLTR  | 258.78  | 274              | 3331.43     | 3558.67  | 3813.63     | 0       | 388.62    |          |
| 12                                                                                   | 11 <sup>th</sup> FLTR  | 258.78  | 274              | 3331.43     | 3558.67  | 3813.63     | 0       | 388.62    |          |
| 13                                                                                   | 12 <sup>th</sup> FLTR  | 258.78  | 77.79            | 3331.43     | 3409.22  | 3687.18     | 0       | 388.62    |          |
| 14                                                                                   | 13 <sup>th</sup> FLTR  | 258.78  | 77.79            | 3331.43     | 3409.22  | 3687.18     | 0       | 388.62    |          |
| 15                                                                                   | 14 <sup>th</sup> FLTR  | 258.78  | 77.79            | 3331.43     | 3409.22  | 3687.18     | 0       | 388.62    |          |
| 16                                                                                   | 15 <sup>th</sup> FLTR  | 332.32  | 0                | 1617.68     | 1617.68  | 1727.67     | 0       | 236.37    |          |
| 17                                                                                   | 16 <sup>th</sup> FLTR  | 332.32  | 0                | 1617.68     | 1617.68  | 1727.67     | 0       | 236.37    |          |
| 18                                                                                   | 17 <sup>th</sup> FLTR  | 332.32  | 0                | 1617.68     | 1617.68  | 1727.67     | 0       | 236.37    |          |
| 19                                                                                   | 18 <sup>th</sup> FLTR  | 332.32  | 0                | 1617.68     | 1617.68  | 1727.67     | 0       | 236.37    |          |
| MACHINE ROOM/STAIR MUJIBAH, CH/ WATER TANKS ON 15 <sup>th</sup> FLOOR, TERRACE FLOOR |                        |         |                  |             |          |             |         |           |          |
| 20                                                                                   | 15 <sup>th</sup> FLOOR | 4082.45 | 0                | 260.4       | 260.4    | 260.40      | 0       | 100.88    |          |
| 21                                                                                   | 16 <sup>th</sup> FLOOR | 4082.45 | 0                | 73636.76    | 73919.21 | 87493.93    | 6502.53 | 1365.88   |          |
| 22                                                                                   | GRAND TOTAL            | 4884.58 | 7536.76          | 73636.76    | 79719.21 | 87493.93    | 6502.53 | 1562.88   |          |


MEMORANDUM CLUB AREA= 5% OF PROPOSED FLOOR AREAS= 888.88

COMPUTABLE FLOOR AREA= 4884.58+888.88= 5773.46

| AREA STATEMENT                                                     |       | CURB AREA CALCULATION |          |          |  |
|--------------------------------------------------------------------|-------|-----------------------|----------|----------|--|
| FLUT AREA = 27485.75 SQ. MT.                                       | S.NO  | FLUT AREA             | B.U.A.   | G.B.U.A. |  |
| PERMANENT GREEN AREAS = 10.00                                      | 1     | FLUT AREA             | 27485.75 | 27485.75 |  |
| PROPOSED HARD = 48386.38 SQ. MT. (7.70)                            | 2     | FLUT AREA             | 27603    | 27603    |  |
| PROPOSED HARD = 31.50 SQ. MT. 48.38 MT.                            | 3     | 1ST FLOOR             | 686.72   | 686.72   |  |
| PERMANENT GREEN GROUND COVER = 131.31                              | 4     | SECOND FLOOR          | 721.63   | 721.63   |  |
| PROPOSED GROUND COVER = 131.31% OF FLUT AREA (40.05 SQ. MT.)       | 5     | THIRD FLOOR           | 631.79   | 631.79   |  |
| PROPOSED GREEN AREA AT OPEN GROUND = 4.86                          | 6     | FOURTH FLOOR          | 615.07   | 615.07   |  |
| PROPOSED POLYUM GREEN AREA AT OPEN GROUND = 24.33% (40.05) SQ. MT. | 7     | FIFTH FLOOR           | 615.07   | 615.07   |  |
| PROPOSED GREEN AREAS AT OPEN GROUND = 4.86                         | 8     | 6TH FLOOR             | 281.6    | 281.6    |  |
| <b>PAVING CALCULATION</b>                                          | 9     | 7TH FLOOR             | 27.24    | 27.24    |  |
| ROAD PAVING = 14885.87 SQ. MT. (75% CONC. 25% ASPHALT PAVING)      | 10    | EIGHTH FLOOR          | 27.24    | 27.24    |  |
| ROAD PAVING = 14885.87 SQ. MT. (51% CONC. 49% ASPHALT)             | 11    | NINTH FLOOR           | 27.24    | 27.24    |  |
| ROAD PAVING = 14885.87 SQ. MT. (51% CONC. 49% ASPHALT)             | 12    | TENTH FLOOR           | 27.24    | 27.24    |  |
| ROAD PAVING = 14885.87 SQ. MT. (51% CONC. 49% ASPHALT)             | 13    | ELEVENTH FLOOR        | 27.24    | 27.24    |  |
| ROAD PAVING = 14885.87 SQ. MT. (51% CONC. 49% ASPHALT)             | 14    | THIRTEEN FLOOR        | 77.79    | 77.79    |  |
| ROAD PAVING = 14885.87 SQ. MT. (51% CONC. 49% ASPHALT)             | 15    | FOURTEEN FLOOR        | 77.79    | 77.79    |  |
| TOTAL PAVING PROPOSED = 673.14                                     | TOTAL | 4002.45               | 4002.45  |          |  |


| PARKING DETAIL                    |                 |                     |                      |
|-----------------------------------|-----------------|---------------------|----------------------|
| PROVIDED E.C.U. IN BASEMENT FLOOR |                 |                     |                      |
|                                   | SURFACE CARS    | SCOOTERS            | TOTAL E.C.U.         |
| BASEMENT FLOOR                    | 244 CARS        | 217 (72.33 E.C.U.)  | 316.33 E.C.U.        |
| PROVIDED E.C.U. ON STILT FLOOR    |                 |                     |                      |
|                                   | SURFACE CARS    | SCOOTERS            | TOTAL E.C.U.         |
| STILT FLOOR                       | 256 CARS        | 409 (136.33 E.C.U.) | 392.33 E.C.U.        |
| PROVIDED E.C.U. IN OPEN AREA      |                 |                     |                      |
|                                   | SURFACE CARS    | SCOOTERS            | TOTAL E.C.U.         |
| OPEN AREA                         | 165 CARS        | 0 (0 E.C.U.)        | 165.00 E.C.U.        |
| <b>TOTAL</b>                      | <b>665 CARS</b> | <b>626 SCOOTERS</b> | <b>873.66 E.C.U.</b> |

The diagram illustrates a rainwater harvesting system. It features a '1st PIT' containing 'STONE PEBBLES' and an 'IRON JAL' at the top. The ground level is marked as 'GROUND LVL'. A 'MAN HOLE COVER' is positioned above the pits. The '1st PIT' has a width of 1m and a depth of 20m. A '2nd PIT' is located below the first, with a width of 1m and a depth of 1.5m. A 'PERFORATED CASING PIPE' is shown connecting the two pits. A 'BORE WELL' is located to the right of the pits, with a diameter of 30m. The 'GROUND LVL' is also marked on the right side, with an arrow indicating 'EXCESS WATER FLOW'. The total length of the system is 12m.

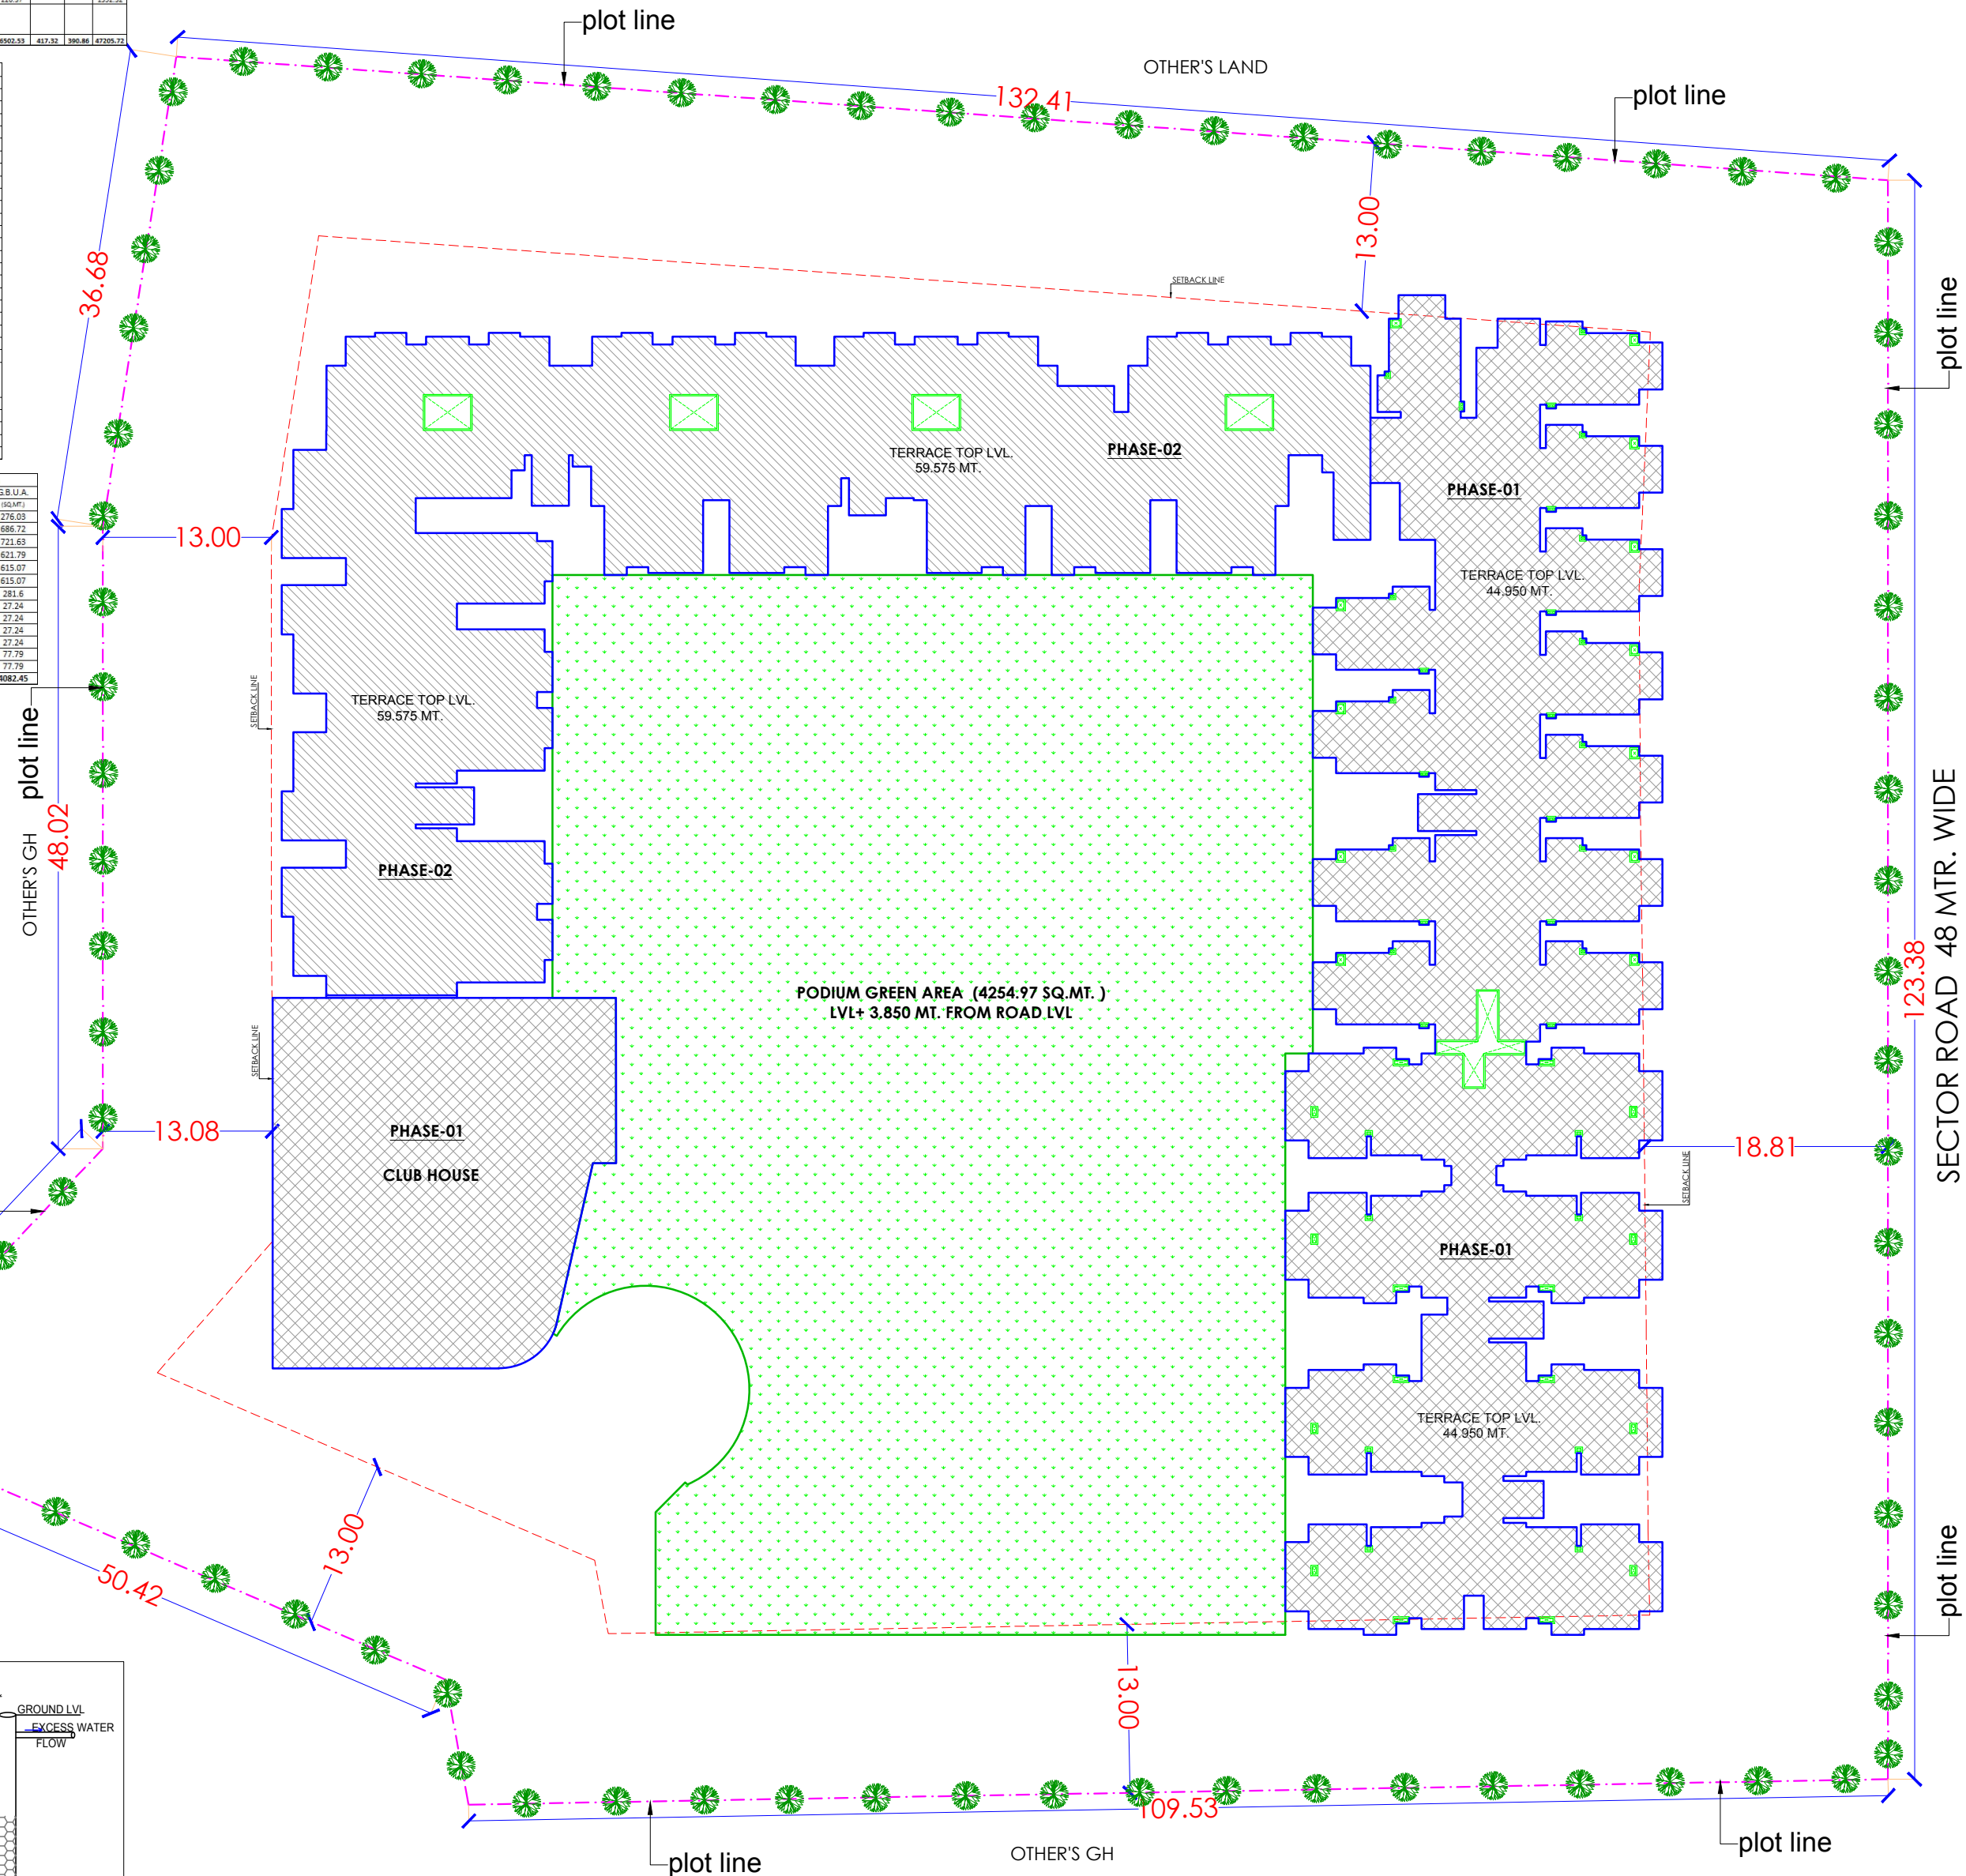


|   |                                                                                                  |
|---|--------------------------------------------------------------------------------------------------|
| SHEET NO. - 01   |                                                                                                  |
| DRAWING TITLE -   |                                                                                                  |
| SITE PLAN   |                                                                                                  |
| <div></div>   |                                                                                                  |
| PROJECT TITLE -   |                                                                                                  |
| PROPOSED GROUP HOUSING<br>KHASRA NO. 240,241,246<br>AT VILLAGE SUKHIYA,<br>TEH.-SANGANER, JAIPUR   |                                                                                                  |
| FOR ABHINANDAN PROJECTS PVT. LTD.<br>ARCHITECT:-   |                                                                                                  |
| ricky mathur & associates<br>architects interior designers planners<br>33, Dhuleshwar Garden,<br>Jaipur, (RAJ.) India. 302 001<br>Tel: 91-141-2362688, 5125444<br>Fax: 91-141-4008700<br>e-mail: ricky@rickymathur.com |                                                                                                  |
|   |                                                                                                  |
| DRAWING TITLE -   |                                                                                                  |
| SITE PLAN   |                                                                                                  |
| SCALE 1 : 200   | DATE AUG_22_2016                                                                                 |
| DEALT BY .....   | STATUS SUBMISSION                                                                                |
| CLIENT'S SIGN.   | ARCHITECT'S SIGN.                                                                                |
| <div></div>   | <div></div>                                                                                      |
| SHEET NO. - 01   | NORTH -<br> |



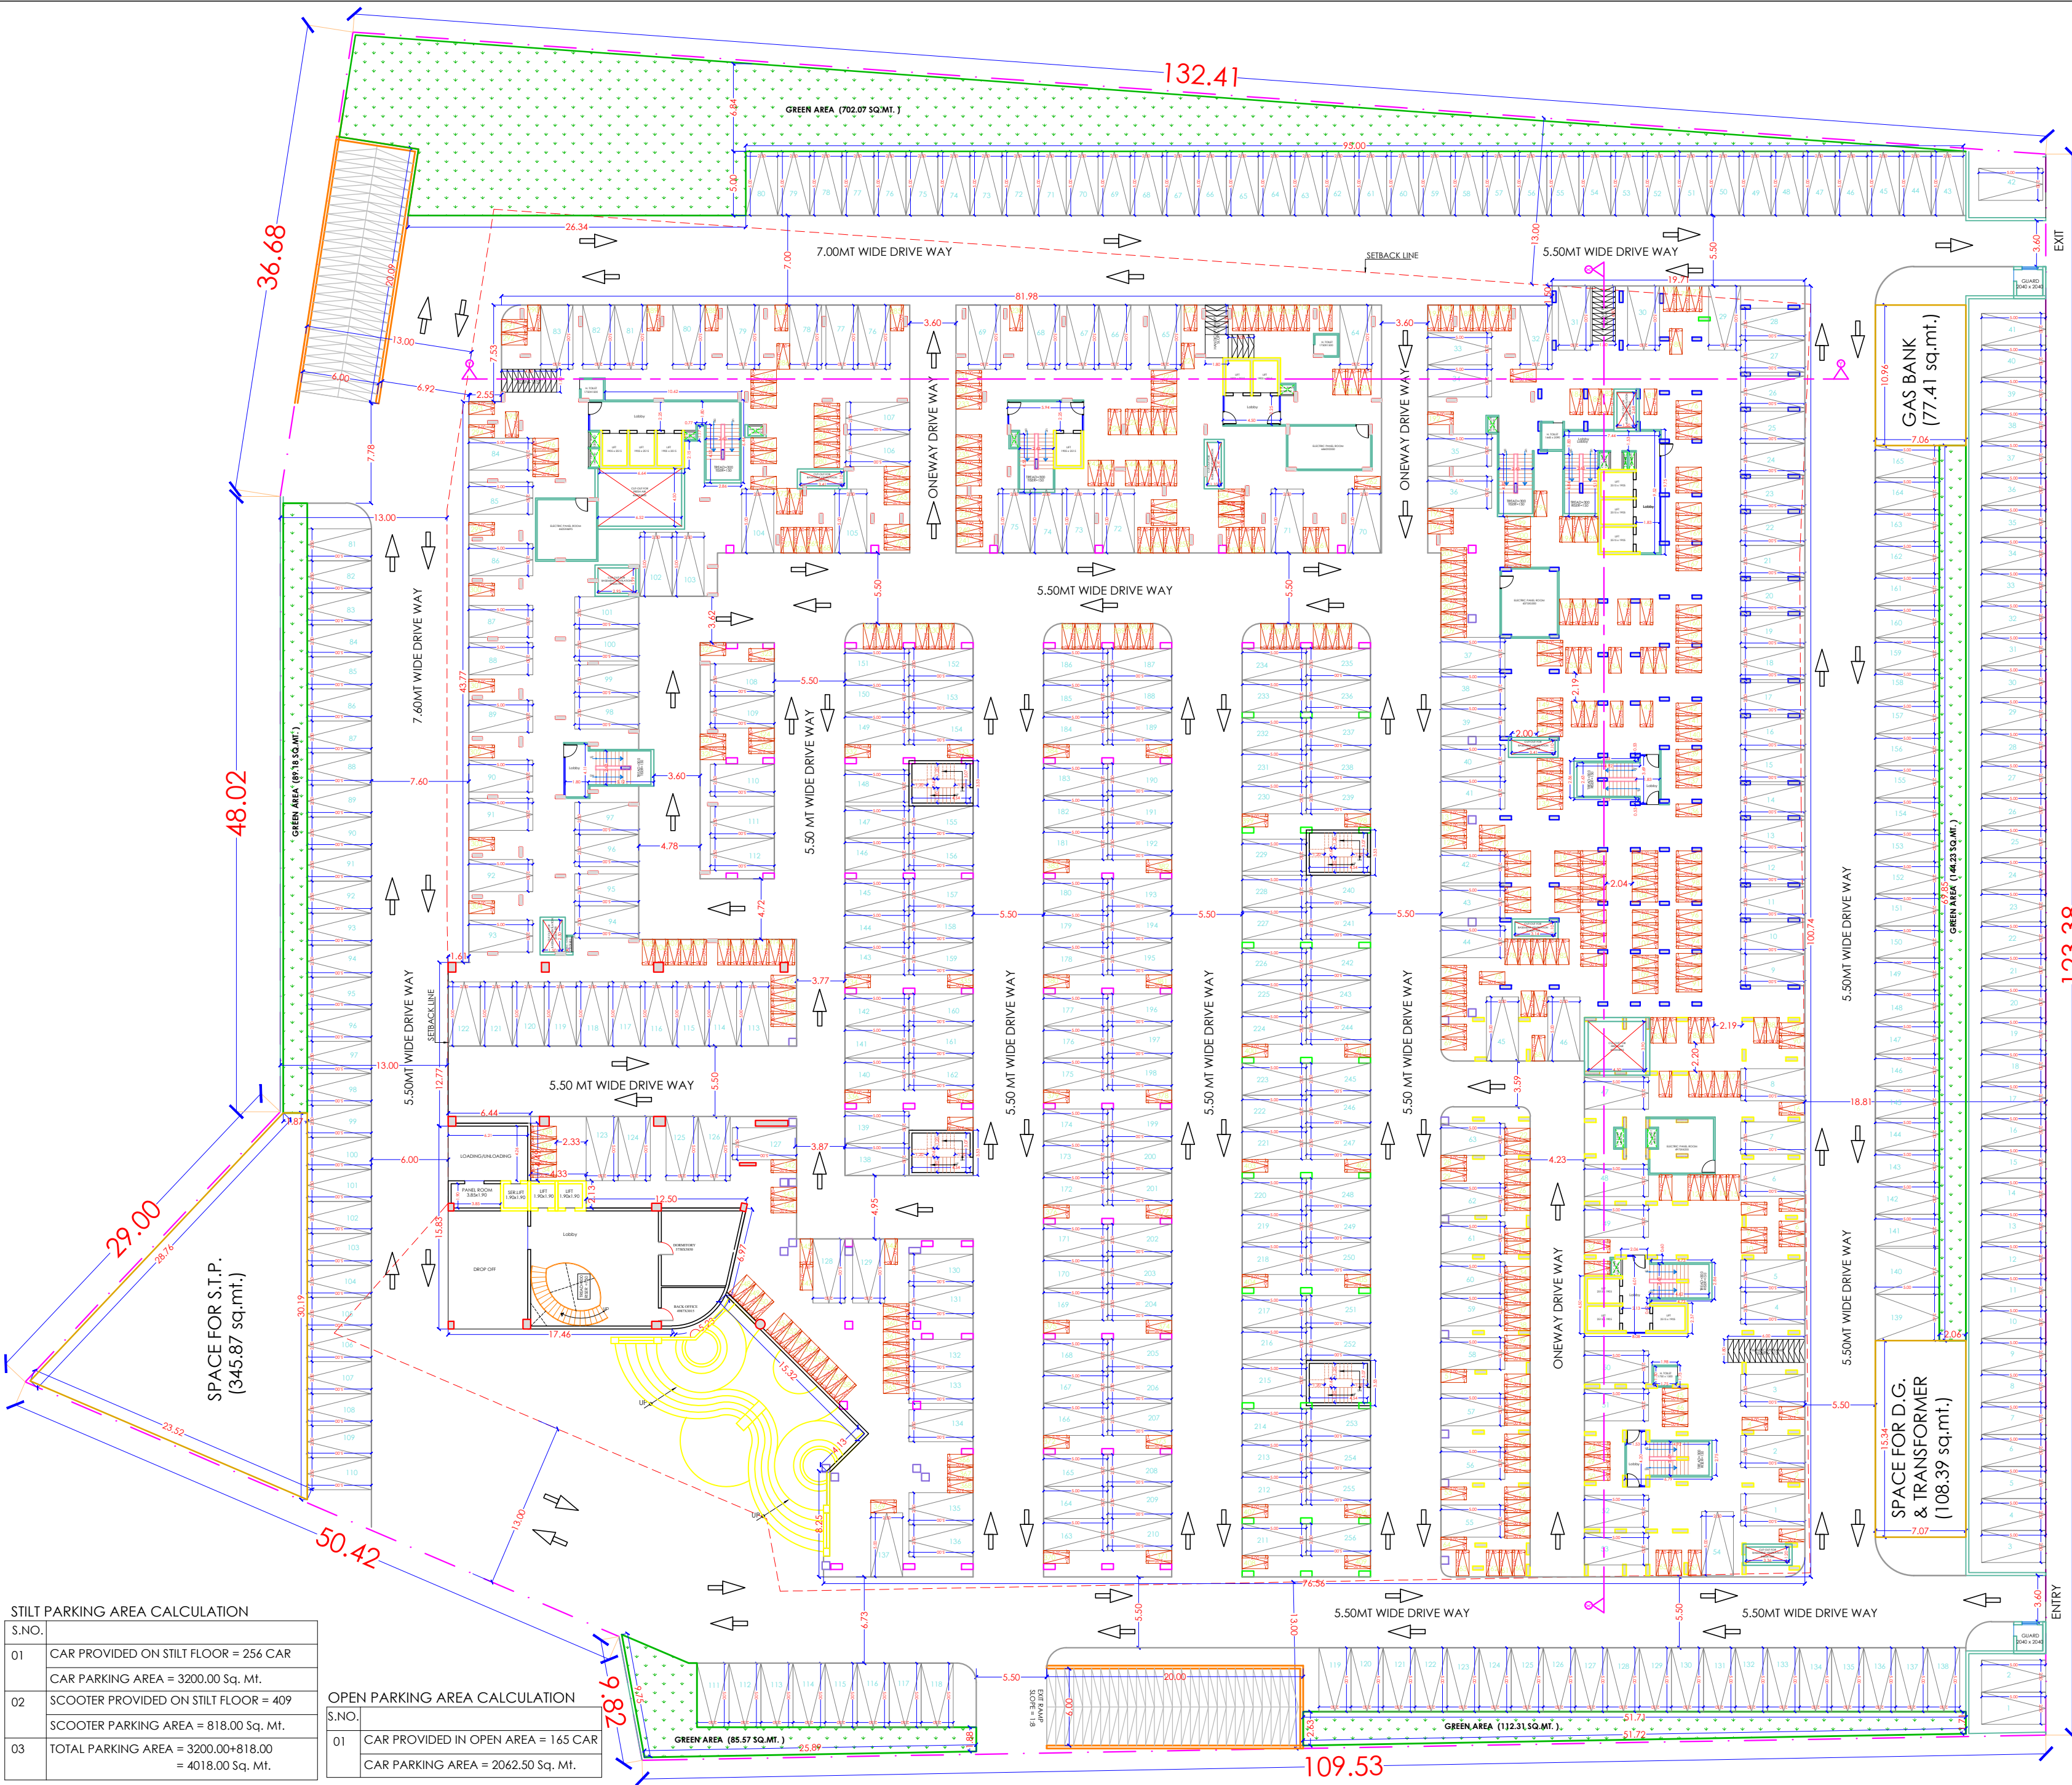


|   |                   |
|---|-------------------|
| SHEET NO. - 02   |                   |
| DRAWING TITLE -   |                   |
| STILT/GROUND FLOOR PLAN   |                   |
| PROJECT TITLE :   |                   |
| PROPOSED GROUP HOUSING<br>KHASRA NO. 240,241,246<br>AT VILLAGE SUKHIYA,<br>TEH.-SANGANER, JAIPUR   |                   |
| FOR ABHINANDAN PROJECTS PVT. LTD.   |                   |
| ARCHITECT:-   |                   |
| ricky mathur & associates<br>architects - interior designers - planners<br>33, Dhuleshwar Garden,<br>Jaipur, (RAJ.) India. 302 001<br>Tel: 91-141-2362688, 5125444<br>Fax: 91-141-4008700<br>e-mail: ricky@rickymathur.com |                   |
| DRAWING TITLE :-   |                   |
| STILT/GROUND FLOOR PLAN   |                   |
| SCALE 1 : 150   | DATE AUG_22_2016  |
| DEALT BY.....   | STATUS SUBMISSION |
| CLIENT'S SIGN.   | ARCHITECT'S SIGN. |
| SHEET NO. - 02   | NORTH -           |

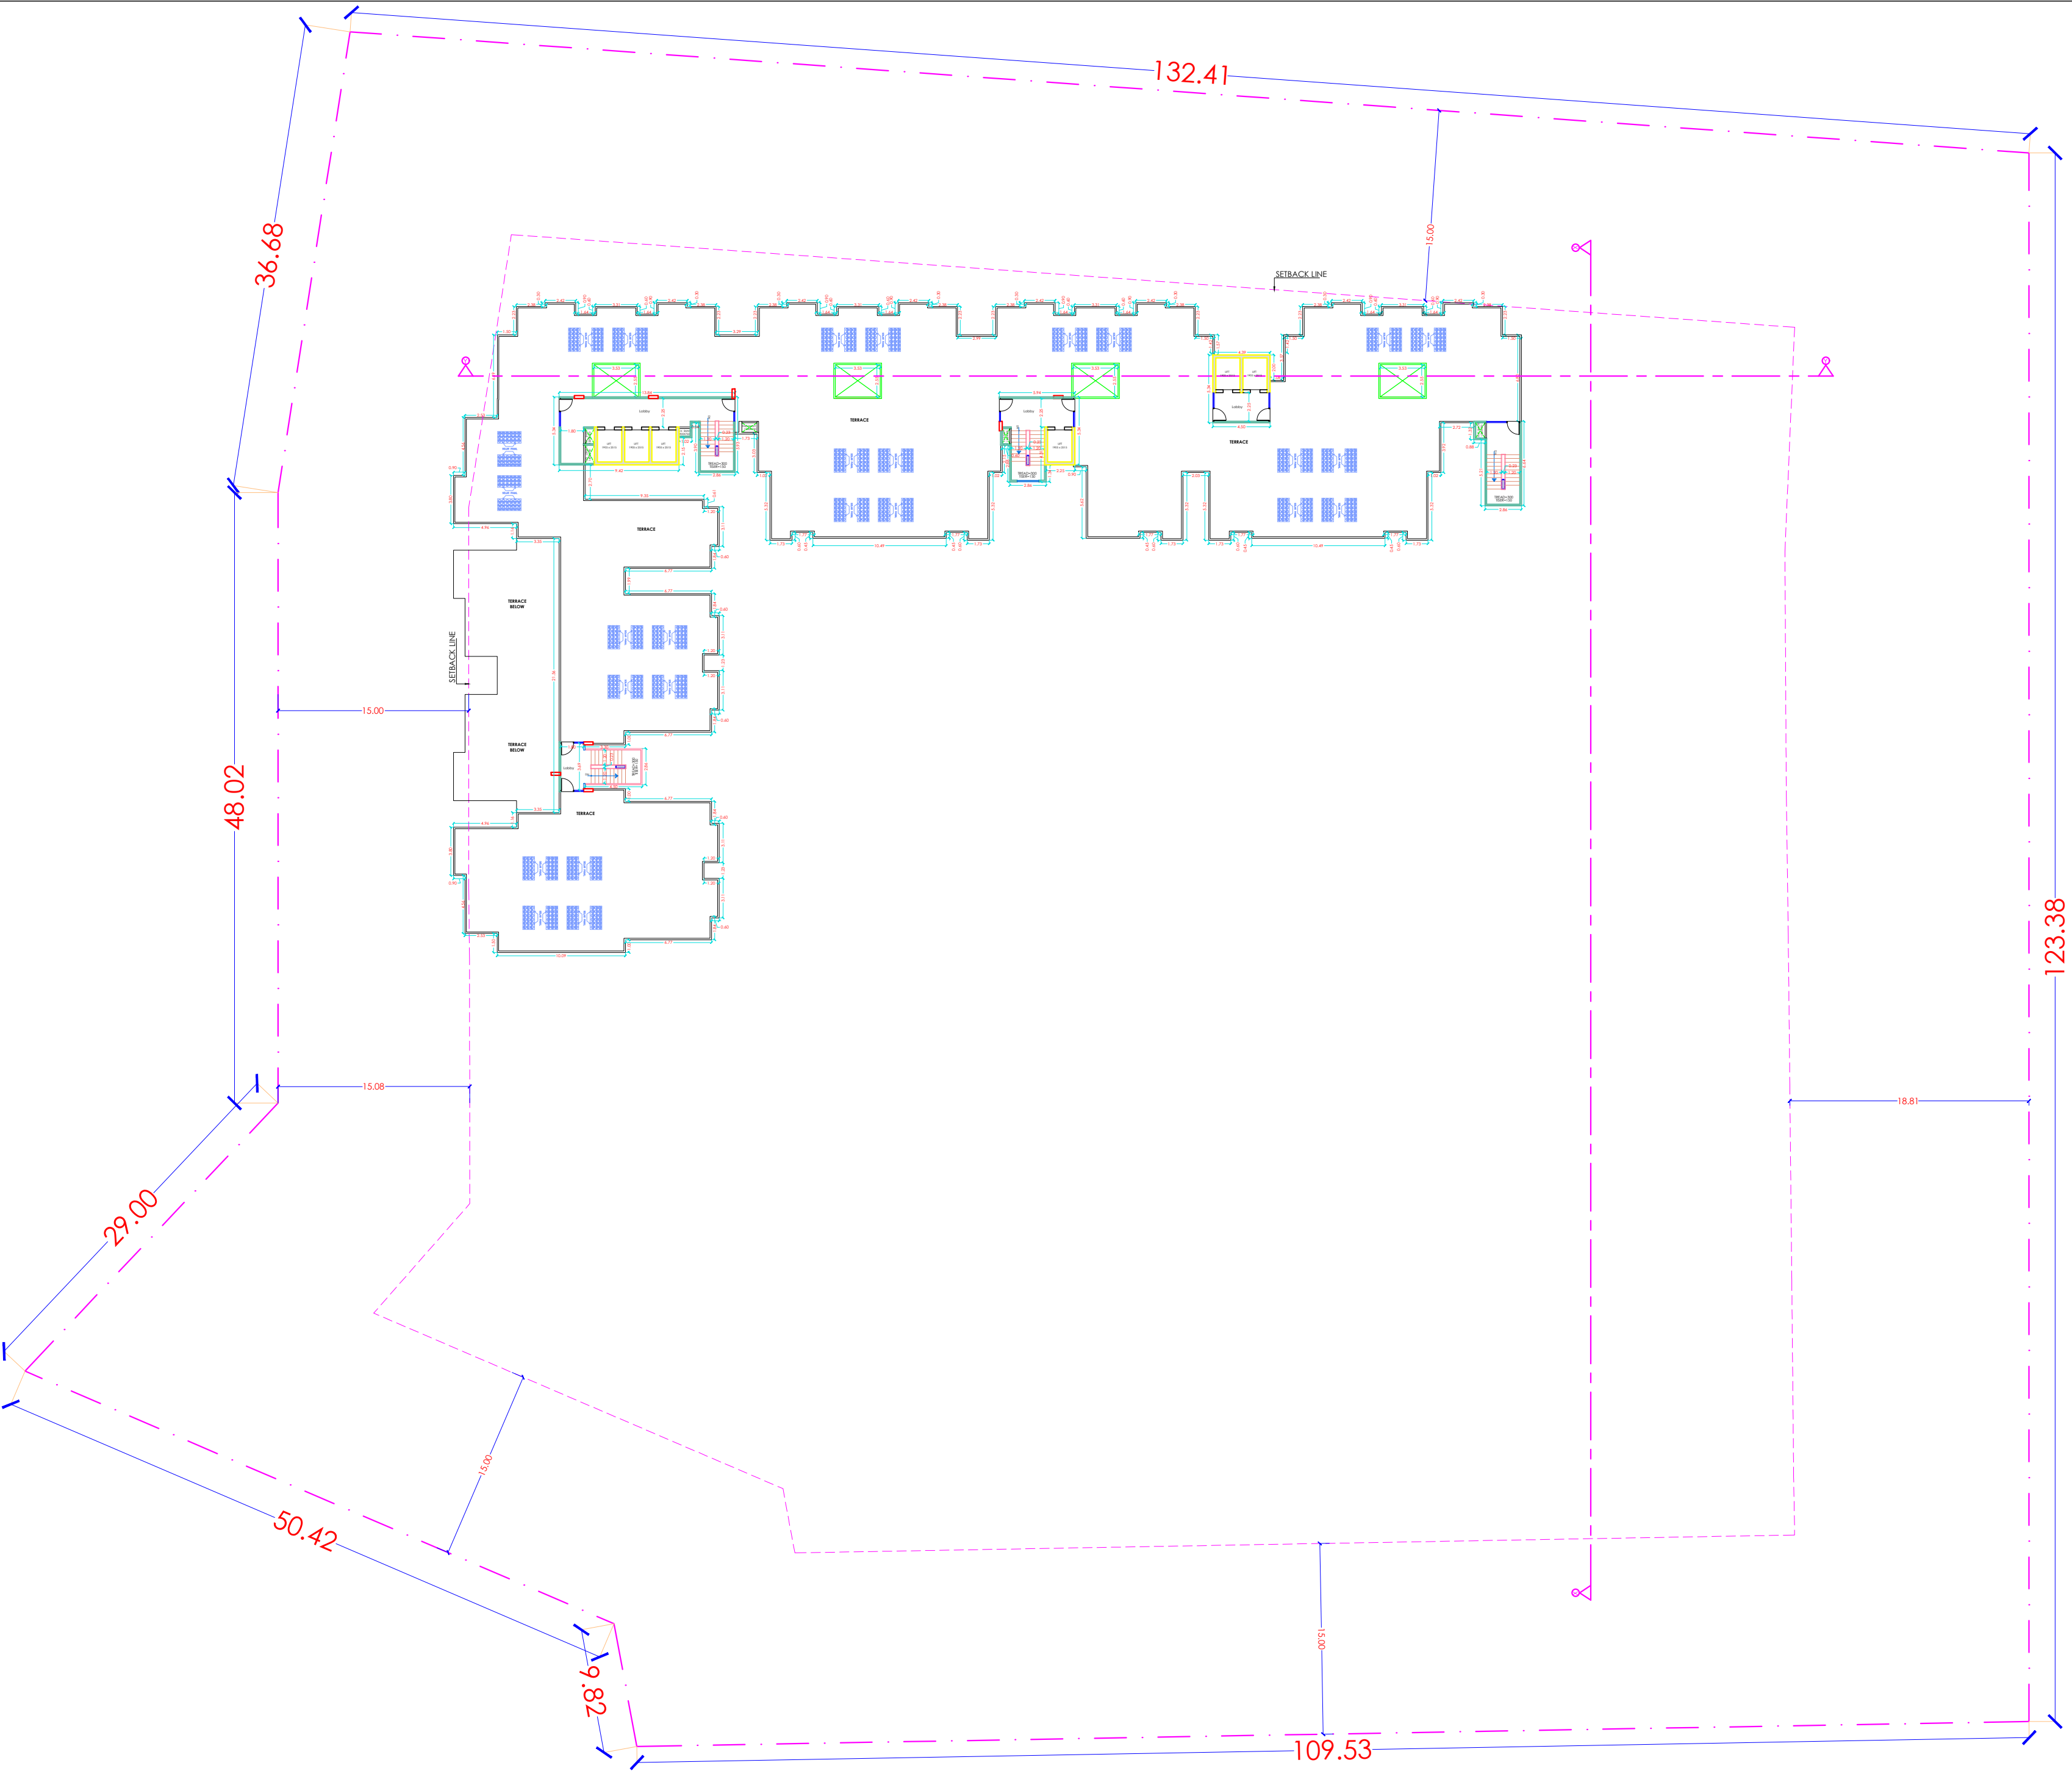


|   |                   |
|---|-------------------|
| SHEET NO. - 08   |                   |
| DRAWING TITLE -   |                   |
| TERRACE FLOOR PLAN   |                   |
| PROJECT TITLE -   |                   |
| PROPOSED GROUP HOUSING<br>KHASRA NO. 240,241,246<br>AT VILLAGE SUKHIYA<br>TEH.-SANGANER, JAIPUR   |                   |
| FOR ABHINANDAN PROJECTS PVT. LTD.   |                   |
| ARCHITECT:-   |                   |
| ricky mathur & associates<br>architects interior designers planners<br>33, Dhulestwar Garden,<br>Jaipur, (RAJ.) India, 302 001<br>Tel: 91-141-2362688, 5125444<br>Fax: 91-141-4008700<br>e-mail: ricky@rickymathur.com |                   |
| DRAWING TITLE:-   |                   |
| TERRACE FLOOR PLAN   |                   |
| SCALE 1:150   | DATE AUG_22_2016  |
| DEALT BY.....   | STATUS SUBMISSION |
| CLIENT'S SIGN.   | ARCHITECT'S SIGN. |
| SHEET NO. - 08   | NORTH -           |



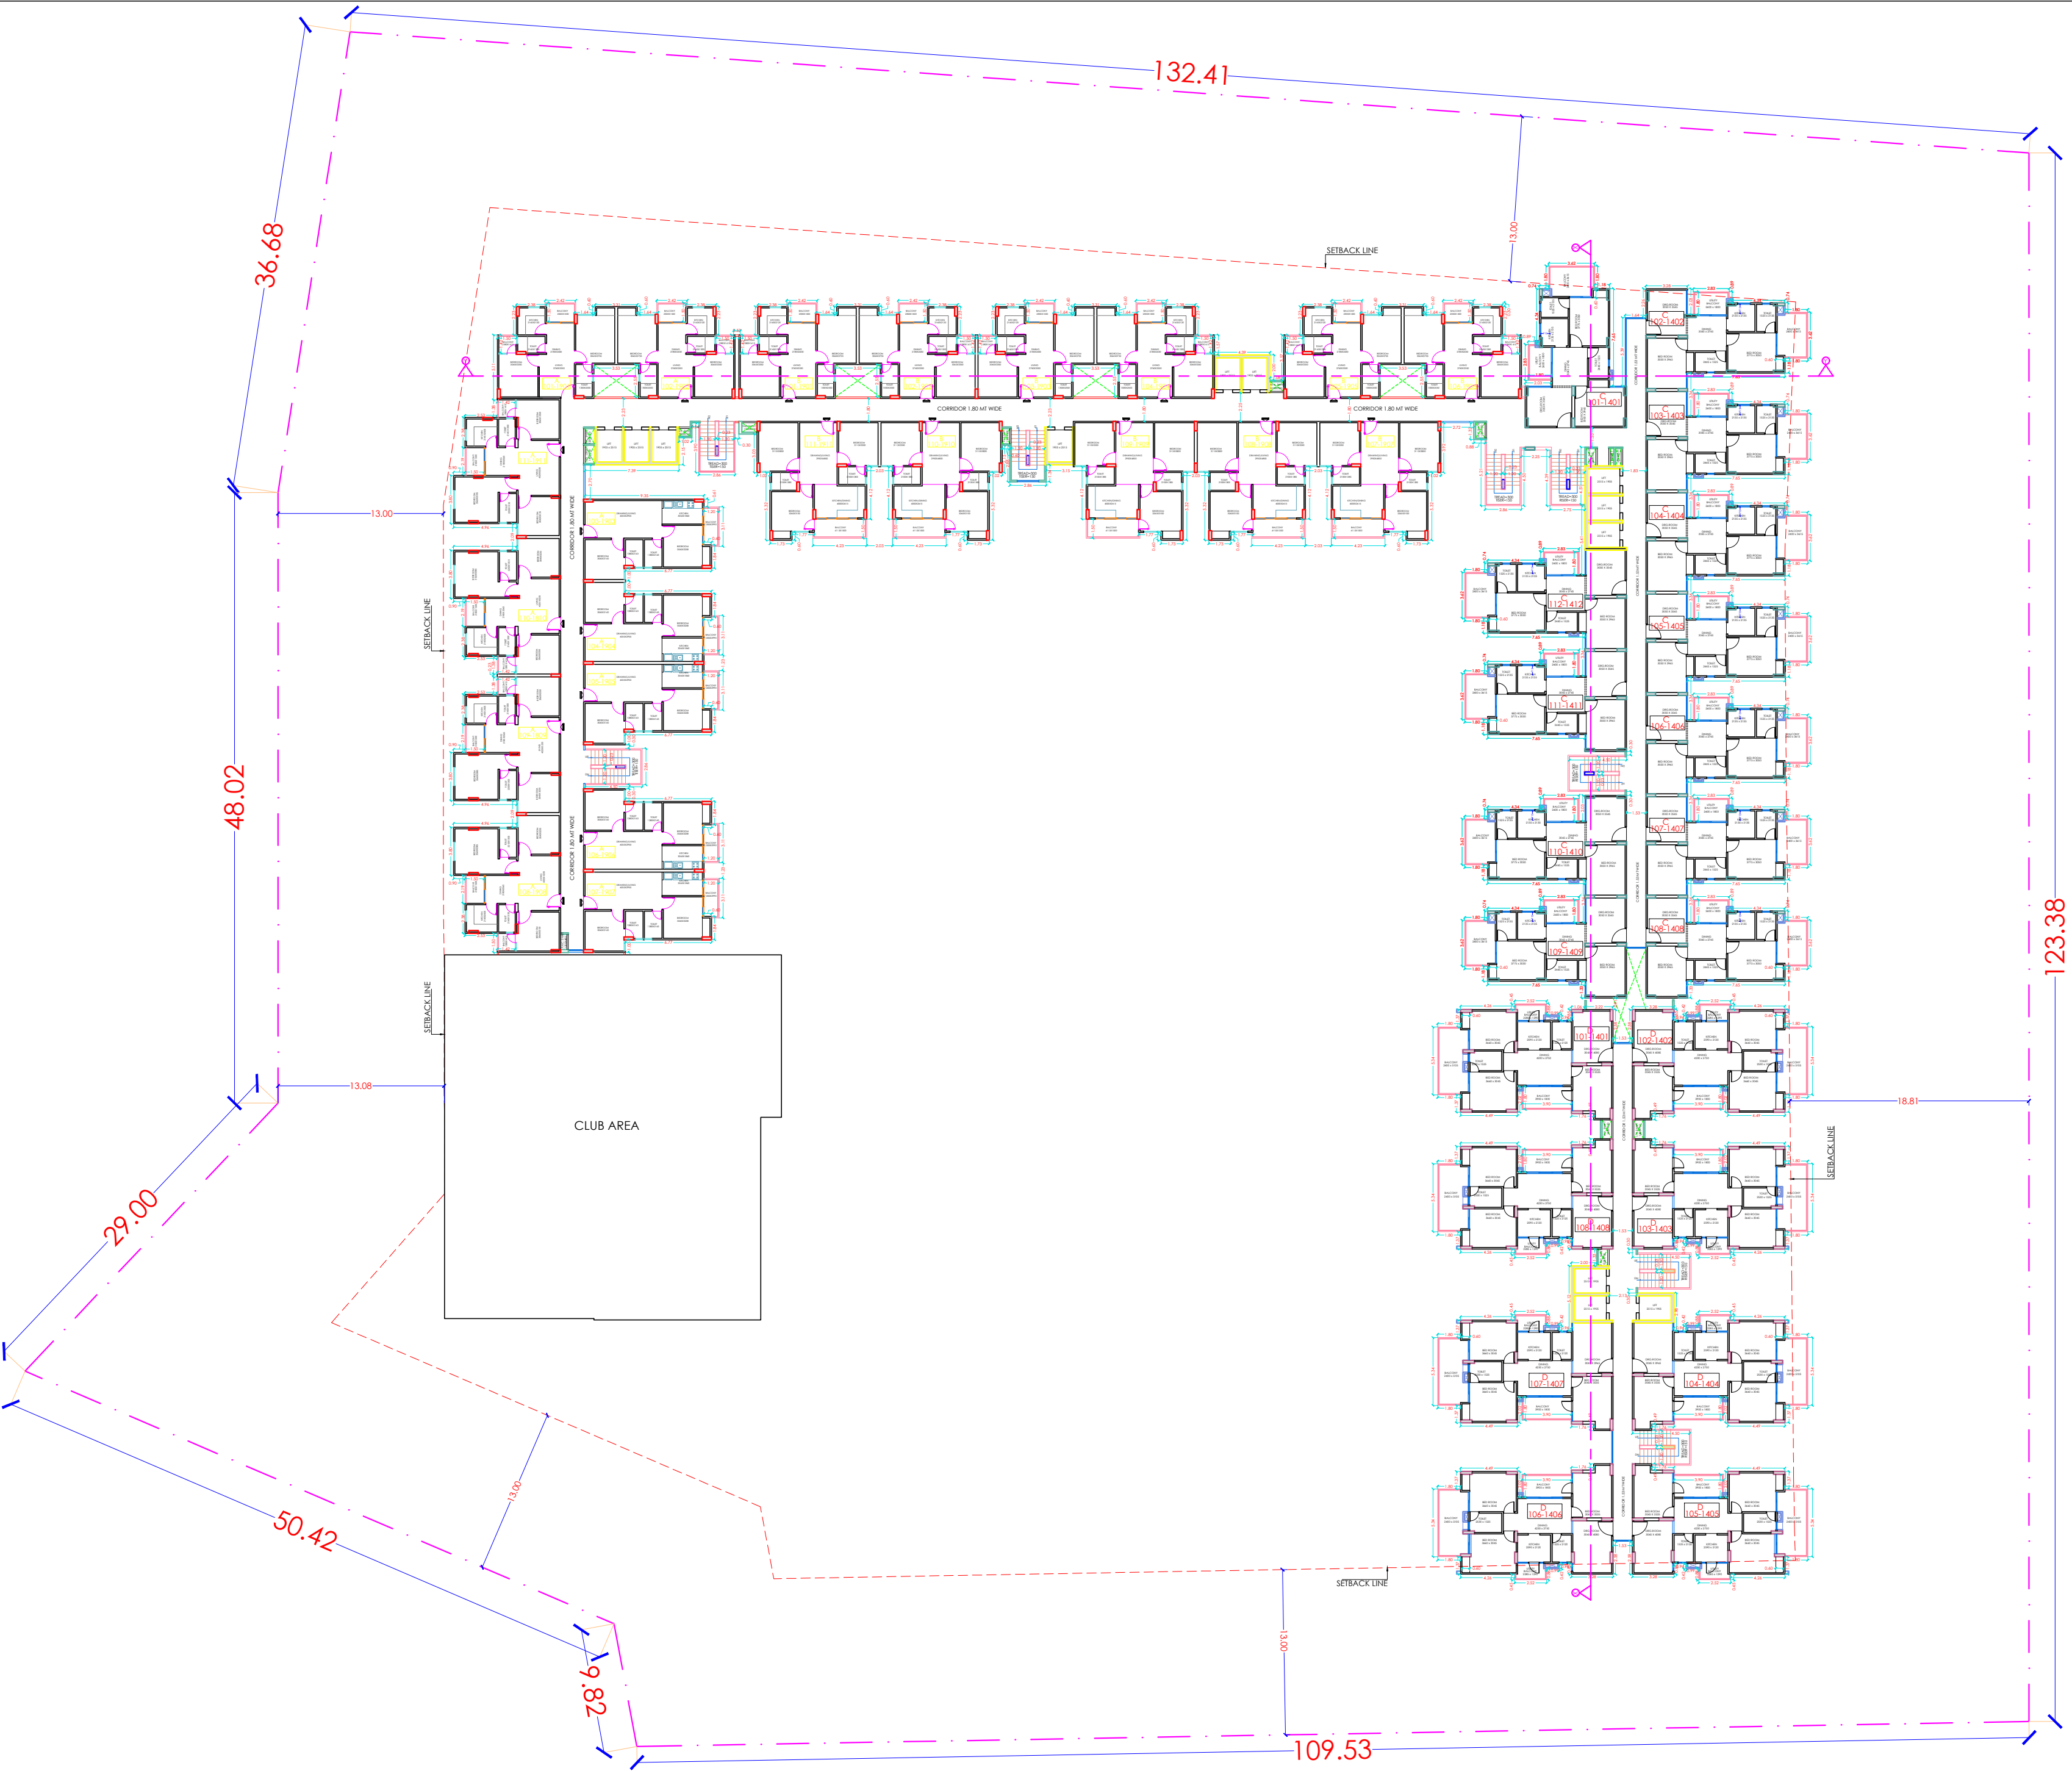

|   |                   |
|---|-------------------|
| SHEET NO. - 05   |                   |
| DRAWING TITLE -   |                   |
| TYPICAL FLOOR PLAN<br>(2nd to 14th FLOOR)   |                   |
| PROJECT TITLE -   |                   |
| PROPOSED GROUP HOUSING<br>KHASRA NO. 240,241,246<br>AT VILLAGE SUKHIYA<br>TEH.-SANGANER, JAIPUR   |                   |
| ARCHITECT -   |                   |
| ricky mathur & associates<br>architects interior designers planners<br>33, Dhuleshwar Garden,<br>Jaipur, (RAJ.) India, 302 001<br>Tel: 91-141-2362688, 5125444<br>Fax: 91-141-4008700<br>e-mail: ricky@rickymathur.com |                   |
| DRAWING TITLE -   |                   |
| TYPICAL FLOOR PLAN<br>(2nd to 14th FLOOR)   |                   |
| SCALE 1:150   | DATE AUG_22_2016  |
| DEALT BY.....   | STATUS SUBMISSION |
| CLIENT'S SIGN.   | ARCHITECT'S SIGN. |
| SHEET NO. - 05   | NORTH -           |



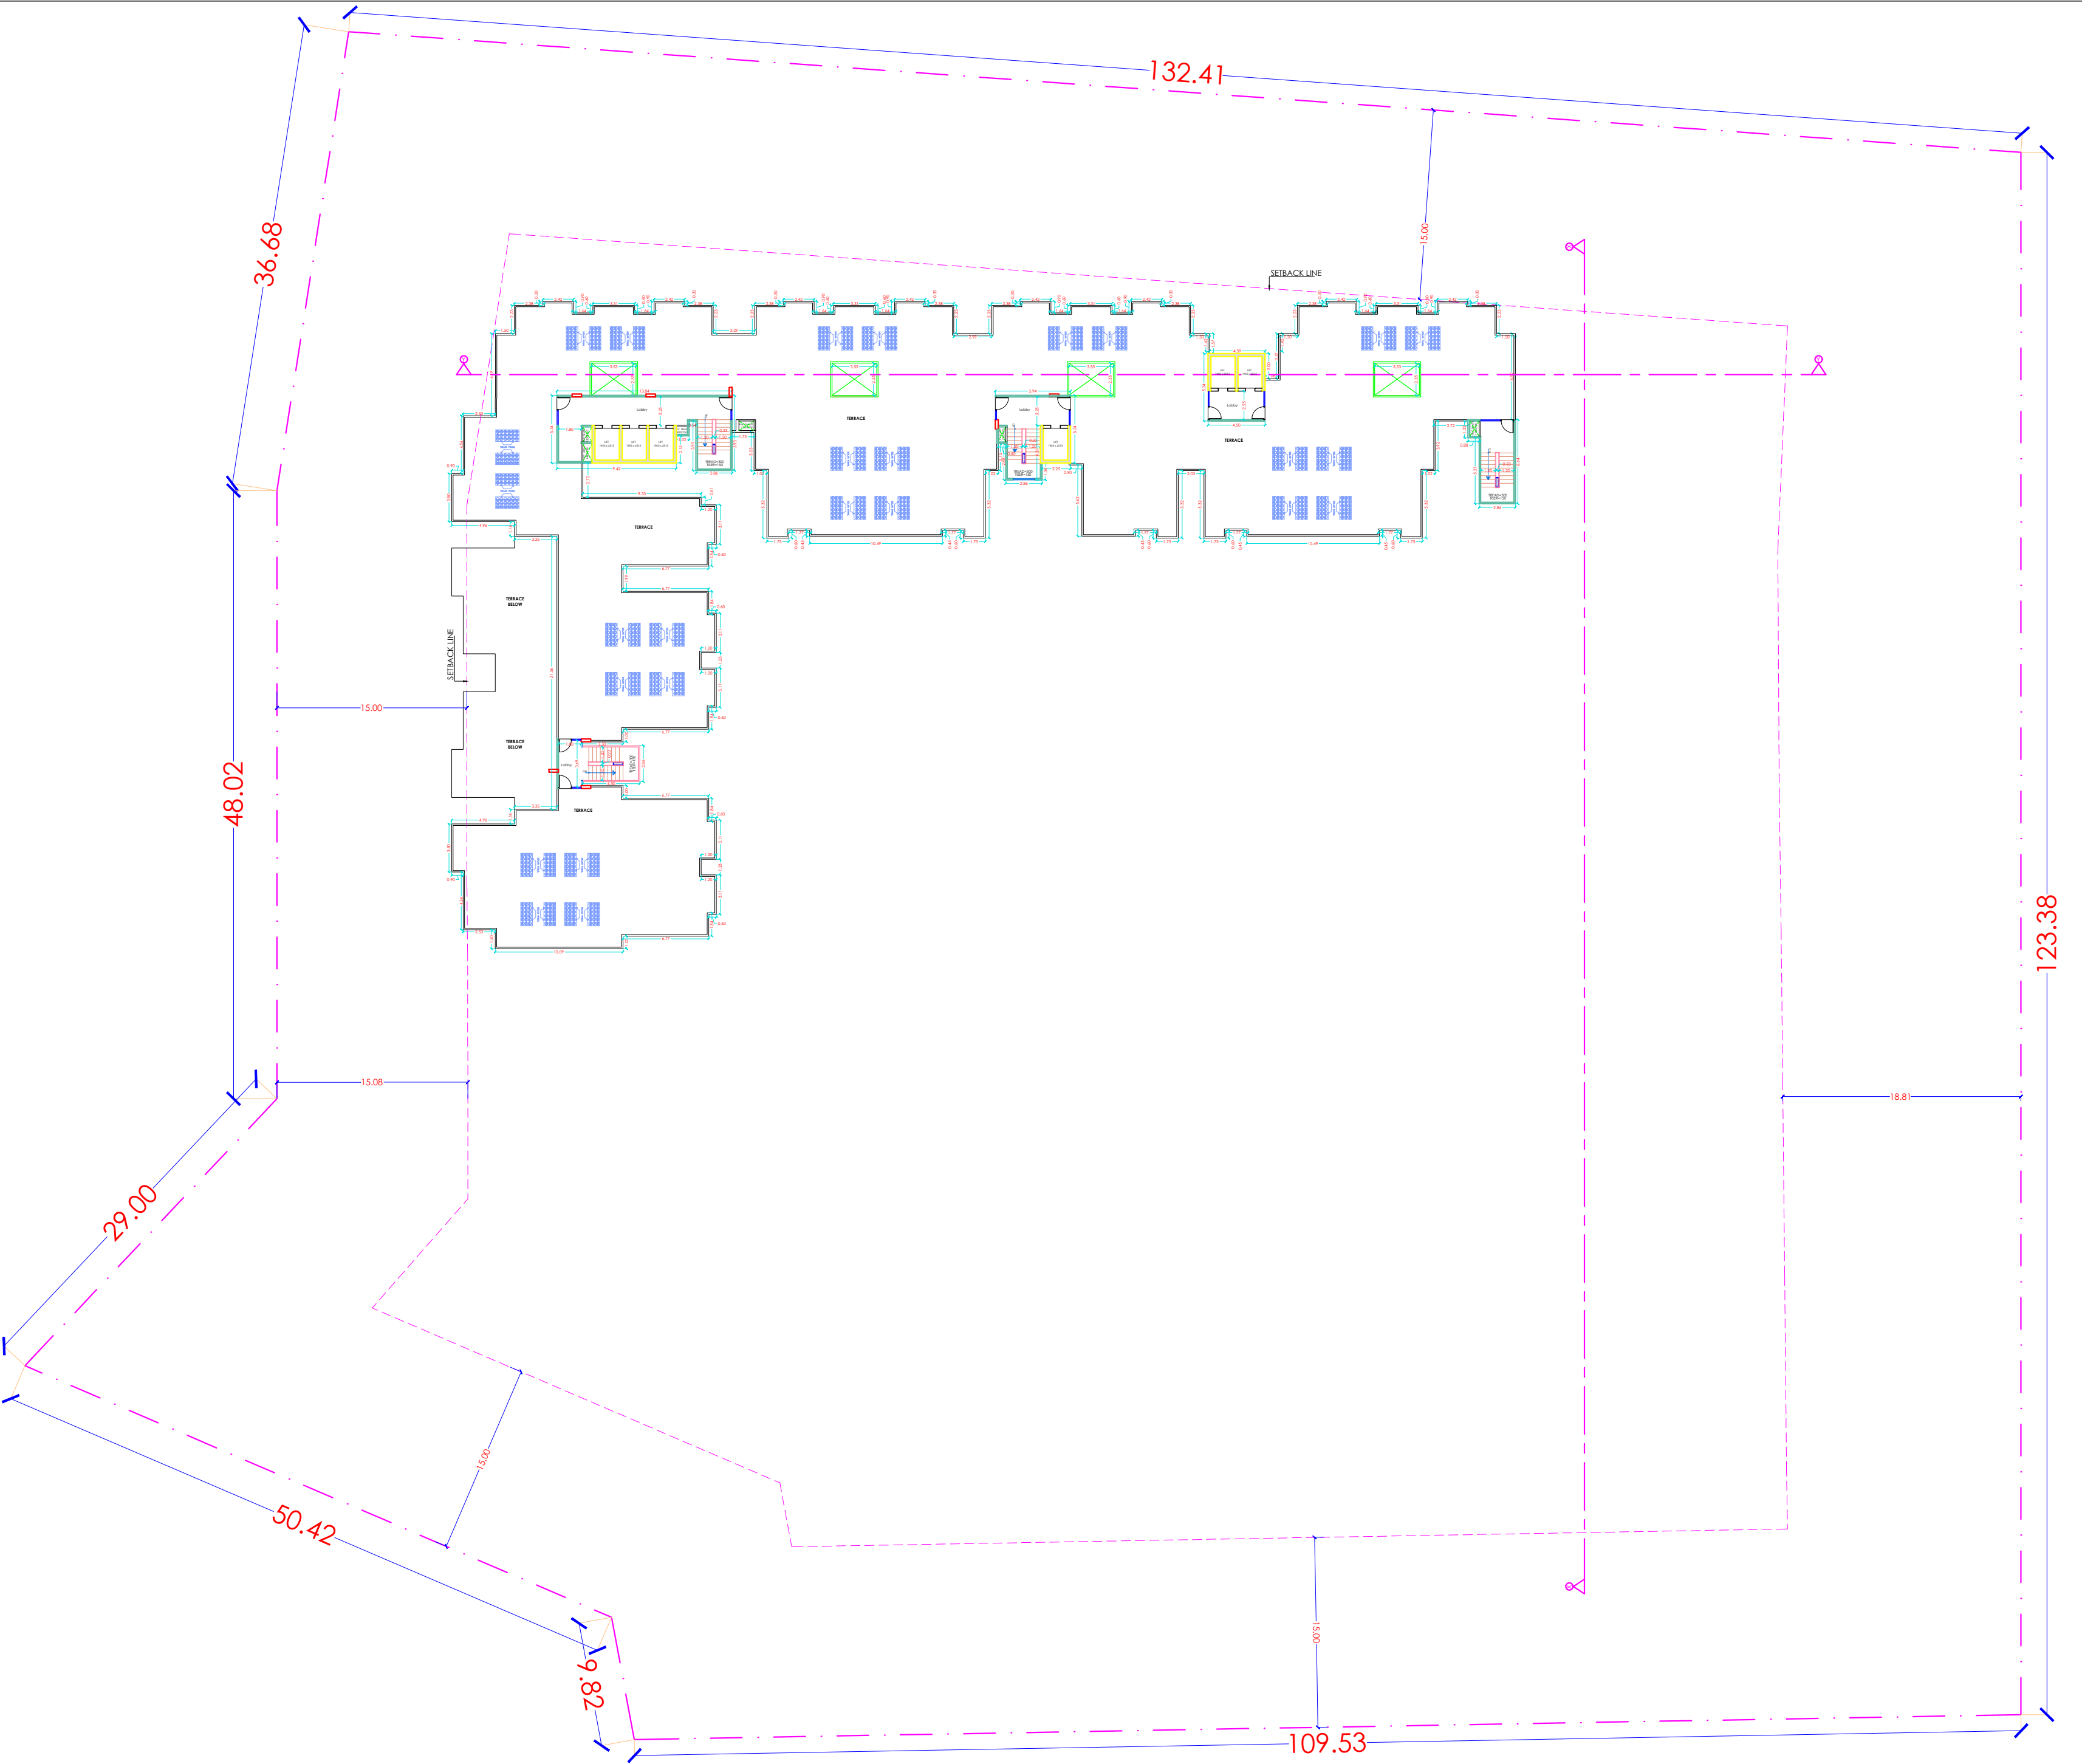

|   |                   |
|---|-------------------|
| SHEET NO. - 08   |                   |
| DRAWING TITLE -   |                   |
| TERRACE FLOOR PLAN   |                   |
| PROJECT TITLE -   |                   |
| PROPOSED GROUP HOUSING<br>KHASRA NO. 240,241,246<br>AT VILLAGE SUKHIYA<br>TEH.-SANGANER, JAIPUR   |                   |
| FOR ABHINANDAN PROJECTS PVT. LTD.   |                   |
| ARCHITECT:-   |                   |
| ricky mathur & associates<br>architects interior designers planners<br>33, Dhulestwar Garden,<br>Jaipur, (RAJ.) India, 302 001<br>Tel: 91-141-2362688, 5125444<br>Fax: 91-141-4008700<br>e-mail: ricky@rickymathur.com |                   |
| DRAWING TITLE:-   |                   |
| TERRACE FLOOR PLAN   |                   |
| SCALE 1:150   | DATE AUG_22_2016  |
| DEALT BY.....   | STATUS SUBMISSION |
| CLIENT'S SIGN.   | ARCHITECT'S SIGN. |
| SHEET NO. - 08   | NORTH -           |