



कार्यालय नगर विकास न्यास, कोटा

क्रमांक :- एफ 7/एस0टी0पी0/2015/2199 - 11

दिनांक :- 5 /11/2015

निमित्त :-


प्रणय इन्फ्राबिल्ड प्रा0लि0 जर्जे निदेशक श्री नीरज सुवालका
प्लॉट नं0 381-382, प्रथम तल, आई.डी.बी.आई. बैंक के ऊपर
रावतभाट रोड़, शॉपिंग सेन्टर, कोटा

विषय :- प्लॉट नं0 B, खसरा नं0 23 (आंशिक) ग्राम कुन्हाड़ी के मानचित्र स्वीकृति के सम्बन्ध में।

उपरोक्त विषयान्तर्गत लेख है कि आपके द्वारा भवन निर्माण स्वीकृति हेतु प्रस्तुत मानचित्रों के परीक्षण उपरांत प्रस्तुत प्रस्ताव पर भवन निर्माण समिति की बैठक दिनांक 15-9-2015 में लिये गए निर्णय के क्रम में निम्न शर्तों के साथ भवन मानचित्र स्वीकृत किये जाते हैं :-

1. यह स्वीकृति राजस्थान भवन विनियम 2013(संशोधित) तथा अन्य सुसंगत विधिक प्रावधानों के अध्याधीन रहेगी तथा इसके प्रावधानों से सुसंगत होने की सीमा तक ही मान्य रहेगी।
2. राजस्थान भवन विनियम 2013(संशोधित) तथा अन्य सुसंगत विधिक प्रावधानों की अपेक्षाओं के अनुरूप भवन निर्माण करने की जिम्मेदारी भवन निर्माण अनुज्ञाधारी की रहेगी। स्वीकृति में किसी भी प्रकार की त्रुटि, भूल एवं लोप को विनियम के प्रावधानों में छूट के रूप में नहीं लिया जा सकेगा। विनियम एवं अन्य सुसंगत विधिक प्रावधानों के अनुसार निर्माण कराने का दायित्व अनुज्ञाधारी का रहेगा। भवन निर्माण स्वीकृति नगर नियोजन शाखा द्वारा प्रकरण का परीक्षण करने पर प्रस्तावानुसार हुई है तथापि यदि स्वीकृति में विनियम एवम् अन्य सुसंगत विधिक प्रावधानों के अनुसार कोई त्रुटि, भूल एवं लोप है, तो भवन निर्माण अनुज्ञाधारी का दायित्व रहेगा कि उस बारे में न्यास कार्यालय का ध्यान आकर्षित करे। त्रुटि, भूल एवं लोप के आधार पर निर्माण मान्य नहीं होगा।
3. प्रस्तुत मानचित्र के अनुसार बेसमेन्ट + स्टिल्ट + 13 मंजिल की स्वीकृति चाही गई है। न्यास की नगर नियोजन शाखा द्वारा आपके प्रस्ताव के परीक्षण उपरांत प्रस्तुत प्रस्तावानुसार कार्यालय आदेश क्रमांक 431-442 दिनांक 27/04/06 व 710-717 दिनांक 21-09-2010 के अनुसार इस समय बेसमेन्ट + स्टिल्ट + प्रथम तल (अधिकतम 8.0 मी. में से) की स्वीकृति भवन विनियम 2013(संशोधित) एवं अन्य सुसंगत प्रावधानों से सुसंगत होने की सीमा तक ही जारी की जा रही है। यह स्वीकृति भवन विनियम 2013(संशोधित) एवं अन्य सुसंगत विधिक प्रावधानों से सुसंगत होने की सीमा तक ही मान्य रहेगी।
4. 20,000 वर्गमीटर क्षेत्रफल से अधिक की स्वीकृति पर्यावरण विभाग की अनापत्ति उपरान्त ही जारी की जावेगी।
5. प्रथम चरण का निर्माण पूर्ण होने पर जांच उपरांत निर्माण स्वीकृत मानचित्र के अनुसार पाये जाने पर द्वितीय चरण में 2.25 एफ0ए0आर0 तक एवं स्टिल्ट + 30 मी. ऊंचाई की स्वीकृति जारी की जावेगी एवं 30 मी. से अधिक ऊंचाई (स्टिल्ट+38.96 मी.) एवं 2.25 से अधिक 3.052 एफ0ए0आर0 तक की निर्माण स्वीकृति राज्य सरकार से स्वीकृति प्राप्त होने के पश्चात् जारी की जावेगी।
6. भवन विनियम 2013 एवं अन्य सुसंगत विधिक प्रावधानों के विरुद्ध निर्माण किये जाने पर "राजस्थान नगर सुधार अधिनियम 1959 की धारा 91 के अन्तर्गत अवैध निर्माण को न्यास द्वारा ध्वस्त किया जा सकेगा, जिसकी समस्त जिम्मेदारी आपकी स्वयं की होगी तथा उक्त कार्यवाही पर किया गया समस्त व्यय आपको ही वहन करना होगा।
7. पार्किंग सम्बन्धी पर्याप्त व्यवस्था मानचित्र में बेसमेन्ट एवं स्टिल्ट तल पर दर्शाये अनुसार की जानी होगी तथा आप द्वारा प्रस्तुत शपथ-पत्र अनुसार पार्किंग क्षेत्र को अन्य उपयोग में नहीं लिया जावेगा।
8. पार्किंग, लिफ्ट इत्यादी सुविधा क्षेत्र के रख-रखाव की व्यवस्था आपको सुनिश्चित करनी होगी।
9. पार्किंग क्षेत्र में कोई निर्माण कार्य नहीं किया जावेगा, न ही इसका बेचान किया जावेगा। इसे पार्किंग हेतु खुला रखा जावेगा। अन्यथा न्यास आपके खर्चे पर बिना पूर्व सूचना पार्किंग क्षेत्र में किये गए निर्माण को ध्वस्त करने के लिये स्वतंत्र होगा।
10. भवन निर्माण के स्ट्रक्चरल डिजाईन की जिम्मेदारी आपके द्वारा नियुक्त वास्तुविद् की होगी। निम्न हस्ताक्षरकर्ता/न्यास किसी भी स्थिति में इसके लिये उत्तरदायी नहीं होगा। निर्माण कार्य अधिकृत वास्तुविद्/अभियन्ता की देख-रेख में करवाया जाना होगा। निर्माण कार्य पूर्ण होने पर सम्बन्धित वास्तुविद् द्वारा प्रमाण-पत्र प्रस्तुत करना होगा एवं दिये गए अण्डरटेकिंग के अनुसार भूकम्प से सुरक्षा हेतु आवश्यक व्यवस्था की जानी होगी।
11. बेसमेन्ट हेतु खुदाई सुरक्षित रूप से की जावेगी, जिससे की आस-पास के भवनों को क्षति होने की आशंका नहीं रहे, तथा आस-पास के लोगों को कोई व्यवधान नहीं हो।
12. यह स्वीकृति भवन निर्माण के लिये दी जा रही है। किसी भी न्यायालय अथवा वाद में इसे भूखण्ड स्वामित्व साक्ष्य के रूप में प्रस्तुत नहीं किया जा सकेगा।
13. निर्माण पश्चात् भवन को उपयोग में लेने से पूर्व नगर निगम से स्थाई अनापत्ति प्रमाण-पत्र प्राप्त कर न्यास से अधिवास प्रमाण-पत्र प्राप्त करना होगा।

14. मानचित्र में दर्शाये अनुसार भूमिगत जलस्तर बढ़ाने हेतु रेनवाटर हारवेस्टिंग व्यवस्था (16 यूनिट) का निर्माण आवश्यक रूप से किया जाना होगा।
15. अनुज्ञा प्राप्ति के दो वर्ष के भीतर अथवा कार्य प्रारंभ करने के छः माह के अन्दर जो भी कम हो, अनुज्ञाधारी को भवन निर्माण कार्य प्रारंभ करने के आशय की सूचना न्यास को देनी होगी।
16. प्लिन्थ लेवल पर निर्माण के पश्चात् न्यास को सूचित करना होगा। न्यास के वरिष्ठ नगर नियोजक द्वारा नियुक्त उप/सहायक नगर नियोजक द्वारा मौके पर निर्माण की जांच उपरान्त प्लिन्थ का निर्माण स्वीकृत मानचित्र एवं भवन विनियम 2013(संशोधित) एवं विधिक अन्य सुसंगत प्रावधानों के अनुसार पाये जाने पर पत्र जारी करने के उपरान्त आगामी निर्माण भवन विनियम 2013 एवं अन्य सुसंगत विधिक प्रावधानों अनुसार किया जा सकेगा।
17. स्वीकृत मानचित्र में दर्शित इन्फोरमल कॉमर्शियल का निर्माण कर न्यास को सूचित करना होगा तथा इस बाबत राज्य सरकार द्वारा 'जनसाथी रोजगार योजना' में निर्धारित नियम/शर्तों की पालना करनी होगी।
18. पर्यावरण की दृष्टि से मानचित्र में दर्शाये अनुसार पेड़ लगाने होंगे। भूखण्ड पर प्रत्येक 100 वर्गमीटर क्षेत्र के लिये कम से कम एक वृक्ष के अनुपात में 6 मीटर से अधिक उंचाई ग्रहण करने वाले वृक्ष लगाने होंगे एवं मानचित्र में दर्शाये अनुसार हरियाली क्षेत्र का आवश्यक रूप से विकास किया जाना होगा।
19. भवन की संरचना, डिजाईन नियमानुसार/विहित अनुसार भूकम्परोधी होना आवश्यक है। इस सम्बन्ध में स्ट्रक्चरल इन्जिनियर से प्रमाण-पत्र प्रस्तुत करना होगा।
20. समय-समय पर राज्य सरकार/न्यास द्वारा जारी नियमों/आदेशों की पालना करनी होगी।
21. राज्य सरकार के पत्र क्रमांक प.10(154)न.वि.वि./3/80 दिनांक 04-11-2008 की पालना की जानी होगी।
22. मानचित्र में दर्शाये गए अनुसार सौर उर्जा का प्रावधान किया जाना होगा।
23. आवेदक मौके पर विहित अनुसार सूचना प्रदर्शित करेगा एवं अभिलेख रखेगा तथा इस स्वीकृति पत्र की प्रति भी रखेगा।
24. सॉलिड वेस्ट डिस्पोजल के लिए प्रत्येक 30 फ्लेट्स/निवास इकाईयों अथवा उसके अंश पर 2 कचरापात्र का प्रावधान आवश्यक होगा, जिसमें एक पात्र 0.67 क्यूबिक मीटर का नॉन बायोडिग्रेडेबल तथा 1.33 क्यूबिक मीटर का दूसरा पात्र बायोडिग्रेडेबल अपशिष्ट हेतु होगा। इन्हें भूतल पर ऐसे स्थान पर रखा जावेगा जहाँ से सफाई कर्मचारी द्वारा आसानी से उठाया जा सके।
25. वर्तमान में सेस हेतु राशि अनुमानित तौर पर ली गई है। यह सेस अधिनियम एवं नियम तथा इस सम्बन्ध में जारी विधिक दिशा-निर्देशों के अनुसार होगी, जिस हेतु आवेदक को अन्तर राशि जमा करानी होगी। आवेदक को सेस अधिनियम एवं नियम तथा इस सम्बन्ध में जारी सुसंगत विधिक प्रावधानों एवं आदेशों के अनुसार समय-समय पर समुचित अधिकारी को सूचना भी प्रस्तुत करनी होगी।
26. उपरोक्त शर्तों की पालना करने तथा भवन में आवश्यक प्रावधान किये जाने पर एवं अधिवास प्रमाण-पत्र जारी होने पर ही अग्निशमन धरोहर राशि, अन्य अमानत राशि की बैंक गारंटी लौटाई जावेगी।

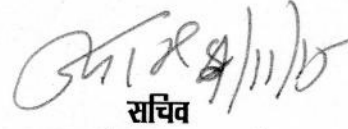
 सचिव

नगर विकास न्यास, कोटा

दिनांक :- /11/2015

क्रमांक :- एफ 7/एस0वी0पी0/2015/

प्रतिलिपि निम्नलिखित को सूचनार्थ एवं आवश्यक कार्यवाही हेतु :-

1. अतिमुख्य अभियंता, नगर विकास न्यास, कोटा।
2. उप सचिव I/II/III, नगर विकास न्यास, कोटा
3. वरिष्ठ नगर नियोजक, नगर विकास न्यास, कोटा
4. संयुक्त श्रम आयुक्त, कलेक्ट्रेट परिसर, कोटा को सूचनार्थ।
5. मुख्य लेखाधिकारी, नगर विकास न्यास, कोटा
6. अधिशाषी अभियन्ता I/II/III/IV को प्रेषित कर लेख है कि सम्बन्धित कनिष्ठ अभियंता को भी समय-समय पर जांच हेतु निर्देशित करे।
7. उप नगर नियोजक, नगर विकास न्यास, कोटा
8. सहायक नगर नियोजक, नगर विकास न्यास, कोटा
9. तहसीलदार प्रथम/द्वितीय/तृतीय, नगर विकास न्यास, कोटा
10. वरिष्ठ विधि अधिकारी, नगर विकास न्यास, कोटा
11. ड्राईंग शाखा को रिकार्ड हेतु।

वरिष्ठ नगर नियोजक
 नगर विकास न्यास, कोटा



कार्यालय नगर विकास न्यास, कोटा

क्रमांक :- एफ 7/डी0टी0पी0/2013/ 822

दिनांक :- 25/09/2013

निमित्त :-

प्रणय इन्फ्राबिल्ड प्रा0लि0

निदेशक,

नीरज सुवालका(मुख्तारआम) श्रीमति सुनीता सुवालका

कुन्हाड़ी, कोटा(राज0)

विषय :- राजस्व ग्राम कुन्हाड़ी के खसरा नं0 23(आंशिक), क्षेत्रफल 11500 वर्गमीटर के ले-आउट प्लान व सम्बन्ध में। (एकल पट्टा, ग्रुप हाउसिंग प्रयोजनार्थ)

प्रसंग :- आपका आवेदन दिनांक 01/03/2011 के सन्दर्भ में।

राज्य सरकार कि अधिसूचना क्रमांक एफ 3 (77)यू.डी.एच./3/2010 दिनांक 28.06.10 द्वारा जारी निजी क्षेत्र में आवासीय, ग्रुप हाउसिंग व अन्य योजनाओं हेतु निती 2010(10 हैक्टेयर से कम) के अन्तर्गत आपके आवेदन के क्रम में ले-आउट प्लान(एकल पट्टा) (ग्रुप हाउसिंग प्रयोजनार्थ) स्वीकृति उपरांत योजना विकसित किये जाने हेतु निम्न शर्तों के साथ जारी किया जा रहा है :-

- 1- अनुमोदित योजना प्लान में उल्लेखित समस्त शर्तों की पालना सुनिश्चित की जानी है।
- 2- नियमानुसार कृषि भूमि रूपान्तरण राशि न्यास कार्यालय में जमा करवानी होगी।
- 3- भूखण्ड पर निर्माण न्यास से नियमानुसार स्वीकृति प्राप्त कर करवाना होगा। भूखण्ड का क्षेत्रफल 500 वर्गमीटर से अधिक होने के कारण नियमानुसार EWS/LIG के आवास का प्रावधान रखा जाना होगा।
- 4- स्वीकृत प्लान अनुसार ही विकास कार्य किये जावेंगे योजना में किसी प्रकार का संशोधन न्यास व पूर्व अनुमति के नहीं किया जा सकेगा।
- 5- रैनवाटर हारवेस्टिंग के लिये व्यवस्था करना अनिवार्य होगी। विकसित की जाने वाली योजना में मास्ट प्लान/सेक्टर प्लान के अनुसार सड़कें, सीवर लाईन, नाले, ओवरहेड, केबल्स आदि के लिये सम्बन्धित संस्था को 'राईट आफ वे' दिया जावेगा।
- 6- स्वीकृत ले-आउट प्लान की प्रति जानकारी हेतु योजना स्थल पर बोर्ड पर लगाई जावे।
- 7- समय-समय पर राज्य सरकार एवं न्यास द्वारा नियमों/शर्तों की पालना करनी होगी।
- 8- टाउनशिप पॉलिसी-2010(संशोधित) में उल्लेखित समस्त शर्तों की पालना करनी होगी।
- 9- उपरोक्तानुसार शर्तों की पालना नहीं होने पर स्वीकृति निरस्त की जा सकेगी।


सचिव

नगर विकास न्यास, कोटा

क्रमांक :- एफ 7/डी0टी0पी0/2013/


दिनांक :- /09/2013

प्रतिलिपि :-

- 1- उप सचिव, नगर विकास न्यास, कोटा।
- 2- अधिशाषी अभियंता() को प्रेषित कर लेख है कि योजना का समय-समय पर मौका निरीक्षण करें एवं समय-समय पर विकास कार्य की जांच कर निर्धारित मानदण्ड अनुसार सुनिश्चिता कर रिपोर्ट प्रस्तुत करें।

सचिव

नगर विकास न्यास, कोटा

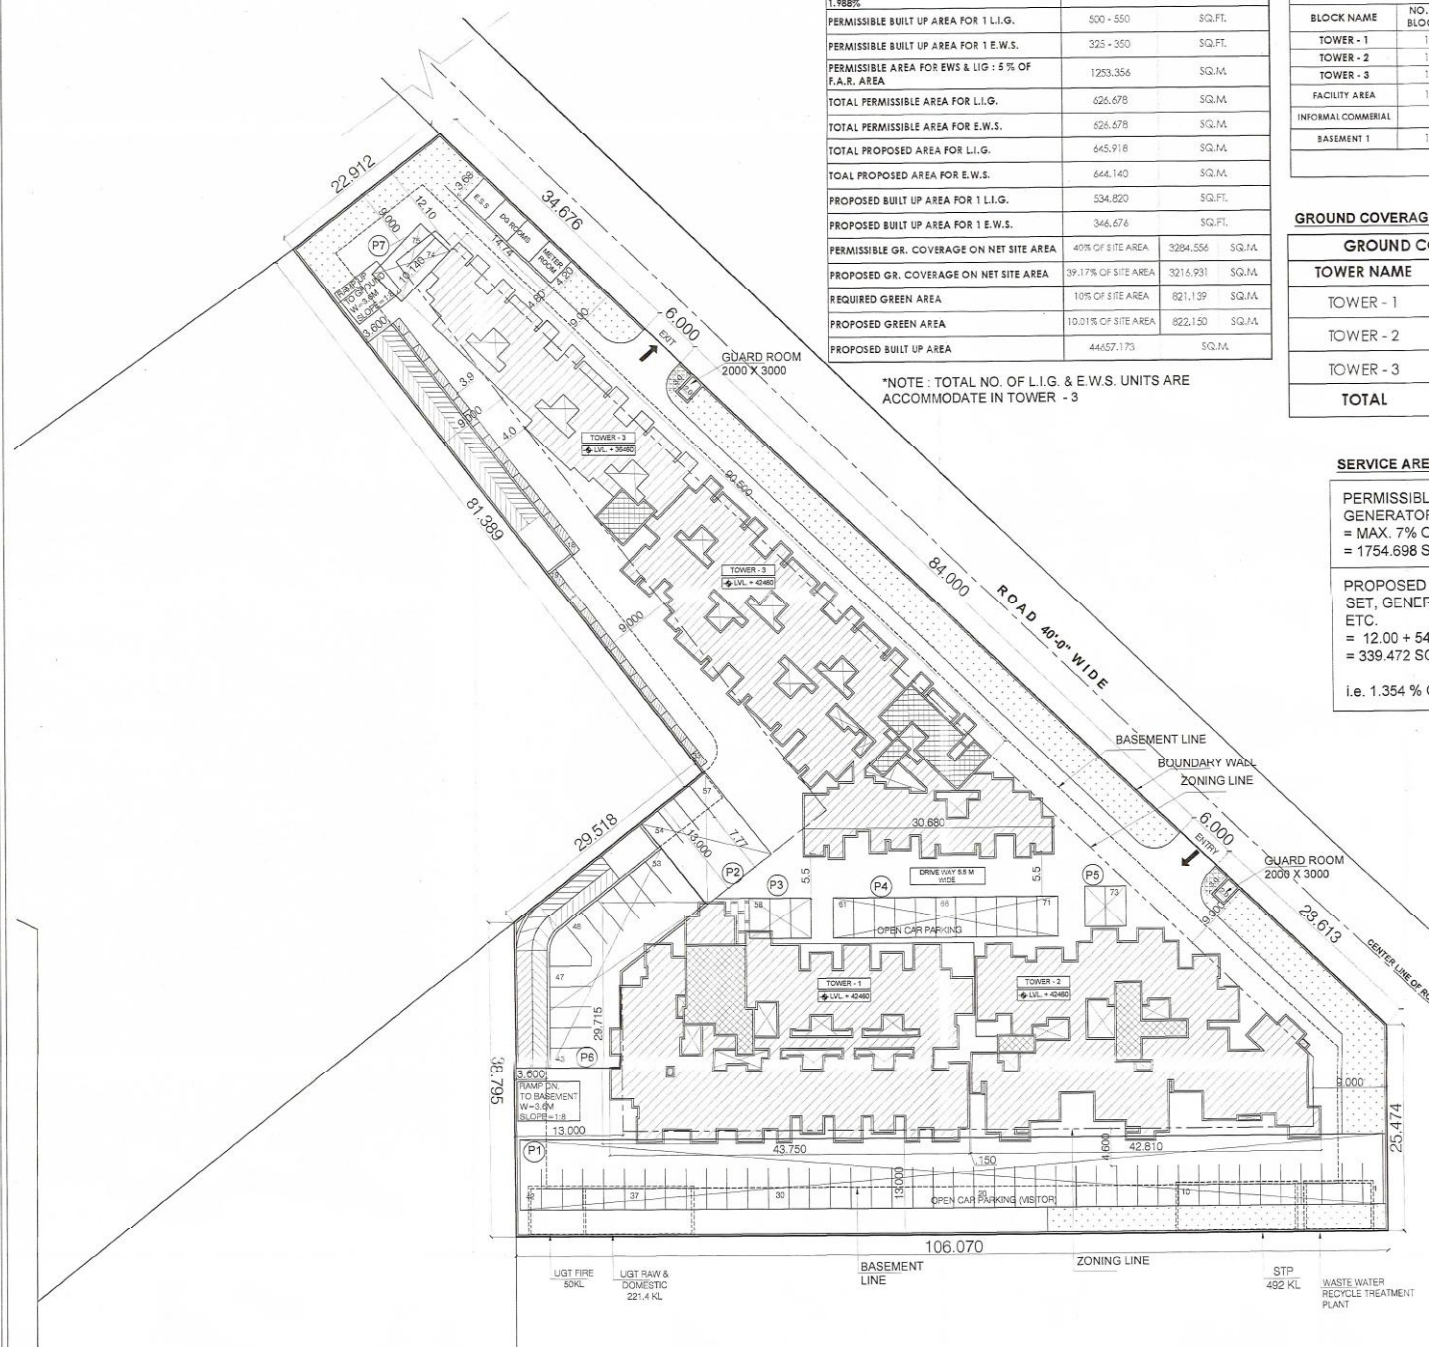

DESCRIPTION	AREA STATEMENT
PLOT AREA	11150.000 SQ.M.
ROAD WIDENING AREA	2938.610 SQ.M.
NET REMAINING SITE AREA	8211.390 SQ.M.
PERMISSIBLE F.A.R. FOR GROUP HOUSING @ 2.25	25067.500 SQ.M.
PROPOSED F.A.R. FOR GROUP HOUSING @ 2.248	25067.121 SQ.M.
PERMISSIBLE FACILITY AREA : 5% OF F.A.R. AREA	1253.356 SQ.M.
PROPOSED FACILITY AREA @ 4.998%	1253.101 SQ.M.
PERMISSIBLE INFORMAL COMMERCIAL AREA : 1.5 - 2 % OF PLINTH AREA	43.220 SQ.M.
PROPOSED INFORMAL COMMERCIAL AREA @ 1.585%	62.868 SQ.M.
PERMISSIBLE BUILT UP AREA FOR 1 L.I.G.	500 - 550 SQ.FT.
PERMISSIBLE BUILT UP AREA FOR 1 E.W.S.	325 - 350 SQ.FT.
PERMISSIBLE AREA FOR EWS & LIG : 5 % OF F.A.R. AREA	1253.356 SQ.M.
TOTAL PERMISSIBLE AREA FOR L.I.G.	625.678 SQ.M.
TOTAL PERMISSIBLE AREA FOR E.W.S.	625.678 SQ.M.
TOTAL PROPOSED AREA FOR L.I.G.	645.918 SQ.M.
TOTAL PROPOSED AREA FOR E.W.S.	644.140 SQ.M.
PROPOSED BUILT UP AREA FOR 1 L.I.G.	534.820 SQ.FT.
PROPOSED BUILT UP AREA FOR 1 E.W.S.	346.674 SQ.FT.
PERMISSIBLE GR. COVERAGE ON NET SITE AREA	40% OF SITE AREA 3284.556 SQ.M.
PROPOSED GR. COVERAGE ON NET SITE AREA	39.17% OF SITE AREA 3214.931 SQ.M.
REQUIRED GREEN AREA	10% OF SITE AREA 821.139 SQ.M.
PROPOSED GREEN AREA	10.01% OF SITE AREA 822.150 SQ.M.
PROPOSED BUILT UP AREA	44657.173 SQ.M.

*NOTE : TOTAL NO. OF L.I.G. & E.W.S. UNITS ARE ACCOMMODATE IN TOWER - 3

F.A.R. CHART

F.A.R. STATEMENT																			TOTAL (SQ.M.)	STORE AREA (SQ.M.)	F.A.R. AREA = TOTAL - STORE AREA (SQ.M.)
BLOCK NAME	NO. OF BLOCKS	HEIGHT	NO. OF UNITS	1ST FL. (SQ.M.)	2ND FL. (SQ.M.)	3RD FL. (SQ.M.)	4TH FL. (SQ.M.)	5TH FL. (SQ.M.)	6TH FL. (SQ.M.)	7TH FL. (SQ.M.)	8TH FL. (SQ.M.)	9TH FL. (SQ.M.)	10 TH FL. (SQ.M.)	11 TH FL. (SQ.M.)	12 TH FL. (SQ.M.)	13 TH FL. (SQ.M.)					
TOWER - 1	1	S+13	221	519.288	619.288	619.288	619.288	619.288	619.288	619.288	619.288	619.288	619.288	619.288	619.288	619.288	8,050.744				
TOWER - 2	1	S+13	104	523.491	523.491	523.491	523.491	523.491	523.491	523.491	523.491	523.491	523.491	523.491	523.491	523.491	6,805.383				
TOWER - 3	1	S+13	331	560.505	560.505	560.505	560.505	560.505	560.505	560.505	560.505	560.505	560.505	560.505	560.505	560.505	10,963.619				
TOTAL	3		656														25,819.746	752.625			

BUILT UP AREA CHART

BUILT UP AREA CALCULATIONS																				
BLOCK NAME	NO. OF BLOCKS	HEIGHT	NO. OF UNITS	GROUND/STILT SQ.M.	1ST FL. (SQ.M.)	2ND FL. (SQ.M.)	3RD FL. (SQ.M.)	4TH FL. (SQ.M.)	5TH FL. (SQ.M.)	6TH FL. (SQ.M.)	7TH FL. (SQ.M.)	8TH FL. (SQ.M.)	9TH FL. (SQ.M.)	10TH FL. (SQ.M.)	11TH FL. (SQ.M.)	12TH FL. (SQ.M.)	13TH FL. (SQ.M.)	MUMTY	M. ROOM + WATER TANK	TOTAL AREA SQ.M.
TOWER - 1	1	S+13	221	69.325	593.738	593.738	593.738	593.738	593.738	593.738	593.738	593.738	593.738	593.738	593.738	593.738	593.738	12.448	88.245	11,788.633
TOWER - 2	1	S+13	104	50.070	725.931	725.931	725.931	725.931	725.931	725.931	725.931	725.931	725.931	725.931	725.931	725.931	725.931	13.940	57.214	9,558.327
TOWER - 3	1	S+13	331	92.958	1,257.457	1,257.457	1,240.837	1,240.837	1,240.837	1,240.837	1,240.837	1,240.837	1,240.837	1,240.837	1,240.837	1,240.837	1,240.837	13.450	107.529	16,051.434
FACILITY AREA	1	G	-----	1,253.101	-----	-----	-----	-----	-----	-----	-----	-----	-----	-----	-----	-----	-----	-----	-----	1,253.101
INFORMAL COMMERCIAL		G	-----	62.868	-----	-----	-----	-----	-----	-----	-----	-----	-----	-----	-----	-----	-----	-----	-----	62.868
BASEMENT 1	1	BASEMENT	-----	3,942.810	-----	-----	-----	-----	-----	-----	-----	-----	-----	-----	-----	-----	-----	-----	-----	5,942.810
TOTAL BUILT UP AREA (SQ.M)																				44,657.173

GROUND COVERAGE CHART

GROUND COVERAGE CALCULATIONS	
TOWER NAME	GROUND COVERAGE (SQ.M.)
TOWER - 1	1,049,218
TOWER - 2	780,351
TOWER - 3	1,387,362
TOTAL	3,216,931

SERVICE AREA CALCULATION:

PERMISSIBLE AREA FOR DG SET, GENERATOR ROOM GUARD ROOM ETC. = MAX. 7% OF F.A.R. = 1754.698 SQ.M.

PROPOSED AREA FOR GUARD ROOM, DG SET, GENERATOR ROOM, UG TANK, STP ETC. = 12.00 + 54.326 + 125.887 + 147.259 SQ.M. = 339.472 SQ.M.

i.e. 1.354 % OF F.A.R.

PARKING CALCULATIONS AS PER AREA REQUIRED :

PROVISION OF PARKING AS PER AREA	
PERMISSIBLE AREA PER E.C.U.	
OPEN	23 SQ.M.
STILT	28 SQ.M.
BASEMENT	32 SQ.M.
E.C.U. IN OPEN AREA	
1486.494 / 23	64.630 SAY 65 E.C.U.
E.C.U. IN STILT AREA	
1572.575 / 26	56.163 SAY 56 E.C.U.
E.C.U. IN BASEMENT AREA	
5787.709 / 32	180.864 SAY 181 E.C.U.
TOTAL E.C.U.	302


PARKING CALCULATIONS AS PER FAR REQUIRED :

PARKING REQUIREMENT		75 SQ.M. PER E.C.U.	
25067.121 / 75	334.228	SAY	334 E.C.U.
25 % PARKING FOR VISITORS			
25 % OF 334 E.C.U.	83.5	SAY	84 E.C.U.
TOTAL PARKING REQUIRED			
334 E.C.U. + 84 E.C.U.	418	E.C.U.	
75 % CARS OF 418 E.C.U.	313.500	SAY	313 E.C.U.
25 % SCOOTERS OF 418 E.C.U.	104.500	SAY	104 E.C.U.
I.E. 104 X 3	312	SCOOTERS	

PARKING CALCULATIONS AS PER UNIT AREA REQUIRED :


PARKING CHART				
UNITS	AREA OF EACH UNIT	NO. OF UNITS	NO. OF CARS	NO. OF SCOOTERS
1 ROOM	39.974	409		409
2 ROOM	48.771	208		208
3 BED	106.037	26	26	
4 BED	160.125	13	13	
TOTAL		656	39	656

PROPOSED PARKING				
	BASEMENT	MECH. PARKING BASEMENT	STILT	OPEN
CAR	124	78	36	75
SCOOTERS	350		146	33
TOTAL				529

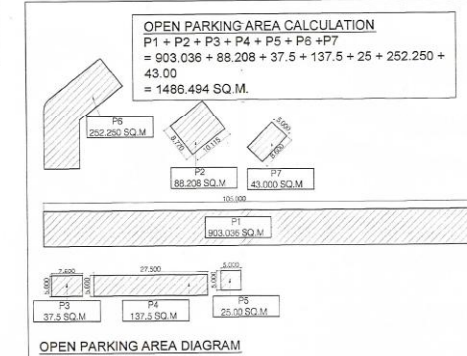

6 कवायल अंश दिनांक 27/04/06 के अनुसार प्रथम चरण में देय 8 मी. ऊंचाई के अन्दरगत प्राप्त एक.ए.आर. 2003.284 SQ.M.

RAINWATER HARVESTING PIT DETAIL

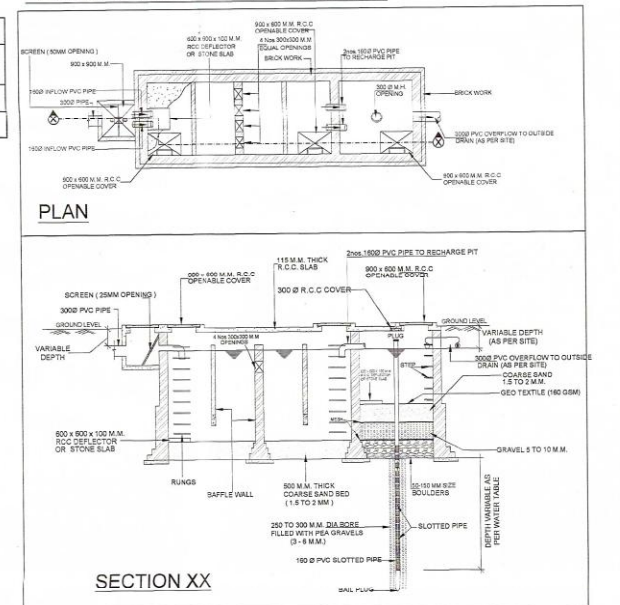

THIS DRG ENCLOSED WITH OUR LETTER No. F/01/18/13-14 DATED 27/04/06

आवश्यक नमूने के लिए प्रेषित किया गया है।

आवश्यक नमूने के लिए प्रेषित किया गया है।

ARCHITECT'S SIGNATURE

ROHIT GARG

CA/94/17868

OWNER'S SIGNATURE

Pranay Infrabuild Pvt. Ltd.

Neeraj Suwalka S/o. Girraj Prasad Suwalka

Director

NAME OF OWNERS

Pranay Infrabuild Pvt. Ltd.

Neeraj Suwalka S/o. Girraj Prasad Suwalka

Director

PROJECT TITLE

PROPOSED GROUP HOUSING SCHEME AT PLOT NO. B, KHASRA NO. 23, VILLAGE KUNHADI, TEHSIL LADPURA, DIST. KOTA, RAJASTHAN

DRAWING TITLE (SUBMISSION DRAWING)

LAYOUT PLAN

SCALE - 1 : 300

DATE - AUGUST, 2015

DRAWN - PRIYANKA

CHECKED - PRIYANKA

DRG. NO.

D1





R.K. & ASSOCIATES

Architects, Engineers & Planners

E-31, GREEN PARK MAIN, NEW DELHI - 110015, INDIA

Ph: 2654-3198, 2651-0741, 2654-7357

Fax: (011) 2658-2540 E-mail: rka.associates@gmail.com

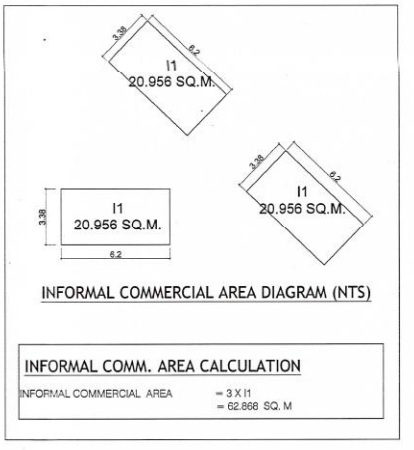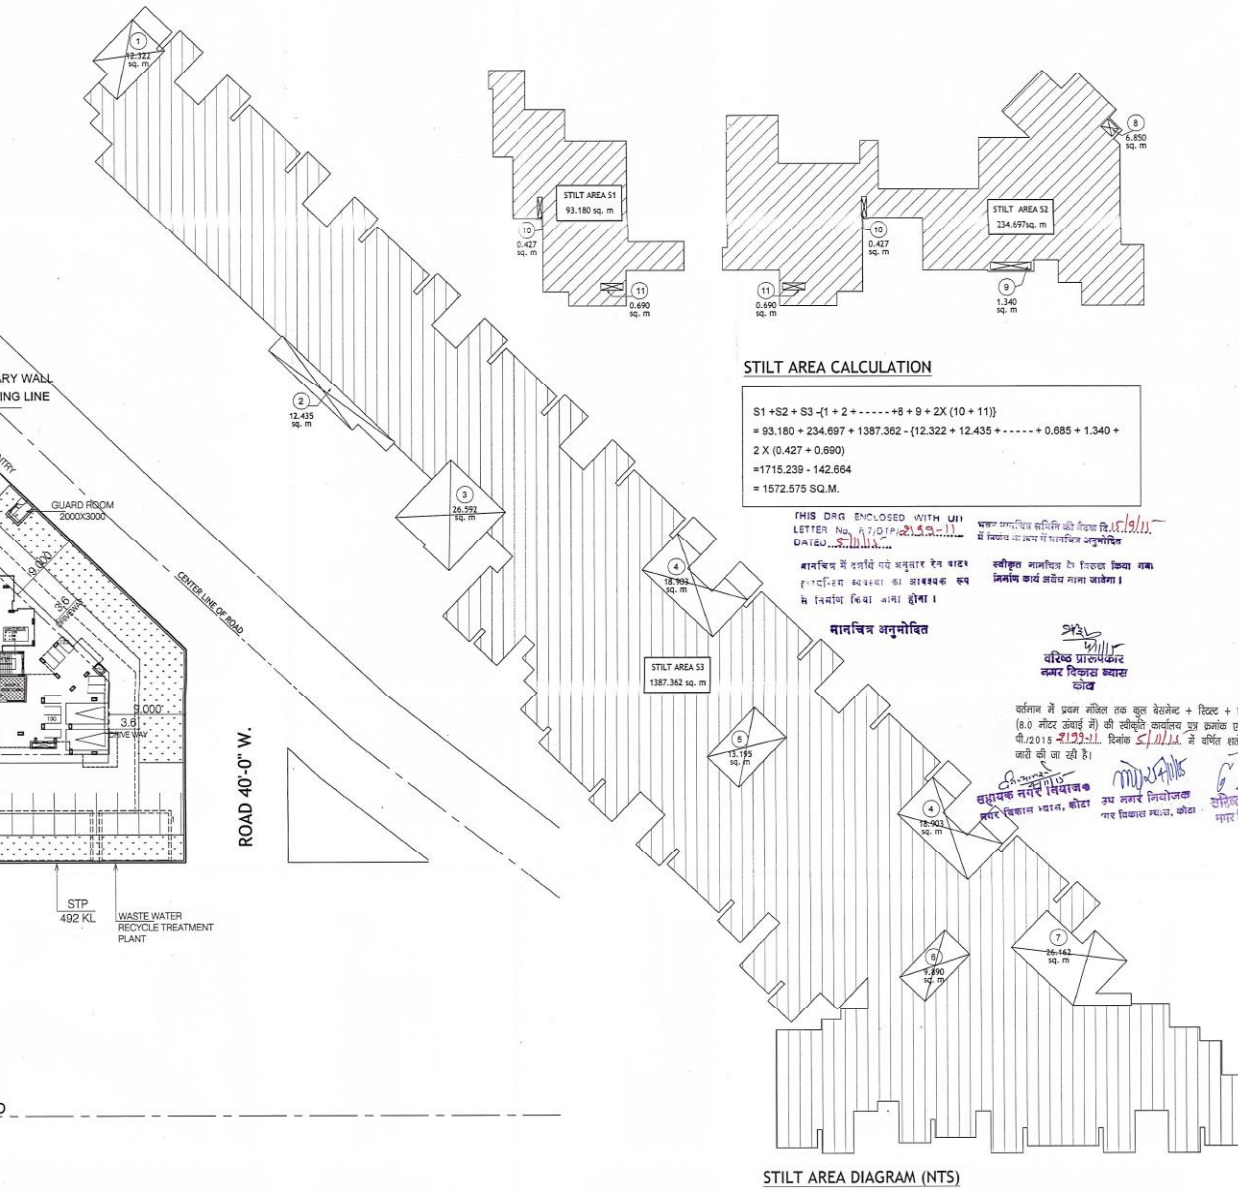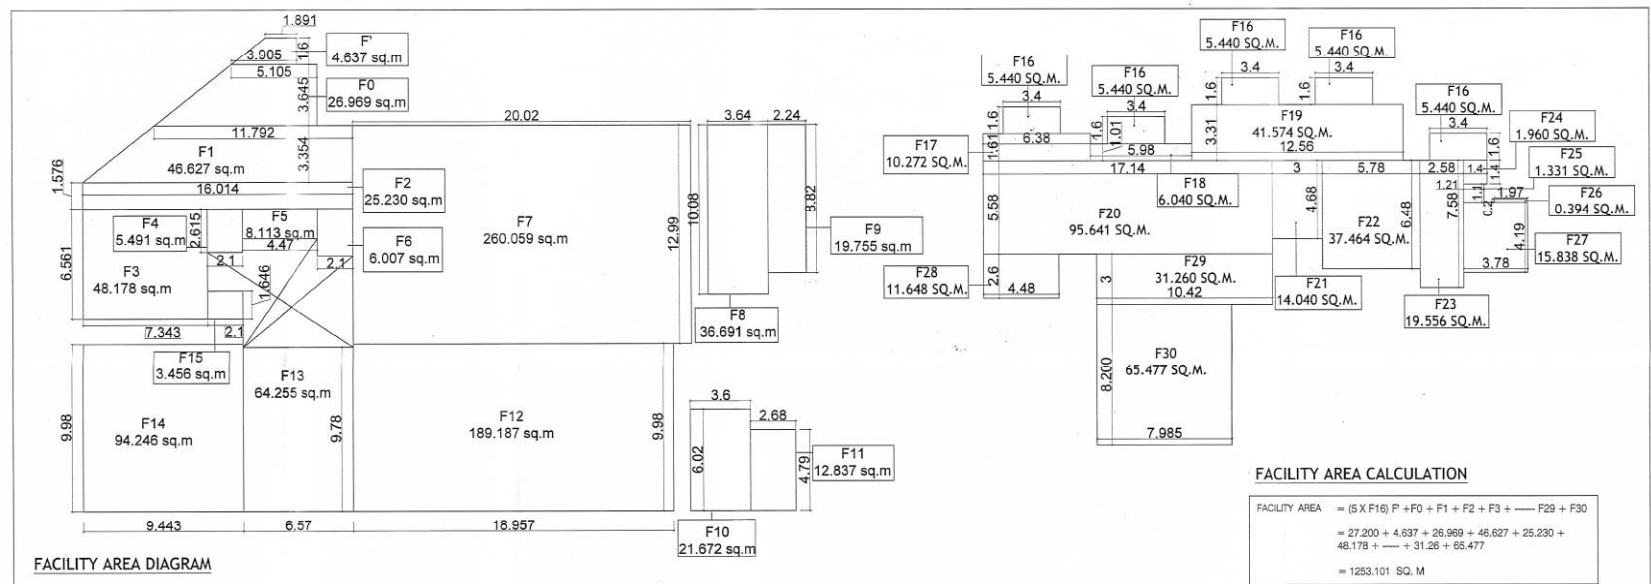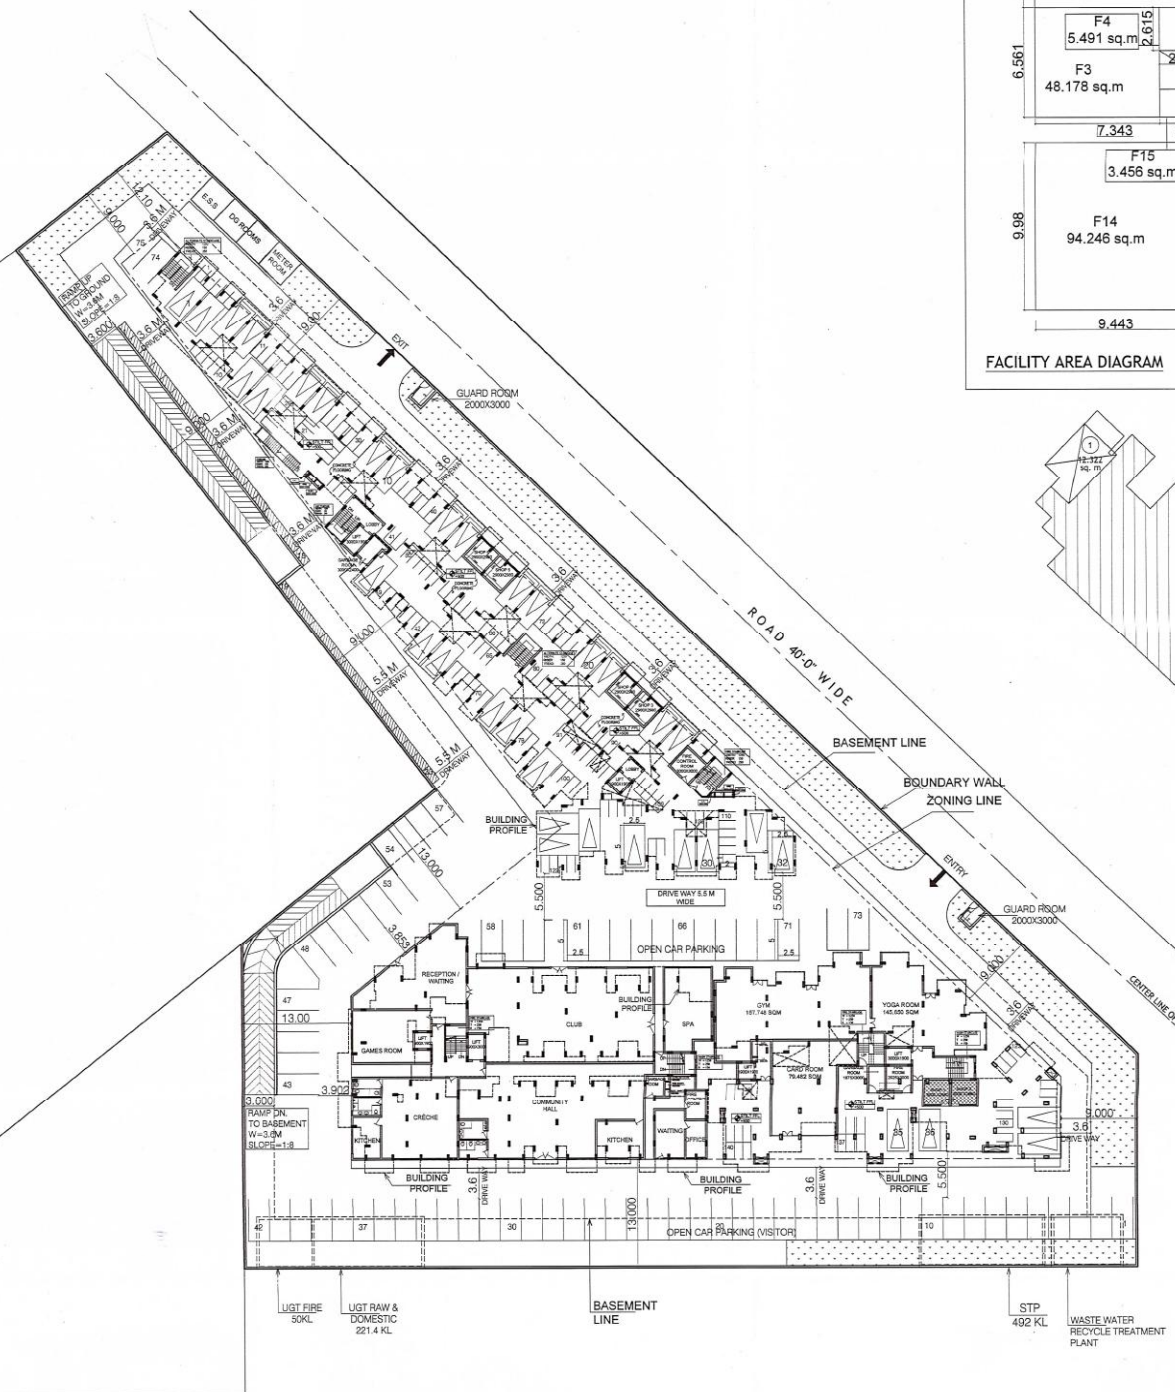


ARCHITECT'S SIGNATURE ROHIT GARG CA/94/17868	OWNER'S SIGNATURE Pranay Infrabuild Pvt. Ltd. Director
NAME OF OWNERS PRANAY INFRABUILD PVT. LTD. NEERAJ SUWALKA S/O. GIRRAJ PRASAD SUWALKA DIRECTOR	
PROJECT TITLE PROPOSED GROUP HOUSING SCHEME AT PLOT NO. B, KHASRA NO. 23, VILLAGE KUNHADI, TEHSIL LADPURA, DIST. KOTA, RAJASTHAN	
DRAWING TITLE STILT PLAN	(SUBMISSION DRAWING)
SCALE - 1:300	DATE - AUGUST, 2015
DRAWN - PRIYA	CHECKED - NITIN
 R.K. & ASSOCIATES Architects, Engineers & Planners E-31, GREEN PARK MAIN, NEW DELHI - 110016, INDIA Tel.: 28 96-3158, 28 51-07 51, 28 58-73 57 Fax: (011) 2888-2540 E-mail: rka.architects@gmail.com	


ROHIT GARG
CA/94/17868



THIS DRAWING IS THE PROPERTY OF THE ARCHITECT AND IS NOT TO BE REPRODUCED OR COPIED IN ANY MANNER WITHOUT THE WRITTEN PERMISSION OF THE ARCHITECT.
DATE: 22.09.12
DRAWN BY: R.K. & ASSOCIATES
CHECKED BY: R.K. & ASSOCIATES
PROJECT NO: CA/94/17868
DRAWING NO: D3
SCALE: 1:300
DATE: AUGUST, 2015
CHECKED BY: NITIN
DRAWN BY: NITIN
PROJECT TITLE: PROPOSED GROUP HOUSING SCHEME AT PLOT NO. B, HASRA NO. 23, VILLAGE KUNHADI, TEHSIL LADPURA, DIST. KOTA, RAJASTHAN
OWNER'S SIGNATURE: For Pranay Infrabuild Pvt. Ltd.
NAME OF OWNERS: Pranay Infrabuild Pvt. Ltd.
Director: Neeraj Suwalka S/o. Girraj Prasad Suwalka
PROJECT TITLE: PROPOSED GROUP HOUSING SCHEME AT PLOT NO. B, HASRA NO. 23, VILLAGE KUNHADI, TEHSIL LADPURA, DIST. KOTA, RAJASTHAN
DRAWING TITLE: (SUBMISSION DRAWING) BASEMENT PLAN & AREAS
DRAWN - NITIN
DATE - AUGUST, 2015
CHECKED - NITIN
D3
R.K. & ASSOCIATES
E-31, GREEN PARK MAIN, NEW DELHI - 110016, INDIA
Tel.: 2616-3158, 2616-6751, 2616-7337
Fax: (011) 2616-2540 Email: rk.associates@gmail.com

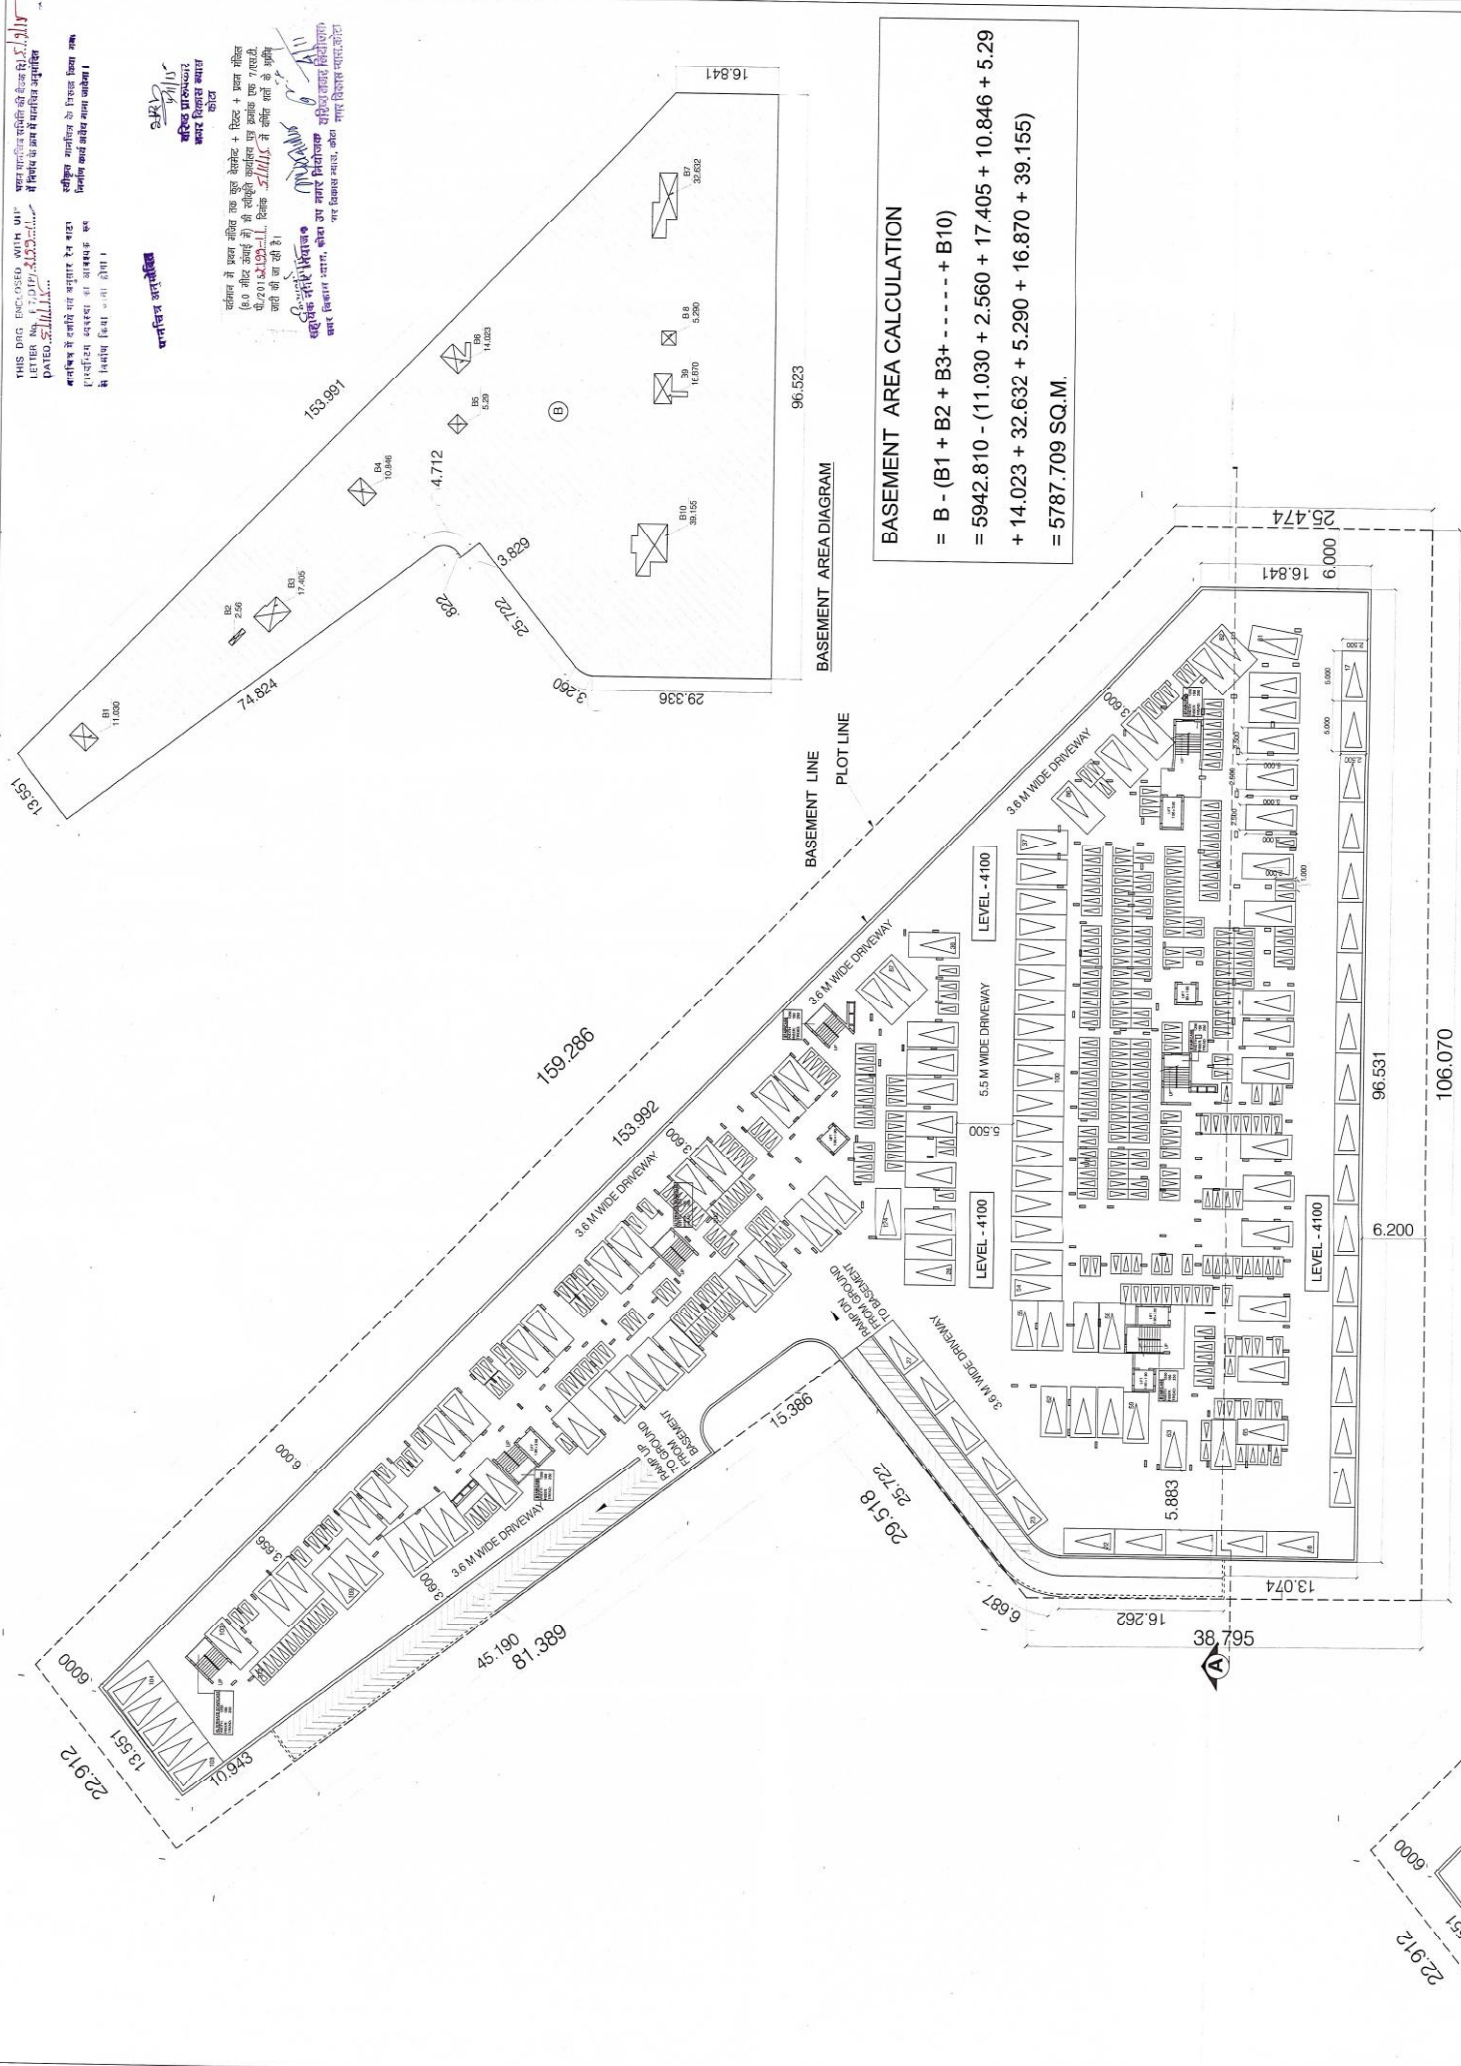


BASEMENT AND PARKING LAYOUT PLAN


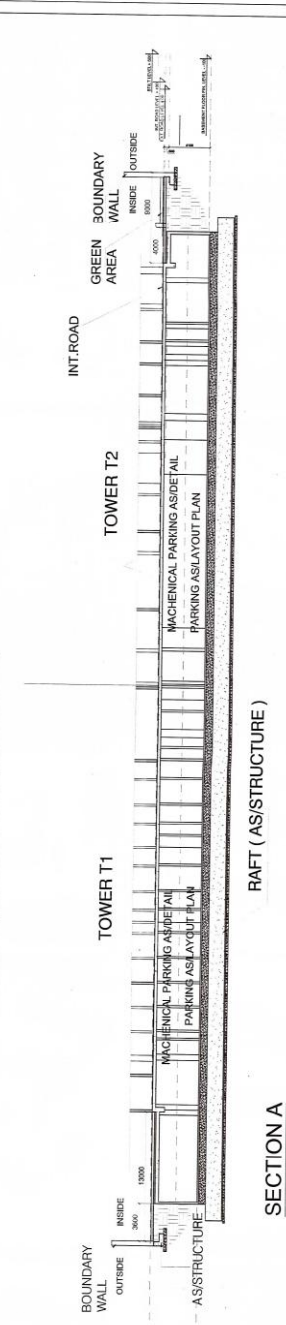


MECHANICAL PARKING PROVISION
25% OF TOTAL CAR PARKING
= 313 X 25 / 100
= 78.25 SAY 78 CARS

CAR PARKING IN BASEMENT = 124
MECHANICAL PARKING CARS = 78
TOTAL CAR PARKING = 202
TOTAL SCOOTER PARKING = 350

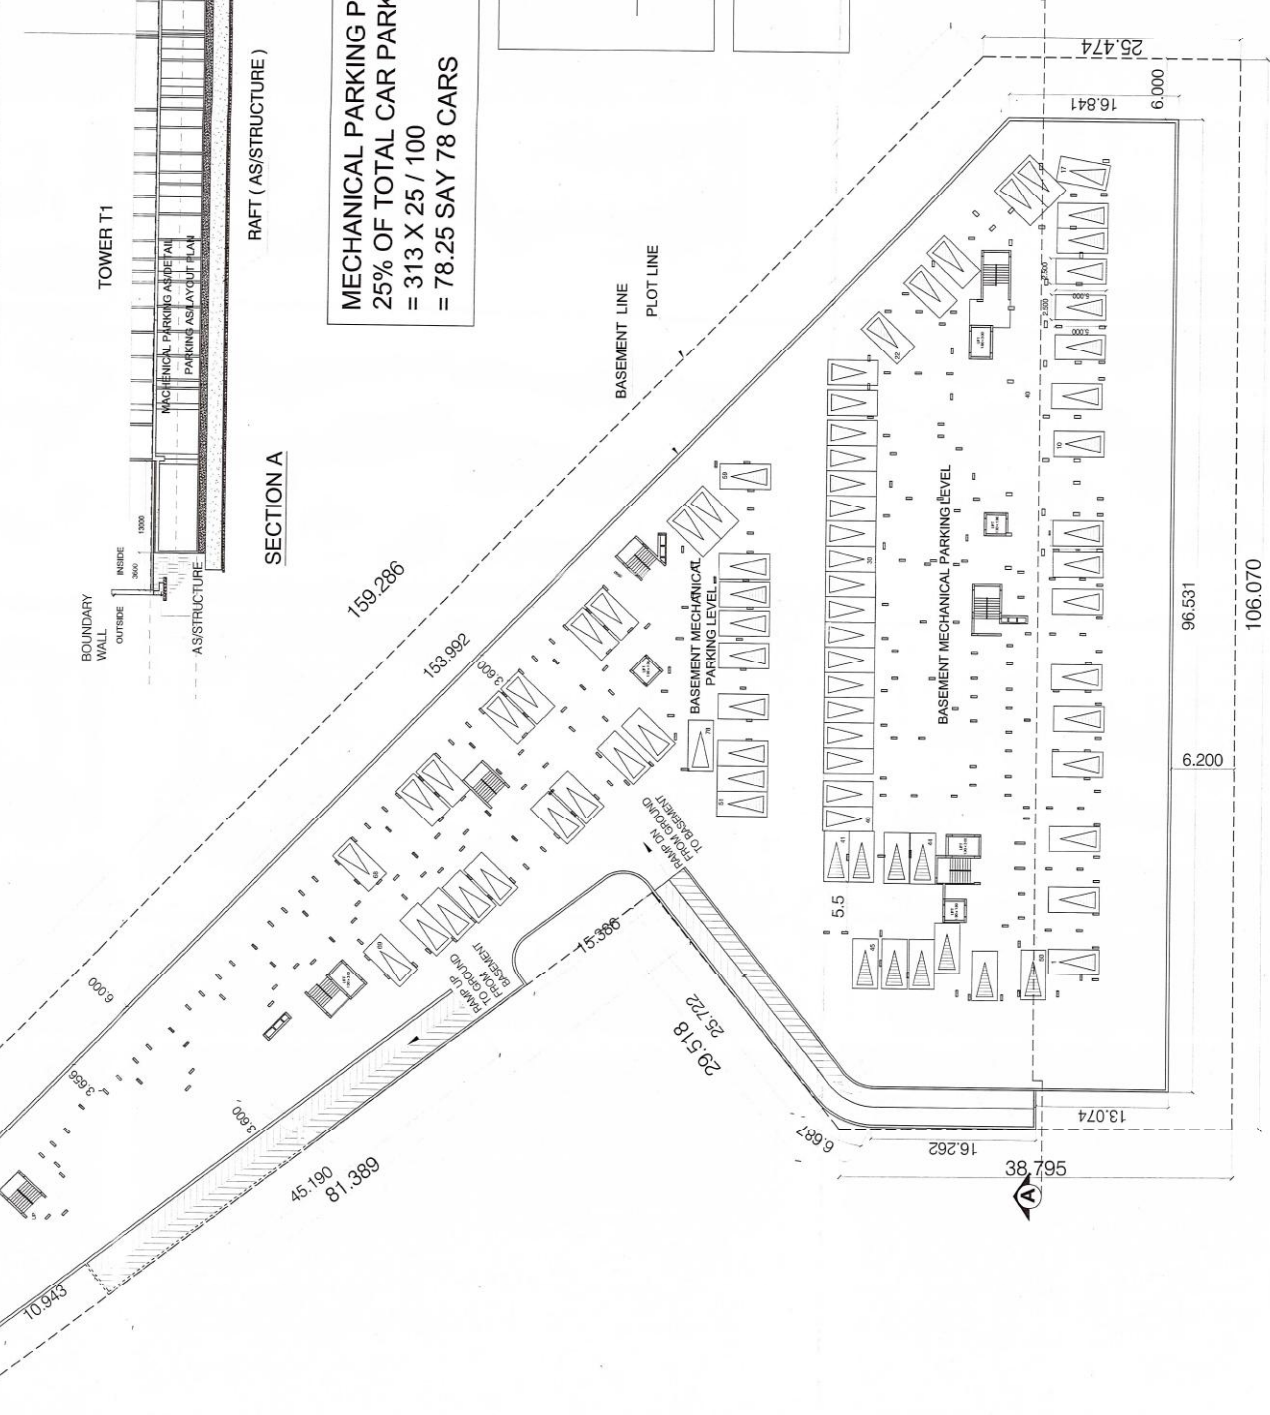

MECHANICAL PARKING LAYOUT PLAN

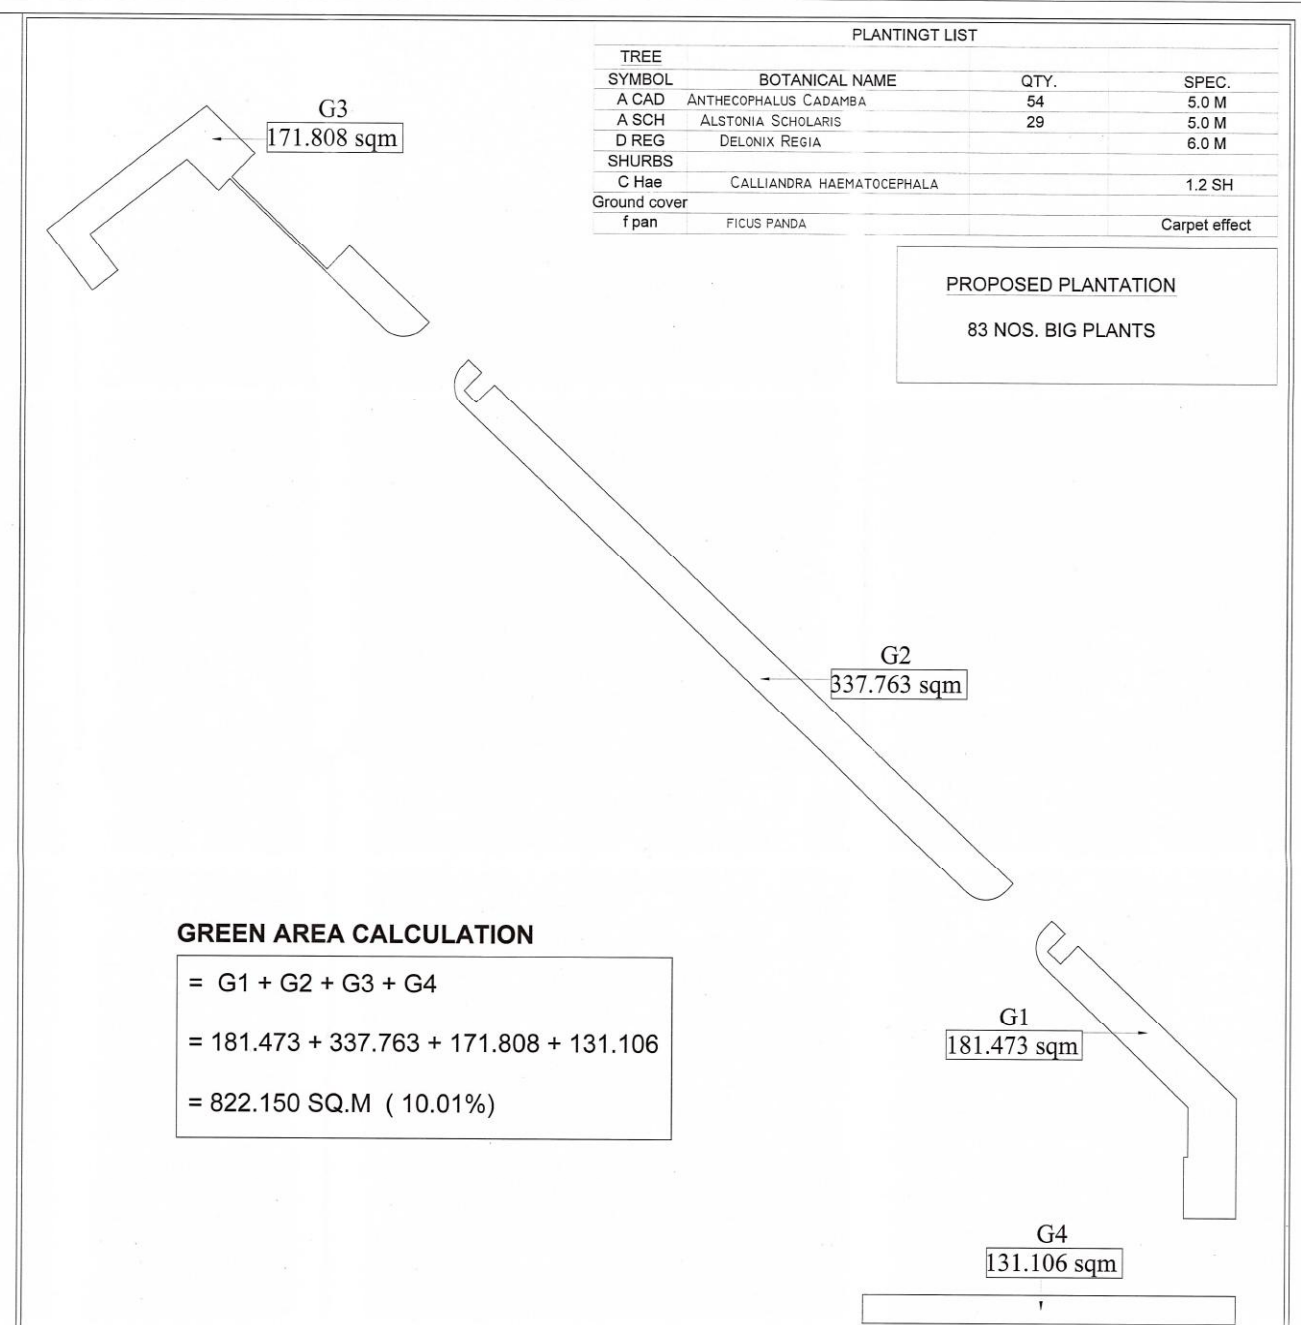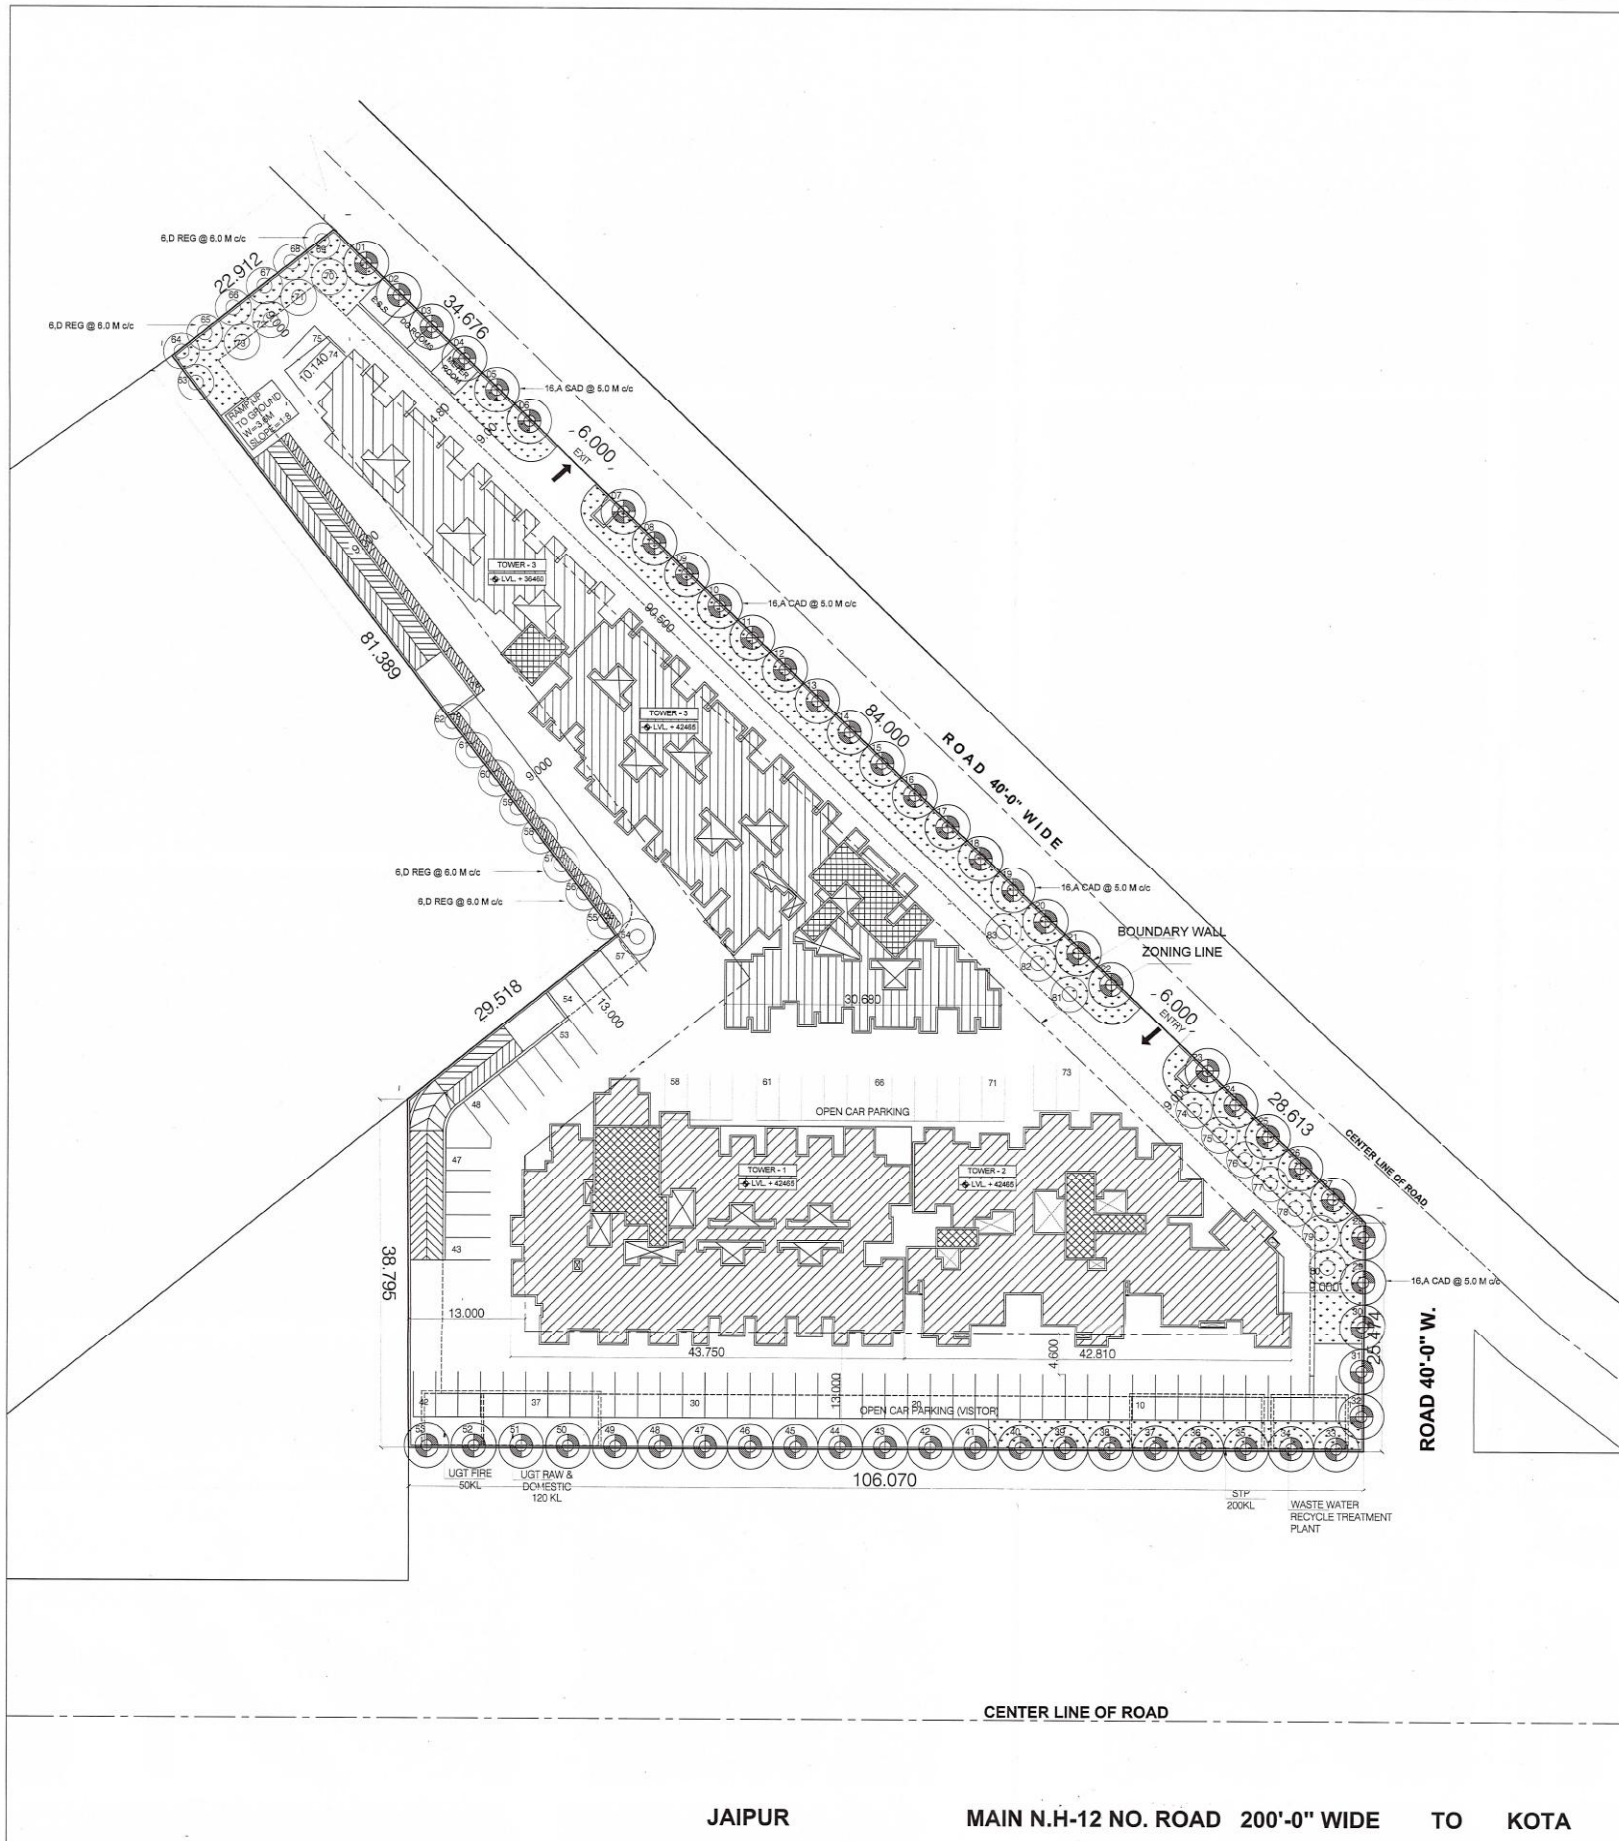

PLANTING LIST			
TREE			
SYMBOL	BOTANICAL NAME	QTY.	SPEC.
A CAD	ANTHECOPHALUS CADAMBA	54	5.0 M
A SCH	ALSTONIA SCHOLARIS	29	5.0 M
D REG	DELONIX REGIA		6.0 M
SHURBS			
C Hae	CALLIANDRA HAEMATOCEPHALA		1.2 SH
Ground cover			
f pan	FICUS PANDA		Carpet effect

GREEN AREA CALCULATION

= G1 + G2 + G3 + G4

= 181.473 + 337.763 + 171.808 + 131.106

= 822.150 SQ.M (10.01%)

THIS DRG ENCLOSED WITH U/I
LETTER NO. 17/01/2015
DATED 17/01/2015
मानविक से दस्तावेज एवं समुदाय के हित
एकत्रित करने का कार्य प्रारम्भ है।
किसी भी प्रकार के अन्याय को रोका जायेगा।
किसी भी प्रकार के अन्याय को रोका जायेगा।

मानविक अनुमोदित

कार्यक्रम में प्रथम मंजूरत तक कुल बेसमेन्ट + फ्लोर + प्रथम मंजूरत
(5.0 मीटर ऊंचाई में) की सीढ़ीय कालोनीय पर प्रमाण एक 1/एच.टी.
पी.2015 के अनुसार किया जायेगा।
कार्यक्रम में प्रथम मंजूरत तक कुल बेसमेन्ट + फ्लोर + प्रथम मंजूरत
(5.0 मीटर ऊंचाई में) की सीढ़ीय कालोनीय पर प्रमाण एक 1/एच.टी.
पी.2015 के अनुसार किया जायेगा।

ARCHITECT'S SIGNATURE
OWNER'S SIGNATURE
ROHIT GARG
CA/94/17868

NAME OF OWNERS
Pranay Infrabuild Pvt. Ltd.
Neeraj Suwalka S/o. Girraj Prasad Suwalka
Director

PROJECT TITLE
PROPOSED GROUP HOUSING SCHEME AT PLOT
NO. B, KHASRA NO. 23, VILLAGE KUNHADI,
TEHSIL LADPURA, DIST. KOTA, RAJASTHAN

DRAWING TITLE (SUBMISSION DRAWING)
LANDSCAPE PLAN

SCALE - 1:300
DATE - SEPTEMBER, 2015
DRAWN - SOUMYA
CHECKED - NITIN

DRG. NO.
D4
R.K. & ASSOCIATES
ARCHITECTS, ENGINEERS & PLANNERS
B-31, GREEN PARK MAIN, NEW DELHI - 110016, INDIA
Tel.: 2656-3158, 2651-6751, 2656-7357
Fax: (011) 2656-2540 Email: rk.associates@gmail.com


THIS DRG. ENCLOSED WITH U.P.
LETTER No. 67/DIP/2015-11
DATED. 22.09.2015

मानचित्र में दर्शाये गये अनुसार र. 112 र.
परिचालन प्रकल्पों की आवश्यक रूप
में निर्माण किया जाना होगा।

मानचित्र अनुमोदित

वर्तमान में प्रकल्प नजिल तक कुल डेवलेपमेंट + रिटर्न + प्रकल्प नजिल
(8.0 मीटर ऊंचाई से) की स्वीकृति कागजात प्रकल्प प्रमाणिक एफ 7 एफ 8.
पी 2015-2016 दिवस 22.09.2015 में वरीत शर्तों के अधीन
जाये की जा रही है।

प्रकल्प नगर विकास
नगर विकास मंडल, बीदा नगर विकास मंडल, कोटा
नगर विकास मंडल, कोटा

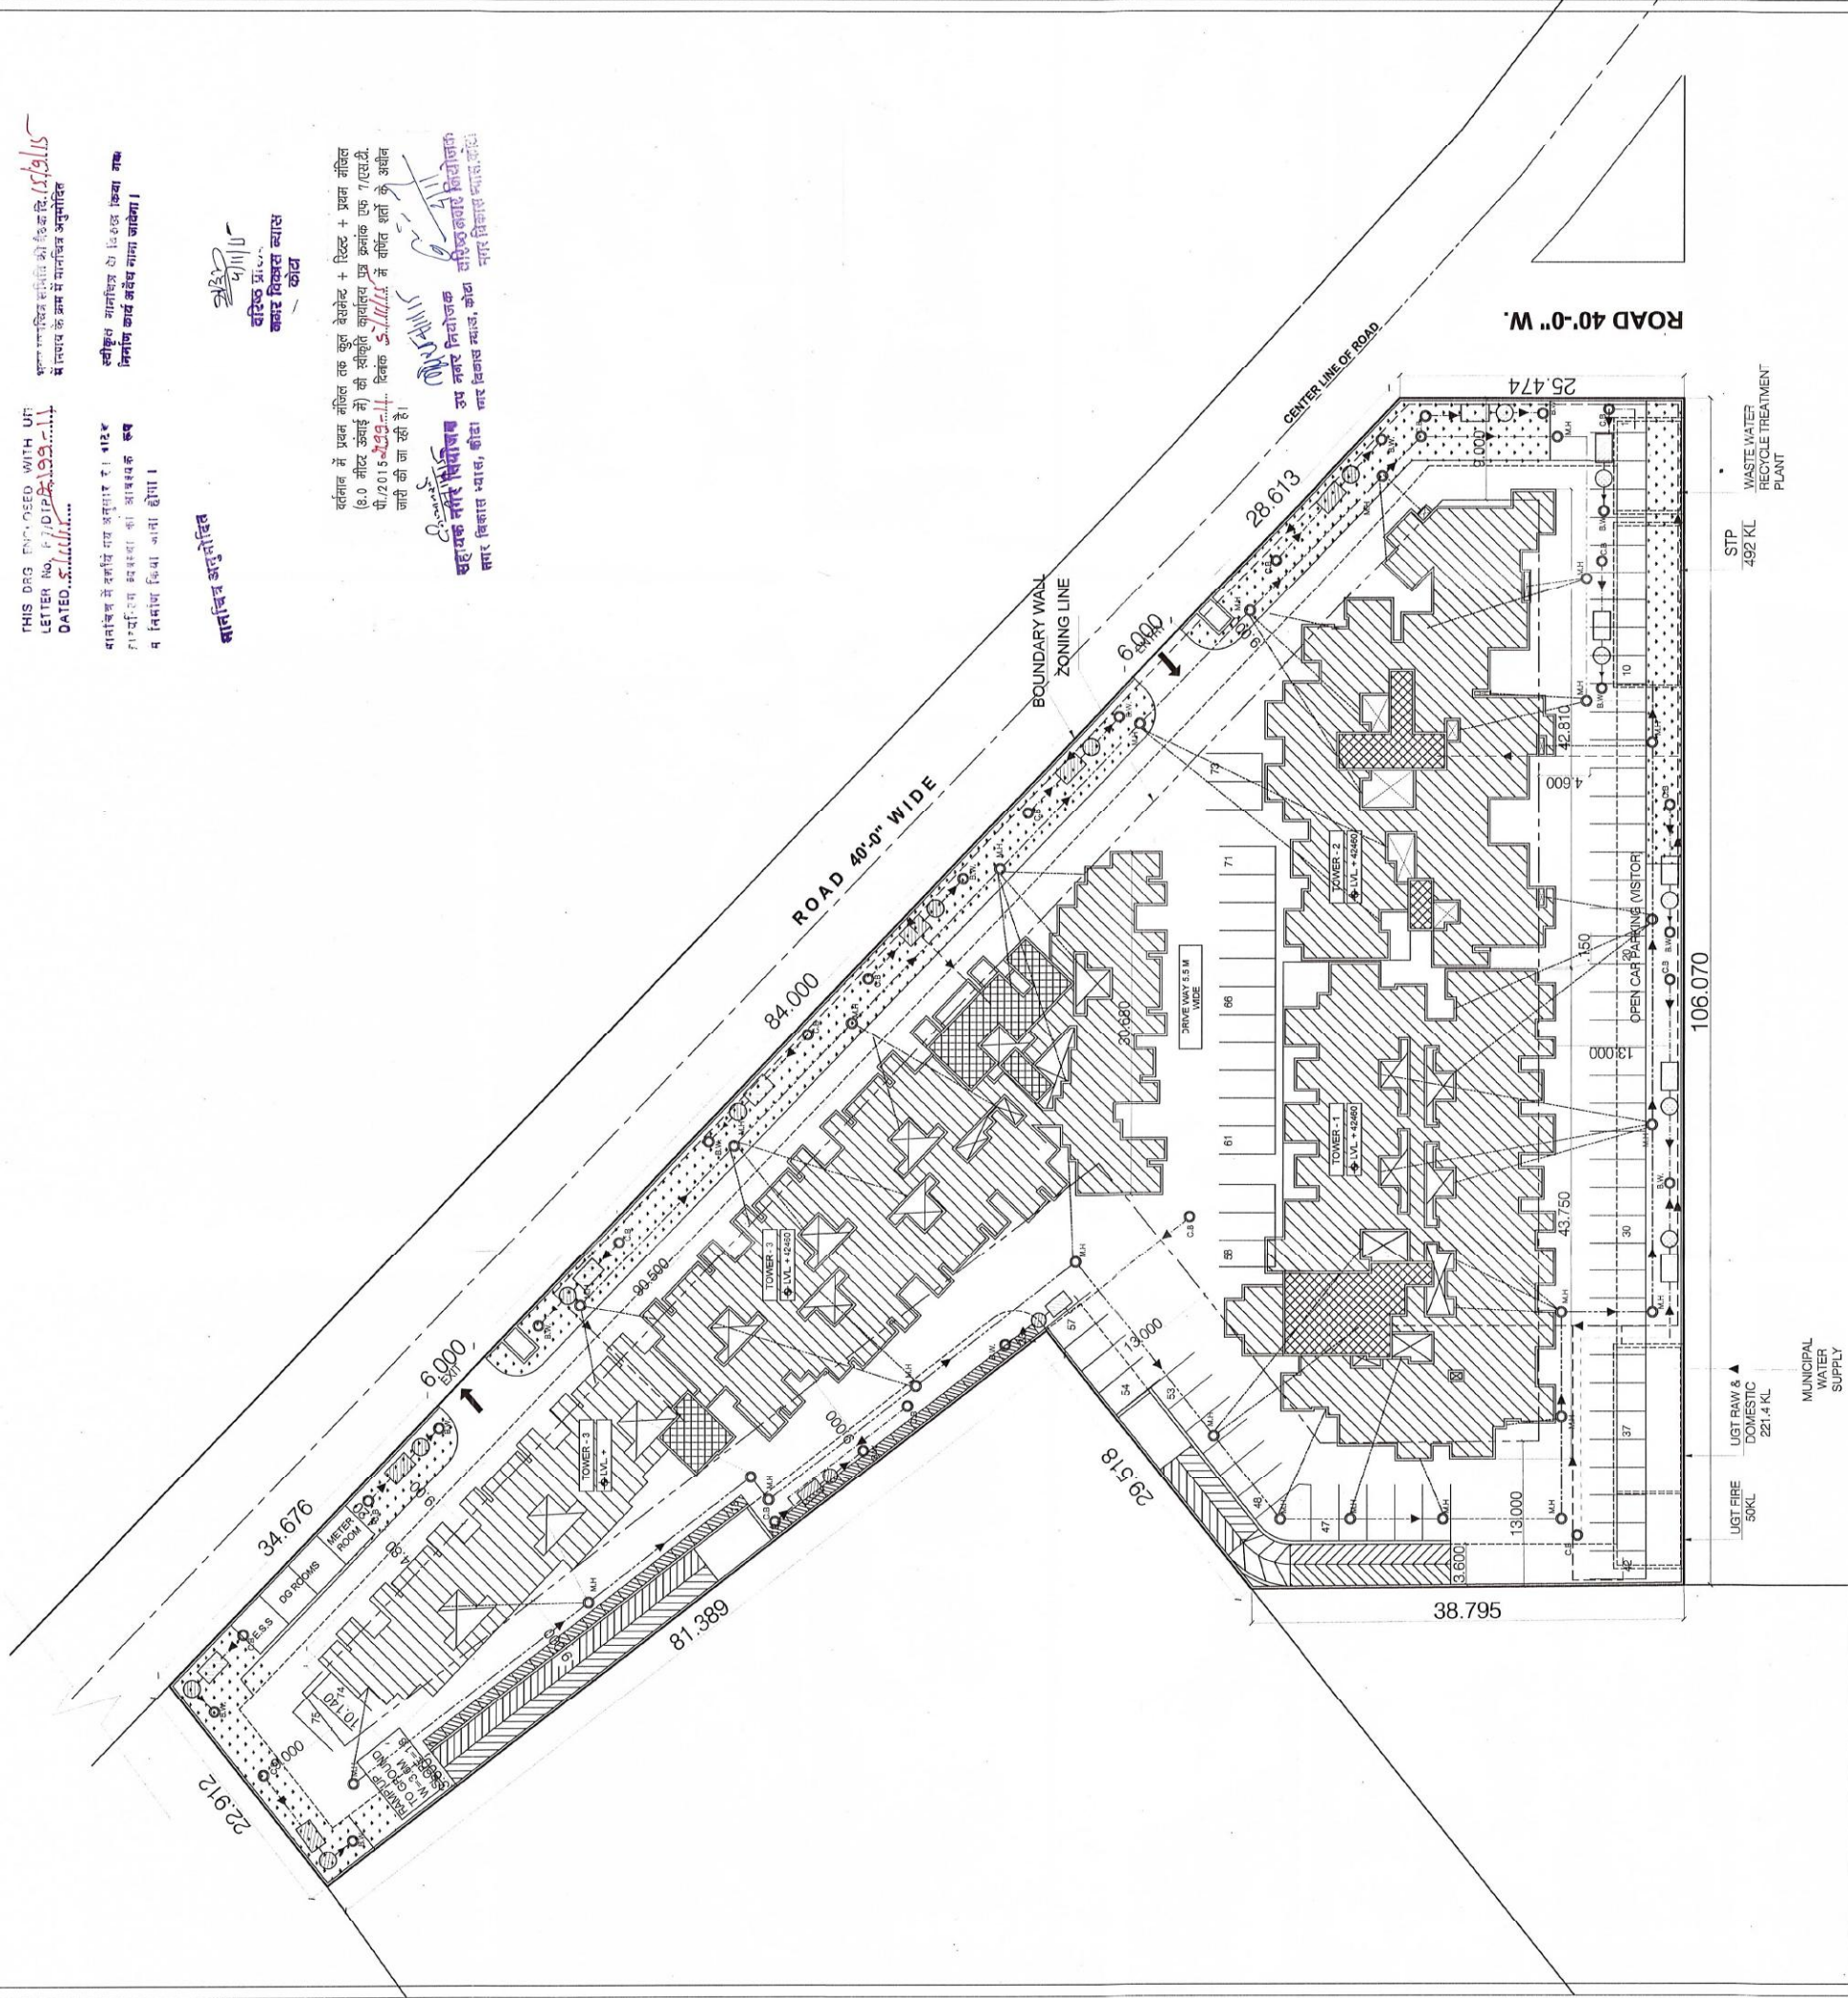

CENTER LINE OF ROAD

JAIPUR


MAIN N.H-12 NO. ROAD 200'-0" WIDE

TO KOTA


LEGEND :	
	VISITORS PARKING
	SEWER LINE
	MANHOLE
	RAIN WATER HARVESTING DESILTING TANK = 5000 x 2000 x 2500 RECHARGE PIT = 2000 x 2000 x 1500
	DOMESTIC WATER SUPPLY PIPE LINE.
	CATCH BASIN

ROHIT GARG
CA/94/17868


ARCHITECT'S SIGNATURE 	OWNER'S SIGNATURE
NAME OF OWNERS PRANAY INFRABUILD PVT. LTD. NEERAJ SUWALKA S/O. GIRRAJ PRASAD SUWALKA DIRECTOR	
PROJECT TITLE PROPOSED GROUP HOUSING SCHEME AT PLOT NO. B, KHASRA NO. 23, VILLAGE KUNHADI, TEHSIL LADPURA, DIST. KOTA, RAJASTHAN	
DRAWING TITLE SERVICE LAYOUT (SUBMISSION DRAWING)	
SCALE - 1:300	DATE - AUGUST, 2015
DRAWN - PRIYA	CHECKED - NITIN
R.K. & ASSOCIATES ARCHITECTS, ENGINEERS & PLANNERS E-31, GREEN PARK MAIN, NEW DELHI - 110016, INDIA Tel.: 28 96-31 66, 28 51-67 51, 28 56-73 97 Fax: (011) 2896-2560 Email: rka.architect@gmail.com	
DRG. NO. D5	

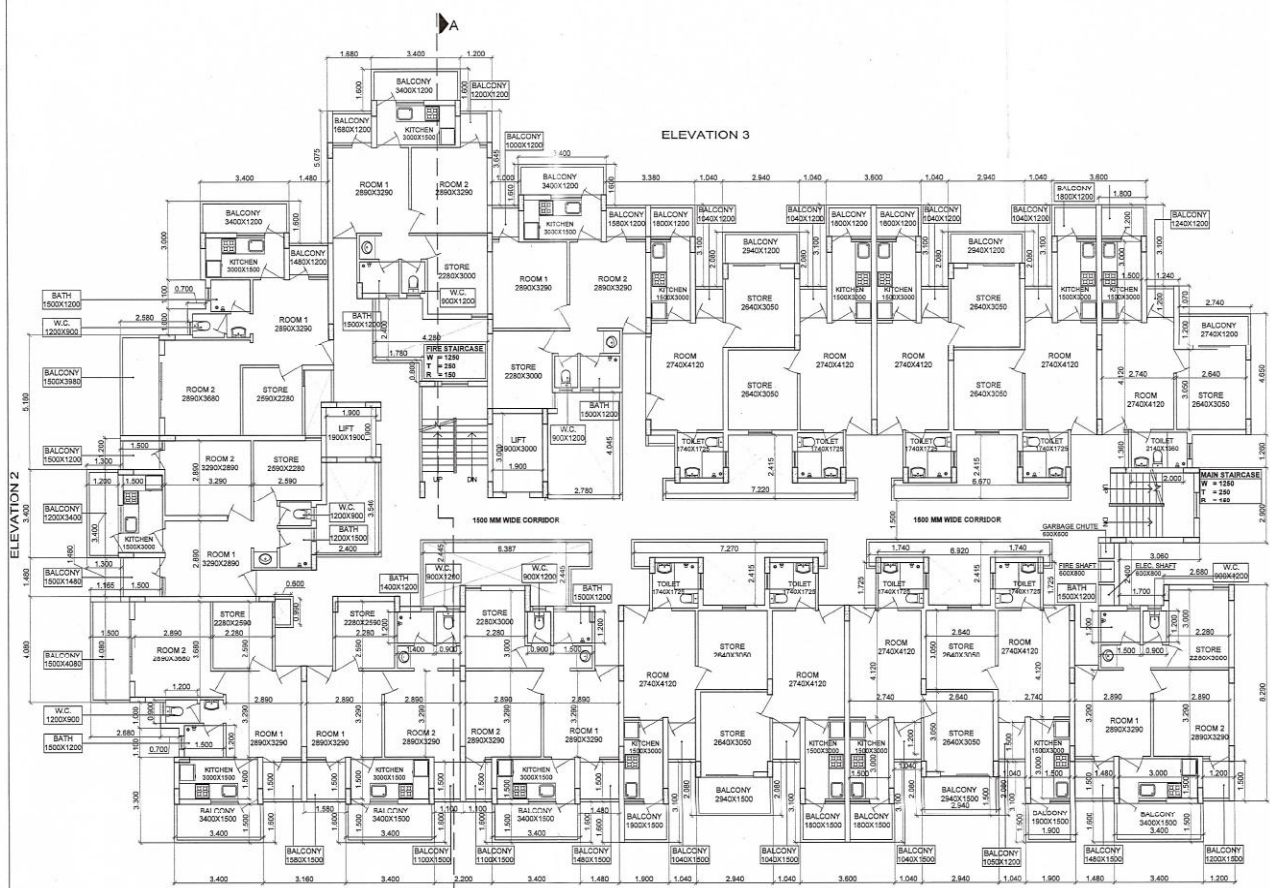


ORIGINAL FLOOR PLAN

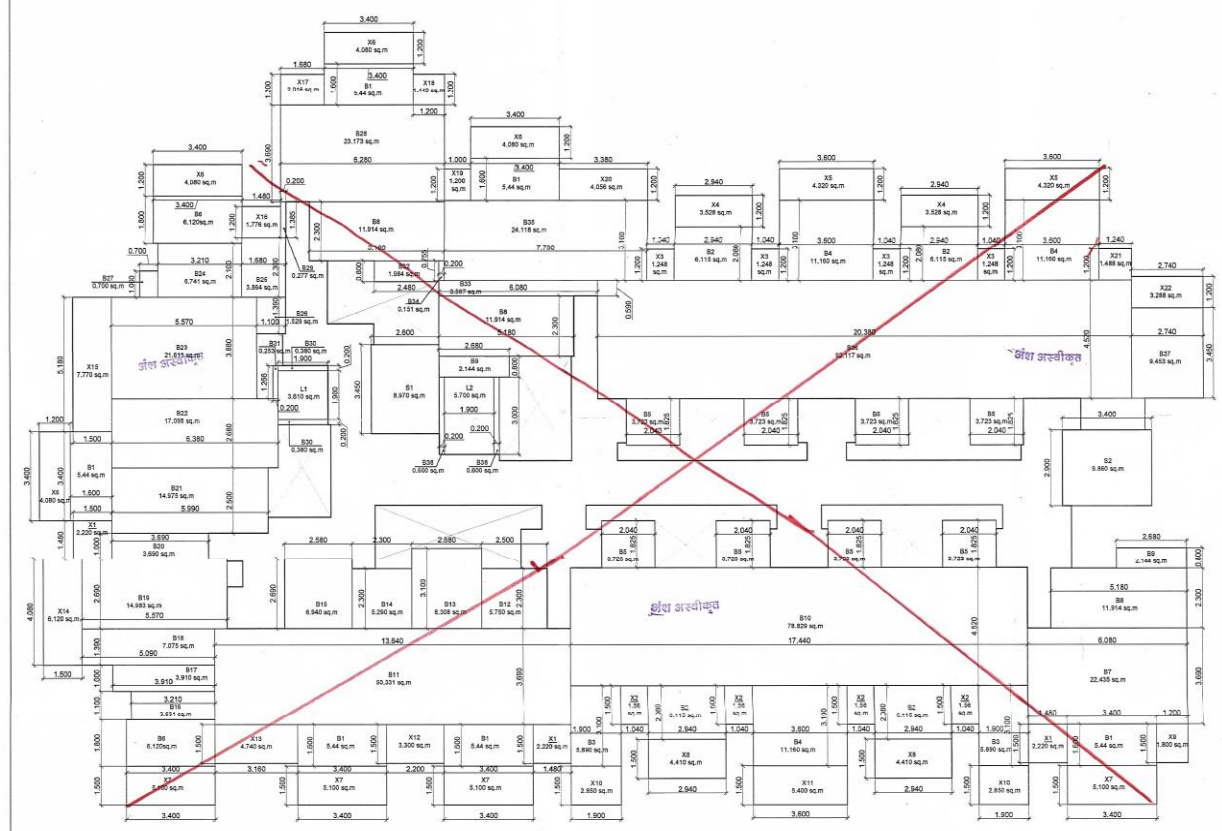


TYPICAL (1st - 13th) FLOOR AREA DIAGRAM

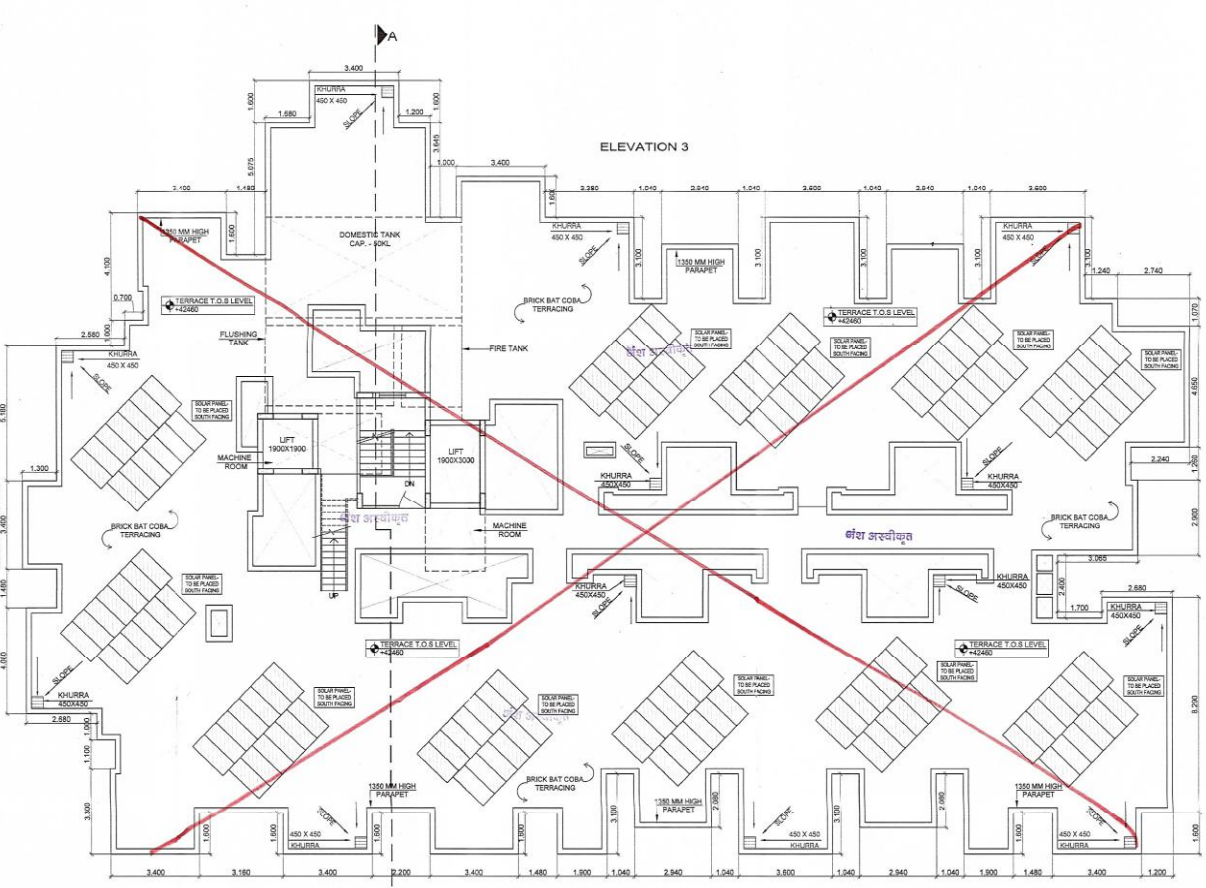

TERRACE FLOOR PLAN

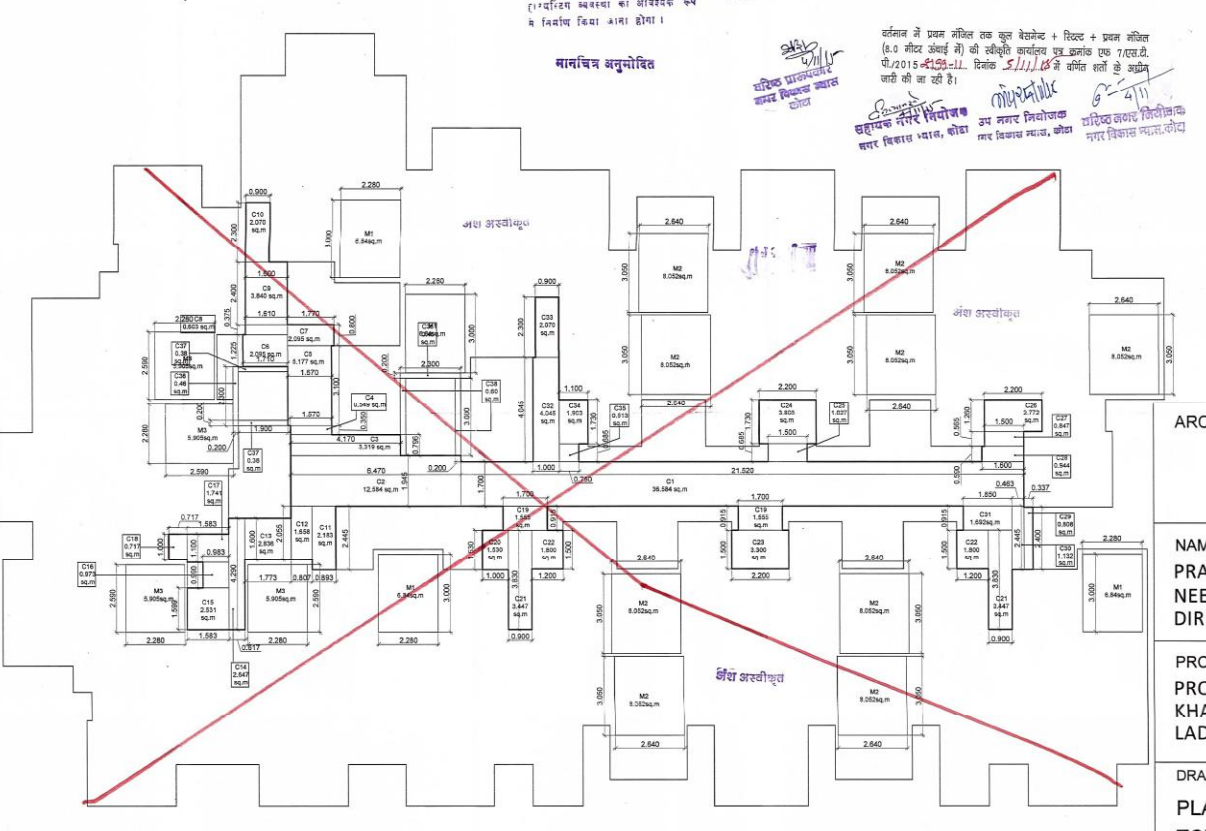


TYPICAL (1st - 13th) FLOOR CIRCULATION AREA DIAGRAM

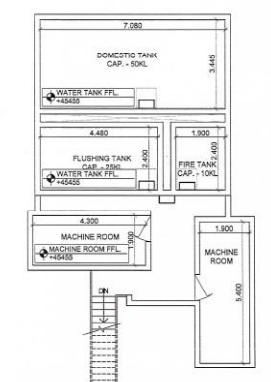


MACHINE ROOM / WATER TANK PLAN

TYPICAL FLOOR AREA CALCULATION	
TYPICAL FLOOR BLOCK AREA	= 903.048 SQ. M
TYPICAL FLOOR BUILT-UP AREA	= (903.048 - 9.310) = 893.738 SQ. M
1. BLOCK AREA	= 903.048 SQ. M
2. LIFTS AREA	= L1 + L2 = 3.610 + 5.700 = 9.310 SQ. M
3. STAIRCASE AREA	= S1 + S2 = 8.370 + 9.860 = 18.630 SQ. M
4. CORRIDOR AREA	= C1 + C2 + C3 + C4 + C5 + C6 + C7 + C8 + C9 + C10 + C11 + C12 + C13 + C14 + C15 + C16 + C17 + C18 + C19 + C20 + C21 + C22 + C23 + C24 + C25 + C26 + C27 + C28 + C29 + C30 + C31 + C32 + C33 + C34 + C35 + C36 + C37 + C38 = 36.584 + 12.584 + 3.319 + 0.549 + 5.177 + 2.095 + 1.418 + 0.603 + 3.940 + 2.070 + 2.183 + 1.658 + 2.837 + 2.647 + 2.631 + 0.973 + 1.741 + 0.717 + 2.155 + 1.530 + 2.347 + 2.150 + 3.300 + 3.808 + 1.027 + 2.772 + 0.847 + 0.944 + 0.605 + 1.102 + 1.892 + 4.040 + 2.772 + 1.903 + 0.513 + 2.048 + 2.035 + 2.035 = 126.398 SQ. M
5. BALCONY AREA	= 30(X1) + 4(X2) + 4(X3) + 2(X4) + 2(X5) + 4(X6) + 4(X7) + 2(X8) + X9 + 2(X10) + X11 + X12 + X13 + X14 + X15 + X16 + X17 + X18 + X19 + X20 + X21 + X22 = 3/2.220 + 4(1.55) + 4(1.248) + 2(3.538) + 2(4.320) + 4(4.080) + 4(5.100) + 2(4.410) + 1.800 + 2(2.550) + 5.400 + 3.300 + 4.740 + 6.120 + 7.770 + 1.776 + 2.016 + 1.440 + 1.200 + 4.056 + 1.488 + 3.288 = 129.222 SQ. M
6. STORE AREA	= 4(M1) X 9(M2) X 4(M3) = 4(8.840) X 9(8.052) X 4(5.905) = 123.456 sq.m
F.A.R. AREA ON ONE TYPICAL FLOOR	
= 1 - (2 + 3 + 4 + 5)	
= 903.048 - (9.310 + 18.630 + 126.398 + 129.222)	
= 903.048 - (283.760)	
= 619.288 SQ. M	
TOTAL F.A.R. AREA FOR 13 FLOORS	
= 13 X 619.288	
= 8050.744 SQ. M	
TOTAL F.A.R. AREA (TOWER-1) = 8050.744 SQ. M	
TOTAL BUILT-UP AREA (TOWER-1) = 11618.594 SQ. M	

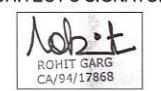
ARCHITECT'S SIGNATURE  ROHIT GARG CA/9/17868		OWNER'S SIGNATURE  For Pranay Infrabuild Pvt. Ltd. Director	
NAME OF OWNERS PRANAY INFRABUILD PVT. LTD. NEERAJ SUWALKA S/O. GIRRAJ PRASAD SUWALKA DIRECTOR			
PROJECT TITLE PROPOSED GROUP HOUSING SCHEME AT PLOT NO. B, KHASRA NO. 23, VILLAGE KUNHADI, TEHSIL LADPURA, DIST. KOTA, RAJASTHAN			
DRAWING TITLE PLANS & AREAS TOWER 1		(SUBMISSION DRAWING) (S+13)	
SCALE - 1:100		DATE - AUG, 2015	
DRAWN - ANUJ		CHECKED - NITIN	
		DRG. NO. D6	


ROHIT GARG
CA/9/17868


R.K. & ASSOCIATES
Architects, Engineers & Planners
E-31, GREEN PARK MAIN, NEW DELHI - 110018, INDIA
Tel.: 2696-3158, 2651-6751, 2656-7357
Fax: (011) 2686-2540 E-mail: rka.architects@gmail.com

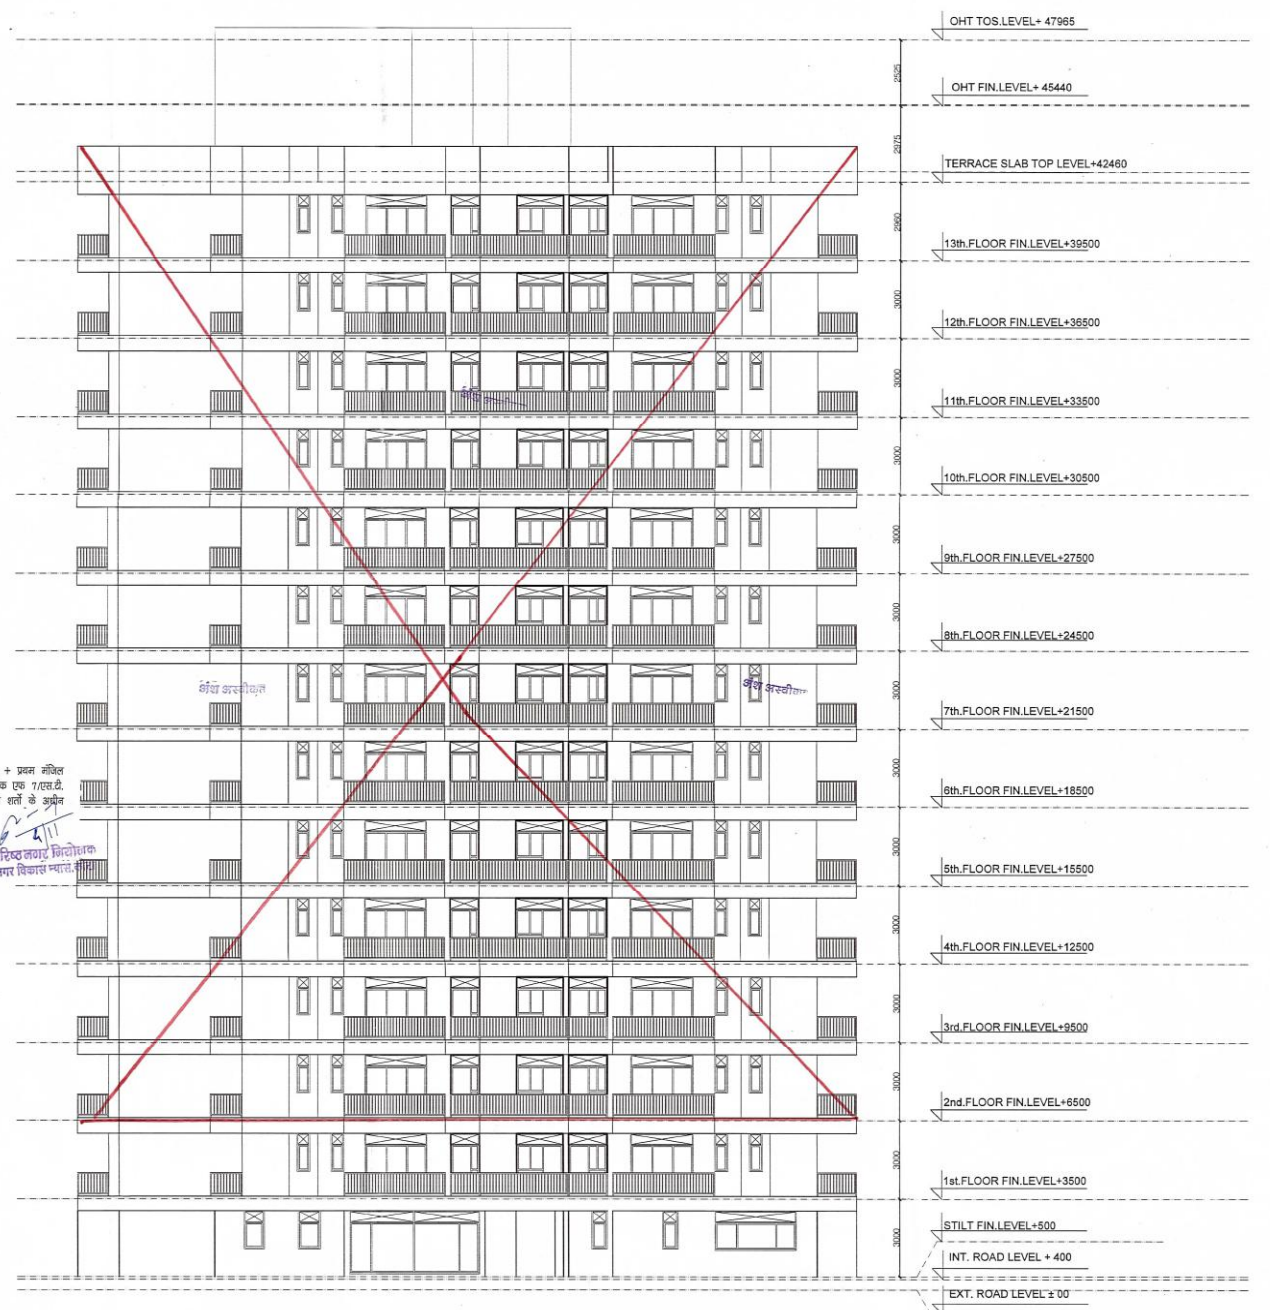


ARCHITECT'S SIGNATURE		OWNER'S SIGNATURE	
 ROHIT GARIG CA/94/17858		For Pranshy InfraBuild Pvt. Ltd.  Director	
NAME OF OWNERS			
PRANAY INFRABUILD PVT. LTD.			
NEERAJ SUWALKA S/O, GIRRAJ PRASAD SUWALKA DIRECTOR			
PROJECT TITLE			
PROPOSED GROUP HOUSING SCHEME AT PLOT NO. B, KHASRA NO. 23, VILLAGE KUNHADI, TEHSIL LADPURA, DIST. KOTA, RAJASTHAN			
DRAWING TITLE		(SUBMISSION DRAWING)	DRG. NO.
ELEVATIONS		(S+13)	
TOWER T1			
SCALE - 1:100	DATE -AUG. 2015		
DRAWN - DIKSHA		CHECKED - NITIN	
 R.K. & ASSOCIATES ARCHITECTS & ENGINEERS E-51, GREEN PARK MAIN, NEW DELHI - 110016, INDIA Tel. : 26 66 - 31 58, 26 51 - 07 51, 26 56 - 73 57 Fax: (011) 2686-2640 E-mail: rka.architects@gmail.com			

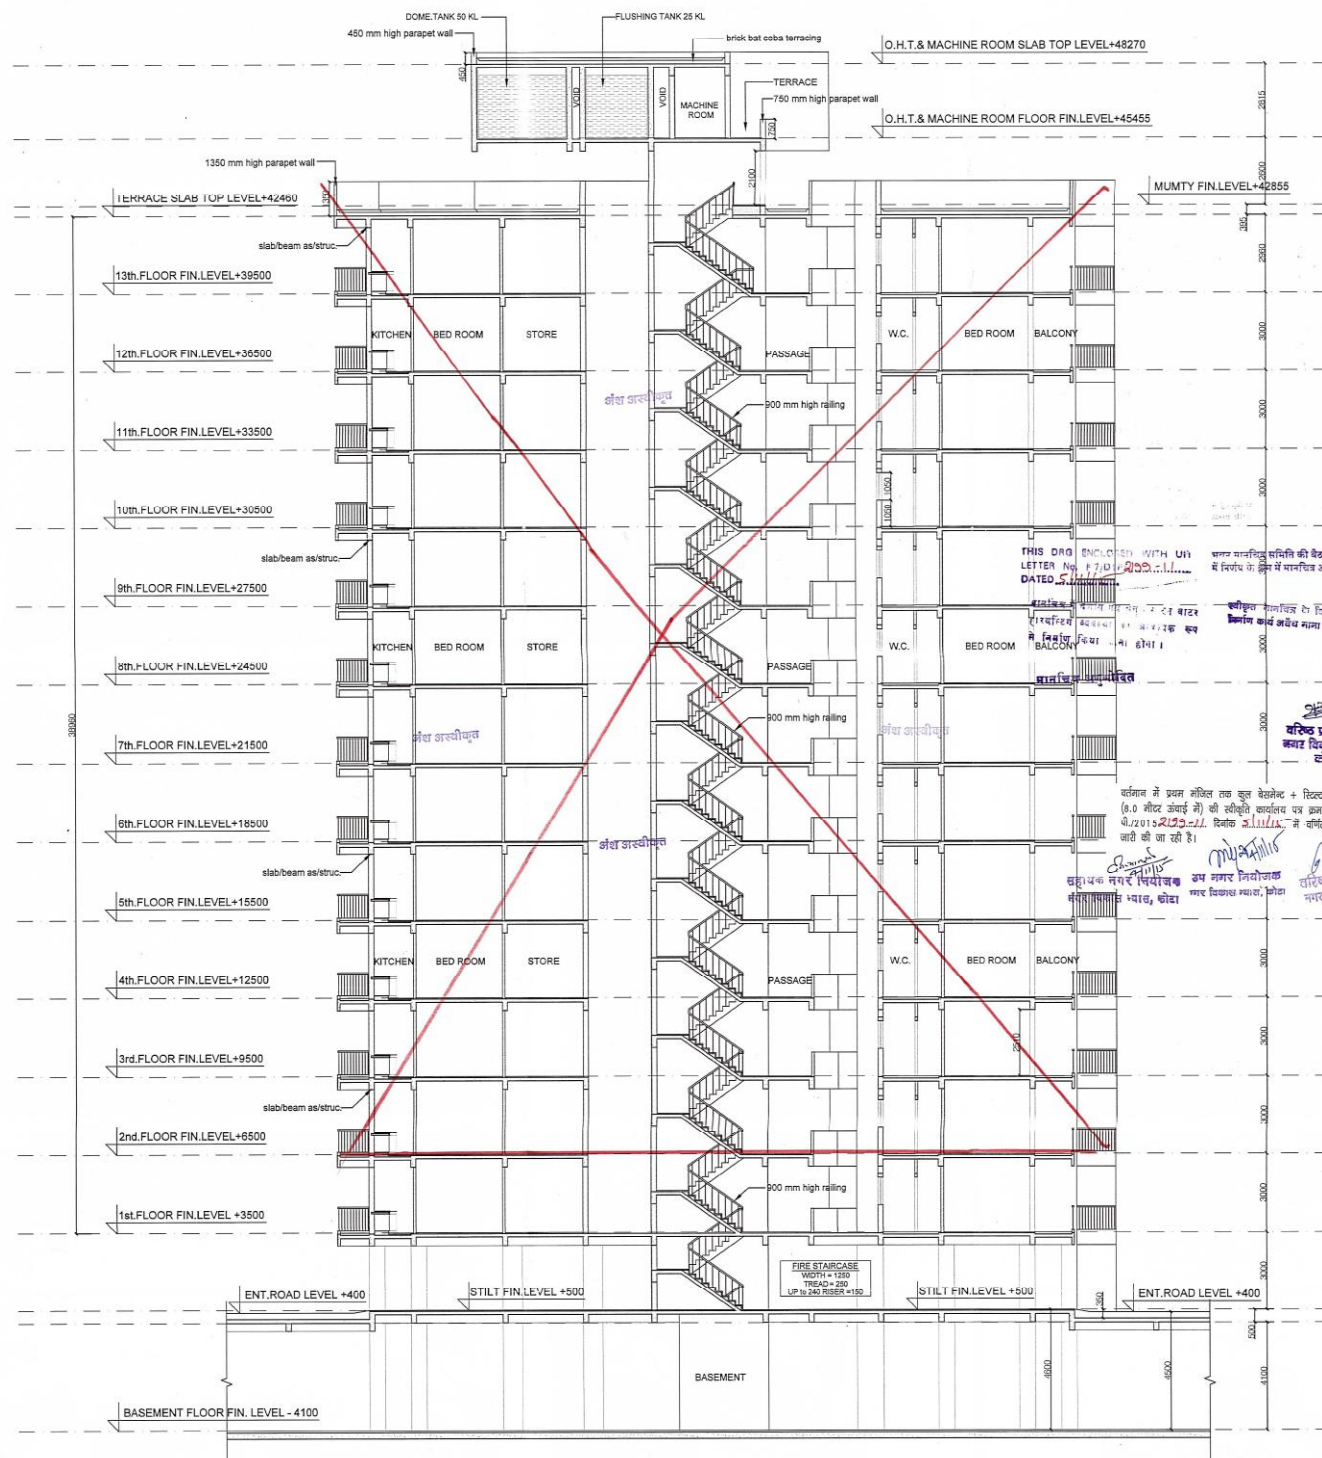



SECTION - A A

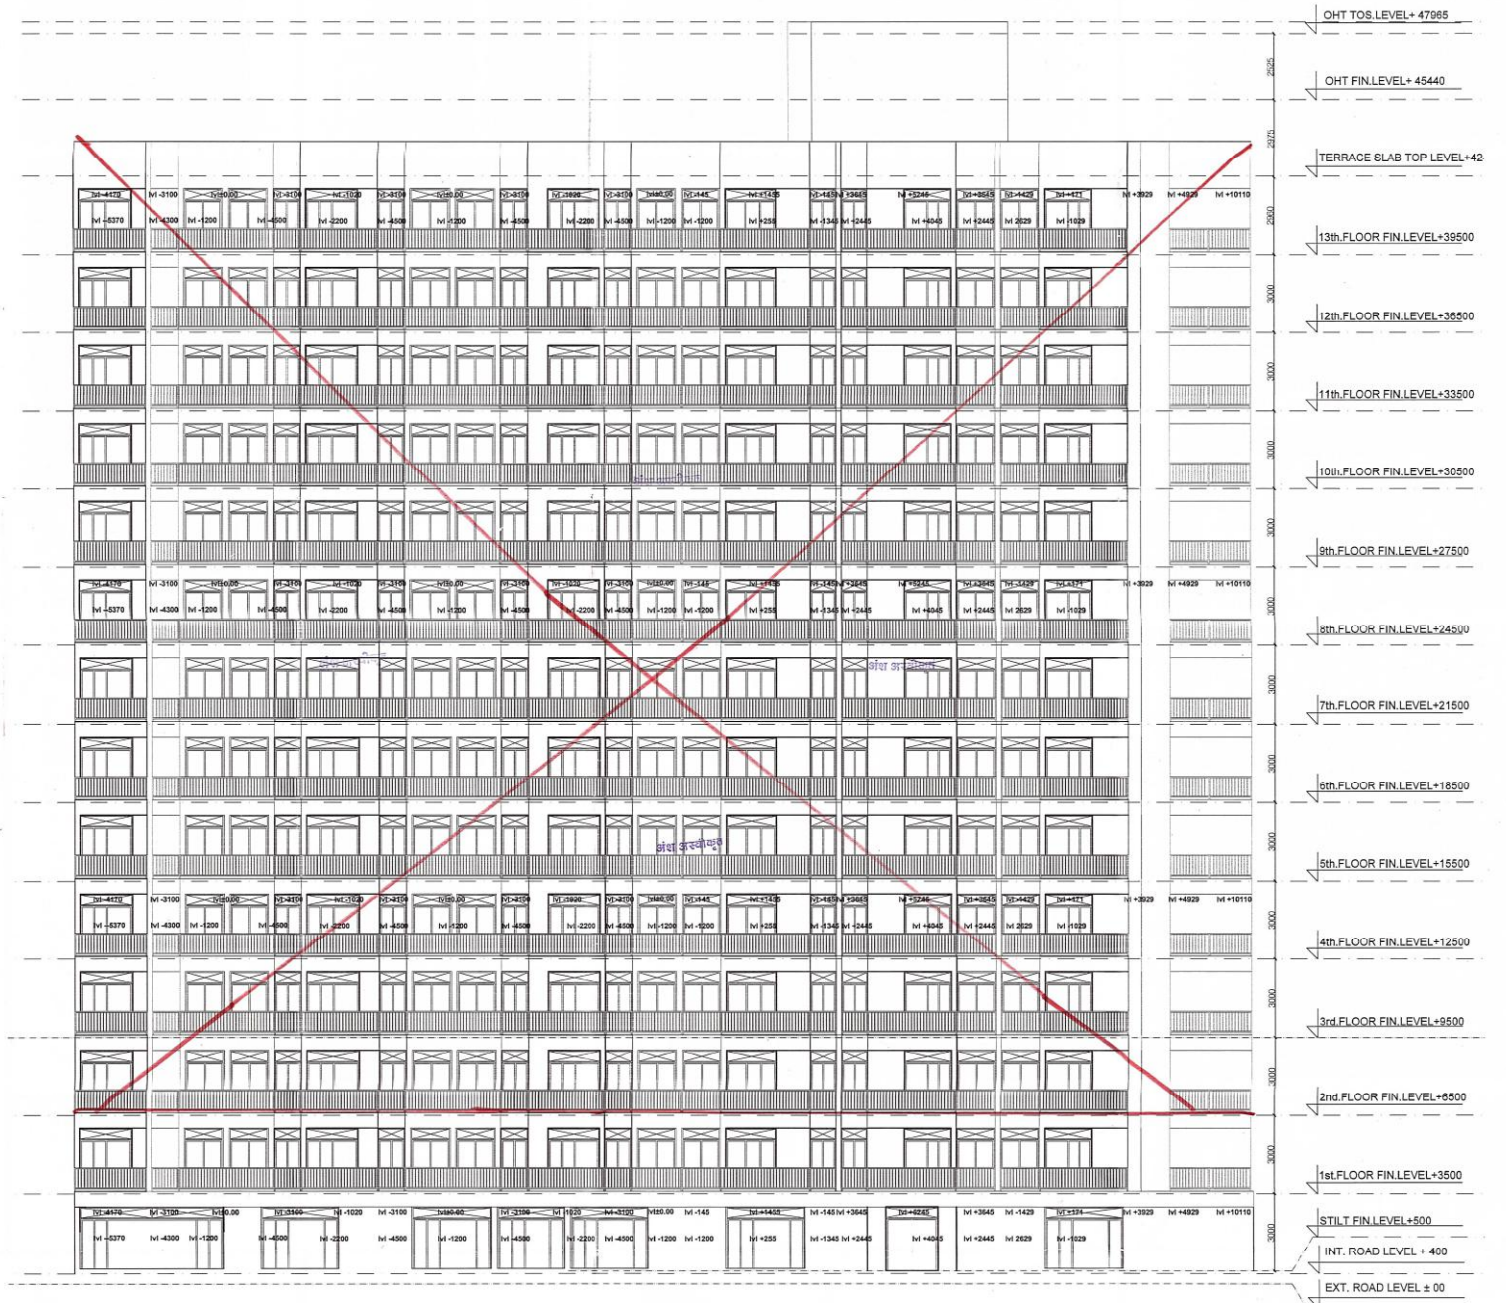


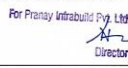ARCHITECT'S SIGNATURE  ROHIT GARG CA/94/17868		OWNER'S SIGNATURE  Pranay Infrabuild Pvt. Ltd. Director	
NAME OF OWNERS PRANAY INFRABUILD PVT. LTD. NEHAJ SUWALKA S/O. GIRRAJ PRASAD SUWALKA DIRECTOR			
PROJECT TITLE PROPOSED GROUP HOUSING SCHEME AT PLOT NO. B, KHASRA NO. 23, VILLAGE KUNHADI, TEHSIL LADPURA, DIST. KOTA, RAJASTHAN			
DRAWING TITLE (SUBMISSION DRAWING) SECTION & ELEVATION (S+13) TOWER T1		DRG. NO. D8	
SCALE - 1:100	DATE - JULY, 2015		
DRAWN - ML SHARMA	CHECKED - NITIN		



ROHIT GARG
CA/94/17868

 **R.K. & ASSOCIATES**
Architects, Engineers & Planners
E-31, GREEN PARK MAIN, NEW DELHI - 110016, INDIA
Tel.: 2616-3158, 2651-4751, 2656-7357
Fax: (011) 2656-2540 E-mail: rka.architects@gmail.com

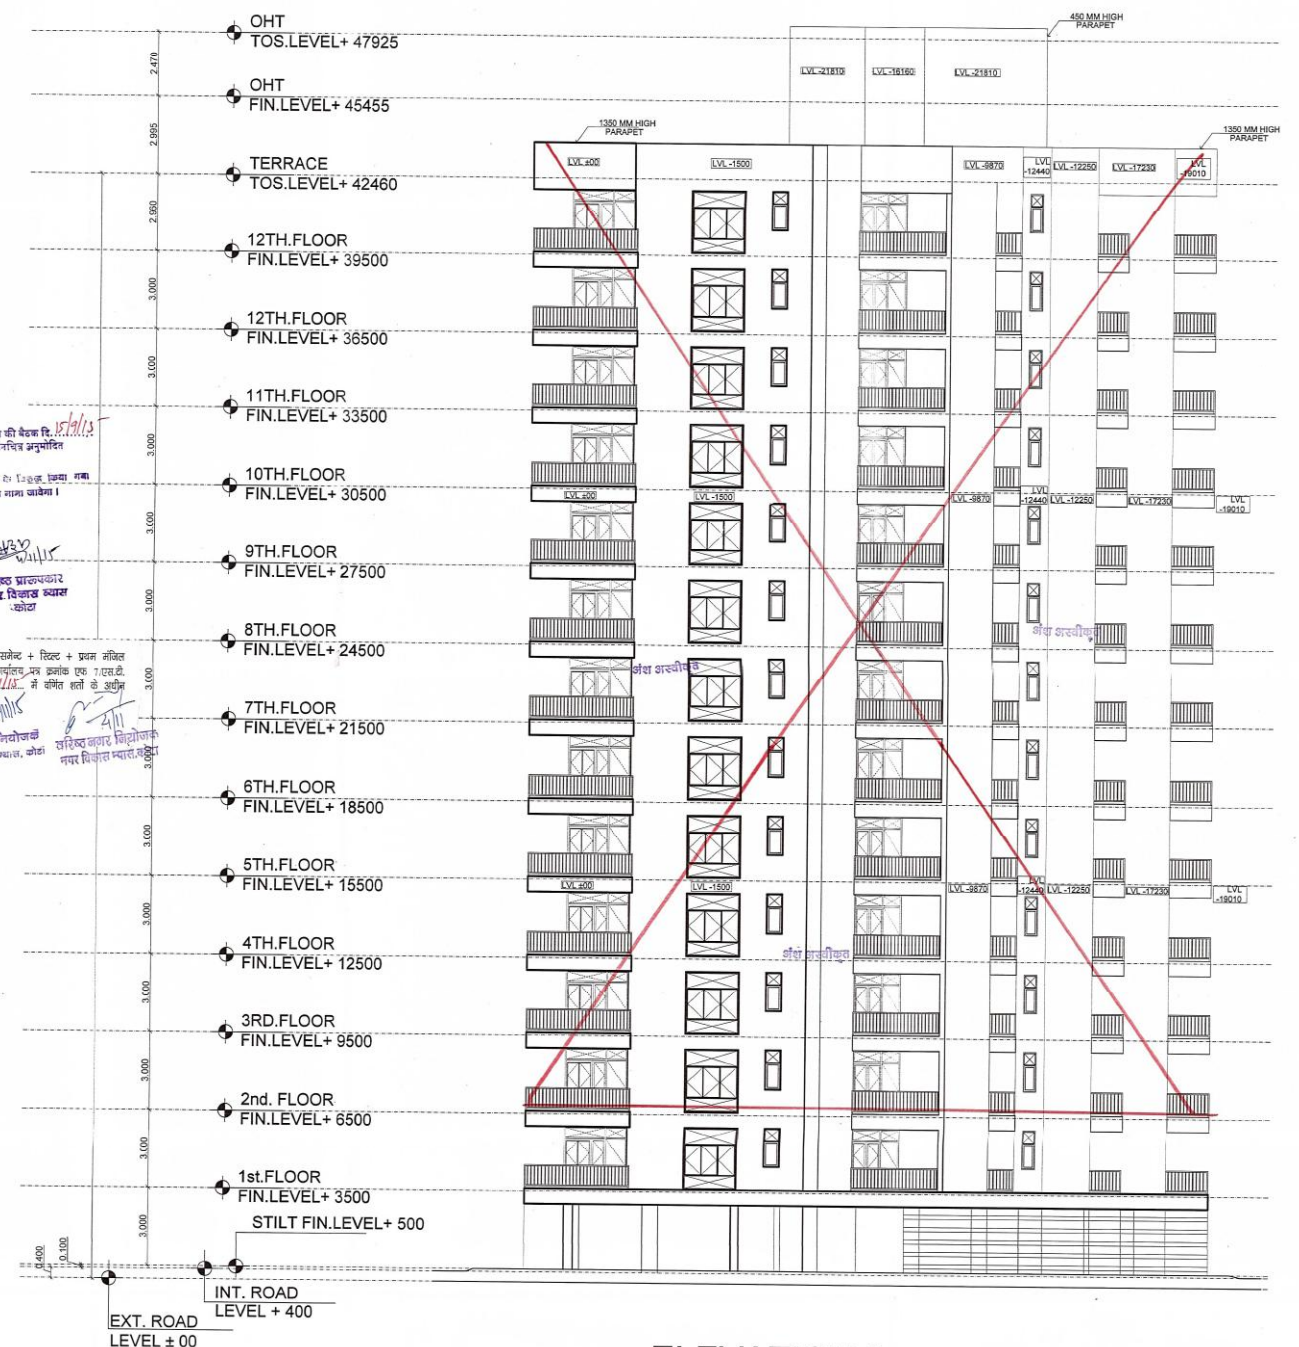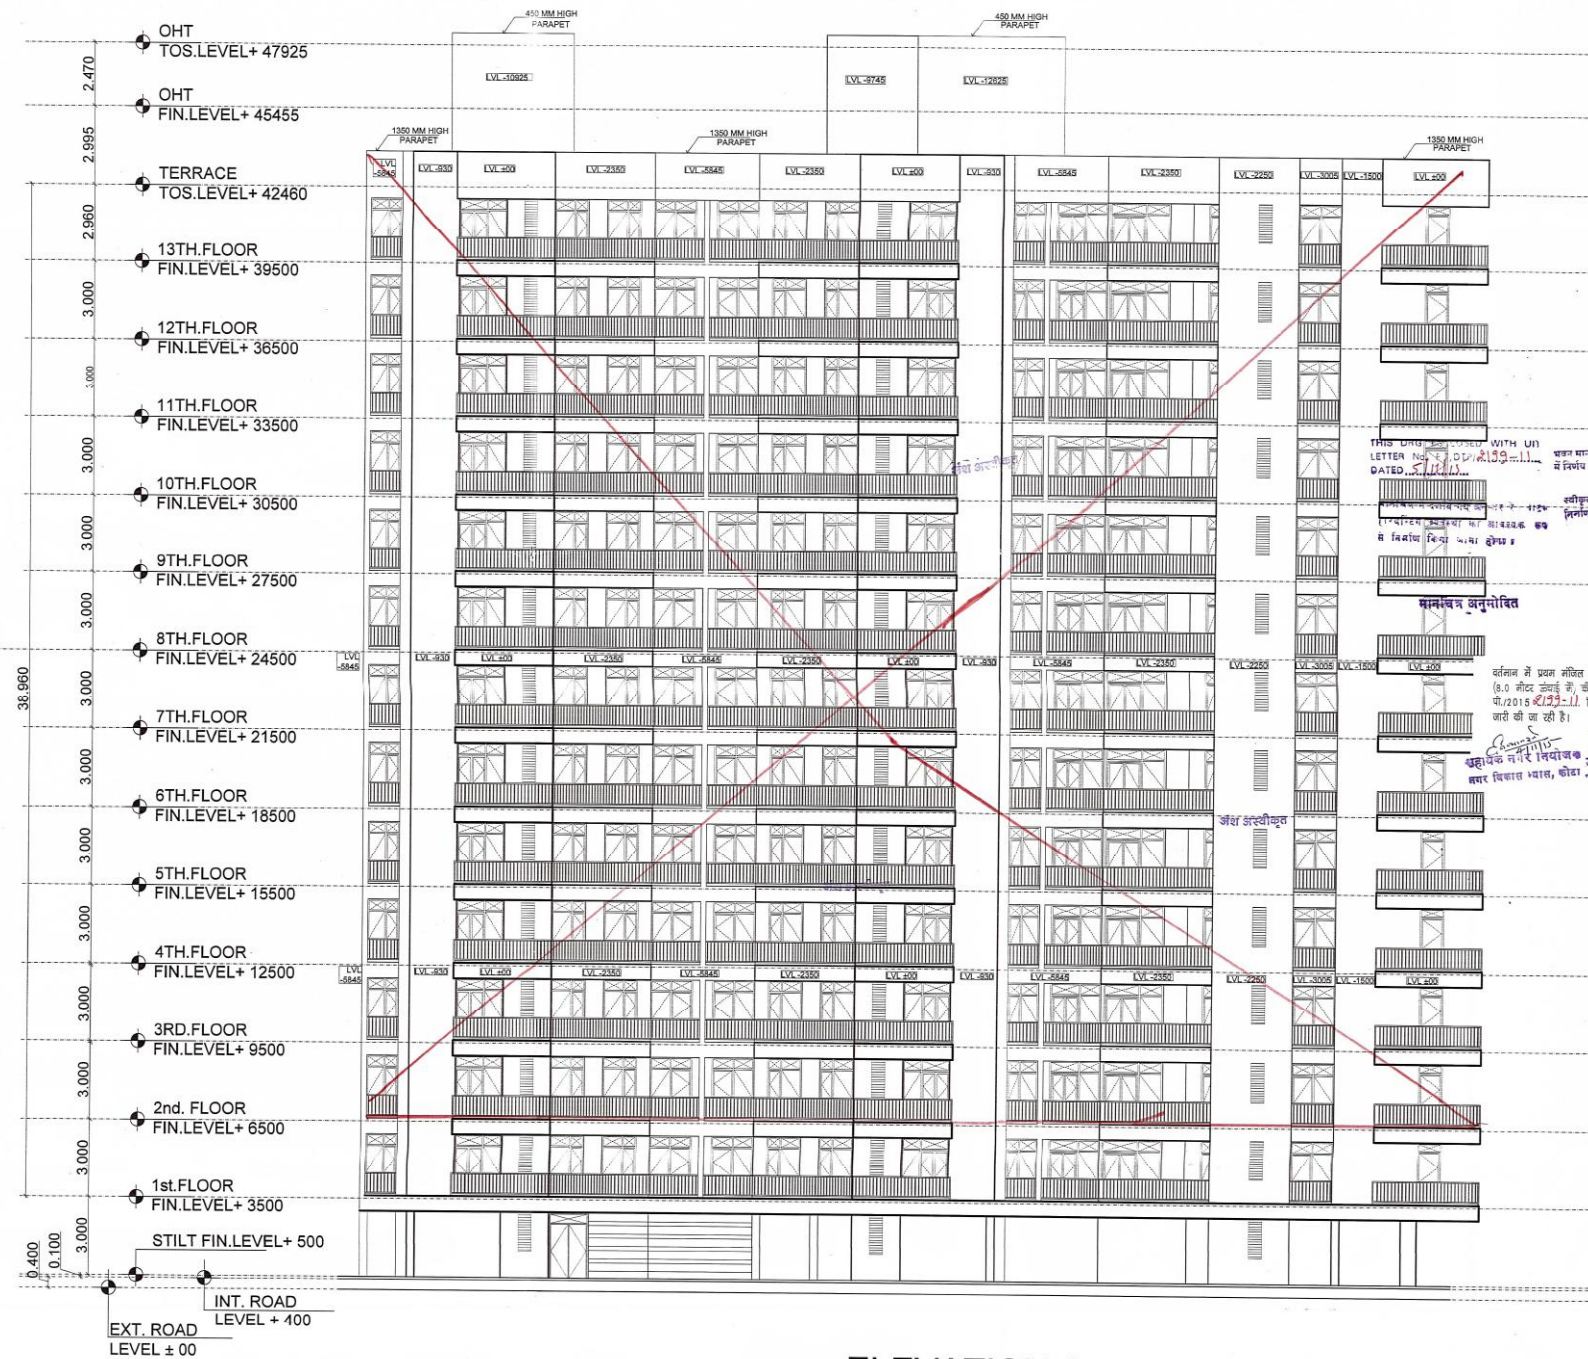

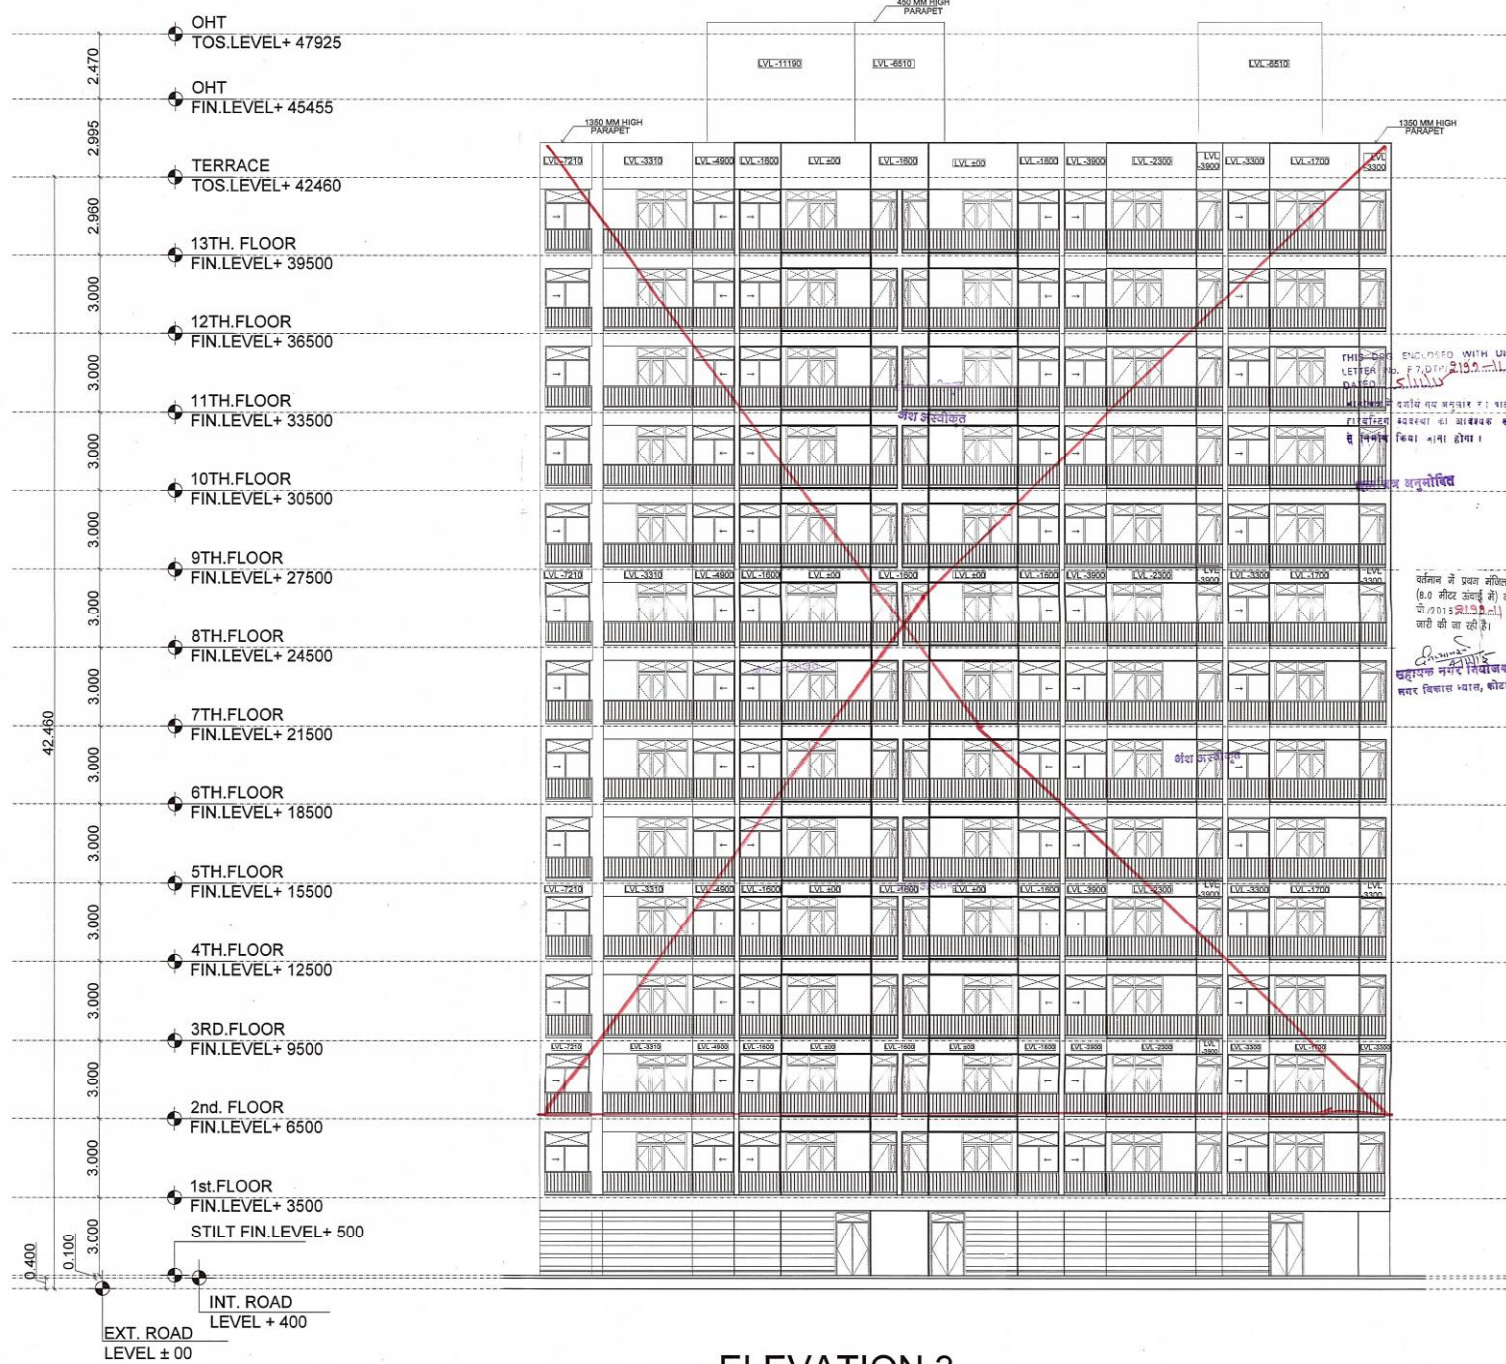

ELEVATION 3

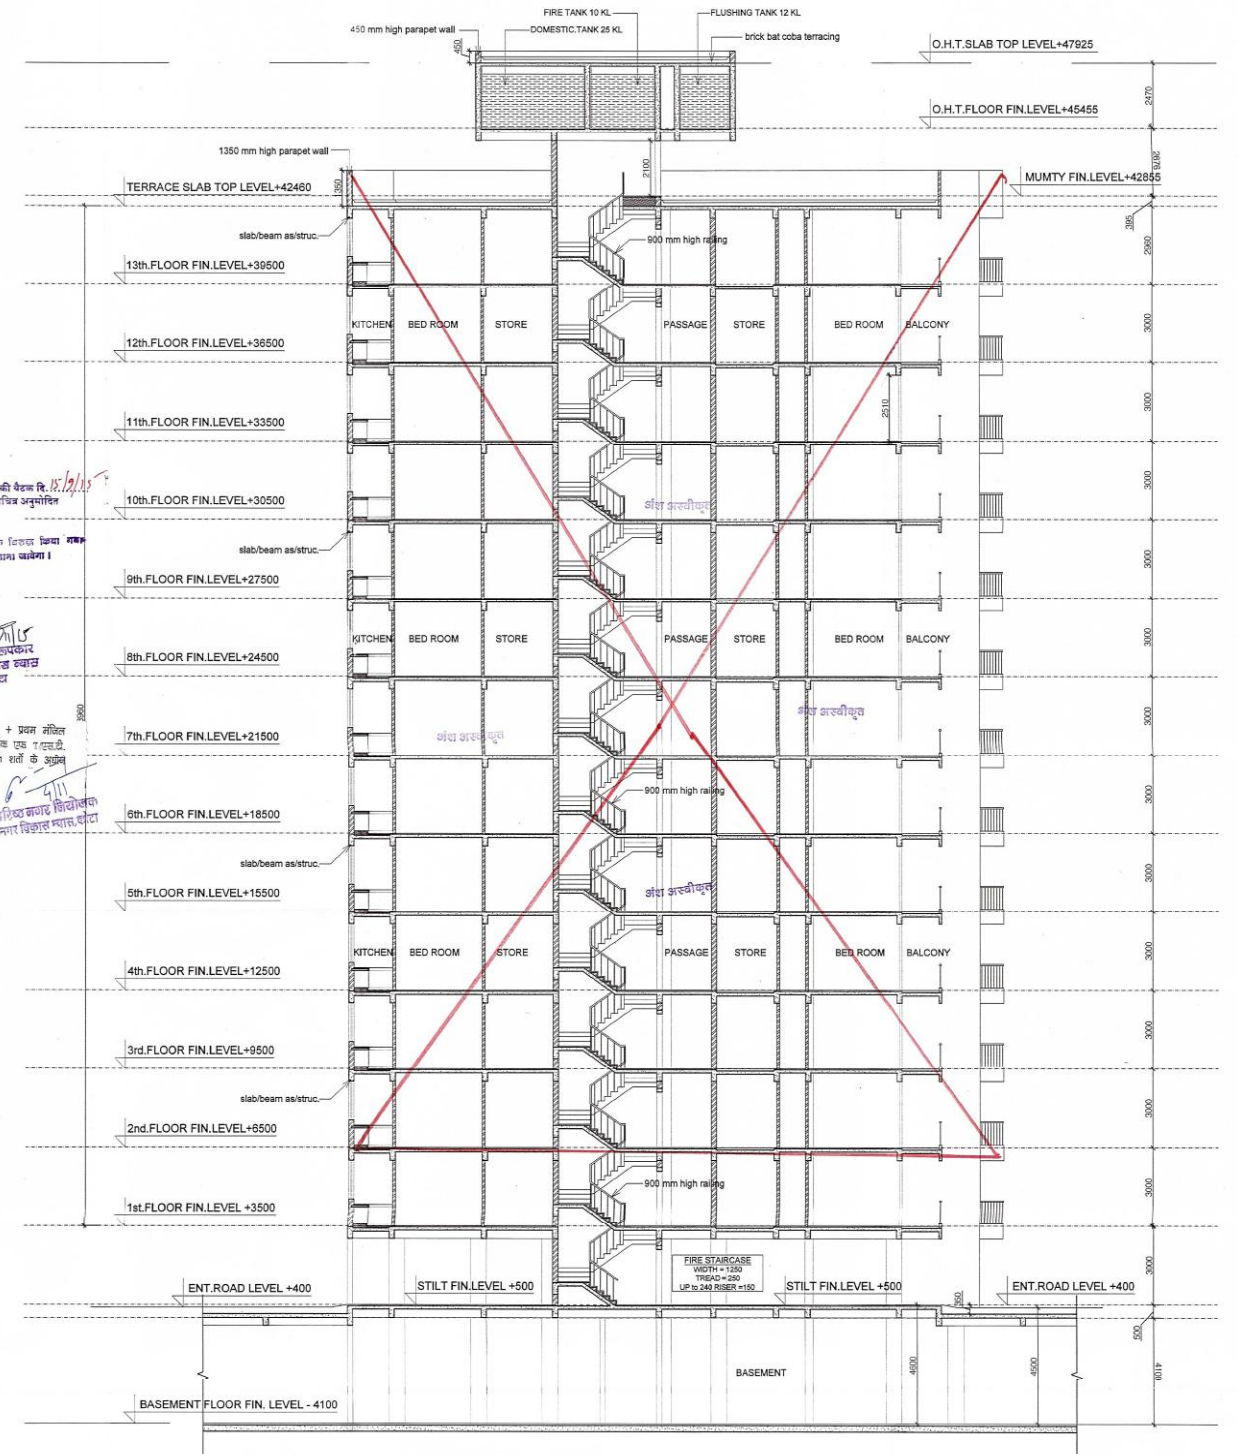

SECTION AA

ARCHITECT'S SIGNATURE  ROHIT GARG CA/94/17868		OWNER'S SIGNATURE For Pranay Infrabuild Pvt. Ltd.  Director	
NAME OF OWNERS PRANAY INFRABUILD PVT. LTD. NEERAJ SUWALKA S/O. GIRRAJ PRASAD SUWALKA DIRECTOR			
PROJECT TITLE PROPOSED GROUP HOUSING SCHEME AT PLOT NO. B, KHASRA NO. 23, VILLAGE KUNHADI, TEHSIL LADPURA, DIST. KOTA, RAJASTHAN			
DRAWING TITLE (SUBMISSION DRAWING) ELEVATION & SECTION (S+13) TOWER 2			DRG. NO. D12
SCALE - 1:100		DATE - AUGUST, 2015	
DRAWN - SOUMYA		CHECKED - NITIN	
 R.K. & ASSOCIATES ARCHITECTS, ENGINEERS & PLANNERS E-31, GREEN PARK MAIN, NEW DELHI - 110016, INDIA Tel.: 2656-3158, 2651-0751, 2656-7357 Fax: (011) 2656-2540 E-mail: rka.architects@gmail.com			




THIS DRG ENCLOSED WITH MY
LETTER No. P/2015/1111
DATED 15/09/15
मानचित्र के दस्तावे में अनुमति है।
प्रमाणित प्रकल्प का आशय यह है
के निर्माण किया जा होना।

मानचित्र अनुमति

15/09/15
प्रमाणित प्रकल्प
कार निर्माण


योजना में प्रमाणित तक कुल बेसमेंट + गिफ्ट + प्रथम मंजिल
(8.0 मीटर ऊंचाई से) की अधिकतम ऊंचाई पर कुल एक 7/एस.टी.
पी.2015/1111-4 दिनांक 15/09/15 से दर्ज हों के अंतर्गत
करीब की जा रही है।
आपके मर्दाना निर्माण पर नगर निगम का अधिकार विरोधी
कार विचार प्राप्त, कोर्टमार्श विचार प्राप्त, और नगर विचार प्राप्त, और

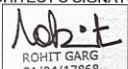ARCHITECT'S SIGNATURE  ROHIT GARG CA/94/17868		OWNER'S SIGNATURE For Pranay Infrabuild Pvt. Ltd.  Director	
NAME OF OWNERS PRANAY INFRABUILD PVT. LTD. NEERAJ SUWALKA S/O. GIRRAJ PRASAD SUWALKA DIRECTOR			
PROJECT TITLE PROPOSED GROUP HOUSING SCHEME AT PLOT NO. B, KHASRA NO. 23, VILLAGE KUNHADI, TEHSIL LADPURA, DIST. KOTA, RAJASTHAN			
DRAWING TITLE (SUBMISSION DRAWING) PLANS SCALE - 1:100 DRAWN - TUHENA		DRG. NO. TOWER 3 (S+13) D13 DATE - AUG., 2015 CHECKED - NITIN	
 R.K. & ASSOCIATES Architects, Engineers & Planners E-31, GREEN PARK MAIN, NEW DELHI - 110016, INDIA Tel.: 2696-3158, 2651-6751, 2656-7357 Fax: (011) 2686-2540 E-mail: rk.associates@gmail.com			


15/09/15
ROHIT GARG
CA/94/17868

ELEVATION - B
1st-2nd FLOOR PLAN

ELEVATION - A
TYPICAL (3rd-12th) FLOOR PLAN

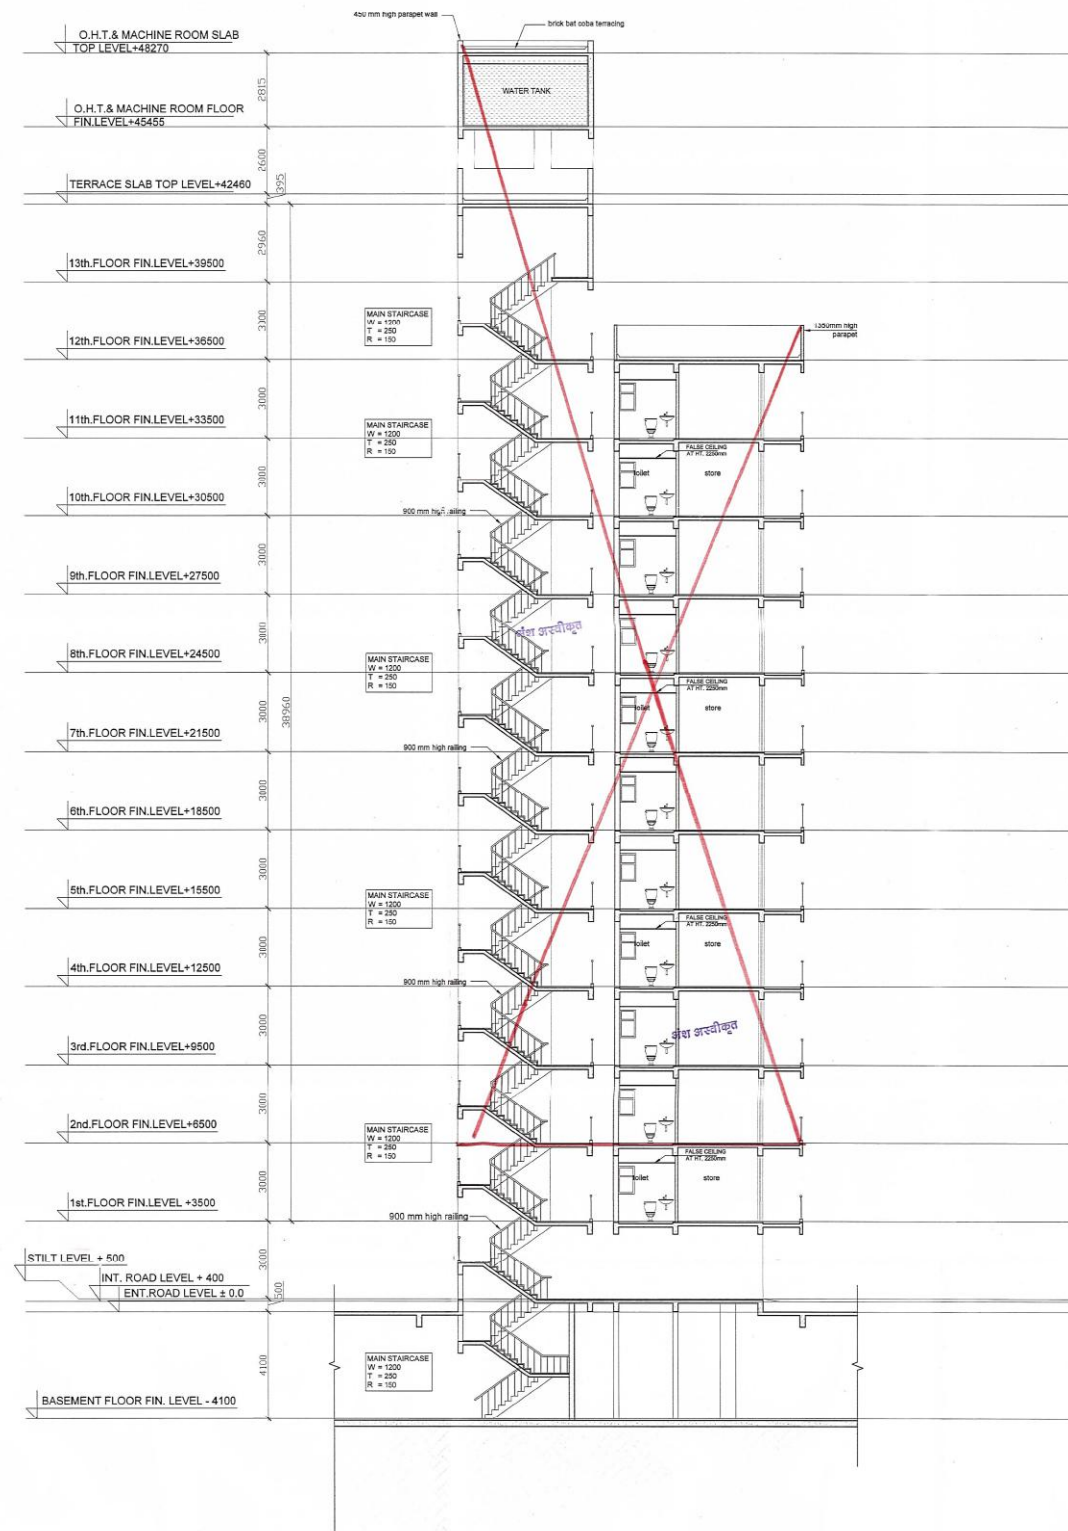

SECTION A-A

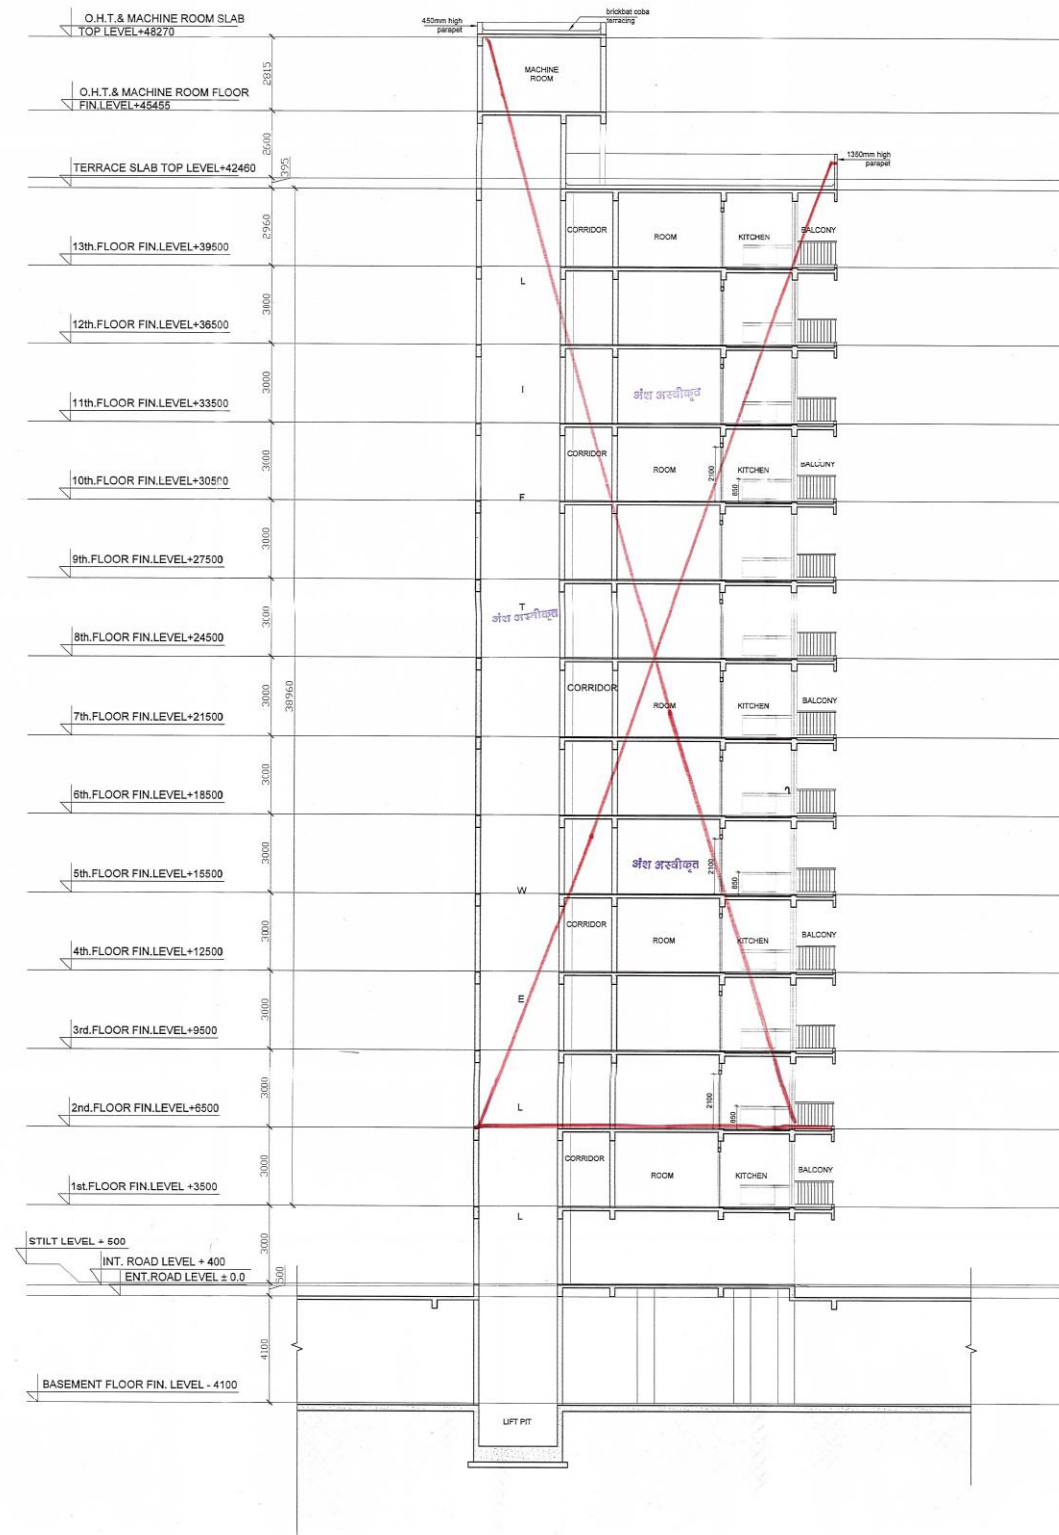

SECTION B-B


THIS DRG ENCLOSED WITH MY
LETTER NO. R/218/2015, DATED 21.08.15
DATE 21.08.15
आमंत्रित करने के लिए मैं आपको सूचित करता हूँ कि
आमंत्रित करने के लिए मैं आपको सूचित करता हूँ कि

ARCHITECT'S SIGNATURE	OWNER'S SIGNATURE
NAME OF OWNERS PRANAY INFRABUILD PVT. LTD. NEERAJ SUWALKA S/O. GIRRAJ PRASAD SUWALKA DIRECTOR	
PROJECT TITLE PROPOSED GROUP HOUSING SCHEME AT PLOT NO. B, KHASRA NO. 23, VILLAGE KUNHADI, TEHSIL LADPURA, DIST. KOTA, RAJASTHAN	
DRAWING TITLE SECTIONS	(SUBMISSION DRAWING) TOWER 3 (S+13)
SCALE - 1:100	DATE - AUG., 2015
DRAWN - JAPINDER	CHECKED - NITIN
DRG. NO. D17	
 R.K. & ASSOCIATES Architects, Engineers & Planners E-31, GREEN PARK MAIN, NEW DELHI - 110016, INDIA Tel.: 26 96-3158, 26 51-8751, 26 56-7357 Fax: (011) 2686-2540 E-mail: rka.architects@gmail.com	


ROHIT GARG
CA/94/17868

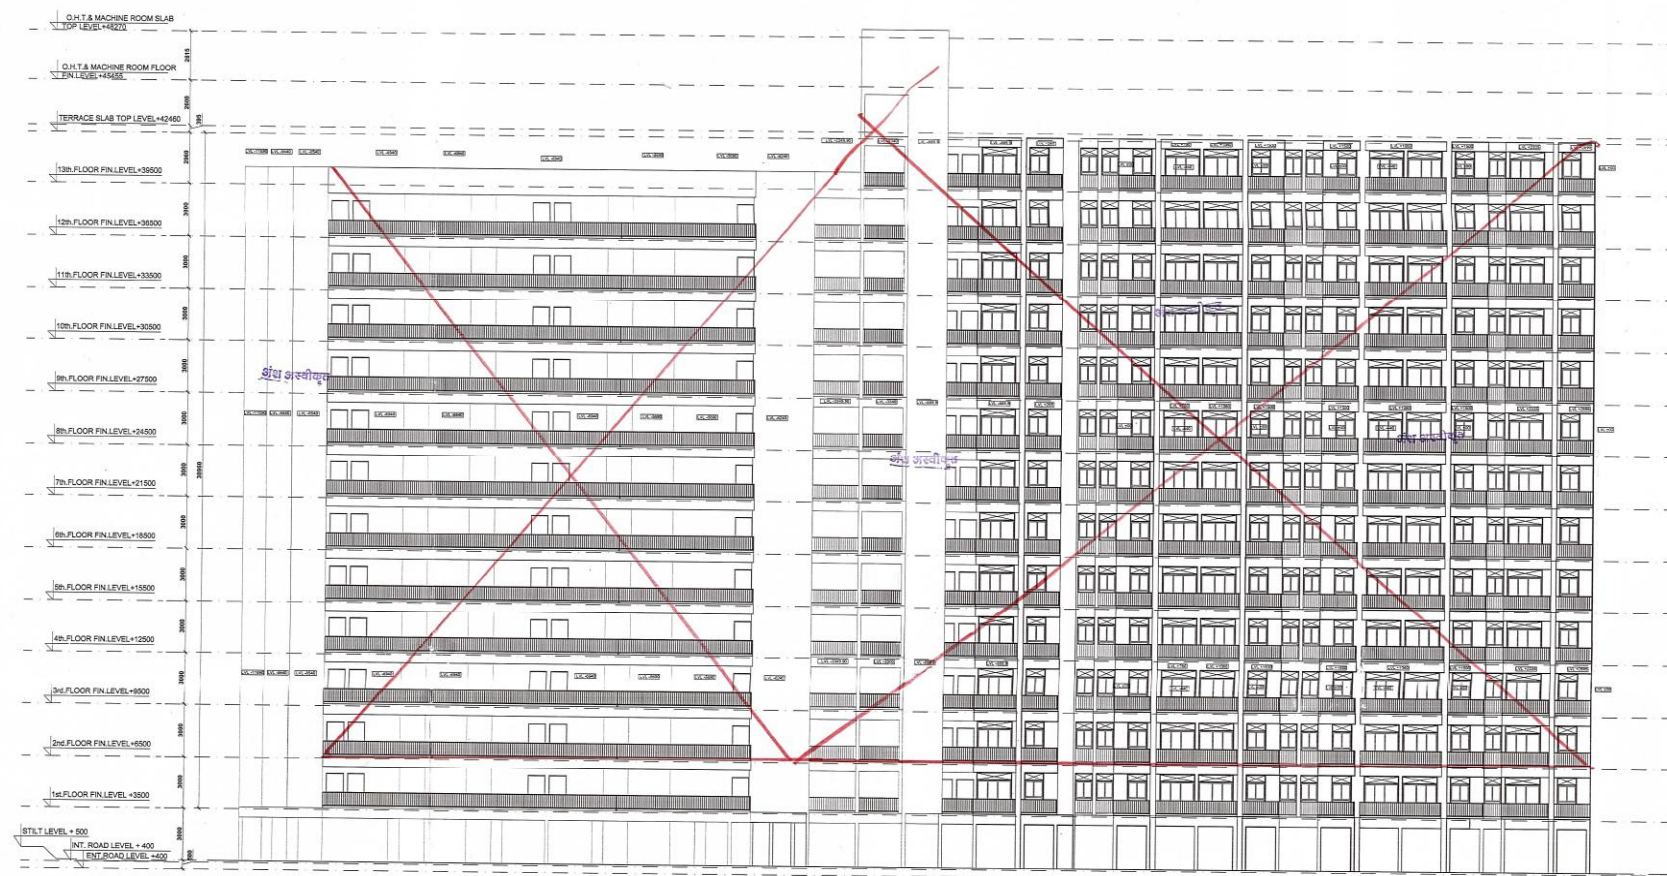

ELEVATION - B

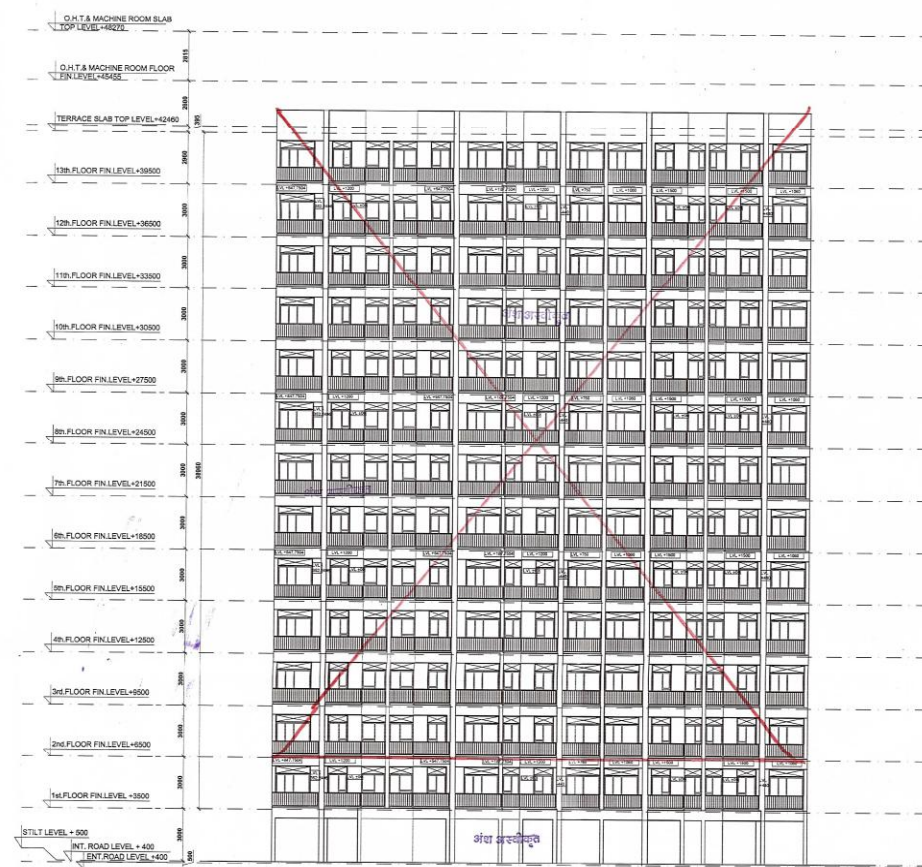



ELEVATION - C

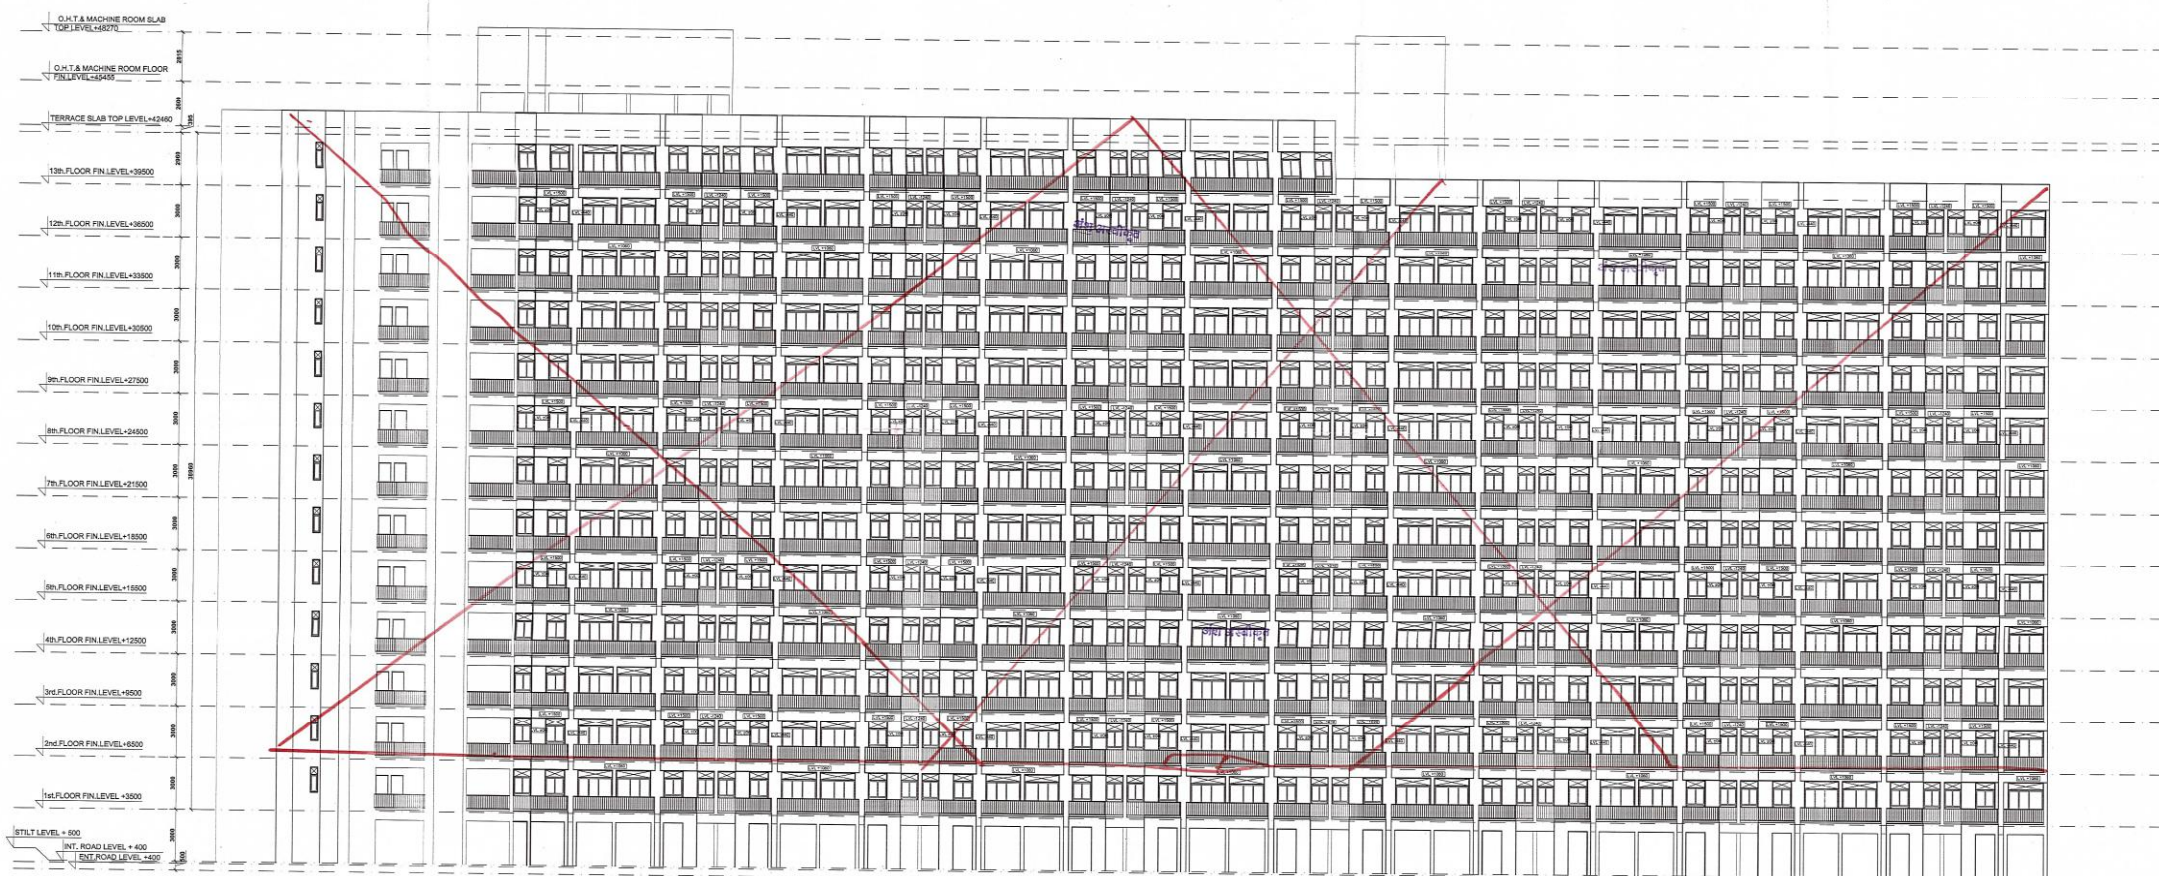

ELEVATION - A

THIS DRAWING ENCLOSED WITH LETTER NO. 1/2/2015/1111 DATED 11.11.2015
 बंधन मानक संहिता की शर्तों के अन्तर्गत
 वास्तु चित्र के अन्तर्गत
 वास्तु चित्र के अन्तर्गत
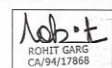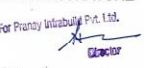ARCHITECT'S SIGNATURE 	OWNER'S SIGNATURE 
NAME OF OWNERS PRANAY INFRABUILD PVT. LTD. NEERAJ SUWALKA S/O. GIRRAJ PRASAD SUWALKA DIRECTOR	
PROJECT TITLE PROPOSED GROUP HOUSING SCHEME AT PLOT NO. B, KHASRA NO. 23, VILLAGE KUNHADI, TEHSIL LADPURA, DIST. KOTA, RAJASTHAN	
DRAWING TITLE ELEVATIONS	(SUBMISSION DRAWING) TOWER 3 (S+13) DRG. NO. D18
SCALE - 1:150	DATE - AUG., 2015
DRAWN - MONI	CHECKED - NITIN
 R.K. & ASSOCIATES Architects, Engineers & Planners E-31, GREEN PARK MAIN, NEW DELHI - 110016, INDIA Tel.: 2696-3158, 2651-6751, 2656-7357 Fax: (011) 2686-2540 E-mail: rka.architects@gmail.com	