



कार्यालय नगर विकास न्यास, कोटा

क्रमांक :- एफ 7/डी0टी0पी0/2017/467-81

दिनांक :- 23/10/2017

निमित्त :-

श्री राजकुमार अग्रवाल
298, हथरोई स्कूल के सामने,
होटल आशीष, अजमेर रोड, जयपुर।

विषय :- भूखण्ड सं0 1 खसरा नं0 95 ग्रुप हाउसिंग ग्राम रामचन्द्रपुरा, कोटा के मानचित्र स्वीकृति के सम्बन्ध में।

उपरोक्त विषयान्तर्गत लेख है कि आपके द्वारा भवन निर्माण स्वीकृति हेतु प्रस्तुत मानचित्रों के परीक्षण उपरान्त प्रस्तुत प्रस्ताव पर भवन निर्माण समिति की बैठक दिनांक 8-9-17 व 5-10-17 में लिये गए निर्णय के क्रम में निम्न शर्तों के साथ भवन मानचित्र स्वीकृत किये जाते हैं :-

1. यह स्वीकृति राजस्थान भवन विनियम 2013(संशोधित) तथा अन्य सुसंगत विधिक प्रावधानों के अध्याधीन रहेगी तथा इसके प्रावधानों से सुसंगत होने की सीमा तक ही मान्य रहेगी।
2. राजस्थान भवन विनियम 2013(संशोधित) तथा अन्य सुसंगत विधिक प्रावधानों की अपेक्षाओं के अनुरूप भवन निर्माण करने की जिम्मेदारी भवन निर्माण अनुज्ञाधारी की रहेगी। स्वीकृति में किसी भी प्रकार की त्रुटि, भूल एवं लोप को विनियम के प्रावधानों में छूट के रूप में नहीं लिया जा सकेगा। विनियम एवं अन्य सुसंगत विधिक प्रावधानों के अनुसार निर्माण कराने का दायित्व अनुज्ञाधारी का रहेगा। भवन निर्माण स्वीकृति नगर नियोजन शाखा द्वारा प्रकरण का परीक्षण करने पर प्रस्तावानुसार हुई है तथापि यदि स्वीकृति में विनियम एवम् अन्य सुसंगत विधिक प्रावधानों के अनुसार कोई त्रुटि, भूल एवं लोप है, तो भवन निर्माण अनुज्ञाधारी का दायित्व रहेगा कि उस बारे में न्यास कार्यालय का ध्यान आकर्षित करे। त्रुटि, भूल एवं लोप के आधार पर निर्माण मान्य नहीं होगा।
3. प्रस्तुत मानचित्र के अनुसार B + S + 12 मंजिल की स्वीकृति चाही गई है। न्यास की नगर नियोजन शाखा द्वारा आपके प्रस्ताव के परीक्षण उपरान्त प्रस्तुत प्रस्तावानुसार कार्यालय आदेश क्रमांक 59 दिनांक 3/10/17 के अनुसार इस समय B + S + 8 (अधिकतम 30 मी. के भीतर 28.15 मी. तक) व 1.848 एफ.ए.आर. की स्वीकृति भवन विनियम 2013(संशोधित) एवं अन्य सुसंगत प्रावधानों से सुसंगत होने की सीमा तक ही जारी की जा रही है। यह स्वीकृति भवन विनियम 2013(संशोधित) एवं अन्य सुसंगत विधिक प्रावधानों से सुसंगत होने की सीमा तक ही मान्य रहेगी।
4. राज्य सरकार के परिपत्र दिनांक 29/6/17 के बिन्दु सं0 6 के कक्ष में आप द्वारा बेटरमेन्ट लेवी की राशि की 4, छमाही किस्तों में से प्रथम किश्त की राशि दिनांक 17/10/17 को जमा करवा दी गयी है। व शेष 3 किस्तों के अग्रिम चैक क्रमशः क्रमांक 849083 दिनांक 17/4/18, 849085 दिनांक 17/10/2018 व 849086 दिनांक 17/4/2019 प्रस्तुत किये गये हैं। जिनका भुगतान किसी भी कारणवश समय पर न होने की दशा में स्वीकृति निरस्त योग्य होगी।
5. 2.25 से अधिक एफ0ए0आर0 एवं 30 मीटर से अधिक ऊंचाई राज्य सरकार से स्वीकृति पश्चात् जारी की जावेगी।
6. भवन विनियम 2013 एवं अन्य सुसंगत विधिक प्रावधानों के विरुद्ध निर्माण किये जाने पर "राजस्थान नगर सुधार अधिनियम 1959 की धारा 91 के अन्तर्गत अवैध निर्माण को न्यास द्वारा ध्वस्त किया जा सकेगा, जिसकी समस्त जिम्मेदारी आपकी स्वयं की होगी तथा उक्त कार्यवाही पर किया गया समस्त व्यय आपको ही वहन करना होगा।
7. पार्किंग सम्बन्धी पर्याप्त व्यवस्था मानचित्र में बेसमेन्ट + स्टिल्ट पर दर्शाये अनुसार की जानी होगी तथा आप द्वारा प्रस्तुत शपथ-पत्र अनुसार पार्किंग क्षेत्र को अन्य उपयोग में नहीं लिया जावेगा।
8. पार्किंग, लिफ्ट इत्यादी सुविधा क्षेत्र के रख-रखाव की व्यवस्था आपको सुनिश्चित करनी होगी।
9. पार्किंग क्षेत्र में कोई निर्माण कार्य नहीं किया जावेगा, न ही इसका बेचान किया जावेगा। इसे पार्किंग हेतु खुला रखा जावेगा। अन्यथा न्यास आपके खर्चे पर बिना पूर्व सूचना पार्किंग क्षेत्र में किये गए निर्माण को ध्वस्त करने के लिये स्वतंत्र होगा।
10. भवन निर्माण के स्ट्रक्चरल डिजाईन की जिम्मेदारी आपके द्वारा नियुक्त वास्तुविद् की होगी। निम्न हस्ताक्षरकर्ता/न्यास किसी भी स्थिति में इसके लिये उत्तरदायी नहीं होगा। निर्माण कार्य अधिकृत वास्तुविद्/अभियन्ता की देख-रेख में करवाया जाना होगा। निर्माण कार्य पूर्ण होने पर सम्बन्धित वास्तुविद् द्वारा प्रमाण-पत्र प्रस्तुत करना होगा एवं दिये गए अण्डरटेकिंग के अनुसार भूकम्प से सुरक्षा हेतु आवश्यक व्यवस्था की जानी होगी।
11. बेसमेन्ट हेतु खुदाई सुरक्षित रूप से की जावेगी, जिससे की आस-पास के भवनों को क्षति होने की आशंका नहीं रहे, तथा आस-पास के लोगों को कोई व्यवधान नहीं हो।
12. यह स्वीकृति भवन निर्माण के लिये दी जा रही है। किसी भी न्यायालय अथवा वाद में इसे भूखण्ड स्वामित्व साक्ष्य के रूप में प्रस्तुत नहीं किया जा सकेगा।
13. निर्माण पश्चात् भवन को उपयोग में लेने से पूर्व नगर निगम से रथाई अनापत्ति प्रमाण-पत्र प्राप्त कर न्यास से अधिवास प्रमाण-पत्र प्राप्त करना होगा।
14. मानचित्र में दर्शाये अनुसार भूमिगत जलस्तर बढ़ाने हेतु रेनवाटर हारवेस्टिंग व्यवस्था का निर्माण आवश्यक रूप से किया जाना होगा।
15. मुख्यमंत्री जन आवास योजना-2015 के प्रावधान 1-ए के तहत आवासीय FAR के 7.5 प्रतिशत क्षेत्रफल के बराबर EWS/LIG आवास उपलब्ध करवाने होंगे। जिनके आवंटन की कार्यवाही मुख्यमंत्री जन आवास योजना के Provision-1A के अनुसार निर्धारित प्रक्रिया एवं निर्धारित दर अनुसार सम्पादित की जानी होगी।
16. अनुज्ञा प्राप्ति के दो वर्ष के भीतर अथवा कार्य प्रारंभ करने के छः माह के अन्दर जो भी कम हो, अनुज्ञाधारी को भवन निर्माण कार्य प्रारंभ करने के आशय की सूचना न्यास को देनी होगी।

17. प्लिनथ लेवल पर निर्माण के पश्चात् न्यास को सूचित करना होगा। न्यास के वरिष्ठ नगर नियोजक द्वारा नियुक्त उप/सहायक नगर नियोजक द्वारा मौके पर निर्माण की जांच उपरान्त प्लिनथ का निर्माण स्वीकृत मानचित्र एवं भवन विनियम 2013(संशोधित) एवं विधिक अन्य सुसंगत प्रावधानों के अनुसार पाये जाने पर पत्र जारी करने के उपरान्त आगामी निर्माण भवन विनियम 2013 एवं अन्य सुसंगत विधिक प्रावधानों अनुसार किया जा सकेगा।
18. स्वीकृत मानचित्र में दर्शाये अनुसार इन्फोरमल कॉमर्शियल का प्रावधान रखना होगा।
19. पर्यावरण की दृष्टि से मानचित्र में दर्शाये अनुसार पेड़ लगाने होंगे। भूखण्ड पर प्रत्येक 100 वर्गमीटर क्षेत्र के लिये कम से कम एक वृक्ष के अनुपात में 6 मीटर से अधिक उंचाई ग्रहण करने वाले वृक्ष लगाने होंगे एवं मानचित्र में दर्शाये अनुसार हरियाली क्षेत्र का आवश्यक रूप से विकास किया जाना होगा।
20. भवन की संरचना, डिजाईन नियमानुसार/विहित अनुसार भूकम्परोधी होना आवश्यक है। इस सम्बन्ध में स्ट्रक्चरल इन्जिनियर से प्रमाण-पत्र प्रस्तुत करना होगा। स्ट्रक्चरल इन्जिनियर जिसके भूकम्परोधी प्रावधान हेतु घोषणा पत्र एवं रचनात्मक सुरक्षा हेतु घोषणा की गयी है, उसी इन्जिनियर से भवन निर्माण पूर्ण होने के पश्चात् यह शपथ पत्र लेकर प्रस्तुत करना होगा कि भवन का निर्माण भूकम्परोधी प्रावधान नेशनल बिल्डिंग कोड के पार्ट VI के प्रावधानों के अनुरूप किया गया है। उसके पश्चात् ही अधिवास प्रमाण पत्र जारी किया जावेगा।
21. समय-समय पर राज्य सरकार/न्यास द्वारा जारी नियमों/आदेशों की पालना करनी होगी।
22. राज्य सरकार के पत्र क्रमांक प.10(154)न.वि.वि./3/80 दिनांक 04-11-2008 की पालना की जानी होगी।
23. मानचित्र में दर्शाये गए अनुसार सौर उर्जा का प्रावधान किया जाना होगा।
24. आवेदक मोके पर विहित अनुसार सूचना प्रदर्शित करेगा एवं अभिलेख रखेगा तथा इस स्वीकृति पत्र की प्रत भी रखेगा।
25. सॉलिड वेस्ट डिस्पोजल के लिए प्रत्येक 30 फ्लेट्स/निवास इकाईयों अथवा उसके अंश पर 2 कचरापात्र का प्रावधान आवश्यक होगा, जिसमें एक पात्र 0.67 क्यूबिक मीटर का नॉन बायोडिग्रेडेबल तथा 1.33 क्यूबिक मीटर का दूसरा पात्र बायोडिग्रेडेबल अपशिष्ट हेतु होगा। इन्हें भूतल पर ऐसे स्थान पर रखा जावेगा जहाँ से सफाई कर्मचारी द्वारा आसानी से उठाया जा सके।
26. लेबर सैस, लेबर डिपार्टमेंट में विकासकर्ता स्वयं के स्तर पर जमा करावे तथा भवन के पूर्णता प्रमाण-पत्र प्राप्त करने से पूर्व लेबर सैस जमा का प्रमाण न्यास में प्रस्तुत करना होगा।
27. आवेदक/विकासकर्ता को Rajasthan Real Estate (Regulation and Development) Act, 2016 के अन्तर्गत बनाये गए Rajasthan Real Estate (Regulation and Development) Rules, 2017 के अन्तर्गत Real Estate Regulatory Authority, Rajasthan, Jaipur में उक्त प्रोजेक्ट का रजिस्ट्रेशन करवाना होगा एवं उपरोक्त नियमों में वर्णित प्रावधानों की पालना की जानी होगी। अतः Real Estate Regulators Authority में रजिस्ट्रेशन करवाकर न्यास में प्रस्तुत करें। उक्त प्रोजेक्ट का RERA में रजिस्ट्रेशन होने के उपरान्त ही आवासों के विक्रय इत्यादि की कार्यवाही की जा सकेगी। उक्त प्रोजेक्ट का Real Estate Regulators Authority में पंजीयन नहीं कराने व उपरोक्त नियमों में वर्णित प्रावधानों की पालना नहीं किये जाने की स्थिति में यह स्वीकृति मान्य नहीं होगी।
28. उपरोक्त शर्तों की पालना करने तथा भवन में आवश्यक प्रावधान किये जाने पर एवं अधिवास प्रमाण-पत्र जारी होने पर ही अग्निशमन घरोहर राशि, अन्य अमानत राशि की बैंक गारंटी लौटाई जावेगी।

(आनन्दी लाल वैष्णव)
सचिव

नगर विकास न्यास, कोटा
दिनांक :- 23/10/2017

क्रमांक :- एफ 7/डी0टी0पी0/2017/ 463-81

प्रतिलिपि निम्नलिखित को सूचना एवं आवश्यक कार्यवाही हेतु :-

1. अतिरिक्त मुख्य अभियंता, नगर विकास न्यास, कोटा।
2. उप सचिव I/II/III, नगर विकास न्यास, कोटा
3. वरिष्ठ नगर नियोजक, नगर विकास न्यास, कोटा
4. संयुक्त श्रम आयुक्त, कलेक्ट्रेट परिसर, कोटा को प्रेषित कर लेख है कि सैस की राशि अपने विभाग स्तर पर वसूल किया जाना सुनिश्चित करें।
5. अधिशाषी अभियन्ता I/II/III/IV को प्रेषित कर लेख है कि सम्बन्धित कनिष्ठ अभियंता को भी समय-समय पर जांच हेतु निर्देशित करें।
6. अधिशाषी अभियंता (आवास), नगर विकास न्यास, कोटा
7. उप नगर नियोजक, नगर विकास न्यास, कोटा
8. लेखाधिकारी, नगर विकास न्यास, कोटा
9. सहायक नगर नियोजक, नगर विकास न्यास, कोटा
10. तहसीलदार प्रथम/द्वितीय/तृतीय, नगर विकास न्यास, कोटा
11. वरिष्ठ विधि अधिकारी, नगर विकास न्यास, कोटा
12. ड्राईंग शाखा को रिकार्ड हेतु।

वरिष्ठ नगर नियोजक
नगर विकास न्यास, कोटा

THIS DMS ENCLOSED
WITH BIL LETTER NO
4-11/2-2017/24
K.A.11/2-2017/24

महानगर नगरपालिकाको विकास विभाग
बाट जारी भएको भवन निर्माण अनुमति पत्र
को लागि यो योजना प्रस्तुत गरिएको छ।

समावेशी
समावेशी
समावेशी

समावेशी
समावेशी
समावेशी



PROJECT:-
PROPOSED GROUP HOUSING AT PLOT NO. 01,
VILLAGE - BHACHANDAPURA, NEAR VILLAGE POLICE LINE,
KATHMANDU, NEPAL

FOR OWNERS/STRUCTURAL ENGINEER/ARCHITECT/

DATE: 10/10/2017

SCALE: 1:100

PROJECT NO. 1110

ARCHITECT: 1110

STRUCTURAL ENGINEER: 1110

DATE: 10/10/2017

SCALE: 1:100

PROJECT NO. 1110

ARCHITECT: 1110

STRUCTURAL ENGINEER: 1110

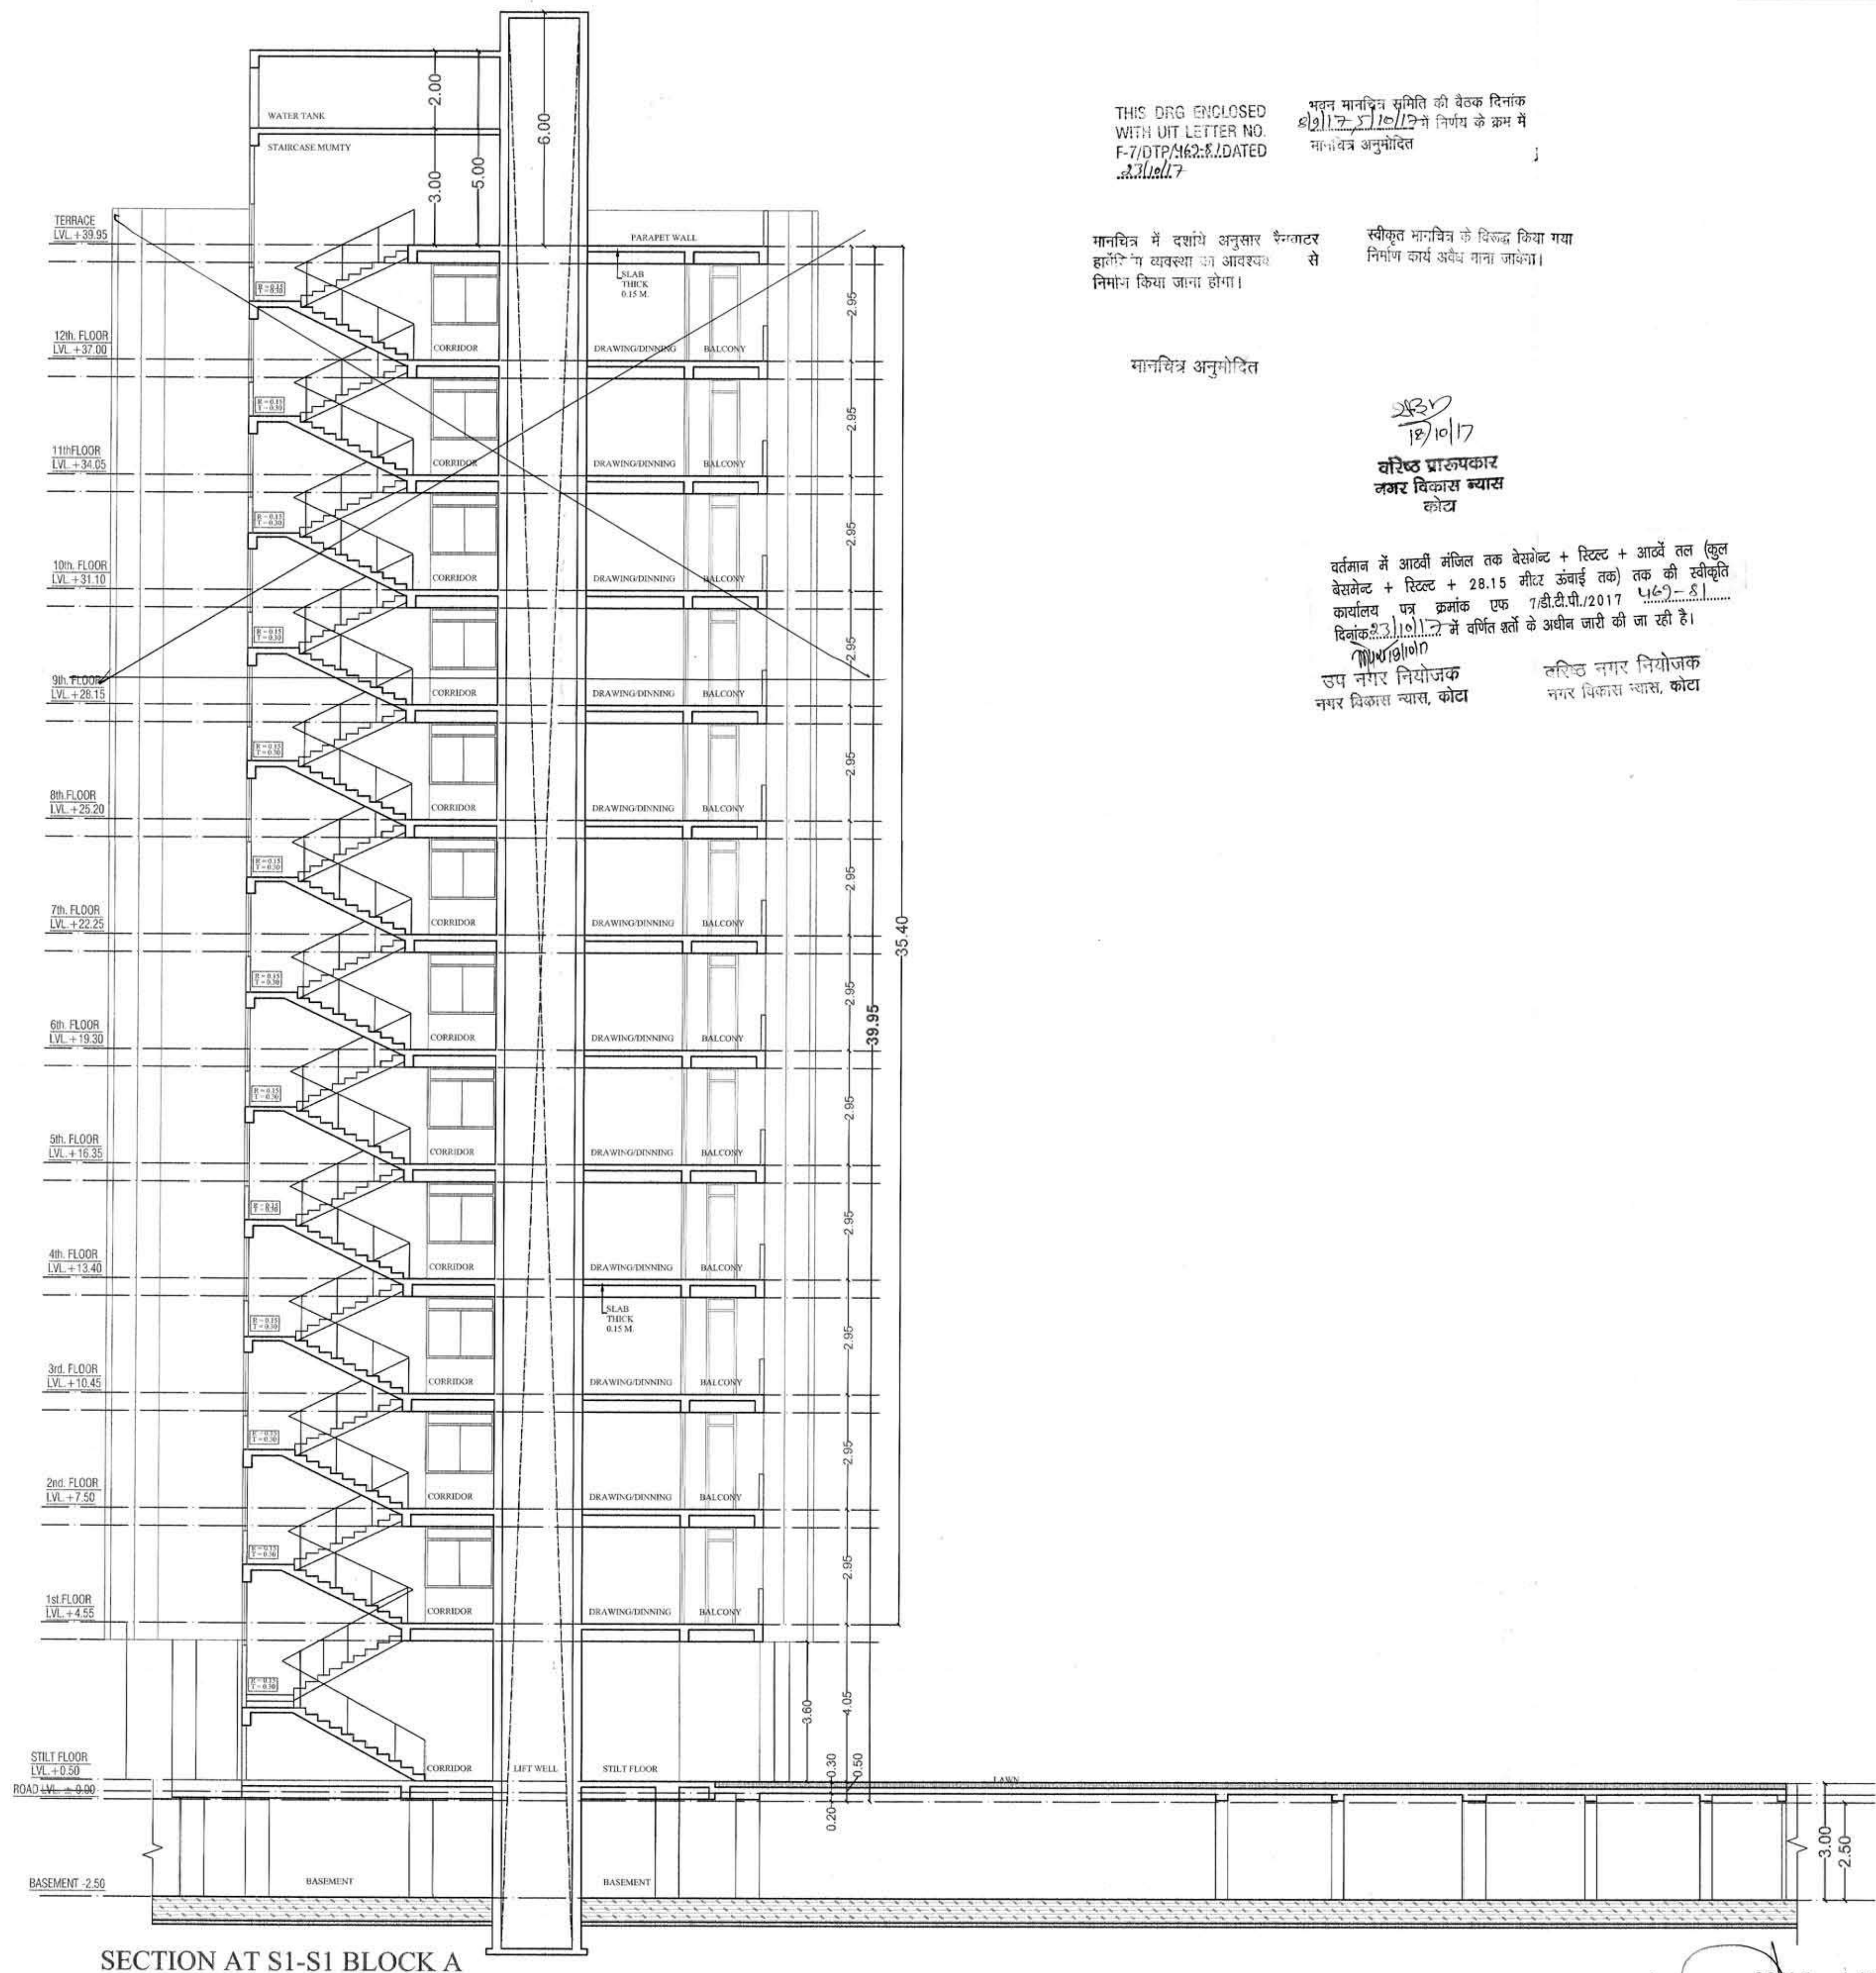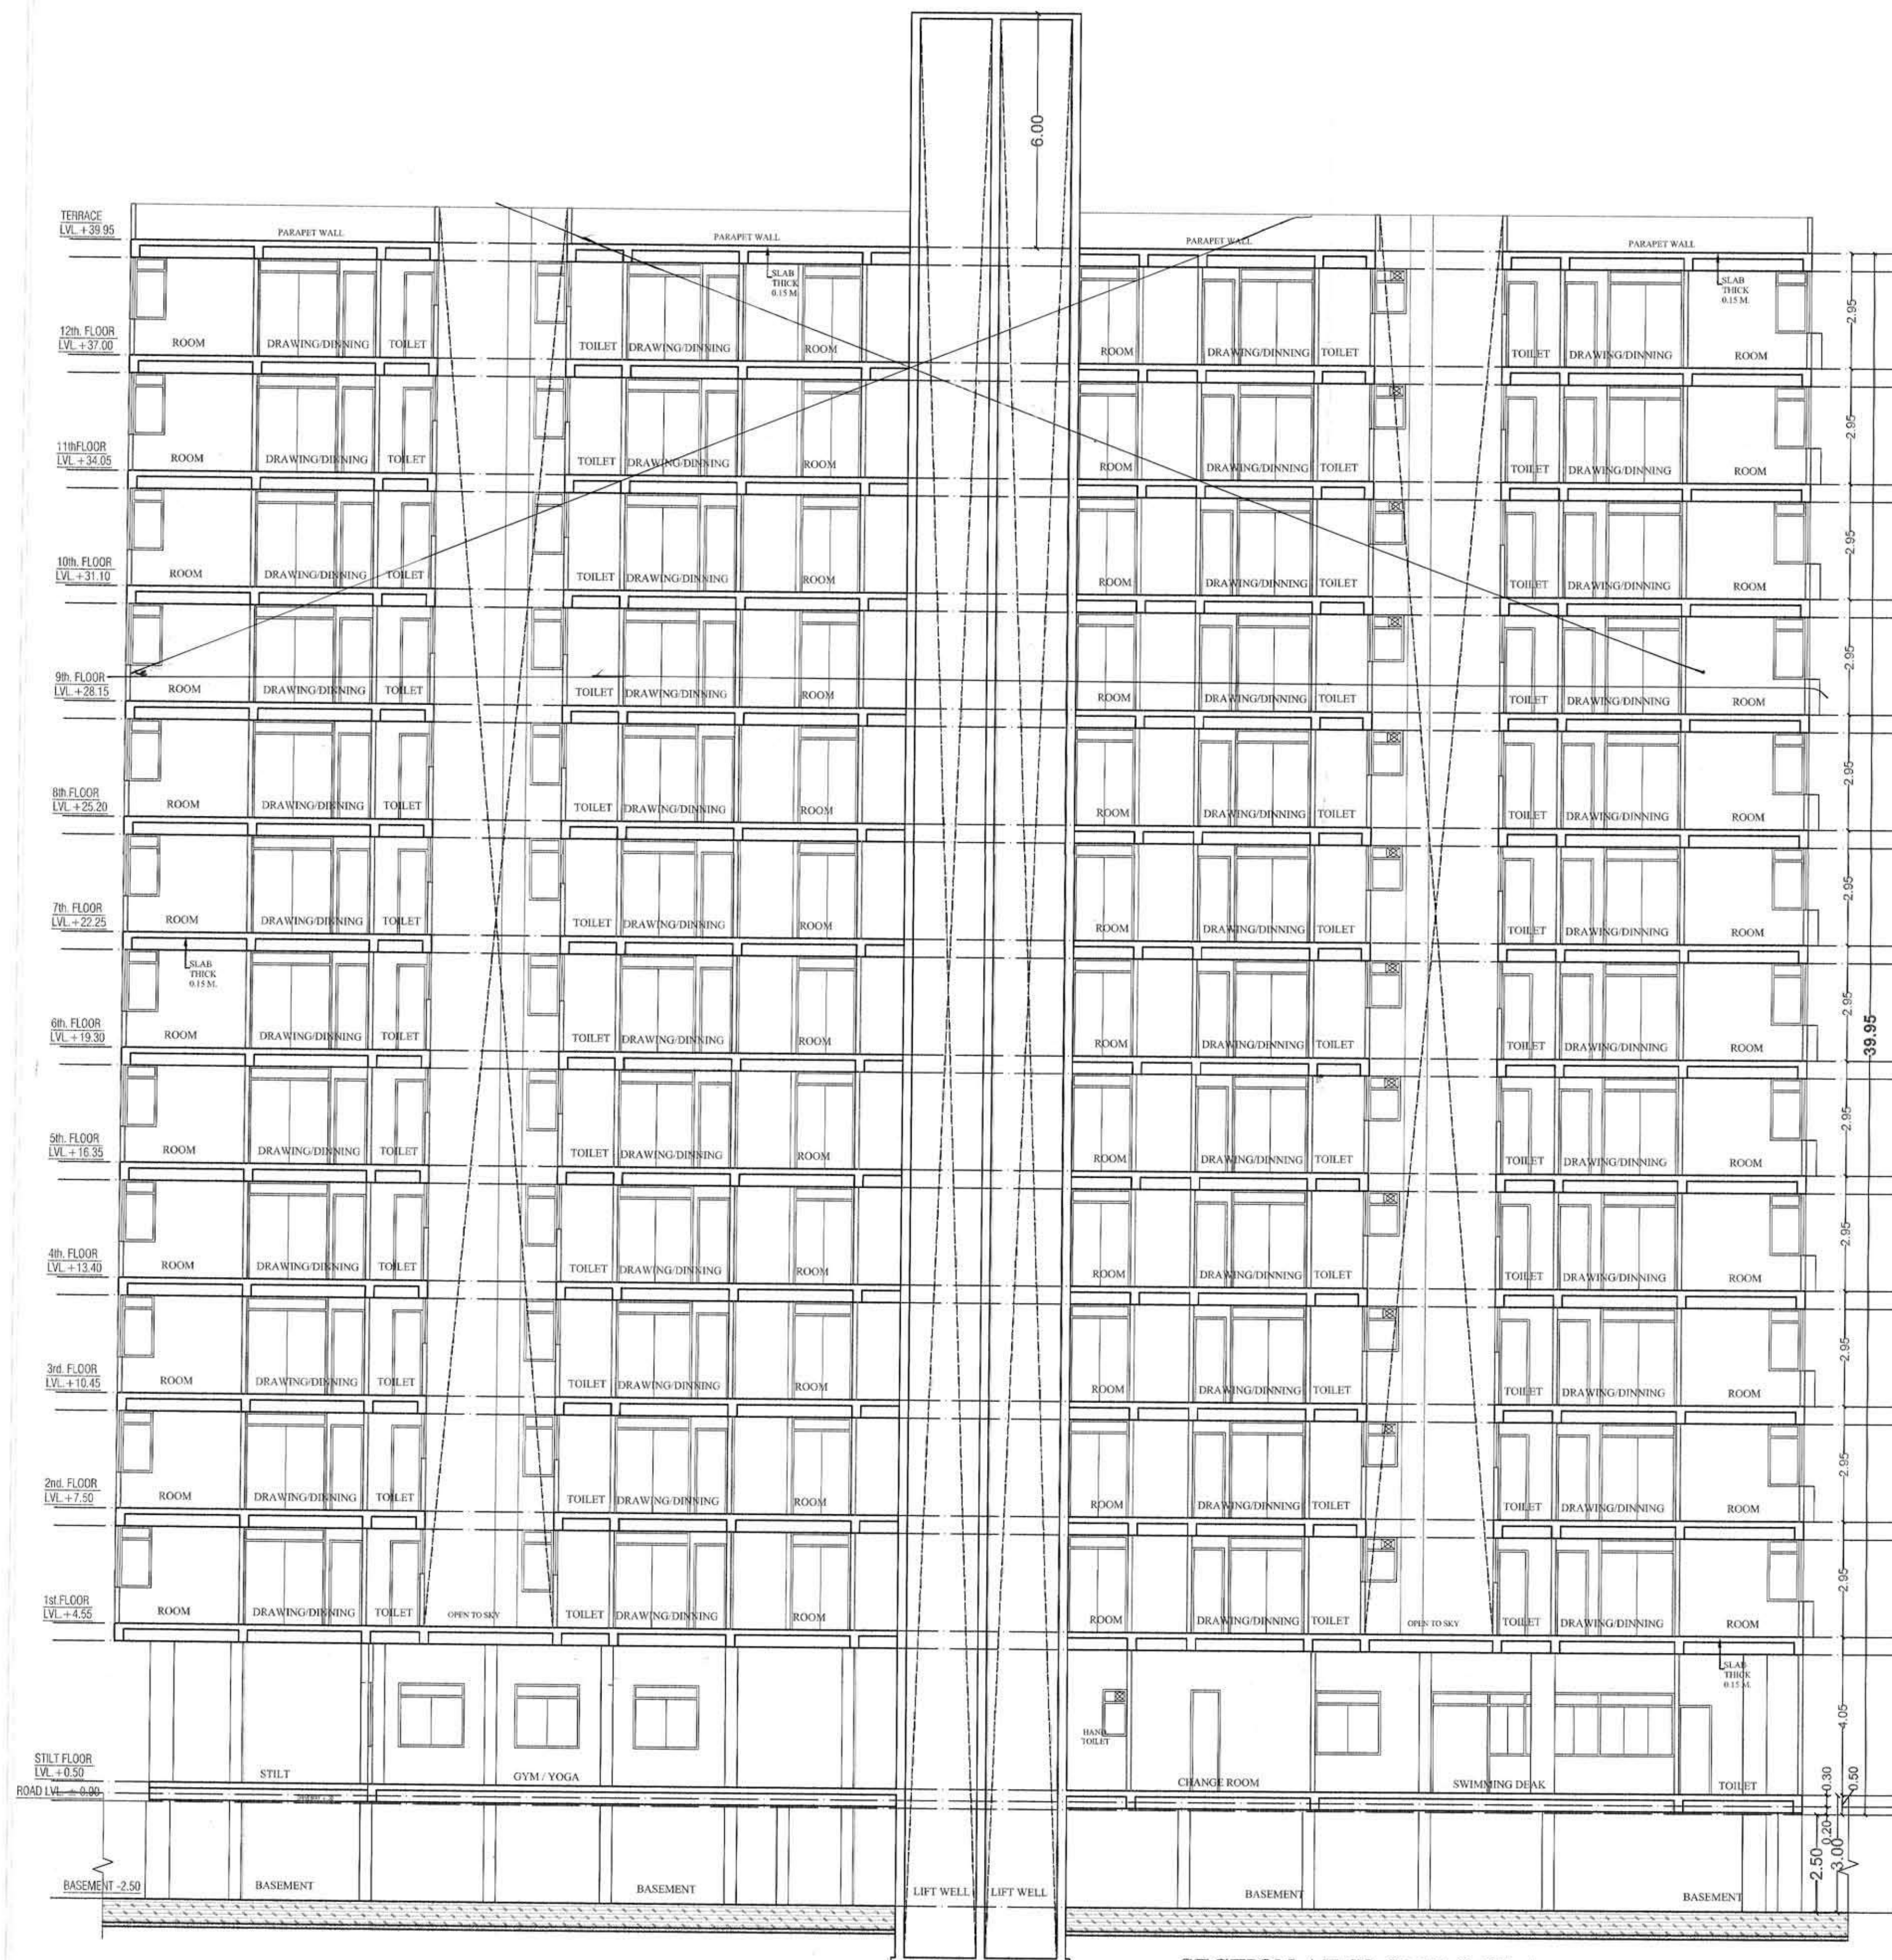

THIS DRG ENCLOSED
WITH LIT LETTER NO.
F-7/07P/462-R/DATED
23/10/17

भवन मानचित्र समिति की बैठक दिनांक
23/10/17 से निर्माण के क्रम में
मानचित्र अनुमोदित

मानचित्र में दर्शाये अनुसार रैगनाटर
हस्ताक्षर व्यवस्था का आवश्यक
निर्माण किया जाना होगा।

स्वीकृत मानचित्र के विरुद्ध किया गया
निर्माण कार्य अवरुद्ध माना जाएगा।

मानचित्र अनुमोदित

23/10/17

चरितेष्ट प्रारूपकार
नगर विकास ब्यास
कोटा

वर्तमान में आधी मंजिल तक वेस्टिंग + रिटल + आर्च तल (कुल
वेस्टिंग + रिटल + 28.15 मीटर ऊंचाई तक) तक की स्वीकृति
कार्यालय पर क्रमांक एक 7/डी.पी.2017 प्लान-81
दिनांक 23/10/17 में वर्णित शर्तों के अधीन जारी की जा रही है।
उप नगर नियोजक नगर विकास ब्यास, कोटा


चरितेष्ट नगर नियोजक
नगर विकास ब्यास, कोटा

PROJECT :-


PROPOSED GROUP HOUSING AT PLOT NO :- 01,
VILLAGE - RAMCHANDRAPURA, NEAR VILLAGE POLICE LINE,
KHASRA NO. 95, KOTA.

For OWNER
Raj Singh

SHRI KRISHNA
ARCHITECT
ARCHITECT CA/99/25-16
SCALE = 1:100
SPACE GRID
C-49 VIDYA APARTMENT PARAS MARG,
BAPU NAGAR NEAR JANTA STORE CIRCLE,
JAIPUR-302015
PH-09314918766, 0141-4005506 (O)
Email:-info.spacegrid@gmail.com

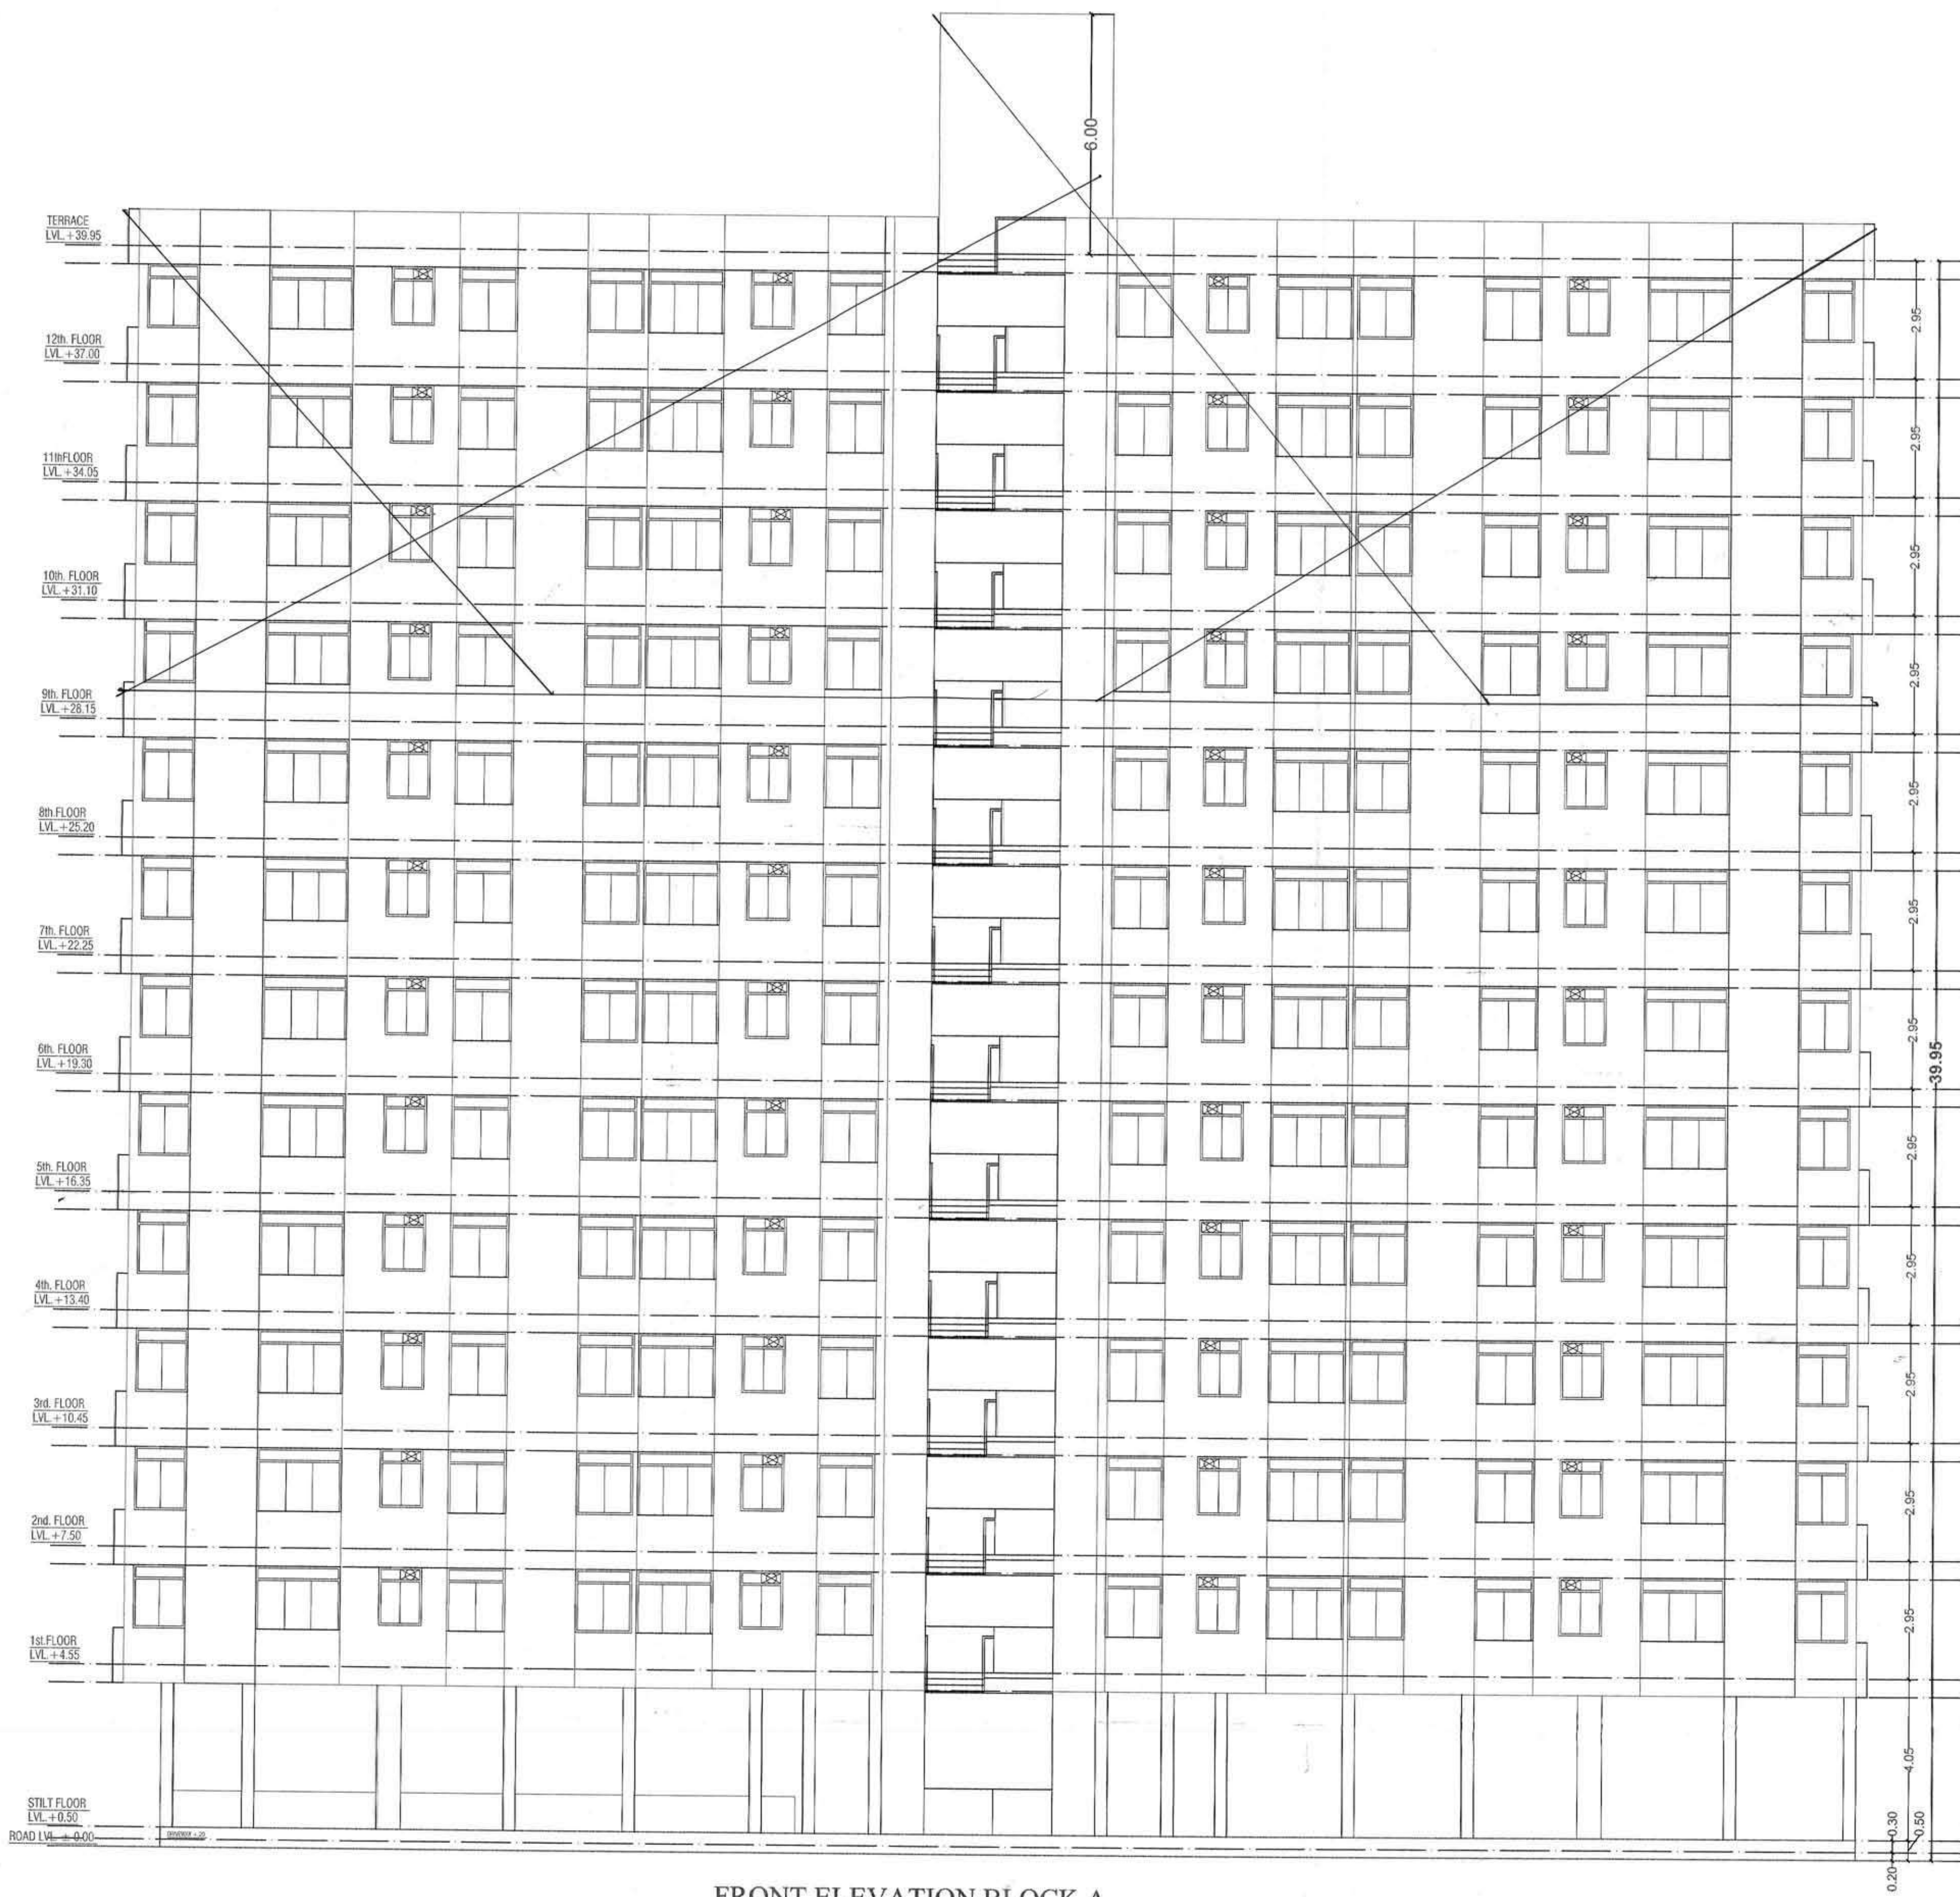

FRONT ELEVATION BLOCK A

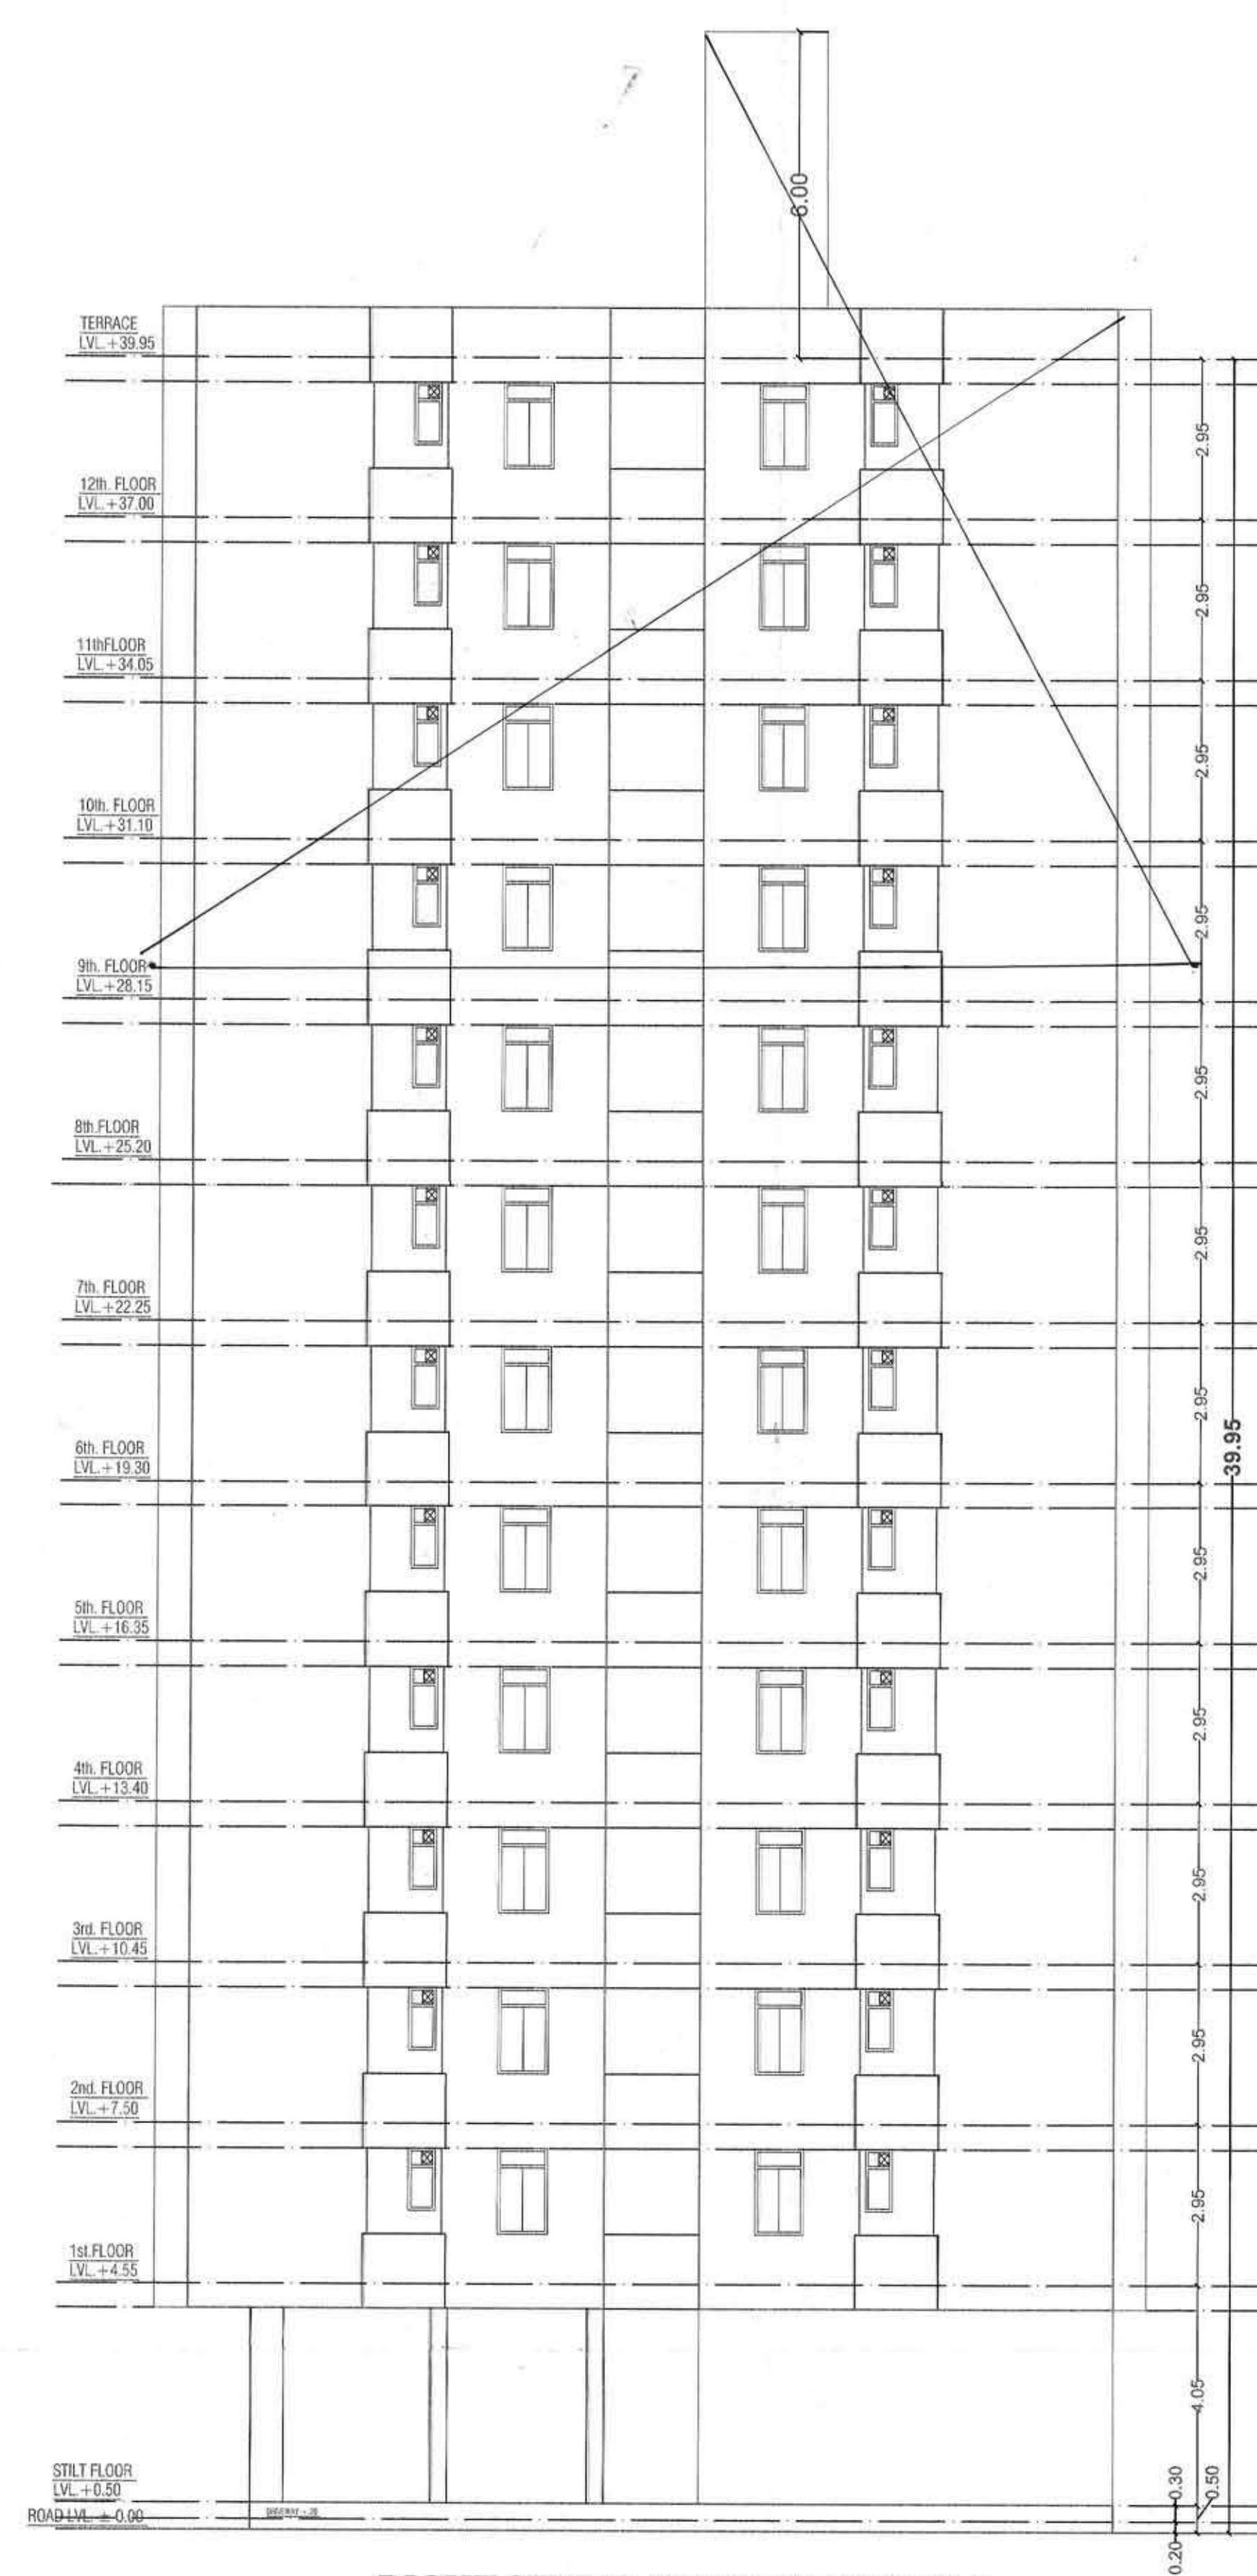

RIGHT SIDE ELEVATION BLOCK A



BACK ELEVATION BLOCK A

THIS DRG ENCLOSED
WITH U/I LETTER NO.
F-7/DTP/142-8 DATED
23/10/14

मानचित्र में दर्शाये अनुसार
होने पर आवश्यकता का आकलन
निर्माण किया जाना होगा।

मानचित्र अनुमोदित

नवियुग समिति की बैठक दिनांक
5/10/17 में निर्णय के क्रम में
अनुमोदित


स्वीकृत मानचित्र से विरुद्ध किया गया निर्माण कार्य अवैध माना जावेगा।

2432
18/10/17

वर्तमान में आठवीं मंजिल तक बेसमेन्ट + स्टिच + आठवें तल (कुल बेसमेन्ट + स्टिच + 28.15 मीटर ऊंचाई तक) तक की स्वीकृति कार्यालय पत्र क्रमांक एफ 7/डी.टी.पी./2017 (469-8) दिनांक 21.11.17 में वर्णित शर्तों के अधीन जारी की जा रही है।

Mysore

वरिष्ठ नगर नियोजन
नगर विकास

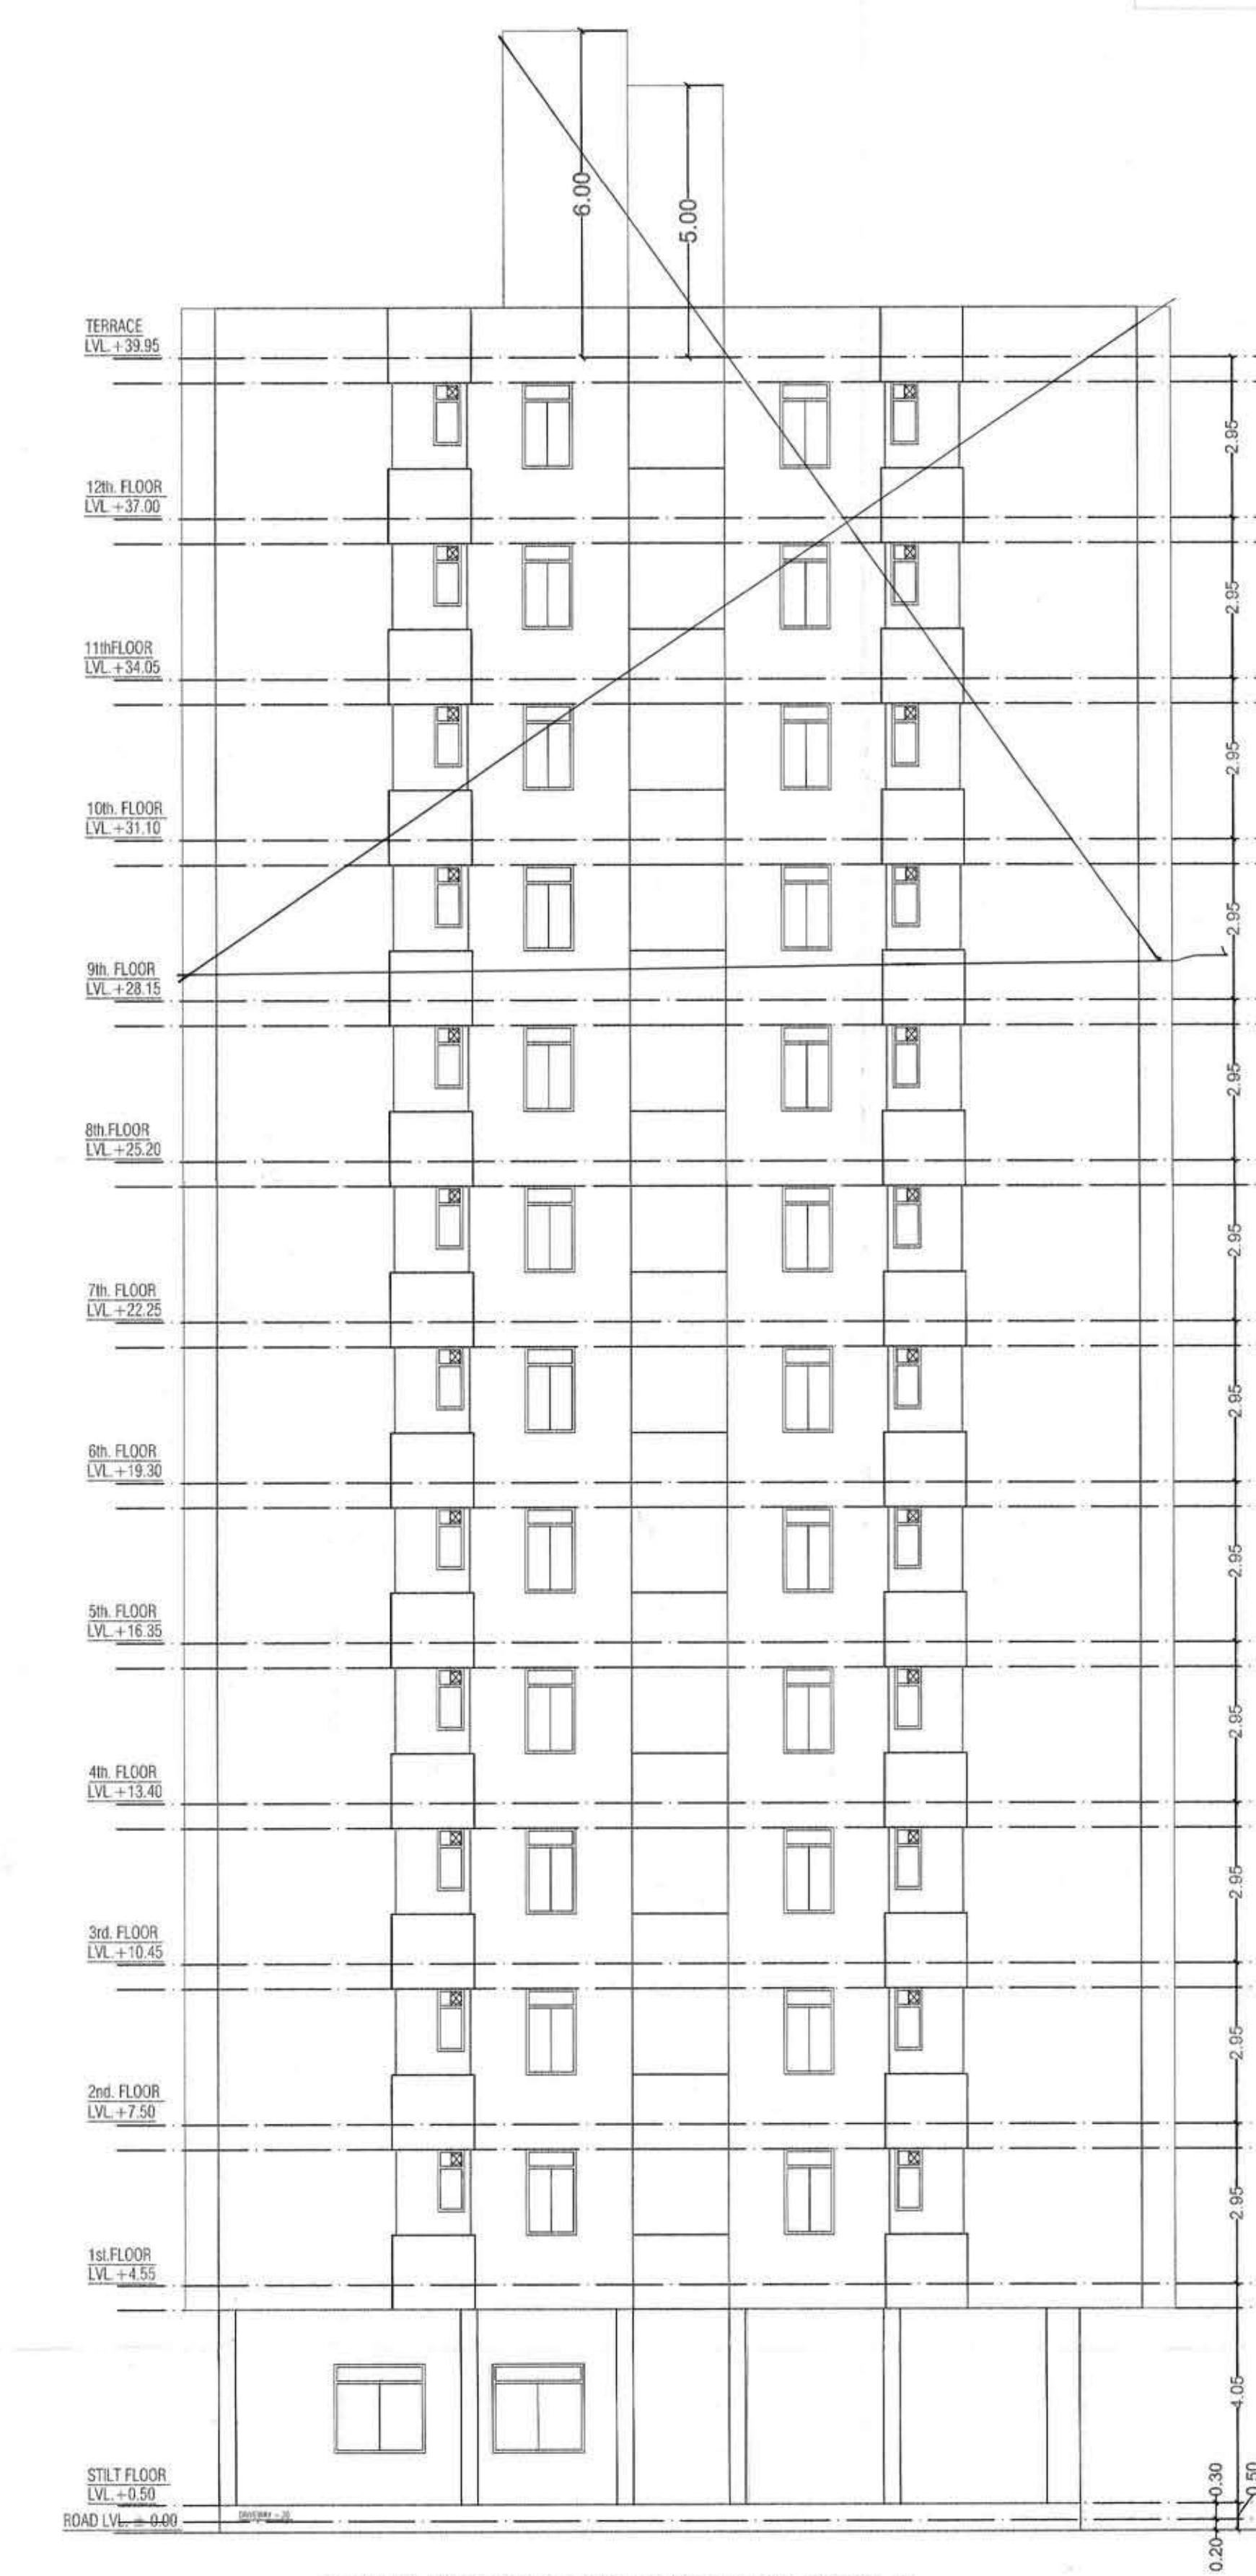

LEFT SIDE ELEVATION BLOCK A

PROJECT :-


PROPOSED GROUP HOUSING AT PLOT NO :- 01,
VILLAGE - RAMCHANDRAPURA , NEAR VILLAGE POLICE LINE
KHASRA NO . 95 , KOTA.

OWNER
For OM CONSTRUCTION
Raj Agarwal
Authorized Signatory


ARCHITECT:

 **SPACE GRID**
C-49, VIDYA APARTMENT, PARAS MARG,
BAPU NAGAR, NEAR JANTA STORE CIRCLE,
JAIPUR-302015
PH-09314918766, 0141-4005506 (O)
Email:-info.spacegrid@gmail.com

SHRI KRISHNAN
ARCHITECT
CA/99/25431

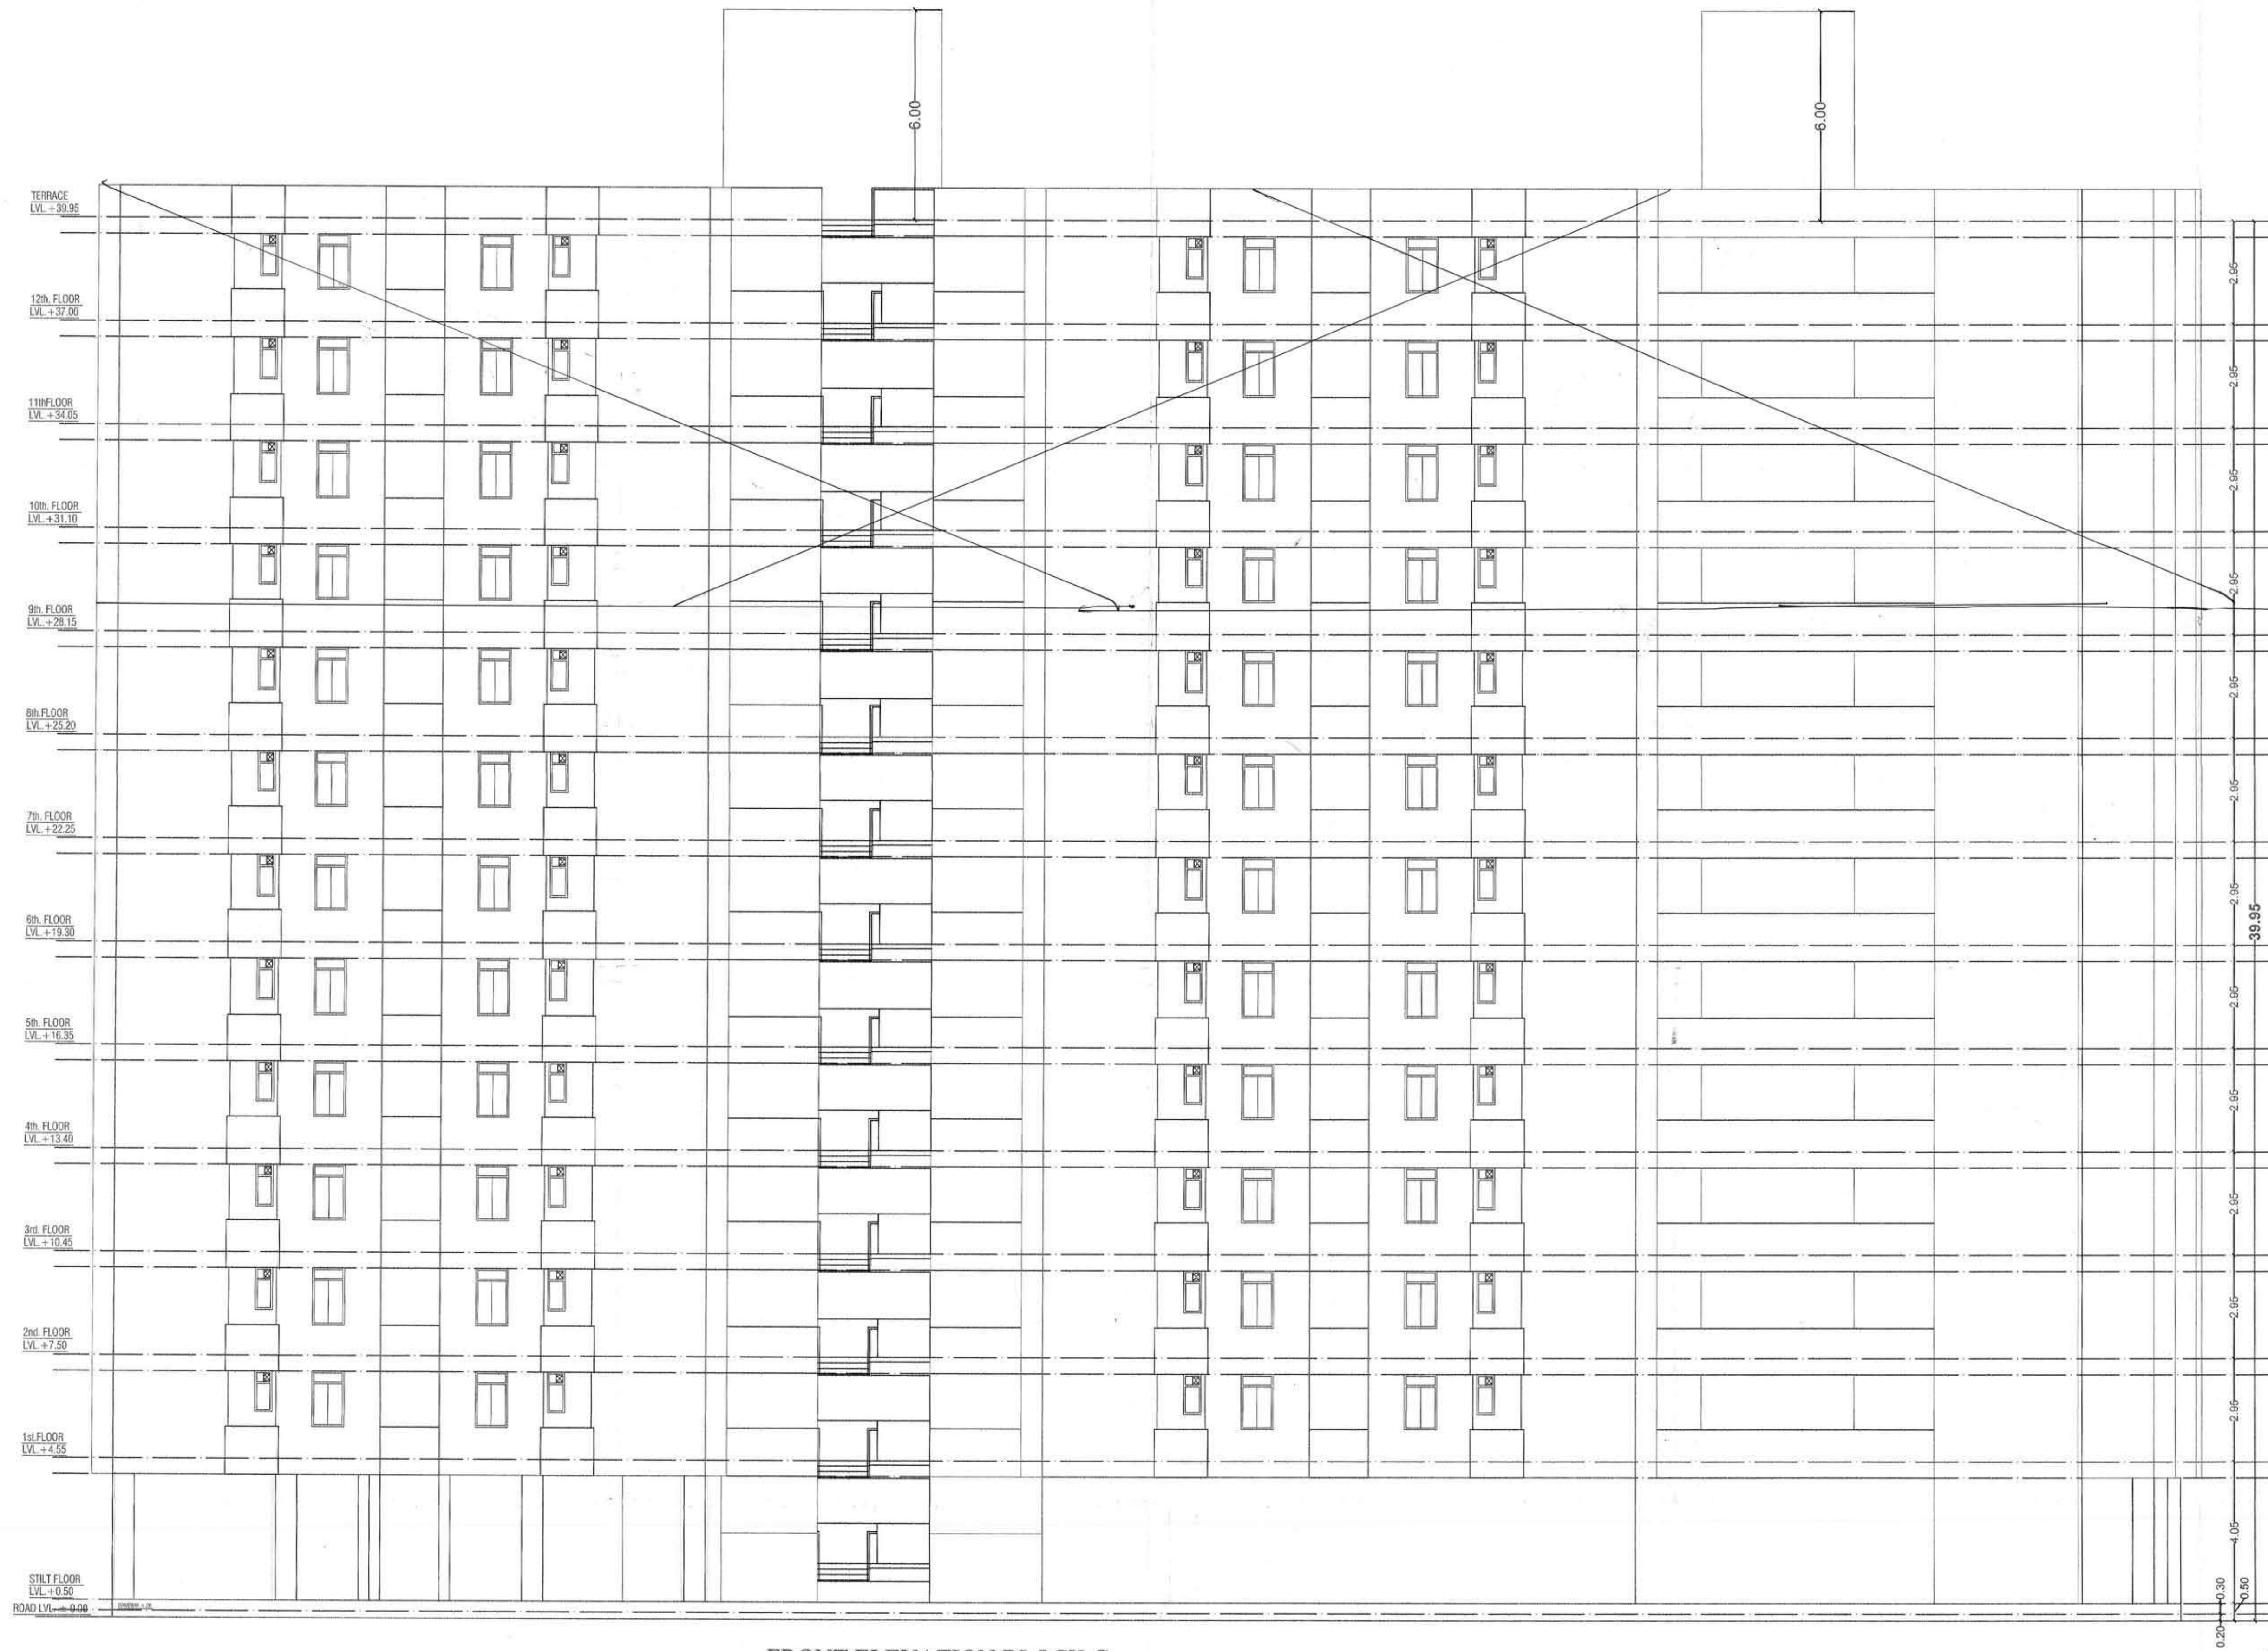

FRONT ELEVATION BLOCK C

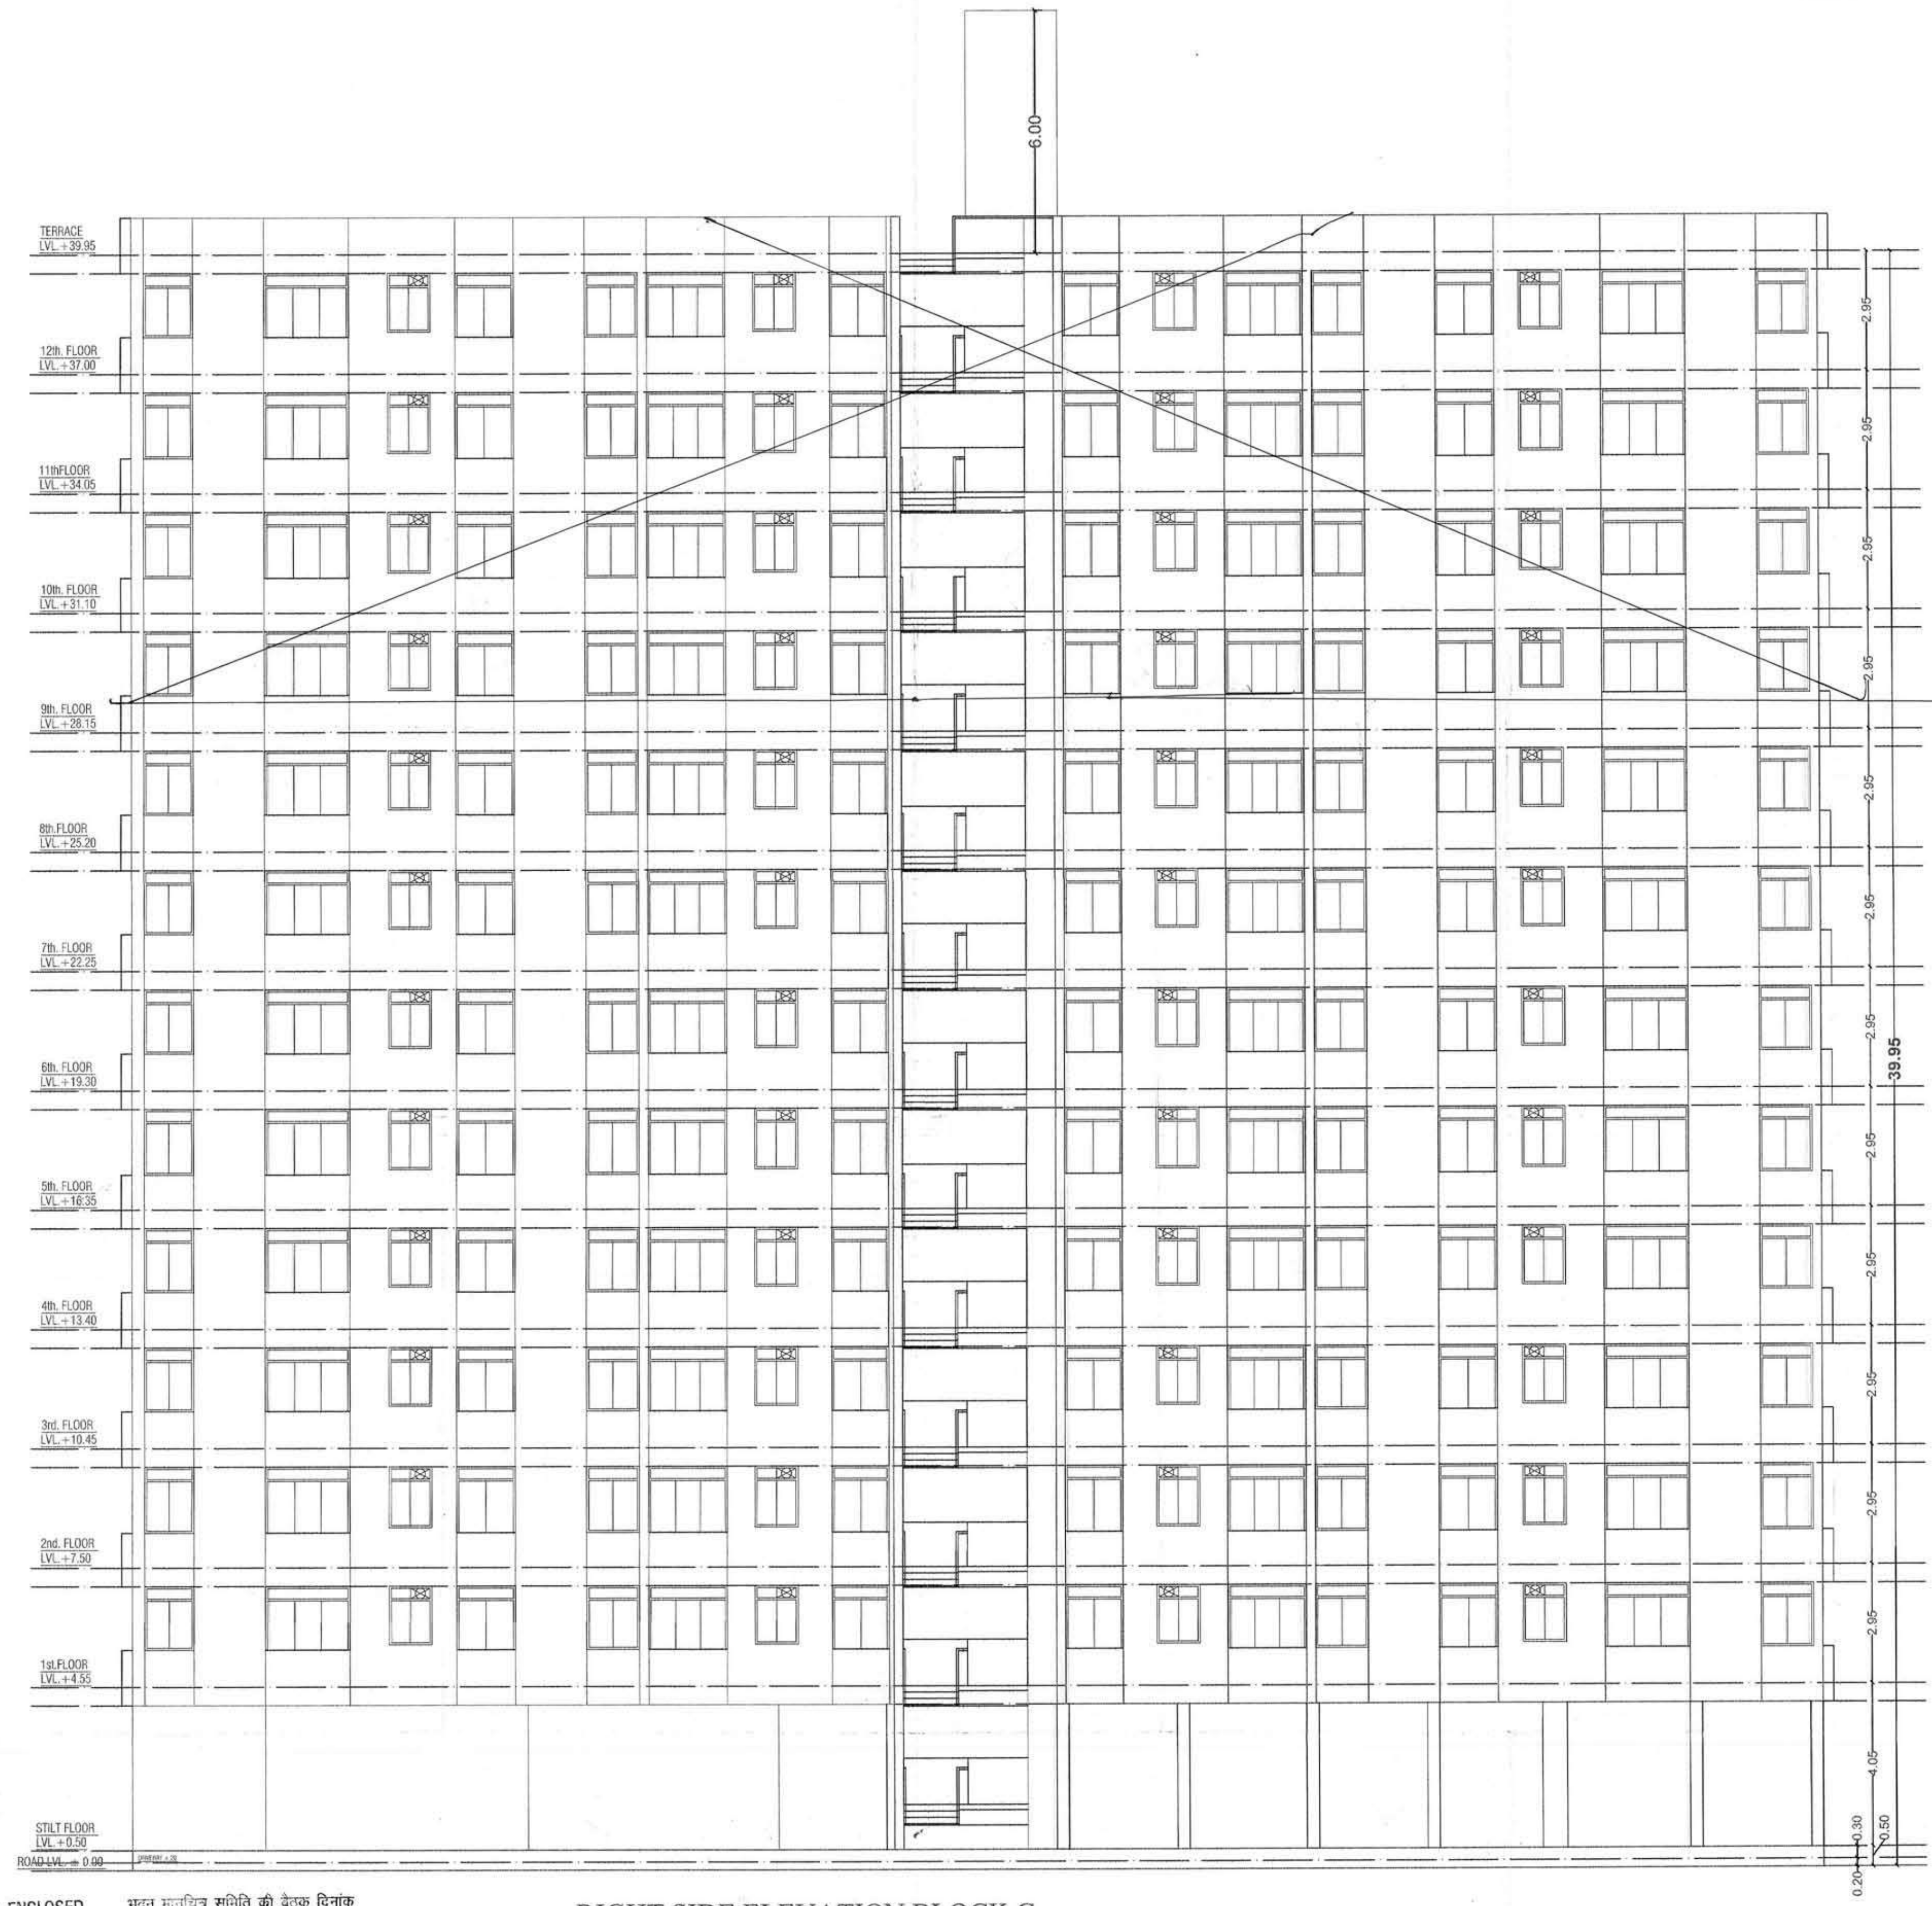

RIGHT SIDE ELEVATION BLOCK C

THIS DRAWING IS ENCLOSED WITH LETTER NO. 6/7/01/2/4/2 DATED 23/10/17

मानचित्र में दर्शाये अनुसार रैमवाटर हाउसिंग प्रकल्प का अवलोकन निम्नानुसार किया गया।

मानचित्र अनुमोदित

मानचित्र में दर्शाये अनुसार रैमवाटर हाउसिंग प्रकल्प का अवलोकन निम्नानुसार किया गया।

वसिष्ठ प्रकल्पकार
वसिष्ठ विकास न्यास
कोटा


वर्तमान में आवडी नजिल तक बेसमेन्ट + रिजल्ट + आवडी तल (कुल बेसमेन्ट + रिजल्ट + 28.15 मीटर ऊँचाई तक) तक की स्वीकृति कार्यालय पर क्रमांक एक 7/डी.पी./2017 दिनांक 23/10/17 में वर्णित शर्तों के अधीन जारी की जा रही है।
उपर नगर नियोजक
नगर विकास न्यास, कोटा

PROJECT :-

PROPOSED GROUP HOUSING AT PLOT NO :- 01,
VILLAGE - RAMCHANDRAPURA, NEAR VILLAGE POLICE LINE,
KHASRA NO. 95, KOTA.

For OWNER
Raj Agarwal

SHRI KRISHNA ARCHITECT
CA/99/25437
SCALE = 1:100
ARCHITECT :-
SPACE GRID
C-49 VIDYA APARTMENT, PARAS MARG,
BAPU NAGAR NEAR JANTA STORE CIRCLE,
JAIPUR-302015
PH-09314918766, 0141-4005506 (0)
Email-info.spacegrid@gmail.com

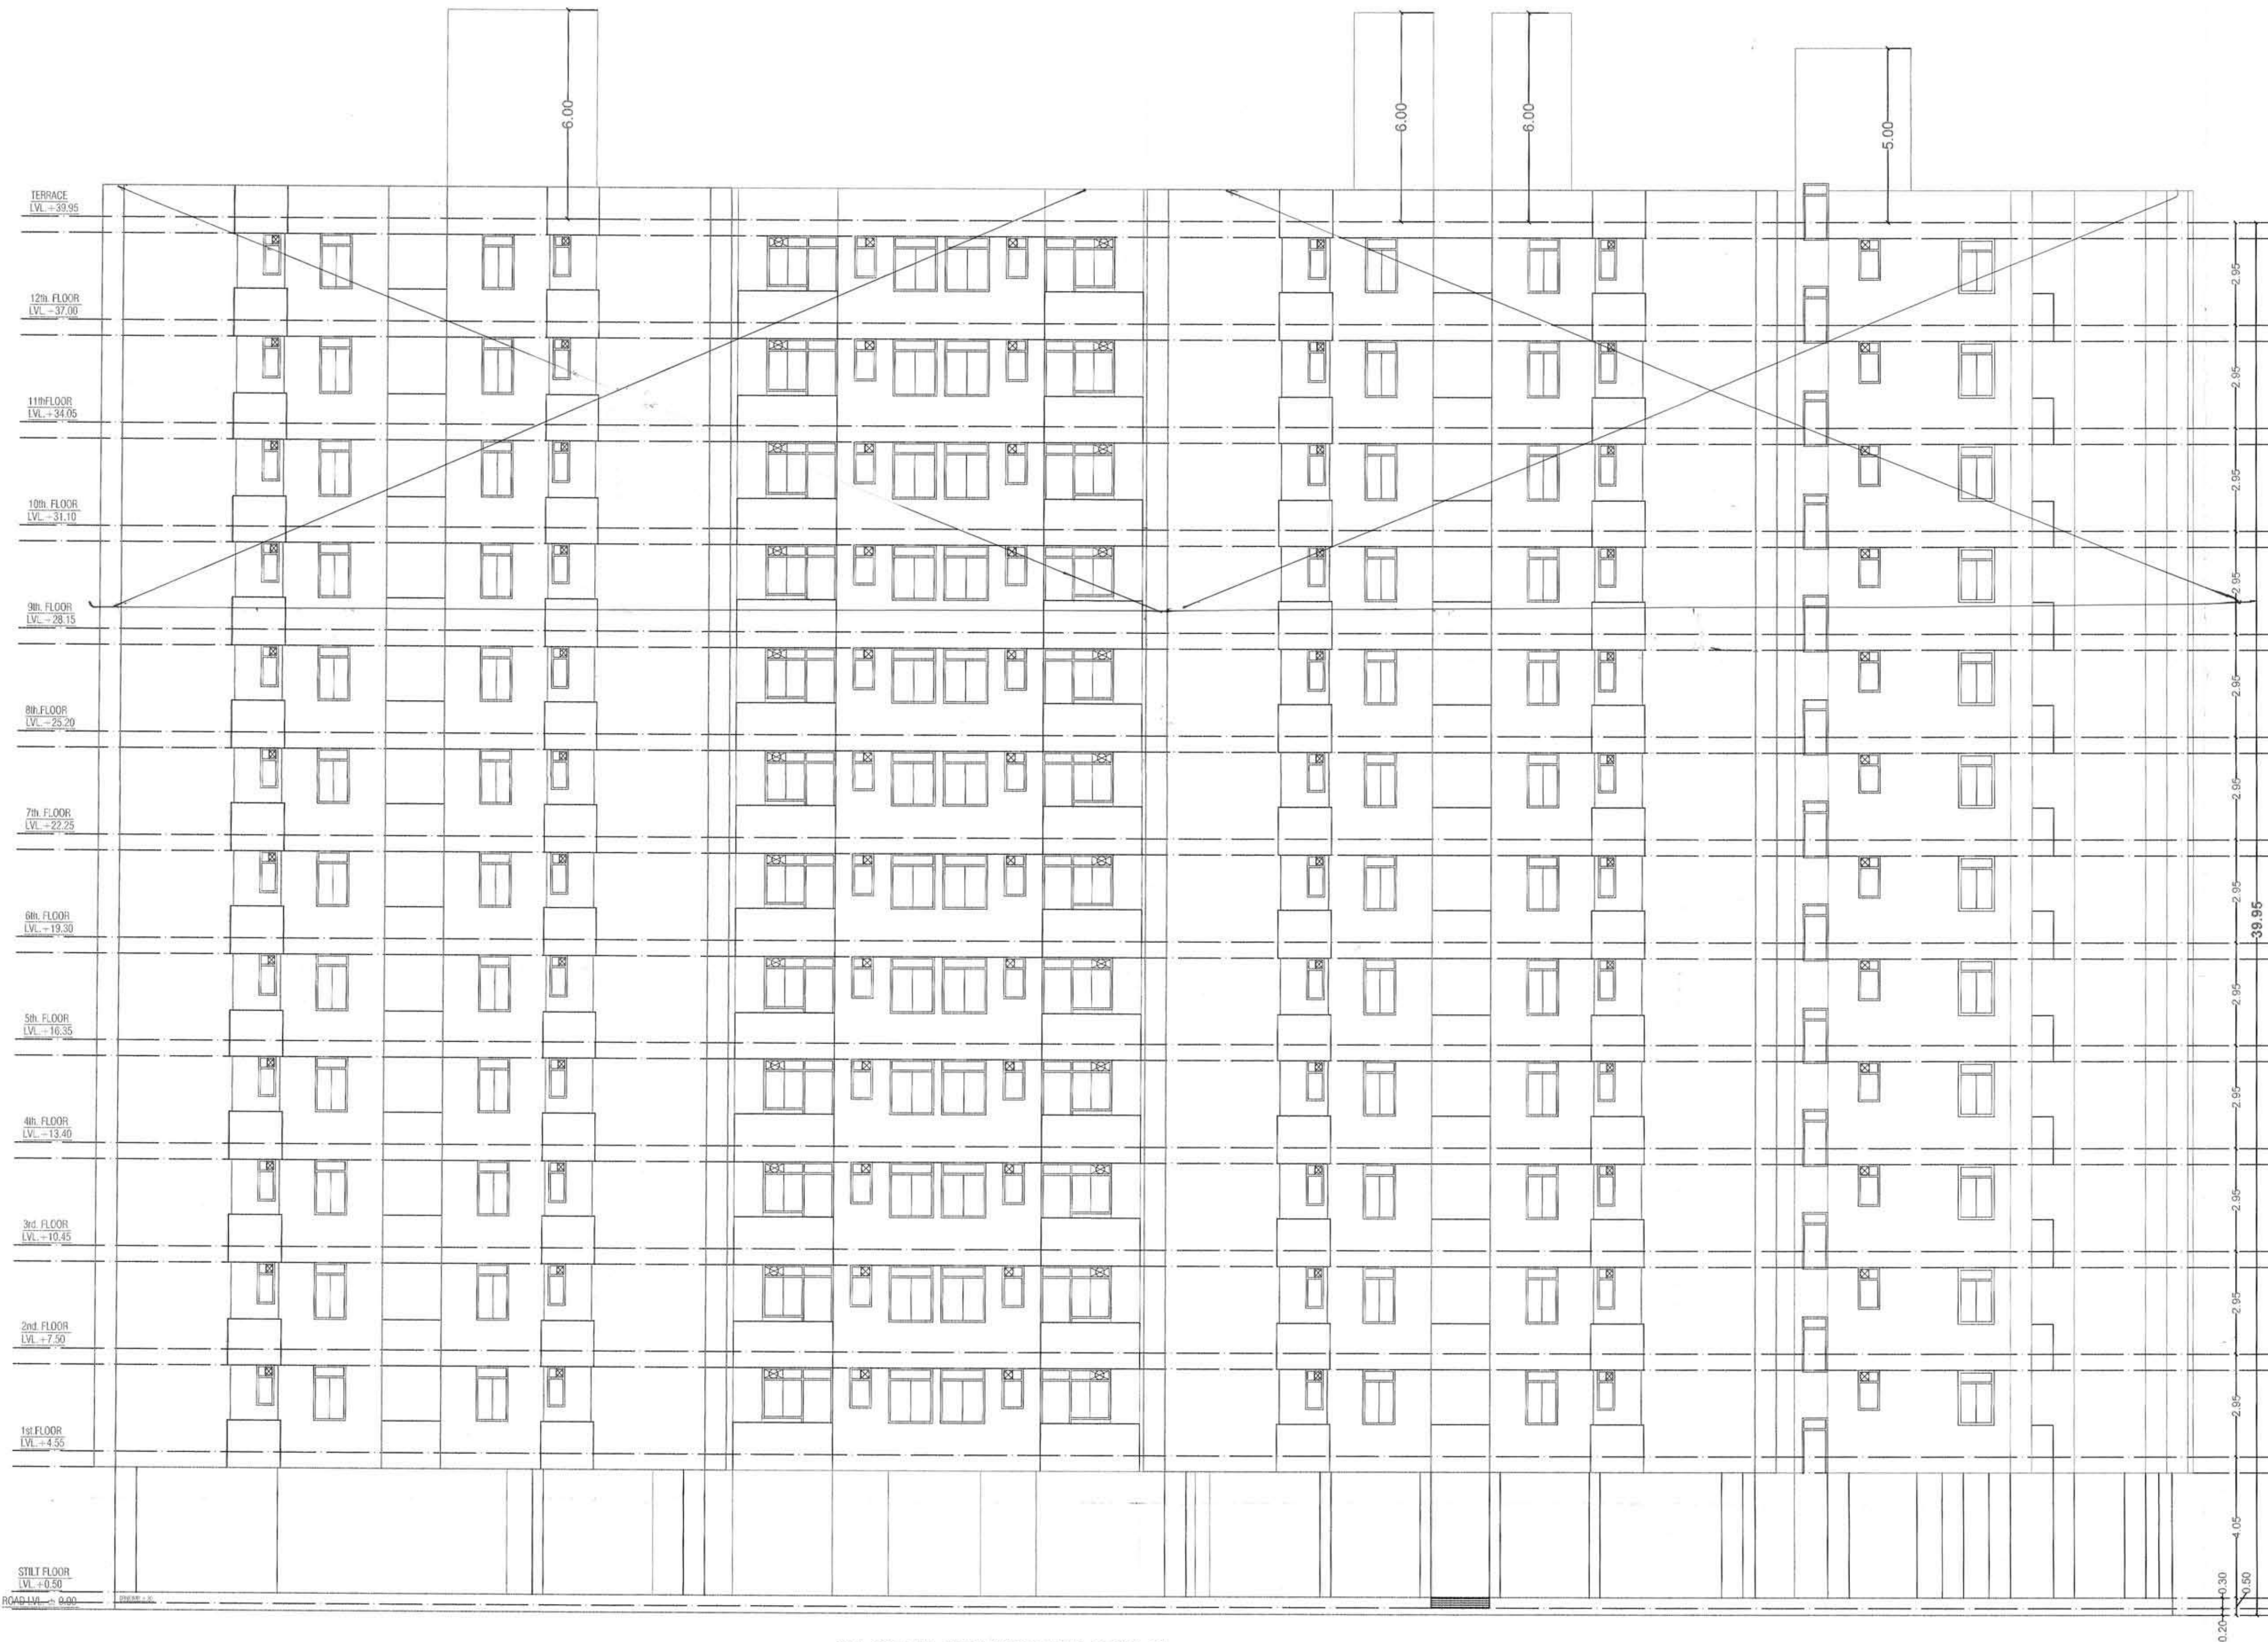

BACK ELEVATION BLOCK C


वर्तमान में आधी मंजिल तक वेस्टिंग + रिट्ट + आठों तल (कुल वेस्टिंग + रिट्ट + 28.15 मीटर ऊंचाई तक) तक की स्वीकृति कार्यालय पत्र क्रमांक एक 7/डी.टी.पी./2017 2/16/2-8.1. दिनांक 21.01.2017 में वर्णित शर्तों के अधीन जारी की जा रही है।
 21/01/17
 राजेश कुमार मिश्रा, कोटा
 वरिष्ठ प्रमुख कार्यकारी
 नगर विकास न्याय, कोटा

THIS DRG ENCLOSED WITH JUT LETTER NO. 7/DT/462-2 DATED 21/01/17
 मानचित्र अनुमोदित
 मानचित्र अनुमोदित

मानचित्र में वर्णित अनुसार वेस्टिंग + रिट्ट + आठों तल (कुल वेस्टिंग + रिट्ट + 28.15 मीटर ऊंचाई तक) तक की स्वीकृति कार्यालय पत्र क्रमांक एक 7/डी.टी.पी./2017 2/16/2-8.1. दिनांक 21.01.2017 में वर्णित शर्तों के अधीन जारी की जा रही है।
 मानचित्र अनुमोदित

मानचित्र अनुमोदित

21/01/17
 राजेश कुमार मिश्रा, कोटा
 वरिष्ठ प्रमुख कार्यकारी
 नगर विकास न्याय, कोटा

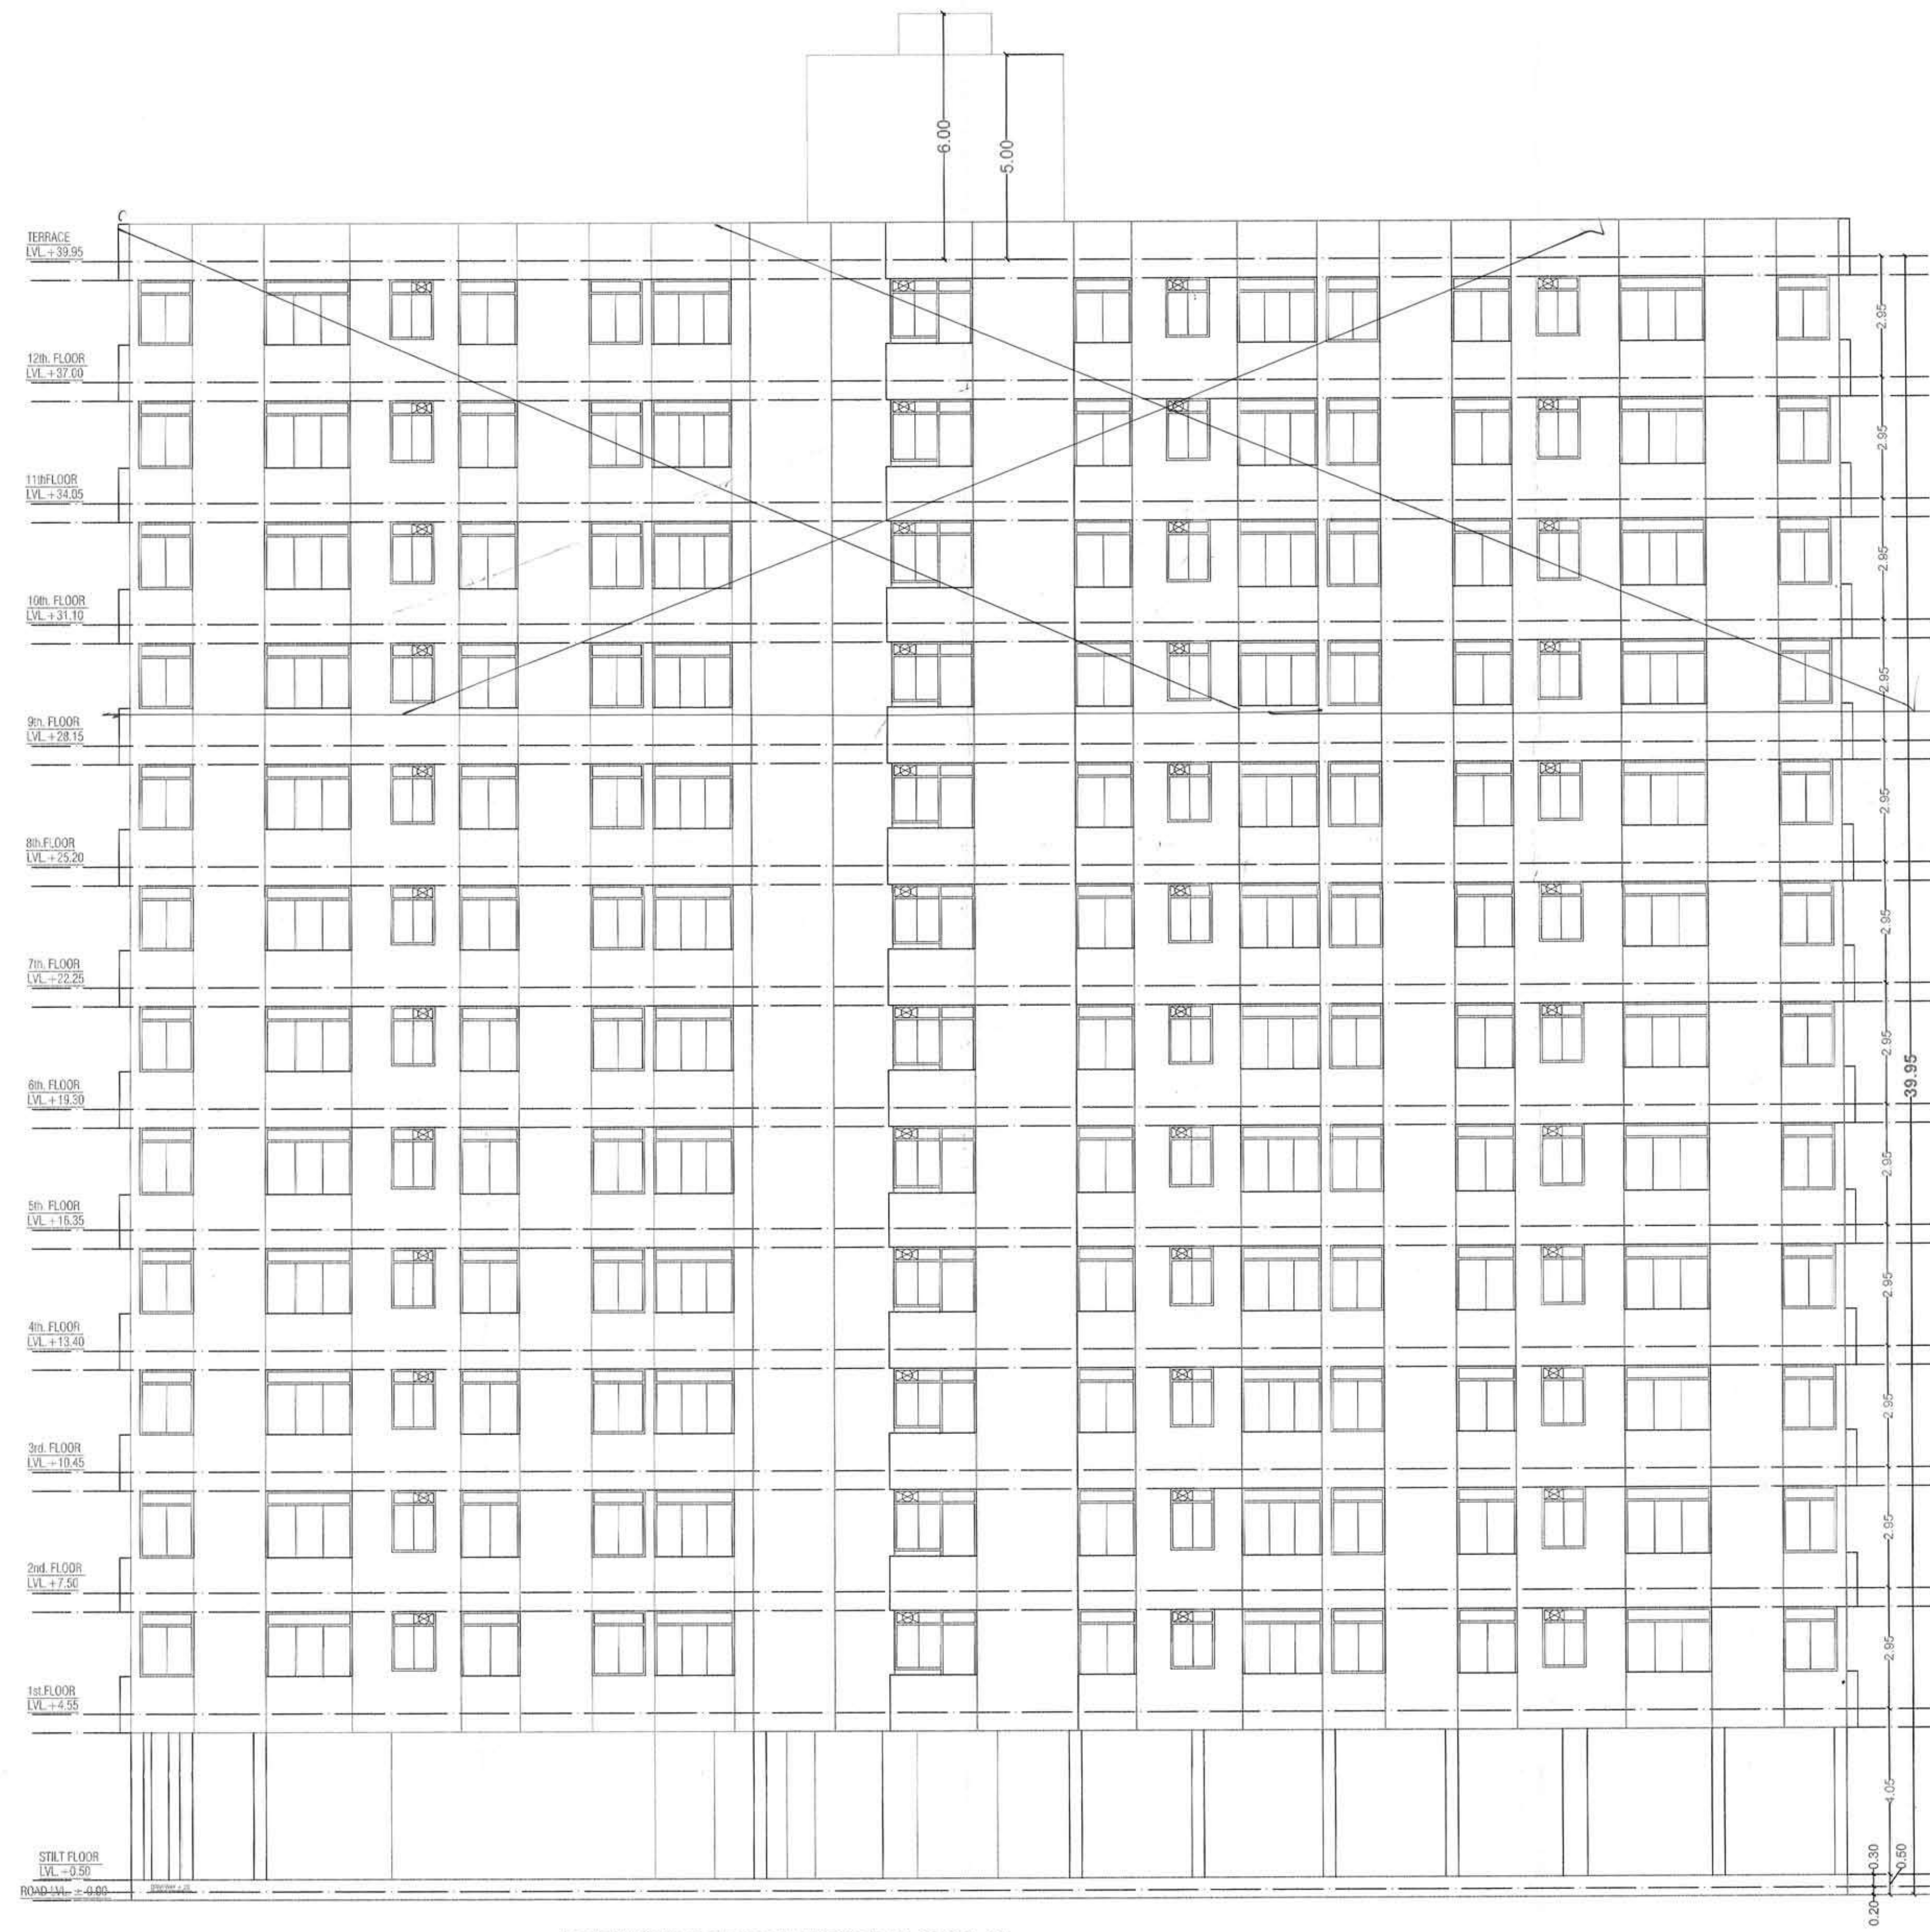

LEFT SIDE ELEVATION BLOCK C

PROJECT :-


PROPOSED GROUP HOUSING AT PLOT NO :- 01,
 VILLAGE - RAMCHANDRAPURA, NEAR VILLAGE POLICE LINE,
 KHASRA NO. 95, KOTA.

OWNER
 FORM CONSTRUCTION
 Rajesh Kumar Mishra


ARCHITECT :-

SPACE GRID
 C-49, VIDYA APARTMENT, PARAS MARG,
 BAPU NAGAR, NEAR JANTA STORE CIRCLE,
 JAIPUR-302015
 PH-09314918766, 0141-4005506 (0)
 Email-info.spacegrid@gmail.com


SHRI KRISHAN
 ARCHITECTS
 CA/99/25/SCALE = 1:100

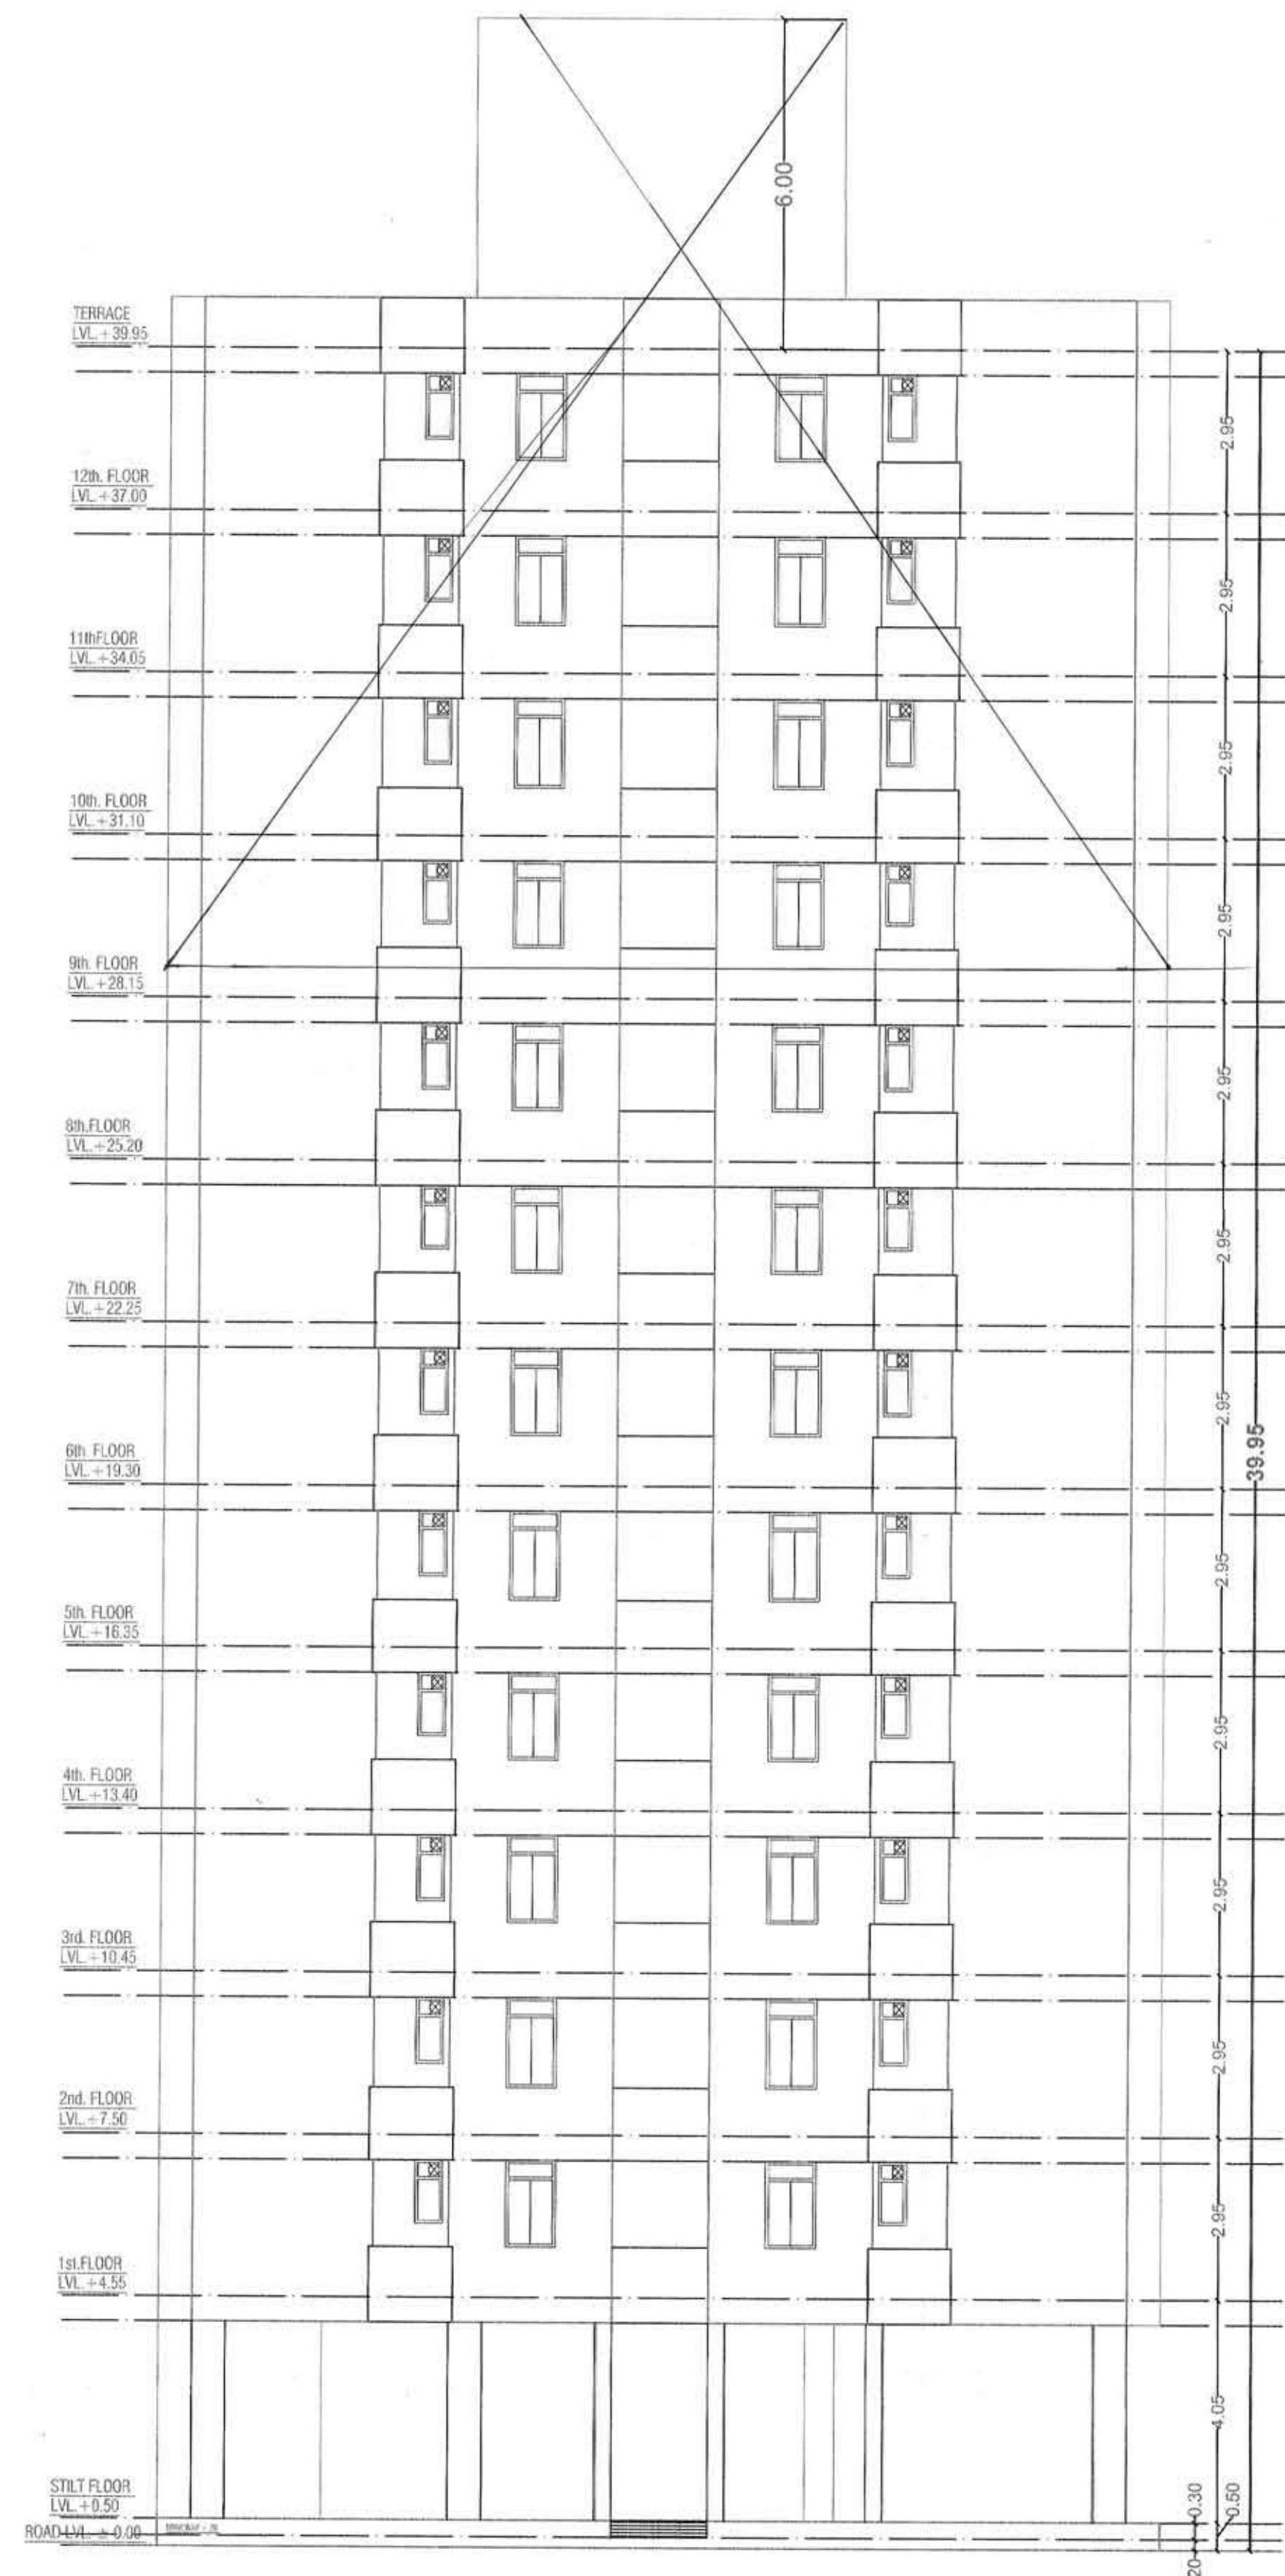

FRONT ELEVATION BLOCK D

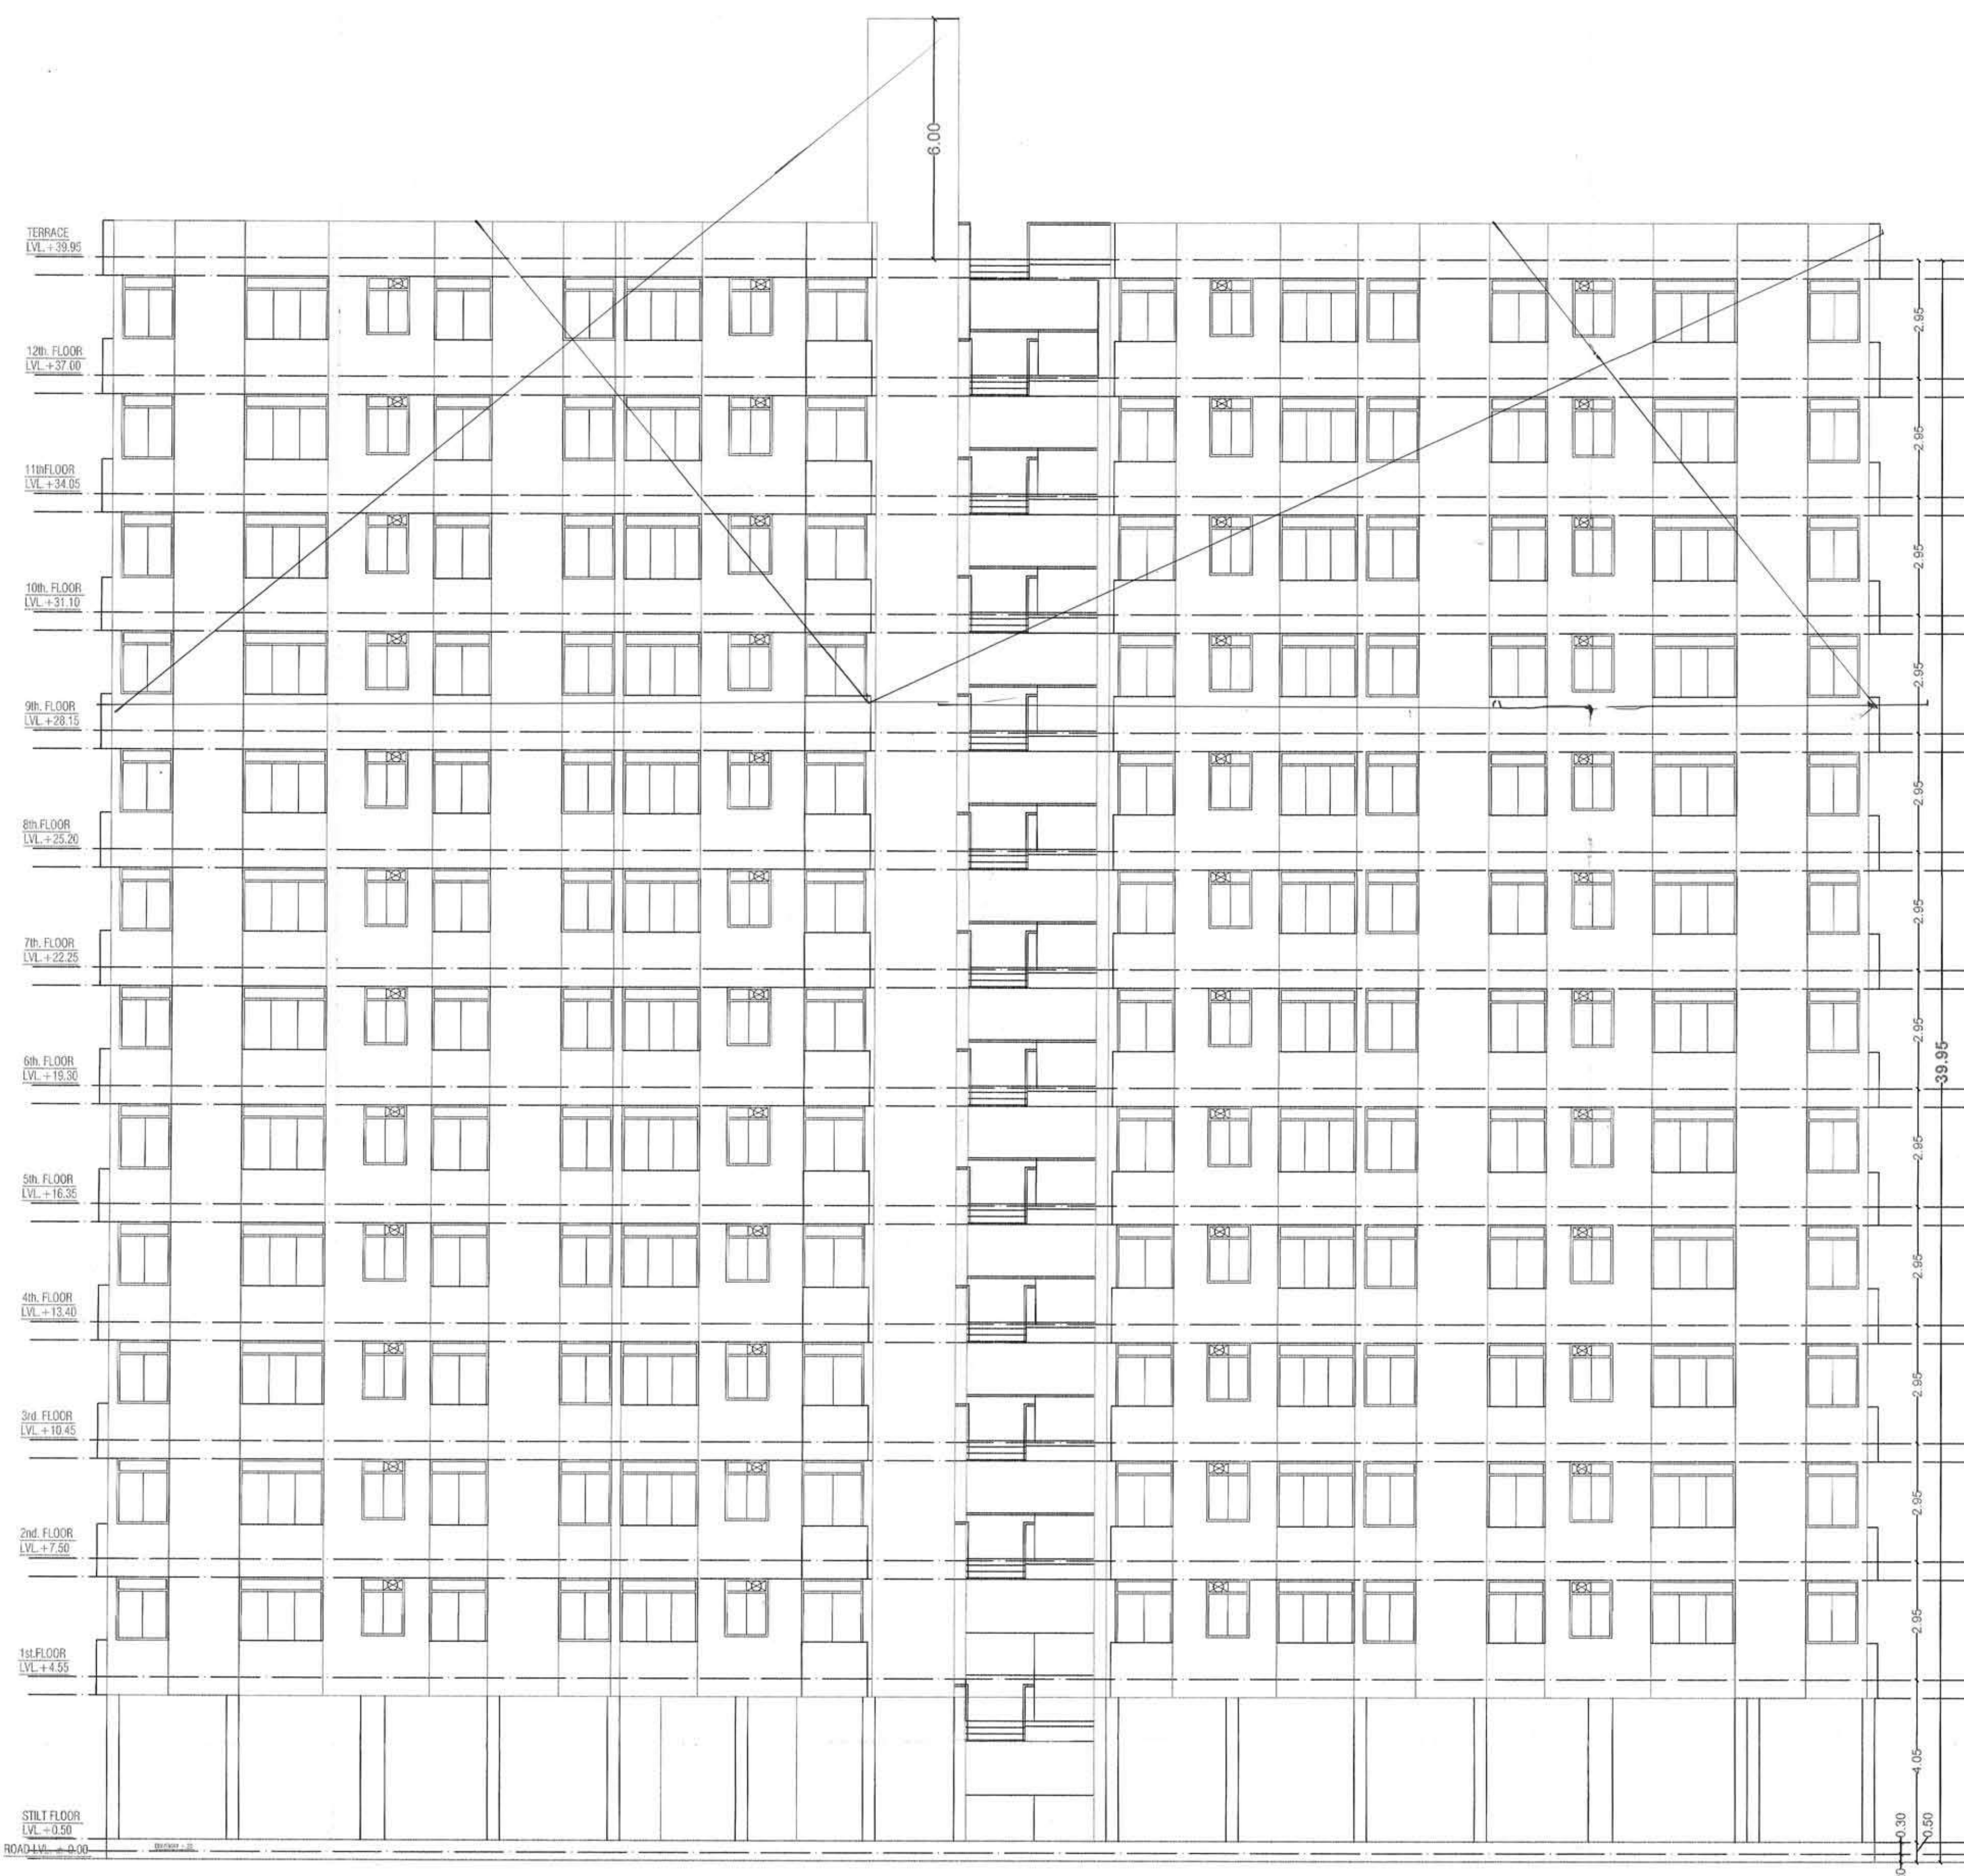

RIGHT SIDE ELEVATION BLOCK D

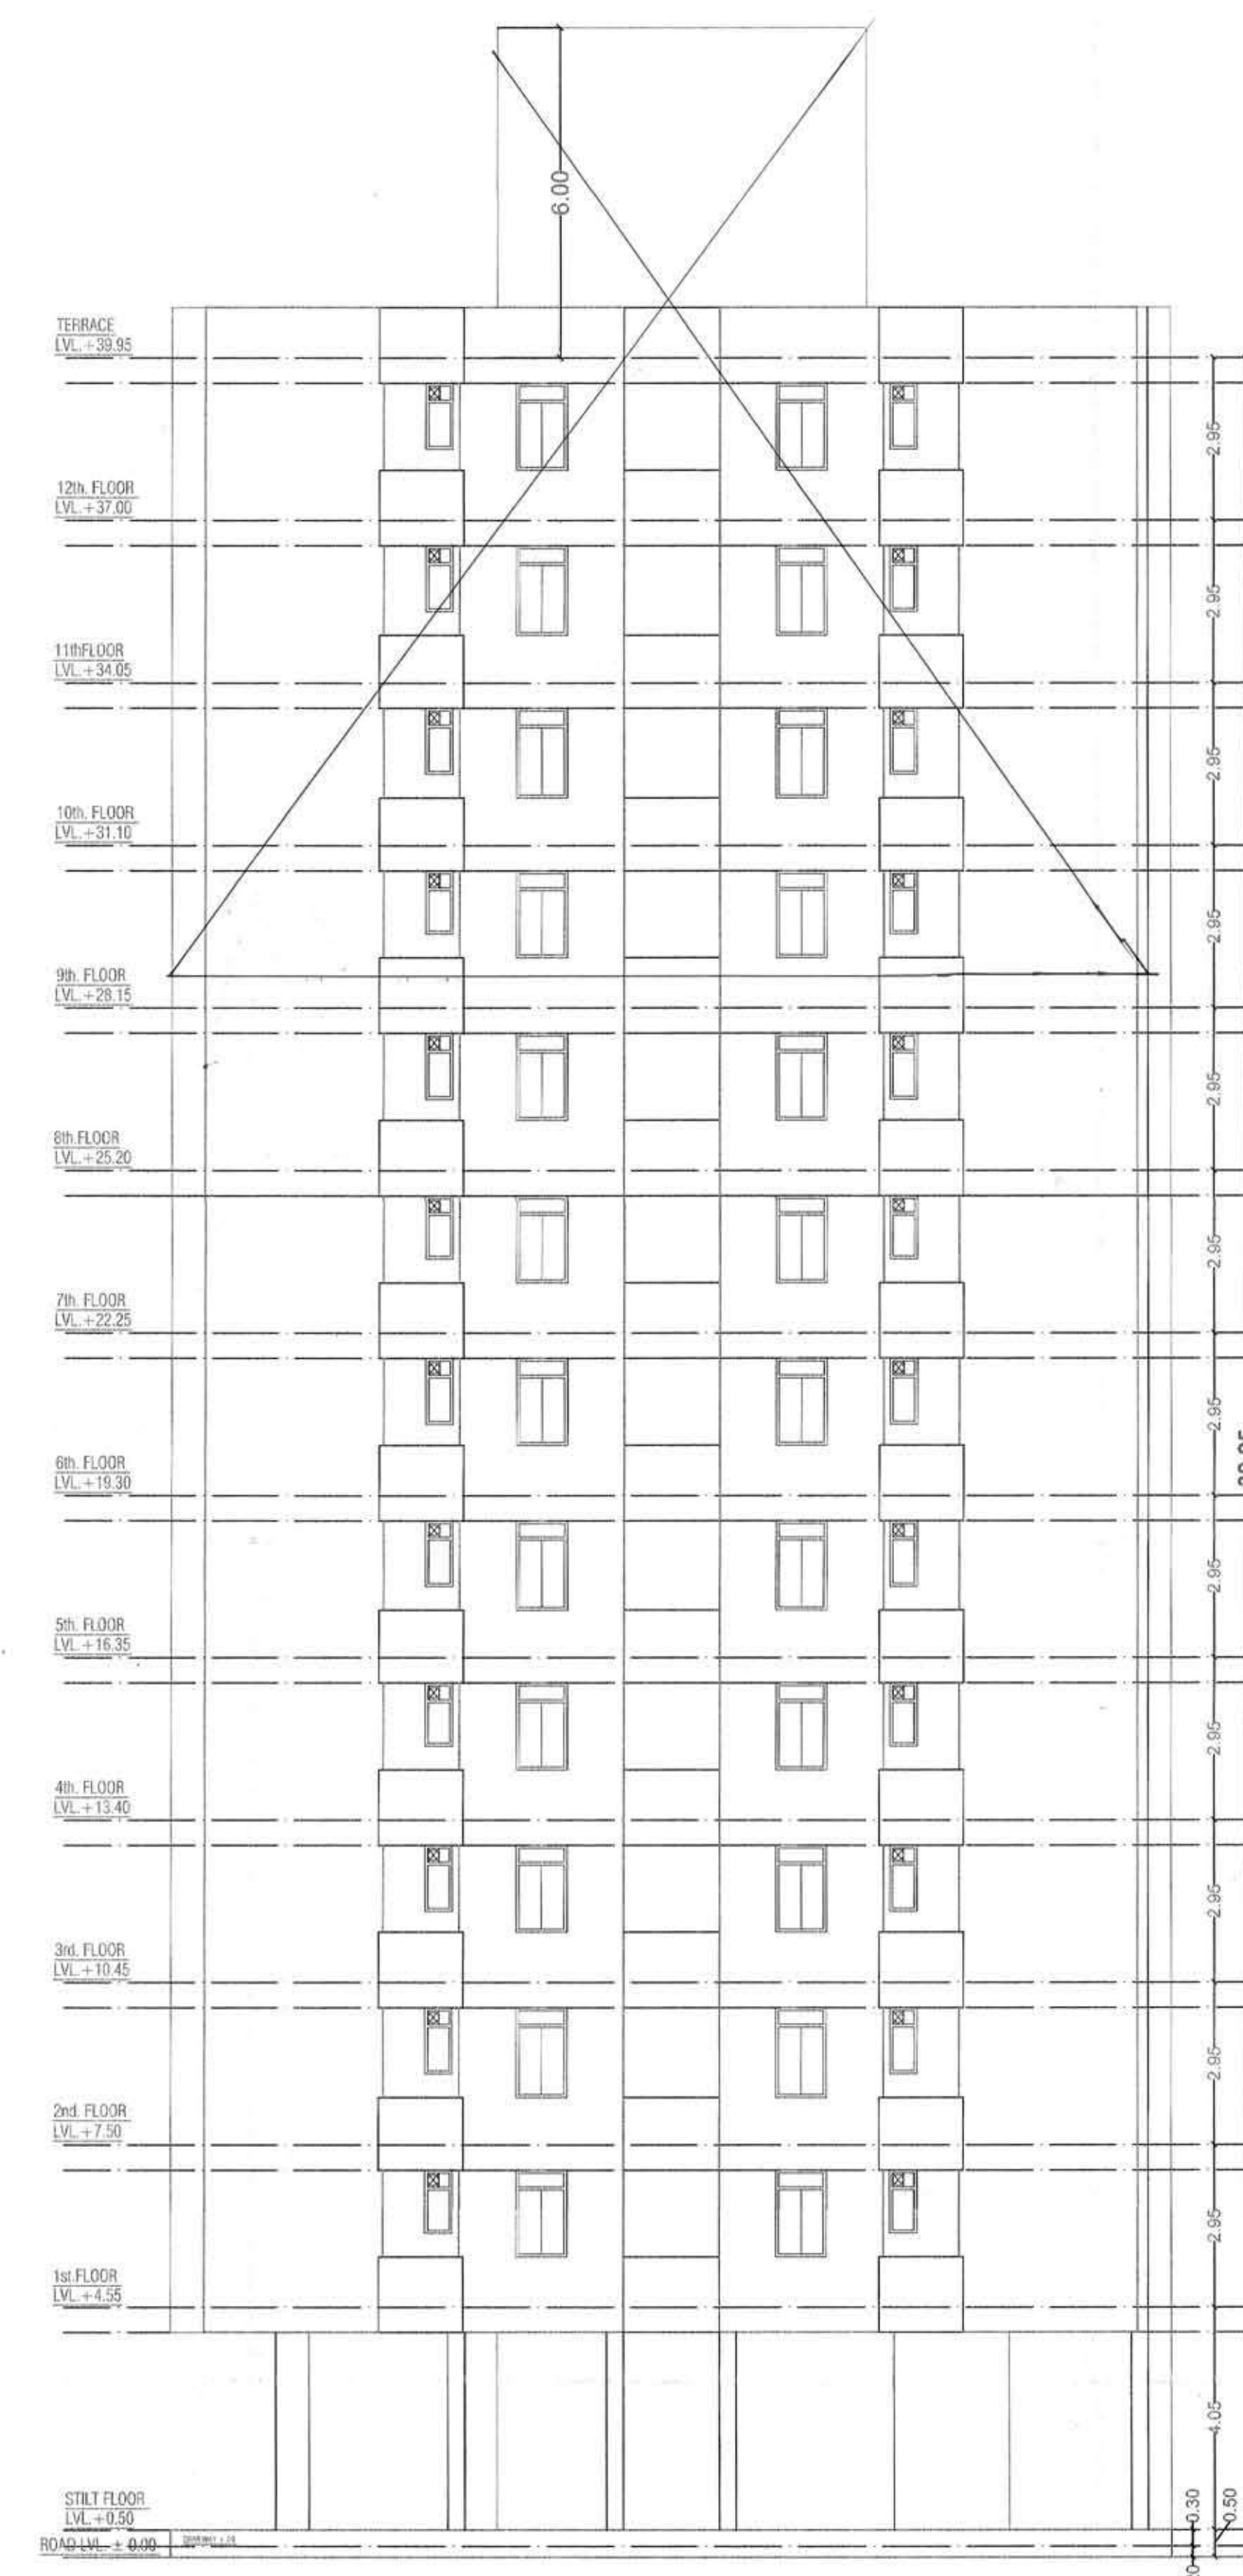

BACK ELEVATION BLOCK D



LEFT SIDE ELEVATION BLOCK D

THIS DRG ENCLOSED WITH LIT LETTER NO. F-7/07P/462/2017 DATED 23.11.17

भूत सम्पत्ति कृषि की सेवा दिनांक 10/10/17 में निर्माता के नाम में मानव अनुमति

भूमि में आधी मॉडल तक बेसमेंट + लिफ्ट + आधी तल (कुल बेसमेंट + लिफ्ट + 28.15 मीटर ऊंचाई तक) तक की स्वीकृत कार्यालय पत्र क्रमांक एक 7/डी.पी./2017 14.6.17-8/17 दिनांक 23.11.17 में वर्णित शर्तों के अधीन जारी की जा रही है।

मानव अनुमति

10/10/17
महेश प्रतापकर
नगर विकास ब्यूरो

वर्गमात्र में आधी मॉडल तक बेसमेंट + लिफ्ट + आधी तल (कुल बेसमेंट + लिफ्ट + 28.15 मीटर ऊंचाई तक) तक की स्वीकृत कार्यालय पत्र क्रमांक एक 7/डी.पी./2017 14.6.17-8/17 दिनांक 23.11.17 में वर्णित शर्तों के अधीन जारी की जा रही है।
उप नगर निरीक्षक
नगर विकास ब्यूरो, कोटा

PROJECT :-
PROPOSED GROUP HOUSING AT PLOT NO :- 01,
VILLAGE - RAMCHANDRAPURA, NEAR VILLAGE POLICE LINE,
KHASRA NO. 95, KOTA.

OWNER
FROM CONSTRUCTION
Res. Agrawal
Authorized Signatures

SHRI KRISHN ARCHITECTS
C-49 VIDYA APARTMENT, PARAS MARG,
BAPU NAGAR, NEAR JANTA STORE CIRCLE,
JALPUR-302015
PH-09314918766, 0141-4005506 (C)
Email:-info.spacegrid@gmail.com

ARCHITECT :-
SPACE GRID