PROPOSED LAY OUT PLAN OF
"Vaishali Estate Block-A Part - 1"

IN VILLAGE- SIRSI & BHANKROTA, TEH. JAIPUR & SANGANER, JAIPUR

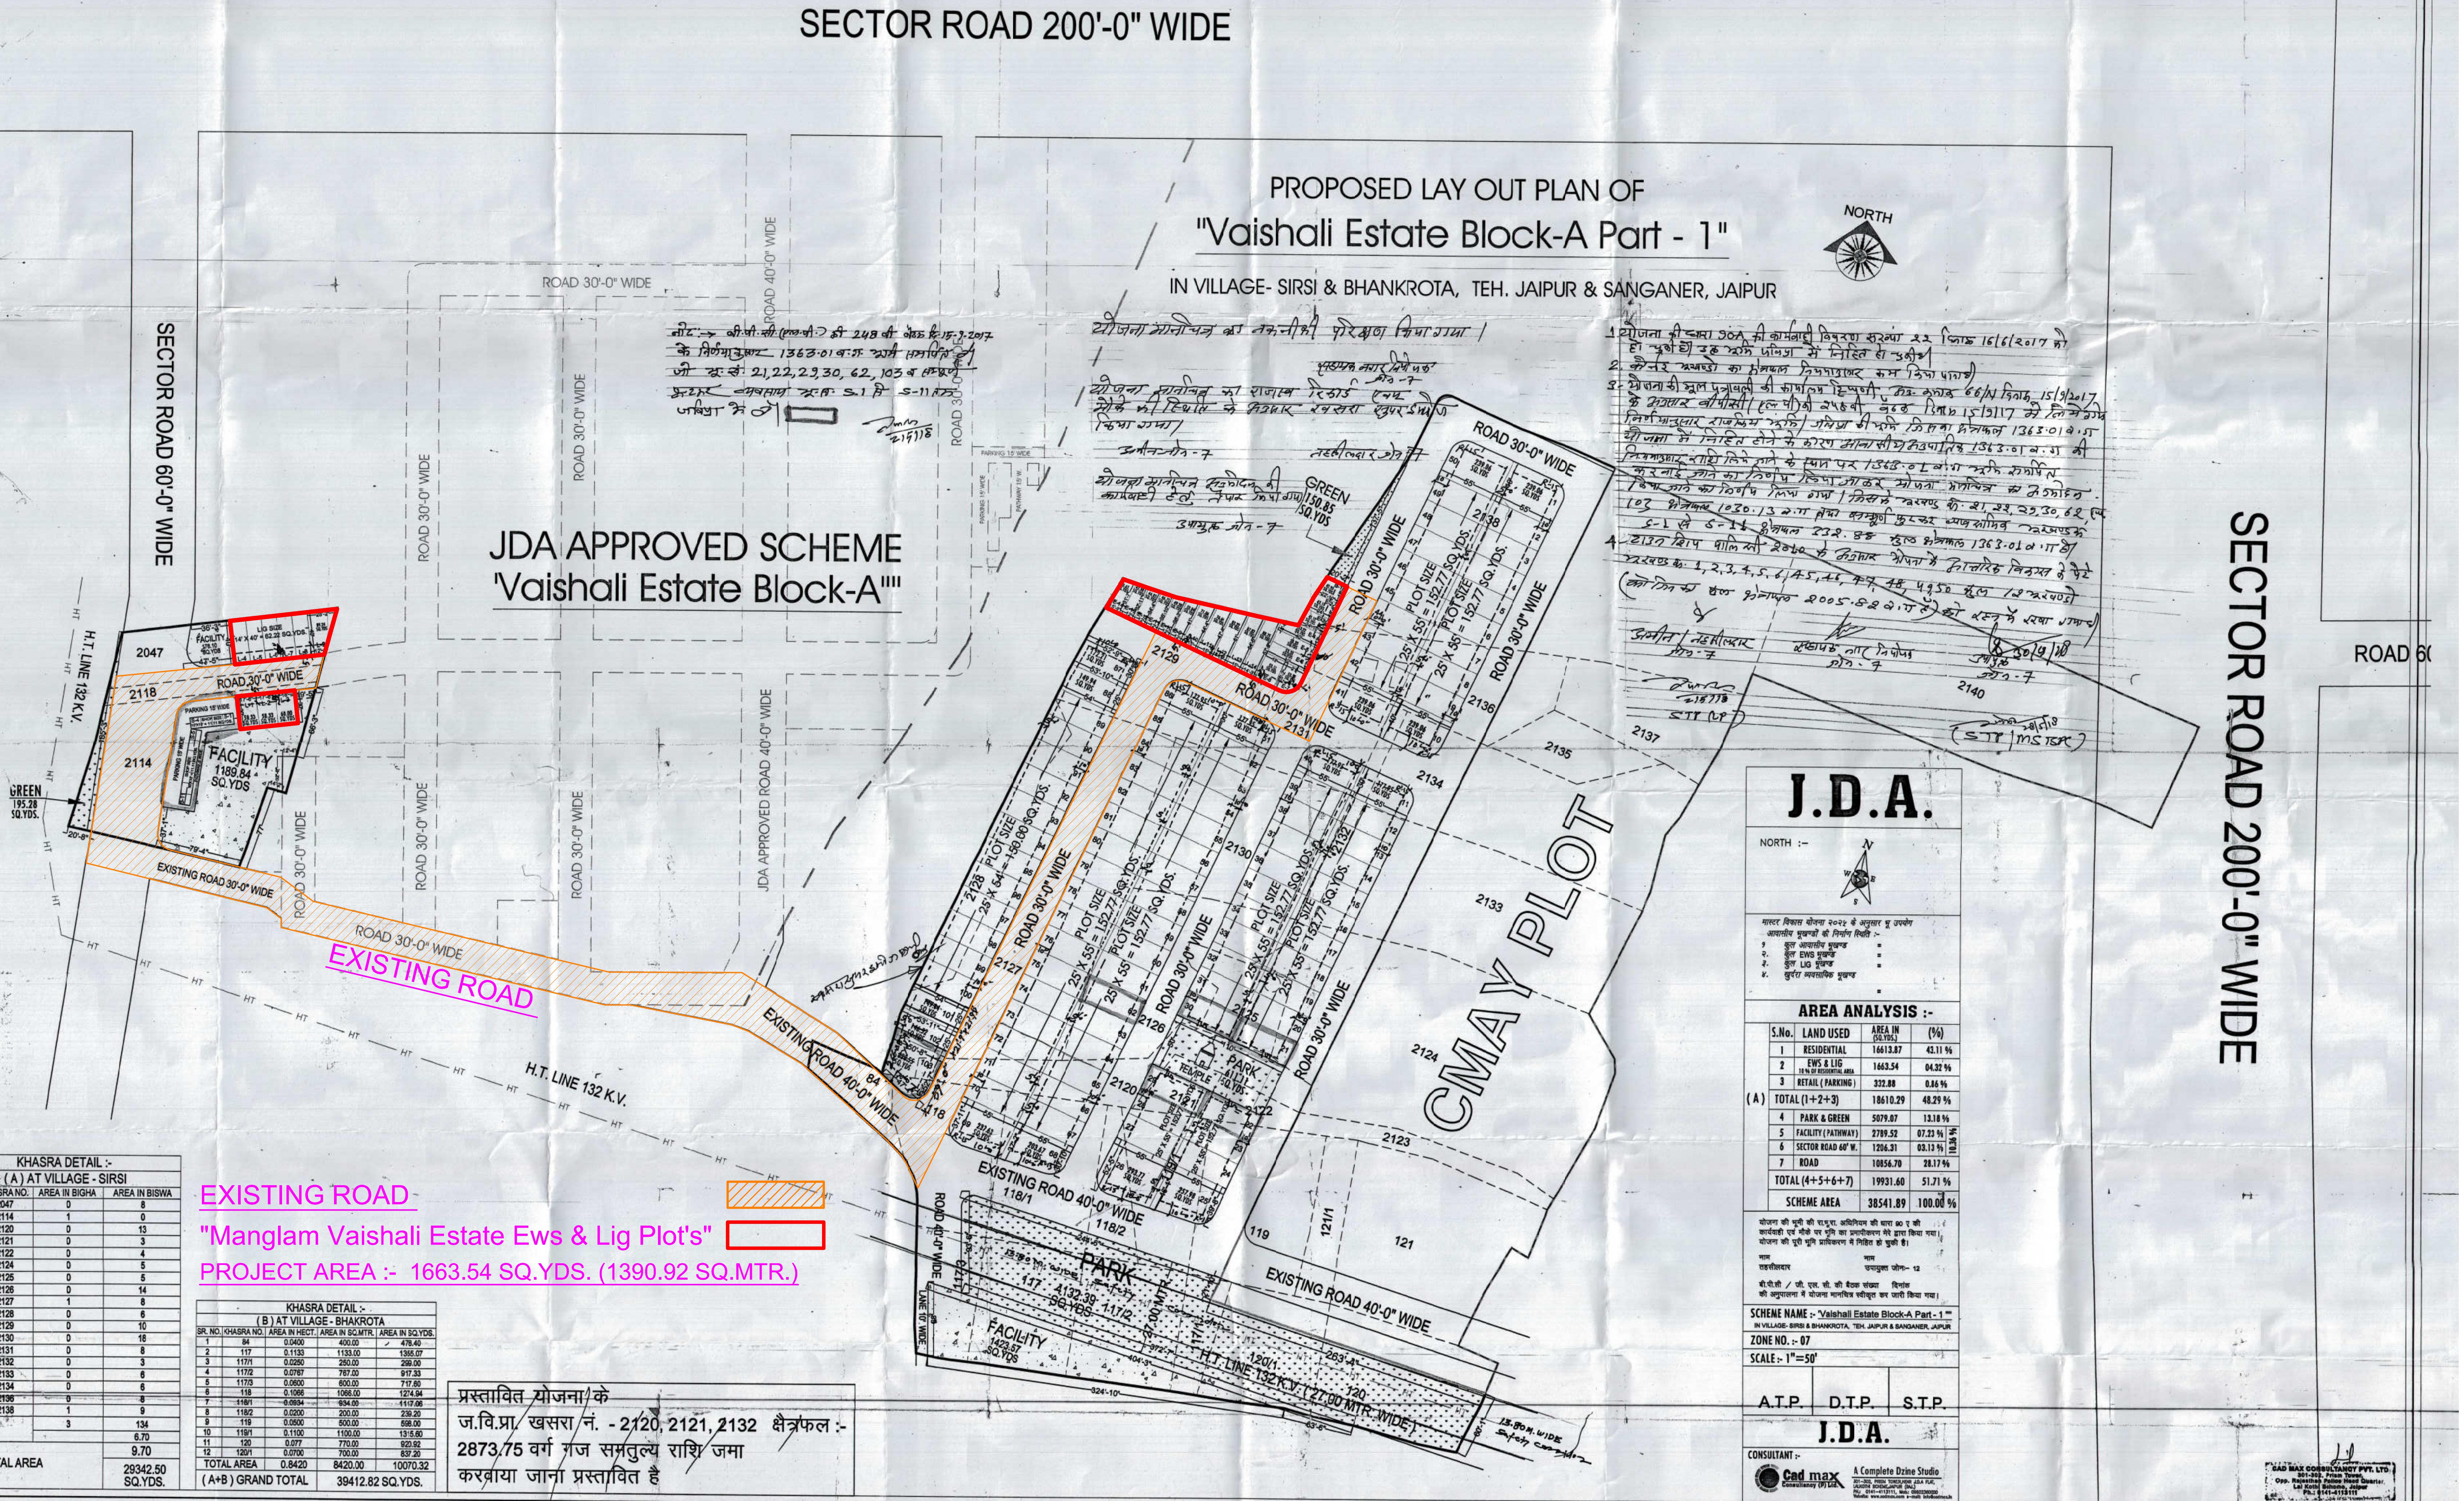
SECTOR ROAD 200'-0" WIDE
SECTOR ROAD 200'-0" WIDE
SECTOR ROAD 60'-0" WIDE
ROAD 60
NORTH
JDA APPROVED SCHEME
'Vaishali Estate Block-A'''
ROAD 30'-0" WIDE
ROAD 40'-0" WIDE
JDA APPROVED ROAD 40'-0" WIDE
PARKING 15' WIDE
PATHWAY 15' W.
H.T. LINE 132 K.V.
HT
GREEN 195.28 SQ.YDS.
2047
2118
2114
FACILITY 1189.84 SQ.YDS
PARKING 15' WIDE
LIG SIZE 14' X 40' = 62.22 SQ.YDS.
ROAD 30'-0" WIDE
EXISTING ROAD 30'-0" WIDE
EXISTING ROAD
EXISTING ROAD 40'-0" WIDE
84
118
2128
PLOT SIZE 25' X 54' = 150.00 SQ.YDS.
2127
2129
2126
2120
2121
2122
2125
2130
2131
2132
2134
2136
2138
25' X 55' PLOT SIZE = 152.77 SQ.YDS.
PARK
TEMPLE
GREEN 150.85 SQ.YDS
ROAD 30'-0" WIDE
2133
2135
2137
2140
2123
2124
CMAY PLOT
119
121
121/1
EXISTING ROAD 40'-0" WIDE
118/1
118/2
117/3
117/1
117/2
117
PARK 4132.39 SQ.YDS
27.00 MTR.
FACILITY 1423.57 SQ.YDS
LANE 10' WIDE
ROAD 40'-0" WIDE
H.T. LINE 132 K.V. (27.00 MTR. WIDE)
120
120/1
13.80 M. WIDE Safety corridor

नोट:→ बी.पी.सी.(एल.पी.) की 248 वीं बैठक दि. 15-9-2017 के निर्णयानुसार 1363.01 व.ग. भूमि समर्पित की जो भू.सं. 21, 22, 29, 30, 62, 103 व सम्पूर्ण फुटकर व्यवसाय भू.क्र. S.1 से S-11 तक जविप्रा के हो।

2/5/18

योजना मानचित्र का तकनीकी परीक्षण किया गया।

सहायक नगर नियोजक
जोन-7

योजना मानचित्र का राजस्व रिकार्ड (मय मौके की स्थिति के अनुसार खसरा सुपरइम्पोज किया गया।

अमीन जोन-7
तहसीलदार जोन-7

योजना मानचित्र संशोधन की कार्यवाही हेतु तैयार किया गया।

उपायुक्त जोन-7

1. योजना की धारा 90A की कार्यवाही विवरण संख्या 22 दिनांक 16/6/2017 को हो चुकी है उक्त भूमि जविप्रा में निहित हो चुकी है।
2. कॉर्नर भूखण्डो का क्षेत्रफल नियमानुसार कम किया जावे।
3- योजना की मूल पत्रावली की कार्यालय टिप्पणी क्र. क्रमांक 66/N दिनांक 15/9/2017 के अनुसार बीपीसी (एल.पी.) की 248वीं बैठक दिनांक 15/9/17 में लिये गये निर्णयानुसार राजकीय भूमि/जविप्रा की भूमि जिसका क्षेत्रफल 1363.01 व.ग. योजना में निहित होने के कारण आनुपातिक 1363.01 व.ग. की नियमानुसार राशि लिये जाने के स्थान पर 1363.01 व.ग. भूमि समर्पित करवाई जाने का निर्णय लिया जाकर योजना मानचित्र का संशोधन किया जाने का निर्णय लिया गया। जिसके भूखण्ड क्र. 21, 22, 29, 30, 62, 103 क्षेत्रफल 1030.13 व.ग. तथा सम्पूर्ण फुटकर व्यवसायिक भूखण्ड S-1 से S-11 क्षेत्रफल 332.88 कुल क्षेत्रफल 1363.01 व.ग. है।
4- टाउनशिप पालिसी 2010 के अनुसार योजना के आन्तरिक विकास के पेटे भूखण्ड क्र. 1, 2, 3, 4, 5, 6, 45, 46, 47, 48, 49, 50 कुल 12 भूखण्डो (जिनका कुल क्षेत्रफल 2005.82 व.ग. है) को रहन में रखा जावे।

अमीन / तहसीलदार
जोन-7

सहायक नगर नियोजक
जोन-7

30/4/18
उपायुक्त
जोन-7

2/5/18
STP (LP)

(STP / MS ISPC)

EXISTING ROAD ▨

"Manglam Vaishali Estate Ews & Lig Plot's" 🟥

PROJECT AREA :- 1663.54 SQ.YDS. (1390.92 SQ.MTR.)

KHASRA DETAIL :-
(A) AT VILLAGE - SIRSI

SR. NO.	KHASRA NO.	AREA IN BIGHA	AREA IN BISWA
1	2047	0	8
2	2114	1	0
3	2120	0	13
4	2121	0	3
5	2122	0	4
6	2124	0	5
7	2125	0	5
8	2126	0	14
9	2127	1	8
10	2128	0	6
11	2129	0	10
12	2130	0	18
13	2131	0	8
14	2132	0	3
15	2133	0	6
16	2134	0	6
17	2136	0	8
18	2138	1	9
		3	134
			6.70
TOTAL AREA			9.70
			29342.50 SQ.YDS.

KHASRA DETAIL :-
(B) AT VILLAGE - BHAKROTA

SR. NO.	KHASRA NO.	AREA IN HECT.	AREA IN SQ.MTR.	AREA IN SQ.YDS.
1	84	0.0400	400.00	478.40
2	117	0.1133	1133.00	1355.07
3	117/1	0.0250	250.00	299.00
4	117/2	0.0767	767.00	917.33
5	117/3	0.0600	600.00	717.60
6	118	0.1066	1066.00	1274.94
7	118/1	0.0934	934.00	1117.06
8	118/2	0.0200	200.00	239.20
9	119	0.0500	500.00	598.00
10	119/1	0.1100	1100.00	1315.60
11	120	0.077	770.00	920.92
12	120/1	0.0700	700.00	837.20
TOTAL AREA		0.8420	8420.00	10070.32
(A+B) GRAND TOTAL			39412.82 SQ.YDS.	

प्रस्तावित योजना के ज.वि.प्रा. खसरा नं. - 2120, 2121, 2132 क्षेत्रफल :- 2873.75 वर्ग गज समतुल्य राशि जमा करवाया जाना प्रस्तावित है

J.D.A.

NORTH :-

मास्टर विकास योजना २०२५ के अनुसार भू उपयोग
आवासीय भूखण्डों की निर्माण स्थिति :-
१ कुल आवासीय भूखण्ड =
२. कुल EWS भूखण्ड =
३. कुल LIG भूखण्ड =
४. खुर्दरा व्यवसायिक भूखण्ड =

AREA ANALYSIS :-

	S.No.	LAND USED	AREA IN (SQ.YDS.)	(%)	
	1	RESIDENTIAL	16613.87	43.11 %	
	2	EWS & LIG 10 % OF RESIDENTIAL AREA	1663.54	04.32 %	
	3	RETAIL (PARKING)	332.88	0.86 %	
(A)	TOTAL (1+2+3)		18610.29	48.29 %	
	4	PARK & GREEN	5079.07	13.18 %	
	5	FACILITY (PATHWAY)	2789.52	07.23 %	10.36 %
	6	SECTOR ROAD 60' W.	1206.31	03.13 %	
	7	ROAD	10856.70	28.17 %	
	TOTAL (4+5+6+7)		19931.60	51.71 %	
	SCHEME AREA		38541.89	100.00 %	

योजना की भूमि की रा.भू.रा. अधिनियम की धारा 90 ए की कार्यवाही एवं मौके पर भूमि का प्रमापीकरण मेरे द्वारा किया गया। योजना की पूरी भूमि प्राधिकरण में निहित हो चुकी है।

नाम
तहसीलदार

नाम
उपायुक्त जोन:- 12

बी.पी.सी / जी. एल. सी. की बैठक संख्या दिनांक की अनुपालना में योजना मानचित्र स्वीकृत कर जारी किया गया।

SCHEME NAME :- 'Vaishali Estate Block-A Part - 1'''
IN VILLAGE- SIRSI & BHANKROTA, TEH. JAIPUR & SANGANER, JAIPUR

ZONE NO. :- 07

SCALE :- 1"=50'

A.T.P.	D.T.P.	S.T.P.

J.D.A.

CONSULTANT :-
Cad max Consultancy (P) Ltd.
A Complete Dzine Studio

CAD MAX CONSULTANCY PVT. LTD.
301-302, Pritam Tower,
Opp. Rajasthan Police Head Quarter,
Lal Kothi Scheme, Jaipur
Ph.: 0141-4115111