



जयपुर विकास प्राधिकरण, जयपुर राजस्थान सरकार



क्रमांक: JDA/2019-20/BPAS/86

दिनांक: 18/02/2020

विषय: — भूखण्ड संख्या/ खसरा नम्बर KHASRA NO. 183/329, 231, 233,, स्कीम VIRAT MURLI, तहसील जयपुर, जयपुर के प्रस्तावित भवन मानचित्र अनुमोदन बाबत।

महोदय,

श्री/श्रीमती VIVEK CHATURVEDI 'फर्म का नाम VIRAT MURLI INFRA LLI' निवासी VAIDIAV COMPLEX, OFFICE NO. 616, 6TH FLOOR, VAIJALALI NAGAR, JAIPUR

आपका प्रार्थना पत्र दिनांक 16/10/2019 के संदर्भ में भूखण्ड संख्या/ खसरा नम्बर KHASRA NO. 183/329, 231, 233, स्कीम VIRAT MURLI, ग्राम कनकपुरा, तहसील जयपुर, में स्थित भूखण्ड (क्षेत्रफल 7744.80 वर्गमीटर) के RESIDENTIAL के भवन मानचित्र अनुमोदन के लिए प्रस्तुत किये गये थे, उनकी स्वीकृति भवन मानचित्र समिति (बीपी) की 222 वीं बैठक दिनांक 04/12/2019 के निर्णयानुसार निम्न शर्तों के साथ दी जाती है:-

1. यह भवन अनुज्ञा दिनांक 25/12/2025 तक प्रभावी है।
2. भवन निर्माण स्वीकृत मानचित्र के अनुसार ही किया जावेगा तथा किसी भी प्रकार का उल्लंघन (डेवियेशन) नहीं किया जायेगा।
3. भूखण्ड के स्वामी एवं मानचित्र तैयार करने वाले तकनीकीविज्ञ का कर्तव्य होगा कि वो यह सुनिश्चित कर ले कि स्वीकृति मानचित्र प्रचलित मास्टर प्लान/जोनल प्लान के अनुरूप है यदि कोई उल्लंघन जानकारी में नहीं है, प्राधिकरण को अधिकार होगा कि किसी स्थिति में उल्लंघन की जानकारी होने पर भवन मानचित्रों को दी गयी अनुज्ञा रद्द/बदली जा सकती है तथा प्रार्थी प्राधिकरण में किसी भी प्रकार की क्षतिपूर्ति का हकदार नहीं होगा।
4. एकीकृत भवन विनियम 2017 के विनियम संख्या 8.11.2 के अनुसार अपशिष्ट जल का शुद्धिकरण एवं रिसाईकिलिंग हेतु भवन विनियमों के प्रावधानों की पालना सुनिश्चित की जानी होगी।
5. एकीकृत भवन विनियम 2017 के विनियम संख्या 8.11.4 के अनुसार ठोस कचरा निस्तारण हेतु भवन विनियमों के प्रावधानों की पालना सुनिश्चित की जानी होगी।
6. एकीकृत भवन विनियम 2017 के विनियम संख्या 8.11.5 के अनुसार सौर ऊर्जा संयंत्र संबंधी भवन विनियमों के प्रावधानों की पालना सुनिश्चित की जानी होगी।
7. एकीकृत भवन विनियम 2017 के विनियम संख्या 10.3 के अनुसार भवन में विद्युत आवश्यकताओं की पूर्ति हेतु संबंधित विद्युत वितरण एजेंसी के प्रावधानों की पालना एवं एनर्जी कन्वर्जेशन बिल्डिंग कोड के प्रावधानों की पालना सुनिश्चित की जानी होगी।
8. आप द्वारा एकीकृत भवन विनियम 2017 की धारा 15.2 के अनुसार भवन निर्माण प्रारम्भ करते समय एक सूचना पट्ट मौके पर लगाया जायेगा। जिसमें संबंधित आयुक्त/उपायुक्त संबंधित जोन व प्रवर्तन अधिकारी के टेलीफोन नम्बर इत्यादि अंकित किये जाने होंगे व अनुमोदित मानचित्र की सूचना व अनुमोदन की शर्तें अंकित की जायेगी। निर्माण के दौरान अनुमोदित मानचित्र की एक प्रति आवश्यक रूप से निर्माणकर्ता द्वारा मौके पर रखी जायेगी।
9. निर्माण कार्य प्रारम्भ करने से पूर्व आप उपायुक्त (जोन-७) प्राधिकरण को निर्धारित प्रपत्र में सूचना प्रस्तुत करेंगे।
10. आप द्वारा एकीकृत भवन विनियम 2017 की धारा 15.3 के अनुसार भवन निर्माण द्वारा प्लिन्थ लेवल तक का निर्माण पूर्ण होने की सूचना निर्धारित प्रपत्र में आवश्यक रूप से उपायुक्त (जोन-७) को दी जानी होगी, यदि इसकी अनुपालना भवन निर्माता द्वारा नहीं की जाती है तो जारी अनुज्ञा को वापस ले लिया जावेगा।
11. एकीकृत भवन विनियम 2017 की धारा 15.5 के अनुसार भवन विनियम के अपेक्षाओं के अनुरूप भवन निर्माण करने की जिम्मेदारी भवन निर्माण अनुज्ञाधारी की होगी।
12. उक्त स्वीकृति के कारण यदि जयपुर विकास प्राधिकरण, जयपुर को किसी न्यायालय, सक्षम अधिकारी तथा नगर भूमि (अधिकतम सीमा एवं विनियम) अधिनियम के तहत नियुक्त अधिकारी के समक्ष किसी कार्यवाही में कोई भी खर्च, नुकसान, मुआवजा देना पड़े या देने योग्य हो तो प्रार्थी उनकी इस क्षति को पूर्ण करने के लिए बाध्य होगा।
13. दरवाजे एवं खिड़कियाँ इस प्रकार लगाए जायेंगे कि वो सड़क की ओर निकले हुए नहीं हों।
14. भूस्वामी प्रत्येक मंजिल के लिए स्वीकृत संस्थानिक ईकाई से अधिक का निर्माण नहीं करेगा।
15. भूस्वामी भवन के परिसर को स्वीकृत उपयोग के अनुसार ही उपयोग में लेगा।
16. तकनीकीविज्ञ के निरीक्षण में स्वामी निर्माण कार्य करवायेगा जिसके संबंध में सूचना प्राधिकरण को पूर्व में देनी होगी। यदि

तकनीकीविज्ञ को बदला जाता है तो इसकी सूचना 48 घन्टे के अन्दर यथोचित प्रमाण-पत्र में प्राधिकरण को देनी होगी।

17. स्वीकृत मानचित्र में विभिन्न वर्गों के लिए प्लेट्सों की संख्या के साथ संबंधित कन्स्ट्रक्शन फर्म का नाम निर्माण प्रारम्भ करने की दिनांक व निर्माण पूर्ण करने की संभावित अवधि मौके पर उपयुक्त स्थान पर बोर्ड लगाकर उस पर स्पष्टरूप से दर्शाने होंगे।

18. आवेदक द्वारा पार्किंग क्षेत्र की पालना एकीकृत भवन विनियम 2017 के विनियम 10.1.16 के अनुसार सुनिश्चित की जानी होगी।

19. भवन परिसर में आगंतुकों की पार्किंग करवाई जाए तथा आगंतुकों हेतु निःशुल्क वाहन पार्किंग का बोर्ड लगवाया जावे।

20. प्रॉपेटे उपलब्ध (विपरीत विकासकर्ता) को मौके पर लगावली पार्किंग क्षेत्र में लगावली जायेगी जहाँ निर्माण कार्य की गुणवत्ता की समय-समय पर जाँच की जाए।

21. स्वीकृत मानचित्र मौके पर उपयुक्त स्थान पर बोर्ड लगाकर उस पर स्पष्टरूप से दर्शाने होंगे।

22. निर्माण स्थल पर स्वीकृति का विवरण अर्थात् अनुमोदित मानचित्र, उपलब्ध पार्किंग की सूचना एवं भवन में सुरक्षा एवं निकास प्लान (Escape Plan) का नक्शा भी प्रदर्शित (Display) उपयुक्त स्थान पर प्रदर्शित किया जावे।

23. भवन का उपयोग प्रारम्भ होने पर एक केयर टेकर की नियुक्ति की जावे जिसके पास भवन का मानचित्र, सुरक्षा एवं निकास प्लान (Escape Plan) उपलब्ध रहें। इस प्रकार नियुक्त केयर टेकर के मोबाईल नंबर एवं Land Line Number भी लिये जाकर पुलिस आयुक्त जयपुर महानगर व उपायुक्त जोन को सूचना उपलब्ध करवाई जावे ताकि किसी भी दुर्घटना की स्थिति में बचाव कार्य प्रभावी रूप से किये जा सकें।

24. एकीकृत भवन विनियम 2017 की धारा 18.3 की अनुपालना में "गलत तथ्यों पर प्राप्त की गई अथवा तथ्यों को छुपाकर प्राप्त की गई स्वीकृति स्वतः निरस्त मानी जायेगी एवं ऐसी निर्माण स्वीकृति प्राप्त करने के लिए आवेदनकर्ता को दोषी माना जायेगा।

25. प्रश्नगत प्रकरण किसी भी न्यायालय में यदि लंबित है तो उसकी समस्त जिम्मेदारी आवेदक की ही होगी। यदि मानचित्र जारी होने के पश्चात यह अवगत हुआ कि किसी भी माननीय न्यायालय में प्रकरण लंबित है अथवा विपरीत निहित है तो मानचित्र स्वतः ही निरस्त समझे जावेंगे।

26. अनुमोदित भवन मानचित्रों को भवन निर्माण शुरू किये जाने के समय भवन निर्माता द्वारा एक बोर्ड पर सम्पूर्ण ब्यौरा सहित जो पठनीय हो, को ऐसे स्थल पर (मुख्य सड़क की ओर) लगाया जावे, जिससे सभी लोगों को निर्मित किये जाने वाले भवन के अनुमोदन की पूर्ण जानकारी प्राप्त हो सके।

27. भवन निर्माण के समय निर्माण सामग्री से आसपास के भवनों के निवासकर्ताओं को किसी प्रकार की असुविधा न हो, इस हेतु भवन निर्माण के दौरान चारों ओर पर्दे लगवाये जावें।

28. भवन मानचित्र इस शर्त के साथ जारी किये जाते हैं कि आप द्वारा परियोजना के पूर्णता प्रमाण पत्र के आवेदन के साथ अग्निशमन विभाग का अनापत्ति प्रमाण पत्र एवं पर्यावरण विभाग का अनापत्ति प्रमाण पत्र नगरीय निकाय में जमा कराना होगा, उसके पश्चात ही पूर्णता प्रमाण पत्र जारी किया जायेगा।

29. निर्मित भवन के प्रवेश द्वार के पास भवन में अनुमोदित व उपलब्ध चार पहिया व दो पहिया वाहनों के पार्किंग की सूचना का बोर्ड (डिस्प्ले) लगवाया जावे।

30. प्रश्नगत भूखण्ड के भवन मानचित्र ऑफलाईन जारी किये जा रहे हैं अतः सिस्टम द्वारा यदि ऑनलाईन भवन मानचित्र जारी किये जाते हैं तो वह मान्य नहीं होंगे।

For VIRAT MURLI INFRA LLP

Partner

अतिरिक्त मुख्य नगर नियोजक,

भवन मानचित्र समिति (बीपी)

जयपुर विकास प्राधिकरण, जयपुर



Signature valid

Digitally Signed by OM PRAKASH PAREEK
Designation : A2/CP
Date: 2020.02.18 12:57:56 IST
Reason: Approved
Location: TEST

नोट: यह एक डिजिटल हस्ताक्षरित प्रमाण पत्र है और इसके लिए किसी भौतिक हस्ताक्षर की आवश्यकता नहीं है।

आवश्यक न्यूनतम 10% का प्लाट पर आवेदन के साथ प्रस्तुत किया जाना चाहिए।
आवश्यक न्यूनतम 10% का प्लाट पर आवेदन के साथ प्रस्तुत किया जाना चाहिए।
इस परियोजना हेतु आवश्यक ई.डब्ल्यू.एस./एल.आई.जी. के आवासीय का प्रावधान Split Location खसरा नम्बर 490, 491, 492, 493, 498/2, ग्राम बिन्दायका, तहसील सांगानेर, जयपुर पर प्रस्तावित हैं जिनके मुख्यमंत्री जन आवास योजना के अन्तर्गत भवन मानचित्रों का अनुमोदन बीपीसी-बीपी की 207वीं बैठक दिनांक 20.11.2018 में कर दिनांक 10.01.2019 को भवन मानचित्र जारी किये गये हैं। प्रस्तुत प्रस्ताव अनुसार बी ब्लॉक में भूतल पर एल.आई.जी. के प्लेट नम्बर LB/G/03 To LB/G/14, तृतीय तल पर LB/III/309 To LB/III/313 सी ब्लॉक में तृतीय तल पर LC/III/307 & LC/III/308, चतुर्थ तल पर LC/IV/405 To LC/IV/412 इस प्रकार कुल 27 प्लेट्स जिनका प्रत्येक का क्षेत्रफल 537.36 वर्गफीट है जिनका संयुक्त क्षेत्रफल 14508.72 वर्गफीट है। सी ब्लॉक में भूतल पर ई.डब्ल्यू. एस. प्लेट नम्बर EC/G/09 & EC/G/10, तृतीय तल पर EC/III/309 & EC/III/310, चतुर्थ तल पर EC/IV/403 To EC/IV/406 & EC/IV/410 इस प्रकार कुल 9 प्लेट्स जिनका प्रत्येक का क्षेत्रफल 391.13 वर्गफीट है जिनका संयुक्त क्षेत्रफल 3520.17 वर्गफीट है।

AREA CALCULATION			
NET PLOT AREA		7744.80	SQ.MT.
PER. B.A.R.	2.0+0.75 (EWS/LIG)	21298.20	SQ.MT.
CONSUMED B.A.R.	4.2	32574.29	SQ.MT.
GR. COVERAGE PER.	40%	3097.92	SQ.MT.
GR. COVERAGE ACHIEVED	39.25%	3039.57	SQ.MT.
GREEN AREA REQUIRED	20%	1548.96	SQ.MT.
GREEN AREA PROVIDED	24.33%	1884.49	SQ.MT.
ON GROUND	7.14%	563.62	SQ.MT.
ON PODIUM	17.19%	1330.87	SQ.MT.

CLUB	2.57%	831.90	SQ.MT.
RETAIL COMMERCIAL	1.02%	330.60	SQ.MT.

PERMISSIBLE HT = 48 MTS.
ACHIEVED HT. = 38.55 MTS + 0.50 (PLINTH)



PARKING CALCULATION			
	B.A.R.	REQ. E.C.U.	
TOTAL B.A.R.	32574.29		
COMMERCIAL B.A.R.	330.60	4.41	
RESIDENTIAL B.A.R.	32243.69	280.38	
TOTAL PARKING REQ.		284.79	

VISITORS PARKING			
FOR 100 ECU	25%	25.00	E.C.U.
FOR 101 TO 200 ECU	20%	20.00	E.C.U.
FOR 201 TO 300 ECU	15%	12.72	E.C.U.
TOTAL VISITORS PARKING REQ.		57.72	E.C.U.
TOTAL REQUIRED PARKING		342.51	E.C.U.
	SAY	343.00	E.C.U.
TOTAL REQUIRED PARKING	75%	257.25	E.C.U.
	25%	85.75	E.C.U.
		257.25	SCOOTER

PROVIDED PARKING			
OPEN		38	0
STILT FLR		48	50
1st BASE FLR		135	154
2nd BASE FLR		62	96
TOTAL		283	300
			383
			E.C.U.

AREA STATEMENT						
FLOOR	BLOCK	CUT OUT	G.B.U.A.	LIFT	FIRE STAIR	BAR
2ND BASEMENT	2813.91	0.00	2813.91	28.98		0.00
1ST BASEMENT	6584.73	0.00	6584.73	28.98		136.92
GROUND	3072.39	48.21	3024.18	28.98	31.70	1203.29
1st FLOOR	2732.57	69.05	2663.52	28.98	31.70	2602.84
2nd FLOOR	2732.57	69.05	2663.52	28.98	31.70	2602.84
3rd FLOOR	2732.57	69.05	2663.52	28.98	31.70	2602.84
4th FLOOR	2732.57	69.05	2663.52	28.98	31.70	2602.84
5th FLOOR	2732.57	69.05	2663.52	28.98	31.70	2602.84
6th FLOOR	2732.57	69.05	2663.52	28.98	31.70	2602.84
7th FLOOR	2732.57	69.05	2663.52	28.98	31.70	2602.84
8th FLOOR	2732.57	69.05	2663.52	28.98	31.70	2602.84
9th FLOOR	2732.57	69.05	2663.52	28.98	31.70	2602.84
10th FLOOR	2732.57	69.05	2663.52	28.98	31.70	2602.84
11th FLOOR	2732.57	69.05	2663.52	28.98	31.70	2602.84
12th FLOOR	2732.57	69.05	2663.52	28.98	31.70	2602.84
TERRACE	116.98		116.98			
TOTAL	45378.85	876.81	44502.04	434.70	412.10	32574.29

GUARD RM	15.39	COMM.	330.60
		CLUB	831.90
		SERVICES	136.92
			40.79
		1ST BASE.	
		STILT	

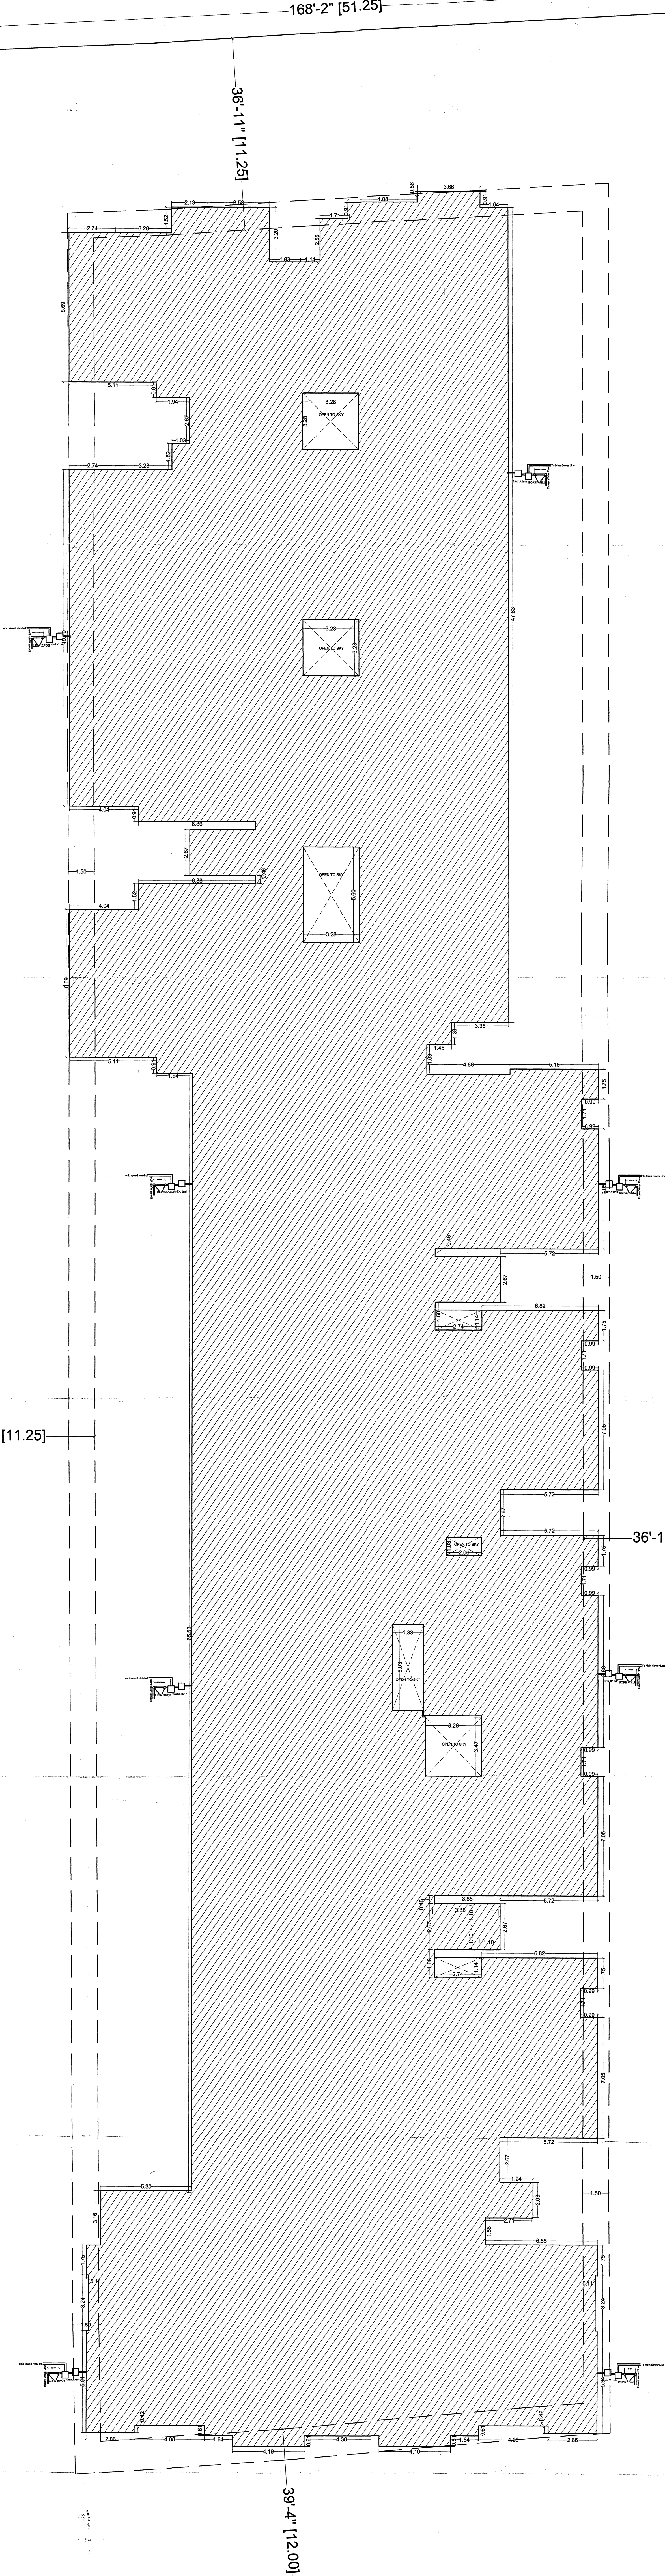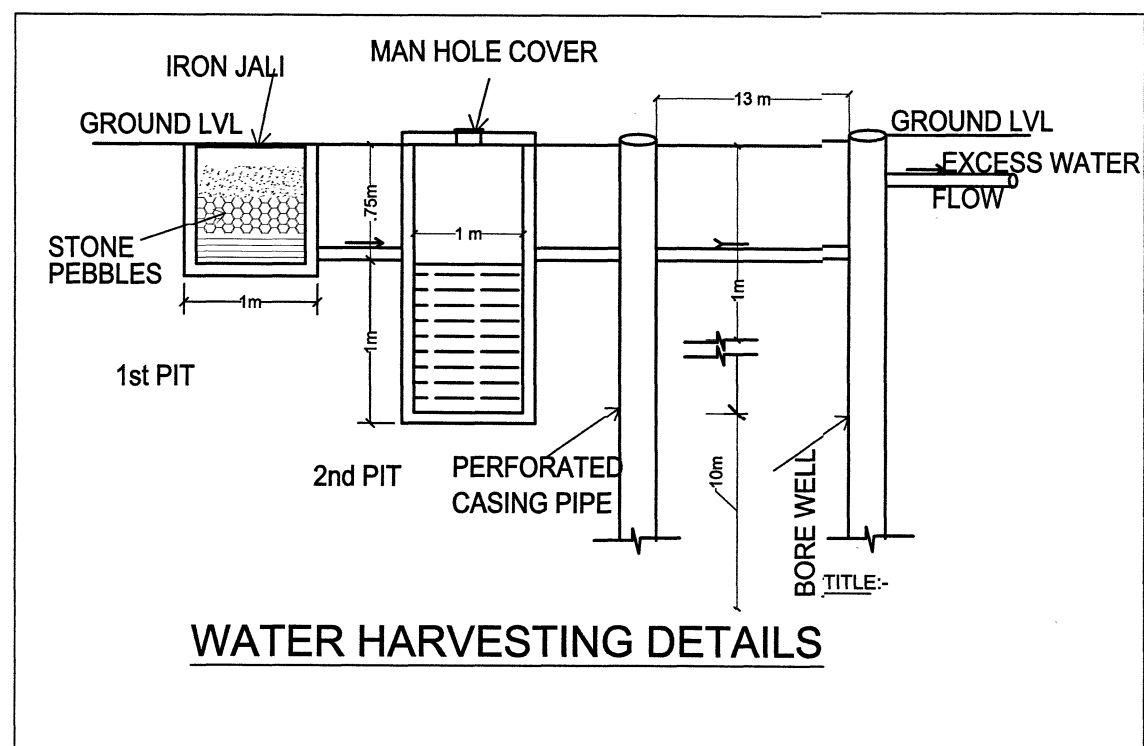

SHEET NO. - 1/6

TITLE:-
SITE PLAN

SITE PLAN

NORTH : SCALE : 1= 125
DATE : 09-01-2020

PROJECT:-
PROPOSED GROUP HOUSING
AT KHASARA NO.- 183/329,231,233
VILLAGE KANAKPURA, JAIPUR



ARCHITECTS:-
ANOOP GUPTA & ASSOCIATES
ARCHITECTS & INTERIOR CONSULTANTS
91, VISINU GARDEN COLONY, NEAR AIRPORT CIRCLE,
TONG ROAD, JAIPUR - 302029
TEL. : 0141-2622948

SIGN :
ARCHITECT
OWNER

For VIKAS MURLI INFRA LLP
Partner

SHEET NO. - 2/6

TITLE:-
1ST BASEMENT FLR PLAN
&
2ND BASEMENT FLR PLAN

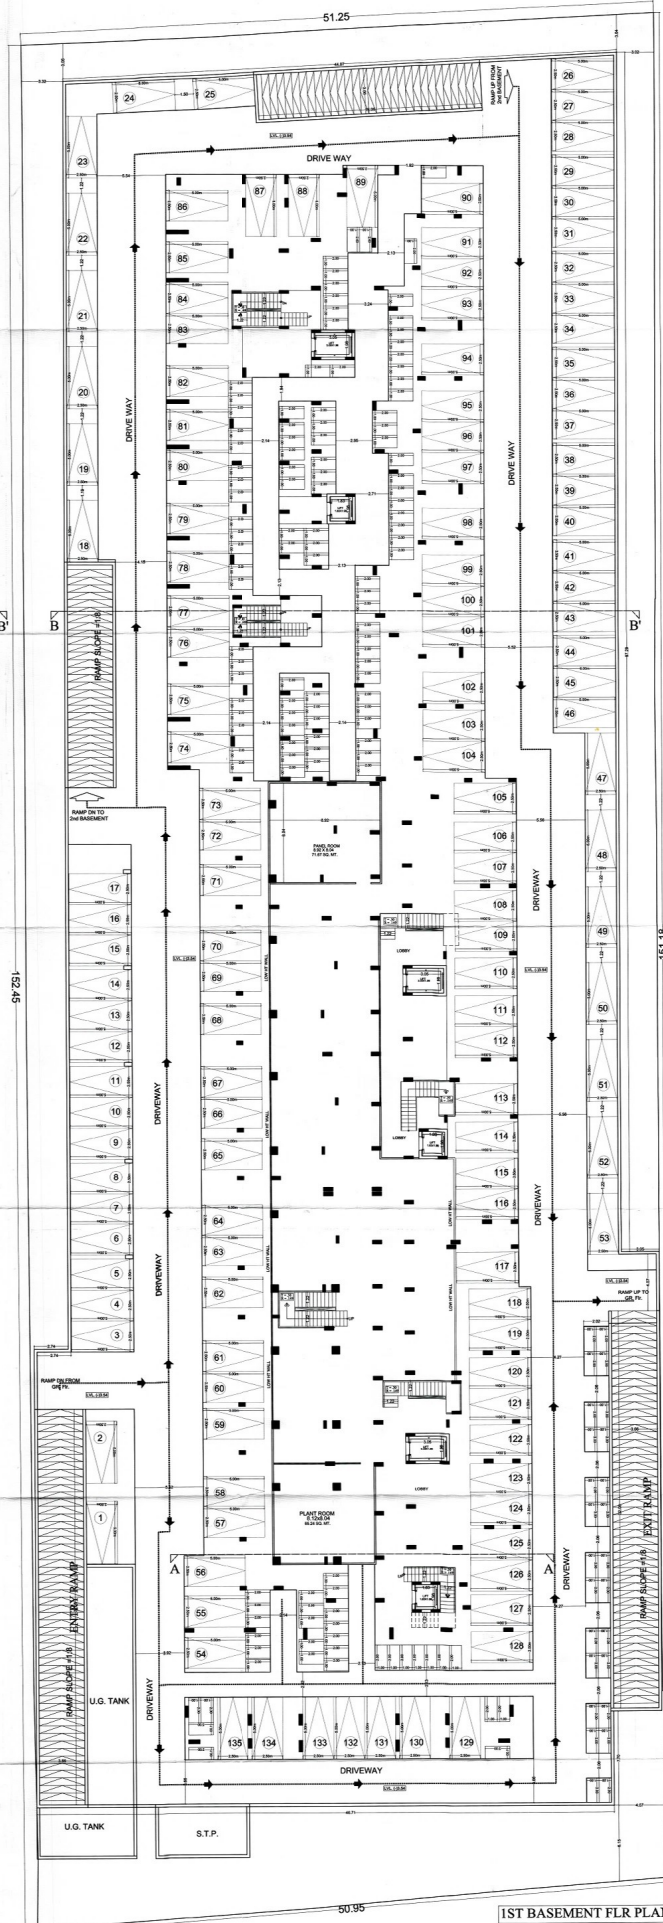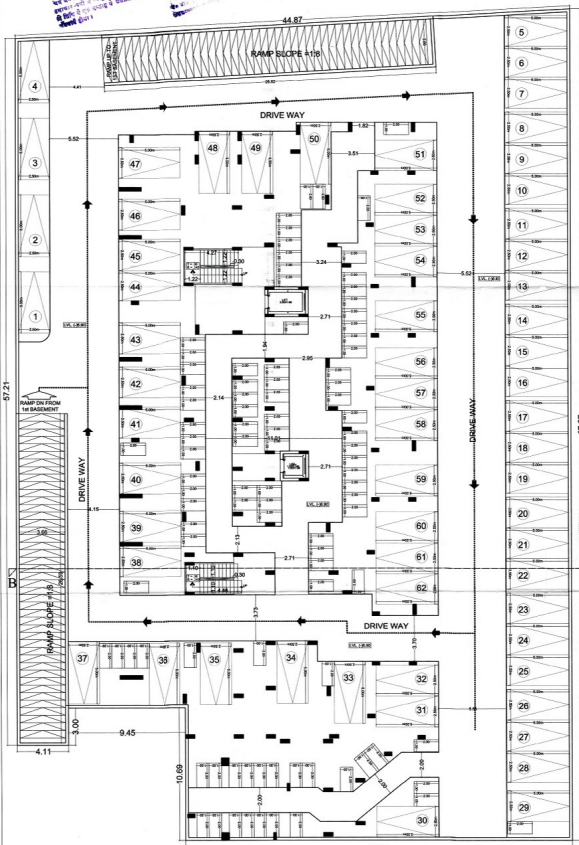

1ST BASEMENT FLR PLAN
&
2ND BASEMENT FLR PLAN

NORTH: SCALE: 1=125

DATE: 09-01-2020

PROJECT:-
PROPOSED GROUP HOUSING
AT KHASARA NO. - 183/329, 231, 233
VILLAGE KANAKPURA, JAIPUR.

ARCHITECTS:-
ANOOP GUPTA & ASSOCIATES
ARCHITECTS & INTERIOR CONSULTANTS
H. VISHW GUPTA COLONY, NEAR AIRPORT CIRCLE,
TONE ROAD, JAIPUR - 302029
TEL: 984-252084


SKIN:-
ARCHITECT

SKIN:-
OWNER

SIGN :
OWNER

For VIRAT MURLI INFRA LLC


[Signature]
Partner

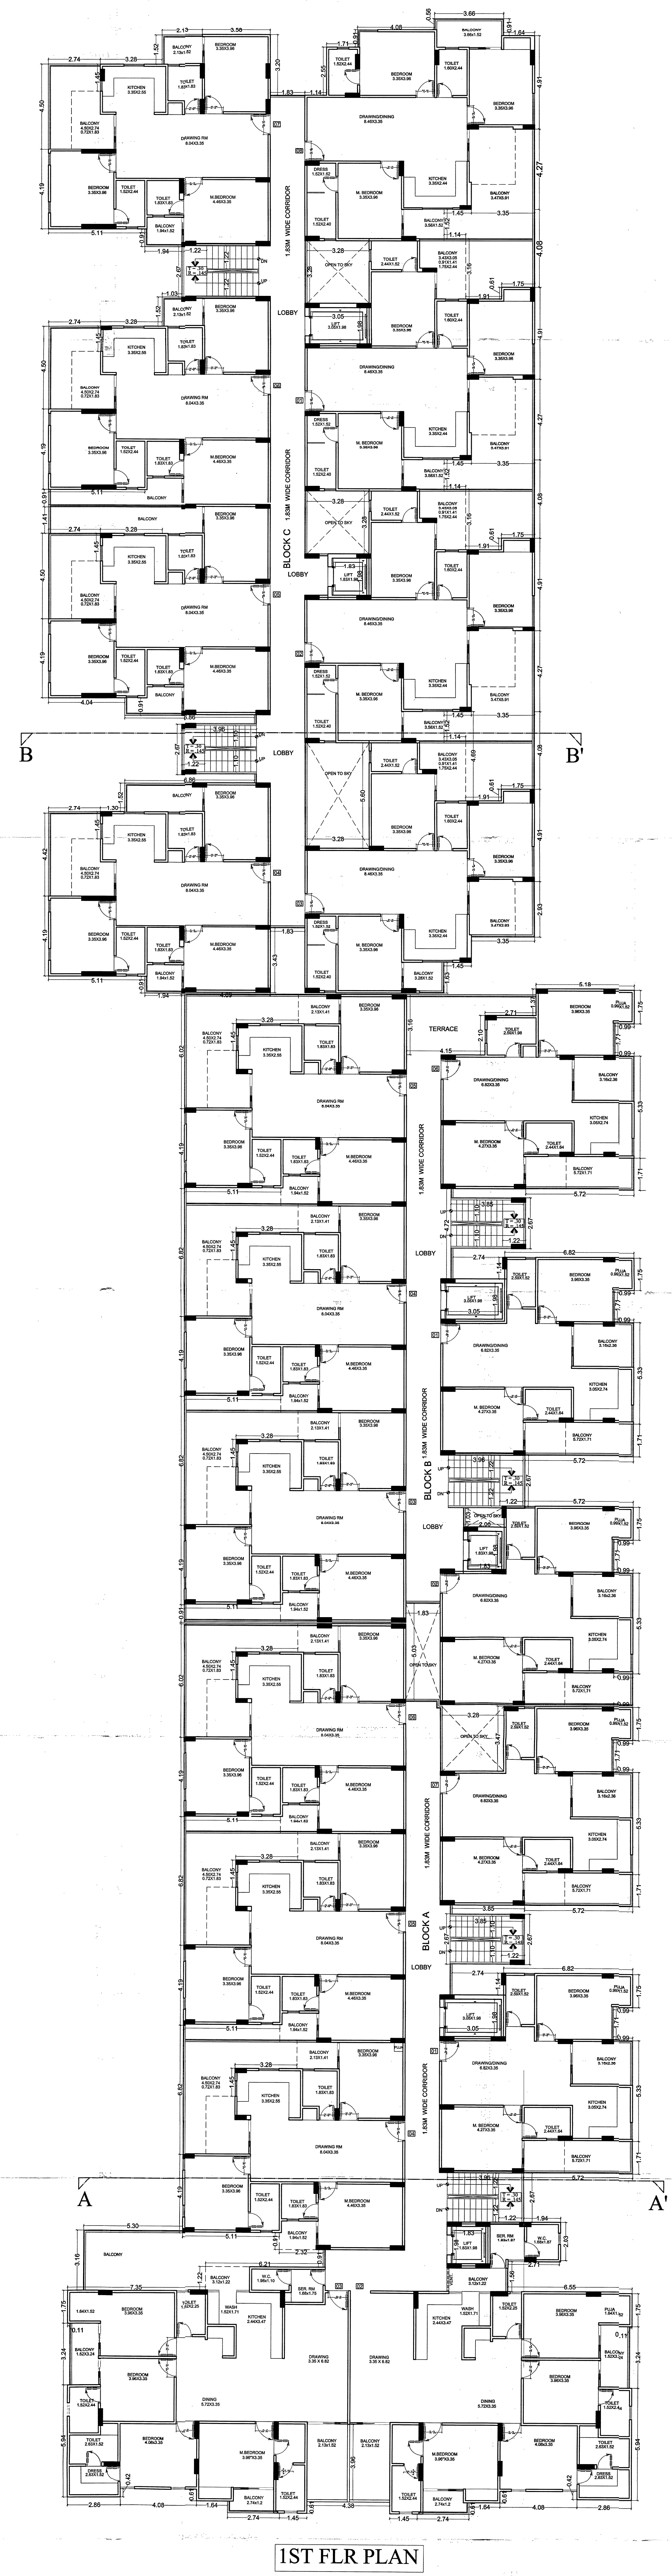


1ST FLR PLAN

SIGN :
OWNER

For VIGAT MURLI INFRA LLP

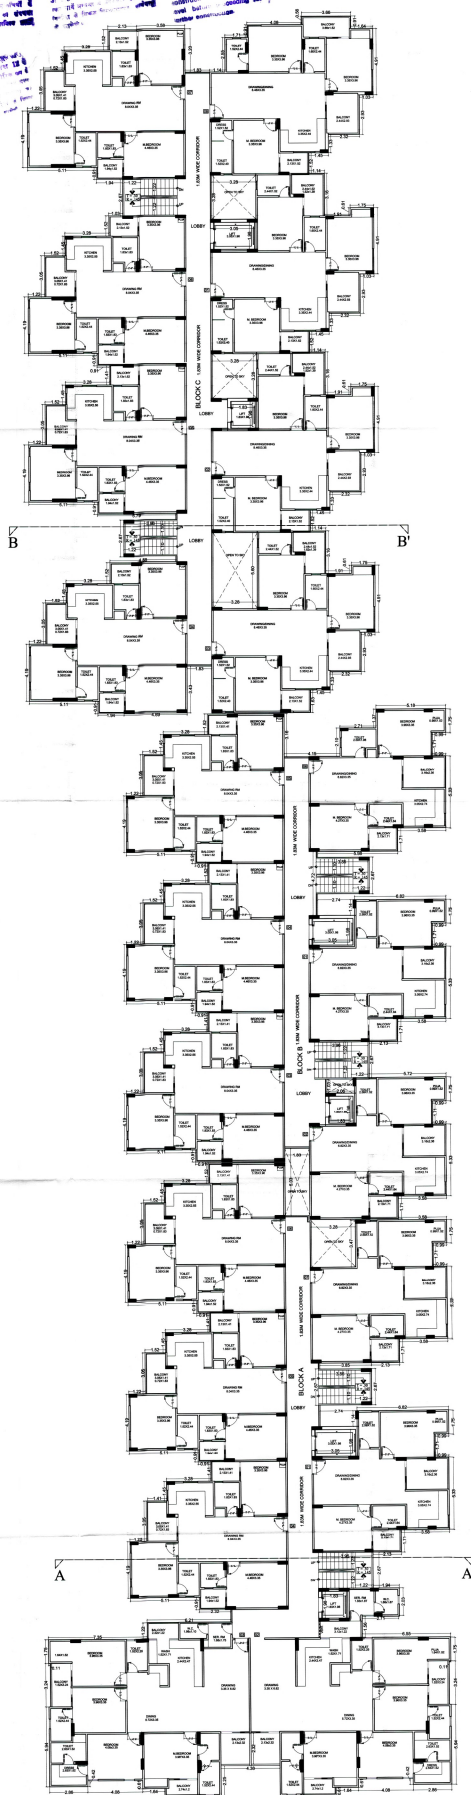

TYPICAL FLR PLAN (2ND TO 12TH)

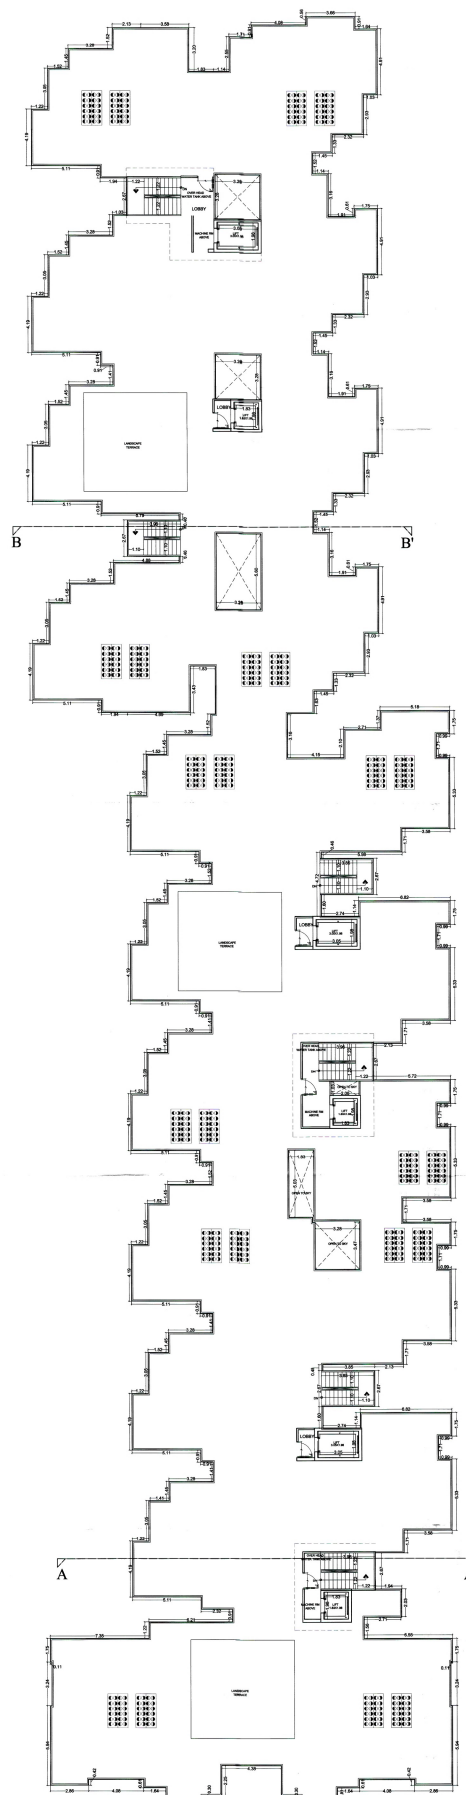


TERRACE FLR PLAN

CONSULTING ARCHITECT
ANUP GUPTA
CA/2002/13098

1. ALL DIMENSIONS ARE IN METERS
 2. ALL DIMENSIONS ARE TO FACE UNLESS SPECIFIED OTHERWISE
 3. ALL DIMENSIONS ARE TO BE MAINTAINED THROUGHOUT THE CONSTRUCTION
SHEET NO. - 6/6
 TITLE:-
 ELEVATIONS & SECTIONS
 ARCHITECT:-
 ANOOP GUPTA & ASSOCIATES
 91, VISHNU GARDEN COLONY, NEAR AIRPORT CIRCLE,
 TONK ROAD, JAIPUR - 302009
 TEL: 0141-2525048

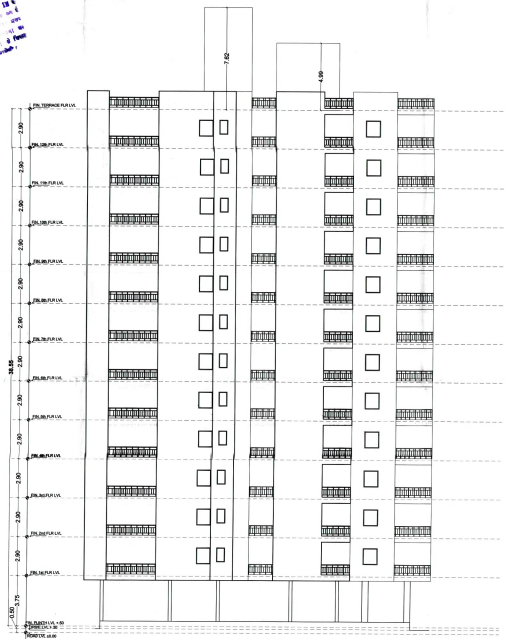


REAR SIDE ELEVATION



FRONT ELEVATION

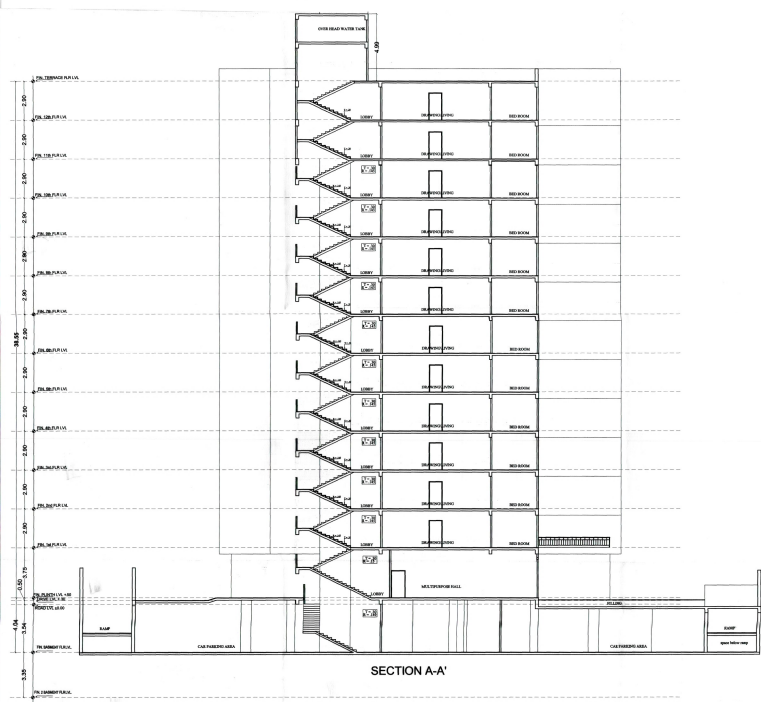

SECTION A-A'

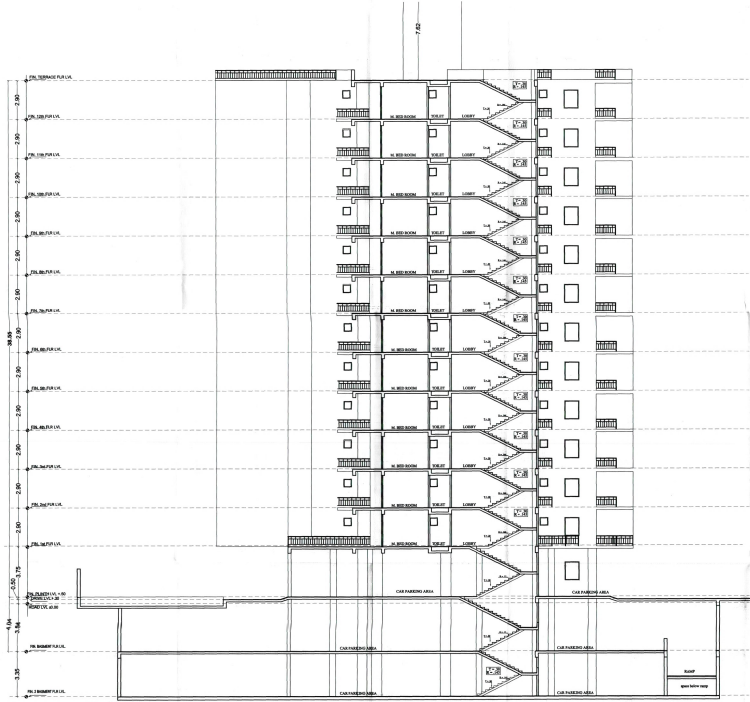

SECTION B-B'


ELEVATIONS & SECTIONS
 NORTH : SCALE : 1=125
 DATE : 09-01-2020
 PROJECT:-
 PROPOSED GROUP HOUSING
 AT KHASARA NO. - 183/329,231,233
 VILLAGE KANAKPURA, JAIPUR
 ARCHITECTS:-
 ANOOP GUPTA & ASSOCIATES
 ARCHITECTS & INTERIOR CONSULTANTS
 91, VISHNU GARDEN COLONY, NEAR AIRPORT CIRCLE,
 TONK ROAD, JAIPUR - 302009
 TEL: 0141-2525048
 SKIN : ARCHITECT
 OWNER
 For VPMR NOTARIAL
 Partner


SIGN :
OWNER

For VIKAT MURLI INFRA LLP

[Signature]
Partner

प्रमाणित प्रमाणित प्रमाणित

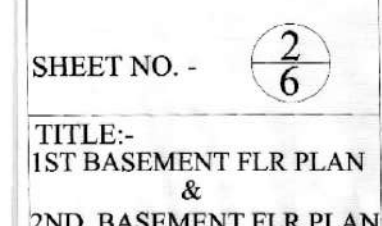

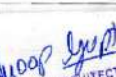
1ST BASEMENT FLR PLAN	
&	
2ND BASEMENT FLR PLAN	
NORTH :	SCALE : 1= 125
	DATE : 09-01-2020
PROJECT -	
PROPOSED GROUP HOUSING AT KHASARA NO- 183/329,231,233 VILLAGE KANAKPURA, JAIPUR	
ARCHITECTS:- ANOO GUPTA & ASSOCIATES ARCHITECTS & INTERIOR CONSULTANTS #1, VISHNU GARDEN COLONY, NEAR AIRPORT CIRCLE, TONK ROAD, JAIPUR - 302003 TEL: 0141-2592948	
SIGN :  ARCHITECT <i>Anoop Gupta</i> CONSULTING ARCHITECT ANOO GUPTA & ASSOCIATES	
SIGN : OWNER FOR VISIT ONLY REFRAIL LLP  Partner	

अनुमोदित

 अधीक्षक, विद्यार्थी विकास विभाग, जयपुर
 जयपुर दिनांक ११/०५/२०२०

46

TITLE:-
TYPICAL FLR PLAN
(2ND TO 12TH) &
TERRACE FLR PLAN

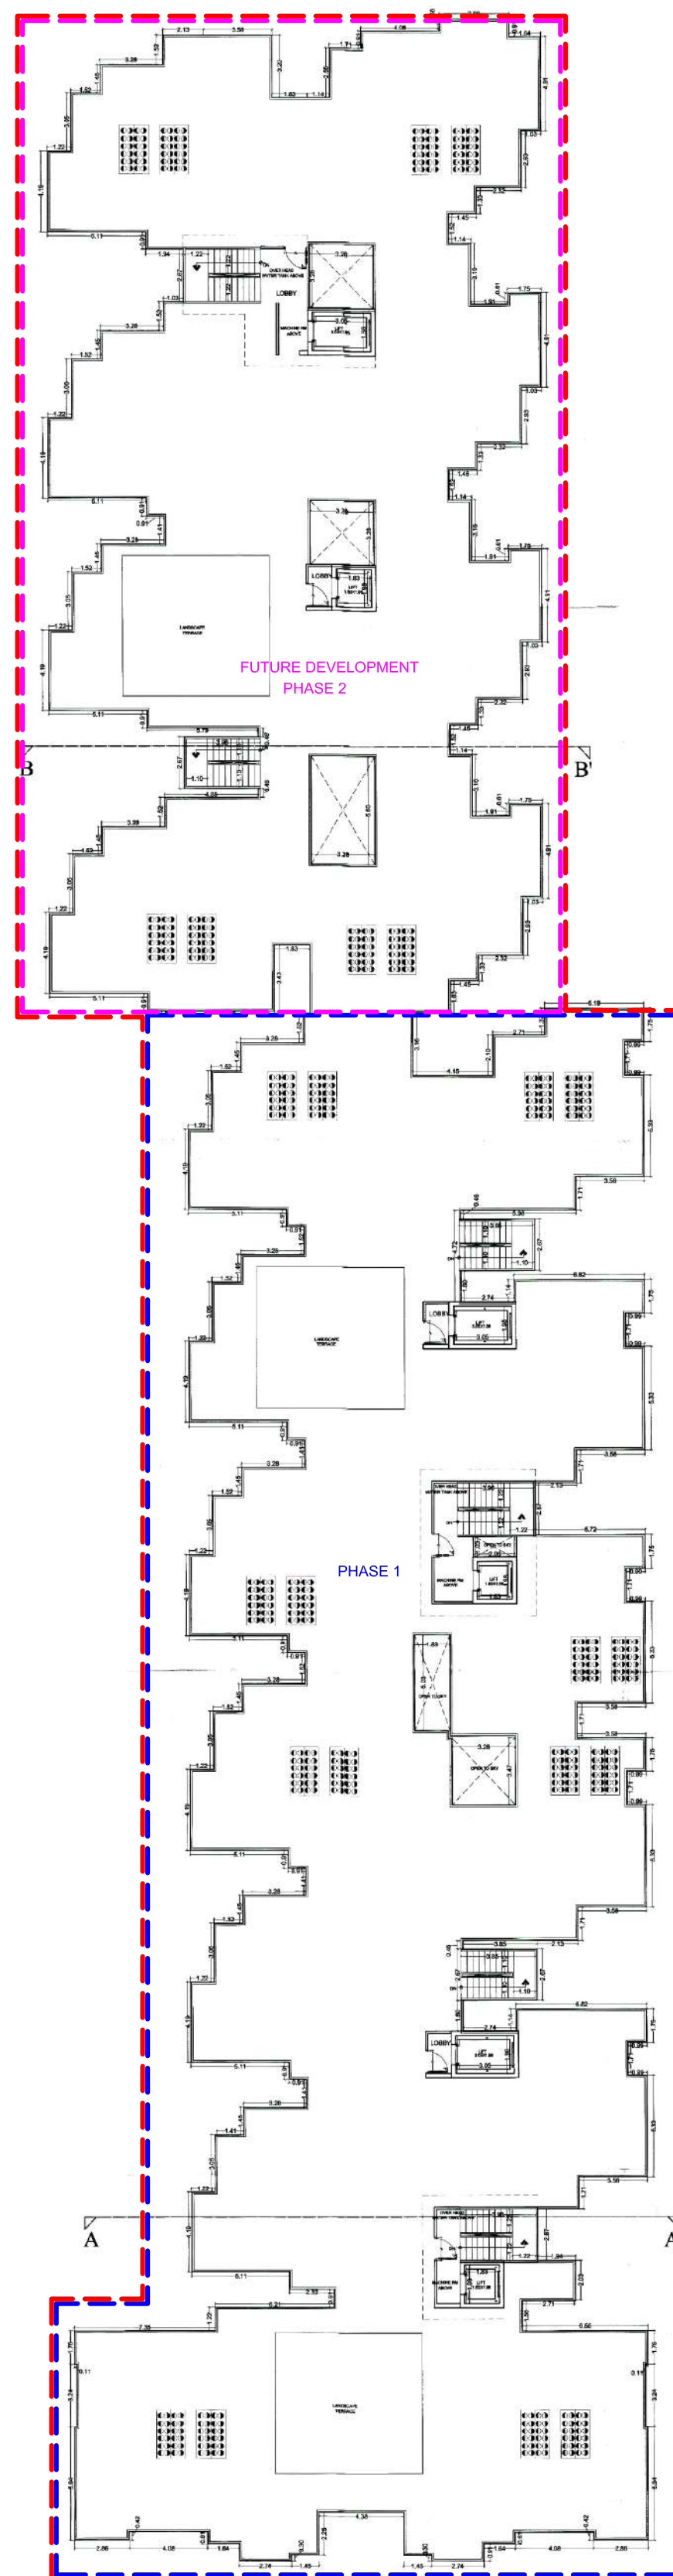

PLOT AREA - 7744.80 SQ. MTS.

PHASE 1
TOTAL AREA - 4630.64 SQ. MTS.
OPEN AREA - 1005.82 SQ. MTS.

FUTURE DEVELOPMENT
PHASE 2
TOTAL AREA - 3114.16 SQ. MTS.

TYPICAL FLR PLAN
(2ND TO 12TH) &
TERRACE FLR PLAN

NORTH :	SCALE : 1 = 125
	DATE : 09-01-2020

PROJECT:-
PROPOSED GROUP HOUSING
AT KHASARA NO.- 183/329,231,233
VILLAGE KANAKPURA, JAIPUR

ARCHITECTS:-
ANOOP GUPTA & ASSOCIATES
ARCHITECTS & INTERIOR CONSULTANTS
91, VISHNU GARDEN COLONY, NEAR AIRPORT CIRCLE,
TONEK ROAD, JAIPUR - 302029

TEL : 0141-2552948

SIGN : *Anoop Gupta*
ARCHITECT
CONSULTING ARCHITECT
ANOOP GUPTA
MOB : 9810120098

SIGN :
OWNER

For VIRAT MURLI INFRA LLP

Partner