

कार्यालय नगर विकास न्यास भिवाडी

क्रमांक 651/15

दिनांक 16/02/16

भवन निर्माण अनुमति पत्र

मै0 आशियाना हाउसिंग लि0
4 फ्लोर, आशियाना विलेज सेन्टर,
वसुन्धरा नगर, भिवाडी

विषय:- मै0 आशियाना हाउसिंग लि0, पंजीकृत कार्यालय 5-एफ एवरेस्ट, 46/सी, चौरंगी रोड कलकत्ता, पश्चिम बंगाल, अधिकृत हस्ताक्षरकर्ता श्री ओम प्रकाश सिंह पुत्र श्री केसव सिंह निवासी प्लेट नं0 बी/155, आशियाना गार्डन भिवाडी द्वारा ग्राम मिलकपुर गुर्जर तह0 तिजारा के खसरा नं0 779, 780, 782, 925/829, 781, 783, 927/844, 929/828 कुल किता 08 कुल क्षेत्रफल 48478.88 वर्ग मी0 भूमि का आवासीय प्रयोजनार्थ भवन मानचित्र स्वीकृति हेतु।


सन्दर्भ:- आपका आवेदन पत्र दिनांक 06.08.2015

आपका आवेदन दिनांक, 06.08.2015 द्वारा मै0 आशियाना हाउसिंग लि0, पंजीकृत कार्यालय 5-एफ एवरेस्ट, 46/सी, चौरंगी रोड कलकत्ता, पश्चिम बंगाल, अधिकृत हस्ताक्षरकर्ता श्री ओम प्रकाश सिंह पुत्र श्री केसव सिंह निवासी प्लेट नं0 बी/155, आशियाना गार्डन भिवाडी द्वारा ग्राम मिलकपुर गुर्जर तह0 तिजारा के खसरा नं0 779, 780, 782, 925/829, 781, 783, 927/844, 929/828 कुल किता 08 कुल क्षेत्रफल 48478.88 वर्ग मी0 भूमि का आवासीय परियोजना के भवन मानचित्र स्वीकृति हेतु प्राप्त हुए हैं। उक्त भवन मानचित्रों को भवन मानचित्र समिति की 51वी बैठक दिनांक 10.09.2015 में लिये गये निर्णयानुसार अनुमोदन कर भवन निर्माण की स्वीकृति निम्न शर्तों पर प्रदान की जाती है:-

01. यह स्वीकृति जारी होने की तिथि से 5 वर्ष तक मान्य रहेगी।
02. भवन निर्माण स्वीकृत मानचित्रों एवं भवन विनियम 2013 के प्रावधानों के अनुसार ही किया जावेगा तथा किसी भी प्रकार का उल्लंघन (डेवियेशन) नहीं किया जायेगा।
03. गलत तथ्यों पर प्राप्त की गई अथवा तथ्यों को छुपाकर प्राप्त की गई स्वीकृति स्वतः ही निरस्त मानी जाएगी एवं ऐसी निर्माण स्वीकृति प्राप्त करने के लिए आवेदनकर्ता को दोषी माना जाएगा।
04. भूखण्ड के स्वामी एवं मानचित्र तैयार करने वाले तकनीकीविज्ञ का कर्तव्य होगा कि वो यह सुनिश्चित कर ले कि स्वीकृति प्रचलित मास्टर प्लान/भवन विनियमों के अनुरूप है कोई उल्लंघन जानकारी में नहीं है, न्यास को अधिकार होगा कि किसी स्थिति में उल्लंघन की जानकारी होने पर भवन मानचित्रों की दी गयी अनुज्ञा रद्द/बदली जा सकती है तथा प्रार्थी न्यास में किसी भी प्रकार की क्षतिपूर्ति का हकदार नहीं होगा।
05. उक्त स्वीकृति के कारण यदि न्यास को किसी न्यायालय, सक्षम अधिकारी तथा नगर भूमि (अधिकतम सीमा एवं विनियम) अधिनियम के तहत नियुक्त अधिकारी के समक्ष किसी कार्यवाही में कोई भी खर्च, नुकसान, मुआवजा देना पड़े या देने योग्य हो तो प्रार्थी उनकी इस क्षति को पूर्ण करने के लिए बाध्य होगा।
06. न्यास की अभियान्त्रीकी शाखा द्वारा किये जा रहे निर्माण कार्य का निरीक्षण कर सत्यापन किया जावेगा।
07. प्लिन्थ लेवल तक निर्माण की सूचना पंजीकृत वास्तुविद से प्रमाणित कर न्यास को सूचित करेंगे। सही निर्माण पाए जाने पर आगे निर्माण जारी रखा जाएगा अन्यथा अनुमोदित/प्रस्तुत मानचित्र (13.4 व 13.5 के प्रावधान में आने वाले प्रकरणों के लिए प्रस्तुत मानचित्र) के विपरीत निर्माण पाए जाने पर संबंधित अतिक्रमण निरोधक अधिकारी द्वारा अवैध निर्माण हटवाने की कार्यवाही की जाएगी।
08. विकासकर्ता द्वारा प्लिन्थ लेवल, जी+1 एवं समय समय पर निर्माण पूर्ण होने की सूचना निर्धारित प्रपत्र में आवश्यक रूप से न्यास को दी जानी होगी, यदि इसकी अनुपालना भवन निर्माता द्वारा नहीं की जाती है तो जारी अनुज्ञा को निरस्त समझा जावेगा।
09. स्वामी प्रत्येक मंजिल के लिए स्वीकृत उपयोग के अनुसार ही उपयोग में लेगा।
10. स्वामी तकनीकीविज्ञ के निरीक्षण में निर्माण कार्य करवायेगा। यदि तकनीकीविज्ञ को बदला जाता है तो इसकी सूचना 48 घण्टे के अन्दर यथोचित प्रमाण-पत्र में न्यास को देनी होगी।

11. स्वीकृत मानचित्र मौके पर, निर्माण पूर्ण होने तक उपयुक्त स्थान पर बोर्ड लगाकर उस पर स्पष्ट रूप से दर्शाने होंगे।
12. भवन परिसर में ही आगुन्तकों की पार्किंग करवाई जावे तथा आगुन्तकों हेतु निःशुल्क वाहन पार्किंग का बोर्ड लगवाया जावे मानचित्र में दर्शाये अनुसार भू-तल का उपयोग किया जावेगा।
13. भवन विनियम, 2013 के प्रावधानों के अनुरूप विकासकर्ता द्वारा भूकम्परोधी प्रावधान, अग्नि शमन हेतु प्रावधानों, विकलांगों हेतु प्रावधान आदि की पालना सुनिश्चित किया जाना आवश्यक होगा।
14. भवन का कुर्सी तल, सड़क के तल से न्यूनतम 0.5 मी० रखा जाना सुनिश्चित किया जाये।
15. भूखण्डों पर निर्माण हेतु स्वीकृत साईट प्लान के अनुरूप सैट बेक्स व अन्य प्रावधान सुनिश्चित करने होंगे।
16. भूखण्ड में आन्तरिक विकास यथा जल वितरण, ड्रेनेज, सीवरेज, सेपटिक टैंक, विद्युत वितरण, सड़कें, टेलीफोन लाईन, वर्षा जल संग्रहण, संरचना, स्नानाघर, तथा रसोई के अवशिष्ट जल के शुद्धिकरण हेतु रिसाईकिलिंग की व्यवस्था आदि का प्रावधान किये जाने की समस्त जिम्मेदारी विकासकर्ता की होगी।
17. प्रस्तुत भवन मानचित्रों में वर्षा जल संग्रहण संरचना एवं इस से संबंधित प्रावधानों की पालना भवन विनियम 2013 के प्रावधान अनुसार इसकी पालना सुनिश्चित कि जावे।
18. अधिवास प्रमाण-पत्र भवन निर्मित होने के उपरान्त आवश्यक रूप से लिया जाना होगा।
19. पार्किंग का प्रावधान भवन विनियम, 2013 के अनुरूप रखा जाना होगा एवं वाहनो के घूमने/पार्क करने हेतु आवश्यक प्रावधान आवेदक/वास्तुविद द्वारा सुनिश्चित करने होंगे।
20. भवन विनियम 2013 एवं नेशनल बिल्डिंग कोड के प्रावधान के अनुसार अग्नि शमन सुरक्षा संबंधित समस्त प्रावधान सुनिश्चित करने होंगे तथा इस बाबत संबंधित विभाग से अग्नि शमन सुरक्षा प्रमाण पत्र प्राप्त करना होगा।
21. EWS हेतु 68 एवं LIG हेतु 31 कुल 99 प्लेट प्रस्तावित किये गये हैं। इन ईकाईयो का निष्पादन न्यास द्वारा राज्य सरकार के परिपत्र दिनांक 02.05.2012 एवं एफोडेबल हाउसिंग पॉलिसी व परिपत्रों / दिशा निर्देशों के अनुसार किया जावेगा।
22. भवन विनियम 2013 एवं नेशनल बिल्डिंग कोड, आई.एस. कोड के प्रावधान के अनुसार भूकम्परोधी भवन हेतु भवन संरचना डिजाइन की जाकर तदनुसार संरचनात्मक सुरक्षित भवन बनाये जाने की जिम्मेदारी आवेदक एवं वास्तुविद की होगी।
23. भवन मानचित्र जारी करने के उपरान्त अन्य शुल्क/ बकाया राशि न्यास द्वारा मांग की जाती है तो विकासकर्ता द्वारा वह राशि न्यास कोष में जमा करानी होगी।
24. भवन विनियमों में उल्लेखित अन्य सम्बन्धित प्रावधानों की पालना विकासकर्ता द्वारा की जायेगी।
25. विकासकर्ता द्वारा नेशनल ग्रीन ट्रिब्युनल कोर्ट द्वारा समय समय पर जारी गाइडलाइन्स की पालना सुनिश्चित की जावेगी।

ऊपर वर्णित शर्तों एवं भवन विनियम के प्रावधानों के तहत अन्य कोई संबंधित शर्त का पालना नहीं होने पर भवन अनुज्ञा रद्द मानी जायेगी।

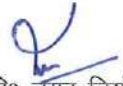
वरि० नगर नियोजक
नगर विकास न्यास,
भिवाडी

संलग्न:- भवन मानचित्र (1.1)

क्रमांक: आयोजना/

दिनांक:

प्रतिलिपि अधिशाषी अभियन्ता, नगर विकास न्यास, भिवाडी को सूचनार्थ एवं आवश्यक कार्यवाही हेतु।

वरि० नगर नियोजक
नगर विकास न्यास,
भिवाडी

भिवाडी इन्टीग्रेटेड विकास प्राधिकरण, भिवाडी

क्रमांक / बीडा / आयोजना / 2629/20

दिनांक 28/10/20

संशोधित भवन निर्माण अनुमति पत्र

मै0 आशियाना हाउसिंग लि0
4 फ्लोर, आशियाना विलेज सेन्टर,
वसुन्धरा नगर, भिवाडी


विषय:- मै0 आशियाना हाउसिंग लि0, पंजीकृत कार्यालय 5-एफ एवरेस्ट, 46/सी, चौरंगी रोड कलकत्ता, पश्चिम बंगाल, अधिकृत हस्ताक्षरकर्ता श्री ओम प्रकाश सिंह पुत्र श्री केसव सिंह निवासी फ्लेट नं0 बी/155, आशियाना गार्डन भिवाडी द्वारा ग्राम मिलकपुर गुर्जर तह0 तिजारा के खसरा नं0 779, 780, 782, 925/829, 781, 783, 927/844, 929/828 कुल किता 08 कुल क्षेत्रफल 48478.88 वर्ग मी0 भूमि का आवासीय प्रयोजनार्थ के स्वीकृत मानचित्रों की समयावधि बढ़ाने की स्वीकृति बाबत।

सन्दर्भ:- आपका आवेदन पत्र दिनांक 03.09.2020

उपरोक्त विषयान्तर्गत लेख है कि आपका आवेदन दिनांक 03.09.2020 के अनुसार ग्राम मिलकपुर गुर्जर तह0 तिजारा के खसरा नं0 779, 780, 782, 925/829, 781, 783, 927/844, 929/828 कुल किता 08 कुल क्षेत्रफल 48478.88 वर्ग मी0 है पर मूल भवन निर्माण स्वीकृति न्यास भिवाडी के पत्र क्रमांक 651/16 दिनांक 16.02.2016 को जारी की गई थी। बीडा भिवाडी द्वारा उपरोक्त प्रकरण को बीडा की भवन मानचित्र समिति की 09 बैठक दिनांक 11.09.2020 के एजेण्डा नं0 03 में पूर्व में जारी मूल भवन निर्माण स्वीकृति में समिति द्वारा पत्रावली, एजेण्डा बिन्दुओं तथा भवन मानचित्रों का अवलोकन कर सर्वसम्मति से विचार विमर्श कर प्रकरण में स्वीकृत मानचित्रों की समयावधि एकीकृत भवन विनियम के नियमानुसार राशि जमा कराकर 2 वर्ष बढ़ाये जाने तथा नगरीय विकास विभाग के आदेश दिनांक 15.05.2020 के अनुसार 6 माह अर्थात् कुल 2.5 वर्ष की समयावृद्धि करने का निर्णय निम्न शर्तों के साथ स्वीकृत किये जाने का निर्णय लिया गया:-

01. यह स्वीकृति आवंटन पत्र/लीजडीड में उल्लेखित शर्तों के अध्याधीन, अधिकतम मूल स्वीकृति 16.02.2016 से 5 वर्ष हेतु मान्य थी जो कि अब 2 वर्ष 6 माह बढ़ाकर 7 वर्ष 6 माह के लिए मान्य होगी।
02. भवन निर्माण स्वीकृत मानचित्रों एवं ग्रेटर भवन विनियम 2013 के प्रावधानों के अनुसार ही किया जावेगा तथा किसी भी प्रकार का उल्लंघन (डेवियेशन) नहीं किया जायेगा।
03. मूल भवन निर्माण अनुमति पत्र दिनांक 16.02.2016 की समस्त शर्त यथावत मान्य होगी।

ऊपर वर्णित शर्तों एवं भवन विनियम के प्रावधानों के तहत अन्य कोई संबंधित शर्त का पालन नहीं होने पर भवन निर्माण अनुज्ञा रद्द मानी जायेगी।

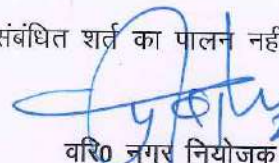
वरि0 नगर नियोजक
बीडा भिवाडी
28/X/2020

क्रमांक: आयोजना/

दिनांक:

प्रतिलिपि:- अधिशाषी अभियन्ता, बीडा भिवाडी को सूचनार्थ एवं आवश्यक कार्यवाही हेतु।

वरि0 नगर नियोजक
बीडा भिवाडी

क्रमांक : 2294/22

दिनांक : 08/04/22

भवन निर्माण अनुमति पत्र

मै0 आशियाना हा0 लि0
ग्राम मिलकपुर तहसील तिजारा
जिला अलवर (राज0)

विषय:- मै0 आशियाना हाउसिंग लि0 ग्राम मिलकपुर गुर्जर त0 तिजारा के ख0न0 779 से 783, 925/829, 930/828, 927/844 व 929/828, कुल किता 09 में पार्ट अ एवं पार्ट ब क्षेत्रफल (48478.88+3526.26)- 52005.14 वर्ग मी0 भूमि के आवासीय (ग्रुप हाउसिंग) परियोजना के संशोधित भवन मानचित्रों की स्वीकृति बाबत।

संदर्भ:- आपका आवेदन पत्र दिनांक 12.11.2021।

उपरोक्त विषयान्तर्गत लेख है कि आपका आवेदन पत्र दिनांक 12.11.2021 के अनुसार मै0 आशियाना हाउसिंग लि0 ग्राम मिलकपुर गुर्जर त0 तिजारा के ख0न0 779 से 783, 925/829, 930/828, 927/844 व 929/828, कुल किता 09 में पार्ट अ एवं पार्ट ब क्षेत्रफल (48478.88+3526.26)- 52005.14 वर्ग मी0 भूमि के आवासीय (ग्रुप हाउसिंग) भूखण्ड पर संशोधित एवं नवीन स्वीकृति बाबत बीडा भिवाड़ी की 15वीं बैठक भवन मानचित्र समिति दिनांक 15.03.2022 के एजेण्डा 05 पर लिये गये निर्णय के अनुसार मानचित्र निम्न शर्तों के साथ स्वीकृत किये जाते हैं-

1. यह स्वीकृति आवंटन पत्र/लीजडीड में उल्लेखित शर्तों के अध्याधीन, पार्ट ब (क्षेत्रफल- 3526.26 वर्ग मीटर) हेतु अधिकतम 7वर्ष हेतु मान्य होगी तथा पार्ट अ हेतु मूल स्वीकृति से 10 वर्ष 6 माह हेतु मान्य होगी। (बीडा के स्वीकृति पत्र क्रमांक 2629/20 दिनांक 28.10.2020 एवं मॉडल भवन विनियम 2021 के प्रावधान संख्या 8.11 एवं उद्योग विभाग के पत्र दिनांक 08.12.2021 तथा नगरीय विकास विभाग द्वारा कोविड-19 के मध्यनजर जारी आदेश दिनांक 12.05.2021 के अनुसार)
2. भवन निर्माण स्वीकृत मानचित्रों एवं बीडा मॉडल भवन विनियम 2021 के प्रावधानों के अनुसार ही किया जावेगा तथा किसी भी प्रकार का उल्लंघन (डेवियेशन) नहीं किया जायेगा।
3. गलत तथ्यों पर प्राप्त की गई अथवा तथ्यों को छुपाकर प्राप्त की गई स्वीकृति स्वतः ही निरस्त मानी जाएगी एवं ऐसी निर्माण स्वीकृति प्राप्त करने के लिए आवेदनकर्ता को दोषी माना जाएगा।
4. भूखण्ड के स्वामी एवं मानचित्र तैयार करने वाले तकनीकीविज्ञ का कर्तव्य होगा कि वह यह सुनिश्चित करें कि निर्माण प्रचलित भवन विनियम एवं स्वीकृत मानचित्रों के अनुरूप है। बीडा भिवाड़ी को अधिकार होगा कि किसी स्थिति में उल्लंघन की जानकारी होने पर भवन मानचित्रों की दी गई अनुज्ञेय रद्द /बदली जा सकती है तथा प्रार्थी बीडा भिवाड़ी में किसी भी प्रकार की क्षतिपूर्ती का हकदार नहीं होगा।
5. उक्त स्वीकृति के कारण यदि बीडा भिवाड़ी को किसी न्यायालय, सक्षम अधिकारी तथा नगर भूमि (अधिकतम सीमा एवं विनियम) अधिनियम के तहत नियुक्त अधिकारी के समक्ष किसी कार्यवाही में कोई भी खर्चा, नुकसान, मुआवजा देना पड़े या देने योग्य हो तो प्रार्थी उनकी इस क्षति को पूर्ण करने के लिए बाध्य होगा।
6. विकासकर्ता द्वारा प्लिन्थ लेवल, एस+1 एवं समय-समय पर निर्माण पूर्ण होने की सूचना निर्धारित प्रपत्र में आवश्यक रूप से बीडा भिवाड़ी को दी जानी होगी, यदि इसकी अनुपालना भवन निर्माण निर्माता द्वारा नहीं की जाती है तो जारी अनुज्ञा को निरस्त समझा जाएगा।
7. स्वामी प्रत्येक मंजिल के लिए स्वीकृत ईकाई एवं स्वीकृत उपयोग के अनुसार ही उपयोग में लेगा।
8. स्वामी तकनीकीविज्ञ के निरीक्षण में निर्माण कार्य करवाएगा। यदि तकनीकीविज्ञ को बदला जाता है तो इसकी सूचना 48 घंटे के अन्दर यथोचित प्रमाण पत्र में बीडा भिवाड़ी को देनी होगी।
9. भवन हेतु आन्तरिक विकास यथा जल विस्तारण, ड्रेनेज, सिवरेज, विद्युत वितरण, सड़कें, टेलीफोन लाईन, वर्षा जल, संग्रहण, संरचना, स्नानाघर, तथा रसोई के अवशिष्ट जल के शुद्धिकरण हेतु रिसाईकिलिंग की व्यवस्था आदि की समस्त जिम्मेदारी विकासकर्ता की होगी।
10. प्रस्तुत भवन मानचित्रों में वर्षा जल संग्रहण संरचना एवं इस से संबन्धित प्रावधानों की पालना बीडा मॉडल भवन विनियम 2021 के प्रावधान अनुसार सुनिश्चित की जावे।
11. परियोजना के मानचित्र स्वीकृति/संशोधन बाबत रियल एस्टेट रेग्युलेशन अधिनियम के अनुसार (रेरा) में रजिस्ट्रेशन किया जाना होगा।
12. पार्किंग का प्रावधान बीडा मॉडल भवन विनियम 2021 के अनुरूप रखा जाना होगा एवं वाहनो के घूमने/पार्क करने हेतु आवश्यक प्रावधान आवेदक/वास्तुविद द्वारा सुनिश्चित करने होंगे मानचित्र में दर्शाये गये अनुसार पार्किंग हेतु ही आरक्षित रखा जावेगा। इस में किसी प्रकार का निर्माण नहीं किया जावेगा।
13. भवन मानचित्र जारी करने के उपरान्त अन्य शुल्क/ बकाया राशि बीडा भिवाड़ी द्वारा मांग की जाती है तो विकासकर्ता द्वारा वह राशि बीडा भिवाड़ी कोष में जमा करानी होगी।

6

14. भूखण्ड में प्रत्येक 50 वर्ग मीटर क्षेत्रफल के लिए कम से कम 2 वृक्ष के अनुपात में बड़े वृक्ष जो 6 मीटर या इससे अधिक उँचाई ग्रहण कर सकते हों, लगाने होंगे।
15. बीडा की अभियांत्रिकी शाखा द्वारा किये जा रहे निर्माण का निरक्षण कर सत्यापन किया जावेगा।
16. कम्पलीशन एवं अधिवास प्रमाण पत्र भवन निर्मित होने के उपरान्त आवश्यक रूप से प्राप्त करना होगा।
17. बीडा मॉडल भवन विनियम 2021 एवं नेशनल बिल्डिंग कोड, आई.एस. कोड के प्रावधान के अनुसार भूकम्परोधी भवन हेतु भवन संरचना डिजाईन की जाकर तदनुसार संरचनात्मक सुशिक्षित भवन बनाये जाने की जिम्मेदारी आवेदक एवं वास्तुविद की होगी।
18. निर्माण कार्य में कोमन एपलुएन्ट टीट्रमेन्ट प्लान्ट (सी.ई.टी.पी) से निकलने वाले परिशोधित जल का उपयोग किया जावेगा।
19. पर्यावरण विभाग द्वारा जारी मानदण्डों के अनुसार ऐसे निर्माण जिनके लिये पर्यावरणीय स्वीकृति अनिवार्य है, बाबत सम्बन्धित विभाग से स्वीकृति प्राप्त की जाकर ही निर्माण किया जा सकेगा। तदनुसार प्रावधान रखने को जिम्मेदारी आवेदक की होगी।
20. भवन में विद्युत आवश्यकताओं की पूर्ति हेतु संबन्धित विद्युत वितरण एजेंसी के प्रावधानों के अनुसार प्रावधान रखे जाने एवं ऐनर्जी कन्जर्वेशन बिल्डिंग कोड एवं समय-समयपर संशोधित प्रावधानों की अनुपालना की जिम्मेदारी निर्माणकर्ता की होगी।
21. भूखण्ड पर भवन का निर्माण, भवन निर्माण स्वीकृति दिनांक से तीन वर्ष में निर्माण कार्य प्रारंभ कर निर्धारित अवधि में स्वीकृत मानचित्र अनुसार कुल प्रस्तावित निर्माण क्षेत्र का कम से कम 50 प्रतिशत क्षेत्र निर्माण किया जाना होगा।
22. आवेदक द्वारा भवन निर्माण प्रारम्भ करते समय एक सूचना पट्ट मौके पर लगाया जाएगा जिसमें उप सचिव/अतिरिक्त मुख्य कार्यकारी अधिकारी, बीडा व प्रवर्तन अधिकारी, बीडा आदि के टेलीफोन नम्बर इत्यादि अंकित किए जाने होंगे व अनुमोदित मानचित्र की सूचना व अनुमोदन की शर्तें अंकित की जाएगी। निर्माण के दौरान अनुमोदित मानचित्र की एक प्रति आवश्यक रूप से निर्माणकर्ता द्वारा मौके पर रखी जाएगी।
23. राज्य सरकार द्वारा जारी आदेश एवं बीडा मॉडल भवन विनियम 2021 एवं एन.बी.सी के अनुसार अग्निशमन के प्रावधान रखे जाने होंगे। अग्निशमन शूल्क व श्रम उपकर राज्य सरकार द्वारा जारी आदेश अनुसार जमा करवाया जावेगा एवं इस संबंध में जारी आदेश के अनुरूप आवश्यक कार्यवाही किया जाना सुनिश्चित किया जावे। भूखण्ड पर निर्माण कार्य प्रारम्भ करने से पूर्व प्रोविजनल अग्नि अनापत्ति प्राप्त कर आवेदक द्वारा बीडा भिवाडी में प्रस्तुत करगा सुनिश्चित किया जावेगा तथा अधिवास प्रमाण पत्र से पूर्व अग्निशमन अनापत्ति प्राप्त करनी होगी।
24. भवनों में बीडा मॉडल भवन विनियम 2021 के उल्लेखानुसार रेनवाटर हार्वेस्टिंग स्ट्रक्चर का निर्माण, एन.बी.सी के प्रावधानानुसार अग्निशसन एवं भूकम्प रोधी प्रावधान, ग्रीनरी एवं प्लान्टेशन की उपलब्धता, सुनिश्चित की जिम्मेदारी विकासकर्ता एवं वास्तुविद की होगी।
25. पार्क, खुले क्षेत्र, सामुदायिक एवं सार्वजनिक सुविधाएं एवं सड़को हेतु आरक्षित क्षेत्र एवं आगन्तुक हेतु रखा गया पार्किंग क्षेत्र संबन्धित स्थानीय आर.डब्ल्यू.ए को संचालन एवं रख रखाव के लिए समर्पित करना होगा।
26. भवन विनियमों के अपेक्षाओं के अनुरूप भवन निर्माण करने की जिम्मेदारी भवन निर्माण अनुज्ञाधारी की होगी। भवन निर्माण के समय निर्माण सामग्री से आस पास के भवनों के निवासकर्ताओं का किसी प्रकार की असुविधा न हो, इस हेतु भवन निर्माण के दौरान चारों ओर पर्दे लगावाये जावें।
27. पर्यावरण संरक्षण हेतु बीडा मॉडल भवन विनियम 2021 के अनुसार रेन वॉटर हार्वेस्टिंग, अपशिष्ट जल का शुद्धिकरण एवं रिसाइकलिंग वृक्षरोपण, सॉलिड वेस्ट डिस्पोजल, सौर ऊर्जा संयंत्र का समुचित एवं नियमानुसार प्रावधान/निर्माण किया जावेगा।

ऊपर वर्णित शर्तों एवं भवन विनियम के प्रावधानों के तहत अन्य कोई संबन्धित शर्त का पालना नहीं होने पर भवन अनुज्ञा रद्द मानी जायेगी।



उप नगर नियोजक

भिवाडी इन्टीग्रेटेड विकास प्राधिकरण,
(बीडा) भिवाडी।

संलग्न:- भवन मानचित्र

क्रमांक: आयोजना/

प्रतिलिपि अधिशाषी अभियन्ता, बीडा भिवाडी इन्टीग्रेटेड विकास प्राधिकरण भिवाडी को सूचनार्थ एवं आवश्यक कार्यवाही हेतु।

दिनांक:



उप नगर नियोजक

भिवाडी इन्टीग्रेटेड विकास प्राधिकरण,
(बीडा) भिवाडी।

अनुमोदित

भारत सरकार की अधिसूचना दिनांक 14.09.2006 की पालना में राज्य सरकार के परिपत्र दिनांक 04.02.2011 के अनुसार 20000 वर्ग मीटर से अधिक का निर्माण प्राप्त करने से पूर्व "पर्यावरण प्रभाव पत्र" अनापत्ति प्रमाण पत्र आवेदक द्वारा प्राप्त किया जाना अनिवार्य होगा।

विद्युत सेवा में नलकारी एवं, जल, मल, निकास अग्नि शमन आदि सेवाएँ नेशनल बिल्डिंग कोड ऑफ इण्डिया के प्रावधानों/भवन विनियमों के प्रावधानों/सम्बन्धित विभागों के प्रावधानों को सुनिश्चित किया जावेगा।

इस मानचित्र का अनुमोदन किसी भी भाति प्रथमगत भूमि/भूखण्ड के प्राति स्वामित्व का प्रमाण-पत्र नहीं माना जावेगा। और न ही इससे किसी के स्वामित्व सम्बन्धी अधिकारी ही प्रभावित होंगे।

Applicants Should get the construction checked at plinth level before proceeding for further construction.

Adequate Light and Ventilation to be Provided as per N.B.C. Norms.

Rain Water Harvesting Unit Shall be Provided as per Rules.

सीर ऊर्जा से पानी गरम करने का नियमानुसार प्रावधान किया जावे।

पार्किंग क्षेत्र का उपयोग केवल पार्किंग हेतु किया जावेगा।

THESE PLANS ARE VALID ONLY UPTO 07 YEAR FROM DATE OF ISSUUE "जारी किये गये अनुमोदित मान-चित्रों में दर्शाये गये भवन निर्माण की संरचना (STRUCTURE) का दायित्व प्राप्ती का ही होगा।"

SHEET NO.02

PARKING SITE PLAN

PLOT DETAILS

Proposed Residential Group housing Ashiana Tarang at Bhiwadi , ASHIANA HOUSING Ltd. Khasra No. 779,780,781,782, 783 , 925 / 829 ,927 / 844, 929 / 828 ,930/828 Village :- Milakpur Gujar Teh. Tijara ; Dist Alwar Rajasthan

Project: Ashiana Tarang at Bhiwadi

Developer: ASHIANA HOUSING LTD

Sheet title: PARKING ARRANGEMENT SITE PLAN

SCALE- 1:750



For ASHIANA HOUSING LTD
Authorised Signatory

BISWAJIT SENGUPTA
B. Arch, FIA, AIID
Regd. Architect : CA/75/886

SIGNATURE OF AUTHORITY SIGNATURE OF ARCHITECT

In Compliance of Layout Plan/
Building Plan Committee Dt.15/3/22
One Set of Building Plans
Approved is issued Along-With
Letter No. 22794/22 Dt. 27/4/22

उप निरीक्षक
नगर प्रमाण

Manish Boda
सहायक नगर नियोजक
मि.इ.मि.प्रा.

उप नगर नियोजक
बीड़ा, भिवाडी

PARKING FACILITY AREA CHART (ALREADY SANCTION)

(Block- A1,B2,A6&E)

1. TOTAL F A R AREA CONSUMED 27985.548 Sq.M
2. TOTAL RESIDENTIAL F A R AREA = 27,795.76 Sq.M
Say = 371
3. TOTAL RESIDENTIAL F A R AREA = 27,795.76 Sq.M
a) ECU @ 75 SqM Required = 27,795.76 / 75 = 370.61
4. 25% VISITOR PARKING = 93 Nos
5. TOTAL ECU REQ. (371 + 93) = 464
SAY = 464 nos Req.
6. TOTAL COMMERCIAL F A R AREA = 189.78
a) ECU @ 50 SqM Required = 189.78 / 50 = 3.79
SAY = 4 nos
7. Total ECU Req(464+4)= 468.00 Nos

PARKING FACILITY AREA CHART (PROPOSED FOR B A R)

(Block-C2,B3,B4,B5,B6,B10,B11&VILLA)

1. TOTAL B A R AREA CONSUMED = 60039.90 Sq.M
2. TOTAL RESIDENTIAL B A R AREA = 60,039.90 Sq.M
a) ECU @ 115 SqM Required = 60,039.90 / 115 = 522.08
Say = 522
3. 10% visitor parking (522) = 52.20 say 52 nos
4. TOTAL ECU REQ. (522+52) = 574 Nos Req.

TOTAL CAR PARKING REQ (F A R + B A R) 468+574= 1042.00 NOS

PARKING PROVIDED

75% of car req (1042)= 783 Nos

25% of scooter req (1042)= 261 x 3 = 783 nos

Car Parking Provided

Ground floor still carparking provi.= 303 nos

Ground floor open carparking provi.= 592 nos

Total carparking prov. = 895 nos

Scooter parking provided

Ground floor Still Scooter parking Provi= 333

Ground floor open Scooter parking Provided = 120

Total scooter parking prov. = 453

Say Total ECU Provided (895 + 151.) = 1046

open carparking provided

P1--- (7 x 3) . . . = 21 Nos	P13---(11 x 1) . . . = 11 Nos
P2---(21 x 1) . . . = 21 Nos	P14---(29 x 1) . . . = 29 Nos
P3---(22 x 2) . . . = 44 Nos	P15---(14 x 1) . . . = 14 Nos
P4---(5 x 1) . . . = 05 Nos	P16---(17 x 1) . . . = 17 Nos
P5---(3 x 2) . . . = 06 Nos	P17---(25 x 1) . . . = 25 Nos
P6---(1 x 2) . . . = 02 Nos	P18---(24 x 1) . . . = 24 Nos
P7---(81 x 1) . . . = 81 Nos	P19---(09 x 1) . . . = 09 Nos
P8---(6 x 2) . . . = 12 Nos	P20---(35 x 2) . . . = 70 Nos
P9---(16 x 3) . . . = 48 Nos	P21---(8 x 1) . . . = 08 Nos
P10---(26 x 2) . . . = 52 Nos	P22---(51 x 1) . . . = 51 Nos
P11---(2 x 4) . . . = 08 Nos	P23---(4 x 1) . . . = 04 Nos
P12---(21 x 1) . . . = 21 Nos	P24---(10 x 1) . . . = 10 Nos

total (P1 to P24) = 592Nos

Covered Car Parking Provided

Block -B1,B8,B9(34 x 3)--- = 102
Block - B7 (23 x 1)--- = 23
Block - B3 to B5 (36 x 3)--- = 108
Block - C2 CORE (22 x 1)--- = 22
Block - B6,B10,B11(16 x 3)--- = 48
TOTAL Covered = 303 Nos
Total Car parking
Open+covered (592 +303) = 895 Nos

open Scooter parking provided

SP1--- (24 x 1) . . . = 24 Nos
SP2---(26 x 1) . . . = 26 Nos
SP3---(49 x 1) . . . = 49Nos
SP4---(6 x 1) . . . = 6 Nos
SP5---(15 x 1) . . . = 15nos
TOTAL = 120 Nos

Covered Scooter Parking Provided

Block -B1,B8,B9(56 x 3)--- = 168
Block - B7 (3 x 1)--- = 03
Block - B3 to B5 (30 x 3)--- = 90
Block - B6,B10,B11(24 x 3)--- = 72
TOTAL Covered = 333 Nos
Total Scootetr parking
Open+covered (120 +333) =453Nos
ECU 453 /3 = 151

अनुमोदित

भारत सरकार की अधिसूचना दिनांक 14.09.2006 की पालना में राज्य सरकार के परिचय दिव्य 04.02.2011 के अनुसार 20000 वर्ग मीटर से अधिक का निर्माण प्रारम्भ करने से पूर्व "पर्यावरण प्रभाव पत्र" अनापत्ति प्रमाण पत्र आवेदक द्वारा प्राप्त किया जाना अनिवार्य होगा।

विद्युत सेवा में नलकारी एव, जल, मल, निकास अति शक्ति आदि सेवाएँ नेशनल बिल्डिंग कोड ऑफ इण्डिया के प्रावधानों/मवन विनियमों के प्रावधानों/सम्बन्धित विभागों के प्रावधानों को सुनिश्चित किया जाएगा।

Applicants Should get the construction checked at plinth level before proceeding for further construction.

Adequate Light and Ventilation to be Provided as per N.B.C. Norms.

Rain Water Harvesting Unit Shall be Provided as per Rules.

इस मानचित्र का अनुमोदन किसी भी भाति प्रशानगत भूमि/मूलाड के प्राति स्वायत्त का प्रमाण-पत्र नहीं माना जायेगा। और न ही इससे किसी के स्वायत्त सम्पत्ती अधिकारी ही प्रभावित होंगे।

BLOCK -B6,B10,B11 (BALCONY 1.80 M)													
FLOOR NAME	G.B.U.A.	CHAISA	CUT OUT	B.U.A.	PRE STAB	LIFT	BAR	BALCONY/VERAND	STAIR	CORRIDOR	STORE	TOTAL	F.A.R.
BASEMENT	92.62	0.00	4.18	88.44	0.00	0.00	88.44	0.00	0.00	0.00	0.00	171.24	0
1ST FLOOR	585.26	32.32	3.10	549.84	14.11	8.86	526.87	59.43	0.00	13.75	24.71	92.89	428.98
2nd FLOOR	585.26	32.32	3.10	549.84	14.11	8.86	526.87	59.43	0.00	13.75	24.71	92.89	428.98
3rd FLOOR	585.26	32.32	3.10	549.84	14.11	8.86	526.87	59.43	0.00	13.75	24.71	92.89	428.98
4th FLOOR	585.26	32.32	3.10	549.84	14.11	8.86	526.87	59.43	0.00	13.75	24.71	92.89	428.98
5th FLOOR	585.26	32.32	3.10	549.84	14.11	8.86	526.87	59.43	0.00	13.75	24.71	92.89	428.98
6th FLOOR	585.26	32.32	3.10	549.84	14.11	8.86	526.87	59.43	0.00	13.75	24.71	92.89	428.98
7th FLOOR	585.26	32.32	3.10	549.84	14.11	8.86	526.87	59.43	0.00	13.75	24.71	92.89	428.98
8th FLOOR	585.26	32.32	3.10	549.84	14.11	8.86	526.87	59.43	0.00	13.75	24.71	92.89	428.98
9th FLOOR	585.26	32.32	3.10	549.84	14.11	8.86	526.87	59.43	0.00	13.75	24.71	92.89	428.98
10th FLOOR	585.26	32.32	3.10	549.84	14.11	8.86	526.87	59.43	0.00	13.75	24.71	92.89	428.98
11th FLOOR	585.26	32.32	3.10	549.84	14.11	8.86	526.87	59.43	0.00	13.75	24.71	92.89	428.98
12th FLOOR	585.26	32.32	3.10	549.84	14.11	8.86	526.87	59.43	0.00	13.75	24.71	92.89	428.98
TERRACE	71.40											71.40	0
TOTAL	7187.14	387.84	41.38	6686.52	169.32	106.32	6430.58	713.16	0.00	140.00	296.52	11744.68	5162.66

सीर केज से पानी गरम करने का नियमानुसार प्राधान किया जावे।


पार्किंग क्षेत्र का उपयोग केवल पार्किंग हेतु किया जावेगा।

पेड़ लगाओ-हरीटायली बढ़ोओ

THESE PLANS ARE VALID ONLY UPTO 07 YEAR FROM DATE OF ISSUE


"जारी किये गये अनुमोदित मान-चित्रों में दर्शाये गये मवन निर्माण की संरचना (STRUCTURE) का दायित्व प्रार्थी का ही होगा।"

ELEVATION - 1

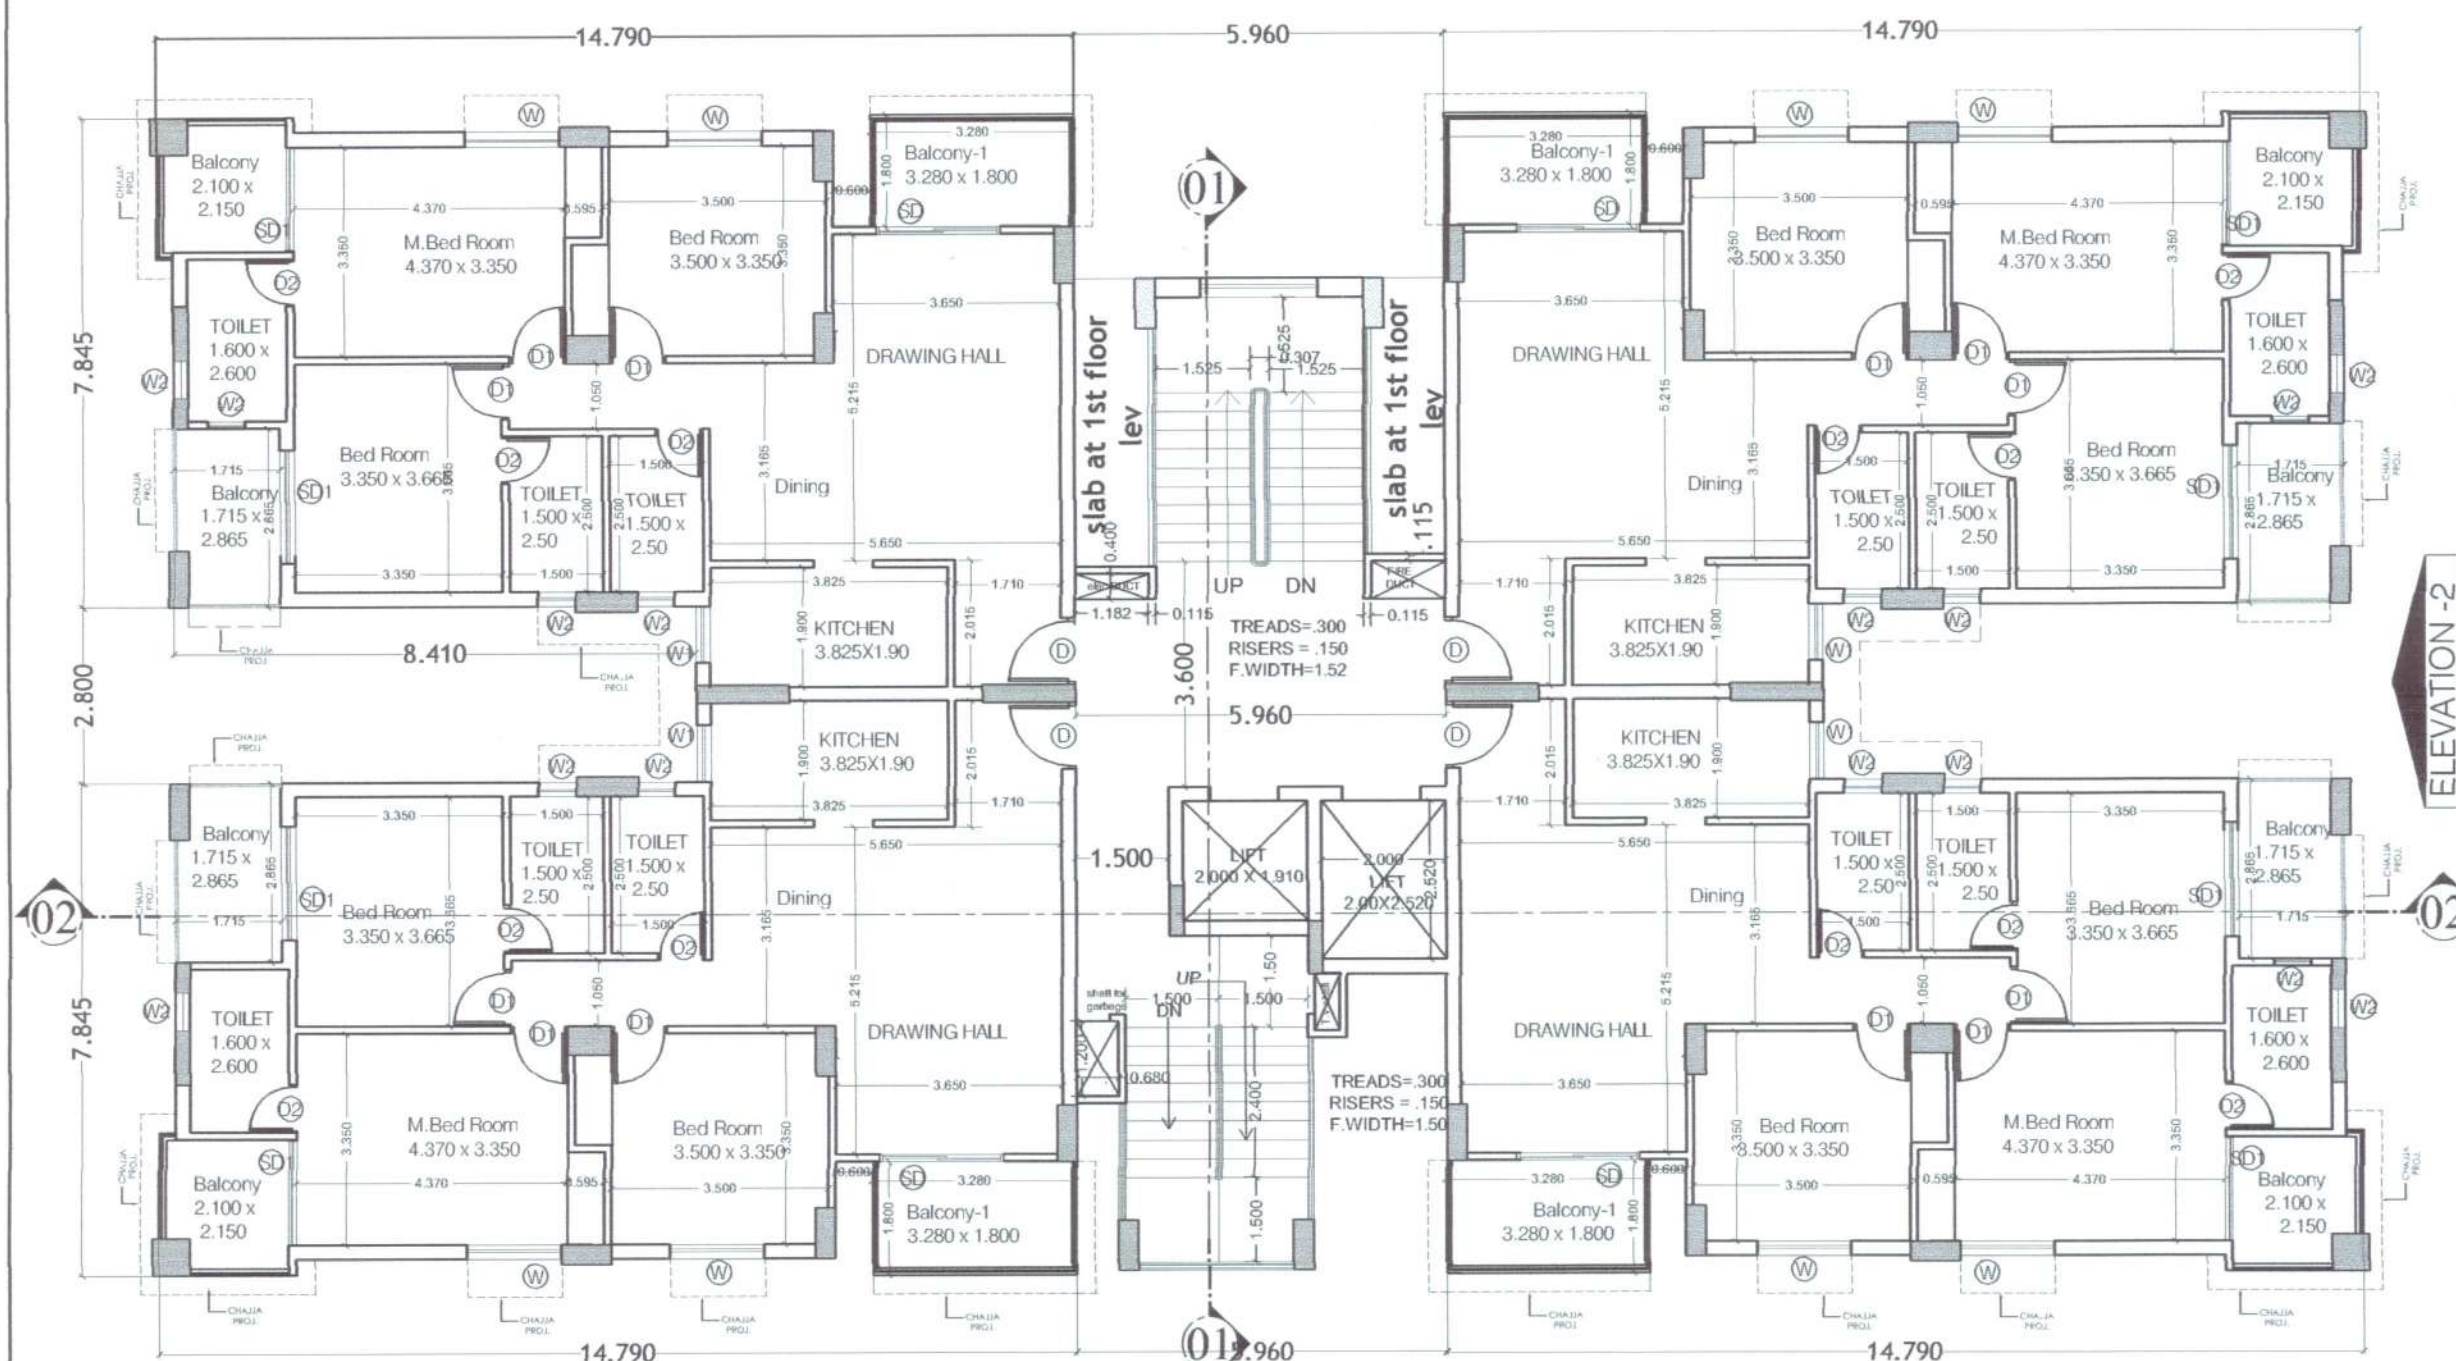


TYPICAL FLOOR PLAN
1ST TO 12TH FLOOR

ELEVATION - 2

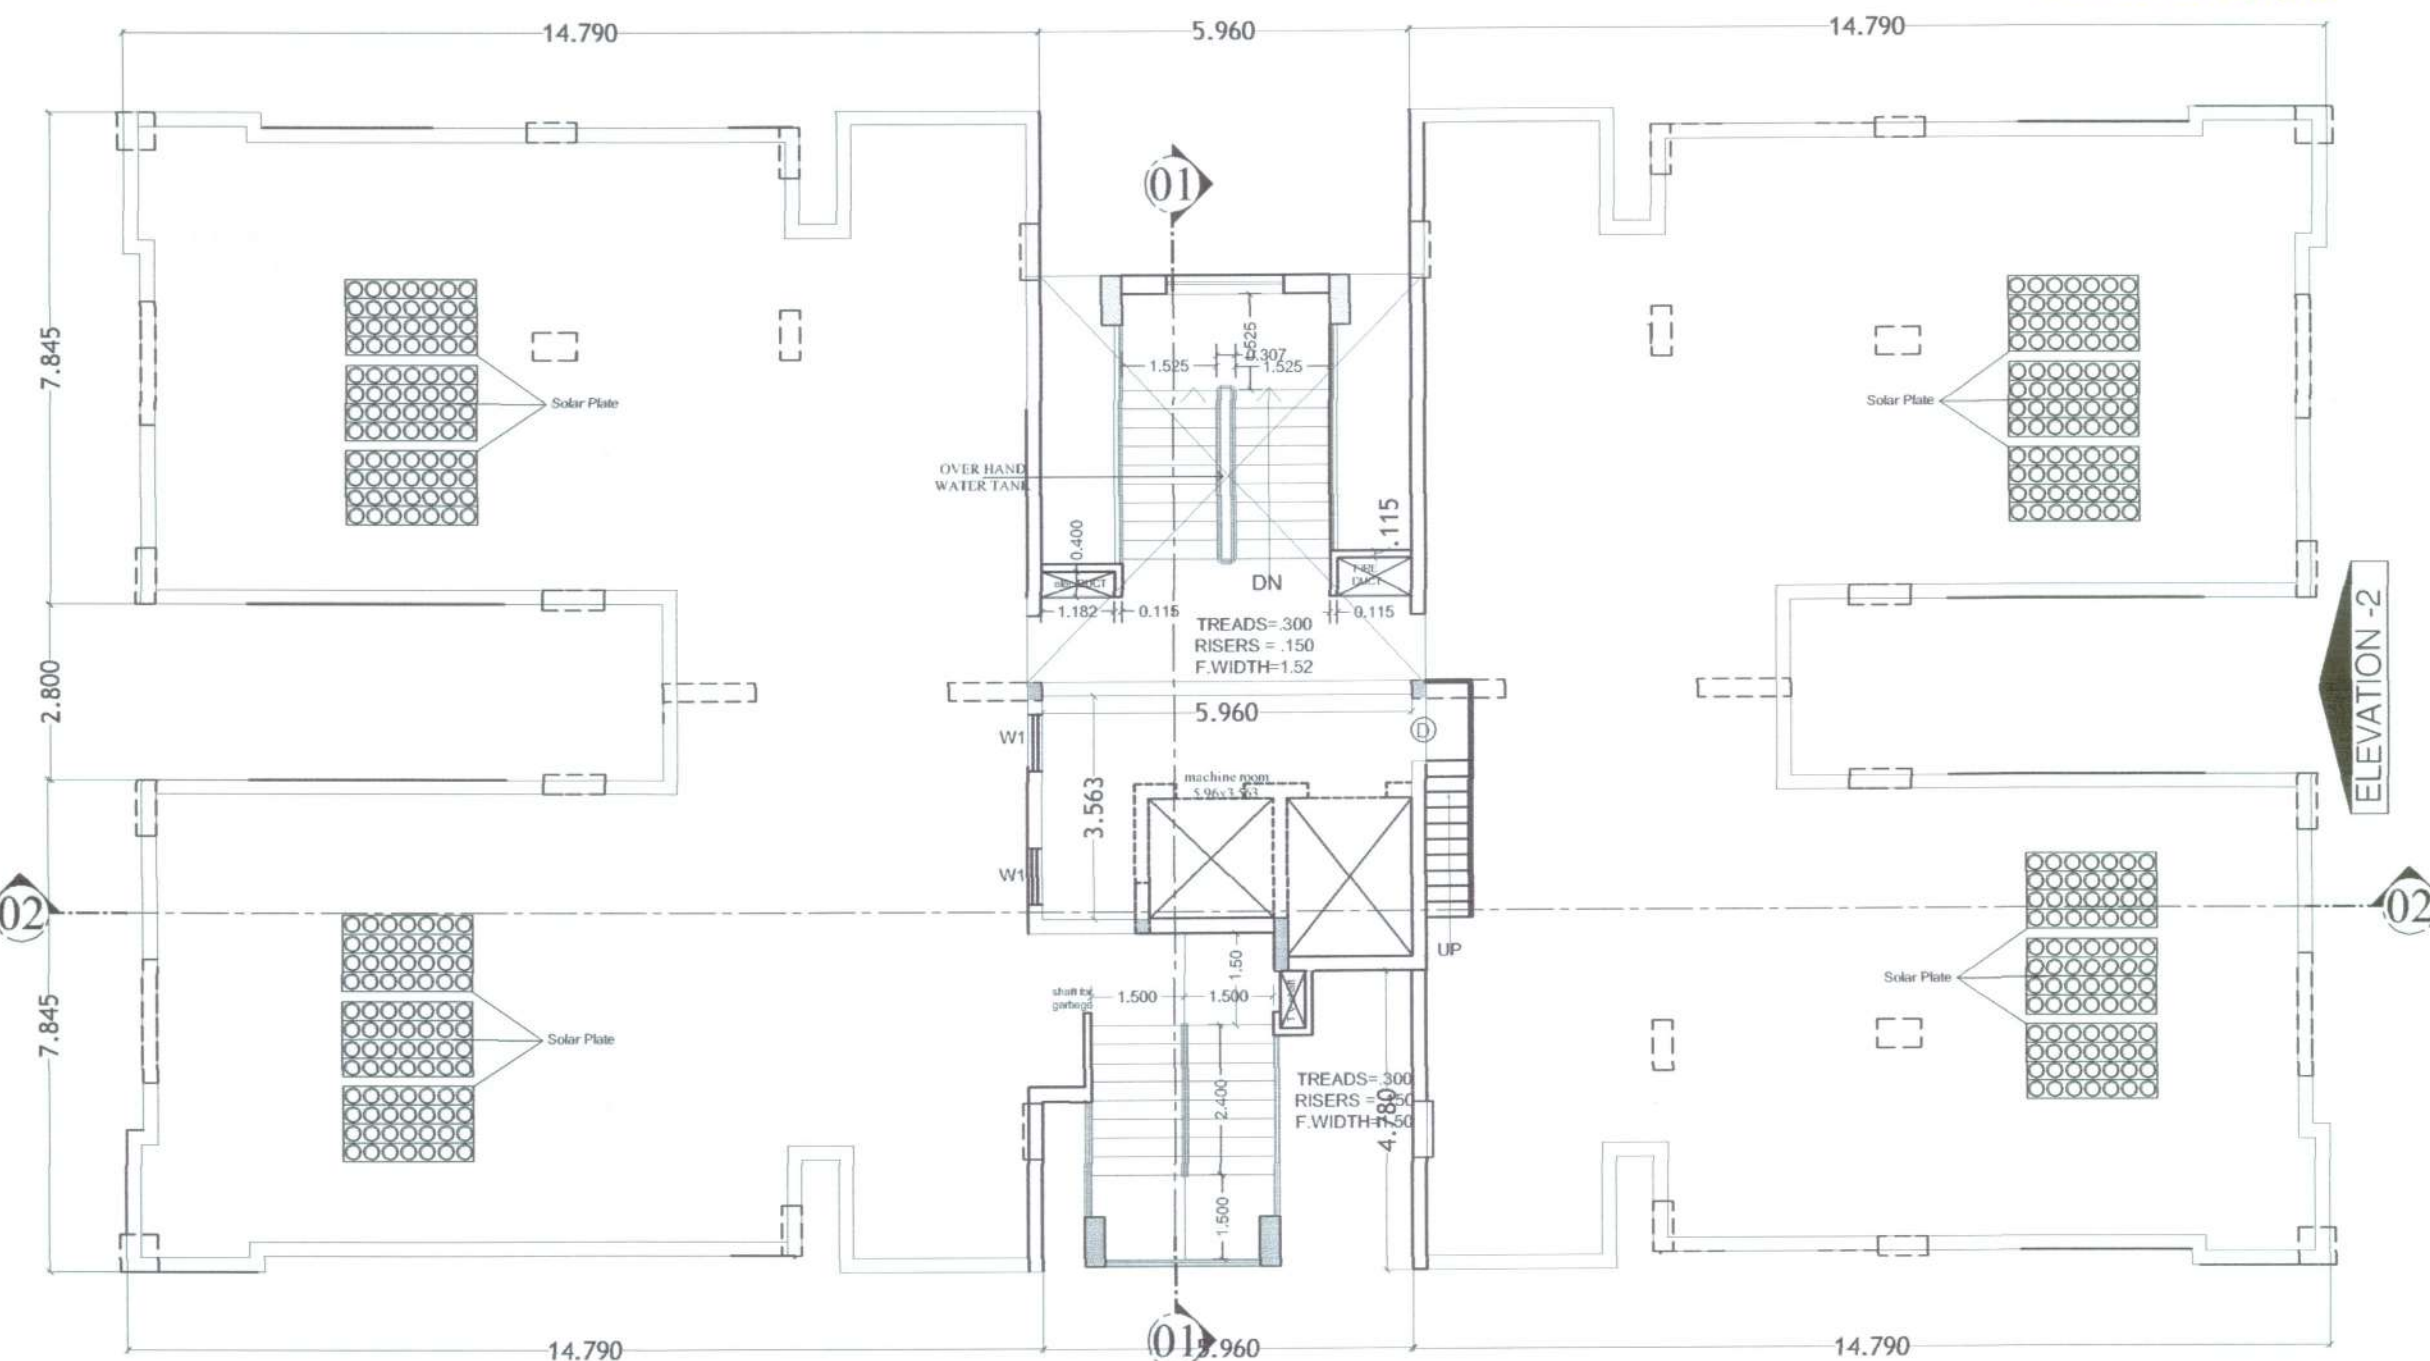


TERRACE FLOOR PLAN

ELEVATION - 1

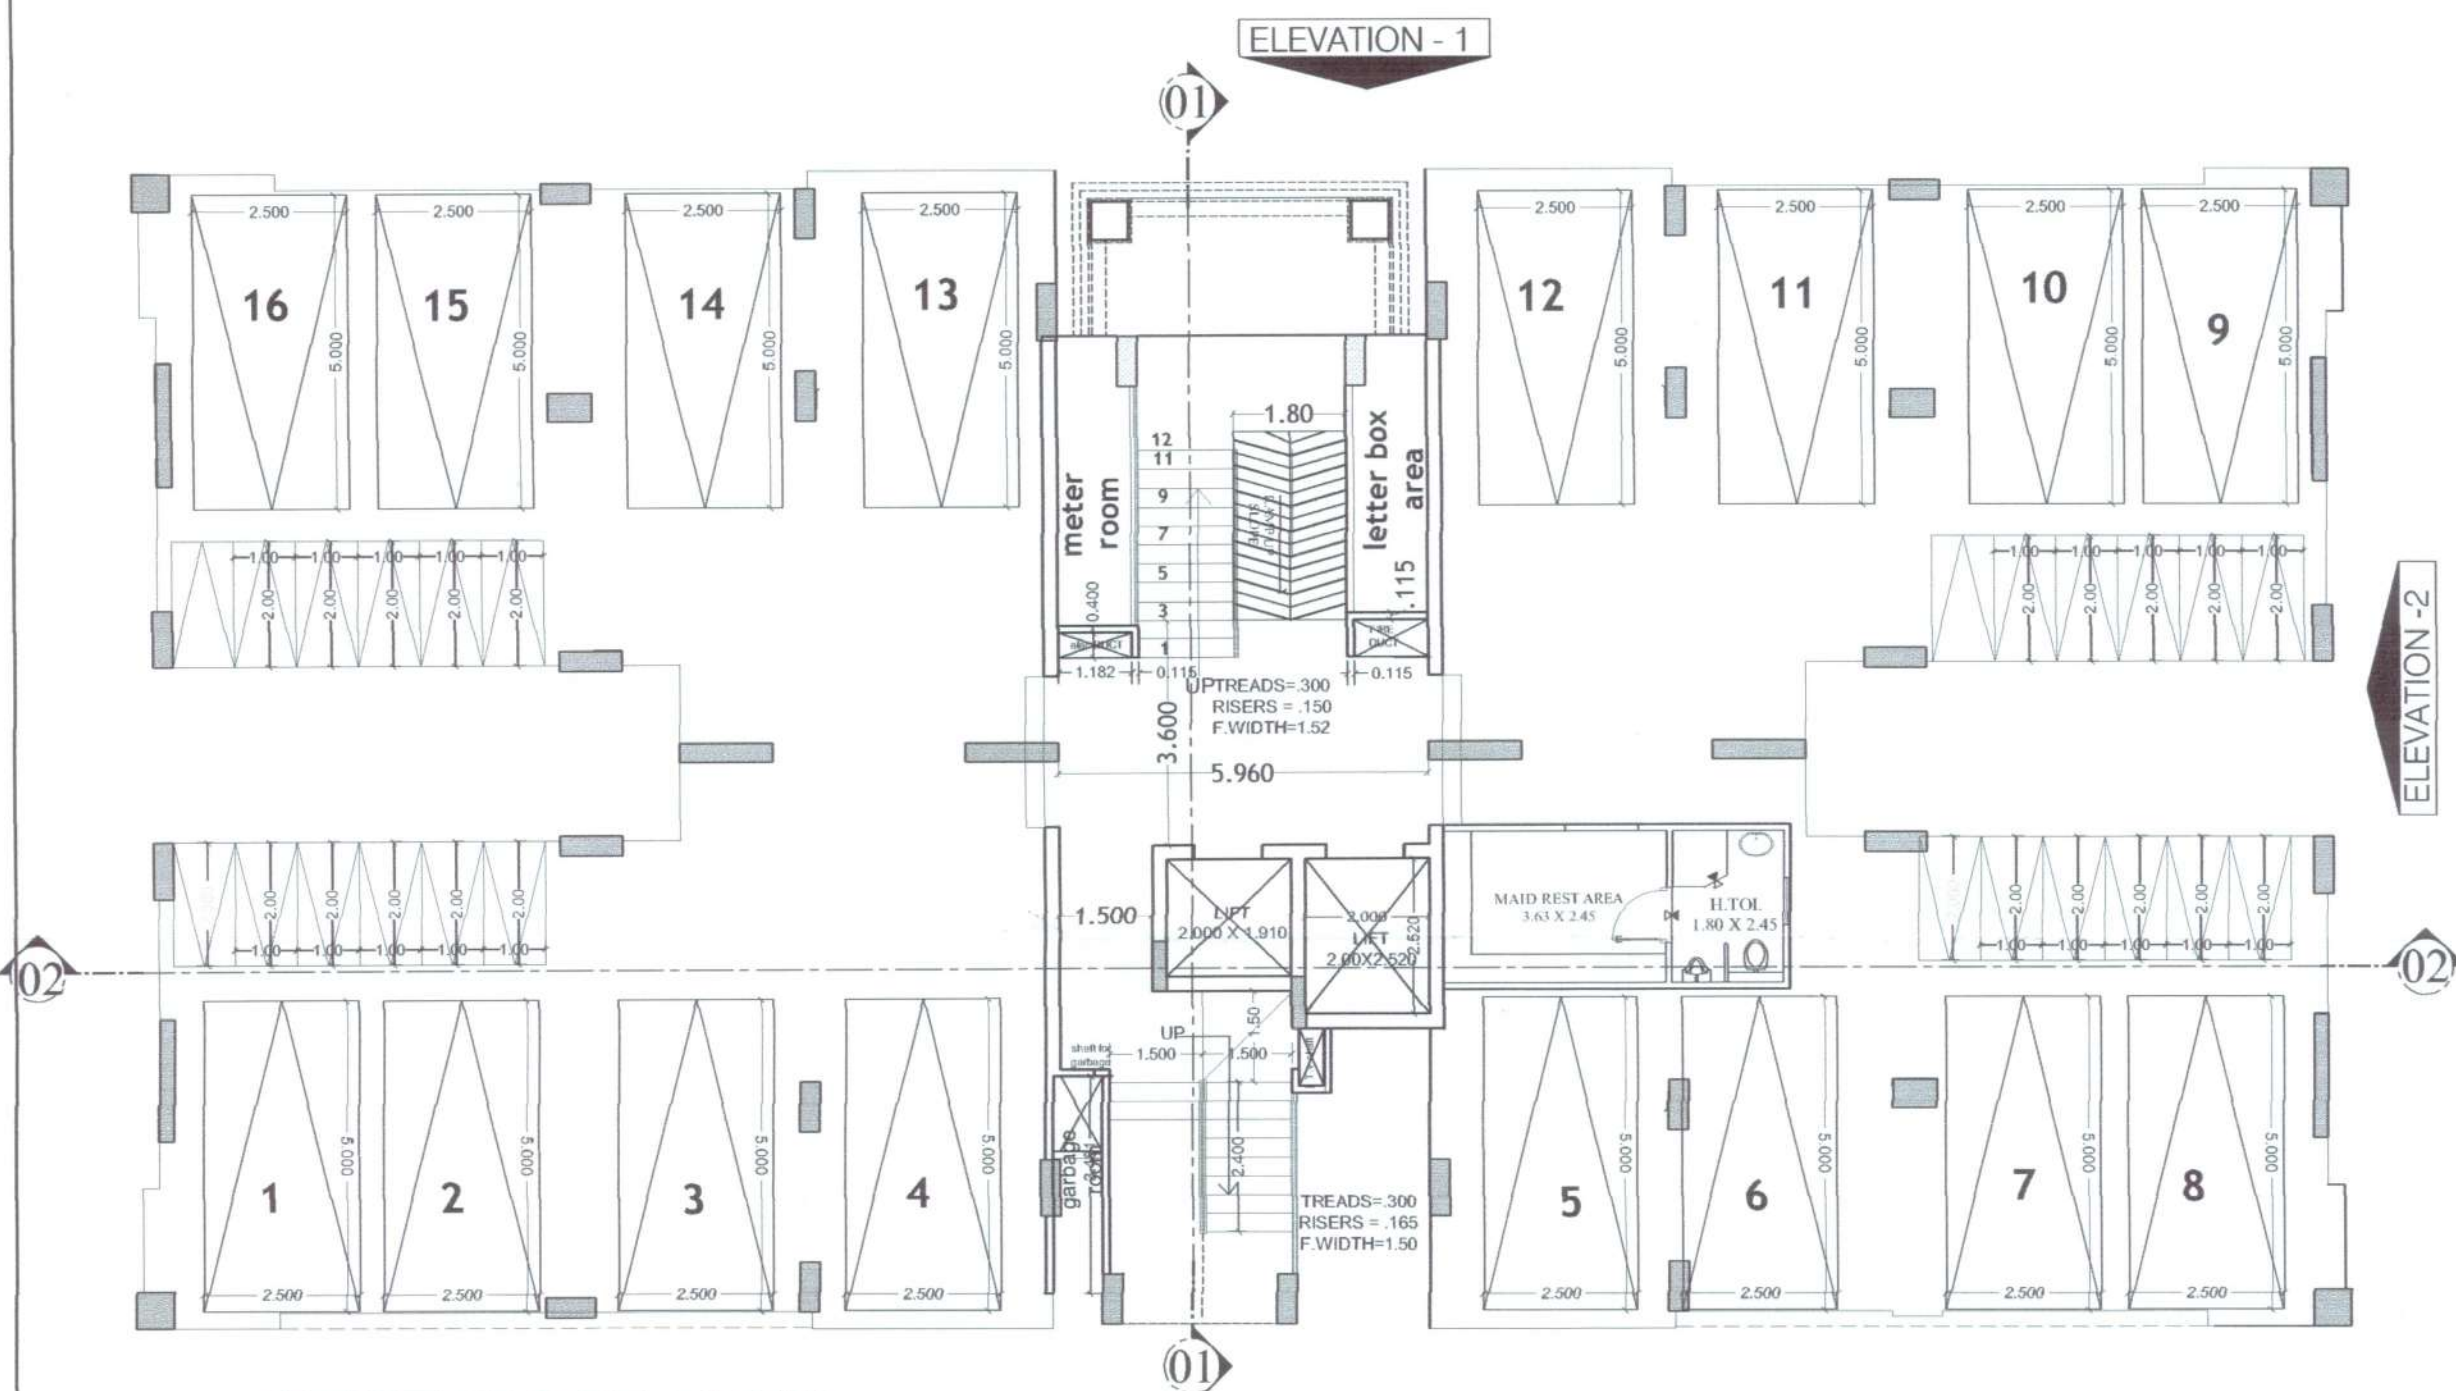

STILT FLOOR PLAN

ELEVATION - 2

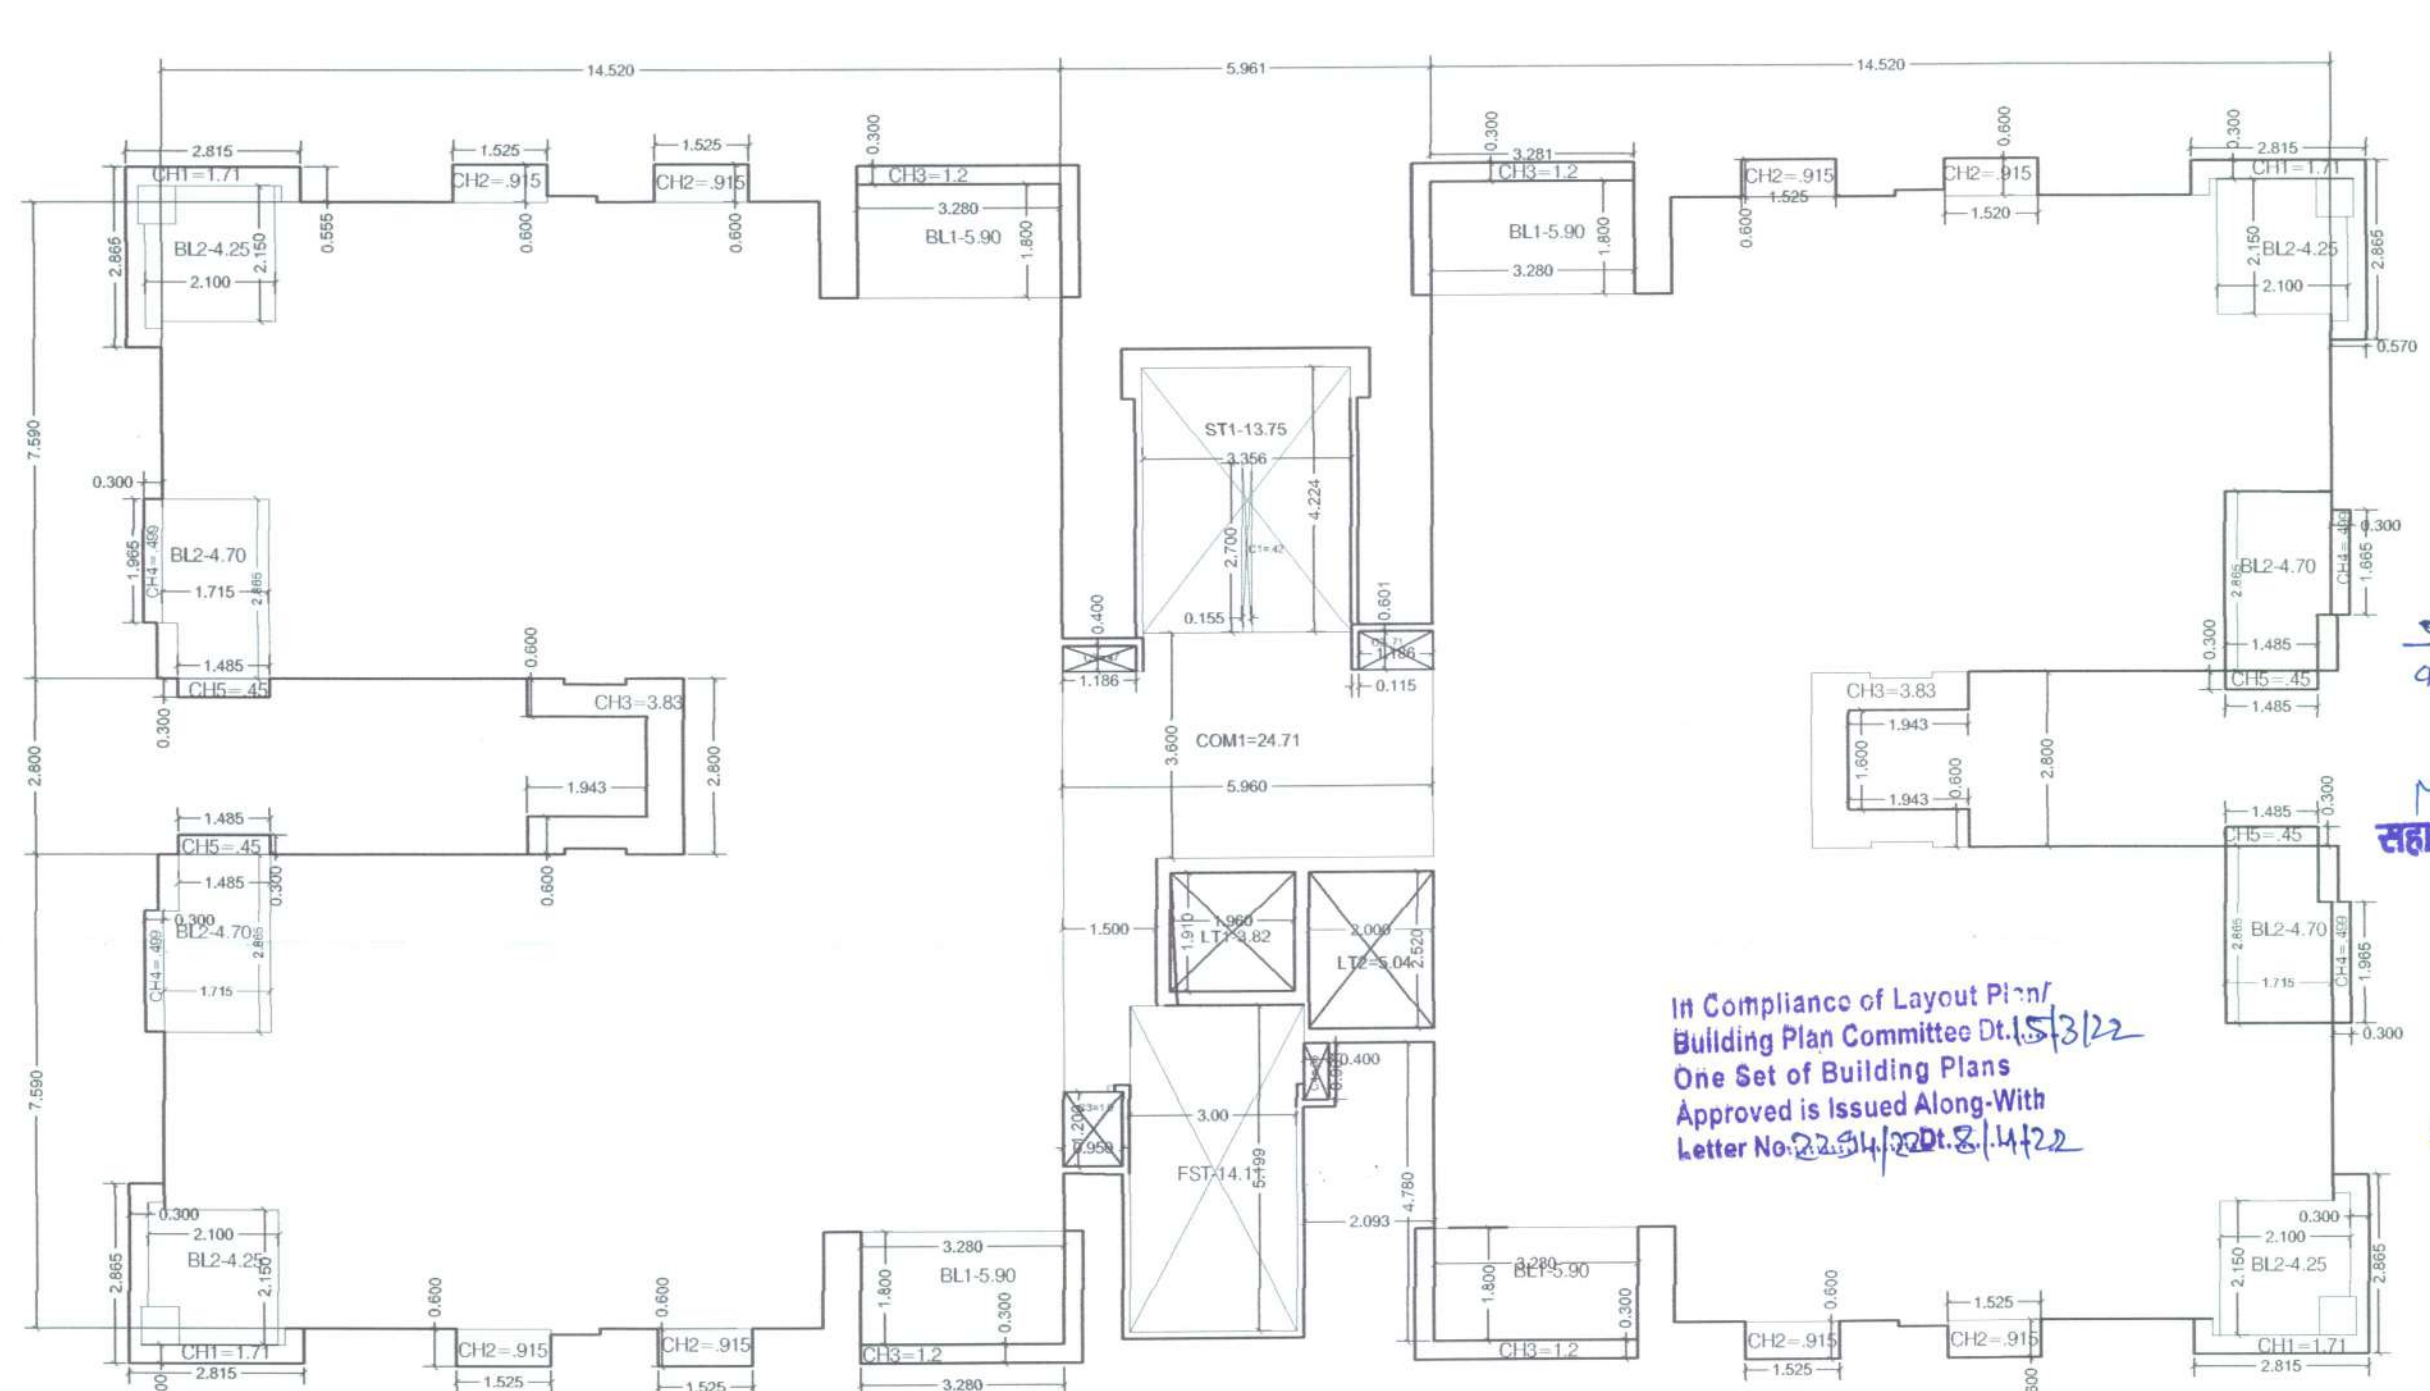

AREA DIAGRAM TYPICAL FLOOR

In Compliance of Layout Plan/
Building Plan Committee D.L.S/3/22
One Set of Building Plans
Approved is Issued Along-With
Letter No. 22/314/2001-2/14722

SHEET NO. 12

Block-
B6,B10,B11

DOOR SCHEDULE

NAME	WIDTH	HEIGHT	SILL HEIGHT	INTEL HEIGHT	REMARK
D	1050	2100	0	2100	
D1	900	2100	0	2100	
D2	750	2100	0	2100	
SD	2000	2350	0	2350	
DW	1650	2100	0	2100	
SD1	1800	2350	0	2350	

WINDOW SCHEDULE

NAME	WIDTH	HEIGHT	SILL HEIGHT	INTEL HEIGHT	REMARK
W	1525	1600	750	2350	
W1	900	1300	1050	2350	KITCHEN
W2	600	900	1200	2100	TOILET
W3	900	1600	750	2350	
W4	2000	2250	100	2350	FRENCH WINDOW

PLOT DETAILS

Proposed Residential Group housing Ashiana Tarang at Bhiwadi , ASHIANA HOUSING Ltd. Khasra No. 779,780,781,782, 783 , 925 / 829 ,927 / 844, 929 / 828 ,930/828 Village :- Milakpur Gujar Teh. Tijara ; Dist Alwar Rajasthan

Project:

Ashiana Tarang at Bhiwadi

Developer:

ASHIANA HOUSING LTD

Sheet title:
GROUND FLOOR PLAN
TYPICAL FLOOR PLAN
TERRACE FLOOR PLAN
AREA DIAGRAM

Block- B6,B10,B11

SCALE- 1:100

For ASHIANA HOUSING LTD
Authorised Signatory

Biswajit Sengupta
B. Arch, FIA, AIHD
Regd. Architect : CA/75/886

SIGNATURE OF AUTHORITY

SIGNATURE OF ARCHITECT

अनुमोदित

भारत सरकार की अधिसूचना दिनांक 14.09.2006 की धारणा में राज्य सरकार के परिपत्र दिनांक 04.02.2011 के अनुसार 20000 वर्ग मीटर से अधिक का निर्माण प्रारम्भ करने से पूर्व "पर्यावरण प्रभाव पत्र" अनिवार्य प्रमाण पत्र आवेक द्वारा प्राप्त किया जाना अनिवार्य होगा।

विद्युत सेवा में नलकारी एवं जल, मल, निकास अग्नि शमन आदि सेवाएँ नेशनल बिलडिंग कोड ऑफ इण्डिया के प्रावधानों/भवन विनियमों के प्रावधानों/सम्बन्धित विभागों के प्रावधानों को सुनिश्चित किया जावेगा।

सीर ऊर्जा से पानी गरम करने का नियमानुसार प्रावधान किया जावे।

इस मानचित्र का अनुमोदन किसी भी भाति प्रशानगत भूमि/भूखण्ड के प्राति स्वामित्व का प्रमाण-पत्र नहीं माना जावेगा। और न ही इससे किसी के स्वामित्व सम्बन्धी अधिकारी ही प्रभावित होंगे।

पार्किंग क्षेत्र का उपयोग केवल पार्किंग हेतु किया जावेगा।

Applicants Should get the construction checked at plinth level before proceeding for further construction.

Adequate Light and Ventilation to be Provided as per M.B.C. Norms.

THESE PLANS ARE VALID ONLY UPTO 07 YEAR FROM DATE OF ISSUE

Rain Water Harvesting Unite Shall be Provided as per Rules.

"जारी किये गये अनुमोदित मान-चित्रों में द्वांरे गये भवन निर्माण की संरचना (STRUCTURE) का दायित्व प्राचीन है।"

SHEET NO.13

Block-
B6,B10,B11

PLOT DETAILS

Proposed Residential Group housing Ashiana Tarang at Bhiwadi , ASHIANA HOUSING Ltd. Khasra No. 779,780,781,782, 783 , 925 / 829 ,927 / 844, 929 / 828 ,930/828 Village :- Milakpur Gujar Teh. Tijara ; Dist Alwar Rajasthan

Project:
Ashiana Tarang at Bhiwadi

Developer:
ASHIANA HOUSING LTD

Sheet title:
FRONT ELEVATION
SIDE ELEVATION

SCALE- 1:100

Block- B6,B10,B11

For ASHIANA HOUSING LTD
Authorised Signatory

Biswajit Sengupta
B. Arch, FIA, AIID
Regd. Architect : CA/75/886

SIGNATURE OF AUTHORITY SIGNATURE OF ARCHITECT

FRONT ELEVATION -1

ELEVATION - 1

SIDE ELEVATION - 2

In Compliance of Layout Plan/
Building Plan Committee DLS/372/2
One Set of Building Plans
Approved is Issued Along-With
Letter No. 334/20.DLS/372/2

अधीनस्थ
नियोजक

Manish Bora
सहायक नगर नियोजक
वि.इ.वि.आ.

उप नगर नियोजक
बीडा, मिवाडी

अनुमोदित

भारत सरकार की अधिसूचना दिनांक 14.09.2006 की धारणा में राज्य सरकार के परिपत्र दिनांक 04.02.2011 के अनुसार 20000 वर्ग मीटर से अधिक का निर्माण प्रारम्भ करने से पूर्व "पर्यावरण प्रमाण पत्र" अनापत्ति प्रमाण पत्र आवेदक द्वारा प्राप्त किया जाना अनिवार्य होगा।

विद्युत सेवा में नलकारी एवं, जल, मल, निकास अग्नि शमन आदि सेवाएँ नेशनल बिल्डिंग कोड ऑफ इण्डिया के प्रावधानों/मवन विनियमों के प्रावधानों/सम्बन्धित विभागों के प्रावधानों को सुनिश्चित किया जावेगा।

इस मानचित्र का अनुमोदन किसी भी भांति प्रशस्तगत भूमि/भूखण्ड के प्राप्ति स्वामित्व का प्रमाण-पत्र नहीं माना जावेगा। और न ही इससे किसी के स्वामित्व सम्बन्धी अधिकारी ही प्रभावित होंगे।

Applicants Should get the construction checked at plinth level before proceeding for further construction.

Adequate Light and Ventilation to be Provided as per N.B.C. Norms.

Rain Water Harvesting Unit Shall be Provided as per Rules.


सौर ऊर्जा से पानी गरम करने का नियमानुसार प्रावधान किया जावे।

पार्किंग क्षेत्र का उपयोग केवल पार्किंग हेतु किया जावेगा।


येड़ लगाओ-हरियाली बढ़ाओ

THESE PLANS ARE VALID ONLY UPTO 07 YEAR FROM DATE OF ISSUE

"जारी किये गये अनुमोदित मान-चित्रों में द्वांहे गये भवन निर्माण की संरचना (STRUCTURE) अब बाधित धारा का ही होगा।"

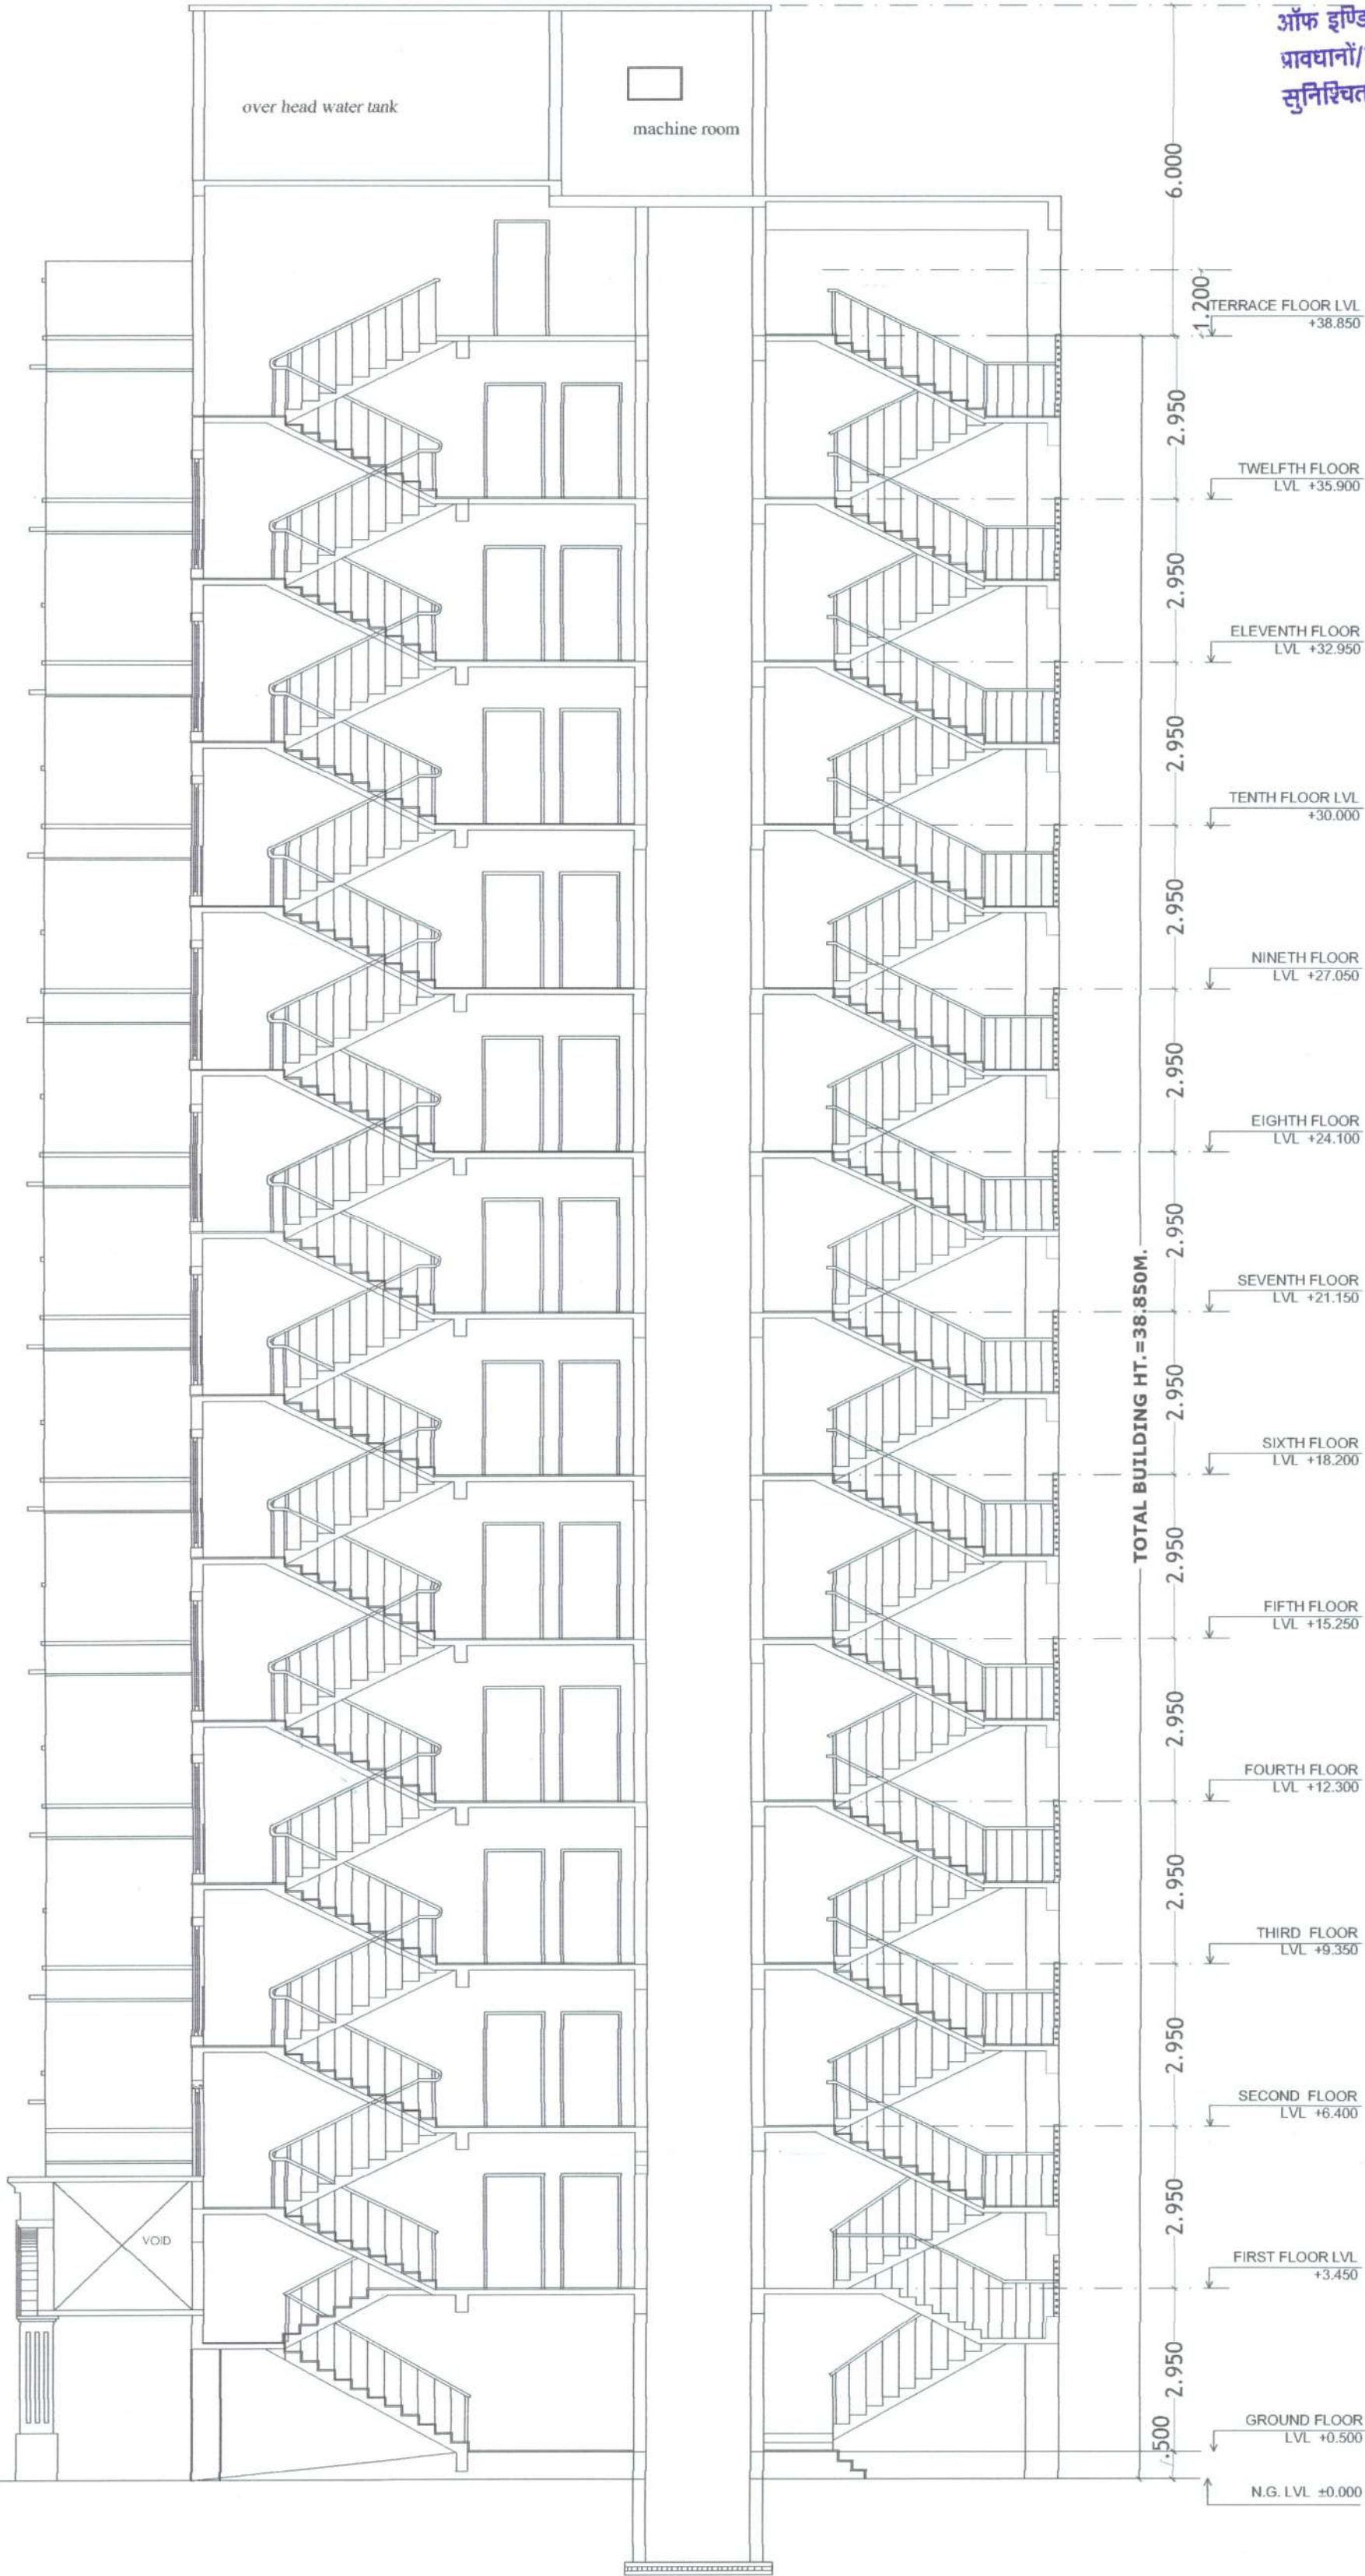

SECTION ON 01-01

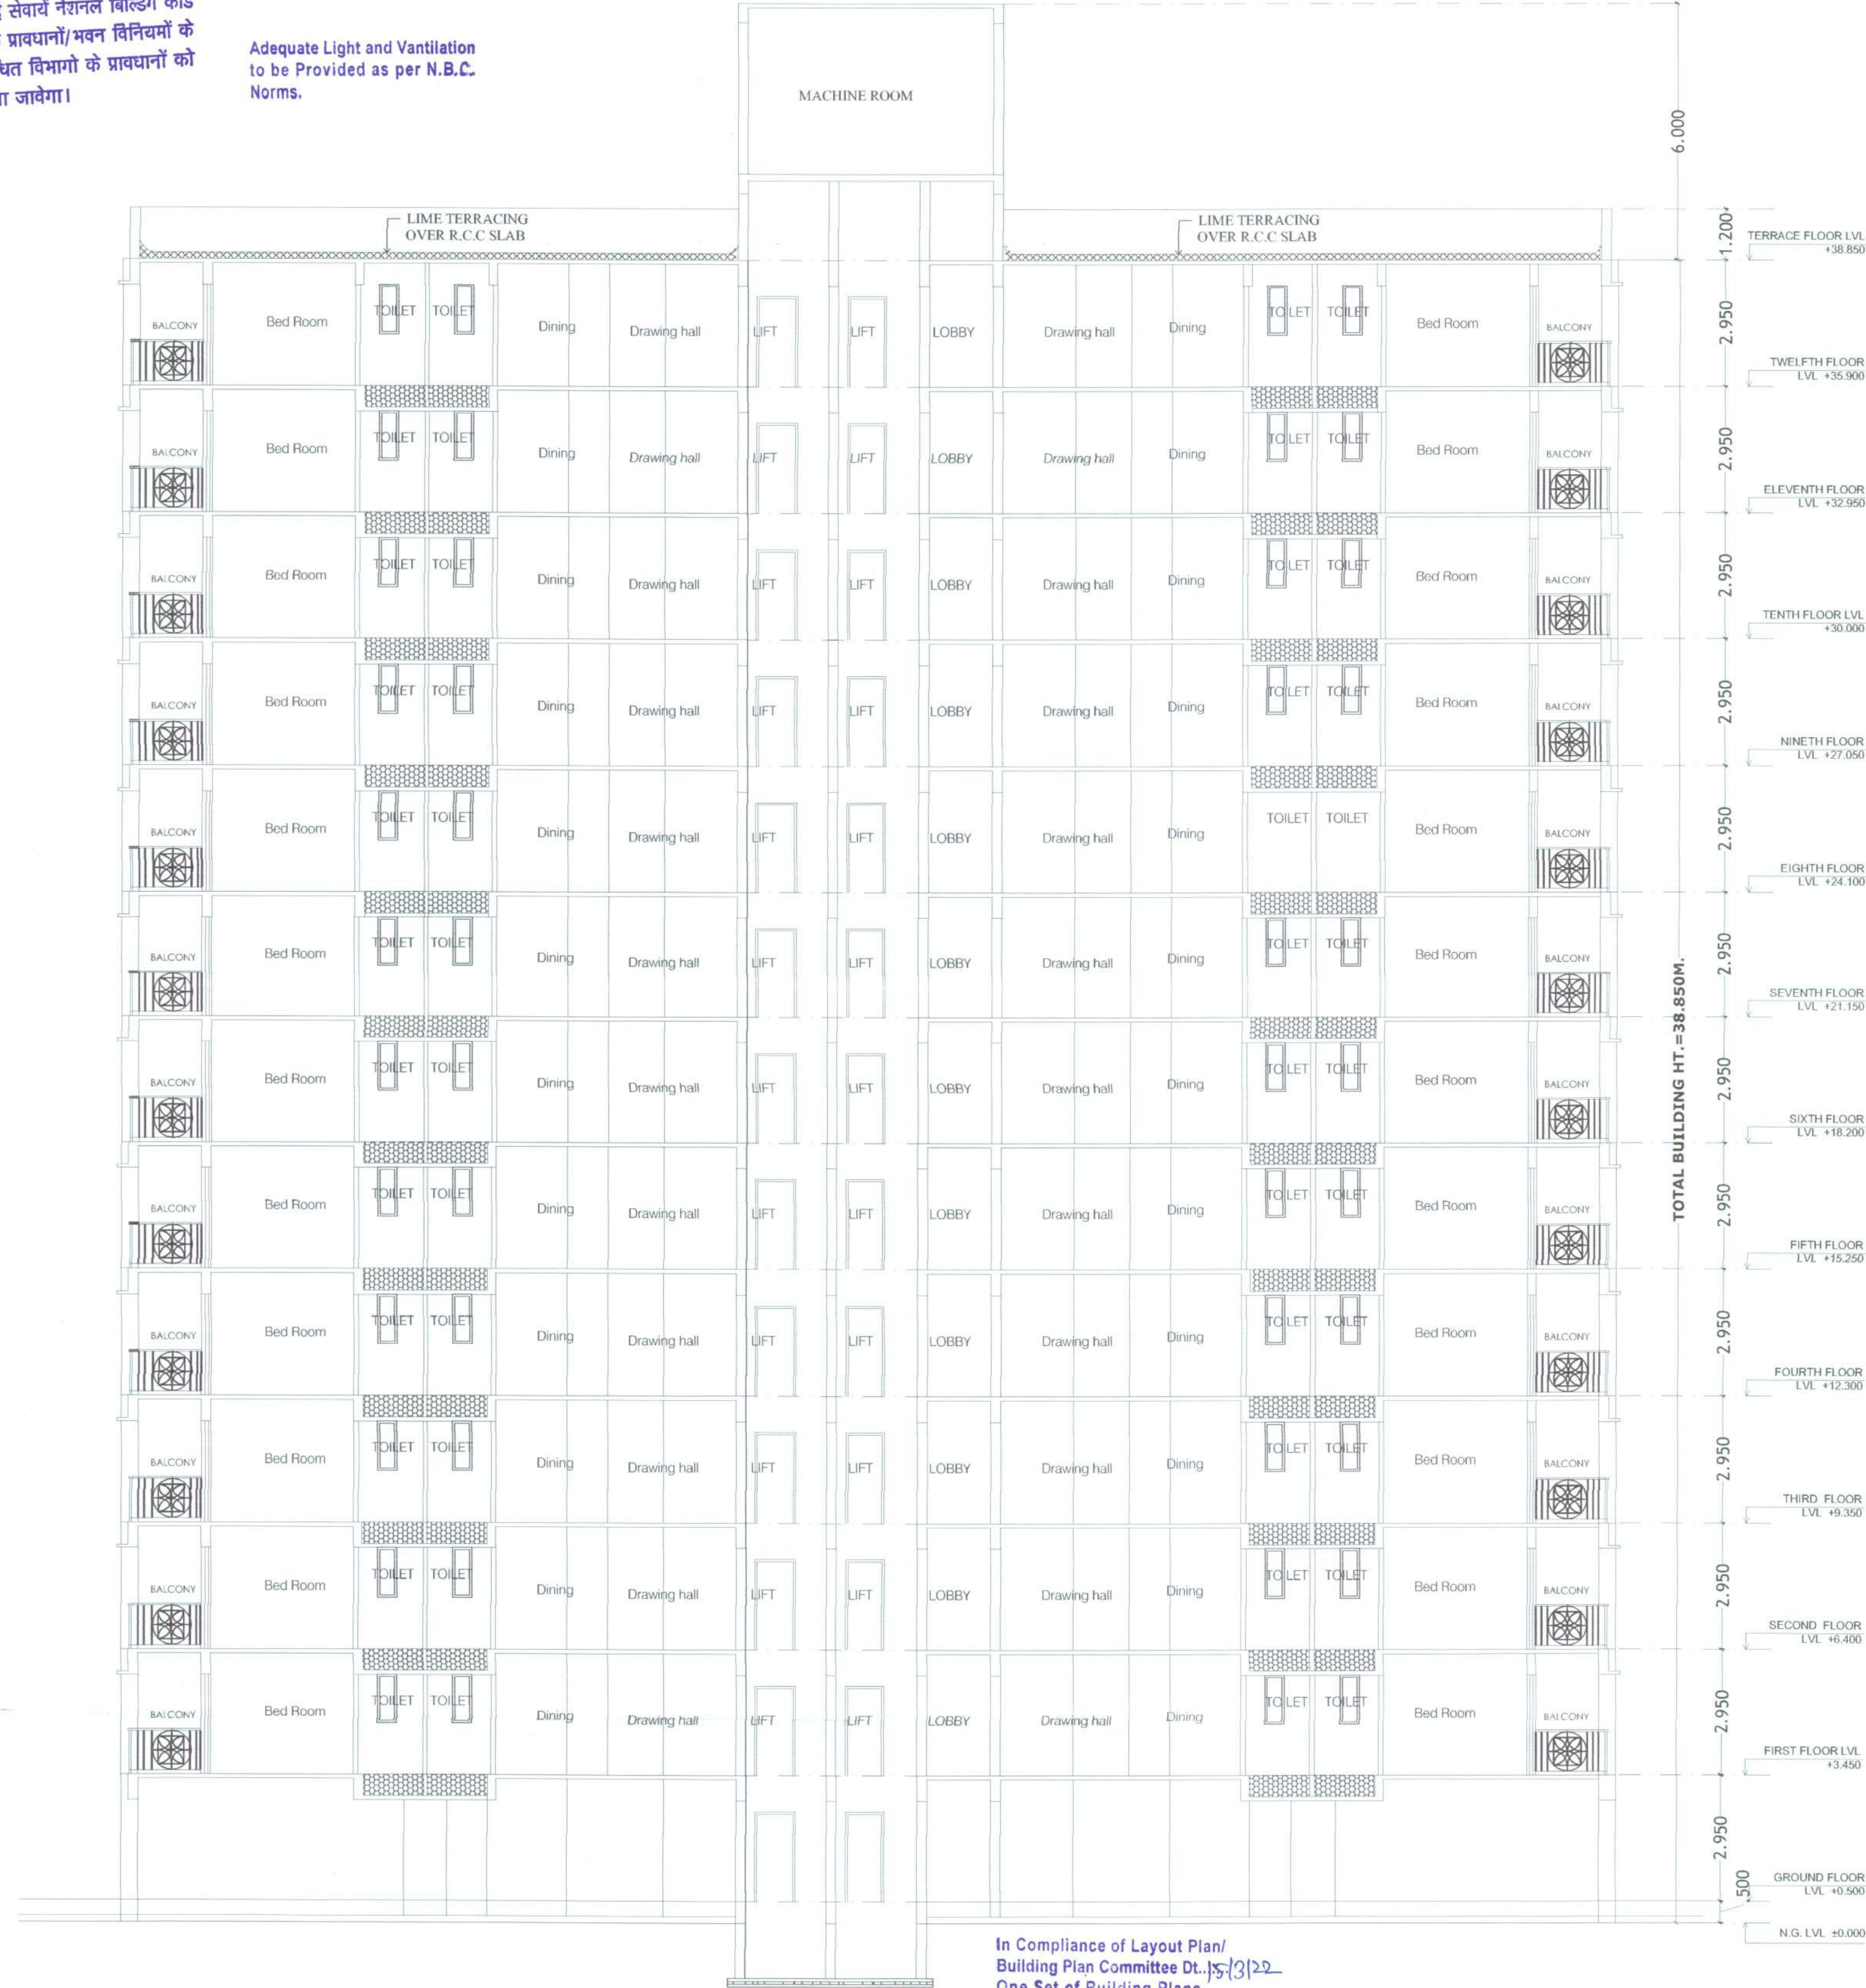

SECTION ON 02-02

In Compliance of Layout Plan/
Building Plan Committee Dt. 15/3/22
One Set of Building Plans
Approved is issued Along With
Letter No 2294/22.DT.8/4/22

उपनिर्देशक
नियोजक

Mawish B. 02/09
सहायक नगर नियोजक
वि.इ.वि.प्र.

उप नगर नियोजक
बीड़ा, भिवाडी

SHEET NO. 14

Block-
B6,B10,B11

PLOT DETAILS

Proposed Residential Group housing Ashiana Tarang at Bhiwadi , ASHIANA HOUSING Ltd.
Khasra No. 779,780.781,782, 783 , 925 / 829 ,927 / 844, 929 / 828 ,930/828 Village :- Milakpur Gujar Teh. Tijara ; Dist Alwar Rajasthan

Project:
Ashiana Tarang at Bhiwadi

Developer:
ASHIANA HOUSING LTD

Sheet title:
FRONT ELEVATION
SIDE ELEVATION

SCALE- 1:100

Block- B6,B10,B11

For ASHIANA HOUSING LTD
Authorised Signatory

Biswajit Sengupta
B. Arch, FIA, AIID
Regd. Architect : CA/75/886

SIGNATURE OF AUTHORITY SIGNATURE OF ARCHITECT