

जयपुर विकास प्राधिकरण, जयपुर।

ज.वि.प्रा./अति.मु.न.नि./बी.पी.सी.(बीपी)/2020/डी-1662

दिनांक:- 04/12/2020

श्री नरेन्द्र सिंह,
अधिकृत हस्ताक्षरकर्ता,
आशियाना हाउसिंग लिमिटेड,
तृतीय तल, अपैक्स मॉल, लालकोठी,
टॉक रोड, जयपुर।

विषय:- पुर्नगठित खसरा नम्बर 453, 454, 454/2, 454/1, 432, 433, 478, 479, 480, 484, 485, 434, 434/735, 435, 436, 437, 437/736, 438, 439, 440, 481, 482, 484, 500, 502, 503, 504/1, 478/716, ग्राम-झाई, तहसील-सांगानेर, महेन्द्रा सेज के पास, अजमेर रोड, जयपुर के प्रस्तावित ग्रुप हाउसिंग के संशोधित भवन मानचित्र बाबत।

महोदय,

आपका प्रार्थना पत्र दिनांक 12.11.2018 के संदर्भ में पुर्नगठित खसरा नम्बर 453, 454, 454/2, 454/1, 432, 433, 478, 479, 480, 484, 485, 434, 434/735, 435, 436, 437, 437/736, 438, 439, 440, 481, 482, 484, 500, 502, 503, 504/1, 478/716, ग्राम-झाई, तहसील-सांगानेर, महेन्द्रा सेज के पास, अजमेर रोड, जयपुर में स्थित भूखण्ड (79,144.22 वर्गमीटर) पर 38.95 मीटर (बेसमेन्ट + स्टिल्ट + 12 तल) ऊँचाई के प्रस्तावित ग्रुप हाउसिंग के संशोधित भवन मानचित्र अनुमोदन के लिए प्रस्तुत किये गये थे, उनकी स्वीकृति भवन मानचित्र समिति (बीपी) की 226वीं बैठक दिनांक 28.05.2020 के निर्णयानुसार निम्न शर्तों के साथ दी जाती है:-

1. यह भवन अनुज्ञा दिनांक 02.08.2025 (दिनांक 03.08.2018 को जारी संशोधित लीजडीड के अनुसार) तक प्रभावी है।
2. भवन निर्माण स्वीकृत मानचित्र के अनुसार ही किया जावेगा तथा किसी भी प्रकार का उल्लंघन (डेवियेशन) नहीं किया जायेगा।
3. भूखण्ड के स्वामी एवं मानचित्र तैयार करने वाले तकनीकीविज्ञ का कर्तव्य होगा कि वो यह सुनिश्चित कर ले कि स्वीकृति मानचित्र प्रचलित मास्टर प्लान/जोनल प्लान के अनुरूप है यदि कोई उल्लंघन जानकारी में नहीं है, प्राधिकरण को अधिकार होगा कि किसी स्थिति में उल्लंघन की जानकारी होने पर भवन मानचित्रों को दी गयी अनुज्ञा रद्द/बदली जा सकती है तथा प्रार्थी प्राधिकरण में किसी भी प्रकार की क्षतिपूर्ति का हकदार नहीं होगा।
4. एकीकृत भवन विनियम 2017 के विनियम संख्या 8.11.2 के अनुसार अपशिष्ट जल का शुद्धिकरण एवं रिसाईकिलिंग हेतु भवन विनियमों के प्रावधानों की पालना सुनिश्चित की जानी होगी।
5. एकीकृत भवन विनियम 2017 के विनियम संख्या 8.11.4 के अनुसार टोस कचरा निस्तारण हेतु भवन विनियमों के प्रावधानों की पालना सुनिश्चित की जानी होगी।
6. एकीकृत भवन विनियम 2017 के विनियम संख्या 8.11.5 के अनुसार सौर ऊर्जा संयंत्र संबंधी भवन विनियमों के प्रावधानों की पालना सुनिश्चित की जानी होगी।
7. एकीकृत भवन विनियम 2017 के विनियम संख्या 10.3 के अनुसार भवन में विद्युत आवश्यकताओं की पूर्ति हेतु संबंधित विद्युत वितरण एजेंसी के प्रावधानों की पालना एवं एनर्जी कन्जर्वेशन बिल्डिंग कोड के प्रावधानों की पालना सुनिश्चित की जानी होगी।
8. आप द्वारा एकीकृत भवन विनियम 2017 के विनियम संख्या 15.2 के अनुसार भवन निर्माण प्रारम्भ करते समय एक सूचना पट्ट मौके पर लगाया जायेगा। जिसमें संबंधित आयुक्त/उपायुक्त संबंधित जोन व प्रवर्तन अधिकारी के टेलीफोन नम्बर इत्यादि अंकित किये जाने होंगे व अनुमोदित मानचित्र की सूचना व अनुमोदन की शर्तें अंकित की जायेगी। निर्माण के दौरान अनुमोदित मानचित्र की एक प्रति आवश्यक रूप से निर्माणकर्ता द्वारा मौके पर रखी जायेगी।
9. निर्माण कार्य प्रारम्भ करने से पूर्व आप उपायुक्त जोन-11 प्राधिकरण को निर्धारित प्रपत्र में सूचना प्रस्तुत करेंगे।
10. एकीकृत भवन विनियम 2017 के विनियम संख्या 15.5 के अनुसार भवन विनियम के अपेक्षाओं के अनुरूप भवन निर्माण करने की जिम्मेदारी भवन निर्माण अनुज्ञाधारी की होगी।
11. उक्त स्वीकृति के कारण यदि जयपुर विकास प्राधिकरण को किसी न्यायालय, सक्षम अधिकारी तथा नगर भूमि (अधिकतम सीमा एवं विनियम) अधिनियम के तहत नियुक्त अधिकारी के समक्ष किसी कार्यवाही में कोई भी खर्च, नुकसान, मुआवजा देना पड़े या देने योग्य हो तो प्रार्थी उनकी इस क्षति को पूर्ण करने के लिए बाध्य होगा।
12. दरवाजे एवं खिड़कियाँ इस प्रकार लगाए जायेंगे कि वो सड़क की ओर निकले हुए नहीं हों।
13. भूस्वामी प्रत्येक मंजिल के लिए स्वीकृत आवासीय ईकाई से अधिक का निर्माण नहीं करेगा।
14. भूस्वामी भवन के परिसर को स्वीकृत उपयोग के अनुसार ही उपयोग में लेगा।
15. तकनीकीविज्ञ के निरीक्षण में स्वामी निर्माण कार्य करवायेगा जिसके संबंध में सूचना प्राधिकरण को पूर्व में देनी होगी। यदि तकनीकीविज्ञ को बदला जाता है तो इसकी सूचना 48 घन्टे के अन्दर यथोचित प्रमाण-पत्र में प्राधिकरण को देनी होगी।
16. आवेदक द्वारा पार्किंग क्षेत्र की पालना एकीकृत भवन विनियम 2017 के विनियम 10.1.16 के अनुसार सुनिश्चित की जानी होगी।
17. भवन परिसर में आगंतुकों की पार्किंग करवाई जाए तथा आगंतुकों हेतु निःशुल्क वाहन पार्किंग का बोर्ड लगवाया जावे।

18. स्वीकृत मानचित्र मौके पर उपयुक्त स्थान पर बोर्ड लगाकर उस पर स्पष्ट रूप से दर्शाने होंगे।
19. निर्माण स्थल पर स्वीकृति का विवरण अर्थात अनुमोदित मानचित्र, उपलब्ध पार्किंग की सूचना एवं भवन में सुरक्षा एवं निकास प्लान (Escape Plan) का नक्शा भी प्रदर्शित (Display) उपयुक्त स्थान पर प्रदर्शित किया जावे।
20. भवन का उपयोग प्रारंभ होने पर एक केयर टेकर की नियुक्ति की जावे जिसके पास भवन का मानचित्र, सुरक्षा एवं निकास प्लान (Escape Plan) उपलब्ध रहें। इस प्रकार नियुक्त केयर टेकर के मोबाईल नंबर एवं Land Line Number भी लिये जाकर पुलिस आयुक्त जयपुर महानगर व उपायुक्त जोन को सूचना उपलब्ध करवाई जावे ताकि किसी भी दुर्घटना की स्थिति में बचाव कार्य प्रभावी रूप से किये जा सकें।
21. एकीकृत भवन विनियम 2017 के विनियम संख्या 18.3 की अनुपालना में "गलत तथ्यों पर प्राप्त की गई अथवा तथ्यों को छुपाकर प्राप्त की गई स्वीकृति स्वतः निरस्त मानी जायेगी एवं ऐसी निर्माण स्वीकृति प्राप्त करने के लिए आवेदनकर्ता को दोषी माना जायेगा।"
22. प्रश्नगत प्रकरण किसी भी न्यायालय में यदि लंबित है तो उसकी समस्त जिम्मेदारी आवेदक की ही होगी। यदि मानचित्र जारी होने के पश्चात यह अवगत हुआ कि किसी भी माननीय न्यायालय में प्रकरण लंबित है अथवा विपरीत निहित है तो मानचित्र स्वतः ही निरस्त समझे जावेंगे।
23. अनुमोदित भवन मानचित्रों को भवन निर्माण शुरू किये जाने के समय भवन निर्माता द्वारा एक बोर्ड पर सम्पूर्ण ब्यौरा सहित जो पठनीय हो, को ऐसे स्थल पर (मुख्य सड़क की ओर) लगाया जावे, जिससे सभी लोगों को निमित्त किये जाने वाले भवन के अनुमोदन की पूर्ण जानकारी प्राप्त हो सके।
24. भवन निर्माण के समय निर्माण सामग्री से आसपास के भवनों के निवासकर्ताओं को किसी प्रकार की असुविधा न हो, इस हेतु भवन निर्माण के दौरान चारों ओर पर्दे लगवाये जावें।
25. भवन मानचित्र इस शर्त के साथ जारी किये जाते हैं कि आप द्वारा परियोजना के पूर्णता प्रमाण पत्र के आवेदन के साथ पर्यावरण विभाग एवं अग्निशमन विभाग का अनापत्ति प्रमाण पत्र नगरीय निकाय में जमा कराना होगा, उसके पश्चात ही पूर्णता प्रमाण पत्र जारी किया जायेगा।
26. निर्मित भवन के प्रवेश द्वार के पास भवन में अनुमोदित व उपलब्ध चार पहिया व दो पहिया वाहनों के पार्किंग की सूचना का बोर्ड (डिस्पले) लगवाया जावे।
27. आप द्वारा Split location भूखण्ड संख्या 485, ग्राम भम्भोरिया, महिन्द्रा सेज, तहसील सांगानेर, जयपुर पर EWS/LIG का निर्माण मूल भूखण्ड की जारी की गई स्वीकृति की दिनांक से 2 वर्ष के भीतर तैयार कर सूचना जविप्रा को दी जानी होगी अन्यथा नियमानुसार कार्यवाही की जावेगी।

संलग्न:- मानचित्रों की प्रति का 1 सेट (18 मानचित्र)

भवदीय,

(ओमप्रकाश पारीक)

अतिरिक्त मुख्य नगर नियोजक,
भवन मानचित्र समिति (बीपी)
जयपुर विकास प्राधिकरण, जयपुर।

प्रतिलिपि:- सूचनार्थ एवं आवश्यक कार्यवाही हेतु।

1. प्रबन्ध निदेशक, जयपुर विद्युत वितरण निगम लि0, विद्युत भवन जनपथ, जयपुर को सूचनार्थ प्रेषित है।
2. मुख्य अभियन्ता, मुख्यालय जन स्वास्थ्य अभियांत्रिकी विभाग हसनपुरा रोड, रेल्वे हाँस्पीटल के पास, जयपुर को सूचनार्थ प्रेषित है।
3. रजिस्ट्रार, Rajasthan Real Estate Regulatory Authority, 2nd & 3rd Floor, RSIC Building, Udyog Bhavan, Tilak Marg, C-Scheme, Jaipur-302005 को सूचनार्थ प्रेषित है।
4. मुख्य नियन्त्रक (प्रवर्तन), जयपुर विकास प्राधिकरण, जयपुर को मानचित्रों की प्रति (18 मानचित्र) संलग्न कर अग्रिम कार्यवाही हेतु प्रेषित है।
5. श्री धर्मपाल सिंह, उपकर निर्धारण अधिकारी एवं संभागीय संयुक्त श्रम आयुक्त, शान्ति नगर, हसनपुरा, जयपुर को सूचनार्थ प्रेषित है।
6. उपायुक्त, जोन-11, जयपुर विकास प्राधिकरण, जयपुर को मानचित्रों की प्रति (18 मानचित्र) संलग्न कर अग्रिम कार्यवाही हेतु प्रेषित है।
7. उपायुक्त राजस्व-प्रथम, नगर निगम, जयपुर को पत्र क्रमांक एफ. 60/उपा. रा (प्रथम)/जननि/2019/18 दिनांक 08.03.2019 के क्रम में सूचनार्थ प्रेषित है।

(ओमप्रकाश पारीक)

अतिरिक्त मुख्य नगर नियोजक,
भवन मानचित्र समिति (बीपी)
जयपुर विकास प्राधिकरण, जयपुर।

जयपुर विकास प्राधिकरण, जयपुर।

ज.वि.प्रा./अति.मु.न.नि./बी.पी.सी.(बीपी)/2021/डी-1572

दिनांक:- 29/11/2021

श्री नरेन्द्र सिंह,
अधिकृत हस्ताक्षरकर्ता,
आशियाना हाउसिंग लिमिटेड,
तृतीय तल, अपेक्स मॉल, लालकोठी,
टोंक रोड़, जयपुर।

विषय:- पुर्नगठित खसरा नम्बर 453, 454, 454/2, 454/1, 432, 433, 478, 479, 480, 484, 485, 434, 434/735, 435, 436, 437, 437/736, 438, 439, 440, 481, 482, 484, 500, 502, 503, 504/1, 478/716, ग्राम-झाँई, तहसील-सांगानेर, महेन्द्रा सेज के पास, अजमेर रोड़, जयपुर के प्रस्तावित ग्रुप हाउसिंग के संशोधित भवन मानचित्र बाबत।

महोदय,

आपका प्रार्थना पत्र दिनांक 12.11.2018 के संदर्भ में पुर्नगठित खसरा नम्बर 453, 454, 454/2, 454/1, 432, 433, 478, 479, 480, 484, 485, 434, 434/735, 435, 436, 437, 437/736, 438, 439, 440, 481, 482, 484, 500, 502, 503, 504/1, 478/716, ग्राम-झाँई, तहसील-सांगानेर, महेन्द्रा सेज के पास, अजमेर रोड़, जयपुर में स्थित भूखण्ड (79,144.22 वर्गमीटर) पर 41.90 मीटर ऊँचाई के प्रस्तावित ग्रुप हाउसिंग के भवन मानचित्र अनुमोदन के लिए बीपीसी-बीपी की 226वीं बैठक दिनांक 28.05.2020 में प्रस्तुत किये गये थे। प्रश्नगत भूखण्ड की ऊँचाई 40 मीटर से अधिक होने के कारण प्रकरण राज्य सरकार को प्रेषित किया गया, राज्य सरकार से स्वीकृति प्राप्त होने में देरी होने के कारण विकासकर्ता द्वारा प्रार्थना पत्र प्रस्तुत कर निवेदन किया गया है कि राज्य सरकार से 40 मीटर ऊँचाई से अधिक की स्वीकृति आने तक 38.95 मीटर ऊँचाई तक के ग्रुप हाउसिंग प्रयोजनार्थ भवन मानचित्र जारी कर दिये जायें। विकासकर्ता द्वारा किये गये निवेदन के क्रम में 38.95 मीटर ऊँचाई (बेसमेन्ट + स्टिल्ट + प्रथम तल से 12 तल) तक के ग्रुप हाउसिंग प्रयोजनार्थ भवन मानचित्र दिनांक 04.12.2020 को जारी किये गये

वर्तमान में राज्य सरकार से 40 मीटर ऊँचाई से अधिक अर्थात् 41.90 मीटर ऊँचाई की स्वीकृति दिनांक 10.09.2021 को प्राप्त हो चुकी है। अतः 41.90 मीटर ऊँचाई (बेसमेन्ट + स्टिल्ट + प्रथम तल से 13 तल) की भवन निर्माण स्वीकृति एवं भवन मानचित्र निम्न शर्तों के साथ जारी किये जाते हैं:-

1. यह भवन अनुज्ञा दिनांक 02.08.2025 (दिनांक 03.08.2018 को जारी संशोधित लीजडीड के अनुसार) तक प्रभावी है।
2. भवन निर्माण स्वीकृत मानचित्र के अनुसार ही किया जावेगा तथा किसी भी प्रकार का उल्लंघन (डेवियेशन) नहीं किया जायेगा।
3. भूखण्ड के स्वामी एवं मानचित्र तैयार करने वाले तकनीकीविज्ञ का कर्तव्य होगा कि वो यह सुनिश्चित कर ले कि स्वीकृति मानचित्र प्रचलित मास्टर प्लान/जोनल प्लान के अनुरूप है यदि कोई उल्लंघन जानकारी में नहीं है, प्राधिकरण को अधिकार होगा कि किसी स्थिति में उल्लंघन की जानकारी होने पर भवन मानचित्रों को दी गयी अनुज्ञा रद्द/बदली जा सकती है तथा प्रार्थी प्राधिकरण में किसी भी प्रकार की क्षतिपूर्ति का हकदार नहीं होगा।
4. एकीकृत भवन विनियम 2017 के विनियम संख्या 8.11.2 के अनुसार अपशिष्ट जल का शुद्धिकरण एवं रिसाईकिलिंग हेतु भवन विनियमों के प्रावधानों की पालना सुनिश्चित की जानी होगी।
5. एकीकृत भवन विनियम 2017 के विनियम संख्या 8.11.4 के अनुसार ठोस कचरा निस्तारण हेतु भवन विनियमों के प्रावधानों की पालना सुनिश्चित की जानी होगी।
6. एकीकृत भवन विनियम 2017 के विनियम संख्या 8.11.5 के अनुसार सौर ऊर्जा संयंत्र संबंधी भवन विनियमों के प्रावधानों की पालना सुनिश्चित की जानी होगी।
7. एकीकृत भवन विनियम 2017 के विनियम संख्या 10.3 के अनुसार भवन में विद्युत आवश्यकताओं की पूर्ति हेतु संबंधित विद्युत वितरण एजेंसी के प्रावधानों की पालना एवं एनर्जी कन्जर्वेशन बिल्डिंग कोड के प्रावधानों की पालना सुनिश्चित की जानी होगी।
8. आप द्वारा एकीकृत भवन विनियम 2017 के विनियम संख्या 15.2 के अनुसार भवन निर्माण प्रारम्भ करते समय एक सूचना पट्ट मौके पर लगाया जायेगा। जिसमें संबंधित आयुक्त/उपायुक्त संबंधित जोन व प्रवर्तन अधिकारी के टेलीफोन नम्बर इत्यादि अंकित किये जाने होंगे व अनुमोदित मानचित्र की सूचना व अनुमोदन की शर्तें अंकित की जायेगी। निर्माण के दौरान अनुमोदित मानचित्र की एक प्रति आवश्यक रूप से निर्माणकर्ता द्वारा मौके पर रखी जायेगी।
9. निर्माण कार्य प्रारम्भ करने से पूर्व आप उपायुक्त जोन-11 प्राधिकरण को निर्धारित प्रपत्र में सूचना प्रस्तुत करेंगे।
10. एकीकृत भवन विनियम 2017 के विनियम संख्या 15.5 के अनुसार भवन विनियम के अपेक्षाओं के अनुरूप भवन निर्माण करने की जिम्मेदारी भवन निर्माण अनुज्ञाधारी की होगी।
11. उक्त स्वीकृति के कारण यदि जयपुर विकास प्राधिकरण को किसी न्यायालय, सक्षम अधिकारी तथा नगर भूमि (अधिकतम सीमा एवं विनियम) अधिनियम के तहत नियुक्त अधिकारी के समक्ष किसी कार्यवाही में कोई भी खर्च, नुकसान, मुआवजा देना पड़े या देने योग्य हो तो प्रार्थी उनकी इस क्षति को पूर्ण करने के लिए बाध्य होगा।
12. दरवाजे एवं खिड़कियाँ इस प्रकार लगाए जायेंगे कि वो सड़क की ओर निकले हुए नहीं हों।
13. भूस्वामी प्रत्येक मंजिल के लिए स्वीकृत आवासीय ईकाई से अधिक का निर्माण नहीं करेगा।
14. भूस्वामी भवन के परिसर को स्वीकृत उपयोग के अनुसार ही उपयोग में लेगा।

15. तकनीकीविज्ञ के निरीक्षण में स्वामी निर्माण कार्य करवायेगा जिसके संबंध में सूचना प्राधिकरण को पूर्व में देनी होगी। यदि तकनीकीविज्ञ को बदला जाता है तो इसकी सूचना 48 घण्टे के अन्दर यथोचित प्रमाण-पत्र में प्राधिकरण को देनी होगी।
16. आवेदक द्वारा पार्किंग क्षेत्र की पालना एकीकृत भवन विनियम 2017 के विनियम 10.1.16 के अनुसार सुनिश्चित की जानी होगी।
17. भवन परिसर में आगंतुकों की पार्किंग करवाई जाए तथा आगंतुकों हेतु निःशुल्क वाहन पार्किंग का बोर्ड लगवाया जावे।
18. स्वीकृत मानचित्र मौके पर उपयुक्त स्थान पर बोर्ड लगाकर उस पर स्पष्ट रूप से दर्शाने होंगे।
19. निर्माण स्थल पर स्वीकृति का विवरण अर्थात् अनुमोदित मानचित्र, उपलब्ध पार्किंग की सूचना एवं भवन में सुरक्षा एवं निकास प्लान (Escape Plan) का नक्शा भी प्रदर्शित (Display) उपयुक्त स्थान पर प्रदर्शित किया जावे।
20. भवन का उपयोग प्रारंभ होने पर एक केयर टेकर की नियुक्ति की जावे जिसके पास भवन का मानचित्र, सुरक्षा एवं निकास प्लान (Escape Plan) उपलब्ध रहें। इस प्रकार नियुक्त केयर टेकर के मोबाईल नंबर एवं Land Line Number भी लिये जाकर पुलिस आयुक्त जयपुर महानगर व उपायुक्त जोन को सूचना उपलब्ध करवाई जावे ताकि किसी भी दुर्घटना की स्थिति में बचाव कार्य प्रभावी रूप से किये जा सकें।
21. एकीकृत भवन विनियम 2017 के विनियम संख्या 18.3 की अनुपालना में "गलत तथ्यों पर प्राप्त की गई अथवा तथ्यों को छुपाकर प्राप्त की गई स्वीकृति स्वतः निरस्त मानी जायेगी एवं ऐसी निर्माण स्वीकृति प्राप्त करने के लिए आवेदनकर्ता को दोषी माना जायेगा।"
22. प्रश्नगत प्रकरण किसी भी न्यायालय में यदि लंबित है तो उसकी समस्त जिम्मेदारी आवेदक की ही होगी। यदि मानचित्र जारी होने के पश्चात यह अवगत हुआ कि किसी भी माननीय न्यायालय में प्रकरण लंबित है अथवा विपरीत निहित है तो मानचित्र स्वतः ही निरस्त समझे जावेंगे।
23. अनुमोदित भवन मानचित्रों को भवन निर्माण शुरू किये जाने के समय भवन निर्माता द्वारा एक बोर्ड पर सम्पूर्ण ब्यौरा सहित जो पठनीय हो, को ऐसे स्थल पर (मुख्य सड़क की ओर) लगाया जावे, जिससे सभी लोगों को निर्मित किये जाने वाले भवन के अनुमोदन की पूर्ण जानकारी प्राप्त हो सके।
24. भवन निर्माण के समय निर्माण सामग्री से आसपास के भवनों के निवासकर्ताओं को किसी प्रकार की असुविधा न हो, इस हेतु भवन निर्माण के दौरान चारों ओर पर्दे लगवाये जावें।
25. भवन मानचित्र इस शर्त के साथ जारी किये जाते हैं कि आप द्वारा परियोजना के पूर्णता प्रमाण पत्र के आवेदन के साथ पर्यावरण विभाग एवं अग्निशमन विभाग का अनापत्ति प्रमाण पत्र नगरीय निकाय में जमा कराना होगा, उसके पश्चात ही पूर्णता प्रमाण पत्र जारी किया जायेगा।
26. निर्मित भवन के प्रवेश द्वार के पास भवन में अनुमोदित व उपलब्ध चार पहिया व दो पहिया वाहनों के पार्किंग की सूचना का बोर्ड (डिस्पले) लगवाया जावे।
27. आप द्वारा Split location भूखण्ड संख्या 485, ग्राम भम्भोरिया, महिन्द्रा सेज, तहसील सांगानेर, जयपुर पर EWS/LIG का निर्माण मूल भूखण्ड की जारी की गई स्वीकृति की दिनांक से 2 वर्ष के भीतर तैयार कर सूचना जविप्रा को दी जानी होगी अन्यथा नियमानुसार कार्यवाही की जावेगी।

संलग्न:- मानचित्रों की प्रति का 1 सेट (19 मानचित्र)

भवदीय,

वरिष्ठ नगर नियोजक

भवन मानचित्र समिति (बीपी)

जयपुर विकास प्राधिकरण, जयपुर।

प्रतिलिपि:- सूचनार्थ एवं आवश्यक कार्यवाही हेतु।

1. मुख्य नियन्त्रक (प्रवर्तन), जयपुर विकास प्राधिकरण, जयपुर को मानचित्रों की प्रति (19 मानचित्र) संलग्न कर अग्रिम कार्यवाही हेतु प्रेषित है।
2. उपायुक्त, जोन-11, जयपुर विकास प्राधिकरण, जयपुर को मानचित्रों की प्रति (19 मानचित्र) संलग्न कर अग्रिम कार्यवाही हेतु प्रेषित है।
3. रजिस्ट्रार, Rajasthan Real Estate Regulatory Authority, 2nd & 3rd Floor, RSIC Building, Udyog Bhavan, Tilak Marg, C-Scheme, Jaipur-302005 को सूचनार्थ प्रेषित है।
4. निदेशक, राजस्थान राज्य विद्युत वितरण निगम लि0, विद्युत भवन जनपथ, जयपुर को सूचनार्थ प्रेषित है।
5. मुख्य अभियन्ता, मुख्यालय जन स्वास्थ्य अभियांत्रिकी विभाग हसनपुरा रोड, रेल्वे हॉस्पिटल के पास, जयपुर को सूचनार्थ प्रेषित है।
6. उपायुक्त राजस्व-प्रथम, नगर निगम, जयपुर को पत्र क्रमांक एफ. 60/उपा. रा (प्रथम)/जननि/2019/18 दिनांक 08.03.2019 के क्रम में सूचनार्थ प्रेषित है।

वरिष्ठ नगर नियोजक,

भवन मानचित्र समिति (बीपी)

जयपुर विकास प्राधिकरण, जयपुर।

PARKING FACILITY AREA CHART OF PREVIOUS APPROVED / EXISTING BUILDING BLOCKS

1. TOTAL B A R AREA CONSUMED IN PREVIOUS APPROVED / EXISTING BUILDING BLOCKS (RESIDENTIAL) = 109426.44 Sq.Mt

2. TOTAL B A R AREA CONSUMED IN PREVIOUS APPROVED / EXISTING BUILDING BLOCKS (COMMERCIAL) = 106.76 Sq.Mt

a) ECU @ 115 Sq.Mt Required = 109426.44 / 115 = 952.40 E.C.U.

b) Commercial ECU @ 75 Sq.Mt Required = 106.76 / 75 = 1.42 E.C.U.

3. TOTAL ECU = 953.82 = 1.42 = 955.24 E.C.U. SAY 955 E.C.U.

25% of Visitor parking (100) = 25 nos

20% of Visitor parking (100) = 20 nos

15% of Visitor parking (100) = 15 nos

10% of Visitor parking (100) = 10 nos

say Total Visitor parking = 70 nos

Therefore Total ECU Req. (156 + 70) = 1082 Nos

PARKING Req.

75% of car req (1082) = 811 Nos

25% of Two wheeler (1082) = 271 x 3 = 813 nos

4. PARKING PROVIDED IN PREVIOUS APPROVED BUILDING BLOCKS

CAR = 1100.00 Nos.

SCOOTERS = 1103.00 Nos.

PARKING FACILITY AREA CHART OF PROPOSED BUILDING BLOCKS

1. TOTAL B A R AREA CONSUMED = 53532.60 Sq.Mt

2. TOTAL COMMERCIAL B A R AREA = 754.57 Sq.Mt

3. TOTAL RESIDENTIAL B A R AREA = 52778.03 Sq.Mt

a) ECU @ 115 Sq.Mt Required = 52778.03 / 115 = 459.44 ECU SAY 459 ECU

b) Commercial ECU @ 75 Sq.Mt Required = 754.57 / 75 = 10.06 ECU SAY 10 ECU

4. TOTAL ECU Required:

A. TOTAL Residential ECU = 459 ECU Req.

25% of Visitor parking (100) = 25 nos

20% of Visitor parking (100) = 20 nos

15% of Visitor parking (100) = 15 nos

10% of Visitor parking (100) = 10 nos

say Total Visitor parking = 70 nos

Therefore Total ECU Req. (459 + 70) = 529 Nos

B. Commercial ECU Required = 10 ECU Req.

25% of Visitor parking (100) = 25 nos

Therefore Total ECU Req. (10 + 3) = 13 Nos

TOTAL ECU Required (Residential + Commercial) = 535 + 13 = 548 Nos

PARKING Req.

75% of car req (548) = 411 Nos

25% of Two wheeler (548) = 137 x 3 = 411 nos

5. PARKING PROVIDED FOR PROPOSED BUILDING BLOCKS

CAR = 646 Nos.

SCOOTERS = 198.00 Nos. / 66 ECU

PARKING PROVIDED			
S.NO.	FLOOR	CAR	SCOOTER
1.	OPEN SPACE	200 ECU	60 (20 ECU)
2.	STILT FLOOR	195 ECU	130 (40 ECU)
3.	BASEMENT FLOOR	185 ECU	185 ECU
TOTAL E.C.U.		646 ECU	198 (66 ECU)

ASHIANA UMANG PHASE - IV
LAND AREA - 7703.00 SQ MT.
(AREA CALCULATED AS PER PHYSICAL
AREA OF THE LAND)
RERA REG.-RAJIP/2017/779

ASHIANA UMANG PHASE - III
LAND AREA - 7208.50 SQ MT.
(AREA CALCULATED AS PER PHYSICAL
AREA OF THE LAND)
RERA REG.-RAJIP/2017/1022

PHASE-IV
already sanction

PHASE-II
already sanction

PHASE-II
already sanction

PHASE-I
already sanction

PHASE-1
already sanction

PHASE-5

PLOT DETAILS:
Khasra No. 453, 454, 454/2, 454/1, 432, 433, 478, 479, 480, 484, 485, 434, 434/735, 435, 436, 437, 437/736, 438, 439, 440, 482, 500, 502, 503, 504/1, 478/716 IN VILLAGE JHAI TEH. SAGANER ON AJMER ROAD, JAIPUR

Project:-
PROPOSED GROUP HOUSING ASHIANA UMANG

Developer:-
ASHIANA HOUSING LTD.

Sheet Title:-
PARKING ARRANGEMENT SITE PLAN

SCALE-
1:500

SITE PLAN

NORTH

Per Ashiana Housing Ltd.
Authorized Signatory

Per Ashiana Housing Ltd.
Authorized Signatory

SIGNATURE OF AUTHORITY

SIGNATURE OF ARCHITECT

LEGEND

WHOLE PROJECT

ASHIANA UMANG PH-1&2

ASHIANA UMANG PH-IV

ASHIANA UMANG PH-V

ASHIANA UMANG PH-VI

ASHIANA UMANG PH-III

ASHIANA UMANG PH-I

ASHIANA UMANG PH-II

ASHIANA UMANG PH-5

ASHIANA UMANG PH-6

BISWAJIT SENGUPTA
B. Arch. FIAT, AIID
Regd. Architect : CA/75/886

ASHIANA UMANG PHASE - VI
LAND AREA - 8312.30 SQ MT. (Phase Area)
(AREA CALCULATED AS PER PHYSICAL
AREA OF THE LAND)
GROUP : 20896.55 Sq.Mt
open area : 6073 Sq.Mt

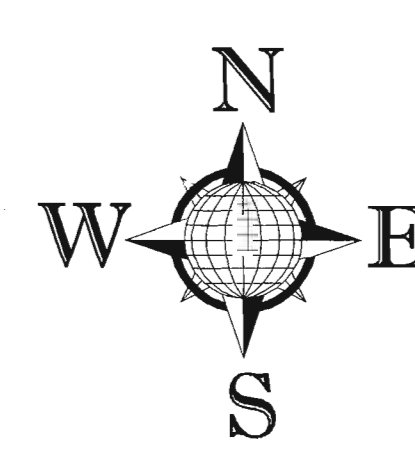
ASHIANA UMANG PHASE - V
LAND AREA - 19618.40 SQ MT.
(AREA CALCULATED AS PER PHYSICAL
AREA OF THE LAND)
RERA REG.-RAJIP/2021/1430

ॐ नमो भगवते वासुदेवाय ॥
 श्रीगणेशाय नमः ॥ श्रीगुरुभ्यो नमः ॥
 श्रीशिवाय नमः ॥ श्रीब्रह्माय नमः ॥
 श्रीविष्णवे नमः ॥ श्रीकृष्णाय नमः ॥
 श्रीनारायणाय नमः ॥ श्रीरामाय नमः ॥
 श्रीसूर्याय नमः ॥ श्रीचंद्राय नमः ॥
 श्रीशुक्राय नमः ॥ श्रीमङ्गलाय नमः ॥
 श्रीशिवसे नमः ॥ श्रीगणेशाय नमः ॥
 श्रीशिवसे नमः ॥ श्रीगणेशाय नमः ॥
 श्रीशिवसे नमः ॥ श्रीगणेशाय नमः ॥

[illegible]

नियुक्ति विभाग, बालिकाओं, युवक युविकाओं
 (प्रधान) निदेशिका, प्रमाणित, 6.15 बें
 विद्या, 6.15 बें, 6.15 बें, 6.15 बें
 आ. प्रमाणित, 6.15 बें, 6.15 बें, 6.15 बें
 बालिका, 6.15 बें, 6.15 बें, 6.15 बें
 निदेशिका, 6.15 बें, 6.15 बें, 6.15 बें
 की आदेशिका, 6.15 बें, 6.15 बें, 6.15 बें

• approval should get to
construction checked at pilot
level before proceeding for
wider construction



KHASRA NO.453,454,454/2,454/1,432,433,478,
479,480,484,485,434,434/735,435,436,437,
437/736,438,439,440,482,500,502,503,504/1
478/716 IN VILLAGE JHAI TEH. SAGANER ON
AJMER ROAD ,JAIPUR

PROPOSED GROUP HOUSING ASHIANA UMANG

ASHIANA HOUSING LTD.

FIRST FLOOR PLAN (ON SITE PLAN)

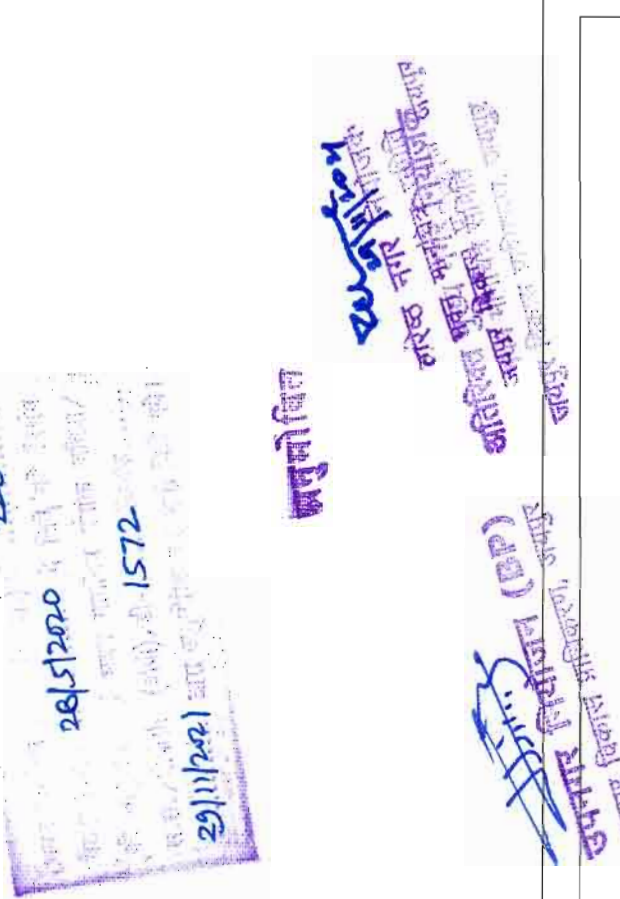
NORTH

For Ashiana Housing Limited
[Signature]
 Authorised Signatory

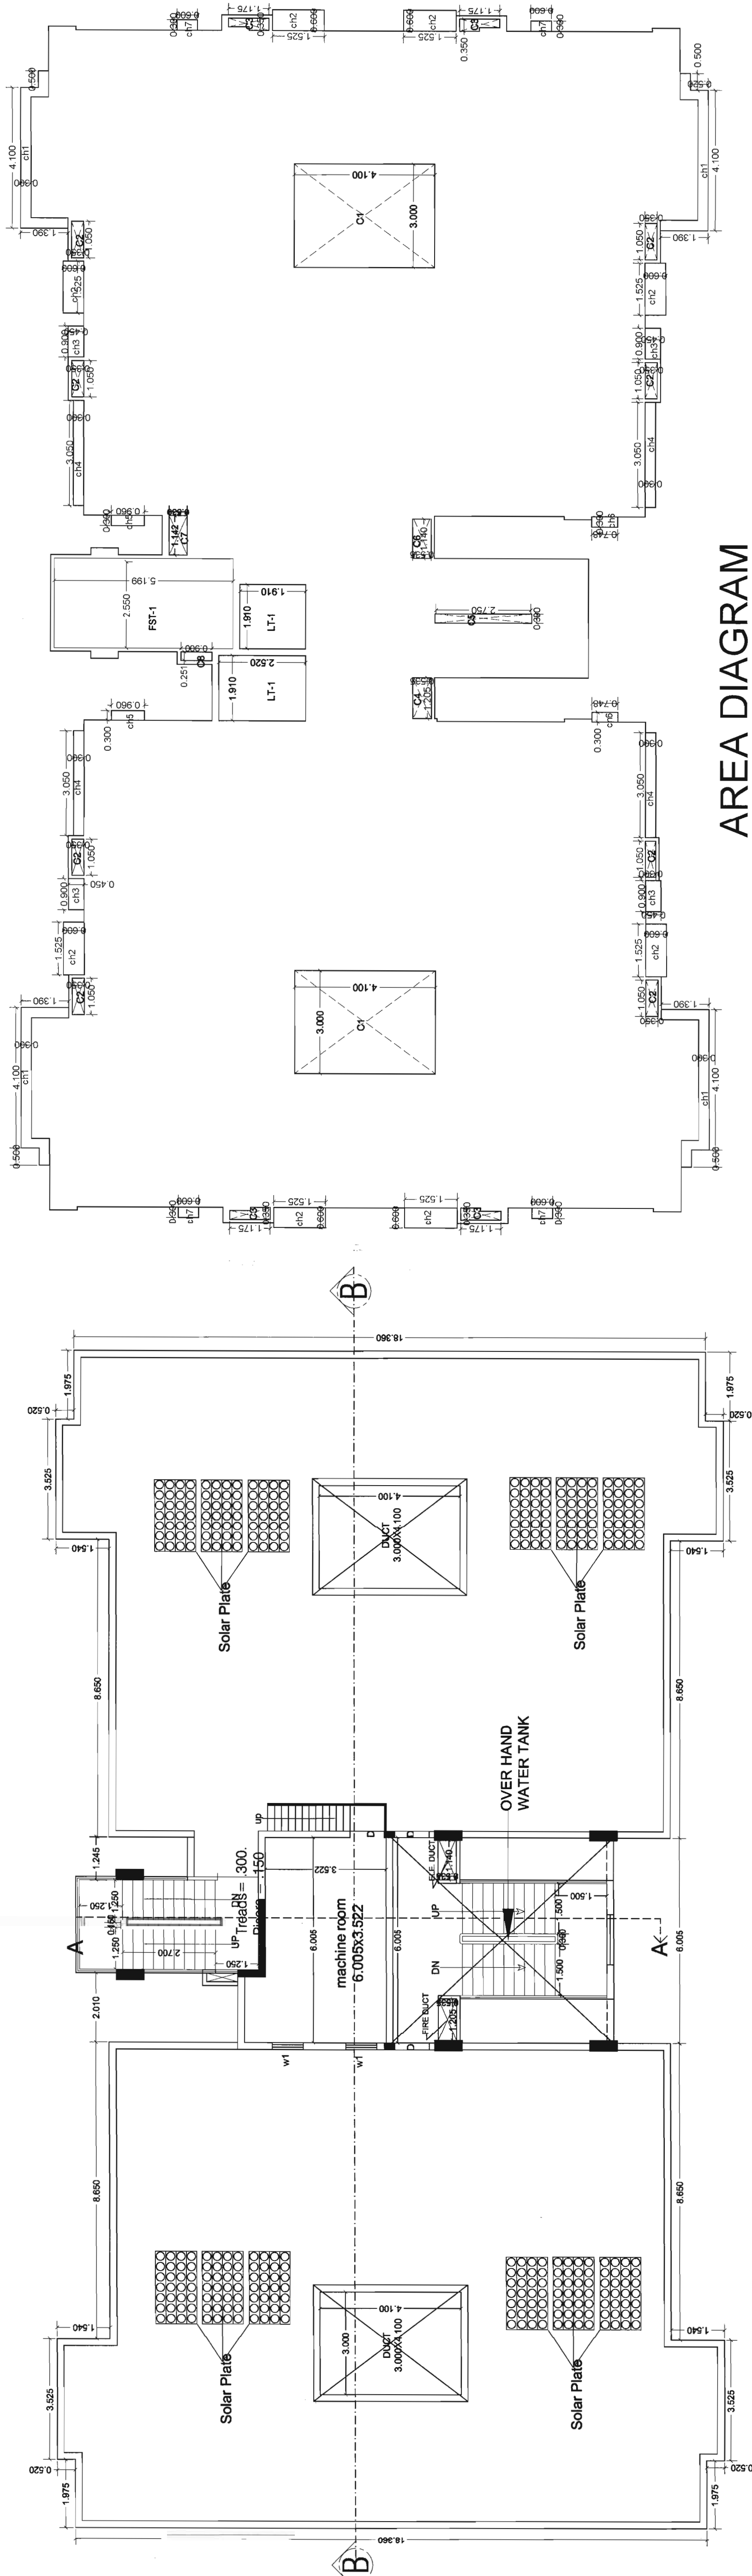
BISWAJIT SENGUPTA
 Regd. Architect : CA/75/886
 Head Architect : CA/75/886

SIGNATURE OF ARCHITECT

OTHER'S LAND

[illegible]

SECTION ON B-B

[illegible]

KHASRA No.453,454,454/2,454/1,432,433,478,
 479,480,484,485,434,434/735,435,436,437,
 437/736,438,439,440,482,500,502,503,504/1
 478/716 IN VILLAGE JHAI TEH. SAGANER ON
 AJMER ROAD, JAIPUR

Project:-
PROPOSED GROUP HOUSING ASHIANA UMANG

Developer:-

Sheet title:-
TERRACE FLOOR PLAN
AREA DIAGRAM
ELEVATIONS & SECTION

SCALE-1:100

BLOCK-Q

RESIDENCE

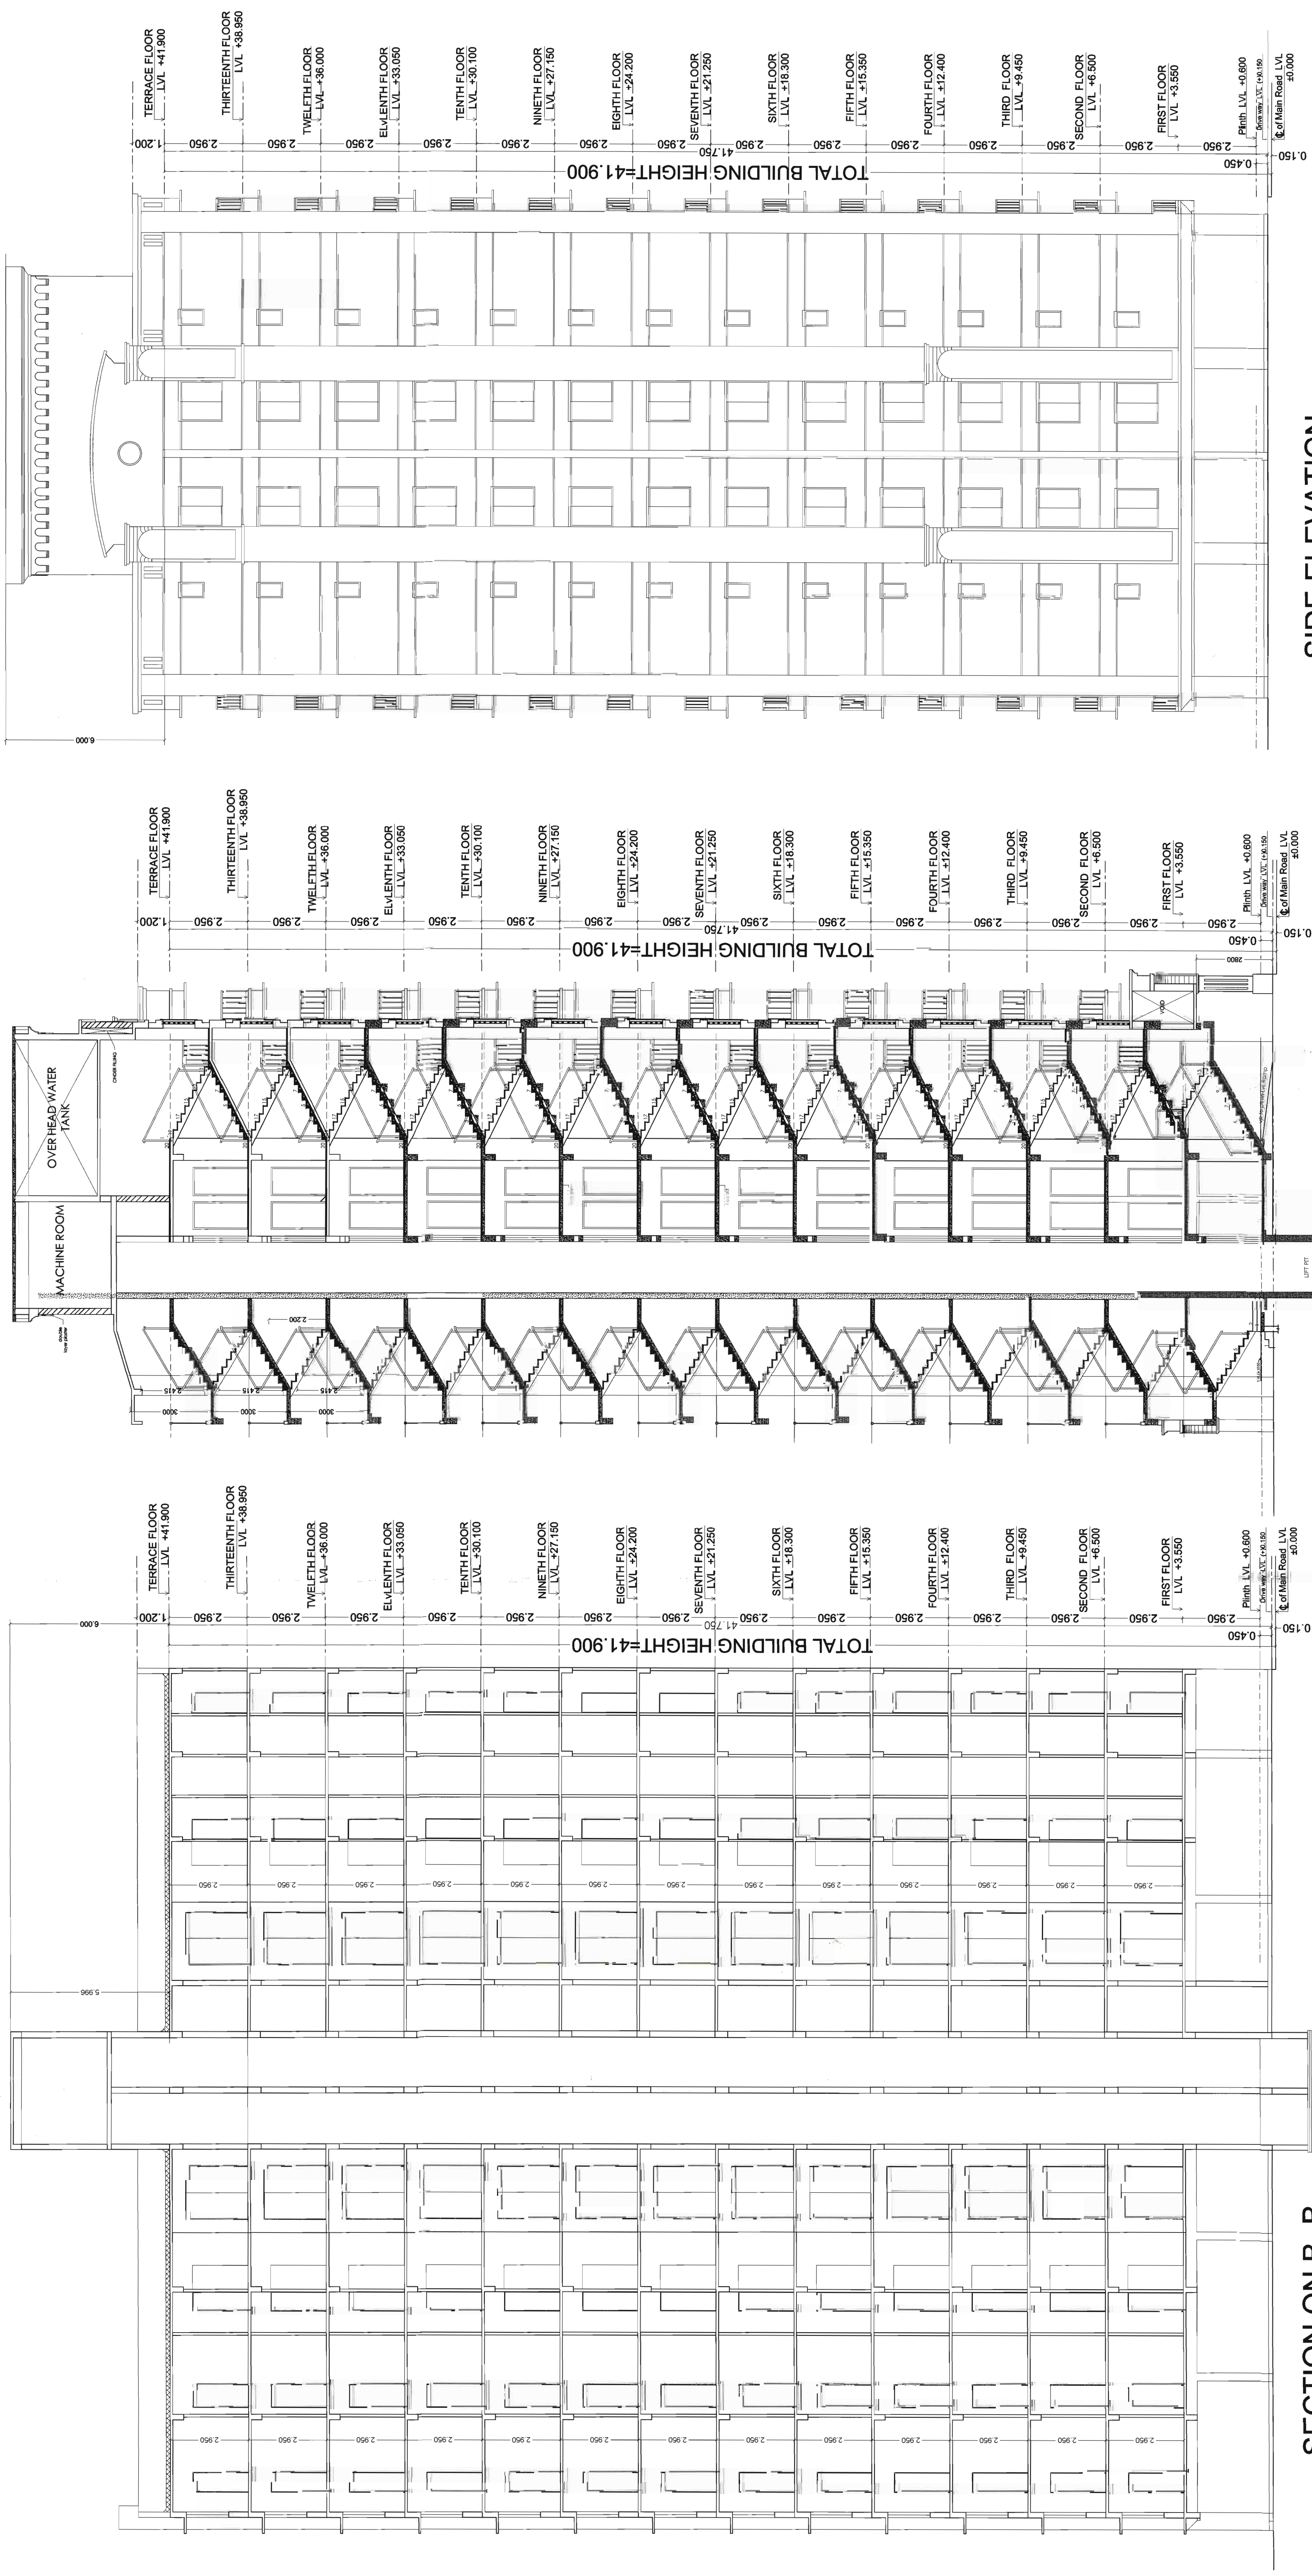
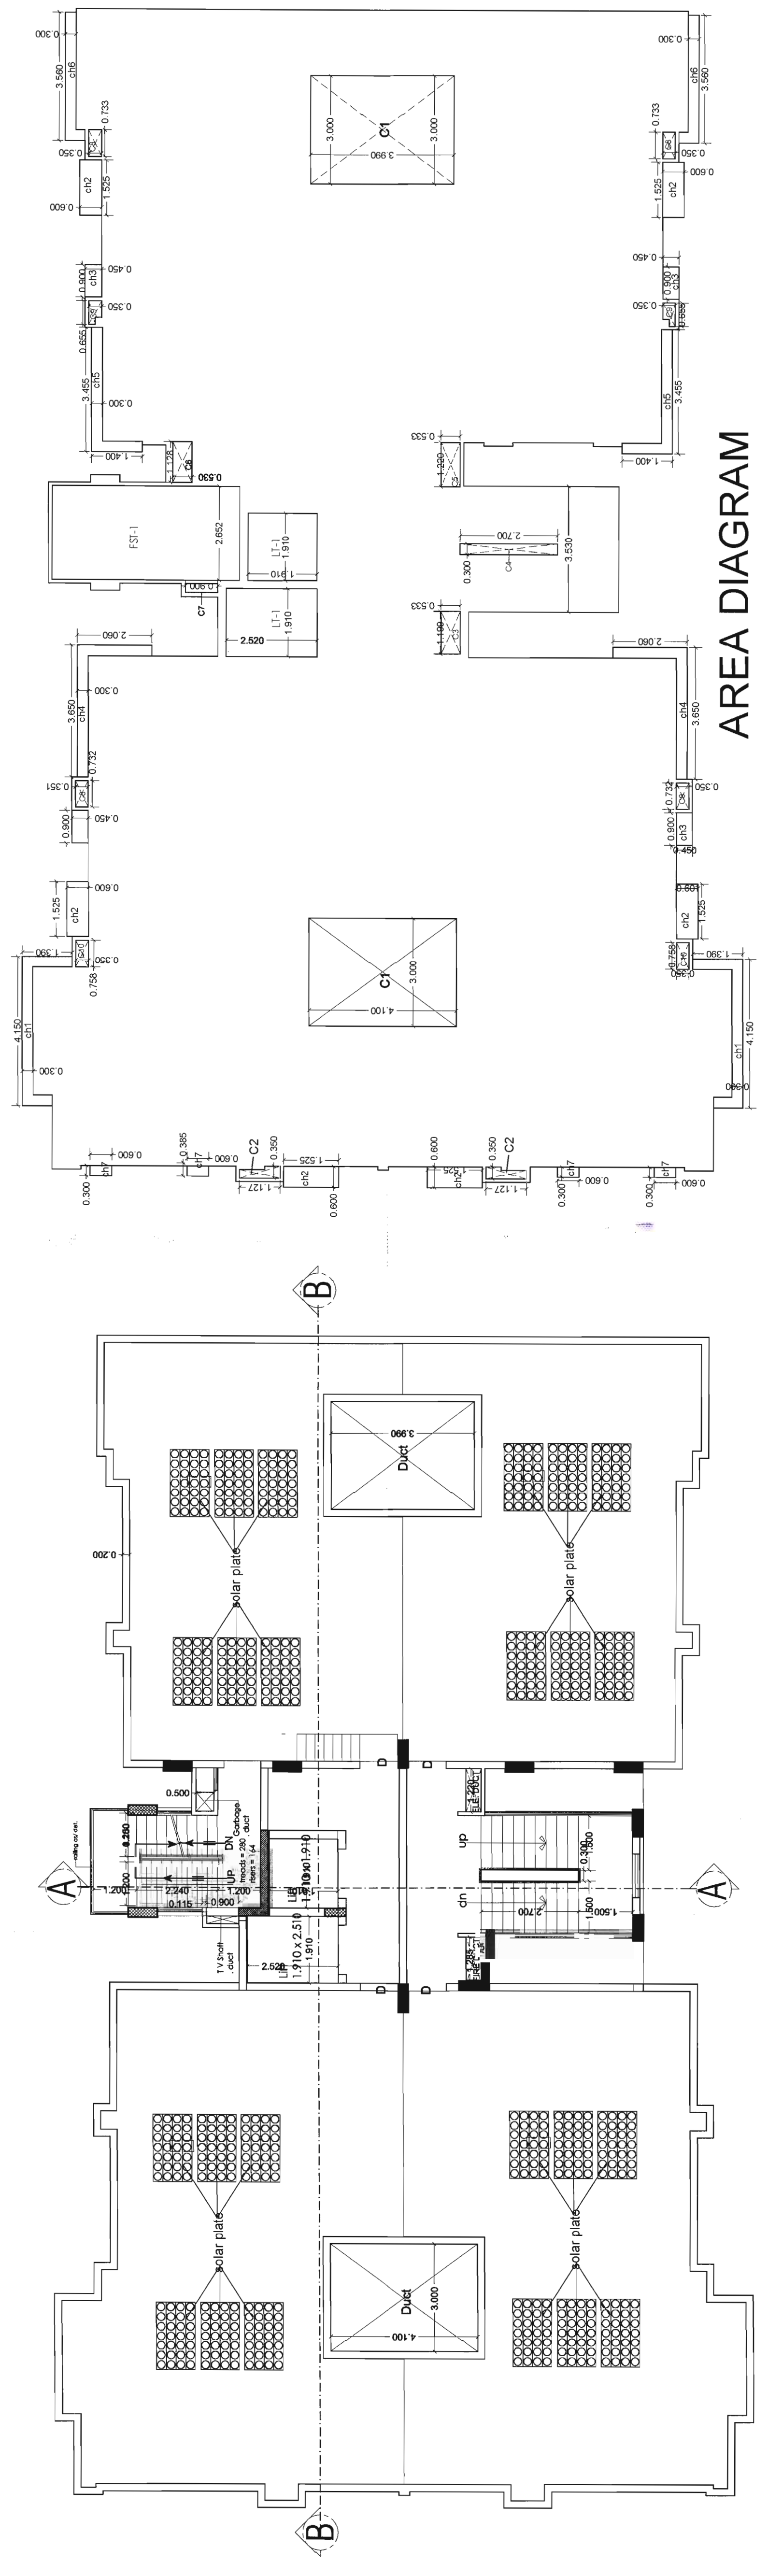
NORTH

For Ashiana Housing Limited
Biswaajit Sengupta
B.Arch, FIA, AIID
Regd. Architect: CA75886
Biswaajit Sengupta
Regd. Architect: CA75886

SIGNATURE OF ARCHITECT

SECTION ON A - A

SECTION ON B -B

[illegible]

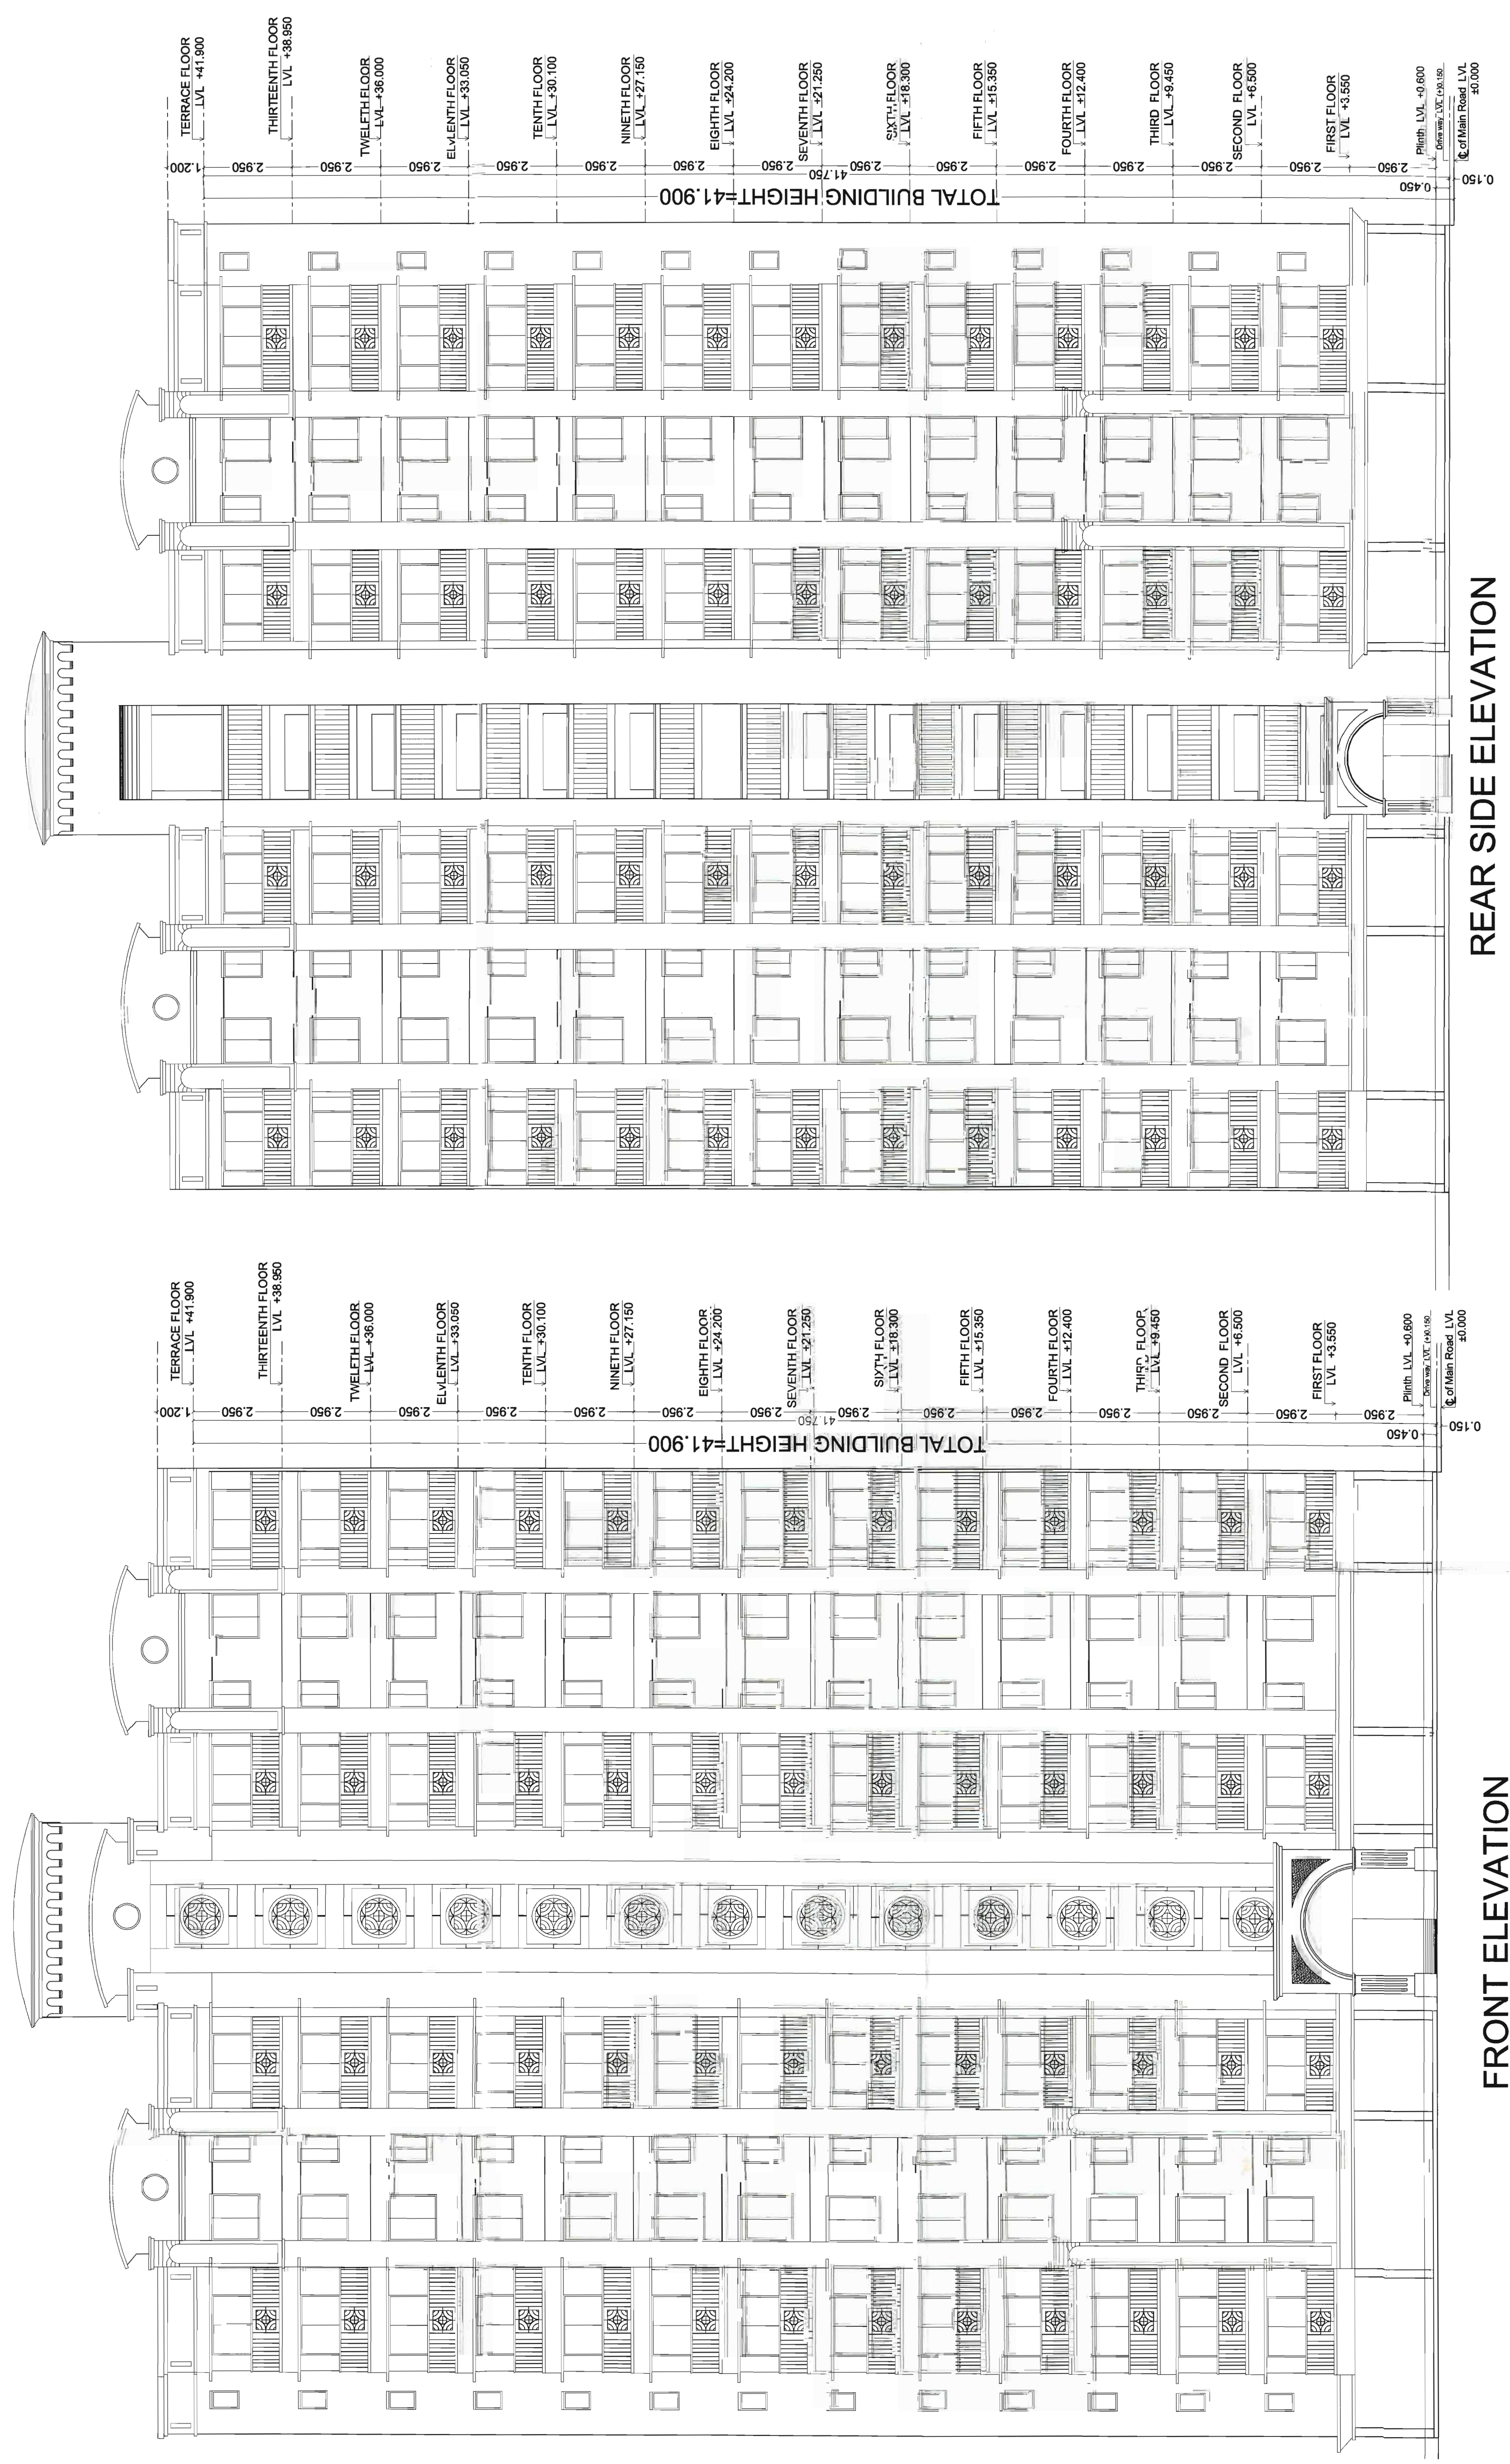
AREA DIAGRAM

TERRACE FLOOR PLAN

28/07/2020
29/07/2020
15.72

28/07/2020
29/07/2020
15.72

SHEET NO.12/18



PLOT DETAILS:
KHASRA NO.453,454,454/2,454/1,432,433,476,
479,480,484,485,434,434,735,435,436,437,
437,736,438,439,440,480,500,502,503,504/1,
478,716 IN VILLAGE JHAI TEH. SAGNER ON
AJMER ROAD JAIPUR

Project:-
PROPOSED GROUP HOUSING ASHIANA UMANG

Developer:-
ASHIANA HOUSING LTD.

Sheet title:-
STILT FLOOR PLAN
TYPICAL FLOOR PLAN
& ELEVATIONS

SCALE: 1:100

BLOCK-R&S
RESIDENCE

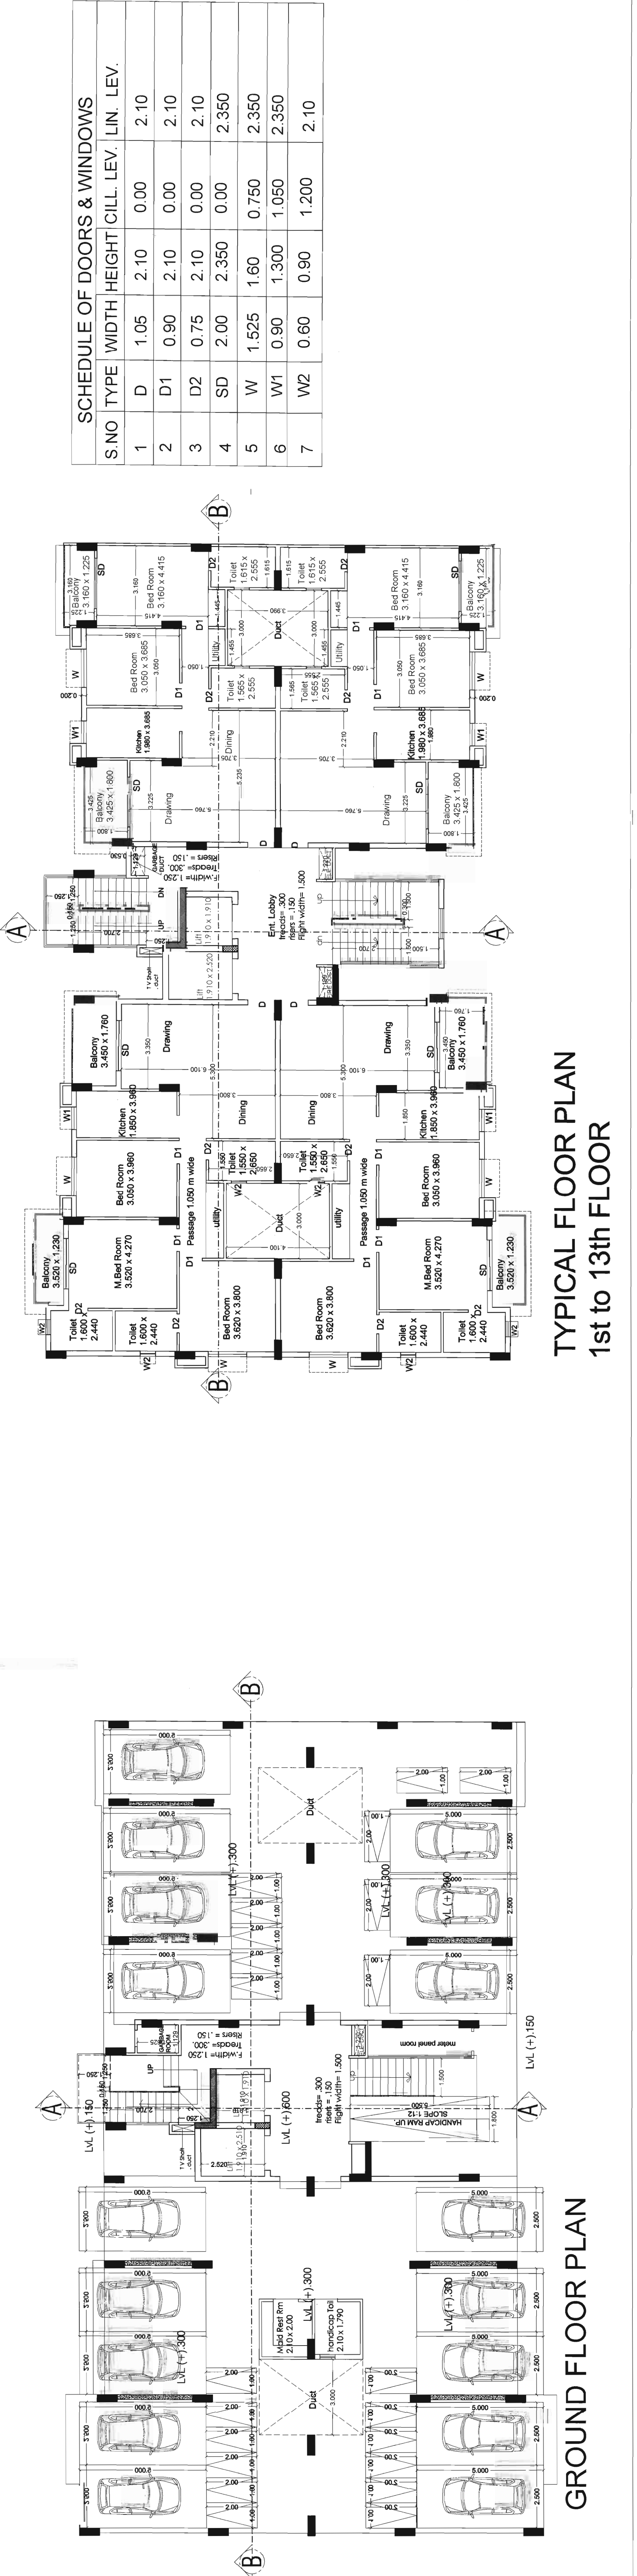
NORTH
variable site plan

Per Ashiana Housing Ltd.
BISWAJIT SENGUPTA
B.Arch, P.E., AEC-C
Regd. Architect, C.A.75886

Regd. Architect
C.A.75886

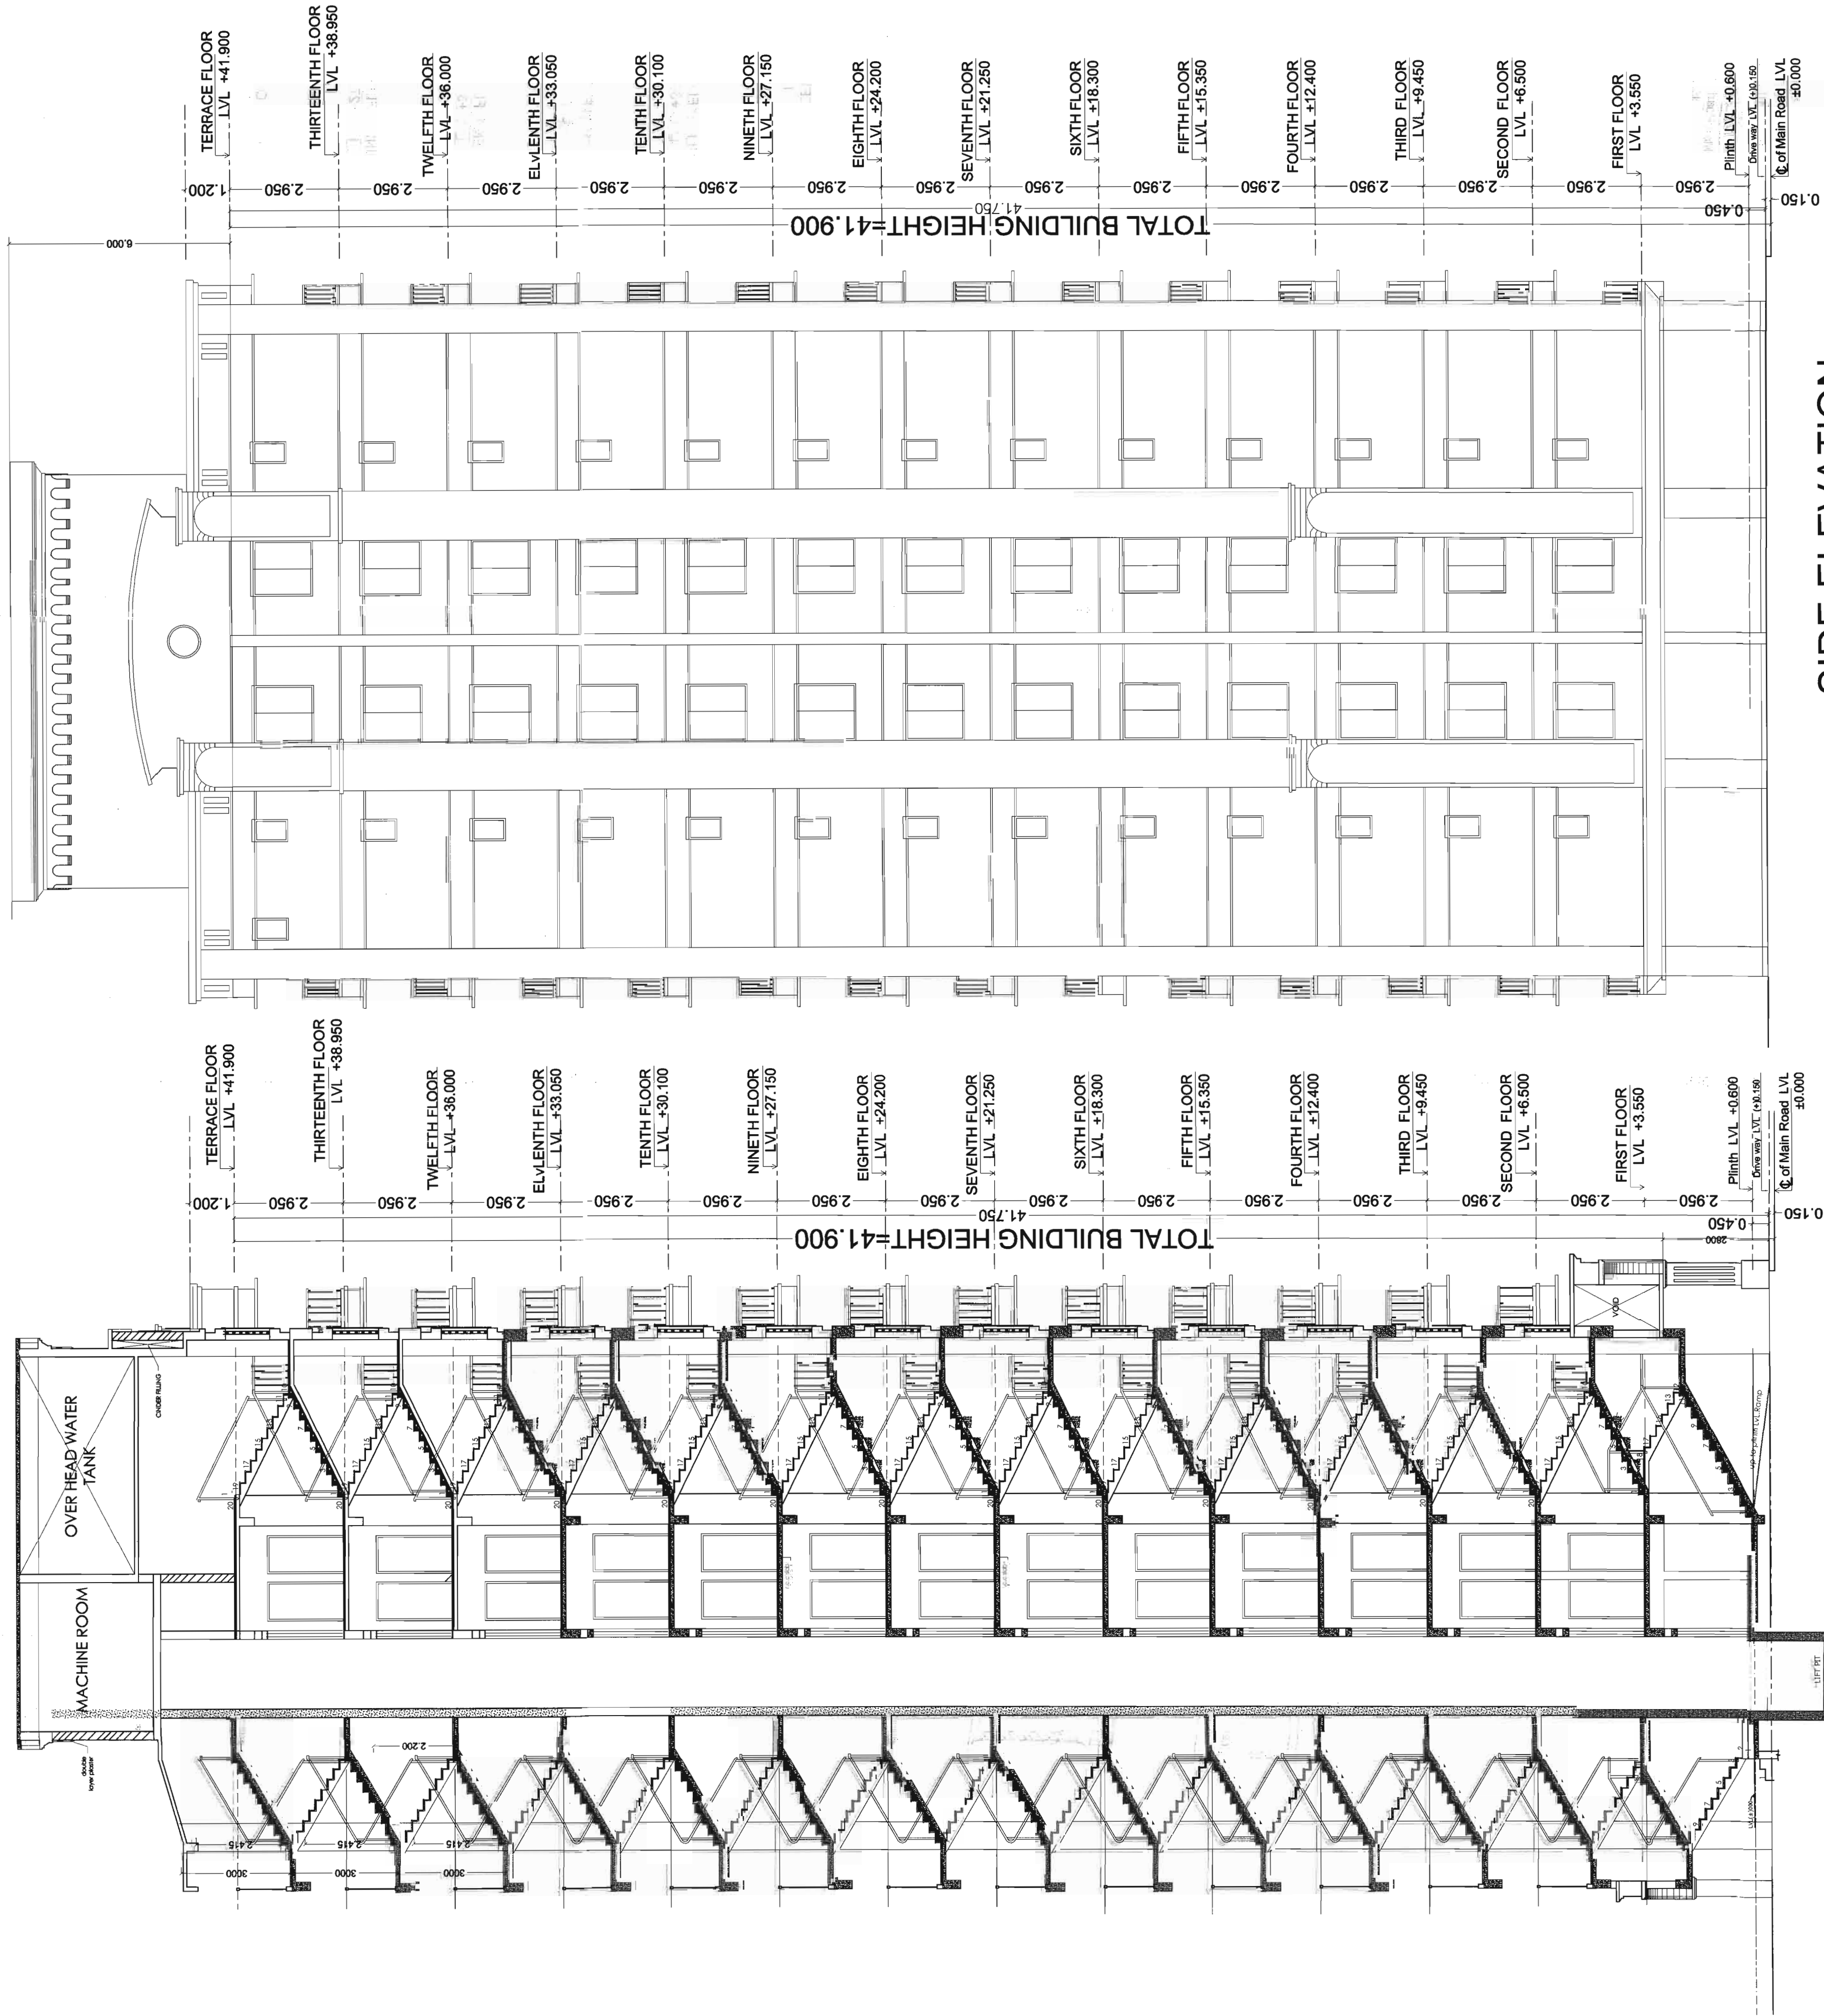
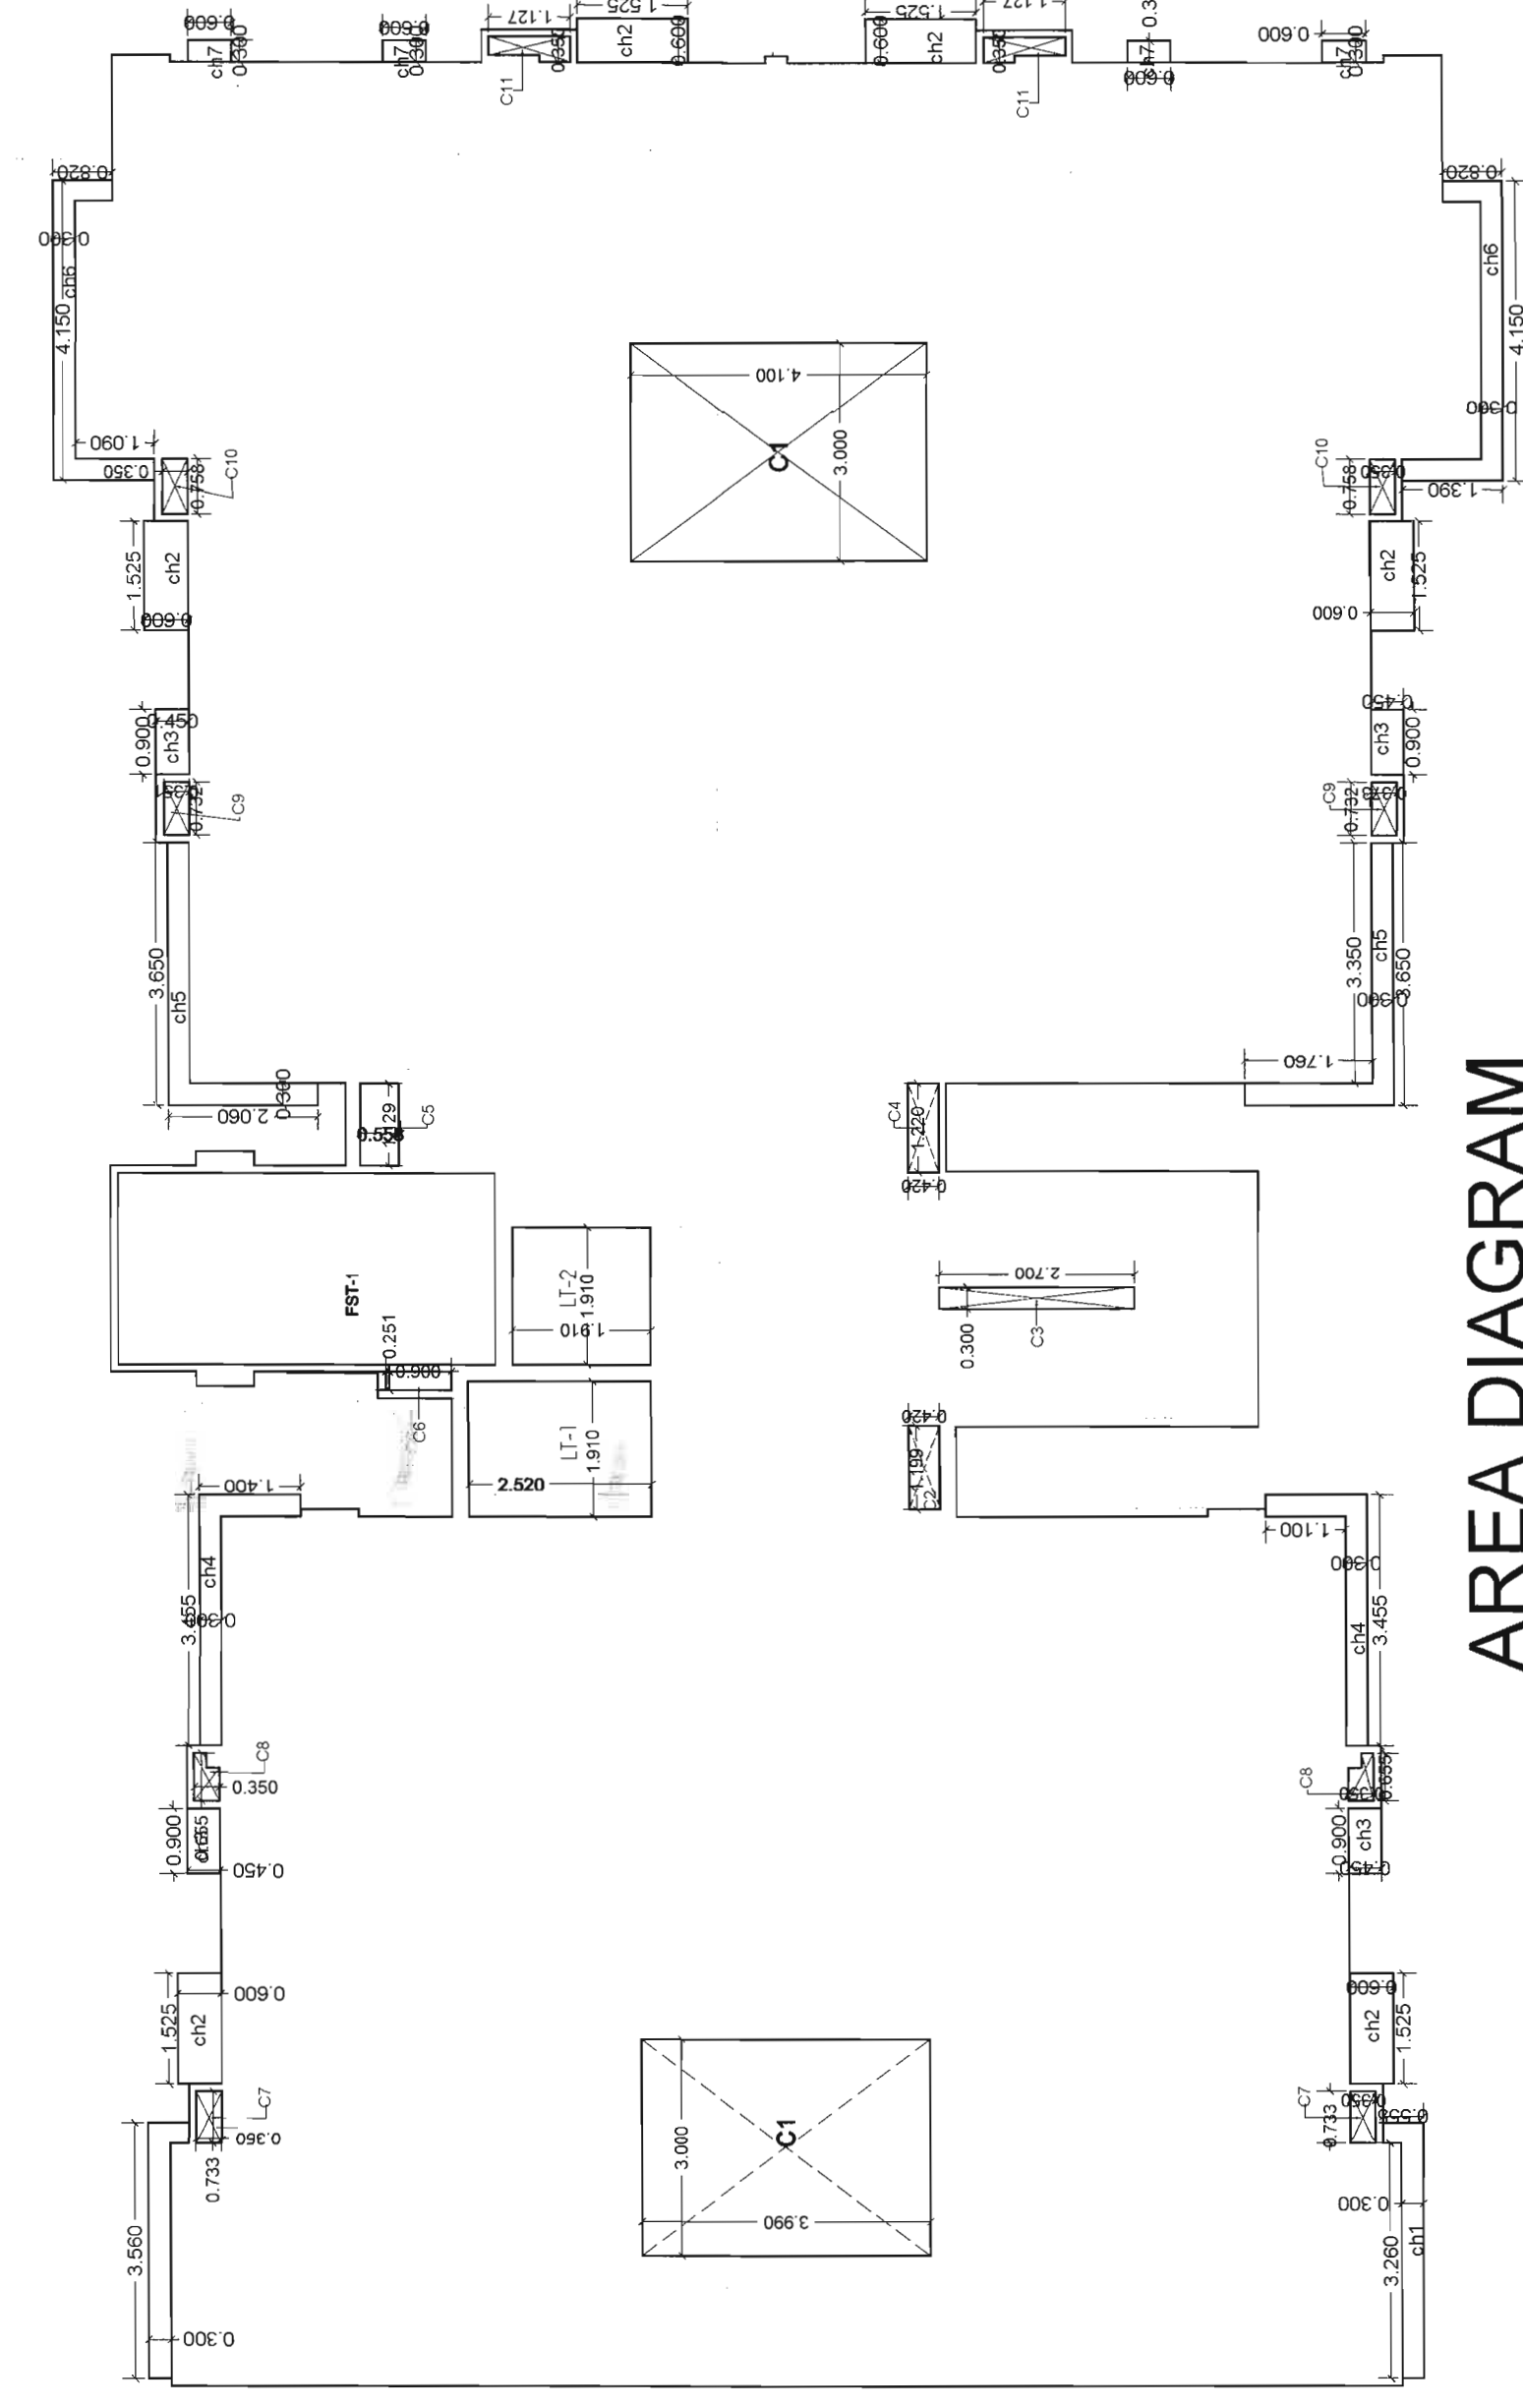
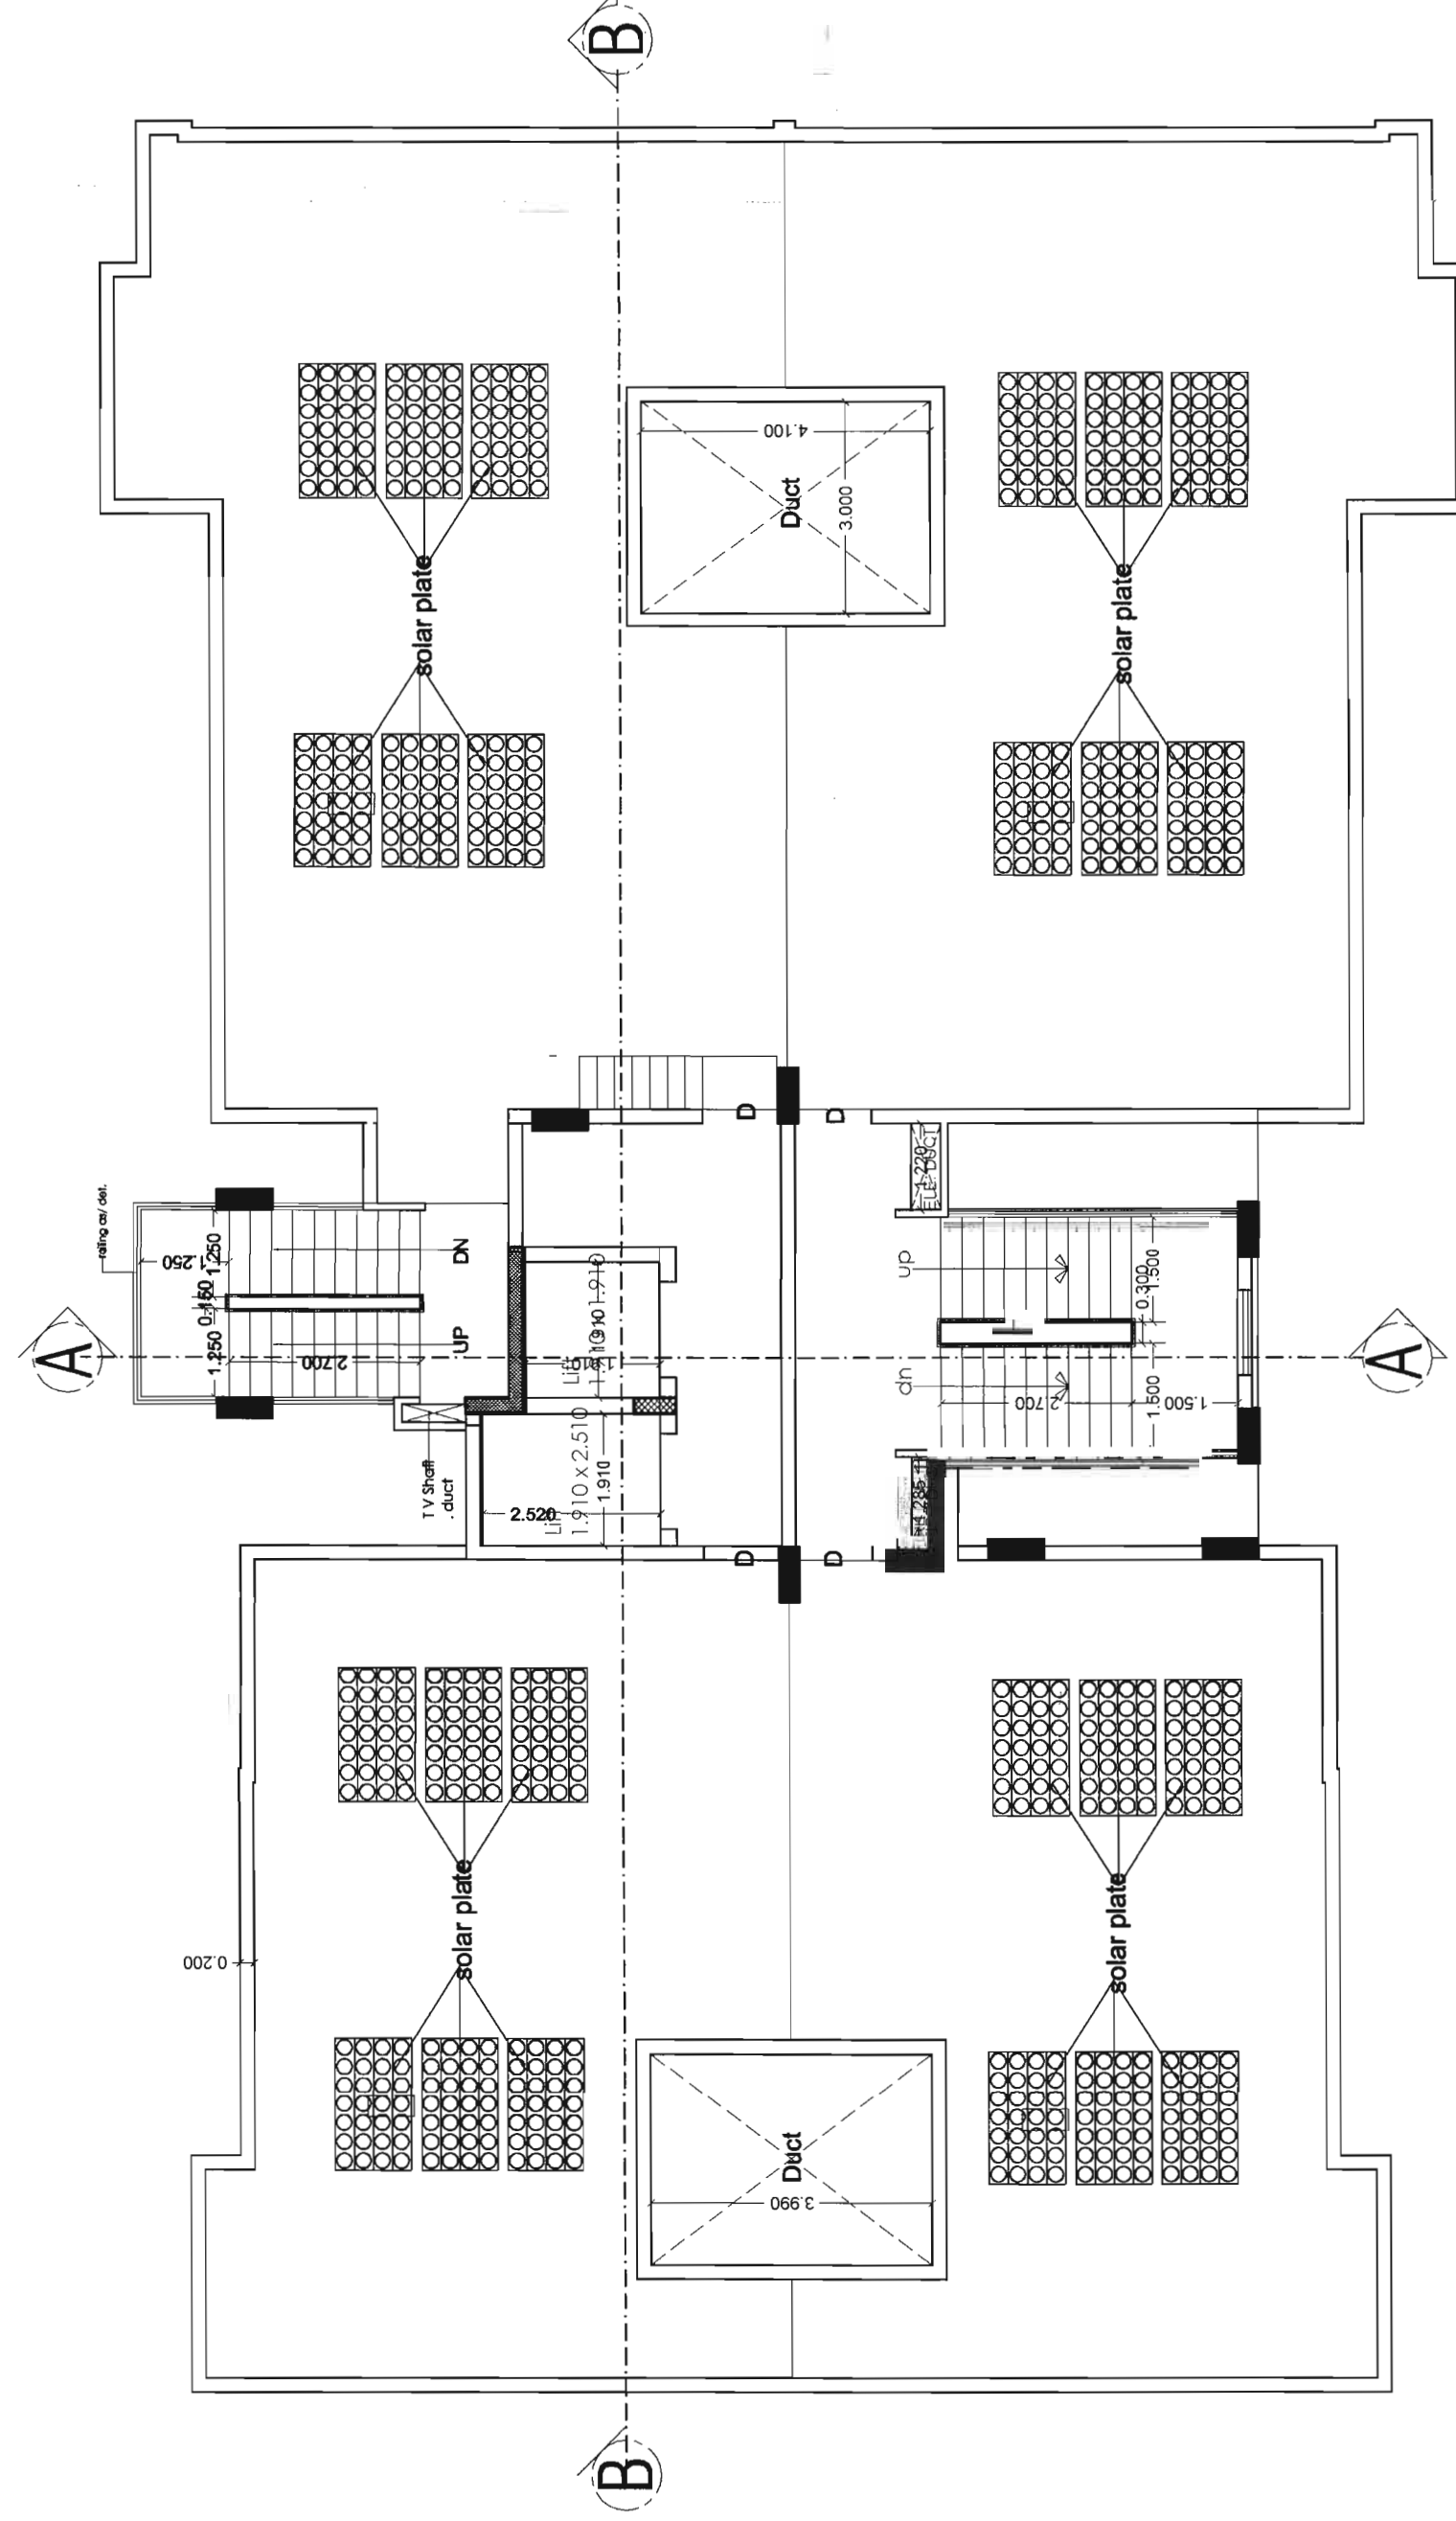
SIGNATURE OF CLIENT

SIGNATURE OF ARCHITECT



SECTION ON A-A

0000-0001-7896-1000

[illegible]

AREA DIAGRAM

KHASRA No.453,454,454/2,454/1,432,433,478,
479,480,484,485,434,434/735,435,436,437,
437/736,438,439,440,482,500,502,503,504/1
478/716 IN VILLAGE JHAJ TEH. SAGANER ON
AJMER ROAD JAIPUR

PROPOSED GROUP HOUSING ASHIANA UMANG

ASHIANA HOUSING LTD.

**TERRACE FLOOR PLAN
AREA DIAGRAM
ELEVATIONS & SECTION**

RESIDENCE

Authorised Signatory
B:Arch, FIA/AAIID
BISWAJIT SENGUPTA

SIGNATURE OF ARCHITECT

SIGNATURE OF ARCHITECT

