

जयपुर विकास प्राधिकरण, जयपुर।

क्रमांक:- ज.वि.प्रा./अति.मु.न.नि./बी.पी.सी.(बीपी)/2023/डी-1042

दिनांक:- 06/9/2023

भवन निर्माण स्वीकृति पत्र

1.	खसरा/भूखण्ड संख्या	खसरा नम्बर 876, 877, 878, 879, 880, 881, 881/2891, 882, 884, 885, 886, 887, 905, ग्राम भांकरोटा कलान, तहसील सांगानेर, जयपुर।
2.	विकासकर्ता का नाम/पता	मैसर्स आशियाना हाउसिंग लिमिटेड, मुख्यारनामा, मैसर्स के.जी.के रियल एस्टेट प्रा.लि., जरिये अधिकृत हस्ताक्षरकर्ता सुश्री समीक्षा बंसल, 401, तृतीय तल, अपेक्स मॉल, लालकोठी, टॉक रोड, जयपुर।
3.	भूखण्ड का क्षेत्रफल	32,693.75 व.मी. 30 मीटर सड़क मार्गाधिकार में समर्पित भूमि = 1001.87 व.मी. 24 मीटर सड़क मार्गाधिकार में समर्पित भूमि = 1291.83 व.मी. नो कन्स्ट्रक्शन सेफ्टी कॉरीडोर = 191.82 व.मी. 5 प्रतिशत सुविधा क्षेत्र हेतु समर्पित भूमि = 1720.72 व.मी.
4.	भूखण्ड के सामने सड़क की चौड़ाई	30 मीटर एवं 24 मीटर
5.	लीजडीड जारी दिनांक	21.10.2013 भू-उपयोग:- आवासीय प्रयोजनार्थ
6.	पुनर्गठित/एकल पट्टा/उप विभाजन	एकल पट्टा
7.	प्रस्तावित भवन मानचित्रों का प्रयोजन	आवासीय (ग्रुप हाउसिंग) प्रयोजनार्थ भवन मानचित्र अनुमोदन बाबत।
8.	वास्तुविद का नाम एवं पंजीयन क्रमांक	श्री रिकी माथुर, सी.ए./24247

अनुमोदित मानदण्ड:-

1.	भवन मानचित्र अनुज्ञा अवधि	भवन मानचित्र अनुज्ञा अवधि मानचित्र जारी होने की दिनांक से 7 वर्ष अर्थात दिनांक 05.09.2030 तक प्रभावी है।
2.	सैटबैक	सामने 15 मी. पार्श्व-I 11.25 मी. पार्श्व-II 9 मी. पीछे 11.25 मी. से 15 मी.
3.	सकल निर्मित क्षेत्रफल	63,091.54 व.मी.
4.	बी.ए.आर.	1.50 (49,283.06 व.मी.)
5.	आच्छादित क्षेत्रफल	27.46 प्रतिशत (8978.88 व.मी.)
6.	ऊँचाई	0.50 मी. (प्लिन्थ) + 3.15 मी. (स्टिल्ट) + 35.40 मी. (प्रथम से 12 तल) कुल 39.05 मीटर
7.	तलों की संख्या	(स्टिल्ट + प्रथम से 12 तल)
8.	पार्किंग	कार स्कूटर बस कुल ईसीयू सरफेस मैकेनिकल 522 - 175 - 580.33

तथ्य:-

1.	प्रथम अनुमोदन/संशोधन	प्रथम अनुमोदन
2.	समिति की बैठक संख्या एवं दिनांक	269वीं बैठक दिनांक 02.03.2023

अनापत्ति प्रमाण पत्र:-

1.	अग्निशमन विभाग	अधिवास प्रमाण पत्र आवेदन के समय प्रस्तुत की जानी है।														
2.	पर्यावरण विभाग का Consent to operate	अधिवास प्रमाण पत्र आवेदन के समय प्रस्तुत की जानी है।														
3.	भारतीय नागरिक उड्डयन विभाग	एयरपोर्ट एन.ओ.सी. दिनांक 22.12.2022 अनुसार 51 मीटर ऊँचाई अनुज्ञेय है, जिसकी वैधता अवधि दिनांक 21.12.2030 तक है। साईट कॉर्डिनेट्स निम्नानुसार है:- <table><tr><td>26 52 17.23 N</td><td>75 40 49.22 E</td></tr><tr><td>26 52 26.39 N</td><td>75 40 50.40 E</td></tr><tr><td>26 52 16.84 N</td><td>75 40 52.08 E</td></tr><tr><td>26 52 20.91 N</td><td>75 40 55.53 E</td></tr><tr><td>26 52 23.10 N</td><td>75 40 55.68 E</td></tr><tr><td>26 52 19.19 N</td><td>75 40 57.75 E</td></tr><tr><td>26 52 22.51 N</td><td>75 40 58.55 E</td></tr></table>	26 52 17.23 N	75 40 49.22 E	26 52 26.39 N	75 40 50.40 E	26 52 16.84 N	75 40 52.08 E	26 52 20.91 N	75 40 55.53 E	26 52 23.10 N	75 40 55.68 E	26 52 19.19 N	75 40 57.75 E	26 52 22.51 N	75 40 58.55 E
26 52 17.23 N	75 40 49.22 E															
26 52 26.39 N	75 40 50.40 E															
26 52 16.84 N	75 40 52.08 E															
26 52 20.91 N	75 40 55.53 E															
26 52 23.10 N	75 40 55.68 E															
26 52 19.19 N	75 40 57.75 E															
26 52 22.51 N	75 40 58.55 E															

सामान्य शर्तः—

प्रकरण भवन मानचित्र समिति (बीपी) की 269वीं बैठक दिनांक 02.03.2023 में प्रस्तुत किया गया, जिस अनुसार कुल 0.50 मी. (फ्लिन्थ) + 3.15 मी. (स्टिल्ट) + 41.30 मी. (प्रथम से 14 तल) = 44.45 मी. + 5.60 मी. (मशीन रूम/ममटी/वाटर टैंक) कुल 50.55 मीटर ऊँचाई व सकल निर्मित क्षेत्रफल 70,720.36 वर्गमीटर के भवन मानचित्र अनुमोदन किये जाने का निर्णय लिया गया, किन्तु प्रकरण में भवन की ऊँचाई 40 मीटर से अधिक होने के कारण राज्य सरकार की स्वीकृति आवश्यक है। आप द्वारा संदर्भित प्रतिवेदन प्रस्तुत कर राज्य सरकार से स्वीकृति प्राप्त होने तक 0.50 मी. (फ्लिन्थ) + 3.15 मी. (स्टिल्ट) + 35.40 मी. (प्रथम से 12 तल) कुल 39.05 मीटर ऊँचाई के मानचित्र जारी किये जाने का निवेदन किया गया है। अतः प्रस्तुत प्रतिवेदन के क्रम में **0.50 मी. (फ्लिन्थ) + 3.15 मी. (स्टिल्ट) + 35.40 मी. (प्रथम से 12 तल) कुल 39.05 मीटर ऊँचाई** के भवन मानचित्र बी.पी.सी. (बी.पी.) की 269वीं बैठक दिनांक 02.03.2023 के निर्णयानुसार निम्न शर्तों के साथ निर्माण स्वीकृति दी जाती है—

1. निर्माण कार्य प्रारम्भ करने से पूर्व आप उपायुक्त जोन-12, प्राधिकरण को निर्धारित प्रपत्र में सूचना प्रस्तुत करेंगे।
2. स्वीकृत मानचित्र मौके पर उपयुक्त स्थान पर बोर्ड लगाकर उस पर स्पष्ट रूप से दर्शाने होंगे।
3. निर्माण स्थल पर स्वीकृति का विवरण अर्थात् अनुमोदित मानचित्र, उपलब्ध पार्किंग की सूचना एवं भवन में सुरक्षा एवं निकास प्लान (Escape Plan) का नक्शा भी प्रदर्शित (Display) उपयुक्त स्थान पर प्रदर्शित किया जावे।
4. भवन का उपयोग प्रारम्भ होने पर एक केयर टेकर की नियुक्ति की जावे जिसके पास भवन का मानचित्र, सुरक्षा एवं निकास प्लान (Escape Plan) उपलब्ध रहें। इस प्रकार नियुक्त केयर टेकर के मोबाईल नंबर एवं Land Line Number भी लिये जाकर पुलिस आयुक्त जयपुर महानगर व उपायुक्त जोन को सूचना उपलब्ध करवाई जावे ताकि किसी भी दुर्घटना की स्थिति में बचाव कार्य प्रभावी रूप से किये जा सकें।
5. विकासकर्ता द्वारा भवन के परिसर को स्वीकृत मानचित्र में दर्शित/निर्धारित अनुसार ही उपयोग में लिया जावेगा।
6. भवन विनियम 2020 के प्रावधान संख्या 10.3.2(x) के अनुसार भवन में अपेक्षित सेवाओं यथा प्रस्तावित जल वितरण प्रणाली, जल मल निकासी प्रणाली, विद्युत सेवाएँ, वातानुकूल सेवाएँ आदि से संबंधित मानचित्रों के दो सैट जो कि आवेदित परियोजना की डिजाईन व निर्माण की क्रियान्विति हेतु अनुबंधित किये गये काउंसिल ऑफ आर्किटेक्चर से रजिस्टर्ड आर्किटेक्ट एवं परियोजना के स्ट्रक्चरल इंजीनियर से ही प्रमाणित किये हुये, अधिकतम 90 दिवस की अवधि में उपलब्ध करवाया जाना आवश्यक होगा।
7. प्रकरण बहुमंजिला भवन होने के कारण भवन विनियम 2020 के प्रावधान संख्या 10.3.2(xi) के अनुसार आप द्वारा भवन में अग्निशमन संबंधित प्रावधान एन.बी.सी. के अनुसार रखे जाने आवश्यक होंगे जिसकी समस्त जिम्मेदारी आपकी होगी। भवन निर्माण पूर्ण हो जाने के पश्चात् अधिवास प्रमाण-पत्र जारी करने से पूर्व अग्निशमन अनापत्ति प्रमाण-पत्र एवं पर्यावरण विभाग का अनापत्ति प्रमाण पत्र प्रस्तुत करना होगा।
8. परियोजना में भूखण्ड के क्षेत्रफल, प्रस्तावित सकल निर्मित क्षेत्रफल एवं ऊँचाई अनुसार भवन विनियम 2020 से संबंधित प्रावधान संख्या 10.11 (पर्यावरण संरक्षण हेतु नियम), नियम 10.11.1 (वर्षा जल संग्रहण), 10.11.2 व नववि के आदेश दिनांक 07.09.2021 (अपशिष्ट जल का शुद्धिकरण एवं रिसाईकिलिंग हेतु प्रावधानों की अनुपालना) 10.11.3 (पर्यावरण हेतु वृक्षारोपण), 10.11.4 (सॉलिड वेस्ट डिस्पोजल), 10.11.5 (सौर ऊर्जा संयंत्र), 10.11.2.5 व 16.3 (सीवरेज ट्रीटमेन्ट प्लान्ट), 12.1 (पार्किंग क्षेत्र की पालना), 12.3 (विद्युत आवश्यक की पूर्ति हेतु संबंधित विद्युत वितरण एजेन्सी के प्रावधान), विनियम संख्या 15 (निर्माण कार्य के दौरान अपनाई जाने वाली प्रक्रिया), नियम संख्या 15.5 (भवन विनियम के अपेक्षाओं के अनुरूप भवन निर्माण) के प्रावधानों की अनुपालना की जानी होगी।
9. भवन विनियम 2020 के प्रावधान संख्या 12.1.4 (अ) के अनुसार आवश्यक पार्किंग का 10 प्रतिशत EV Charging Facility के प्रावधान की मौके पर सुनिश्चितता की जावेगी।
10. भवन में RPWD Act 2016, UNCRPD Act 2006 एवं प्रचलित भवन विनियम में विनिर्दिष्ट धाराओं के अनुसार विशेष योग्यजनों के लिए आवश्यक मापदण्ड/सुविधाओं/साईन बोर्ड/दिशा निर्देशों की पालना सुनिश्चित की जानी होगी।
11. नगरीय विकास विभाग, राजस्थान सरकार के आदेश दिनांक 14.12.2022 के अनुसार भवन विनियम 2020 के प्रावधान संख्या 12.4 के अनुसार भवन में Common Telecom Infrastructure (CTI) के प्रावधान की पालना सुनिश्चित की जानी होगी।
12. नगरीय विकास विभाग, राजस्थान सरकार के आदेश दिनांक 10.08.2023 के अनुसार भूखण्ड से लगती हुई सम्पूर्ण सभी सड़कों का विकास, फुटपाथ एवं वृक्षारोपण का प्रावधान स्वयं के व्यय पर सुनिश्चित किया जाना होगा।
13. नगरीय विकास विभाग, राजस्थान सरकार के आदेश दिनांक 10.08.2023 के अनुसार भवन में प्रत्येक लिफ्ट में ए. आर.डी. (Automatic Rescue Device) सिस्टम का प्रावधान रखा जाना होगा।
14. आकाशीय बिजली से बचाव हेतु भवन में Thunder stick (तडित चालक) का प्रावधान रखा जाना अनिवार्य होगा।

15. भवन परिसर में आगंतुकों की पार्किंग उपलब्ध करवाई जाए तथा आगंतुकों हेतु निःशुल्क वाहन पार्किंग का बोर्ड लगवाया जावे।
16. निर्मित भवन के प्रवेश द्वार के पास भवन में अनुमोदित व उपलब्ध चार पहिया व दो पहिया वाहनों के पार्किंग की सूचना का बोर्ड (डिस्प्ले) लगवाया जावे।
17. भवन विनियम 2020 के विनियम संख्या 18.3 की अनुपालना में "गलत तथ्यों पर प्राप्त की गई अथवा तथ्यों को छुपाकर प्राप्त की गई स्वीकृति स्वतः निरस्त मानी जायेगी एवं ऐसी निर्माण स्वीकृति प्राप्त करने के लिए आवेदनकर्ता को दोषी माना जायेगा।"
18. प्रश्नगत प्रकरण किसी भी न्यायालय में यदि लंबित है तो उसकी समस्त जिम्मेदारी आवेदक की ही होगी। यदि मानचित्र जारी होने के पश्चात यह अवगत हुआ कि किसी भी माननीय न्यायालय में प्रकरण लंबित है अथवा विपरीत निहित है तो मानचित्र स्वतः ही निरस्त समझे जावेंगे।
19. उक्त स्वीकृति के कारण यदि जयपुर विकास प्राधिकरण को किसी न्यायालय, सक्षम अधिकारी तथा नगर भूमि (अधिकतम सीमा एवं विनियम) अधिनियम के तहत नियुक्त अधिकारी के समक्ष किसी कार्यवाही में कोई भी खर्च, नुकसान, मुआवजा देना पड़े या देने योग्य हो तो प्रार्थी उनकी इस क्षति को पूर्ण करने के लिए बाध्य होगा।
20. तकनीकीविज्ञ के निरीक्षण में स्वामी निर्माण कार्य करवायेगा जिसके संबंध में सूचना प्राधिकरण को पूर्व में देनी होगी। यदि तकनीकीविज्ञ को बदला जाता है तो इसकी सूचना 48 घन्टे के अन्दर यथोचित प्रमाण-पत्र में प्राधिकरण को देनी होगी।
21. भवन मानचित्र इस शर्त के साथ जारी किये जाते हैं कि आप द्वारा परियोजना का निर्माण कार्य पूर्ण किये जाने के पश्चात नियमानुसार पूर्णता एवं अधिवास प्रमाण पत्र प्राप्त किया जाना आवश्यक है।
22. यह भवन निर्माण स्वीकृति स्वामित्व का दस्तावेज नहीं है।

विशेष शर्त:-

1. जोन की रिपोर्ट दिनांक 14.06.2022 अनुसार प्रशासन शहरों के संग अभियान के अन्तर्गत भवन निर्माण अवधि दिनांक 31.03.2023 तक देय थी। किन्तु नववि के आदेश दिनांक 31.03.2023 अनुसार भवन निर्माण अवधि में दिनांक 30.09.2023 तक छूट दिये जाने के आदेश प्रदान किये गये हैं। अतः भवन निर्माण अवधि में दिनांक 30.09.2023 तक देय होगी।
 2. यह भवन अनुज्ञा अवधि, भवन मानचित्र जारी की दिनांक से 7 वर्ष अर्थात् दिनांक 05.09.2030 तक प्रभावी है।
- संलग्न:- मानचित्रों की प्रति का 1 सेट (28 मानचित्र)**


भवदीय,


 अतिरिक्त मुख्य नगर नियोजक,
 भवन मानचित्र समिति (बीपी)
 जयपुर विकास प्राधिकरण, जयपुर।


प्रतिलिपि:- सूचनार्थ एवं आवश्यक कार्यवाही हेतु।

1. मुख्य नियन्त्रक (प्रवर्तन), जयपुर विकास प्राधिकरण, जयपुर को मानचित्रों की प्रति (28 मानचित्र) संलग्न कर अग्रिम कार्यवाही हेतु प्रेषित है।
2. उपायुक्त, जोन-12, जयपुर विकास प्राधिकरण, जयपुर को मानचित्रों की प्रति (28 मानचित्र) संलग्न कर अग्रिम कार्यवाही हेतु प्रेषित है।
3. प्रबंध निदेशक, जयपुर विद्युत वितरण निगम लि0, विद्युत भवन जनपथ, जयपुर को सूचनार्थ प्रेषित है।
4. मुख्य अभियन्ता, मुख्यालय जन स्वास्थ्य अभियांत्रिकी विभाग हसनपुरा रोड, रेल्वे हॉस्पिटल के पास, जयपुर को सूचनार्थ प्रेषित है।
4. उपायुक्त राजस्व-प्रथम, नगर निगम, जयपुर को पत्र क्रमांक एफ. 60/उपा. रा (प्रथम)/जननि/2019/18 दिनांक 08.03.2019 के क्रम में सूचनार्थ प्रेषित है।
5. श्री विष्णु मोहन झा, चीफ एयरपोर्ट अधिकारी, जयपुर इन्टरनेशनल एयरपोर्ट, जयपुर को पत्र क्रमांक 5253-56 दिनांक 22.12.2022 के क्रम में सूचनार्थ प्रेषित है।

अतिरिक्त मुख्य नगर नियोजक,
 भवन मानचित्र समिति (बीपी)
 जयपुर विकास प्राधिकरण, जयपुर।

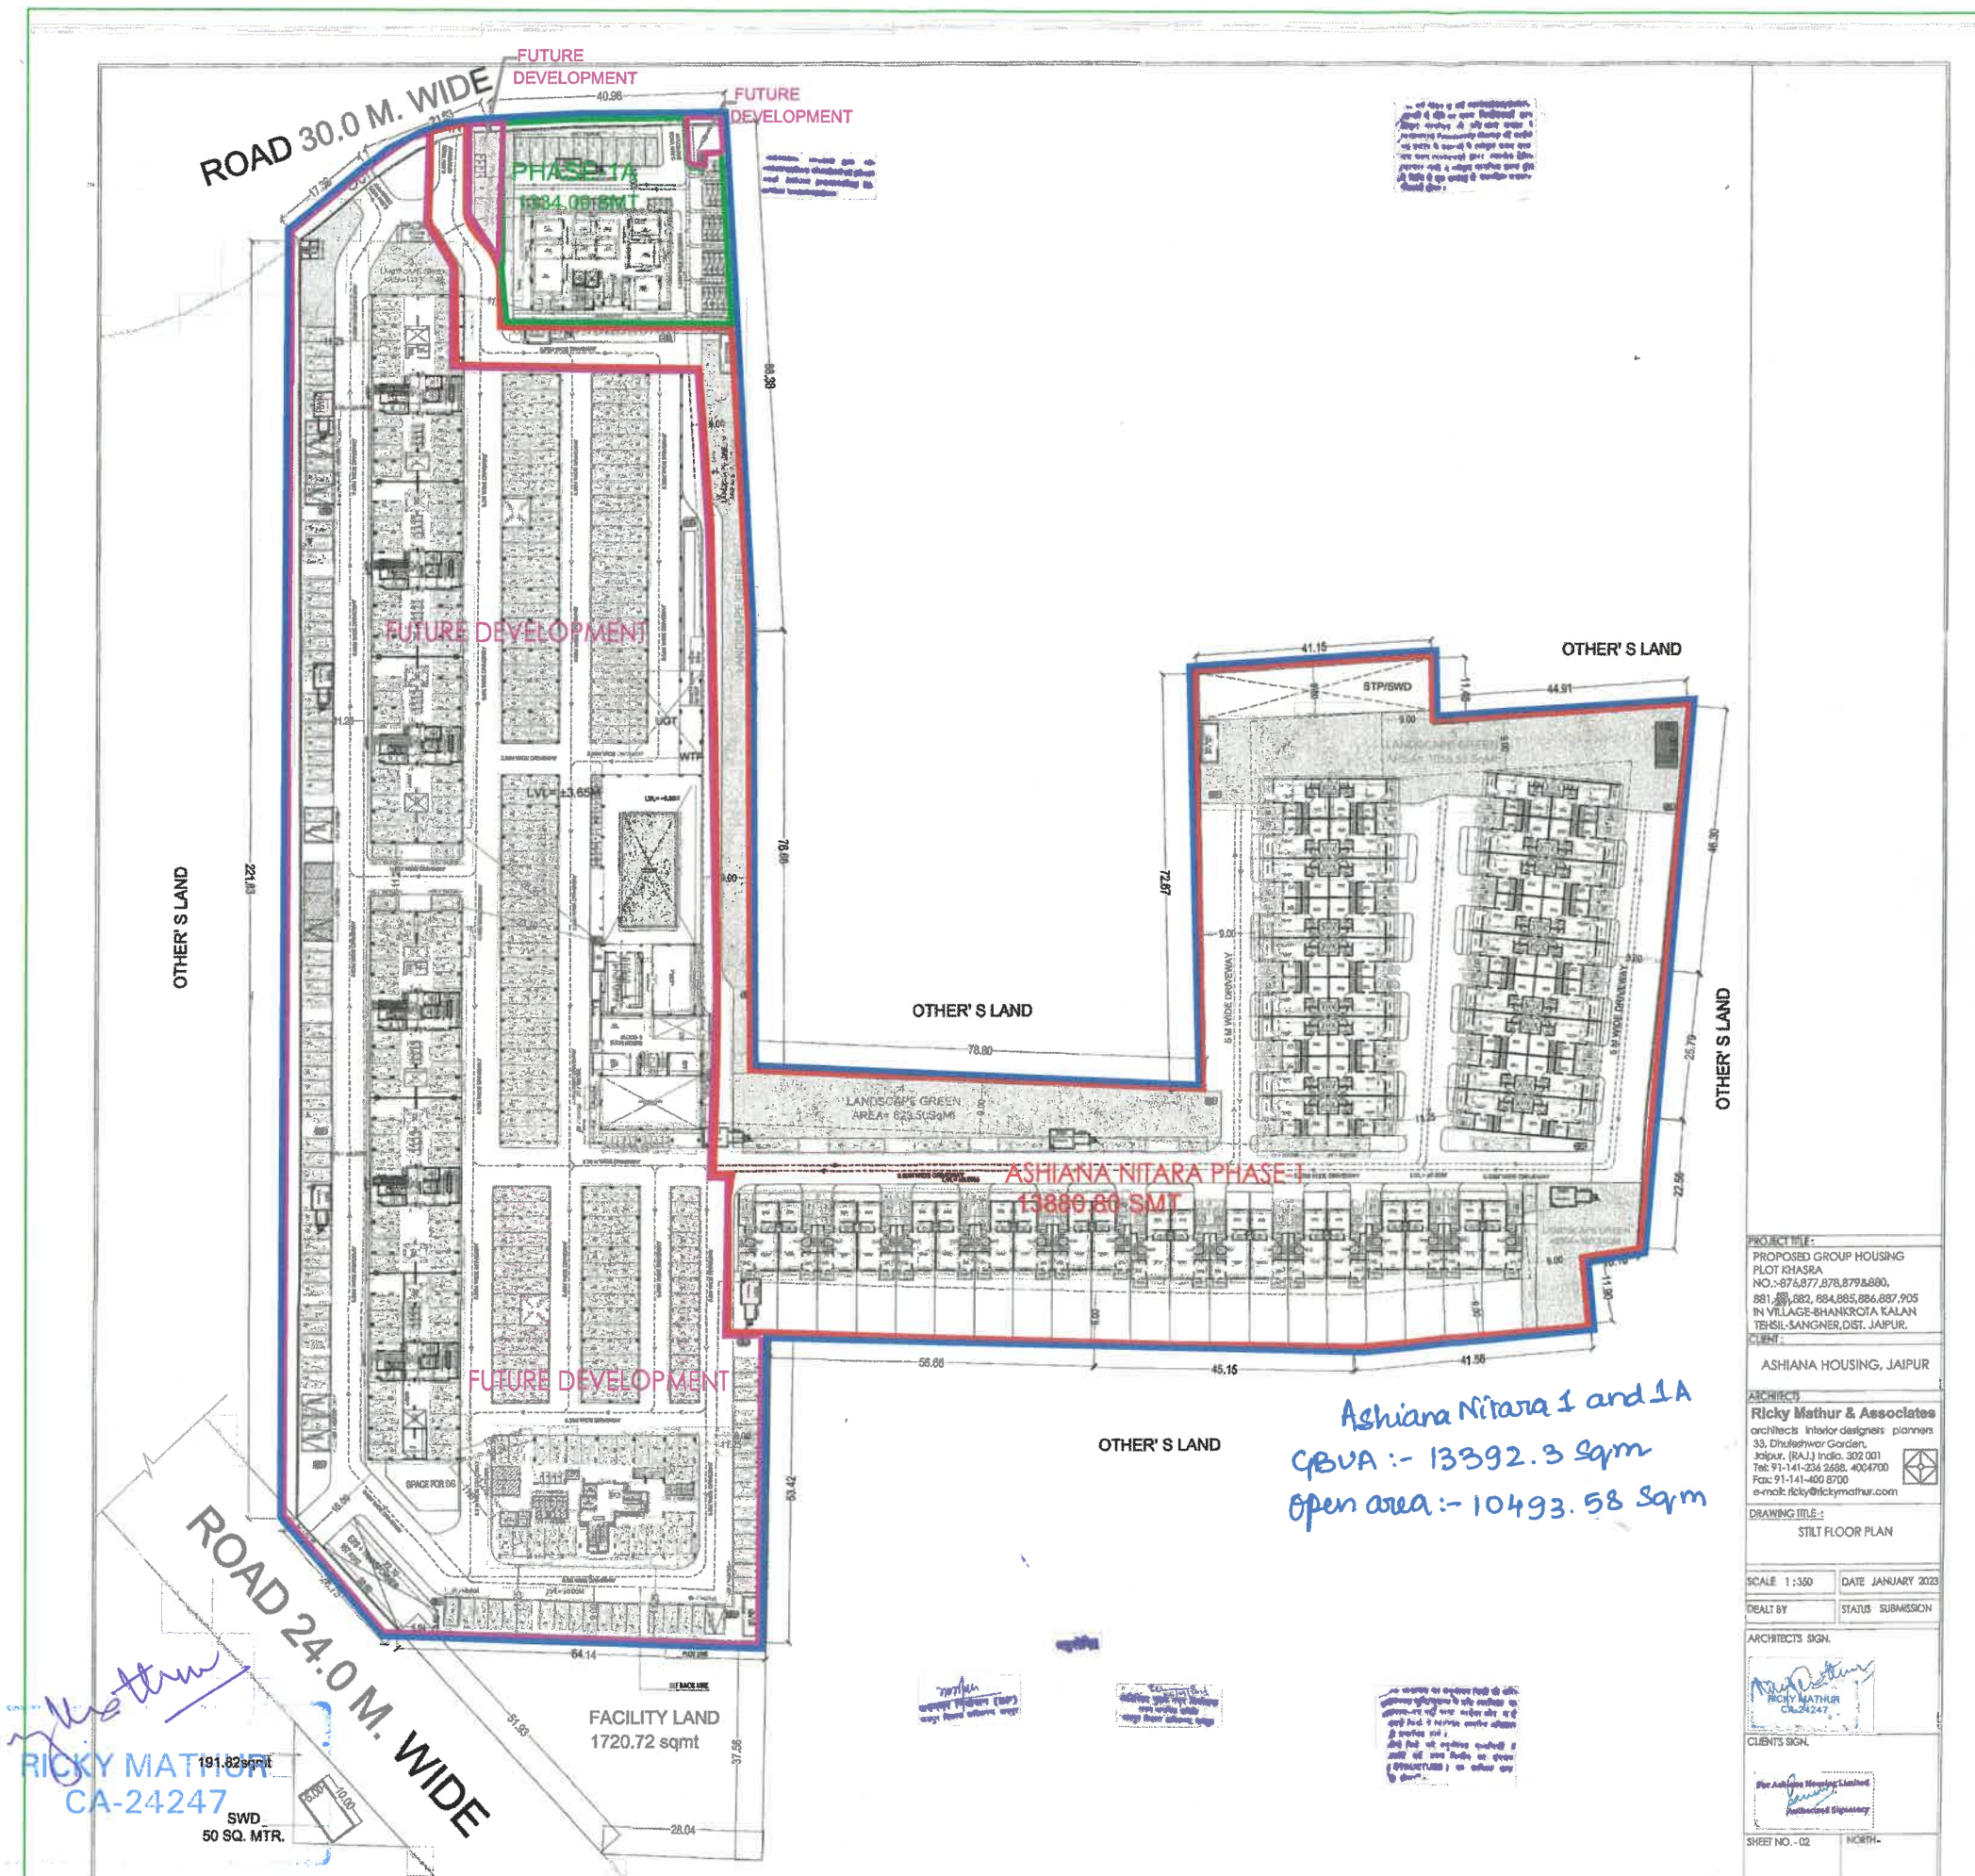

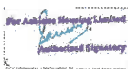PROJECT TITLE :	
PROPOSED GROUP HOUSING PLOT KHASRA NO.-87,877,878,879,880, 881,882,884,885,886,887,905 IN VILLAGE-BHANKOTA KALAN TEHSIL-SANGNER,DIST. JAIPUR.	
CLIENT :	
ASHIANA HOUSING, JAIPUR	
ARCHITECT :	
Ricky Mathur & Associates architects interior designers planners 33, Dhruveshwar Garden, Jaipur, (RAJ.) India. 302 001 Tel: 91-141-234 2688, 4004700 Fax: 91-141-400 8700 e-mail: ricky@rickymathur.com	
DRAWING TITLE :	
STILT FLOOR PLAN	
SCALE 1:350	DATE JANUARY 2023
DEALT BY	STATUS SUBMISSION
ARCHITECTS SIGN.	
 RICKY MATHUR CA-24247	
CLIENT'S SIGN.	
 Ashiana Housing Limited Authorized Signatory	
SHEET NO. - 02	NORTH

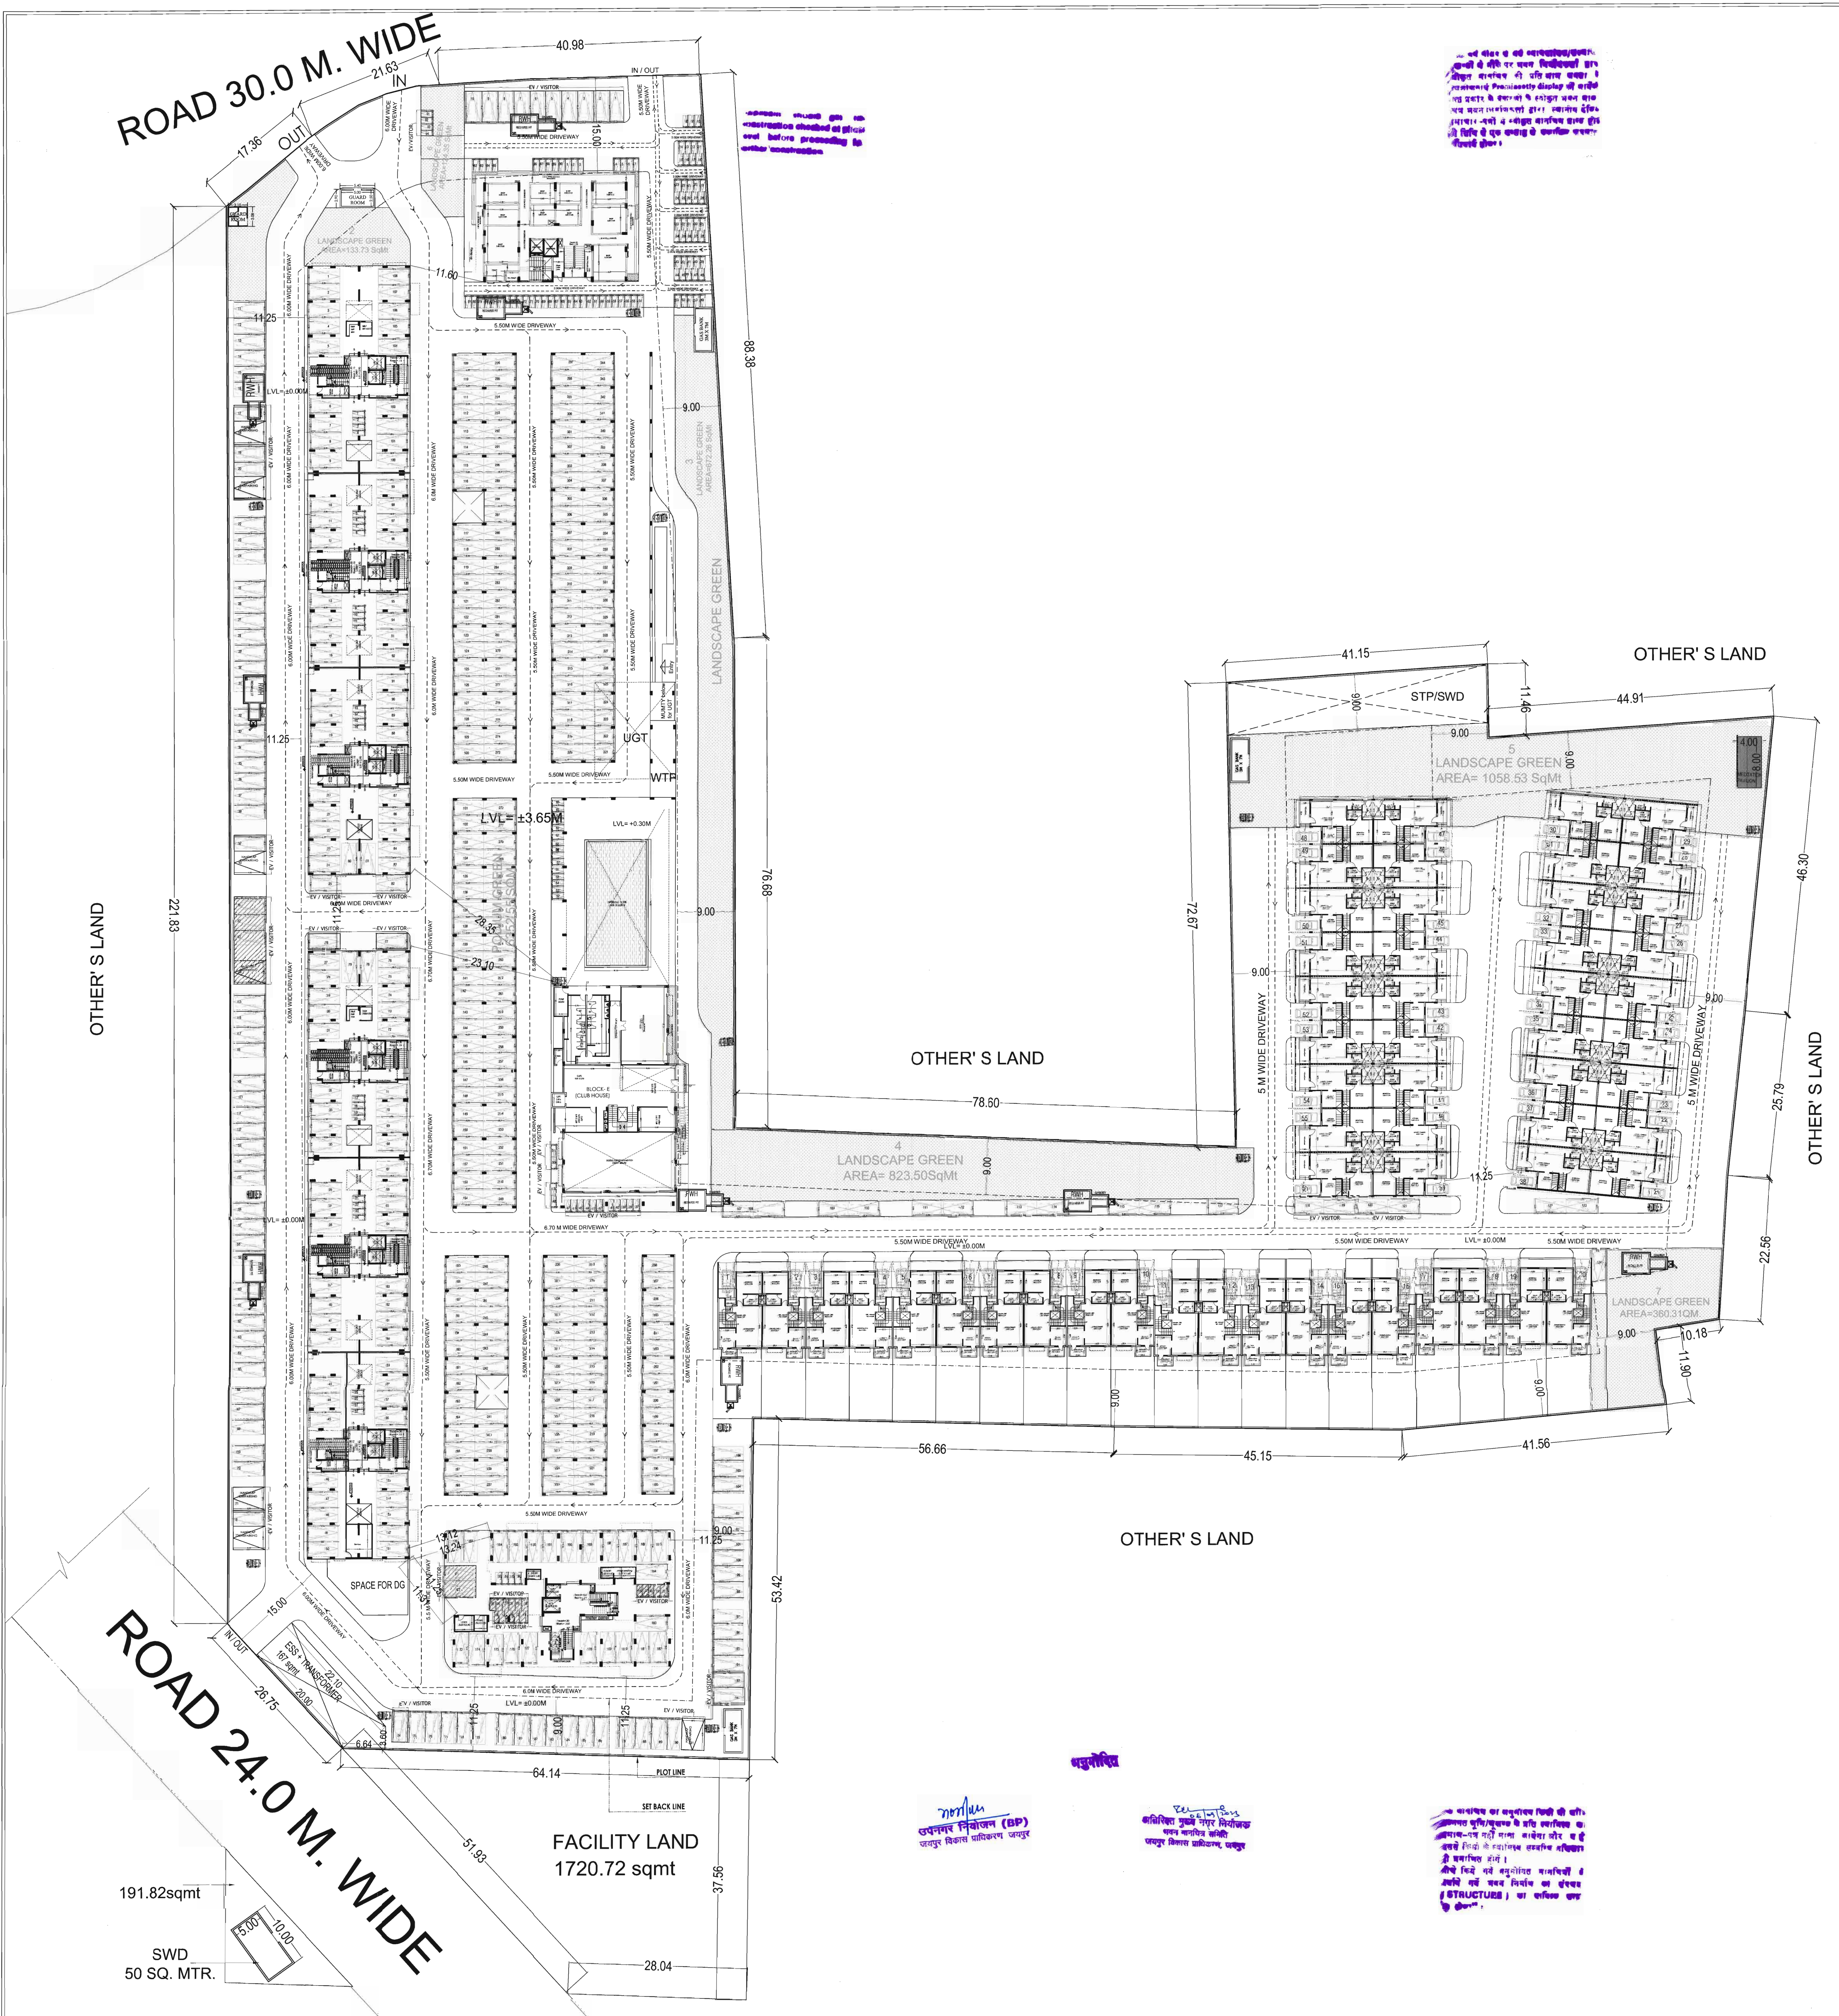

PROJECT TITLE :
PROPOSED GROUP HOUSING
PLOT KHASRA
NO.-876,877,878,879&880,
881,882,884,885,886,887,905
IN VILLAGE-BHANKROTA KALAN
TEHSIL-SANGNER,DIST. JAIPUR.

CLIENT :
ASHIANA HOUSING, JAIPUR

ARCHITECTS
Ricky Mathur & Associates
architects interior designers planners
33, Dhuleshwar Garden,
Jaipur. (RAJ.) India-302 001
Tel: 91-141-236 2688, 4004700
Fax: 91-141-400 8700
e-mail: ricky@rickymathur.com

DRAWING TITLE :-
STILT FLOOR PLAN

SCALE 1 : 350 DATE JANUARY 2023


DEALT BY STATUS SUBMISSION

ARCHITECT'S SIGN.


CLIENTS SIGN.

For Ashiana Housing Limited
Authorized Signatory


SHEET NO. - 02 NORTH -

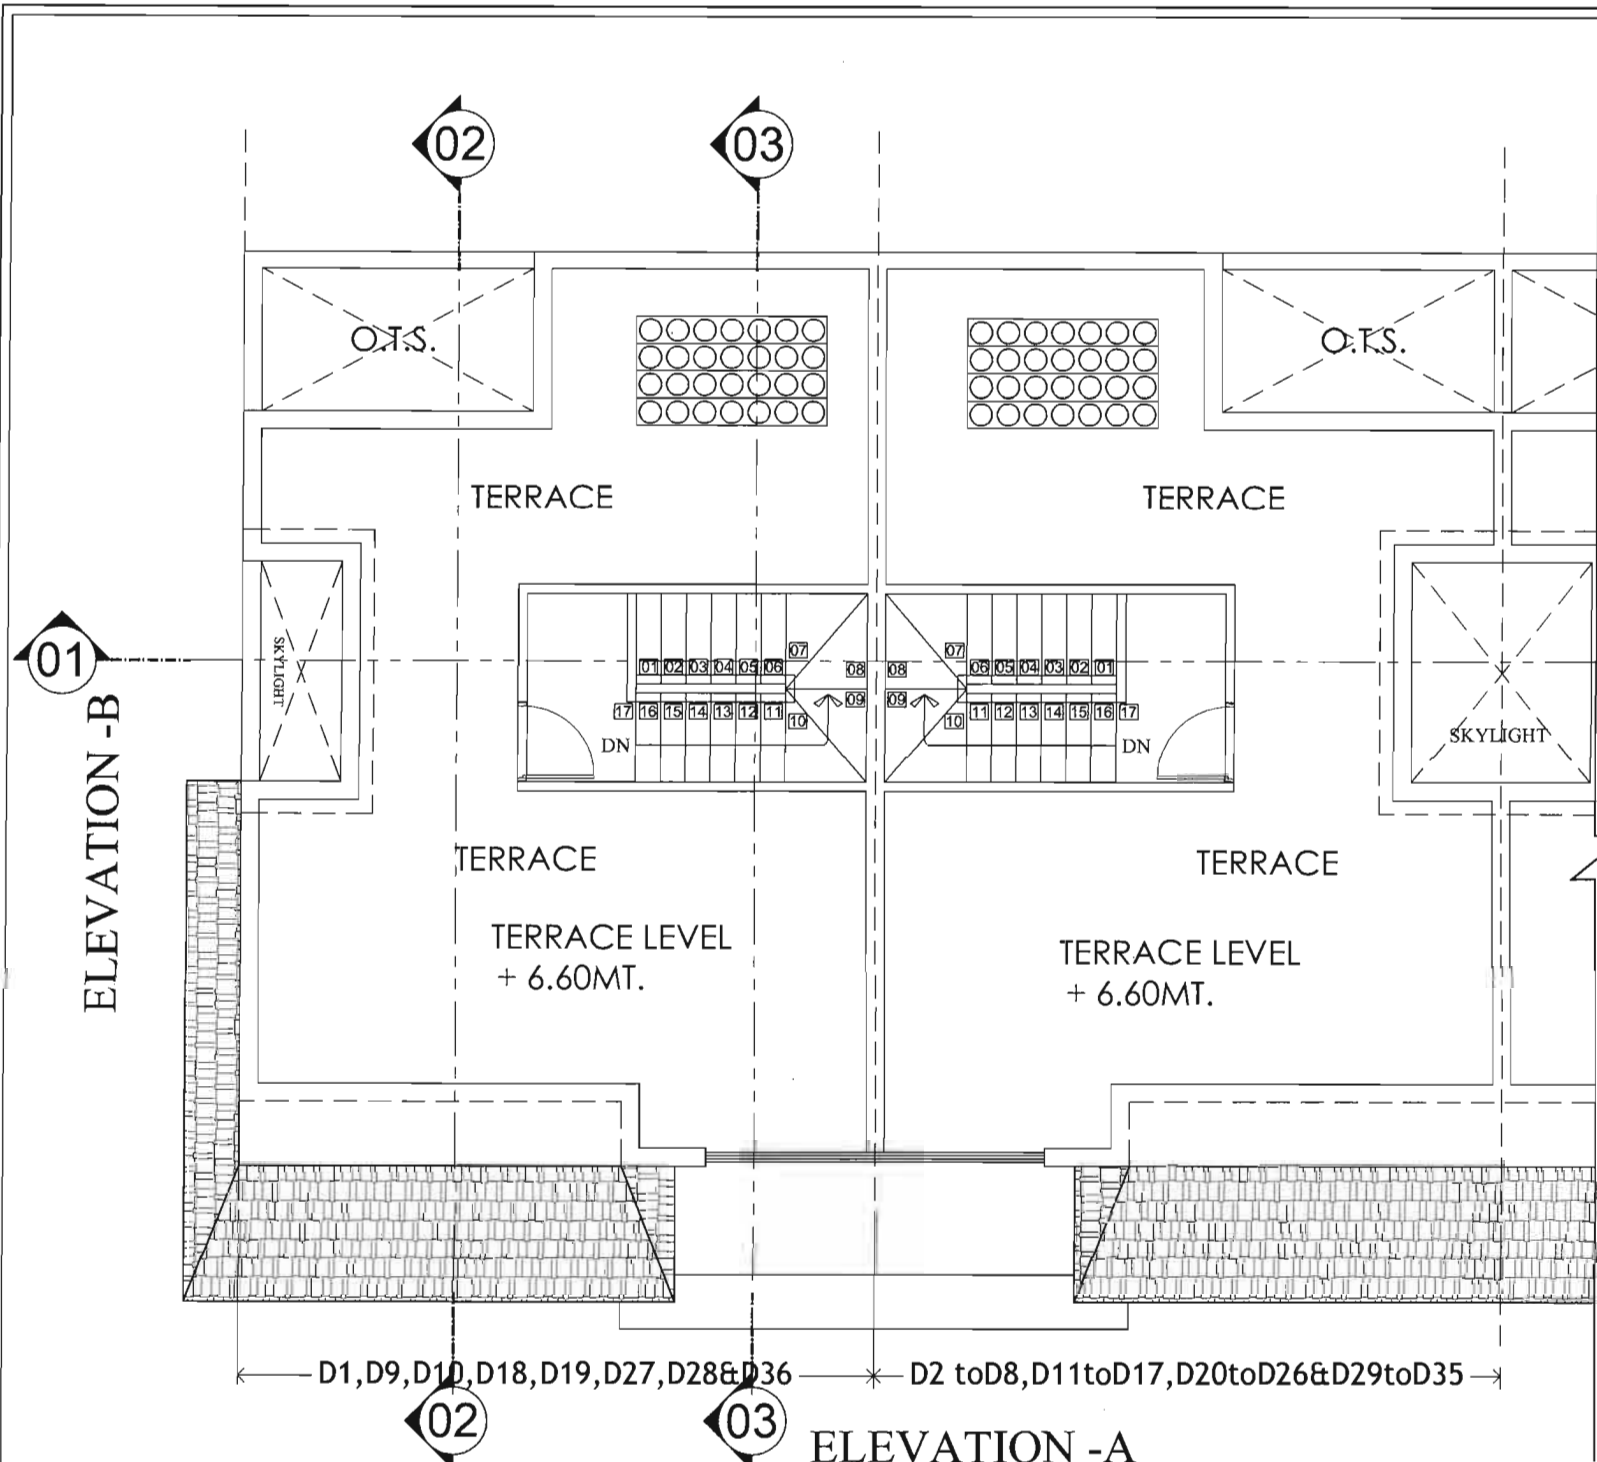

TERRACE FLOOR PLAN

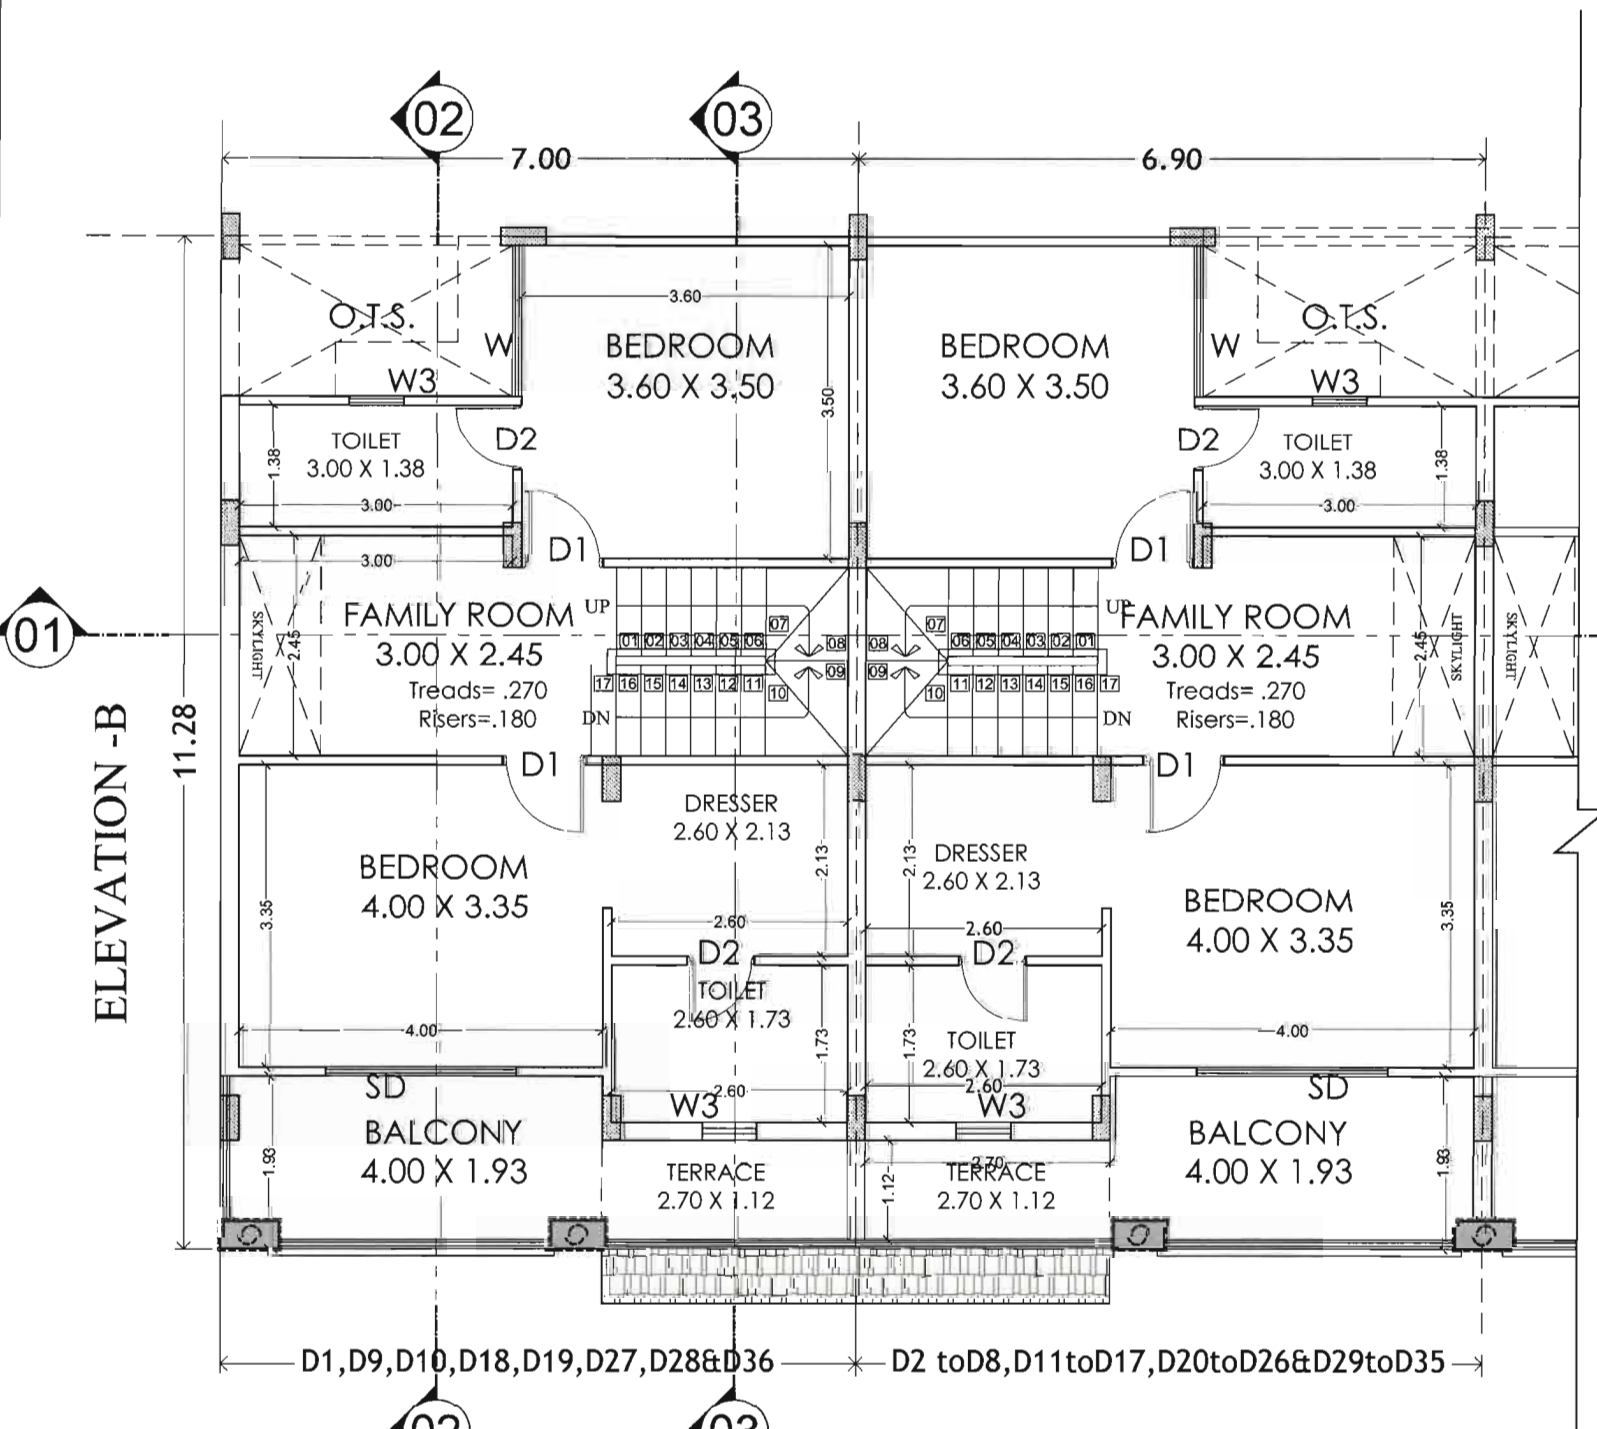


FIRST FLOOR PLAN

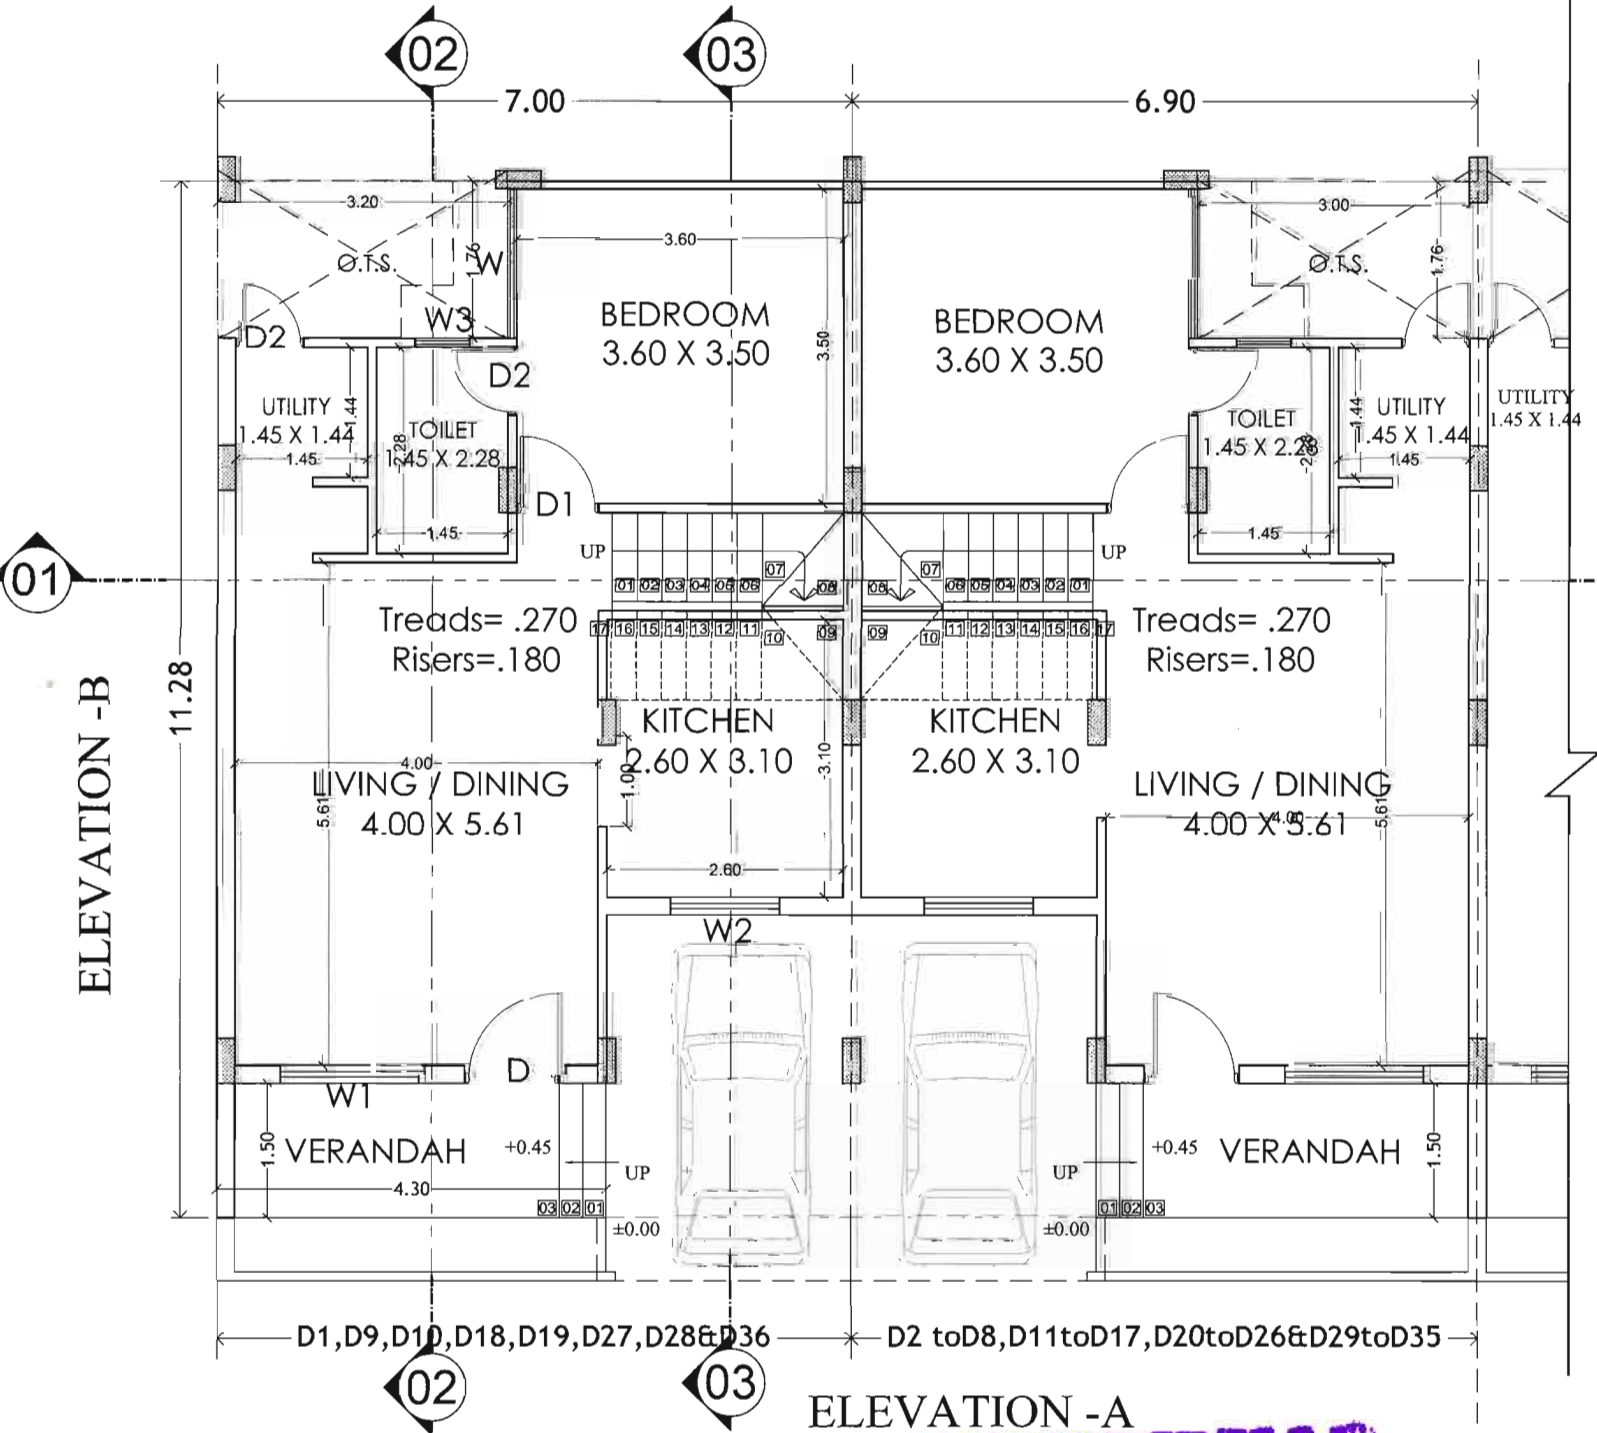


GROUND FLOOR PLAN

BLOCK - SMALL VILLA (D1,D9,D10,D18,D19,D27,D28 & D36)									
S.NO	FLOOR	BLOCK AREA	CUT OUT AREA	Built up Area	Fire Escape	Uft area	B.A.R.	Total Blocks No	TOTAL B.U.A
1	Ground Floor	78.96	5.01	73.95	8.00	0.00	65.95	8.00	591.60
2	1st Floor	75.66	5.01	70.65	0.00	0.00	70.65	8.00	565.20
3	Terrace Floor	9.08	0.00	9.08	0.00	0.00	0.00	8.00	72.64
	TOTAL	163.70	10.02	153.68	8.00	0.00	136.60		1229.44

BLOCK - SMALL VILLA (D2 to D8, D11 to D17, D20 to D26 & D29 to D35)									
S.NO	FLOOR	BLOCK AREA	CUT OUT AREA	Built up Area	Porch	Uft area	B.A.R.	Total Blocks No	TOTAL B.U.A
1	Ground Floor	77.83	5.01	72.82	8.00	0.00	64.82	28.00	2038.96
2	1st Floor	74.53	5.01	69.52	0.00	0.00	69.52	28.00	1946.56
3	Terrace Floor	9.08	0.00	9.08	0.00	0.00	0.00	28.00	254.24
	TOTAL	161.44	10.02	151.42	8.00	0.00	134.34		4239.76

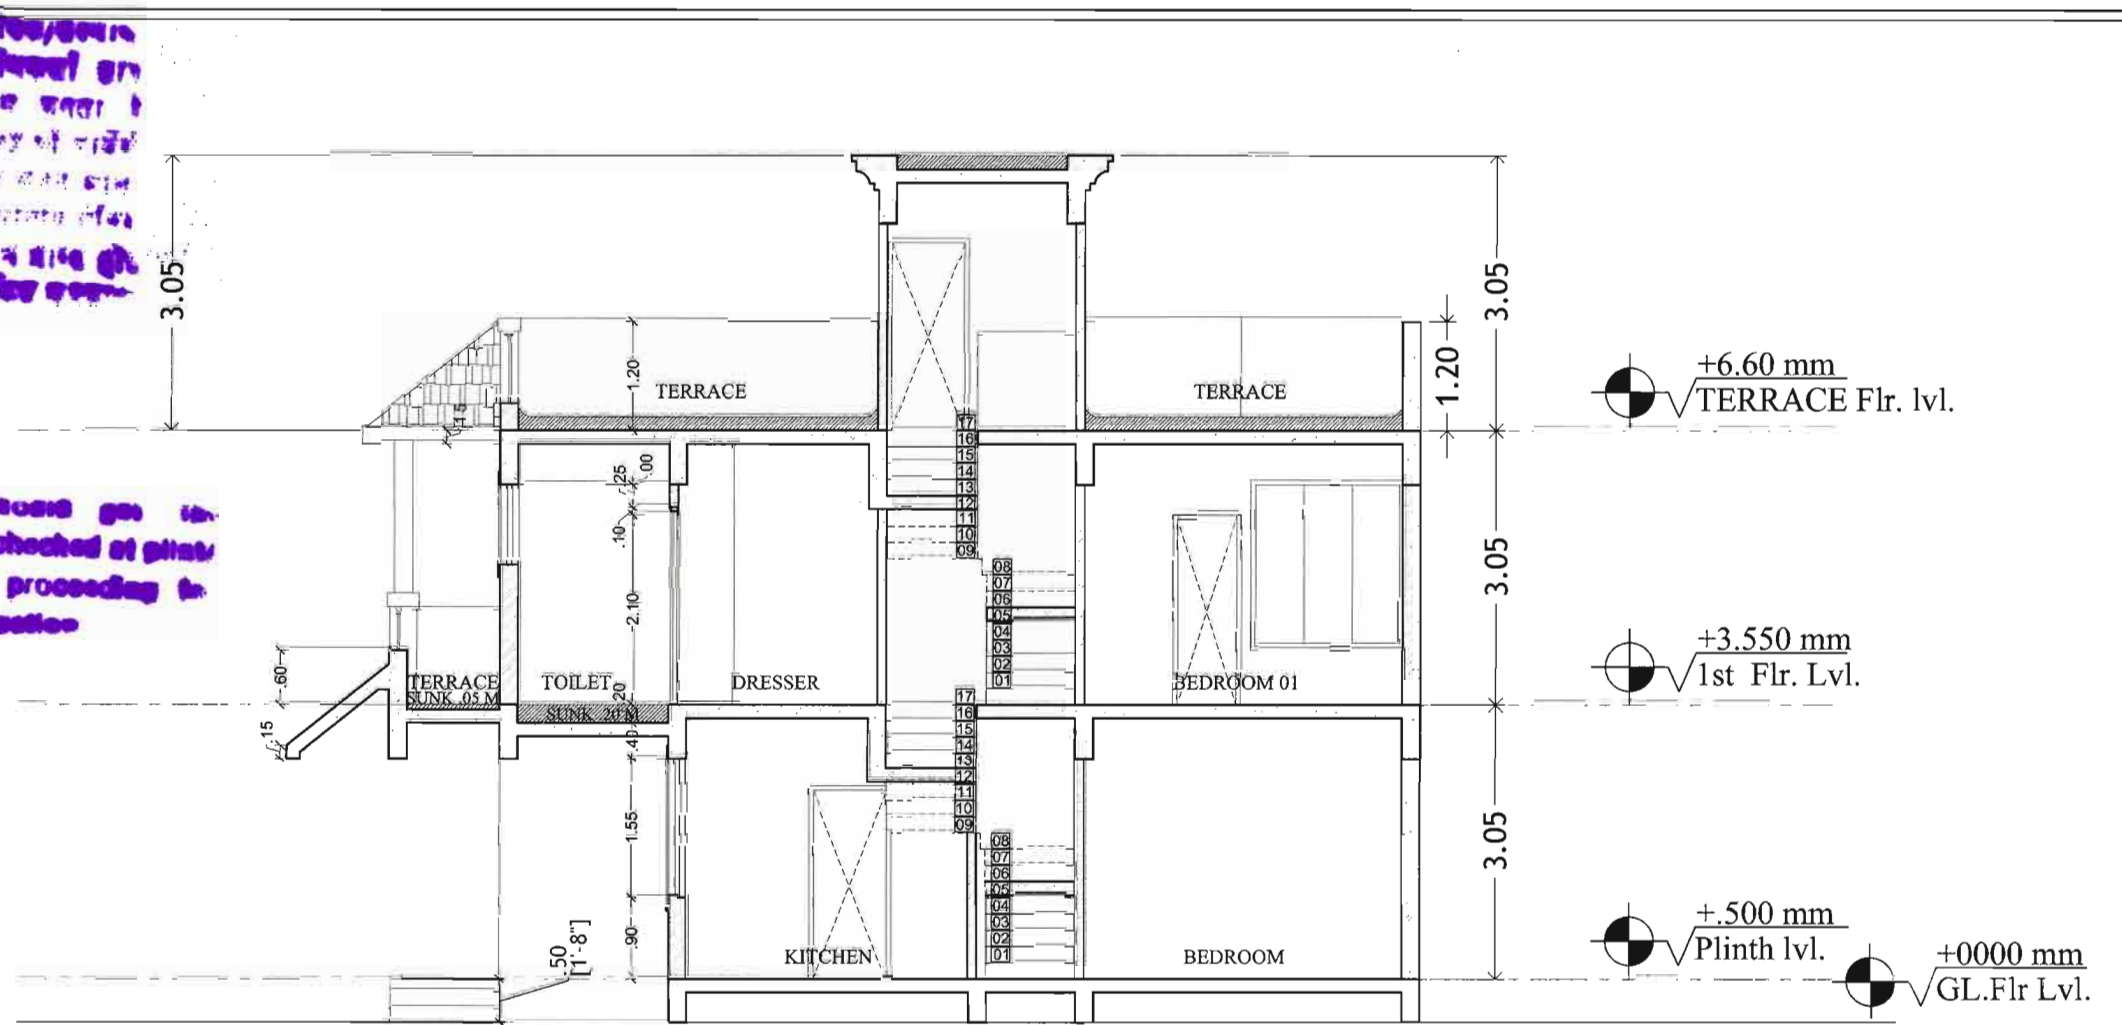


SECTION ON 3-3

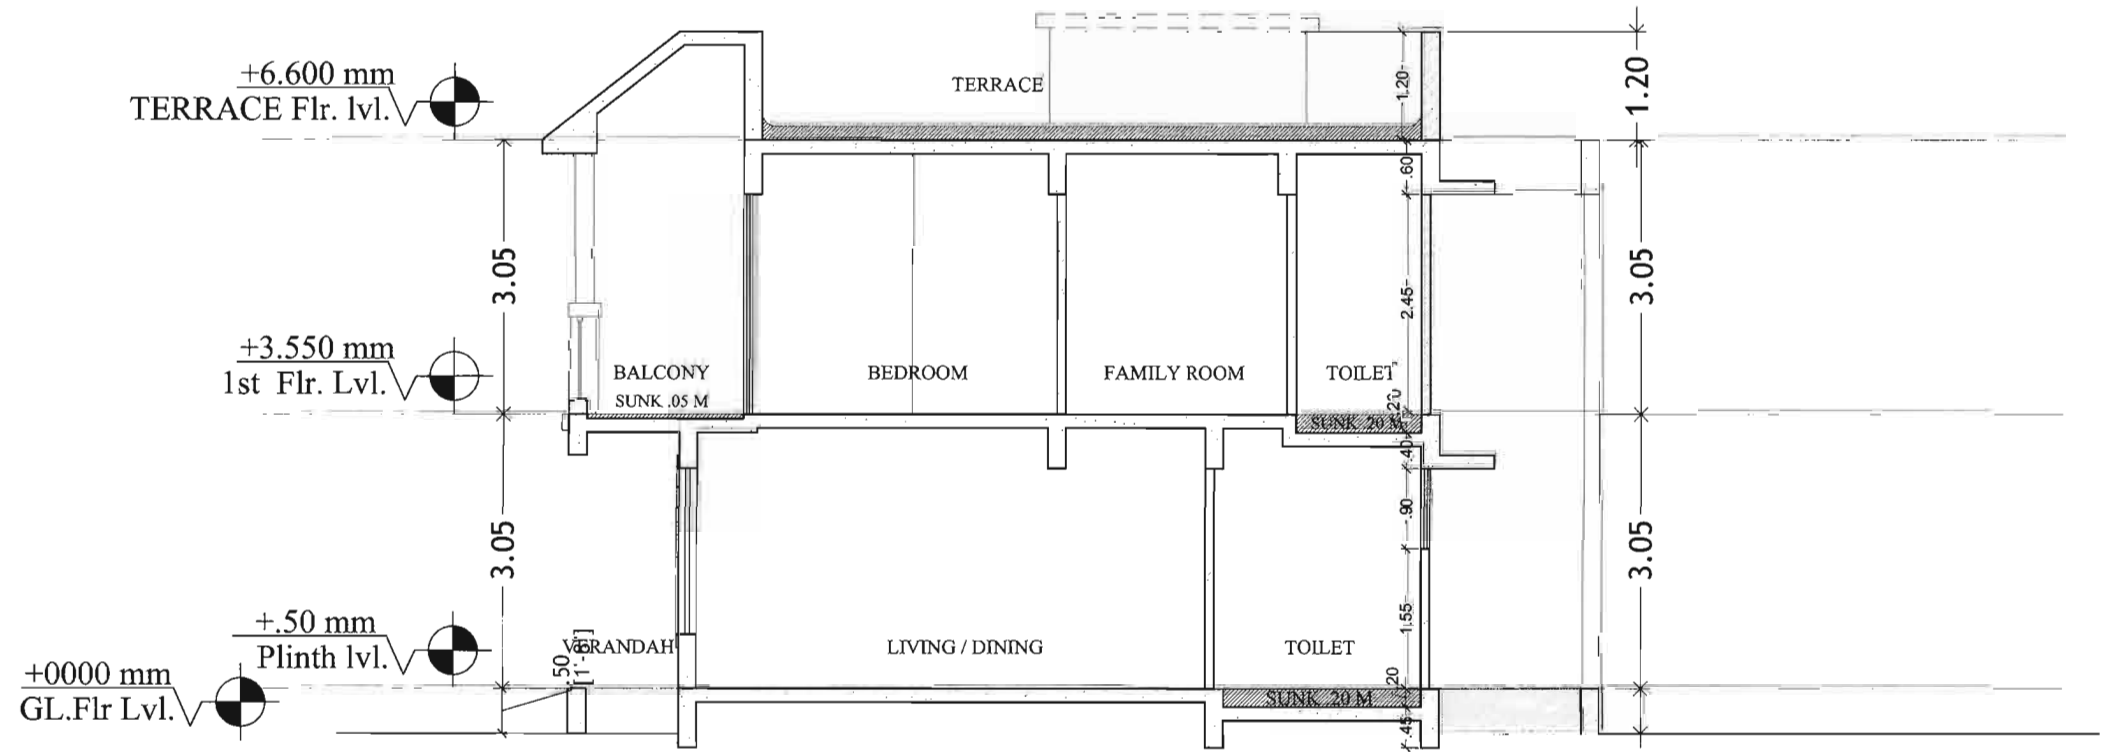

SECTION ON 2-2

SECTION 2

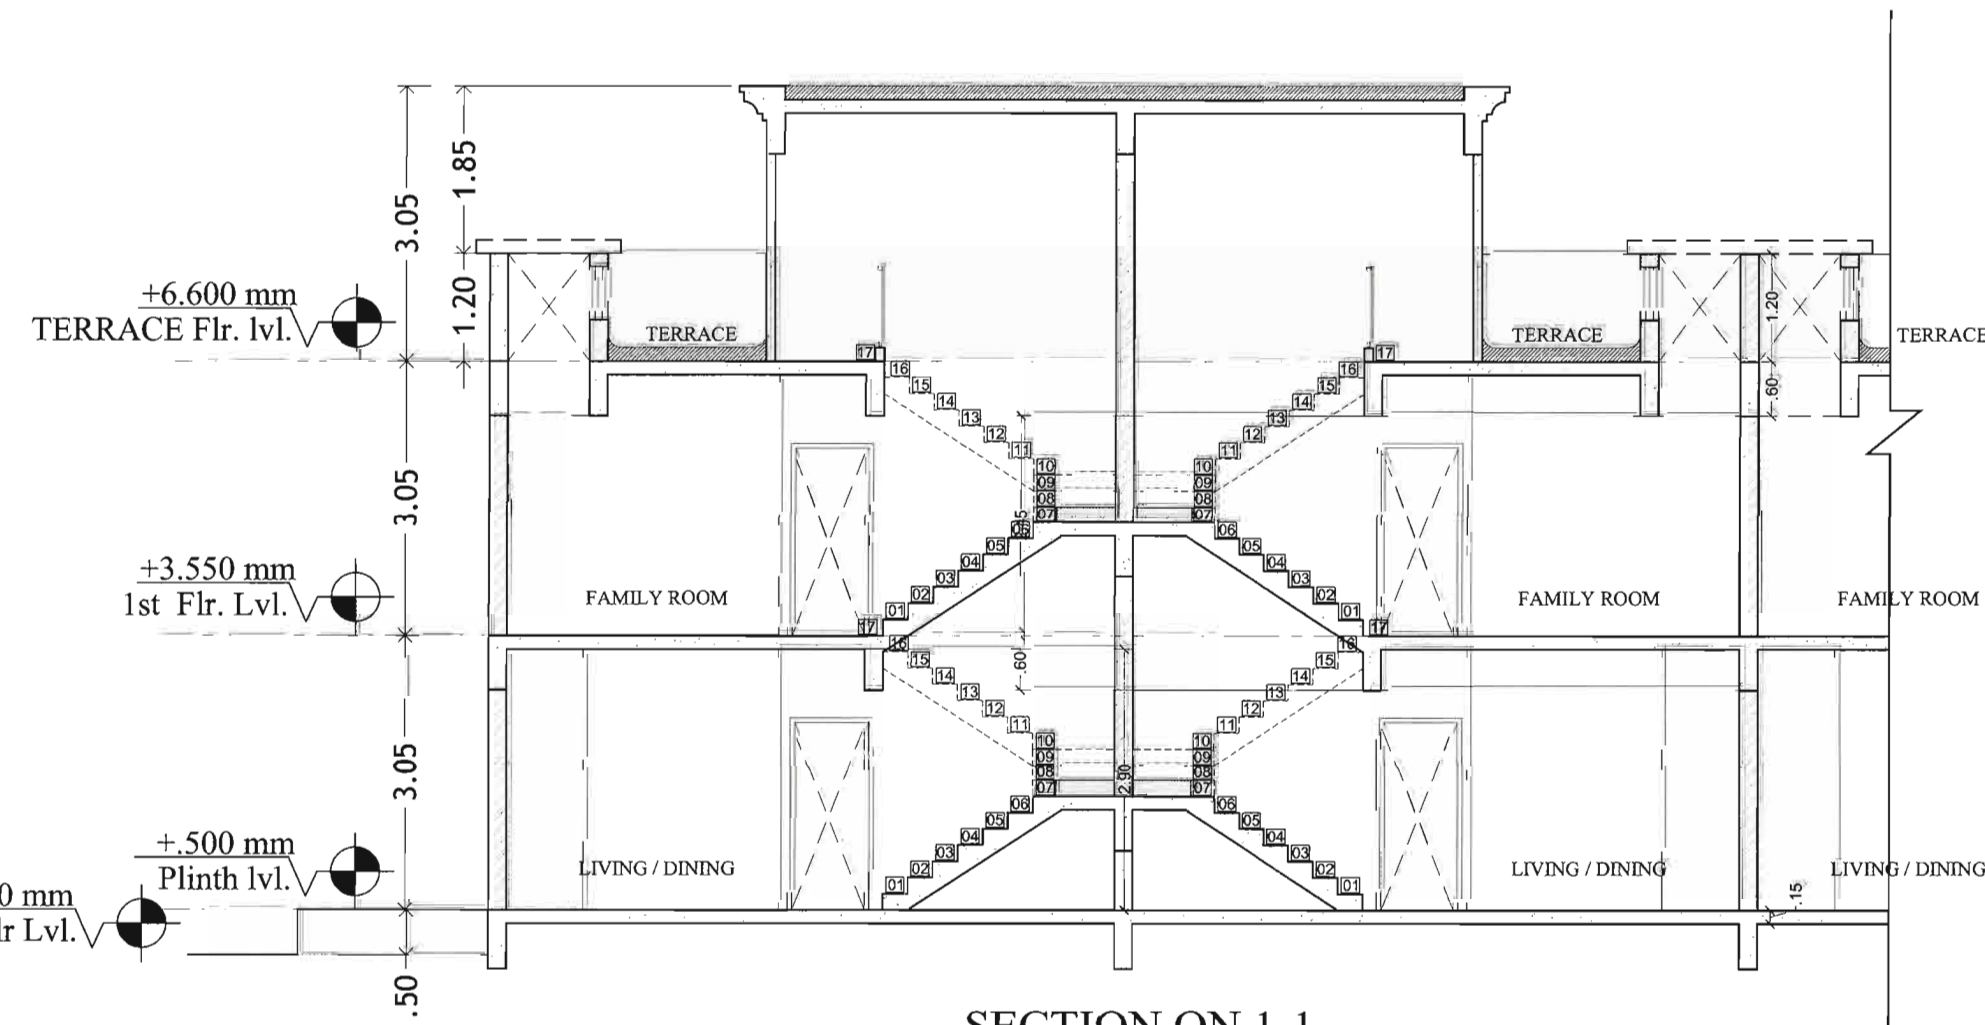

SECTION ON 1-1



ELEVATION -A

PROJECT TITLE :
PROPOSED GROUP HOUSING
PLOT KHASRA
NO.: 876,877,878,879&880,
881,882,884,885,886,887,905
IN VILLAGE-BHANKROTA KALAN
TEHSIL-SANGNER,DIST. JAIPUR.

CLIENT :
ASHIANA HOUSING, JAIPUR

ARCHITECTS
Ricky Mathur & Associates
architects interior designers planners
33, Dhuleshwar Garden,
Jaipur, (RAJ.) India. 302 001
Tel: 91-141-236 2688, 4004700
Fax: 91-141-400 8700
e-mail: ricky@rickymathur.com

DRAWING TITLE :-
SMALL VILLA (D1 to D36)


SCALE 1 : 100 DATE JANUARY 2023

DEALT BY STATUS SUBMISSION

ARCHITECT'S SIGN.
Ricky Mathur
RICKY MATHUR
CA-34247





CLIENT'S SIGN.
For Ashiana Housing Limited
Authorised Signatory

SHEET NO. - 20 NORTH -

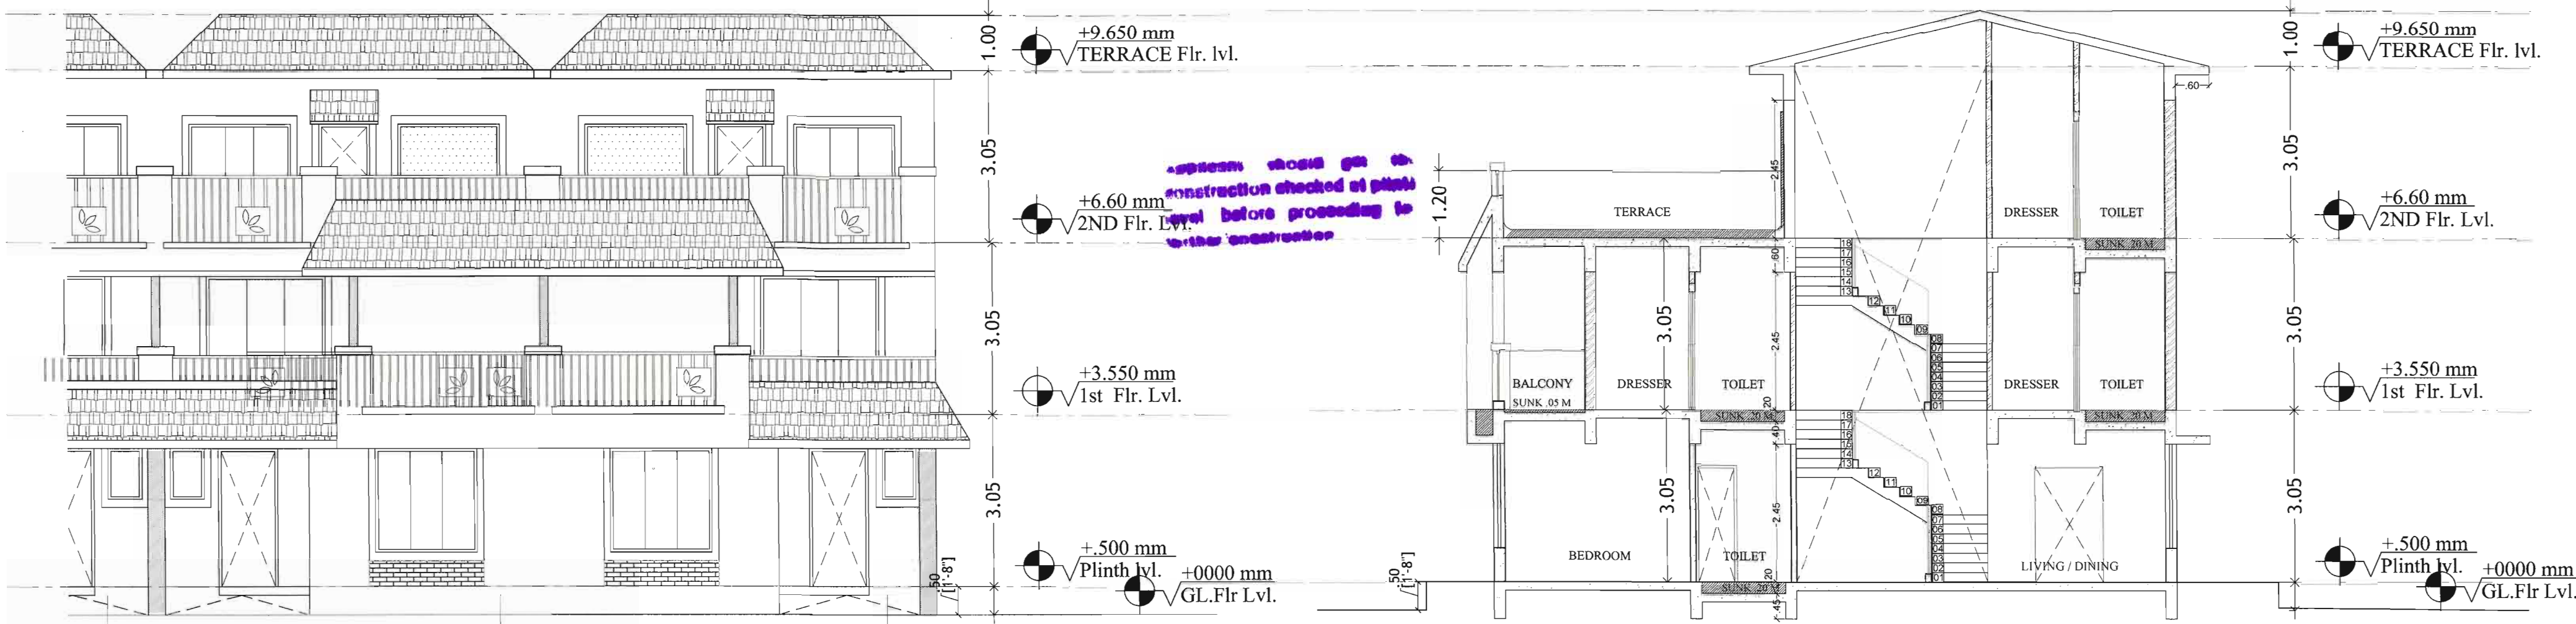

BLOCK - BIG VILLA (C1 & C 20)									
S.NO	FLOOR	BLOCK AREA	CUT OUT AREA	Built up Area	Porch	Lift area	B. A. R.	Total Blocks Nos	TOTAL B.U.A
1	Ground Floor	83.30	0.00	83.30	10.60	0.00	72.70	2.00	166.60
2	1st Floor	87.04	1.70	85.34	0.00	0.00	85.34	2.00	170.68
3	Second Floor	48.12	10.98	37.14	0.00	0.00	37.14	2.00	74.28
TOTAL		218.46	12.68	205.78	10.60	0.00	195.18		390.36

BLOCK - BIG VILLA (C2 to C19)									
S.NO	FLOOR	BLOCK AREA	CUT OUT AREA	Built up Area	Porch	Lift area	B. A. R.	Total Blocks Nos	TOTAL B.U.A
1	Ground Floor	82.09	0.00	82.09	10.60	0.00	71.49	18.00	1477.62
2	1st Floor	85.83	1.70	84.13	0.00	0.00	84.13	18.00	1514.34
3	Second Floor	47.43	10.98	36.45	0.00	0.00	36.45	18.00	656.10
TOTAL		215.35	12.68	202.67	10.60	0.00	192.07		3648.06

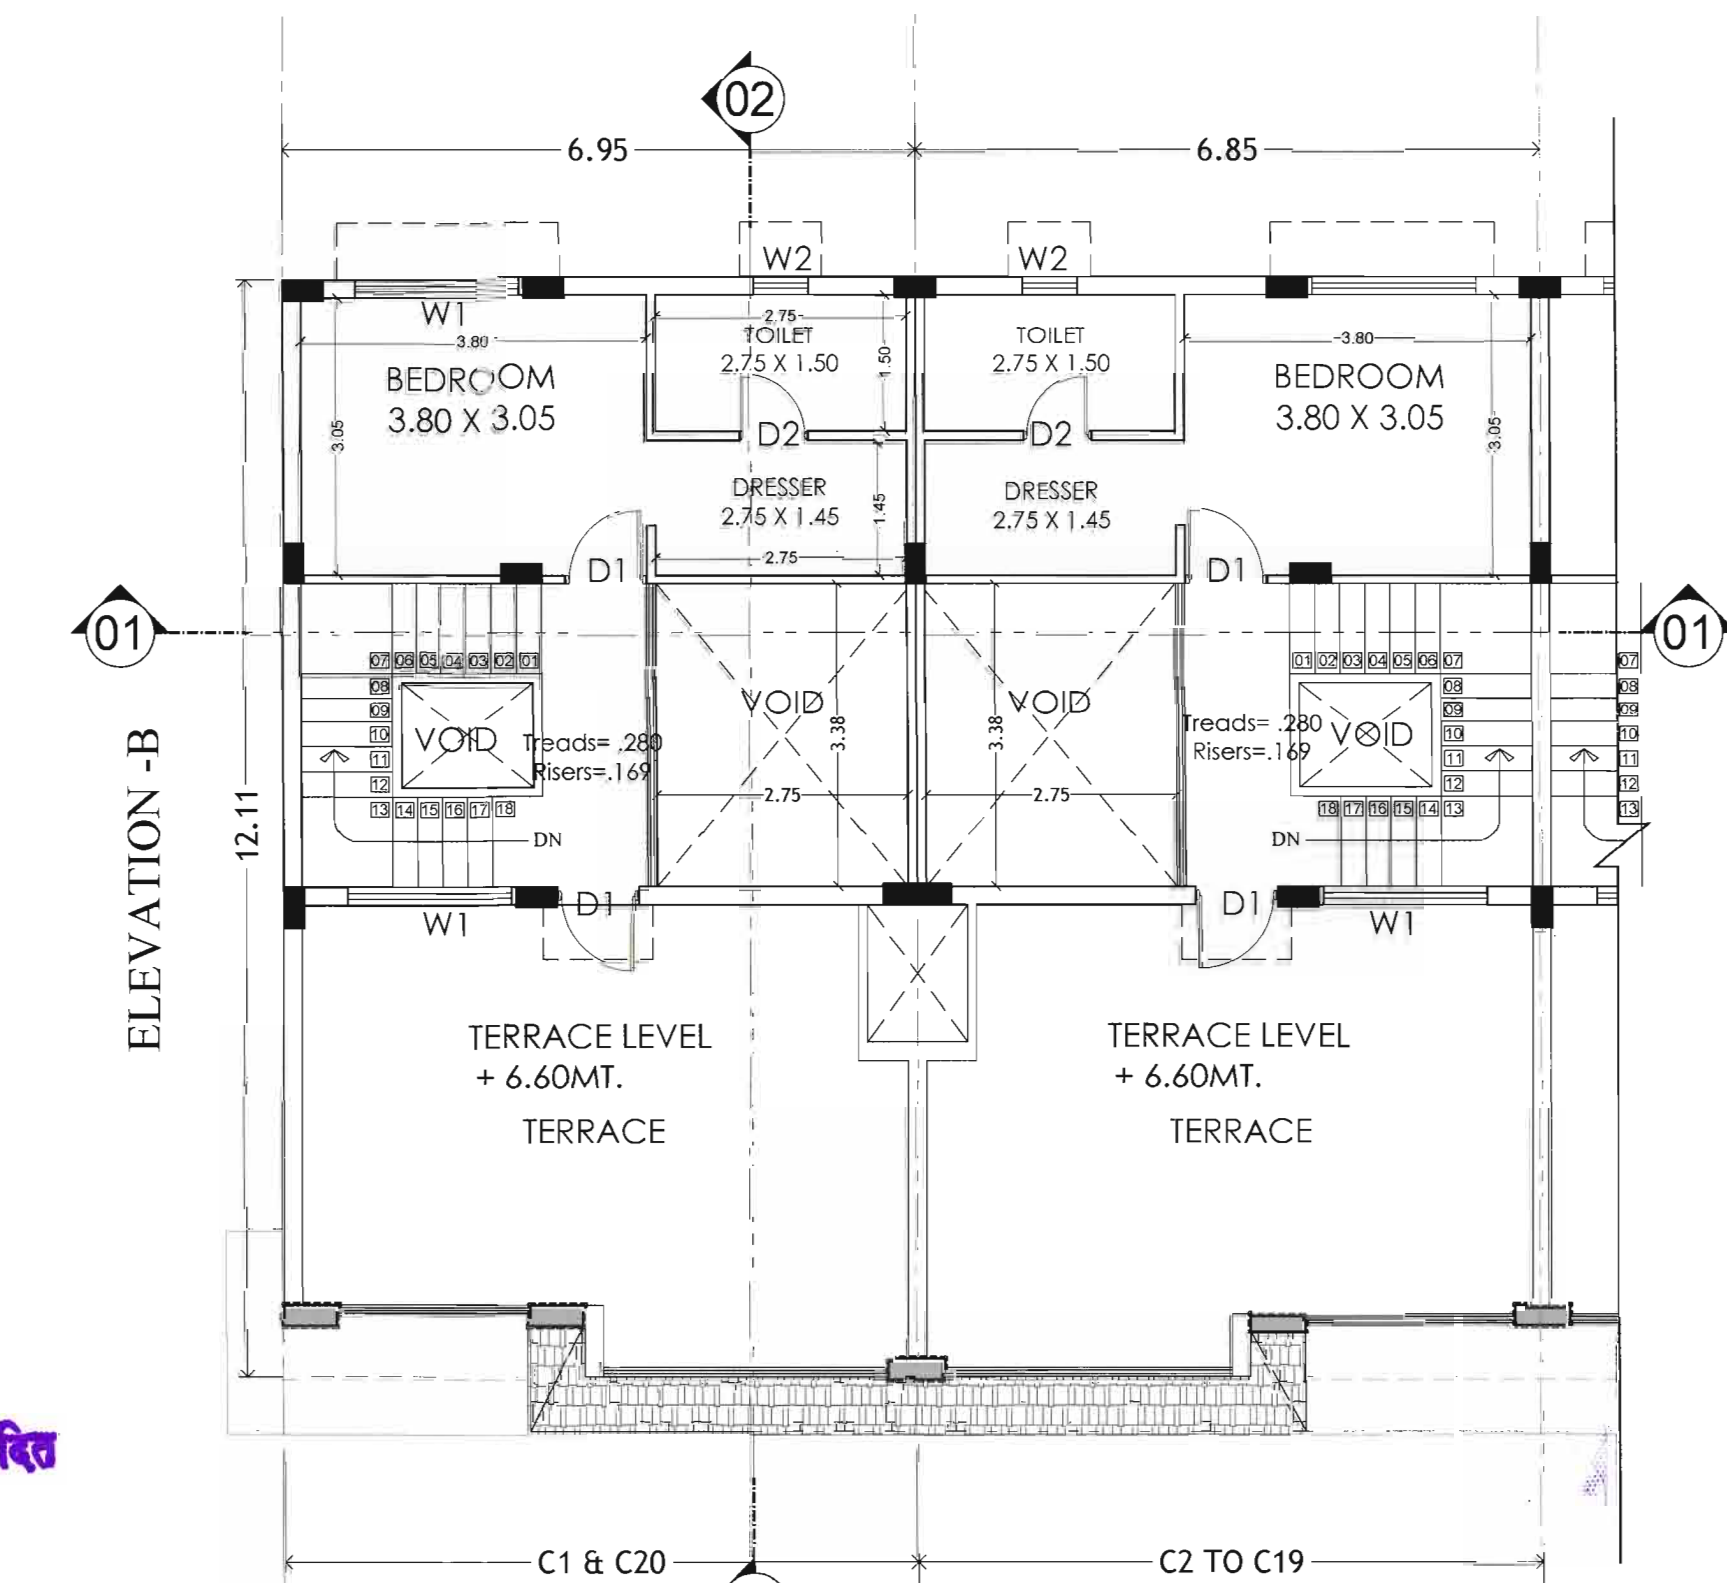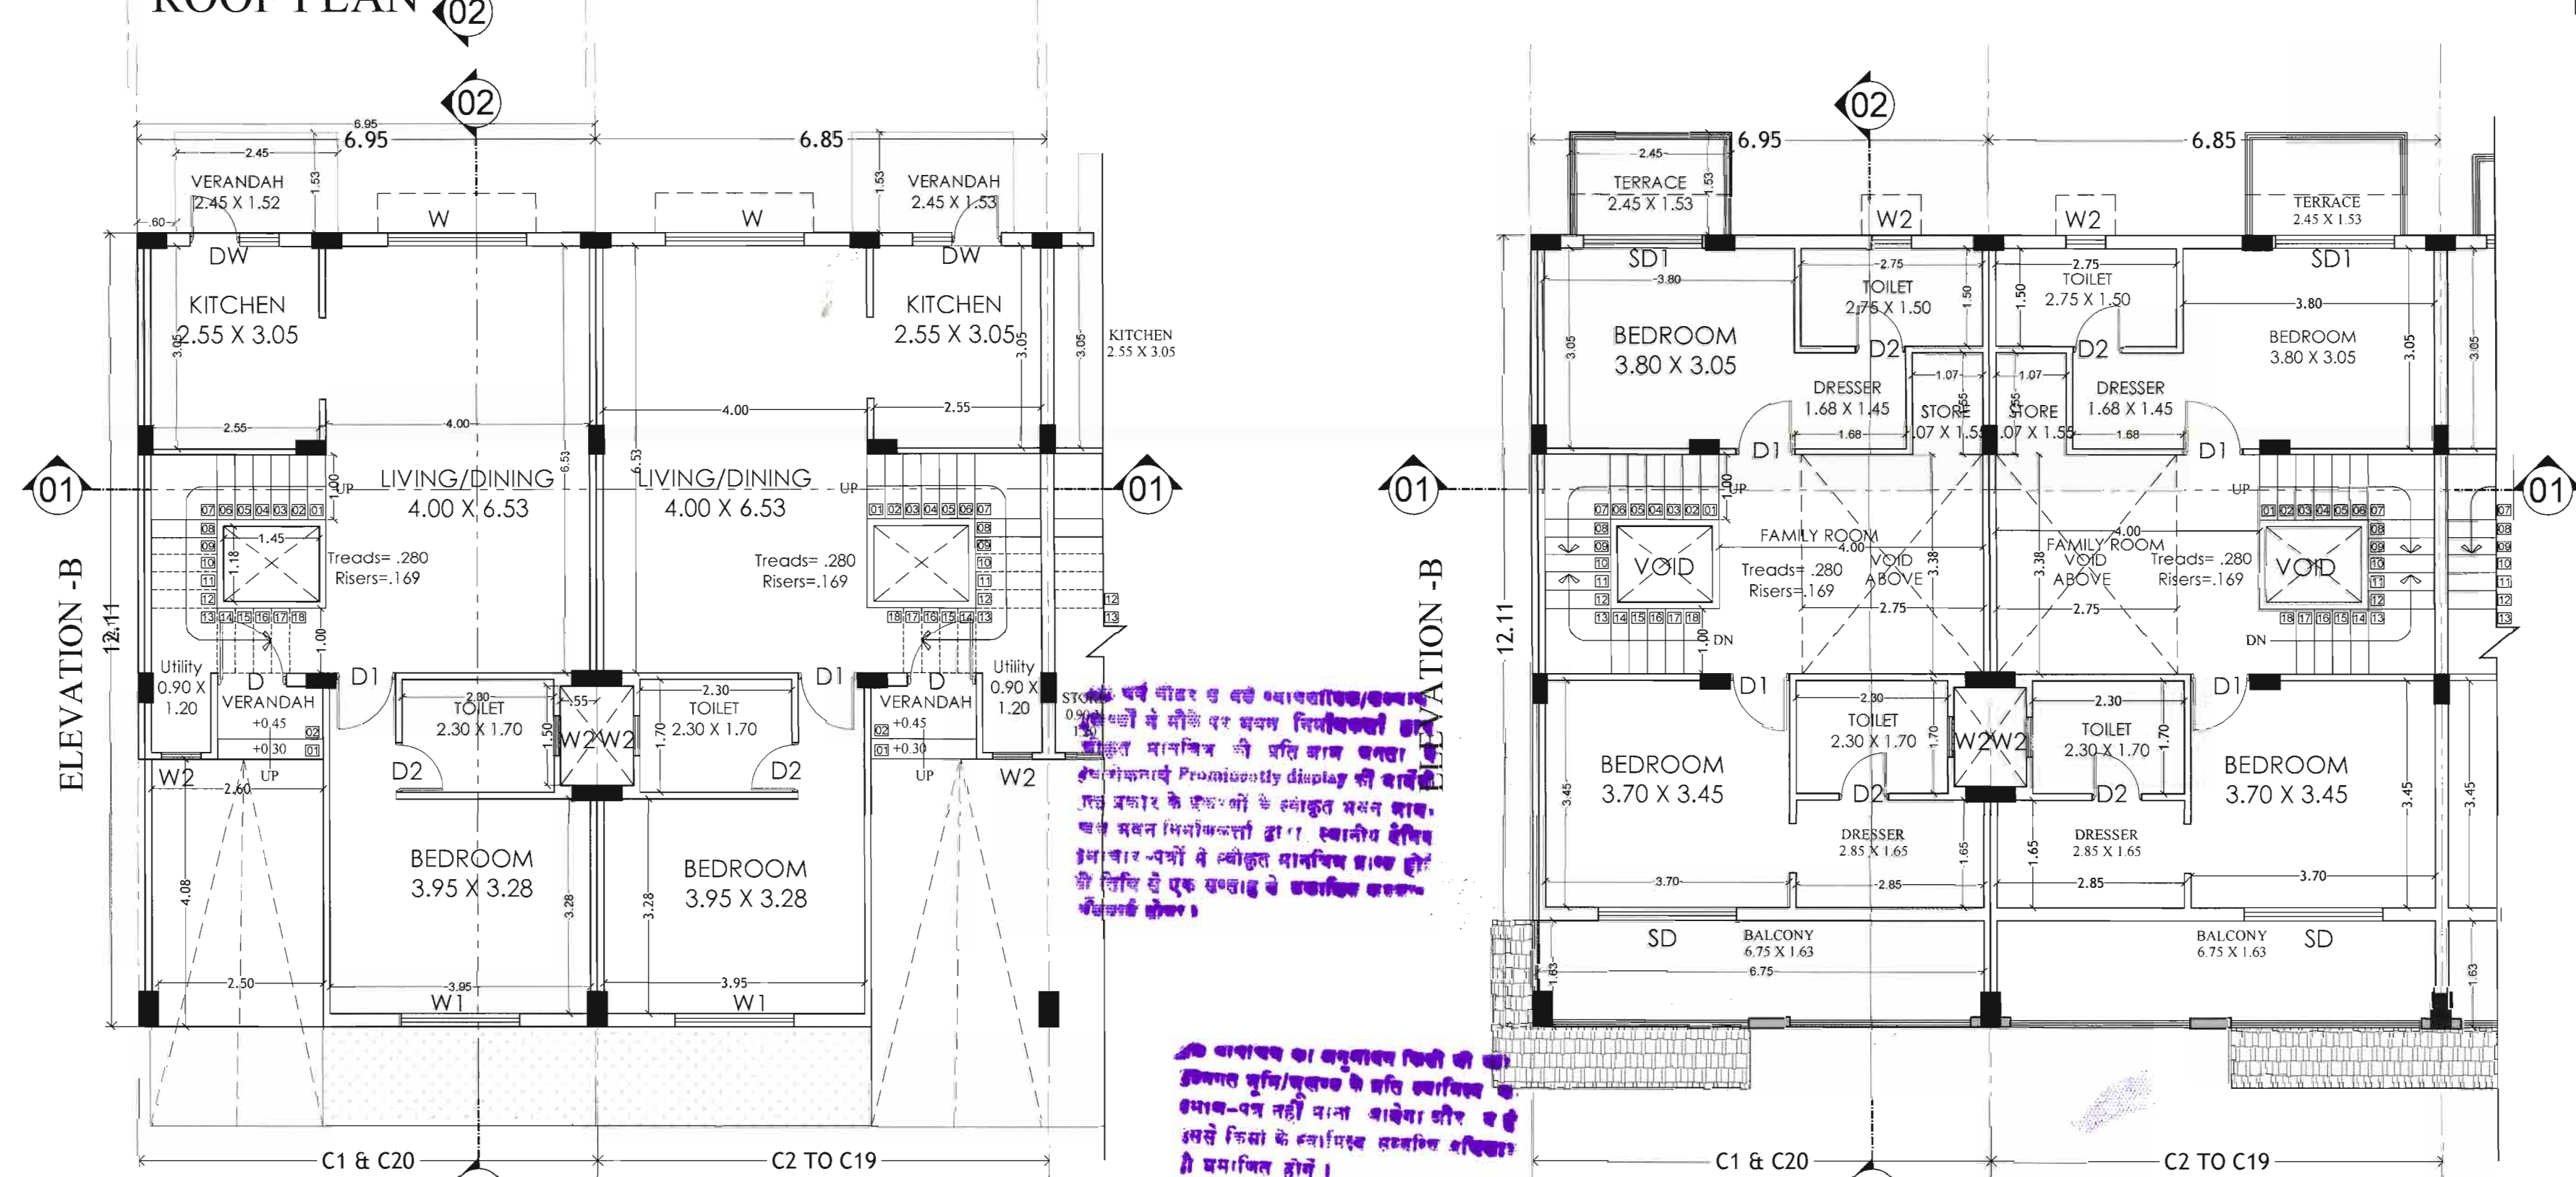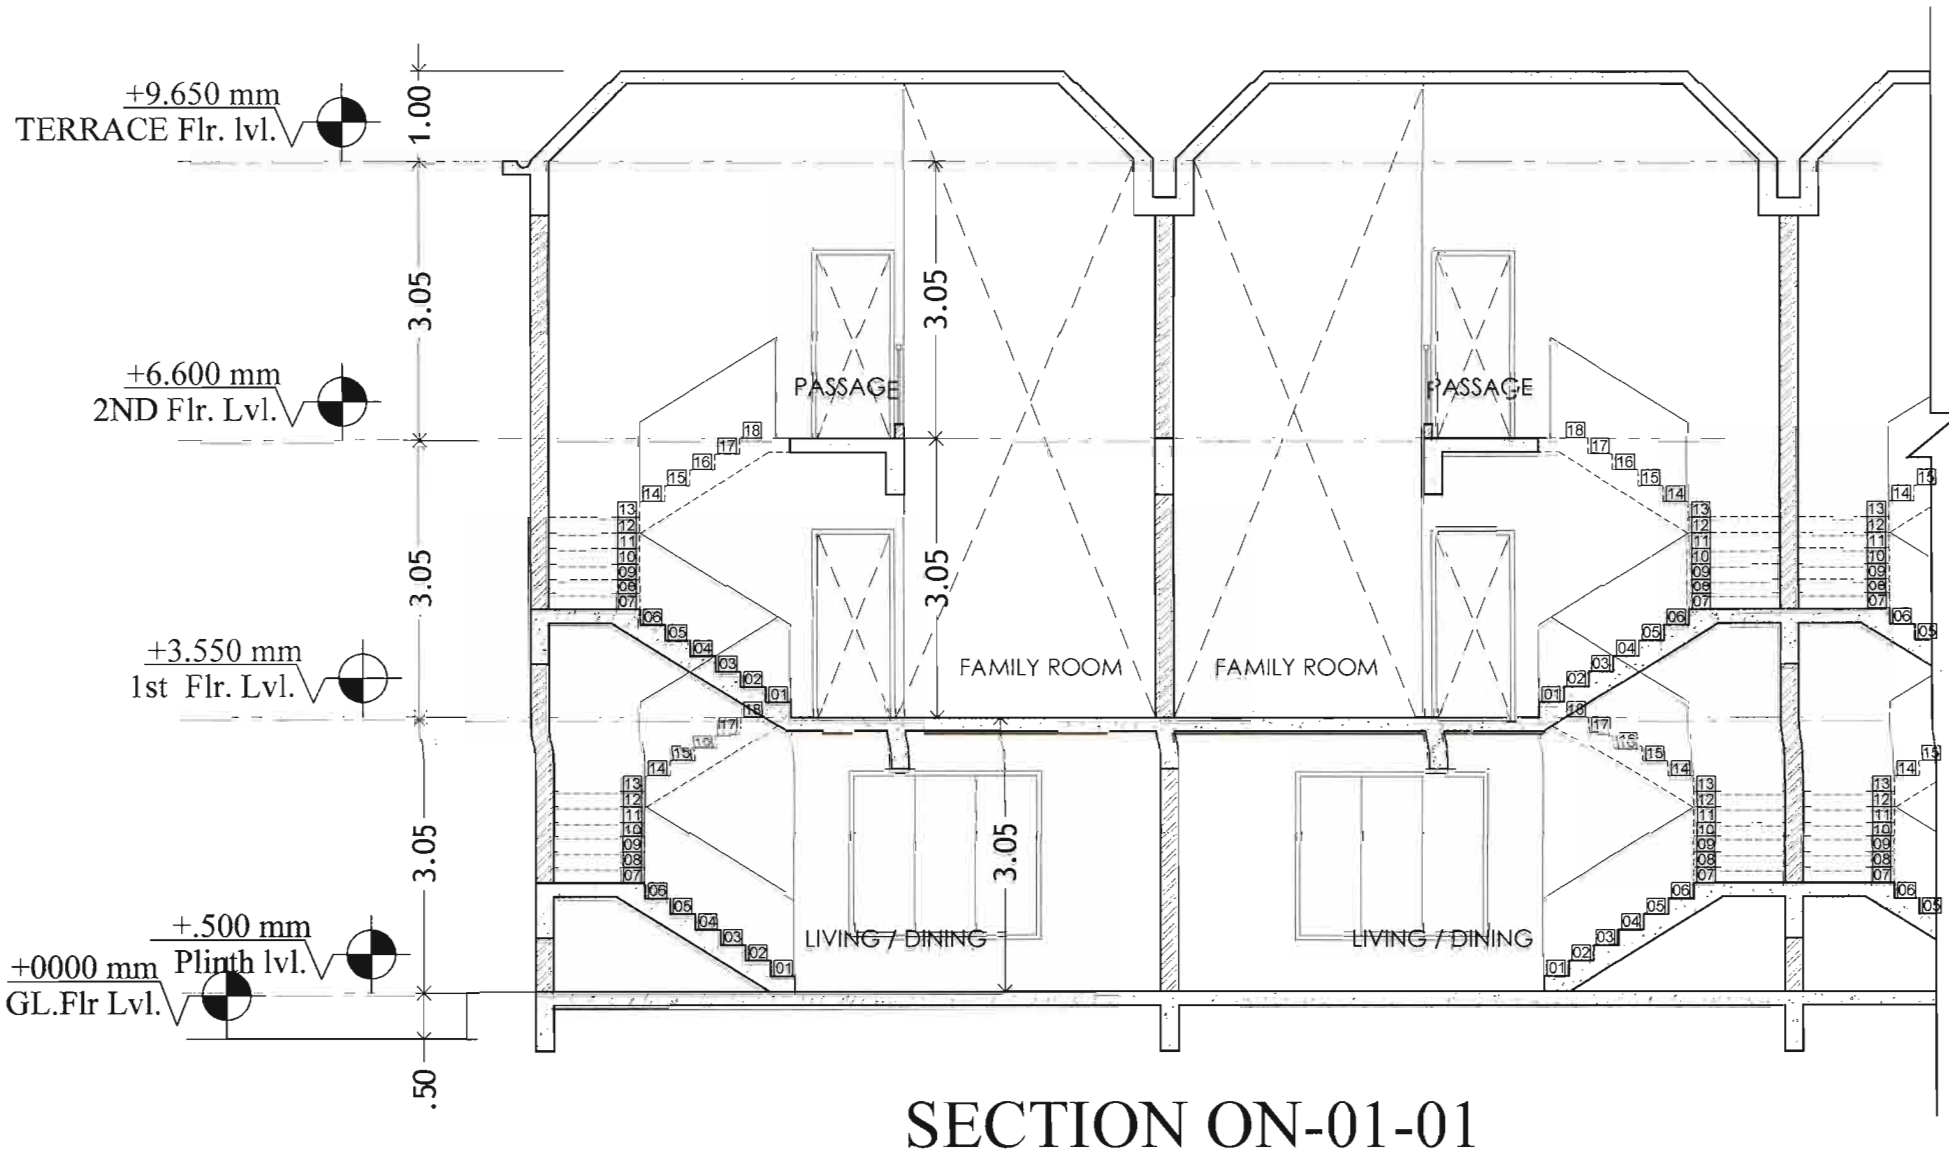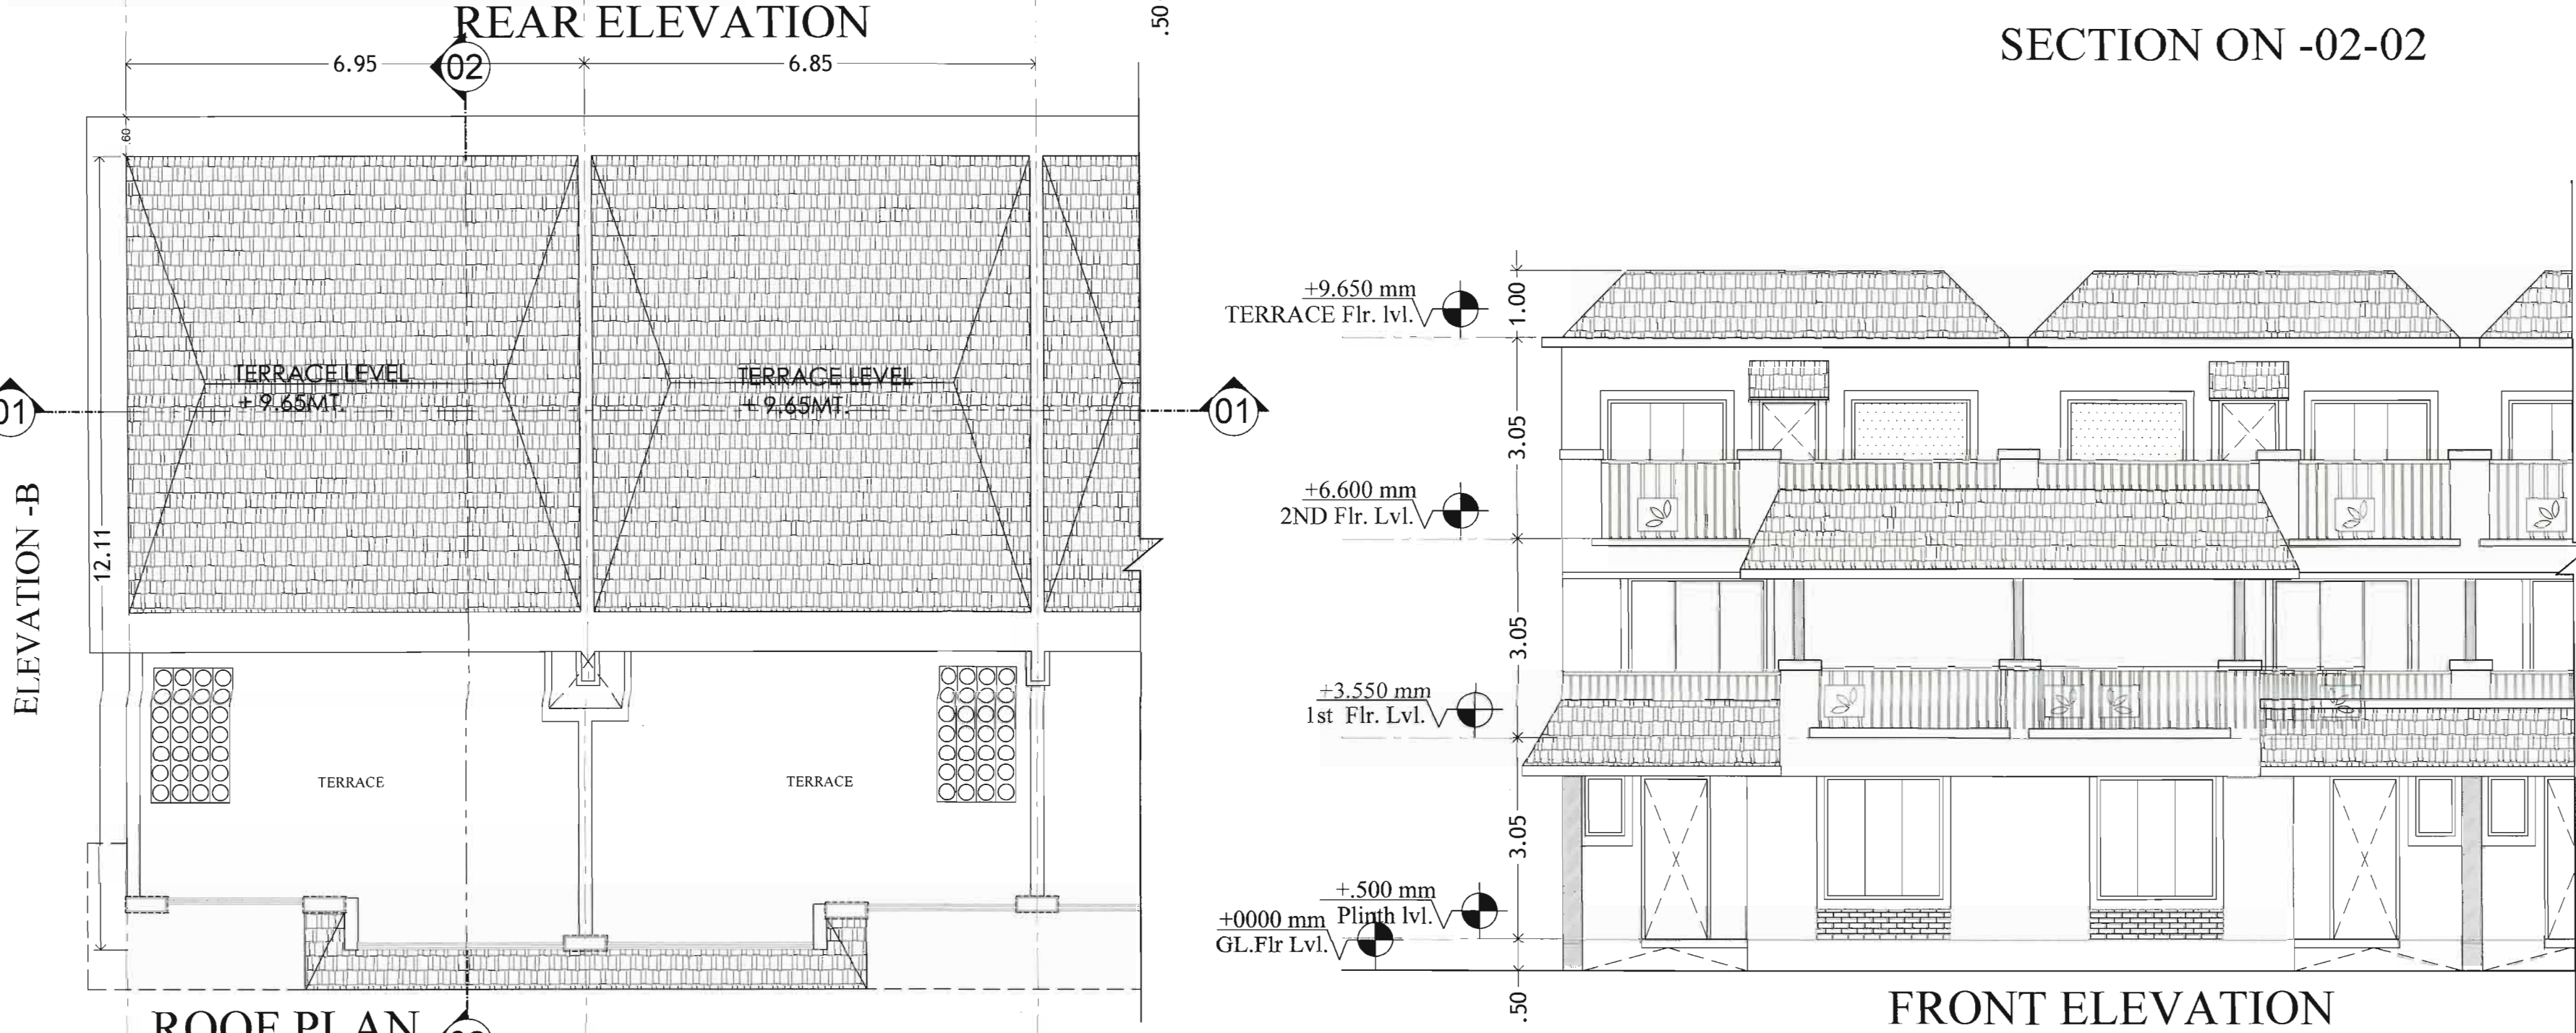


PROJECT TITLE :
PROPOSED GROUP HOUSING
PLOT KHASRA
NO.:-876,877,878,879&880,
881,882,884,885,886,887,905
IN VILLAGE-BHANKROTA KALAN
TEHSIL-SANGNER,DIST. JAIPUR.

CLIENT :
ASHIANA HOUSING, JAIPUR

ARCHITECTS
Ricky Mathur & Associates
architects interior designers planners
33, Dhuleshwar Garden,
Jaipur, (RAJ.) India. 302 001
Tel: 91-141-236 2688, 4004700
Fax: 91-141-400 8700
e-mail: ricky@rickymathur.com

DRAWING TITLE :-
BIG VILLA (C1 TO C20)

SCALE 1:100 DATE JANUARY 2023
DEALT BY STATUS SUBMISSION

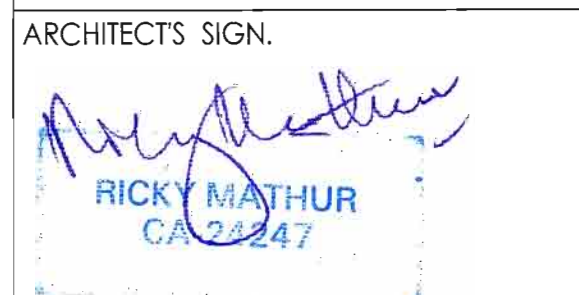ARCHITECTS SIGN.

RICKY MATHUR
CA 24247


CLIENT'S SIGN.

For Ashiana Housing Limited
Authorised Signatory


SHEET NO. - 21 NORTH -

BLOCK -E (CLUB HOUSE)										
S.NO	FLOOR	BLOCK AREA	CUT OUT AREA	Built up Area	Pool/Deck	Lift area	B .A .R.	Total Blocks Nos	TOTAL B.U.A	TOTAL B.A.R
1	Basement fl.	250.43	0.00	250.43	0.00	4.00	246.43	1.00	250.43	246.43
2	Ground Floor	1046.19	165.11	881.08	462.24	4.00	414.84	1.00	881.08	414.84
3	First Floor	567.86	38.79	529.07	0.00	4.00	529.07	1.00	529.07	529.07
	TOTAL	1864.48	203.90	1660.58			1190.34		1660.58	1190.34

ELEVATION C

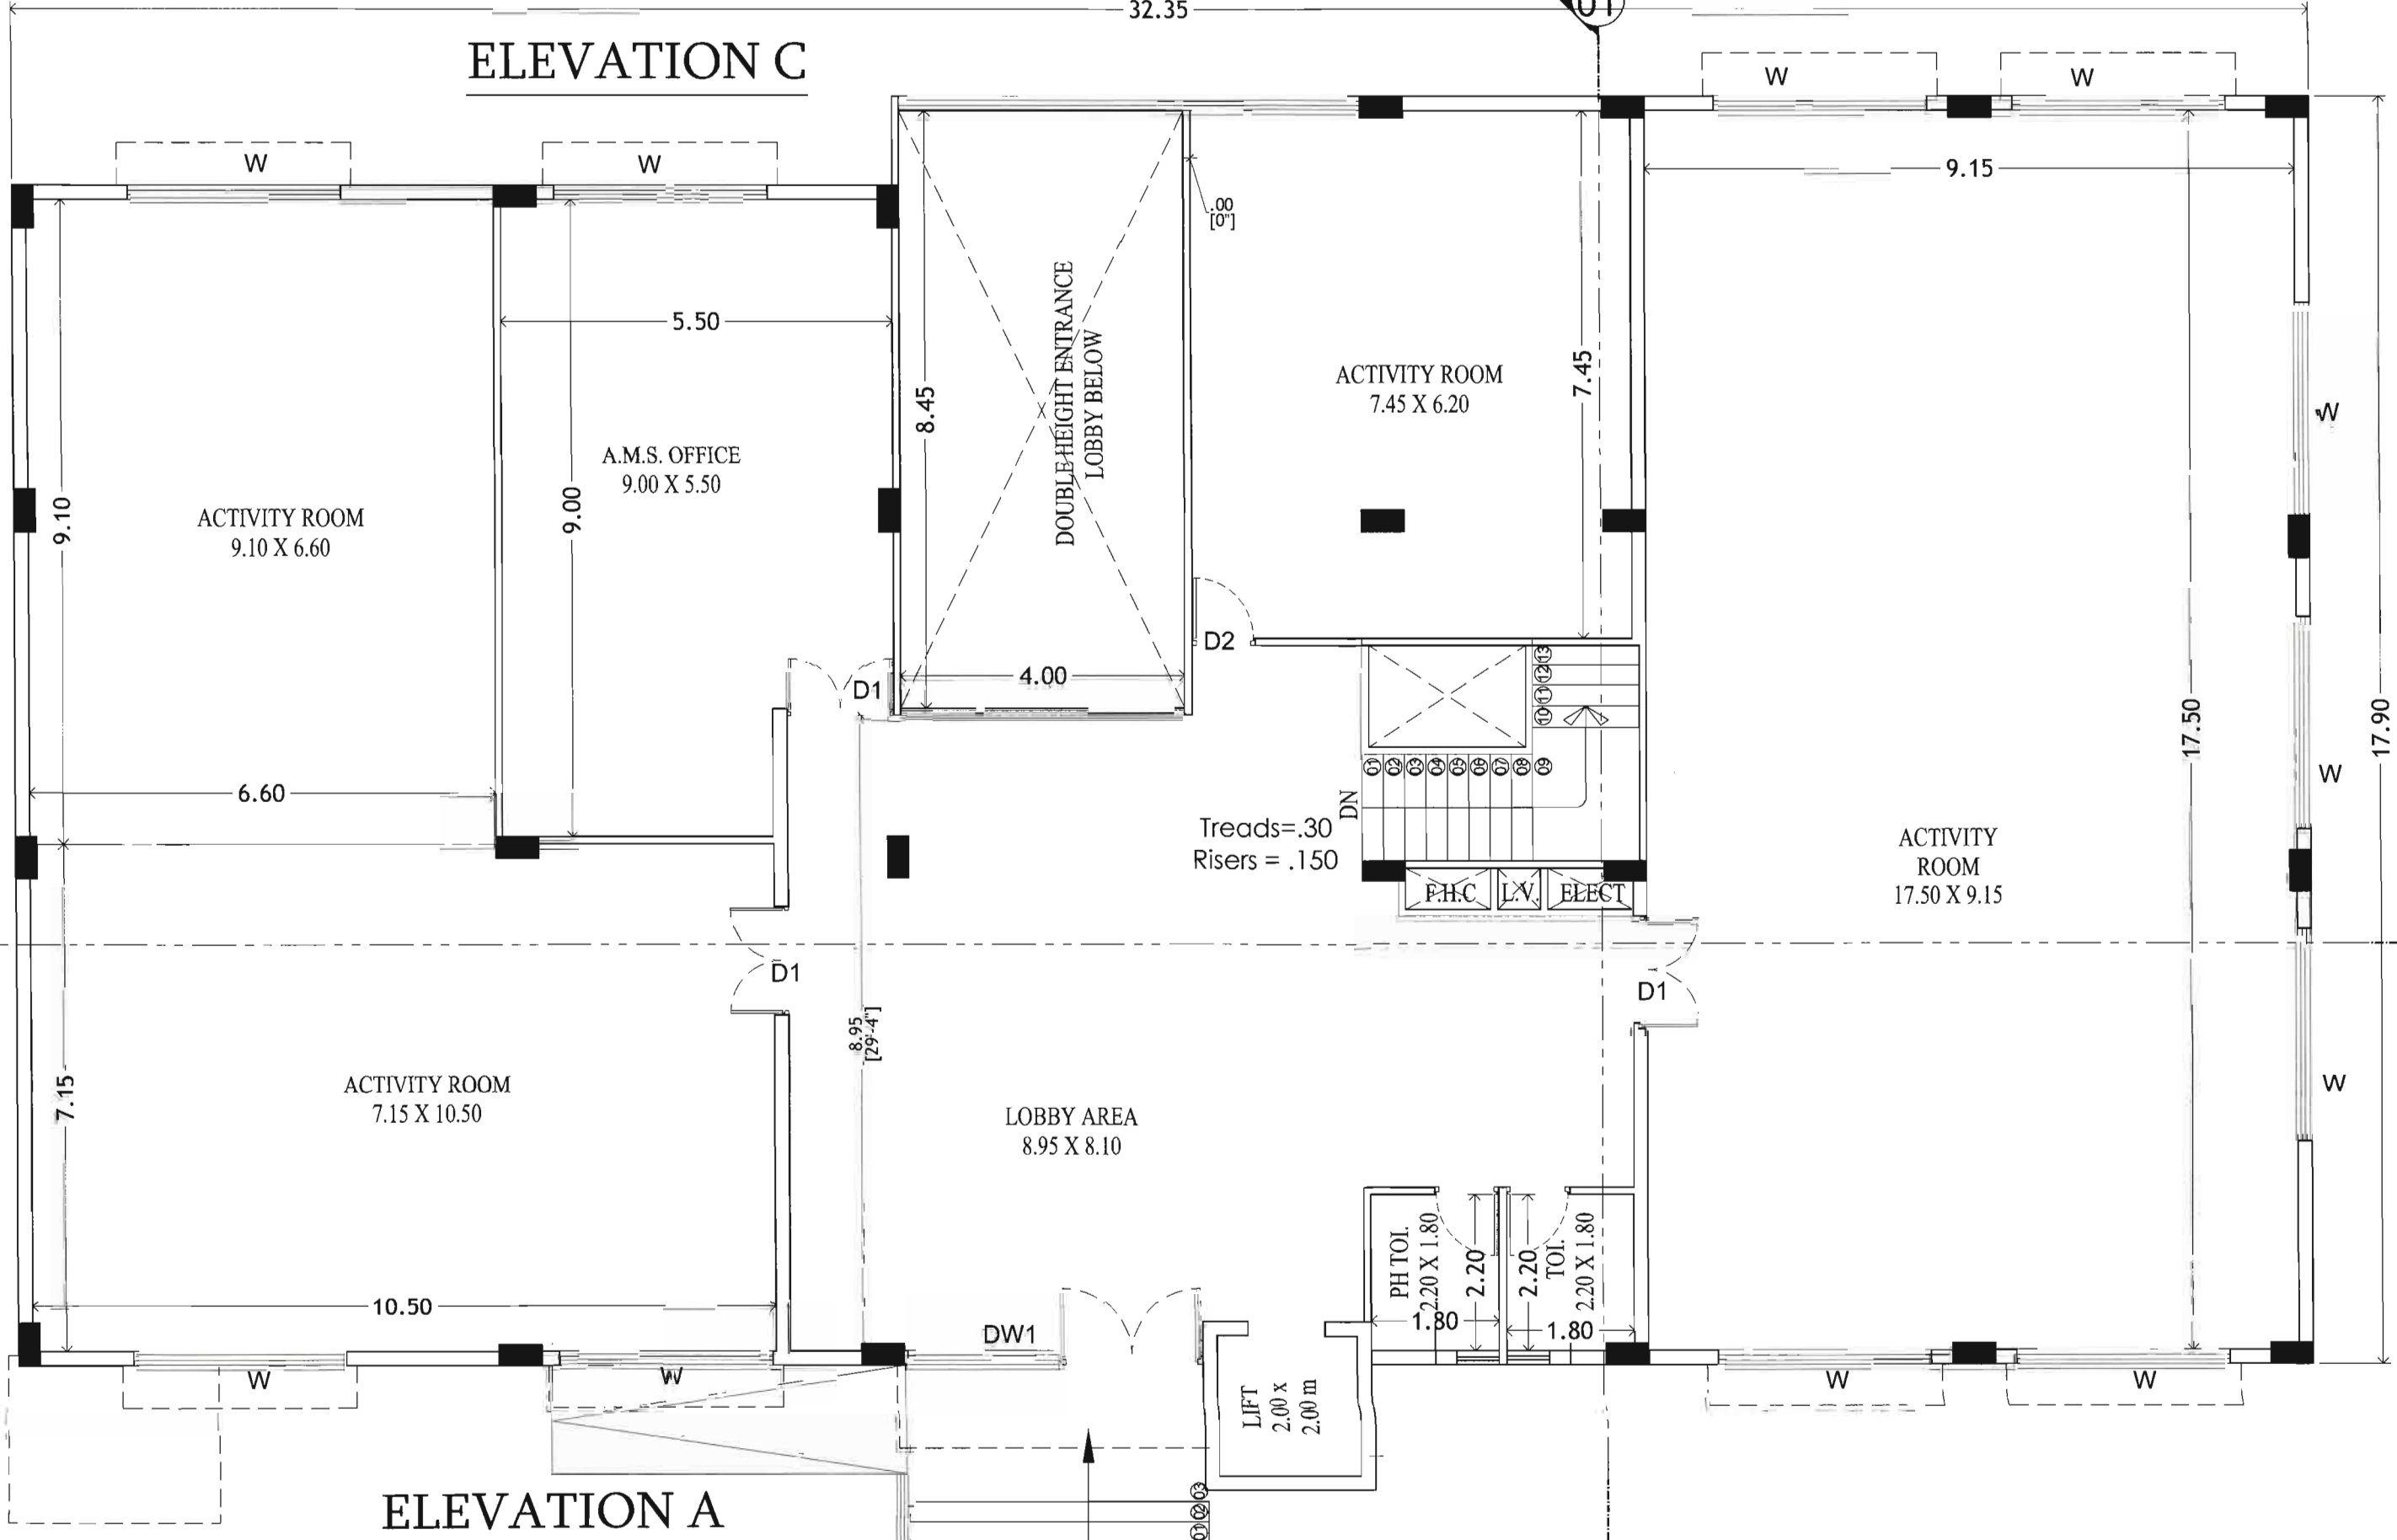

FIRST FLOOR PLAN

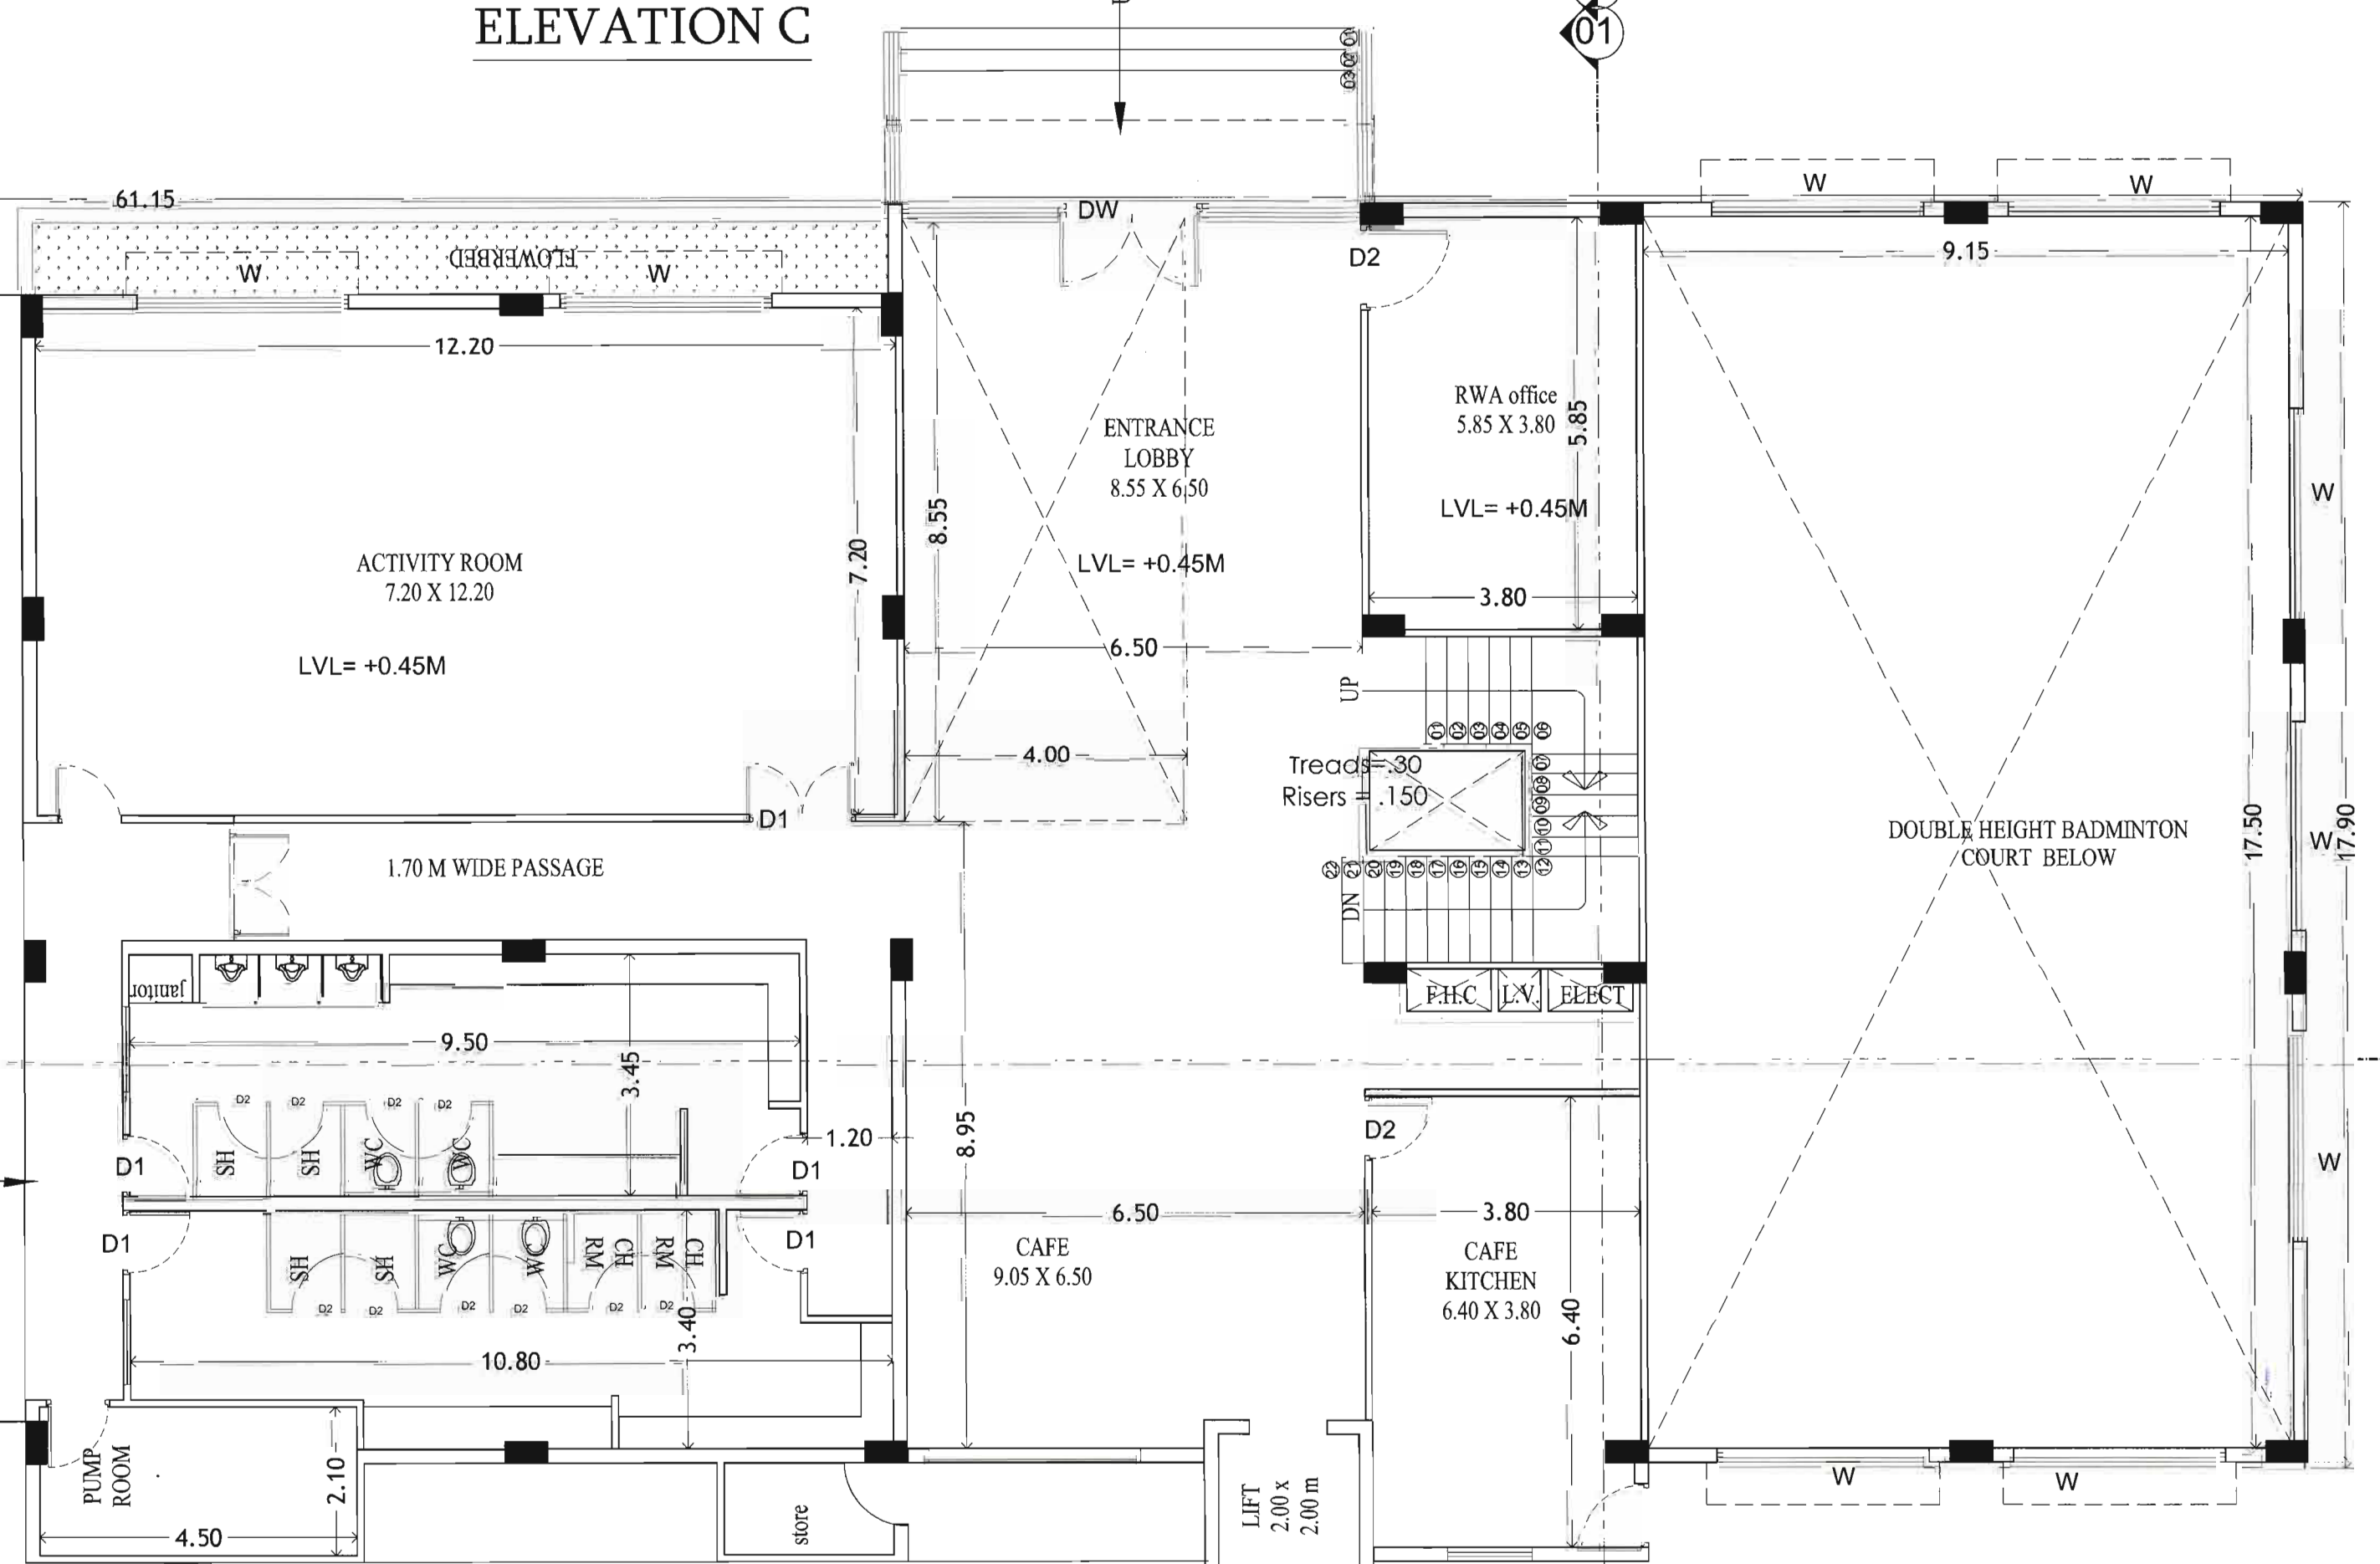

GROUND FLOOR PLAN

PROJECT TITLE :

PROPOSED GROUP HOUSING
PLOT KHASRA
NO.:-876,877,878,879&880,
881,882,883,884,885,886,887,905
IN VILLAGE-BHANKROTA KALAN
TEHSIL-SANGNER,DIST. JAIPUR.

CLIENT :

ASHIANA HOUSING, JAIPUR

ARCHITECTS

Ricky Mathur & Associates
architects interior designers planners
33, Dhuleshwar Garden,
Jaipur. (RAJ.) India, 302 001
Tel: 91-141-236 2688, 4004700
Fax: 91-141-400 8700
e-mail: ricky@rickymathur.com

DRAWING TITLE :-

BLOCK- E (CLUB House)
FLOOR PLANS

SCALE 1 : 100	DATE JANUARY 2023
DEALT BY	STATUS SUBMISSION

ARCHITECT'S SIGN.

CLIENT'S SIGN.


For Ashiana Housing Limited
Authorised Signatory

SHEET NO. - 22 NORTH -


S.NO	FLOOR	BLOCK AREA	CUT OUT AREA	Built up Area	Fire Escape	Lift area	B. A. R.	Total Blocks Nos	TOTAL B.U.A	TOTAL B.A.R
1	Ground Floor	346.38	3.74	342.64	14.87	8.99	318.78	1.00	342.64	318.78
2	First Floor	409.38	3.74	405.64	14.87	8.99	381.78	1.00	405.64	381.78
3	Terrace	0.00	0.00	0.00					0.00	0.00
	TOTAL	755.76	7.48	748.28	29.74	17.98	700.56	1.00	748.28	700.56

कृपया नोट करें कि आवासीय इकाई के लिए केवल एक ही एंटरेंस प्रदान किया गया है।
 सभी कमरे के लिए पर्याप्त प्रकाश व्यवस्था प्रदान की गई है।
 सभी कमरे के लिए पर्याप्त वेंटिलेशन प्रदान किया गया है।
 सभी कमरे के लिए पर्याप्त स्टोरेज प्रदान किया गया है।
 सभी कमरे के लिए पर्याप्त फर्निचर प्रदान किया गया है।
 सभी कमरे के लिए पर्याप्त एप्लiances प्रदान किया गया है।
 सभी कमरे के लिए पर्याप्त सफाई सुविधाएं प्रदान की गई हैं।
 सभी कमरे के लिए पर्याप्त सुरक्षा सुविधाएं प्रदान की गई हैं।
 सभी कमरे के लिए पर्याप्त आवासीय सुविधाएं प्रदान की गई हैं।


कृपया नोट करें कि आवासीय इकाई के लिए केवल एक ही एंटरेंस प्रदान किया गया है।
 सभी कमरे के लिए पर्याप्त प्रकाश व्यवस्था प्रदान की गई है।
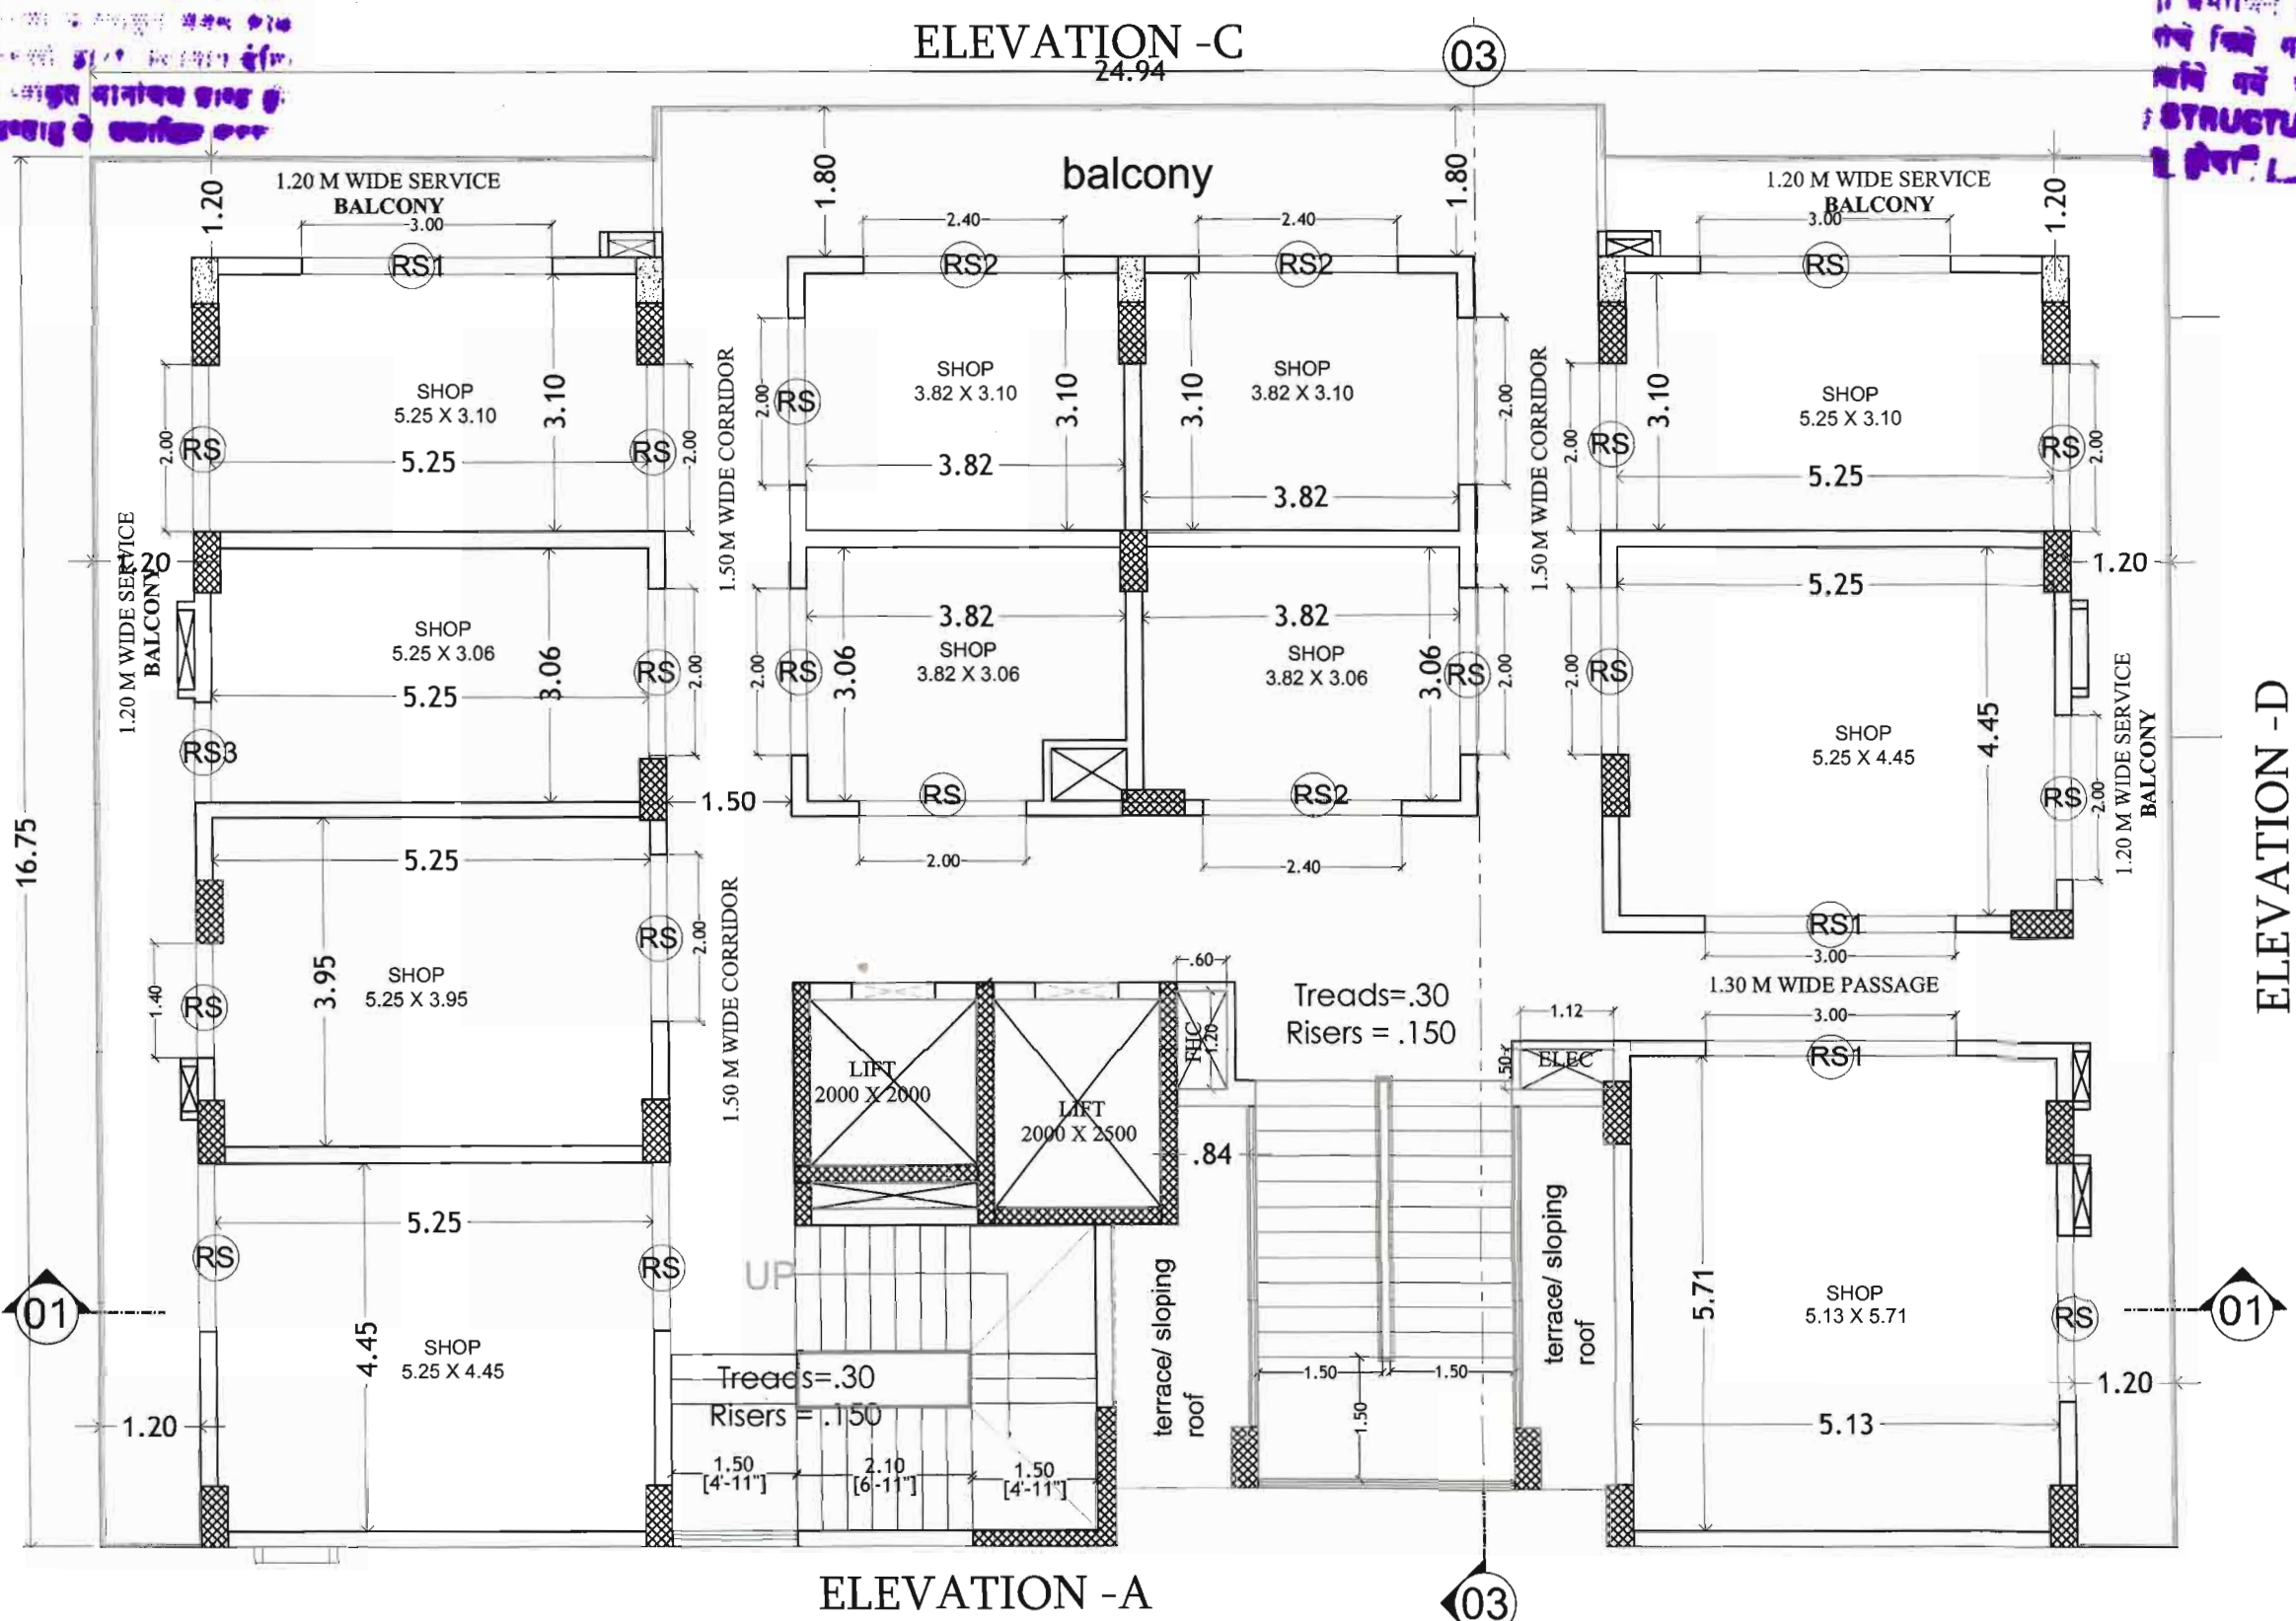


1ST FLOOR PLAN

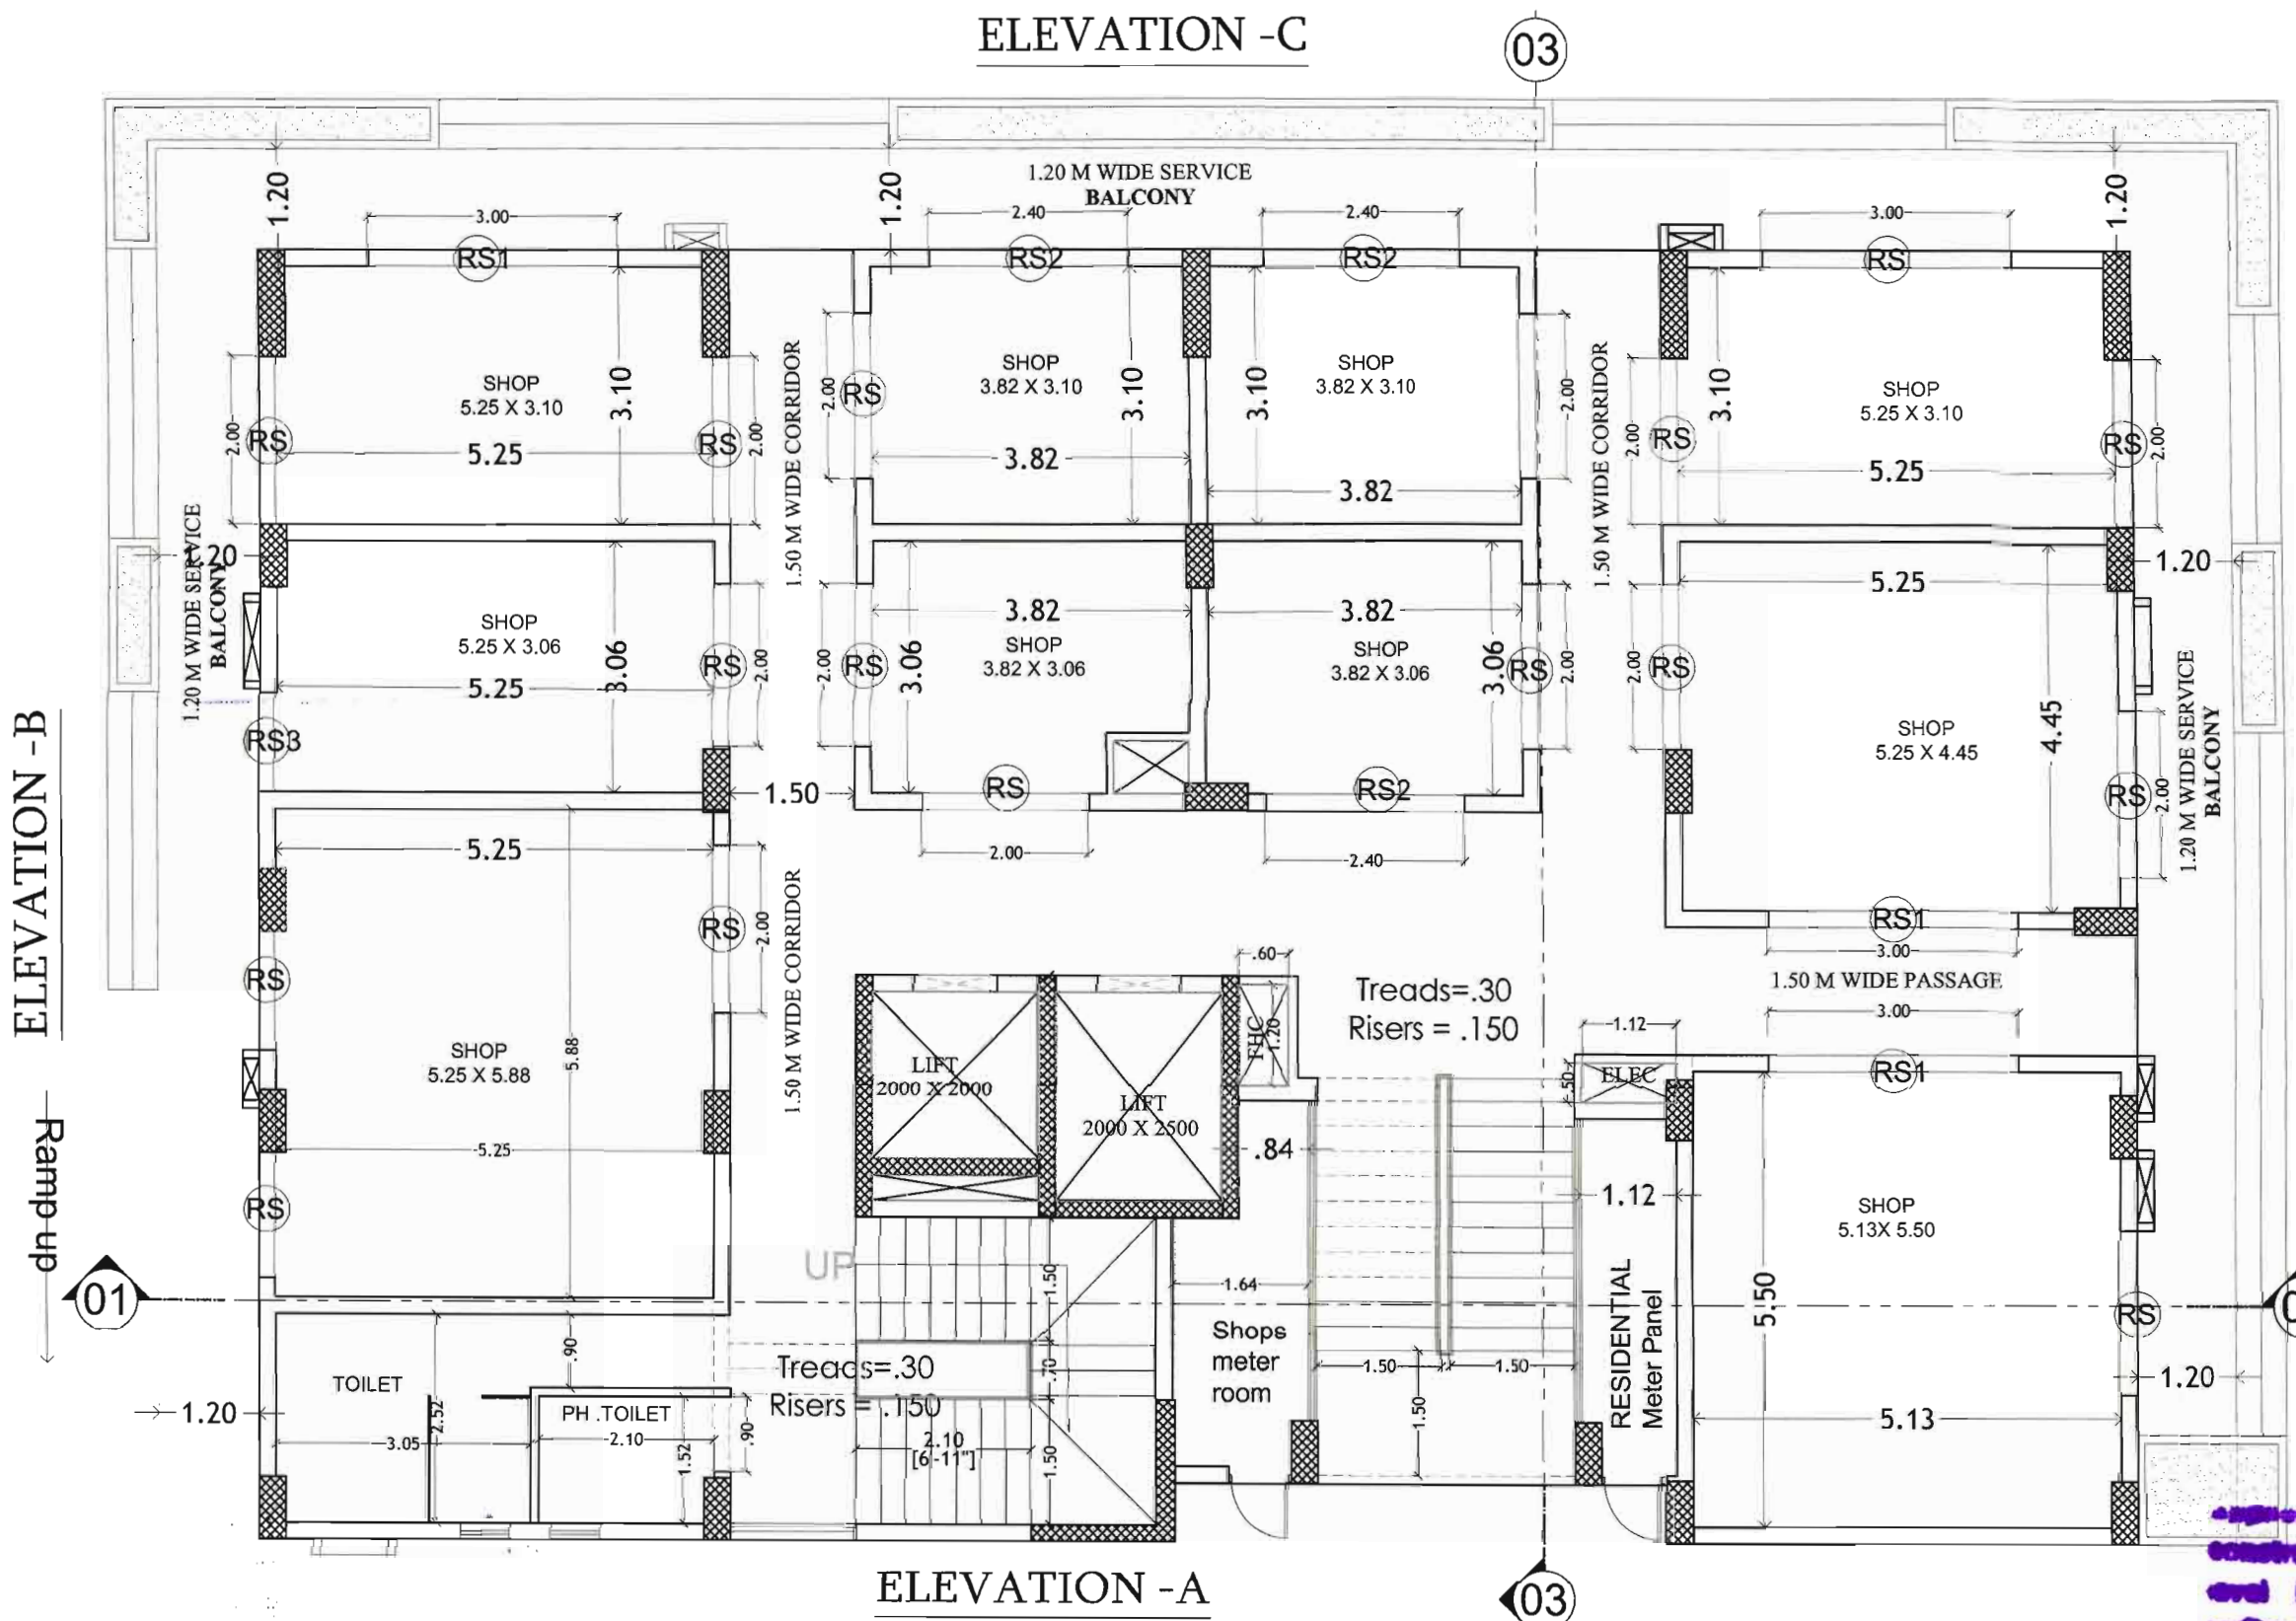



GROUND FLOOR PLAN

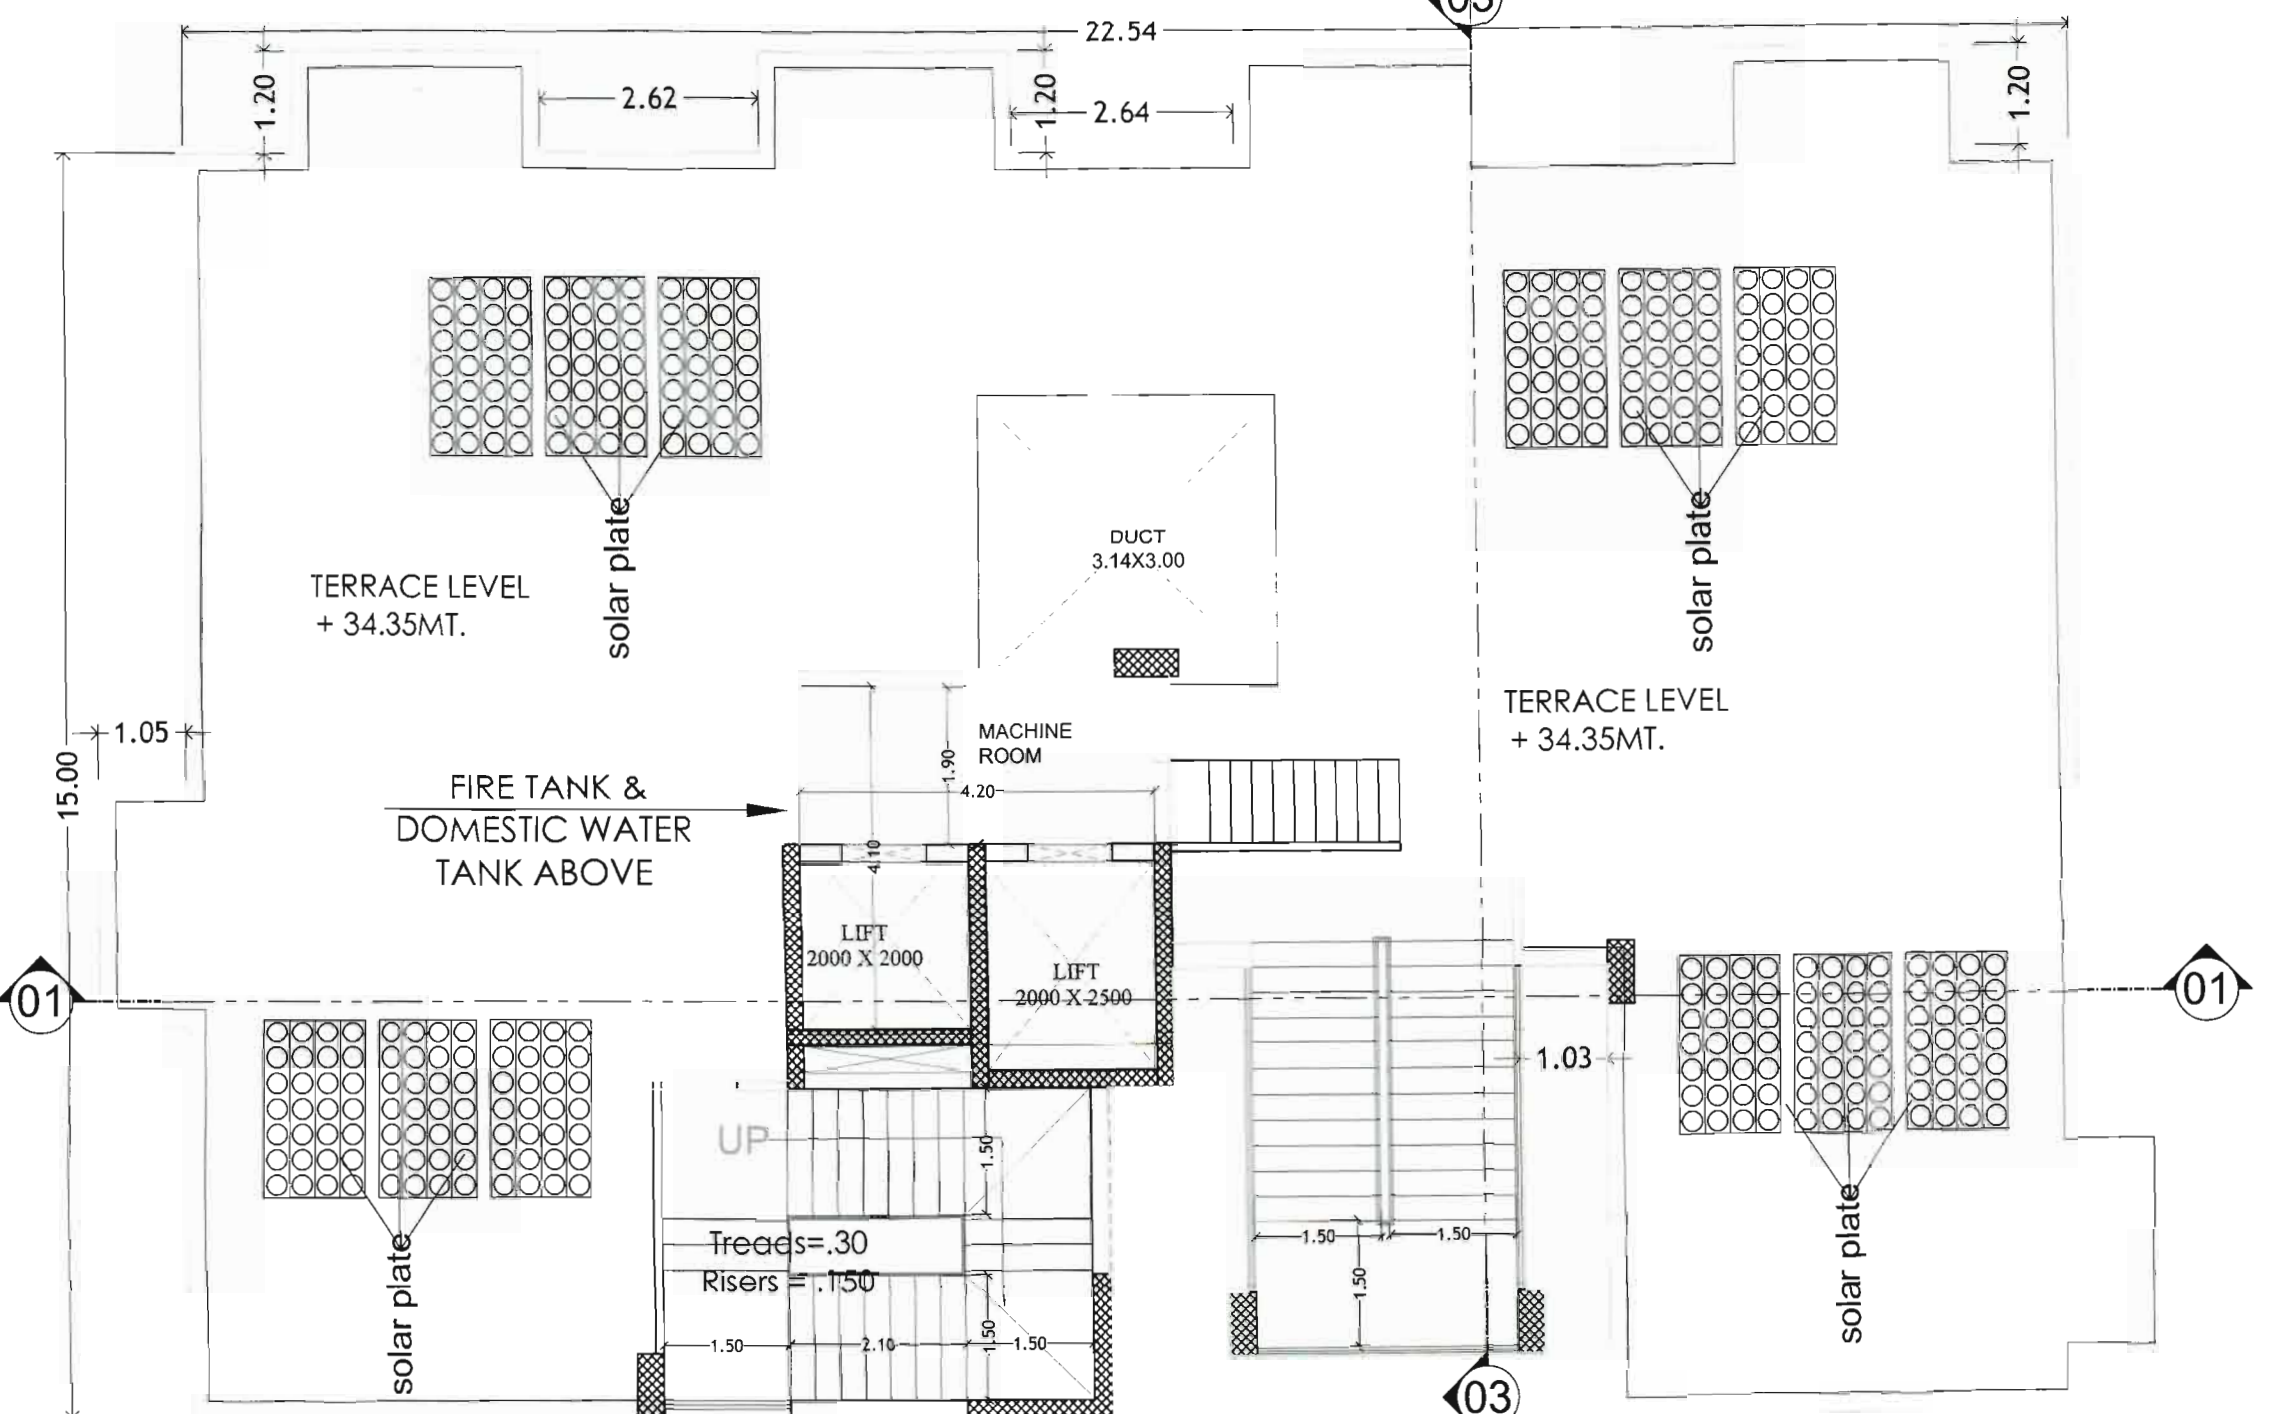

TERRACE FLOOR PLAN

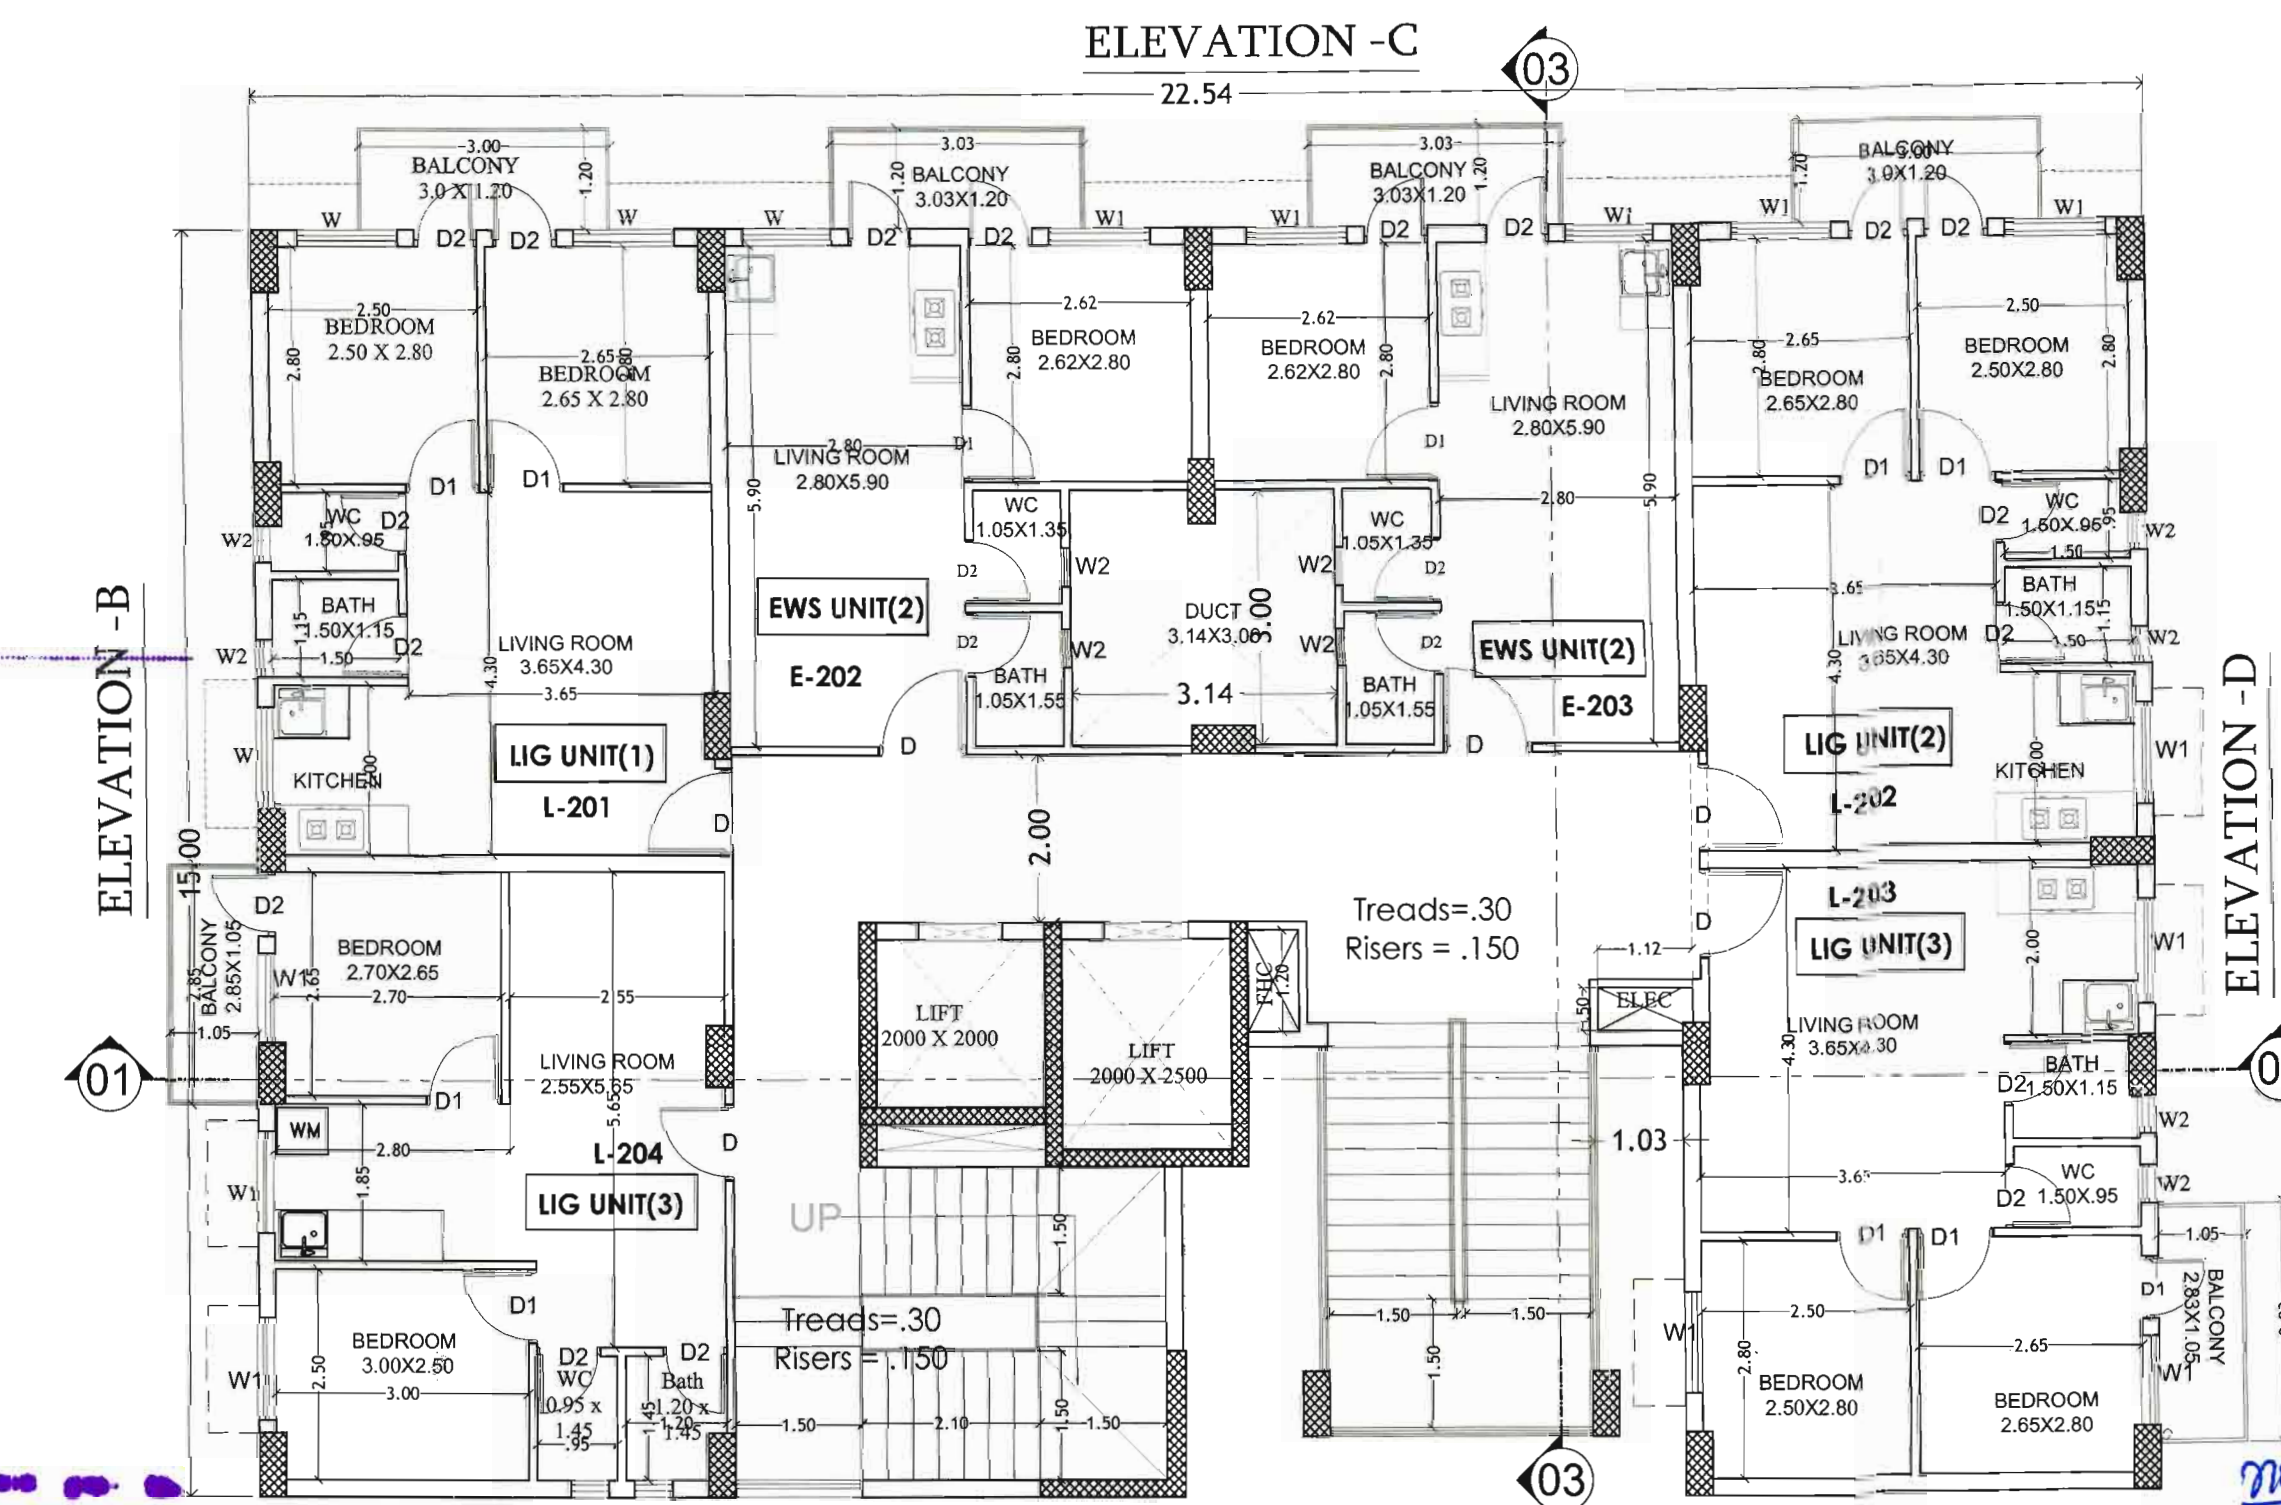

TYPICAL FLOOR PLAN
 2nd to 10th FLOOR PLAN

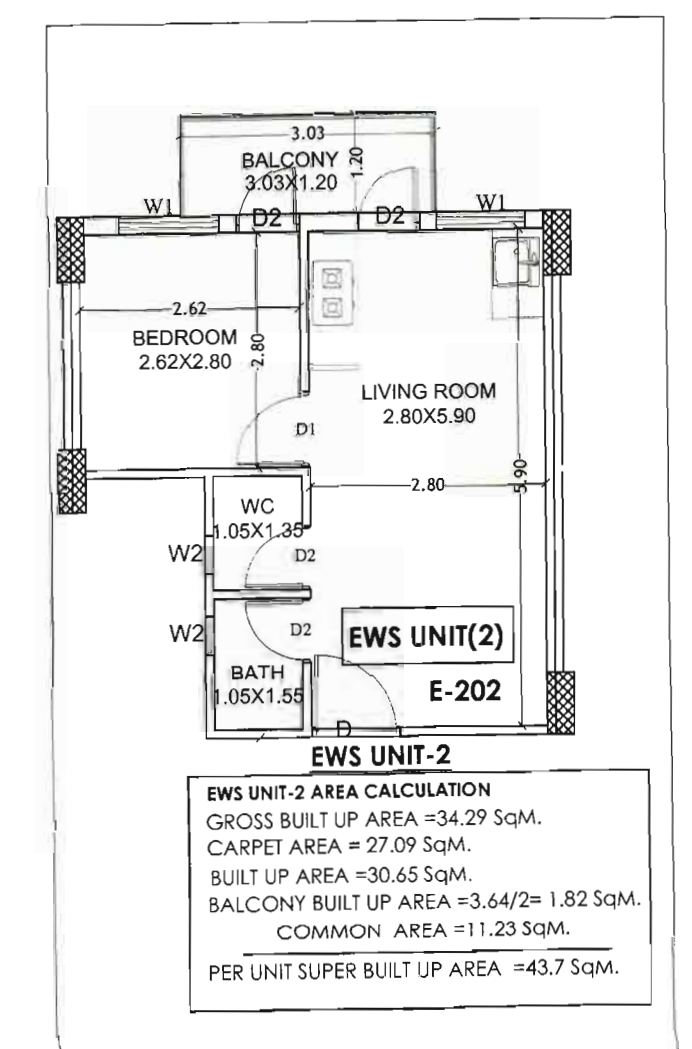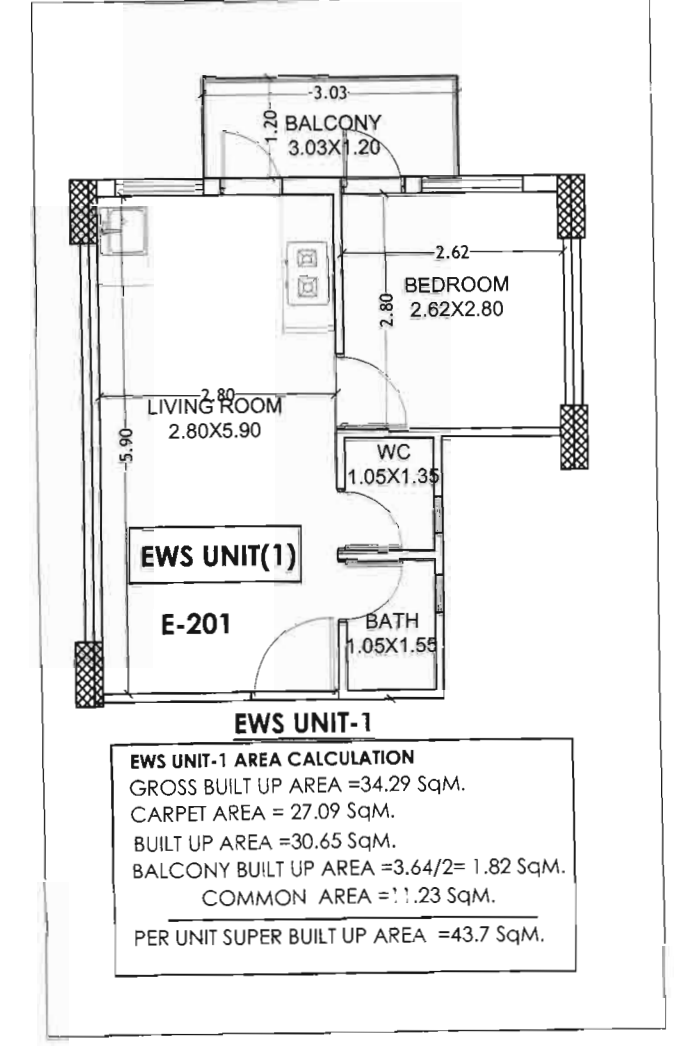

पञ्चोदित

उपनगर नियोजन (BP)
 जयपुर विकास प्राधिकरण जयपुर

अशियाना
 अशियाना ग्रुप लिमिटेड
 जयपुर विकास प्राधिकरण, जयपुर

BLOCK - F (EWS/LIG)									
Floor	G.R.A.	B.U.A.	PER PRELANT	CARPET AREA	BALCONY PER UNIT	COMMON	S.B.U.A	PER UNIT	S.B.U.A
2nd floor	45.37	45.37	45.37	36.54	3.65/2 = 1.82	14.81	100.00	100.00	100.00
L-201	45.37	45.37	45.37	36.54	3.65/2 = 1.82	14.81	100.00	100.00	100.00
L-202	45.37	45.37	45.37	36.54	3.65/2 = 1.82	14.81	100.00	100.00	100.00
L-203	45.37	45.37	45.37	36.54	3.65/2 = 1.82	14.81	100.00	100.00	100.00
L-204	45.37	45.37	45.37	36.54	3.65/2 = 1.82	14.81	100.00	100.00	100.00
3rd floor	45.37	45.37	45.37	36.54	3.65/2 = 1.82	14.81	100.00	100.00	100.00
L-301	45.37	45.37	45.37	36.54	3.65/2 = 1.82	14.81	100.00	100.00	100.00
L-302	45.37	45.37	45.37	36.54	3.65/2 = 1.82	14.81	100.00	100.00	100.00
L-303	45.37	45.37	45.37	36.54	3.65/2 = 1.82	14.81	100.00	100.00	100.00
L-304	45.37	45.37	45.37	36.54	3.65/2 = 1.82	14.81	100.00	100.00	100.00
4th floor	45.37	45.37	45.37	36.54	3.65/2 = 1.82	14.81	100.00	100.00	100.00
L-401	45.37	45.37	45.37	36.54	3.65/2 = 1.82	14.81	100.00	100.00	100.00
L-402	45.37	45.37	45.37	36.54	3.65/2 = 1.82	14.81	100.00	100.00	100.00
L-403	45.37	45.37	45.37	36.54	3.65/2 = 1.82	14.81	100.00	100.00	100.00
L-404	45.37	45.37	45.37	36.54	3.65/2 = 1.82	14.81	100.00	100.00	100.00
5th floor	45.37	45.37	45.37	36.54	3.65/2 = 1.82	14.81	100.00	100.00	100.00
L-501	45.37	45.37	45.37	36.54	3.65/2 = 1.82	14.81	100.00	100.00	100.00
L-502	45.37	45.37	45.37	36.54	3.65/2 = 1.82	14.81	100.00	100.00	100.00
L-503	45.37	45.37	45.37	36.54	3.65/2 = 1.82	14.81	100.00	100.00	100.00
L-504	45.37	45.37	45.37	36.54	3.65/2 = 1.82	14.81	100.00	100.00	100.00
6th floor	45.37	45.37	45.37	36.54	3.65/2 = 1.82	14.81	100.00	100.00	100.00
L-601	45.37	45.37	45.37	36.54	3.65/2 = 1.82	14.81	100.00	100.00	100.00
L-602	45.37	45.37	45.37	36.54	3.65/2 = 1.82	14.81	100.00	100.00	100.00
L-603	45.37	45.37	45.37	36.54	3.65/2 = 1.82	14.81	100.00	100.00	100.00
L-604	45.37	45.37	45.37	36.54	3.65/2 = 1.82	14.81	100.00	100.00	100.00
7th floor	45.37	45.37	45.37	36.54	3.65/2 = 1.82	14.81	100.00	100.00	100.00
L-701	45.37	45.37	45.37	36.54	3.65/2 = 1.82	14.81	100.00	100.00	100.00
L-702	45.37	45.37	45.37	36.54	3.65/2 = 1.82	14.81	100.00	100.00	100.00
L-703	45.37	45.37	45.37	36.54	3.65/2 = 1.82	14.81	100.00	100.00	100.00
L-704	45.37	45.37	45.37	36.54	3.65/2 = 1.82	14.81	100.00	100.00	100.00
8th floor	45.37	45.37	45.37	36.54	3.65/2 = 1.82	14.81	100.00	100.00	100.00
L-801	45.37	45.37	45.37	36.54	3.65/2 = 1.82	14.81	100.00	100.00	100.00
L-802	45.37	45.37	45.37	36.54	3.65/2 = 1.82	14.81	100.00	100.00	100.00
L-803	45.37	45.37	45.37	36.54	3.65/2 = 1.82	14.81	100.00	100.00	100.00
L-804	45.37	45.37	45.37	36.54	3.65/2 = 1.82	14.81	100.00	100.00	100.00
9th floor	45.37	45.37	45.37	36.54	3.65/2 = 1.82	14.81	100.00	100.00	100.00
L-901	45.37	45.37	45.37	36.54	3.65/2 = 1.82	14.81	100.00	100.00	100.00
L-902	45.37	45.37	45.37	36.54	3.65/2 = 1.82	14.81	100.00	100.00	100.00
L-903	45.37	45.37	45.37	36.54	3.65/2 = 1.82	14.81	100.00	100.00	100.00
L-904	45.37	45.37	45.37	36.54	3.65/2 = 1.82	14.81	100.00	100.00	100.00
10th floor	45.37	45.37	45.37	36.54	3.65/2 = 1.82	14.81	100.00	100.00	100.00
L-1001	45.37	45.37	45.37	36.54	3.65/2 = 1.82	14.81	100.00	100.00	100.00
L-1002	45.37	45.37	45.37	36.54	3.65/2 = 1.82	14.81	100.00	100.00	100.00
L-1003	45.37	45.37	45.37	36.54	3.65/2 = 1.82	14.81	100.00	100.00	100.00
L-1004	45.37	45.37	45.37	36.54	3.65/2 = 1.82	14.81	100.00	100.00	100.00

PROJECT TITLE :
 PROPOSED GROUP HOUSING
 PLOT KHASRA
 NO.:-876,877,878,879&880,
 881,882, 883, 884,885,886,887,905
 IN VILLAGE-BHANKROTA KALAN
 TEHSIL-SANGNER,DIST. JAIPUR.

CLIENT :
 ASHIANA HOUSING, JAIPUR

ARCHITECTS
Ricky Mathur & Associates
 architects interior designers planners
 33, Dhuleshwar Garden,
 Jaipur. (RAJ.) India. 302 001
 Tel: 91-141-236 2688, 4004700
 Fax: 91-141-400 8700
 e-mail: ricky@rickymathur.com

DRAWING TITLE :
 BLOCK - F (COMMERCIAL)
 PLANS

SCALE 1:100
 DATE JANUARY 2023
 DEALT BY
 STATUS SUBMISSION

ARCHITECT'S SIGN.

 RICKY MATHUR
 CA-24247

CLIENT'S SIGN.

For Ashiana Housing Limited

 Authorised Signatory

SHEET NO. - 25
 NORTH -

आवासीय का संयोजन किया की जायेगा
अवगत भूमि/संपत्ति के प्रति स्वामित्व का
हस्ताक्षर-पत्र नहीं माना जायेगा और यह
हस्ताक्षर-पत्र के हस्ताक्षर स्वामित्व अधिकार
की प्रमाणित होंगे।
शेष शेष भू-खंड पर अवगत मानचित्र के
अनुसार भवन निर्माण का संयोजन
(STRUCTURE) का निर्माण करना
होगा


आवासीय का संयोजन किया की जायेगा
अवगत भूमि/संपत्ति के प्रति स्वामित्व का
हस्ताक्षर-पत्र नहीं माना जायेगा और यह
हस्ताक्षर-पत्र के हस्ताक्षर स्वामित्व अधिकार
की प्रमाणित होंगे।
शेष शेष भू-खंड पर अवगत मानचित्र के
अनुसार भवन निर्माण का संयोजन
(STRUCTURE) का निर्माण करना
होगा

उपनगर नियोजन (BP)
जयपुर विकास प्राधिकरण, जयपुर

अनुमोदित

अतिरिक्त मूल्यांकन और नियोजन
जयपुर विकास प्राधिकरण, जयपुर

अवगत भूमि/संपत्ति के प्रति स्वामित्व का
हस्ताक्षर-पत्र नहीं माना जायेगा और यह
हस्ताक्षर-पत्र के हस्ताक्षर स्वामित्व अधिकार
की प्रमाणित होंगे।
शेष शेष भू-खंड पर अवगत मानचित्र के
अनुसार भवन निर्माण का संयोजन
(STRUCTURE) का निर्माण करना
होगा

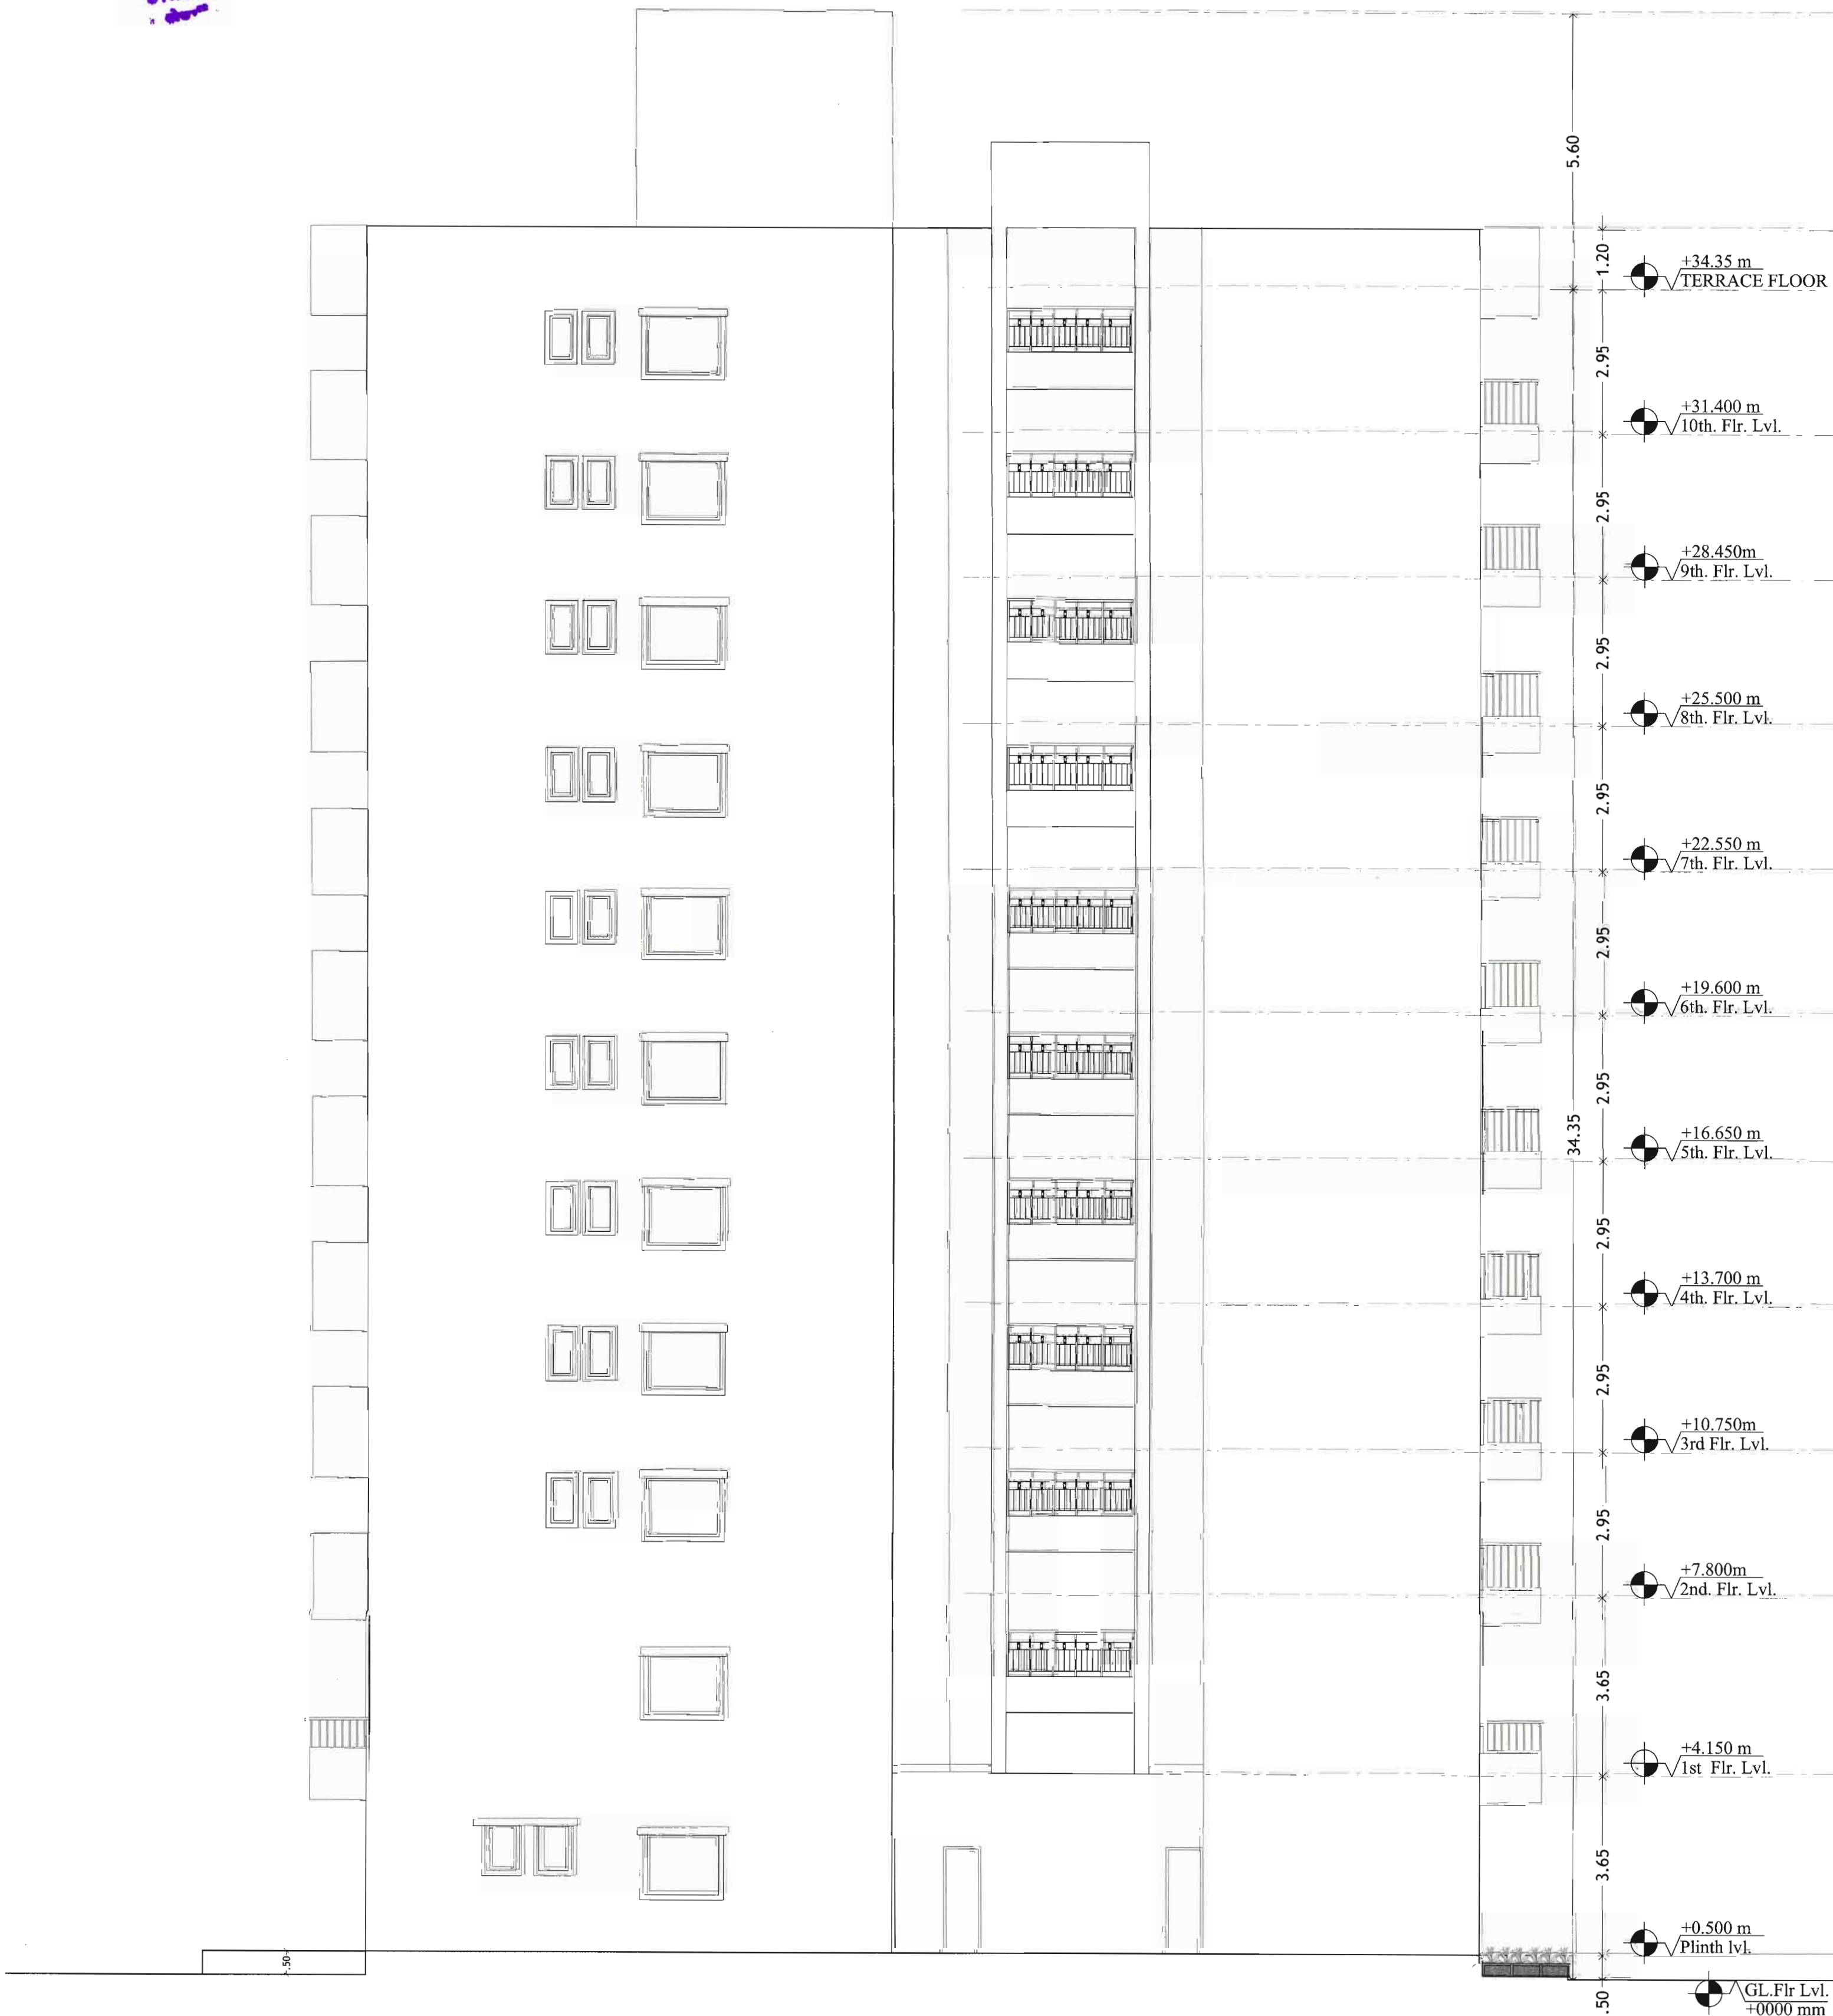

ELEVATION -A



ELEVATION -B

PROJECT TITLE :	
PROPOSED GROUP HOUSING PLOT KHASRA NO.: -876,877,878,879&880, 881,882,883,884,885,886,887,905 IN VILLAGE-BHANKROTA KALAN TEHSIL-SANGNER, DIST. JAIPUR.	
CLIENT :	
ASHIANA HOUSING, JAIPUR	
ARCHITECTS	
Ricky Mathur & Associates architects interior designers planners 33, Dhuleshwar Garden, Jaipur. (RAJ.) India. 302 001 Tel: 91-141-236 2688, 4004700 Fax: 91-141-400 8700 e-mail: ricky@rickymathur.com	
DRAWING TITLE :-	
BLOCK- F (COMMERCIAL) ELEVATIONS	
SCALE 1 : 100	DATE JANUARY 2023
DEALT BY	STATUS SUBMISSION
ARCHITECT'S SIGN.	
	
CLIENT'S SIGN.	
	
SHEET NO. - 26	NORTH -

Construction checked at plot
level before proceeding to
other construction.

आवासीय का अनुमति पत्र की शर्तों
अनुसार भूखण्ड के प्रति स्थापित
आवासीय-वर्ग नहीं माना जाएगा और
इसके निर्माण के अंतर्गत संरचनात्मक
प्रमाणित होगा।
केवल किन्हीं सर्वेक्षण/संरचनात्मक
प्रमाणित (STRUCTURES) का स्थापित
होना होगा।


उपनगर नियोजन (BP)
जयपुर विकास प्राधिकरण, जयपुर

अतिरिक्त मुख्य नगर नियोजक
जयपुर विकास प्राधिकरण, जयपुर

यदि बाहर से कोई भी व्यक्ति/व्यक्ति
आवासीय के लिए घर बनाने के लिए
आवासीय-वर्ग के लिए स्थापित
आवासीय-वर्ग के लिए स्थापित
ELEVATION -C

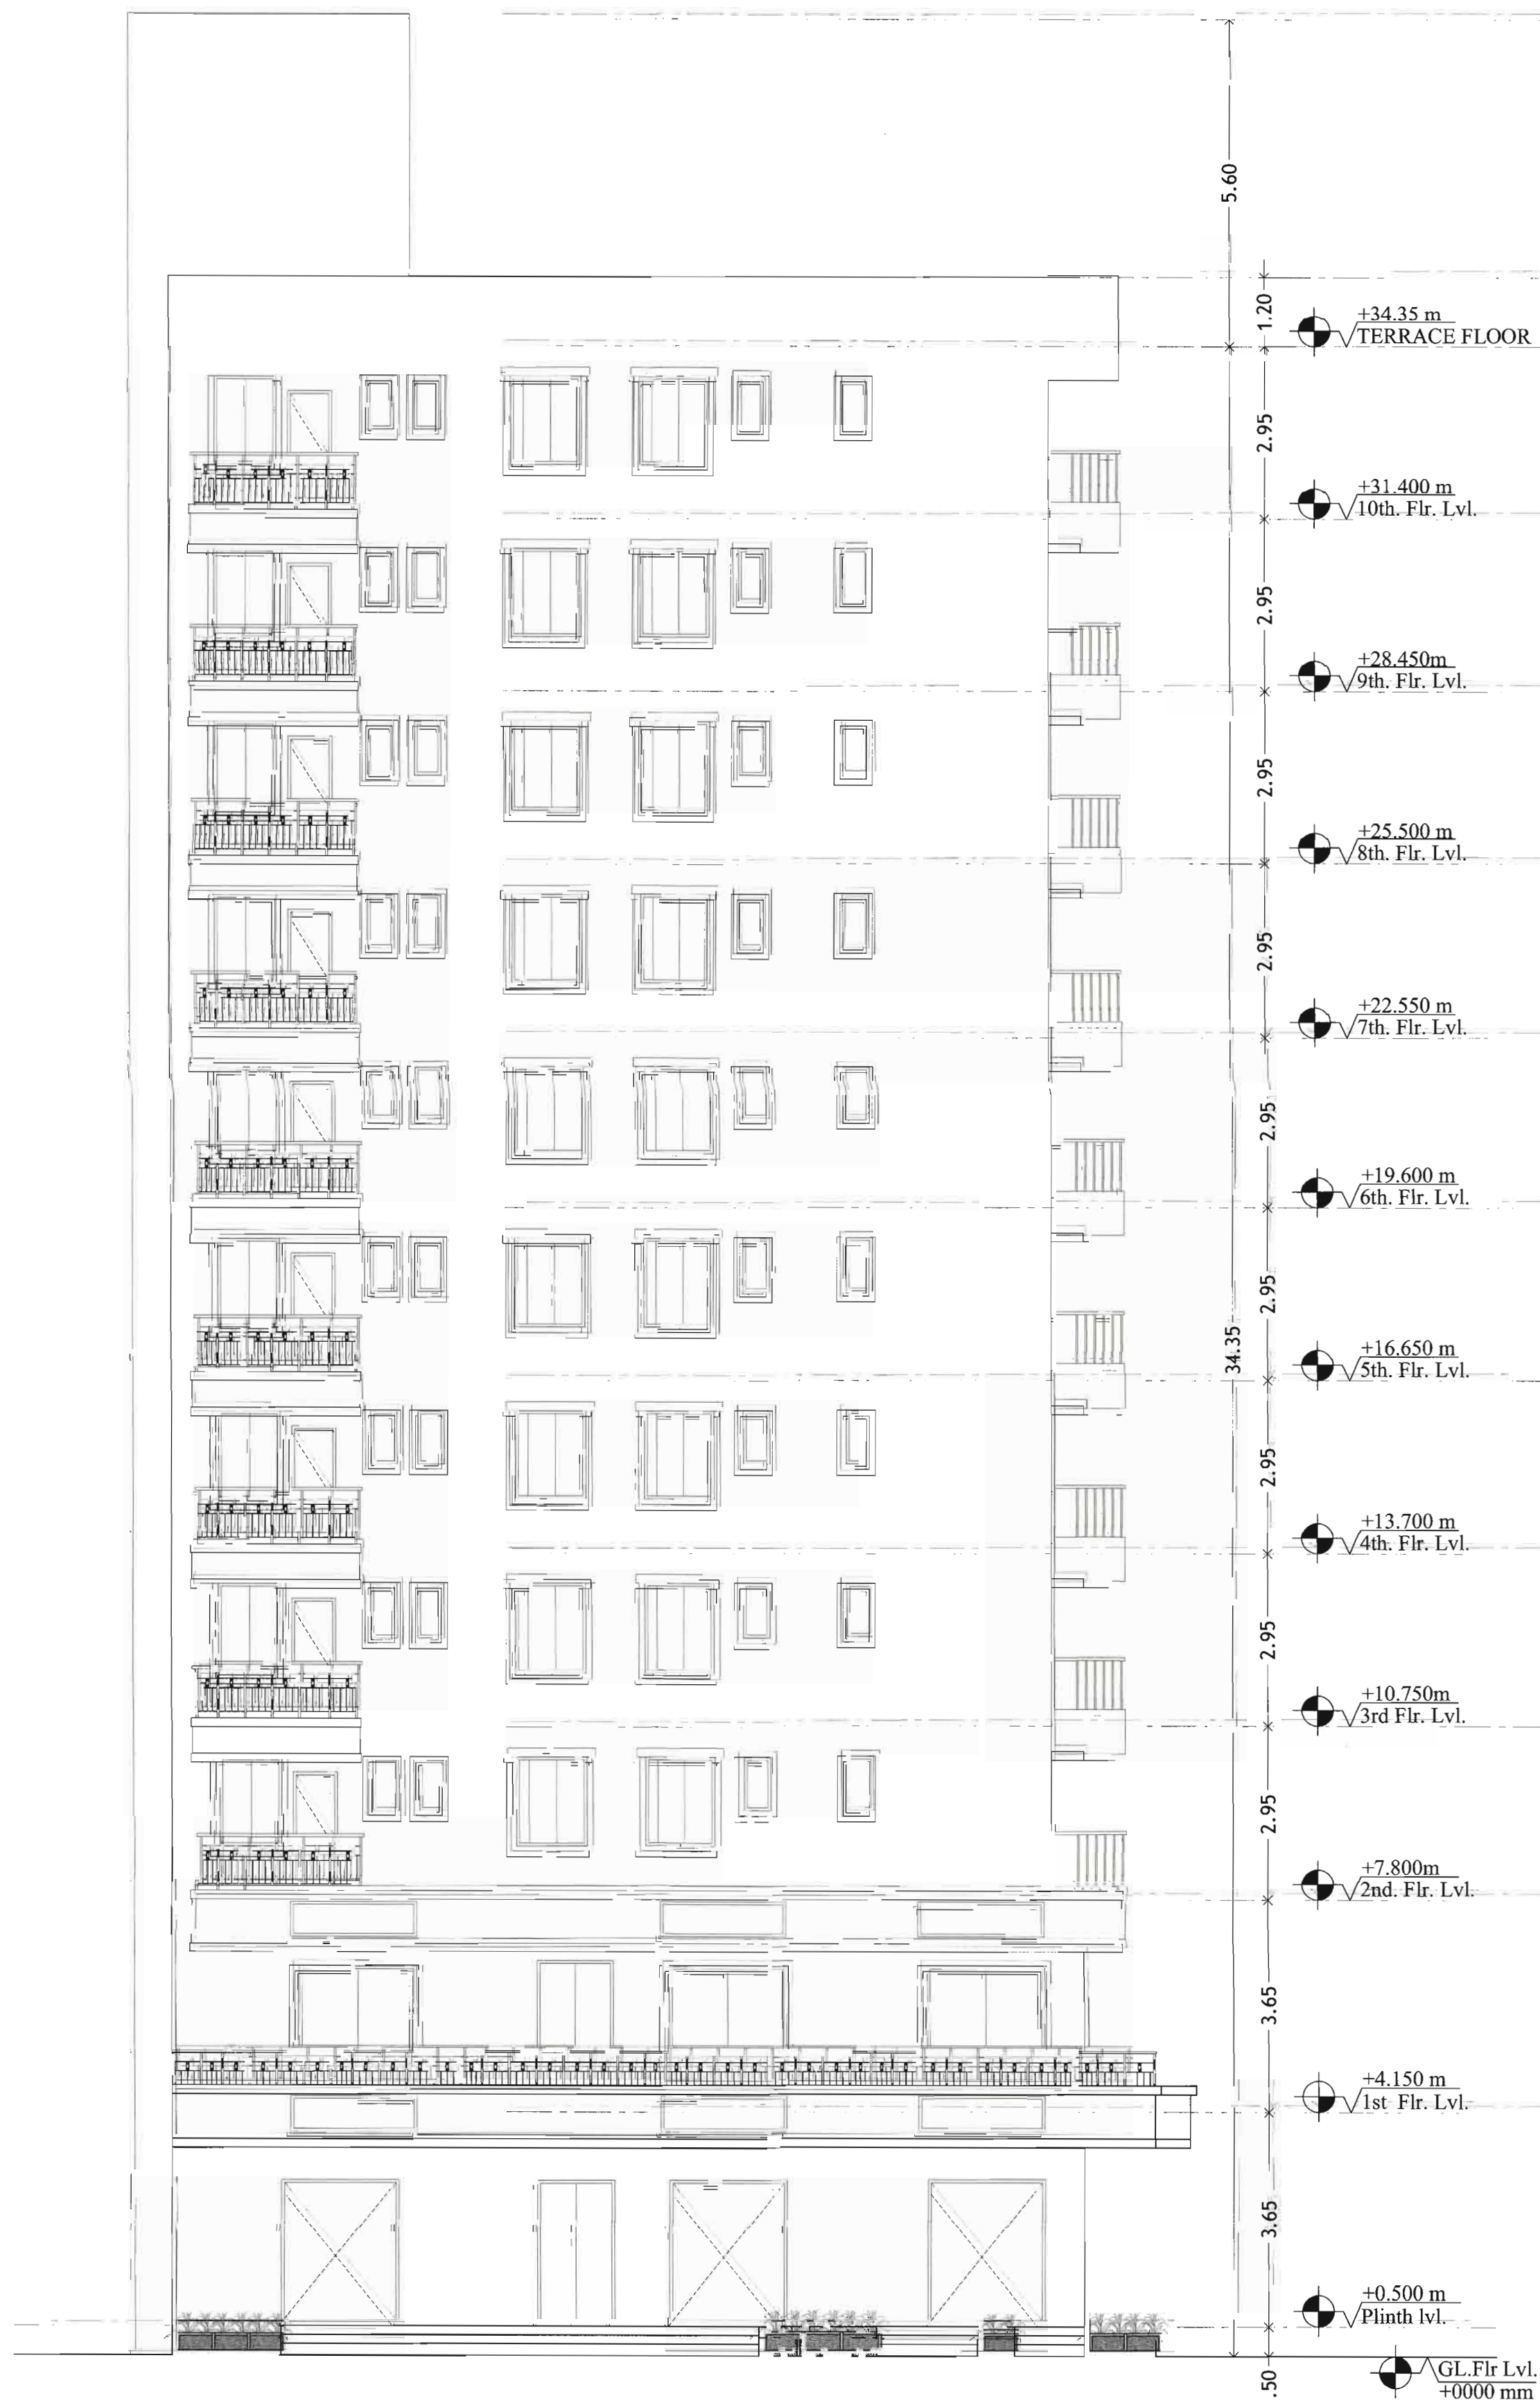

ELEVATION -D

PROJECT TITLE :
PROPOSED GROUP HOUSING
PLOT KHASRA
NO.:-876,877,878,879&880,
881,882,883,884,885,886,887,905
IN VILLAGE-BHANKROTA KALAN
TEHSIL-SANGNER,DIST. JAIPUR.

CLIENT :
ASHIANA HOUSING, JAIPUR

ARCHITECTS
Ricky Mathur & Associates
architects interior designers planners
33, Dhuleshwar Garden,
Jaipur. (RAJ.) India. 302 001
Tel: 91-141-236 2688, 4004700
Fax: 91-141-400 8700
e-mail: ricky@rickymathur.com

DRAWING TITLE :-
BLOCK- F (COMMERCIAL)
ELEVATIONS

SCALE 1 : 100 DATE JANUARY 2023

DEALT BY STATUS SUBMISSION

ARCHITECT'S SIGN.
Ricky Mathur
RICKY MATHUR
CA-24247

CLIENT'S SIGN.
For Ashiana Housing Limited
Ricky Mathur
Authorized Signatory

SHEET NO. - 27 NORTH -


अनुमोदित का अर्थ है कि यह योजना/ड्राइंग
सम्पूर्ण रूप से सही है और इसमें कोई भी
त्रुटि नहीं है। यह योजना/ड्राइंग
सम्पूर्ण रूप से सही है और इसमें कोई भी
त्रुटि नहीं है।

अनुमोदित का अर्थ है कि यह योजना/ड्राइंग
सम्पूर्ण रूप से सही है और इसमें कोई भी
त्रुटि नहीं है। यह योजना/ड्राइंग
सम्पूर्ण रूप से सही है और इसमें कोई भी
त्रुटि नहीं है।


उपनगर निगम (BP)
जयपुर विकास प्राधिकरण जयपुर

अतिरिक्त प्रमाणित किया गया
जन मानचित्र संहिता
जयपुर विकास प्राधिकरण, जयपुर

अनुमोदित का अर्थ है कि यह योजना/ड्राइंग
सम्पूर्ण रूप से सही है और इसमें कोई भी
त्रुटि नहीं है। यह योजना/ड्राइंग
सम्पूर्ण रूप से सही है और इसमें कोई भी
त्रुटि नहीं है।

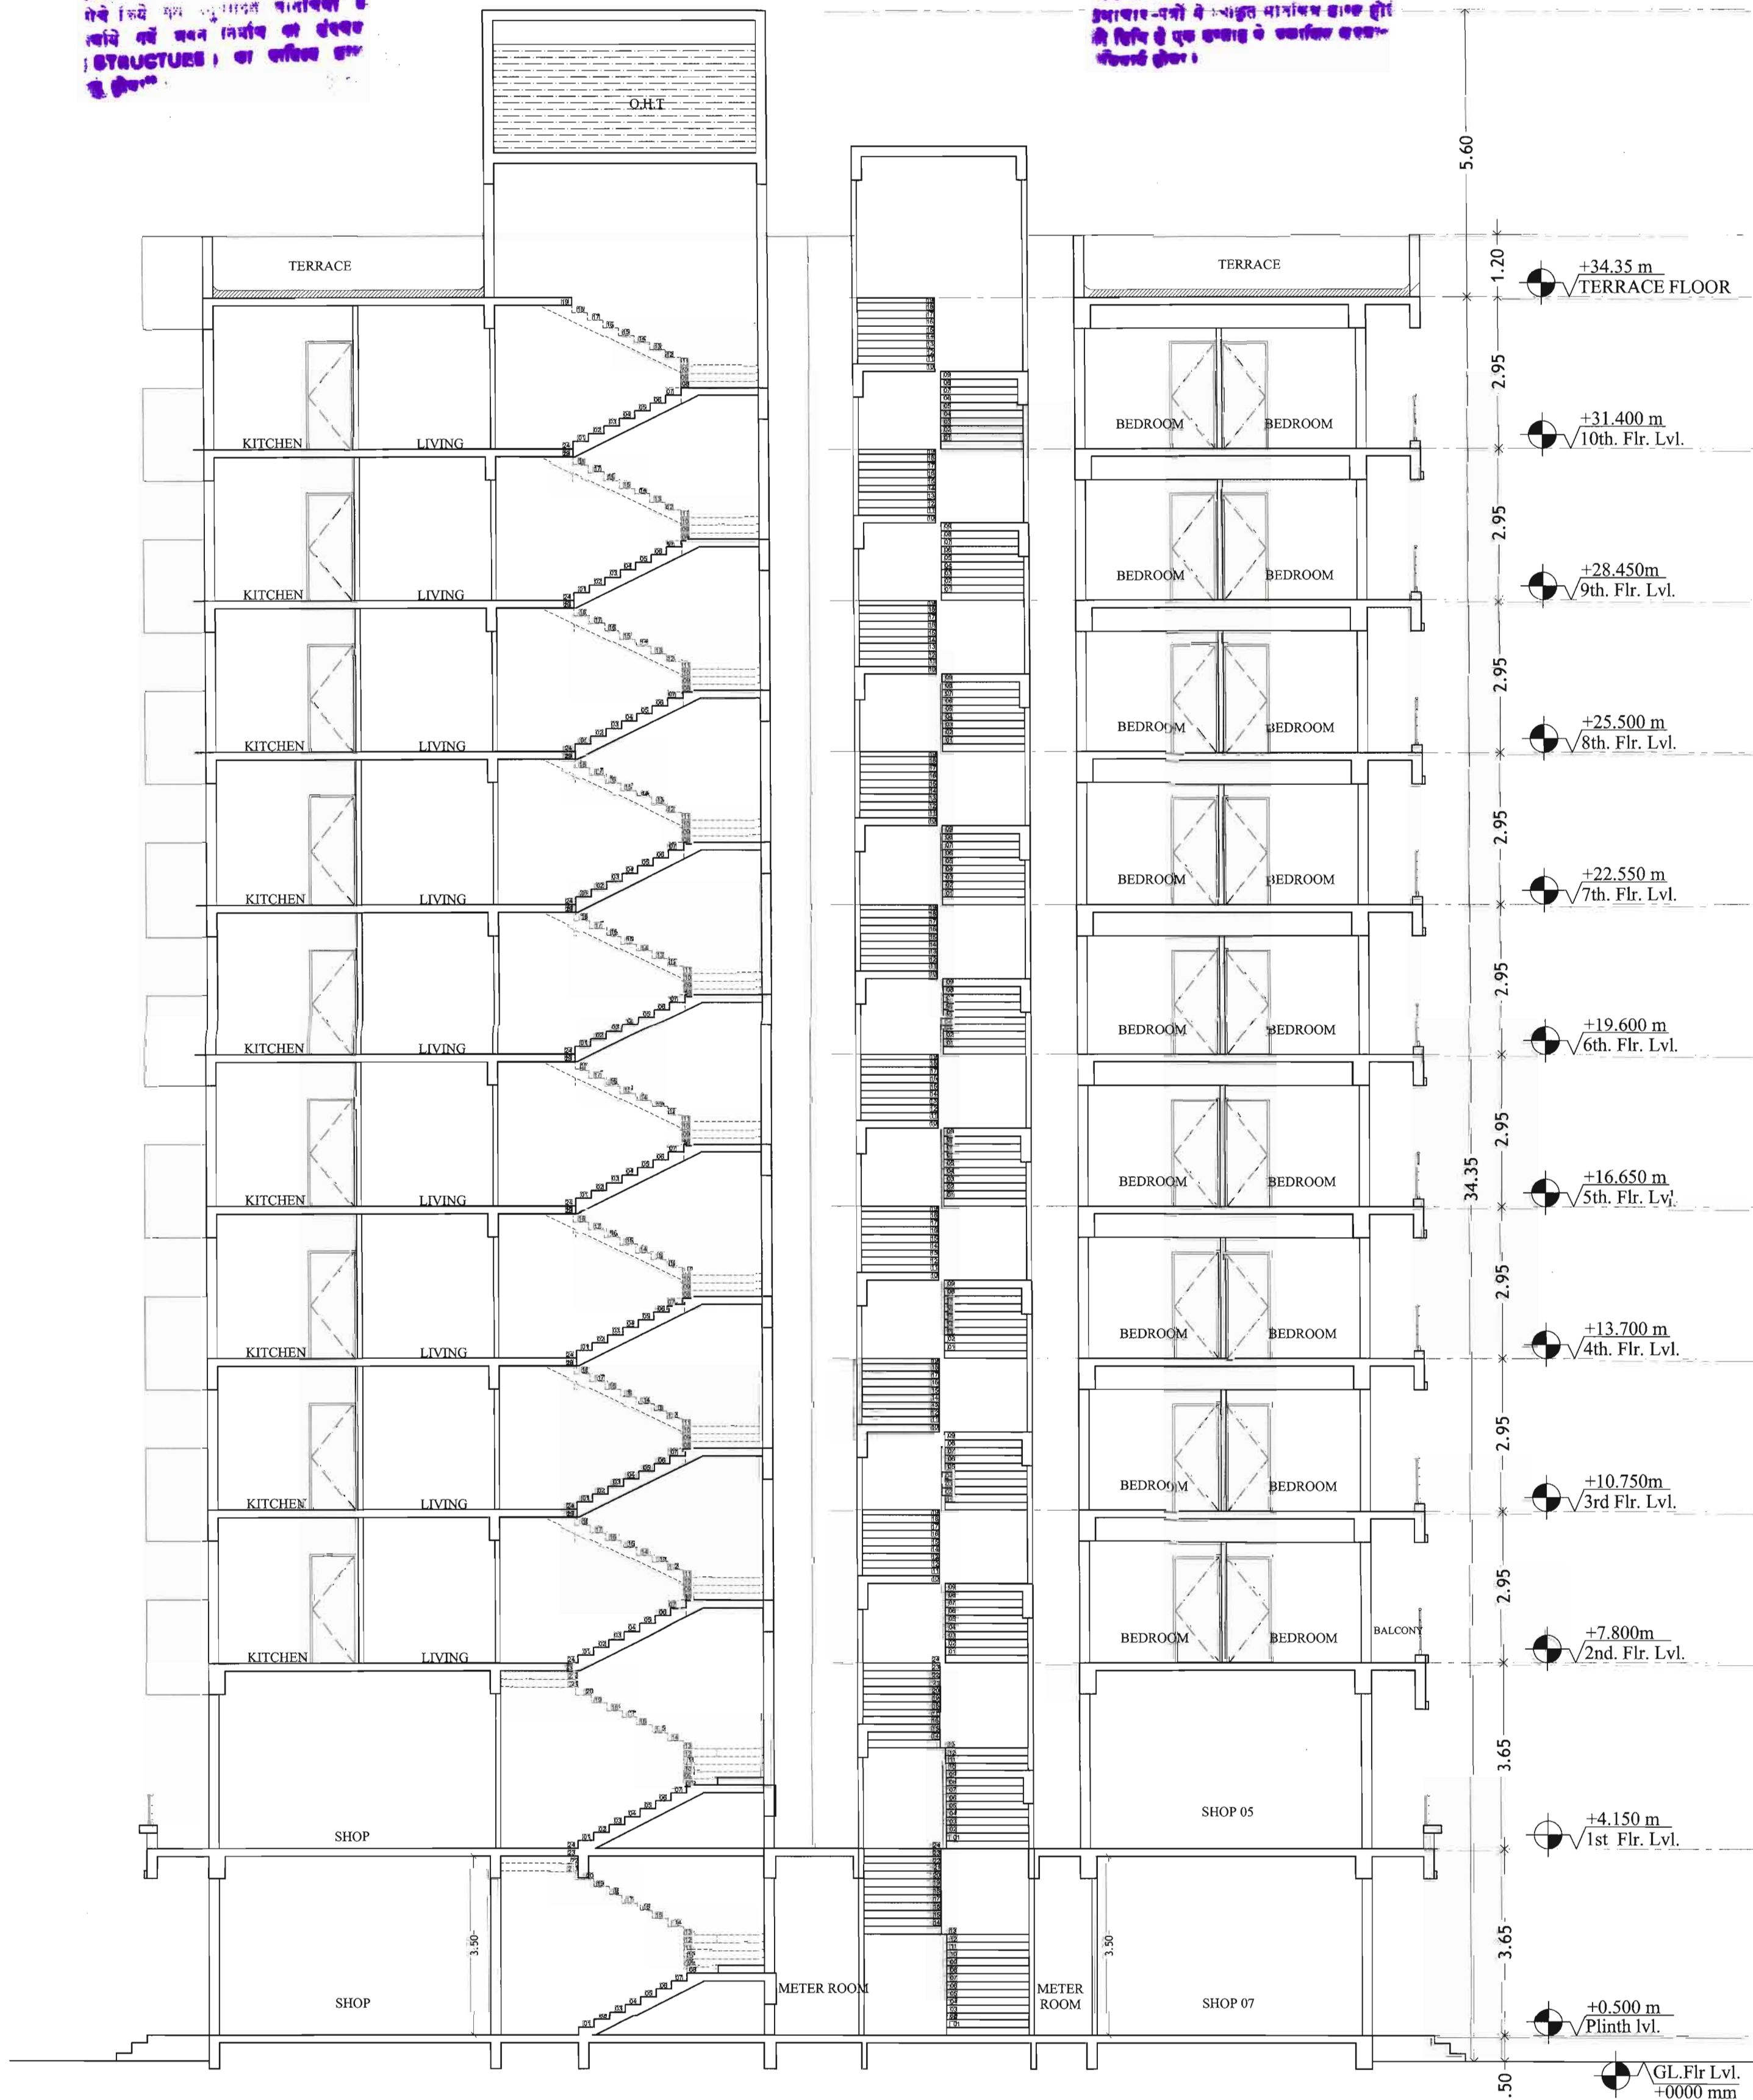

SECTION ON -01-01

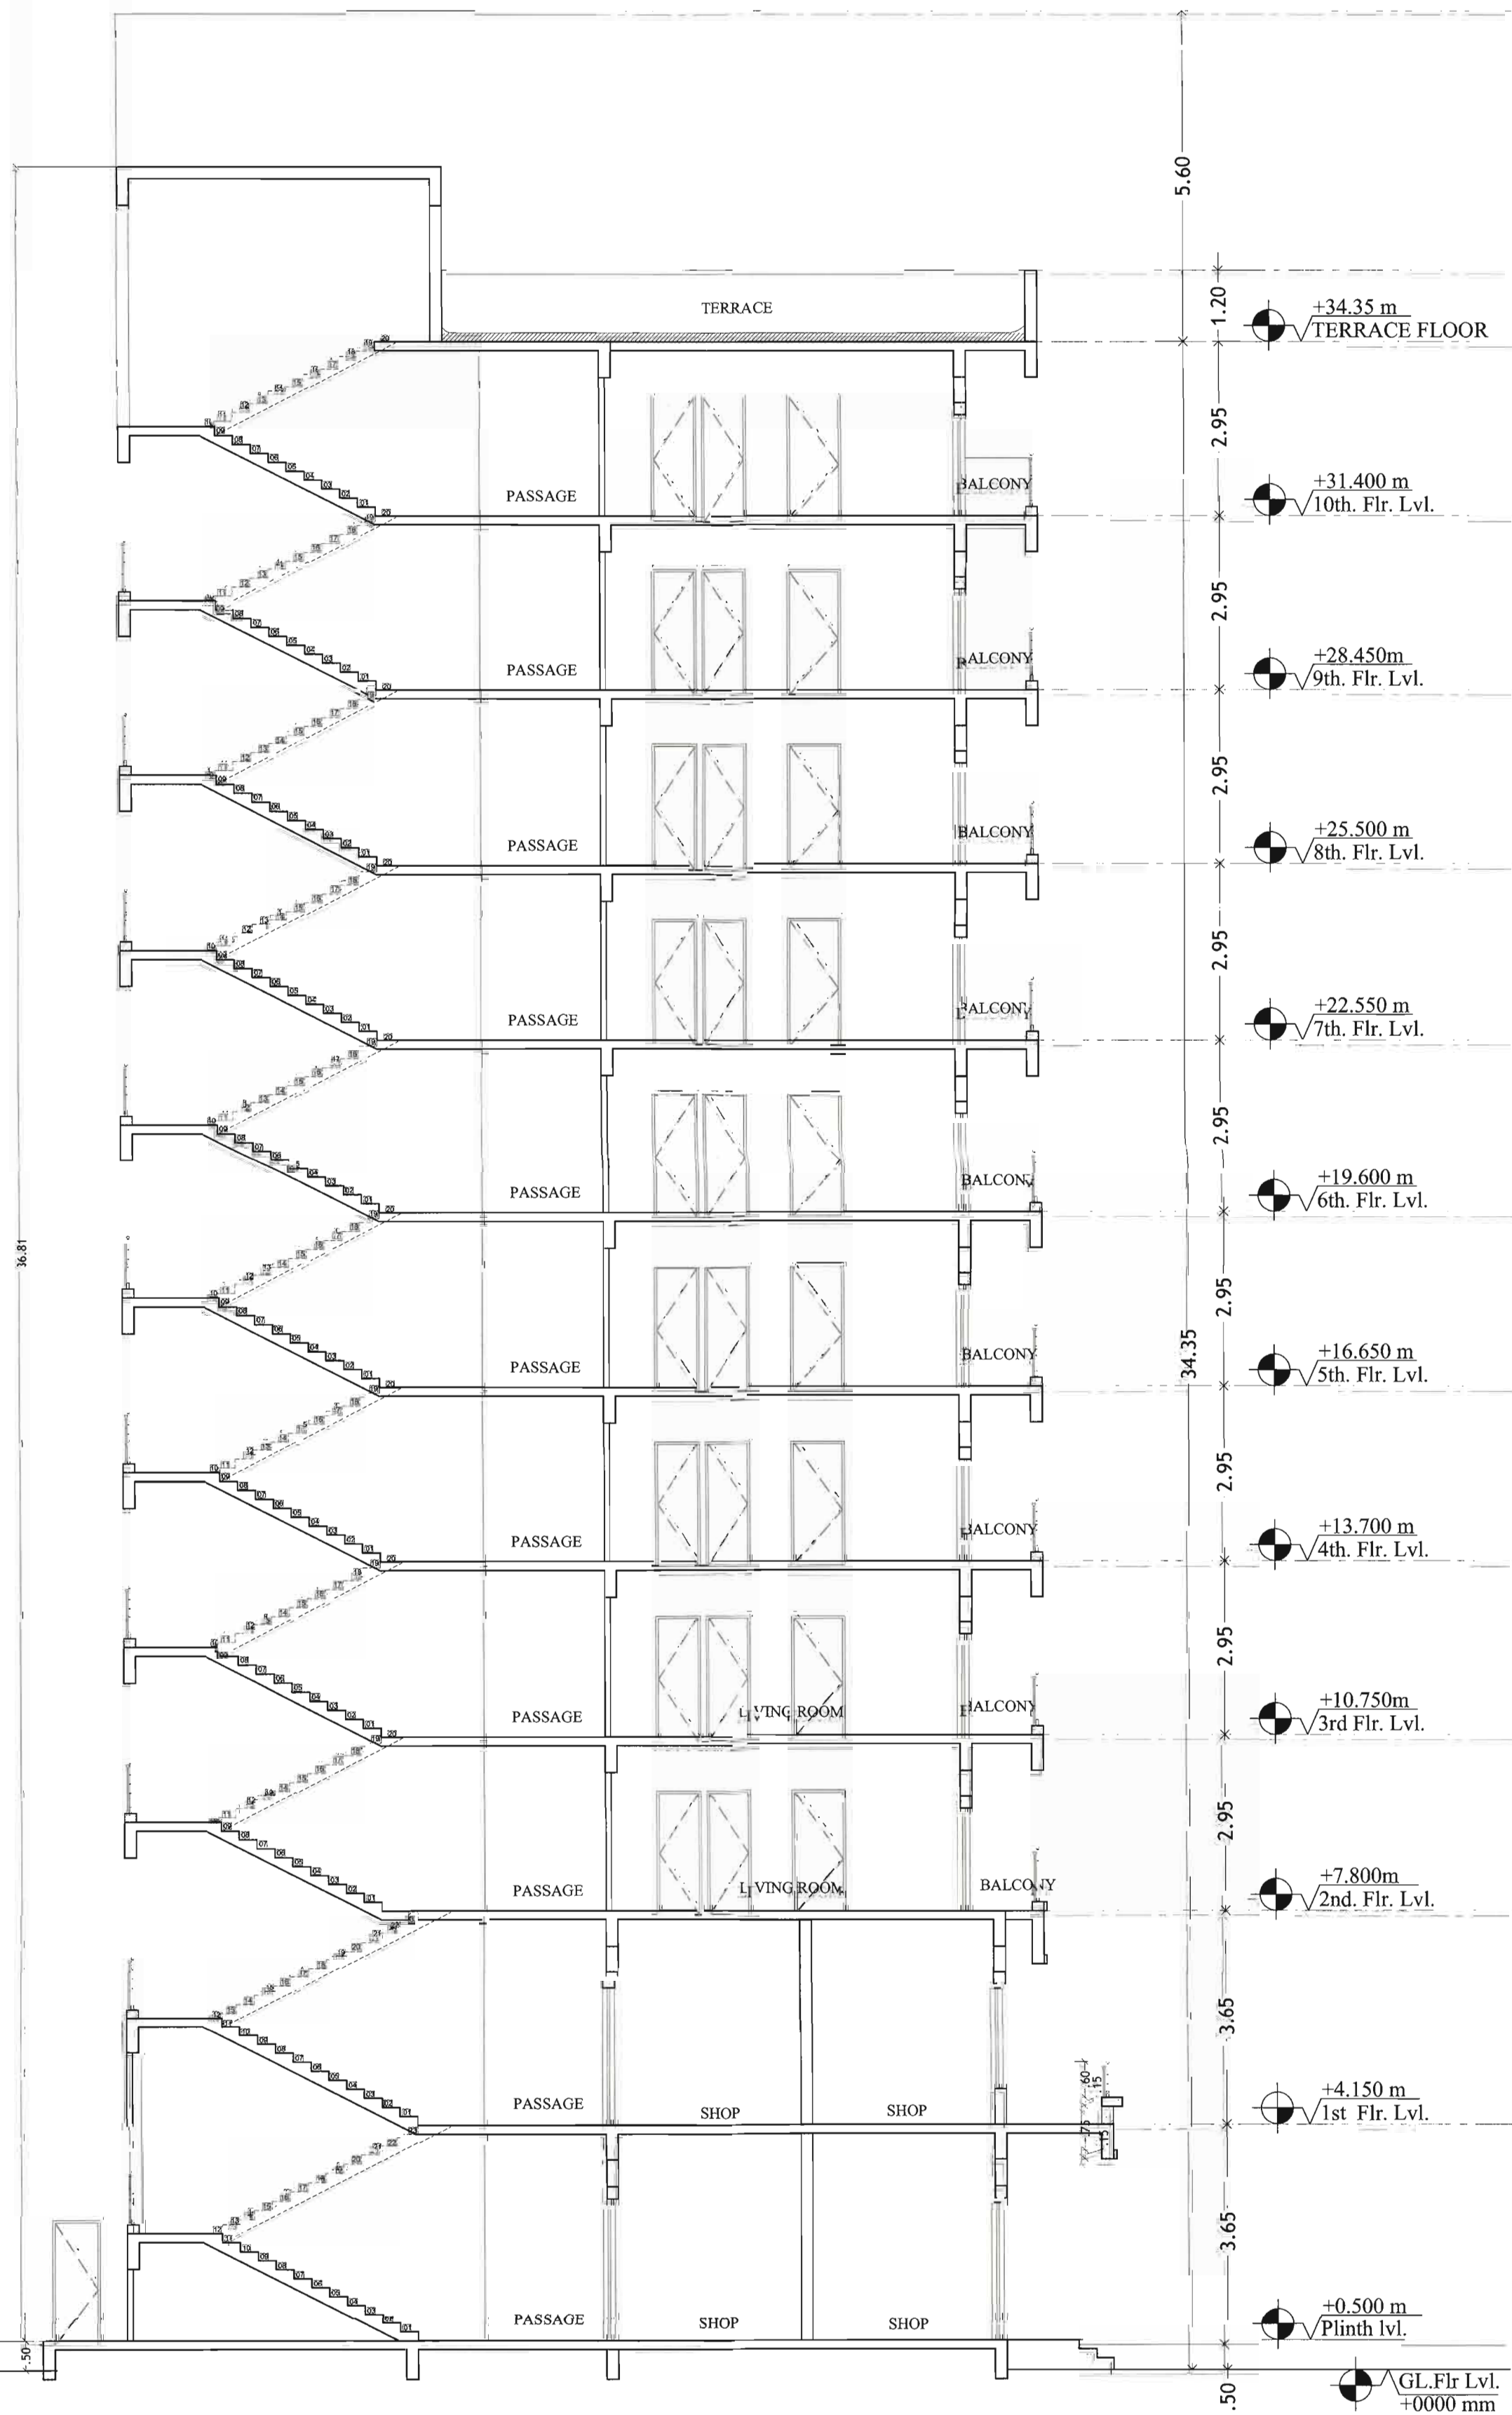

SECTION ON 03-03

PROJECT TITLE :
PROPOSED GROUP HOUSING
PLOT KHASRA
NO.: 876,877,878,879&880,
881,882,883,884,885,886,887,905
IN VILLAGE-BHANKROTA KALAN
TEHSIL-SANGNER,DIST. JAIPUR.


CLIENT :
ASHIANA HOUSING, JAIPUR

ARCHITECTS
Ricky Mathur & Associates
architects interior designers planners
33, Dhuleshwar Garden,
Jaipur, (RAJ.) India, 302 001
Tel: 91-141-236 2688, 4004700
Fax: 91-141-400 8700
e-mail: ricky@rickymathur.com

DRAWING TITLE :-
BLOCK- F ((COMMERCIAL)
SECTIONS

SCALE 1:100 DATE JANUARY 2023

DEALT BY STATUS SUBMISSION

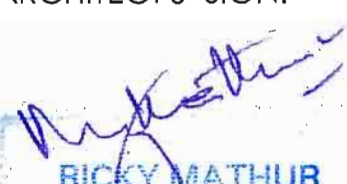ARCHITECT'S SIGN.

RICKY MATHUR
CA-24247

CLIENT'S SIGN.

For Ashiana Housing Limited
Authorised Signatory

SHEET NO. - 28 NORTH -