

कार्यालय अतिरिक्त मुख्य नगर नियोजक
राजस्थान आवासन मण्डल, जयपुर

क्रमांक:- अति.मु.न.नि./रा.आ.म./जयपुर/2023-24/364

दिनांक : 20.11.2023

वंशदीप बिल्डर्स प्राइवेट लिमिटेड,
एस/58, राज आंगन,
एन.आर.आई. कॉलोनी,
सेक्टर-24, प्रताप नगर,
सांगानेर, जयपुर।

विषय:- आवासीय भूखण्ड संख्या-5 (क्षेत्रफल 1713.59 वर्ग मीटर) सेक्टर-16, कोचिंग हब आर्कड, प्रताप नगर, सांगानेर, जयपुर के भवन मानचित्र अनुमोदन बाबत।

महोदय,

1. उक्त स्वीकृति भवन विनियम-2020 के तहत जारी की गयी है।
2. उक्त स्वीकृति भवन विनियम-2020 के बिन्दु संख्या-8.11 के अनुसार जारी दिनांक से 7 (सात) वर्ष के लिये मान्य होगी।
3. इस निर्माण स्वीकृति को स्वामित्व का आधार नहीं माना जायेगा और न ही इसमें किसी के स्वामित्व संबंधी अधिकार ही प्रभावित होंगे एवं स्वामित्व विवादित होने की स्थिति में भूमि पर दिये गये निर्माण स्वीकृति के लिए राजस्थान आवासन मण्डल जिम्मेदार नहीं होगा, क्योंकि निर्माण स्वीकृति केवल मात्र प्रश्नगत भूमि पर क्या निर्माण किया जा सकता है, अथवा अनुज्ञेय है, यही दर्शाता है।
4. भवन निर्माण में निर्धारित मानदण्डों के उल्लंघन होने या निर्माण मानक स्तर के अनुरूप नहीं होने पर निर्माण को रोका जा सकता है। इसे आंशिक या पूर्ण रूप से ध्वस्त कराया जा सकेगा एवं ऐसे समस्त निर्माण की जिम्मेदारी अनुज्ञाधारी की होगी।
5. गलत तथ्यों पर प्राप्त की गई अथवा तथ्यों को छुपाकर प्राप्त की गई स्वीकृति स्वतः निरस्त मानी जायेगी एवं ऐसी निर्माण स्वीकृति प्राप्त करने के लिए आवेदनकर्ता को दोषी माना जायेगा।
6. विद्युत सेवा हेतु नेशनल बिल्डिंग कोड इण्डिया के आबंधों में वर्णित प्रावधानों का पालन आवश्यक होगा।
7. नलकारी एवं जल, मूल निकास सेवायें नेशनल बिल्डिंग कोड ऑफ इण्डिया के उपबंधों के अनुरूप होंगी।
8. अनुमोदनानुसार वर्षा जल संग्रहण यूनिट मौके पर वास्तव में आवेदनकर्ता द्वारा लगाई जावेगी।
9. अनुमोदनानुसार सौर ऊर्जा उपकरण सिस्टम मौके पर वास्तव में आवेदनकर्ता द्वारा लगाया जावेगा।
10. भवन निर्माण में आंतरिक मानदण्ड बाबत में जिन विषयों पर ब्यौरा यहाँ नहीं दिया गया है, उन बाबत मानदण्ड नेशनल बिल्डिंग कोड ऑफ इण्डिया के उपबंधों के अनुसार होंगे।
11. भवन का संरचनात्मक अभिकल्पन एवं सुरक्षा नेशनल बिल्डिंग कोड ऑफ इण्डिया के उपबंधों के अनुसार होगा।
12. आवेदनकर्ता की स्वयं की यह जिम्मेदारी होगी कि उनके द्वारा भवन विनियमों के समस्त संबंधित प्रावधानों की पालना भवन निर्माण के दौरान की जा रही है। अन्यथा यह स्वीकृति स्वतः ही निरस्त मानी जावेगी।
13. अनुमोदित मानचित्रों में जिस भाग को पार्किंग हेतु अनुमोदित किया है वह भाग आवेदनकर्ता द्वारा किसी को बेचा नहीं जावेगा एवं केवल पार्किंग हेतु उपयोग में लिया जावेगा। इस का पार्किंग के अलावा अन्य उपयोग पाये जाने पर राजस्थान आवासन मण्डल बिना किसी सूचना के तोड़ने का हकदार होगा एवं तोड़ने का हर्जा खर्चा जिस व्यक्ति ने पार्किंग के अलावा उपयोग किया है से वसूला जा सकता है।

“उपरोक्त शर्तों का उल्लंघन करने पर राजस्थान आवासन मण्डल हर्जा खर्चा वसूलने एवं अन्य दण्डात्मक कार्यवाही जैसे आर्थिक दण्ड कर सकता है जिसे आवेदनकर्ता देने के लिए बाध्य रहेंगे।”

14. अनुमोदित मानचित्रों की प्रति निर्माण स्थल पर बोर्ड पर आवेदनकर्ता द्वारा चरपा कर प्रदर्शित की जावेगी, साथ ही वास्तुविद्, भवन मालिक व ठेकेदार का नाम भी अंकित किया जावेगा। यदि भवन निर्माण के समय मौके पर उक्त वर्णित डिस्ले नहीं है तो संबंधित उप आवासन आयुक्त द्वारा निर्माण कार्य तुरन्त प्रभाव से रूकवा दिया जावेगा।
15. प्रत्येक 50 वर्ग मीटर क्षेत्रफल के लिए कम से कम एक वृक्ष के अनुपात में बड़े वृक्ष जो 6 मीटर या इससे अधिक ऊंचाई ग्रहण कर सकते हो, लगाने होंगे।
16. भवन विनियम-2020 के विनियम संख्या 16 एवं 17 के अनुसार भवन का निर्माण पूर्ण होने पर भवन निर्माणकर्ता को पूर्णता प्रमाण पत्र एवं अधिवास प्रमाण पत्र प्राप्त करना आवश्यक होगा।
17. निदेशालय, स्थानीय निकाय के पत्र क्रमांक एफ 55 (22) पीए/एस.ई./डीएलबी/05/आपदा/18726 दिनांक 18.05.05 द्वारा जारी दिशा-निर्देशों के अनुसार भूकम्परोधी भवन बनाने की जिम्मेदारी आवेदनकर्ता की होगी।
18. भवन के पूर्णता प्रमाण पत्र चाहने पर संस्था द्वारा लेबर डिपार्टमेंट में लेबर सैस स्वयं के स्तर पर जमा करवाकर संबंधित प्रमाण पत्र प्रस्तुत करने पर भवन का पूर्णता प्रमाण पत्र जारी किया जा सकेगा।
19. पूर्णता प्रमाण पत्र जारी करने के समय स्थायी अग्निशमन प्रमाण पत्र प्रस्तुत करने पर पूर्णता प्रमाण पत्र जारी किया जा सकेगा।
20. आवेदनकर्ता द्वारा कचरापात्र की व्यवस्था सुनिश्चित करनी होगी।
21. आवेदनकर्ता द्वारा तडित चालक की व्यवस्था सुनिश्चित करनी होगी।
22. आवेदनकर्ता द्वारा कुल पार्किंग का 10 प्रतिशत EV Charging Points का प्रावधान किया जाना होगा।
23. आवेदनकर्ता द्वारा विजिटर पार्किंग का अंकन वास्तविक रूप में किया जाना होगा।
24. आवेदनकर्ता द्वारा अग्निशमन संबंधी सुरक्षात्मक प्रावधान एवं अन्य मापदण्ड राज्य सरकार द्वारा इस संबंध में जारी अधिसूचना क्रमांक F.17(5)UDH/RVLES/2020 दिनांक 09.01.2020 तथा समय-समय पर जारी आदेशों की पालना सुनिश्चित की जानी होगी।
25. आवेदनकर्ता द्वारा बहुमंजिले भवन में 24.00 मीटर ऊंचाई पर बालकनी को शरण क्षेत्र प्रस्तावित किया गया है। अतः इस क्षेत्र को कवर्ड नहीं किया जायेगा।

संलग्न :- अनुमोदित भवन मानचित्र का एक सैट।

भवदीय




(अनिल माथुर)

अतिरिक्त मुख्य नगर नियोजक
राजस्थान आवासन मण्डल,
जयपुर।

प्रतिलिपि:- निम्न को सूचनार्थ एवं आवश्यक कार्यवाही हेतु प्रेषित है।

1. निजी सचिव, आवासन आयुक्त, राजस्थान आवासन मण्डल, जयपुर।
2. उप आवासन आयुक्त, वृत्त-प्रथम, राजस्थान आवासन मण्डल, जयपुर।
3. आवासीय अभियन्ता, खण्ड-कोथिंग हब, राजस्थान आवासन मण्डल, जयपुर को अनुमोदित भवन मानचित्रों का एक सैट संलग्न कर प्रेषित किया जा रहा है। कृपया सुनिश्चित करें कि भवन निर्माण अनुमोदित मानचित्रों के अनुसार हों।
4. रक्षित पत्रावली।


/
अतिरिक्त मुख्य नगर नियोजक

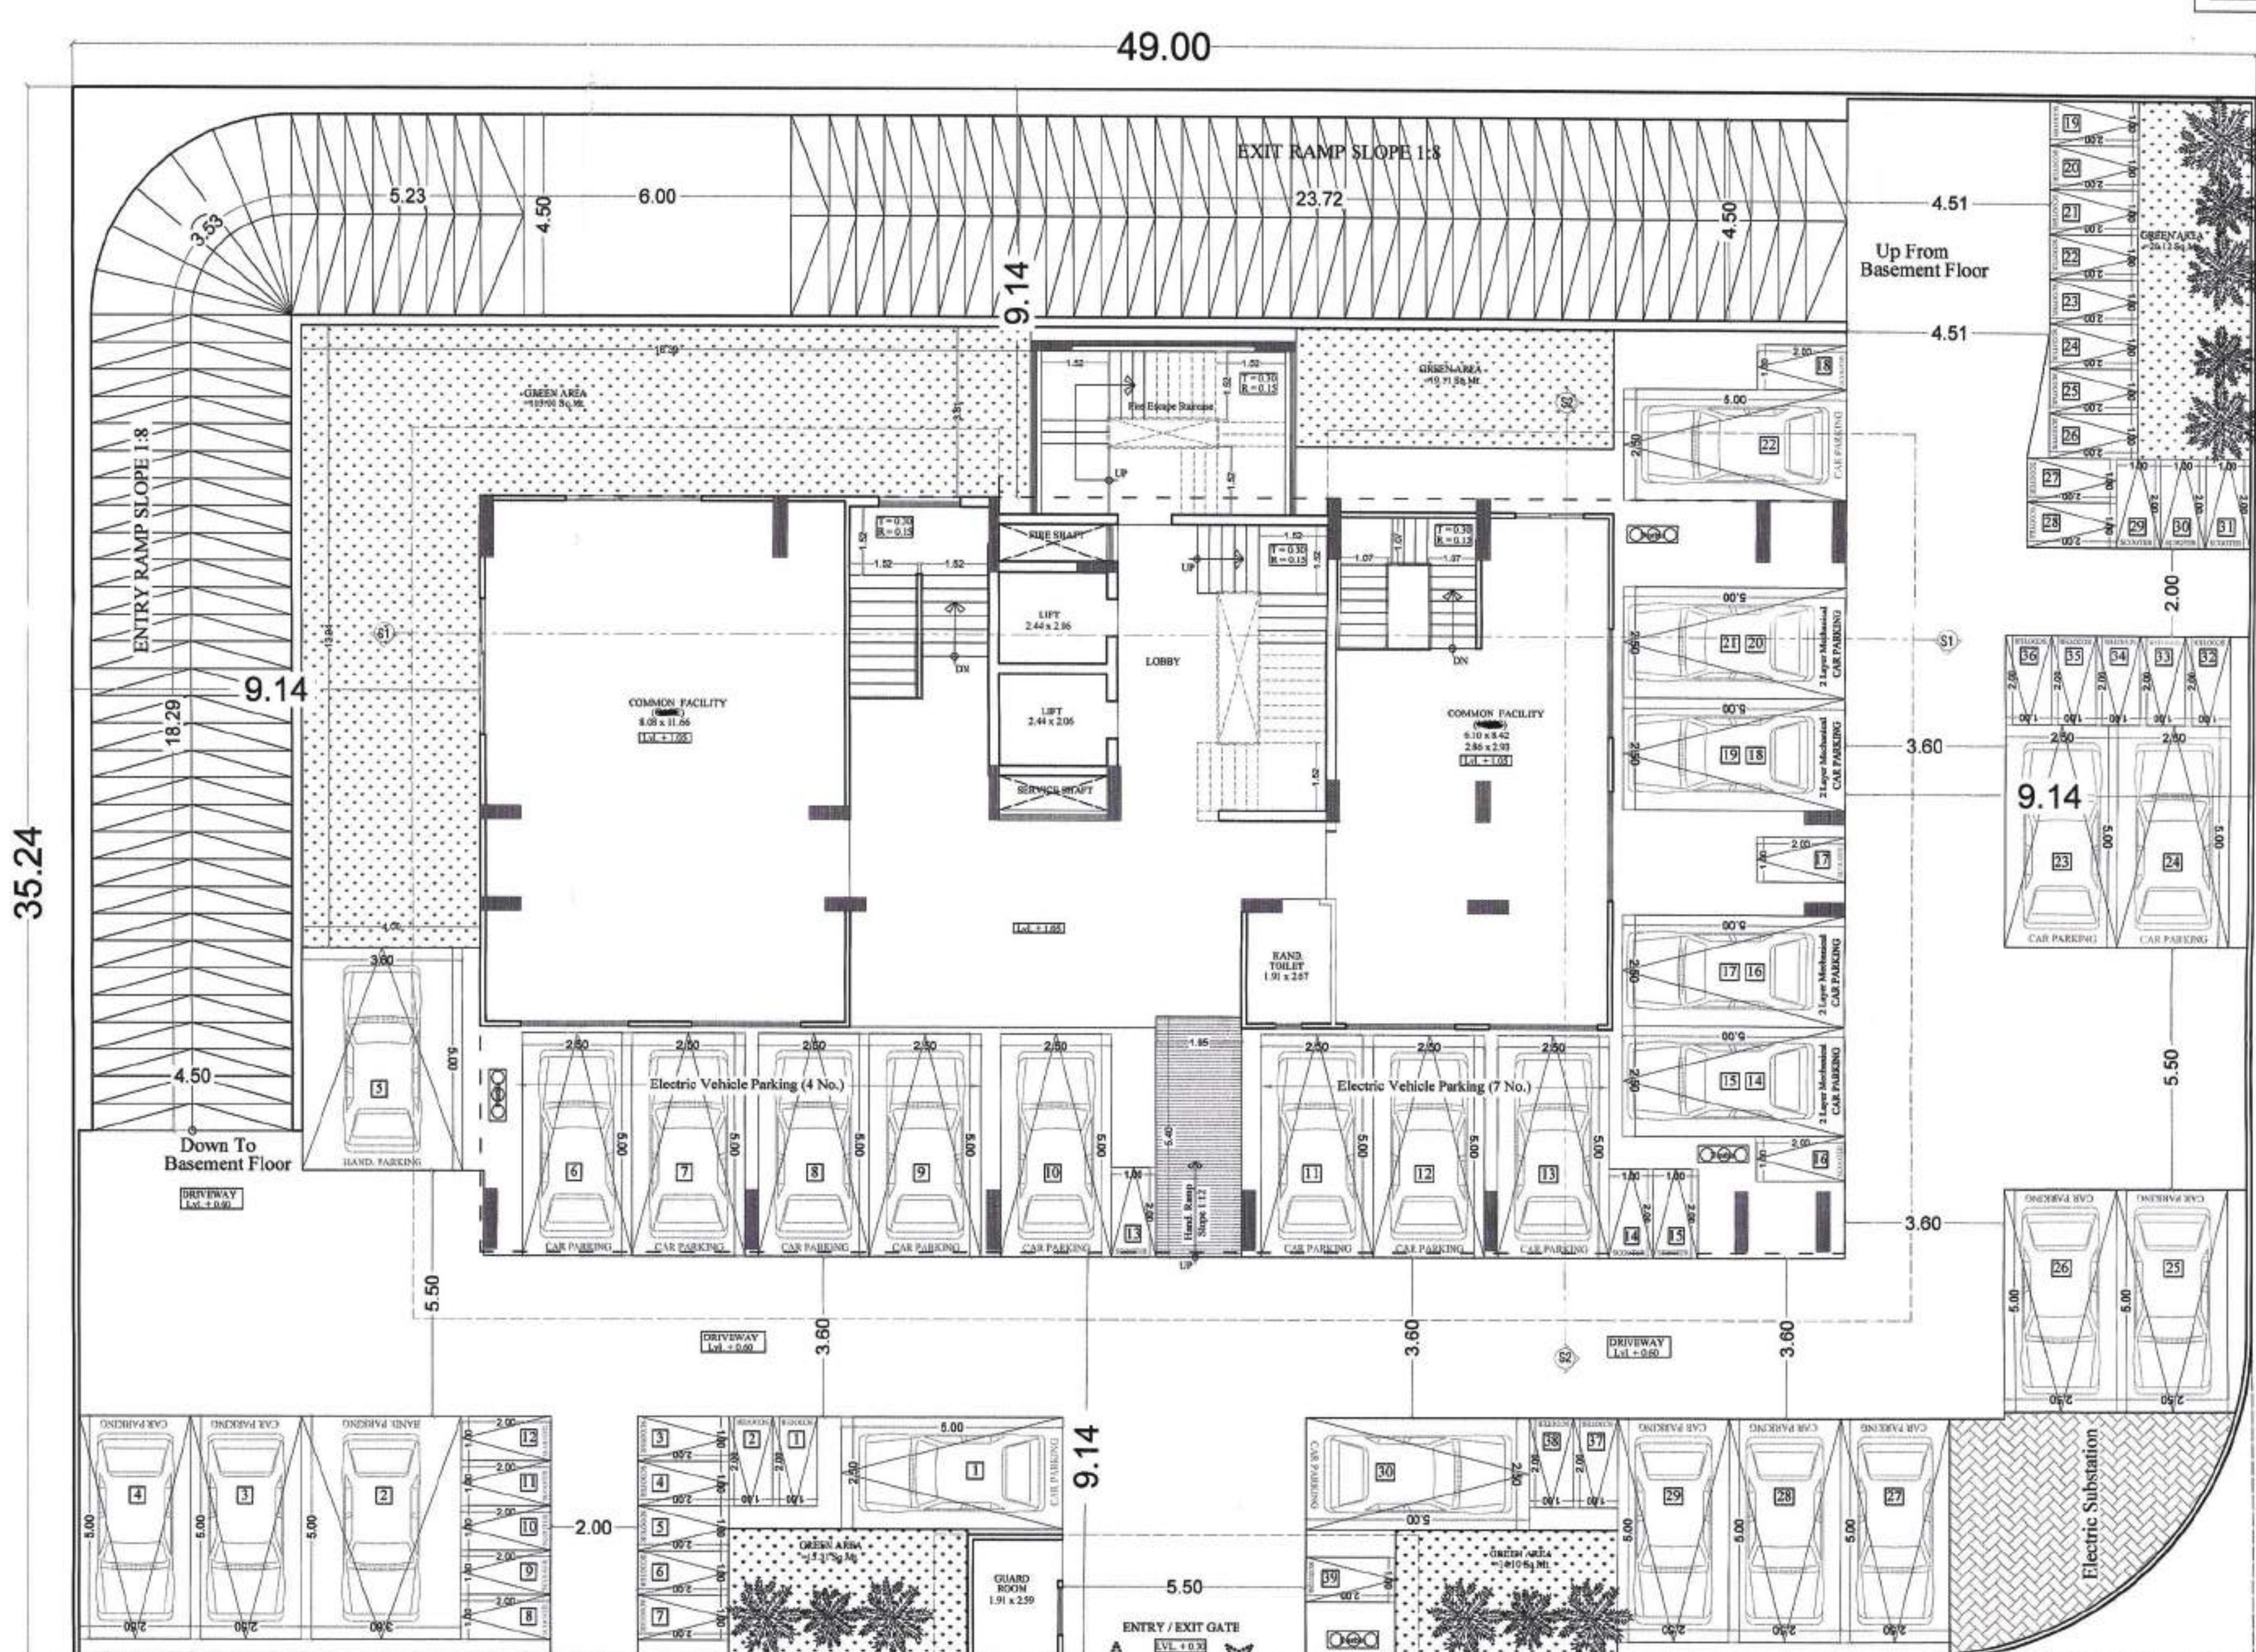


----- ROAD 60'-0" WIDE -----

AREA CALCULATION (AREA IN SQ. MTR.)									
S.NO.	FLOOR	GROSS BUILTUP	FIRE STAIR	ARCHITECTURAL ELEMENT	LIFT WELL	PARKING	SERVICE SHAFT	B.A.R.	FACILITIES
1	Basement Floor, UG Water Tank	949.33	-	-	10.03	880.75	-	58.55	-
2	Stilt Floor	682.95	23.10	-	10.03	471.72	-	178.10	178.10
	Guard Room	6.35	-	-	-	-	-	-	-
	Electric Substation	46.56	-	-	-	-	-	-	-
3	1st Floor	674.14	23.10	5.07	10.03	-	3.90	632.04	-
4	2nd Floor	674.14	23.10	5.07	10.03	-	3.90	632.04	-
5	3rd Floor	674.14	23.10	5.07	10.03	-	3.90	632.04	-
6	4th Floor	674.14	23.10	5.07	10.03	-	3.90	632.04	-
7	5th Floor	674.14	23.10	5.07	10.03	-	3.90	632.04	-
8	6th Floor	674.14	23.10	5.07	10.03	-	3.90	632.04	-
9	7th Floor	674.14	23.10	5.07	10.03	-	3.90	632.04	-
10	8th Floor	674.14	23.10	5.07	10.03	-	3.90	632.04	-
11	9th Floor	674.14	23.10	5.07	10.03	-	3.90	632.04	-
12	10th Floor	674.14	23.10	5.07	10.03	-	3.90	632.04	-
13	11th Floor	674.14	23.10	5.07	10.03	-	3.90	632.04	-
14	12th Floor	674.14	23.10	5.07	10.03	-	3.90	632.04	-
15	Mummy/ Stair Architectural Element	192.27	-	-	-	-	-	-	-
16	TOTAL	9967.14	-	-	-	-	-	7821.13	-


SHRI KRISHNA
ARCHITECT
CA/98/25451

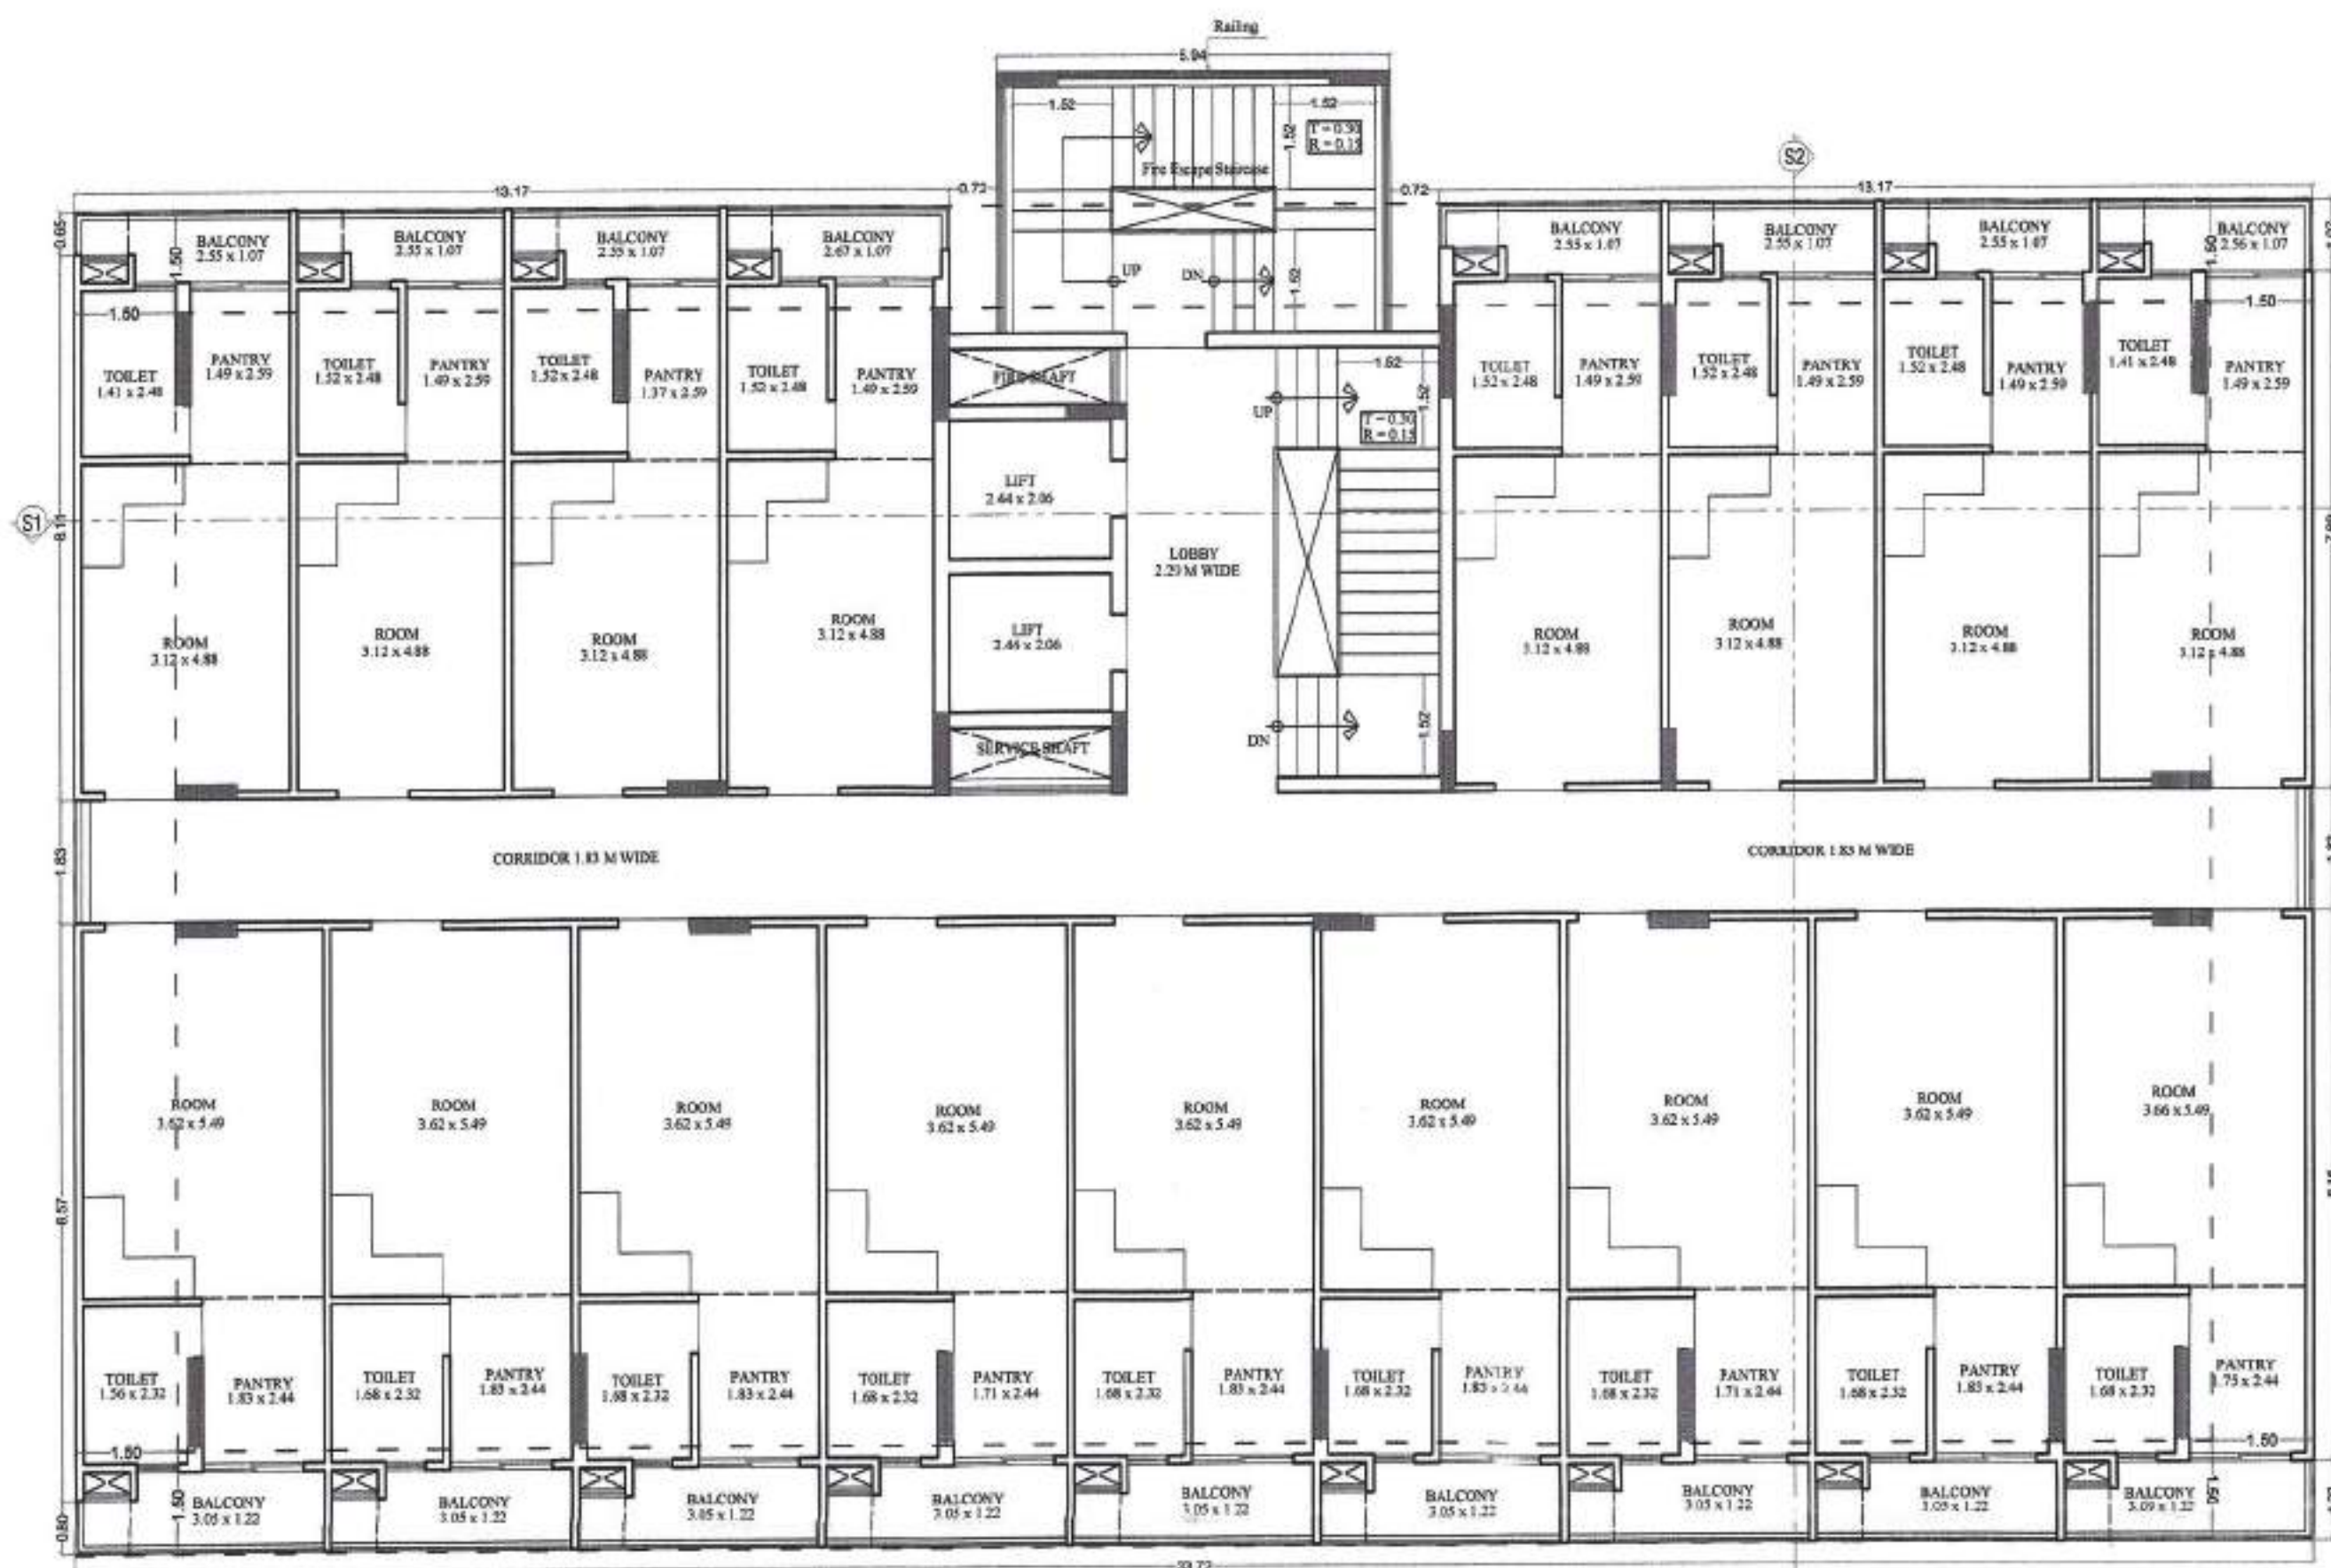

1st FLOOR PLAN

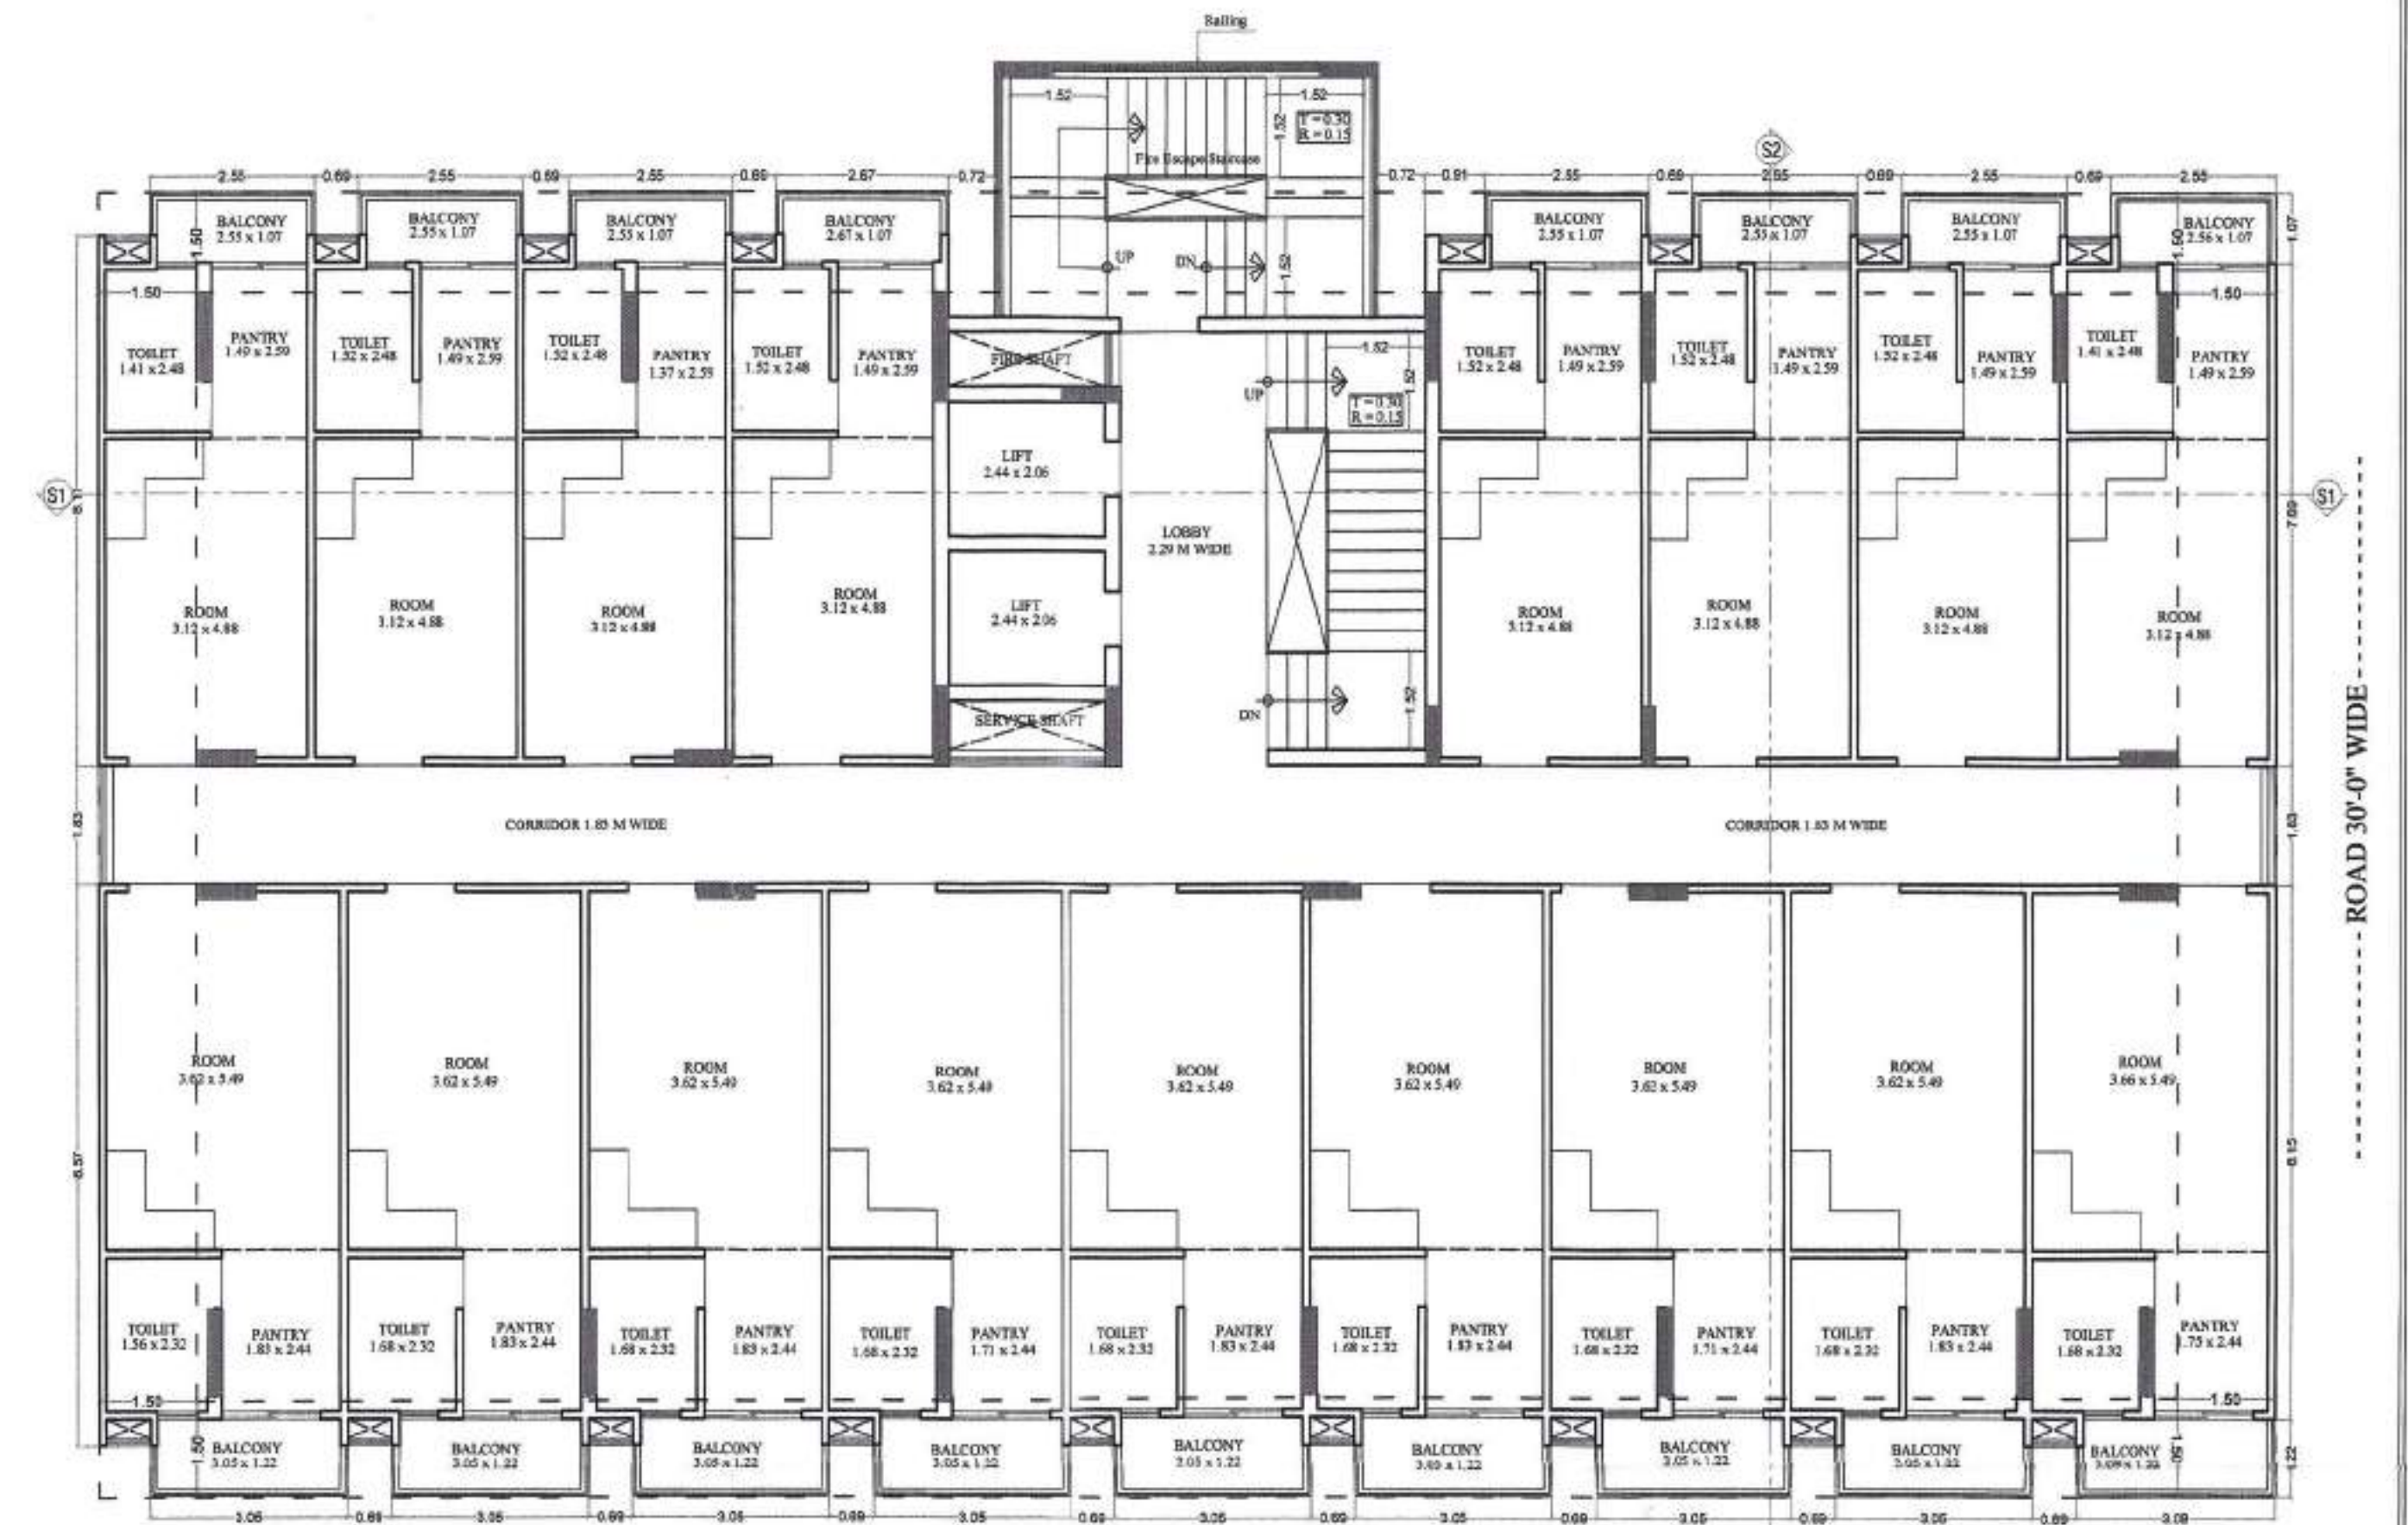

TYPICAL PLAN (2nd to 12th Floor)

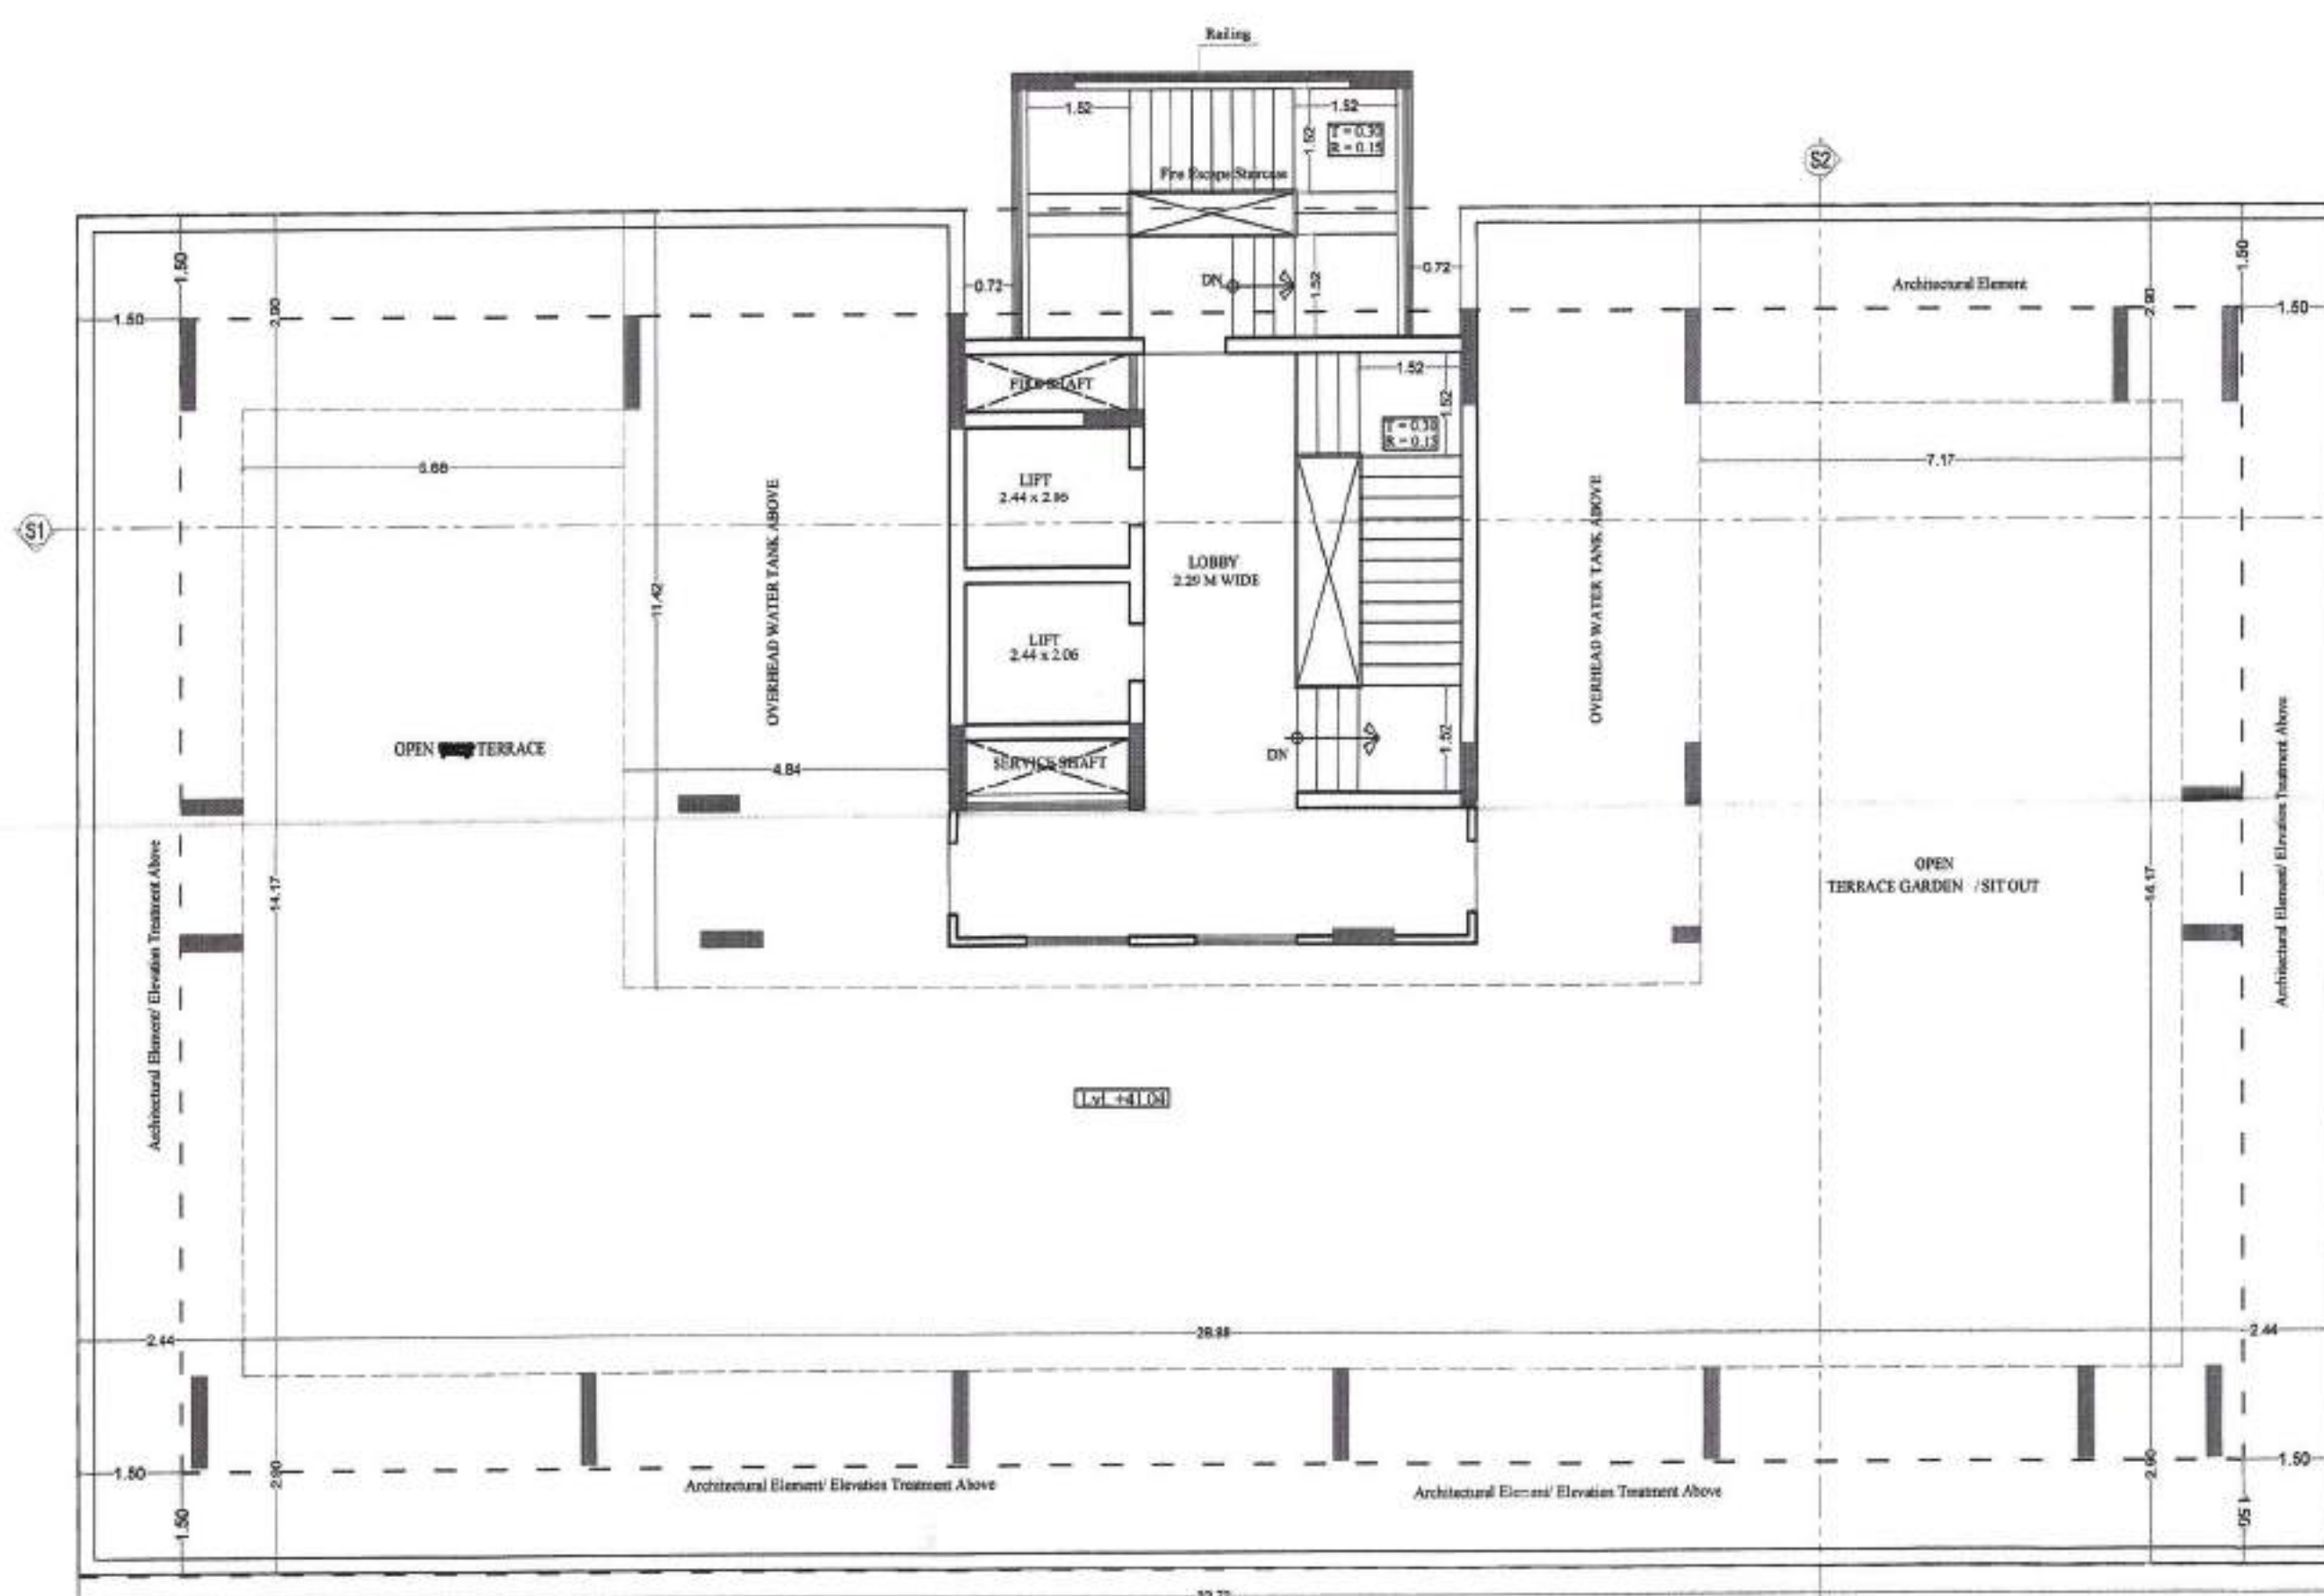

TERRACE PLAN

पार्किंग क्षेत्र का उपयोग केवल पार्किंग हेतु किया जायेगा।

“करी किये गये अनुमोदित मानचित्र में दर्शाये गये भवन निर्माण की संरचना (STRUCTURE) का दायित्व प्राचीन की होगा।”

Adequate Light and Ventilation to be Provided as per N. B. C. MUMTY PLAN Norms.

इस मानचित्र का अनुमोदन किसी भी भाग में संशोधन, परिवर्तन के प्रति स्पष्टता के अभाव में प्रमाणित नहीं किया जायेगा और यदि इससे किसी भी व्यक्ति को नुकसान हो तो वह स्वयं की ज़िम्मेदारी होगी।

शारीरिक रूप से विकलांग व्यक्तियों के लिए विशेष सुविधा का प्रावधान नियमानुसार किया जाये।

सौर ऊर्जा से पानी गरम करने का नियमानुसार प्रावधान किया जाये।


विद्युत सेवा, नलकरी एवं जल, पत निवारण सेवाएं नेशनल मिनिमम कोड ऑफ प्रैक्टिस का अनुसरण होगी।

THESE PLANS ARE VALID ONLY UPTO SEVEN YEARS FROM DATE OF ISSUE.

Rain Water Harvesting Units Shall be Provided as per Rules

अनुमोदित

प्रस्तावित भवन 15 मीटर से अधिक ऊँचाई होने के कारण 15 मीटर से अधिक मंजूर पर निर्माण होकर करने से पूर्व मुख्य अतिरिक्त शक्ति और अन्य आवश्यकताओं के अनुसार आवश्यक मापदंडों का पालन किया जायेगा। (NOC) प्रस्ताव की शर्तों के अंतर्गत 15 मीटर से अधिक ऊँचाई पर निर्माण होना आवश्यक है।

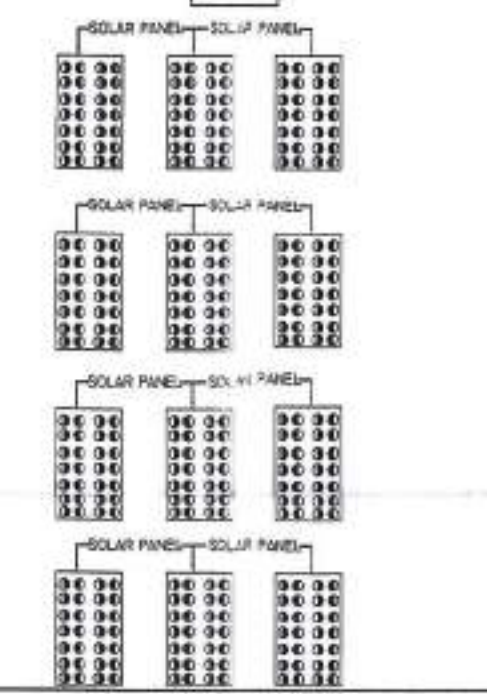


रजि. 17-11-23
उप नगर नियोजक
राजस्थान आवासन मण्डल
जयपुर

अतिरिक्त नगर नियोजक
राजस्थान आवासन मण्डल
जयपुर

अतिरिक्त नगर नियोजक
राजस्थान आवासन मण्डल
जयपुर

यह मानचित्र पत्र सं. 36Y
दि. 20.11.23 को जारी किया गया है।



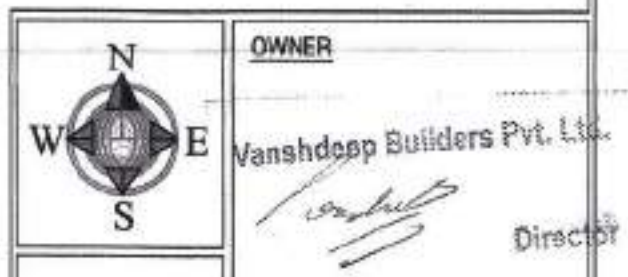


SCALE = 1:100

PROJECT :-
PROPOSED STUDIO APARTMENT AT
PLOT NO. 5, COACHING HUB,
PRATAP NAGAR, JAIPUR

ARCHITECT :-
SPACE GRID
C-49, VIDYA APARTMENT, PARAS MARG,
BAPU NAGAR, NEAR JANTA STORE CIRCLE,
JAIPUR-302015
PH-09314918766, 0141-4005506 (O)
Email:-info.spacegrid@gmail.com

SHRI KRAISHAN
ARCHITECT
CA/99/25451

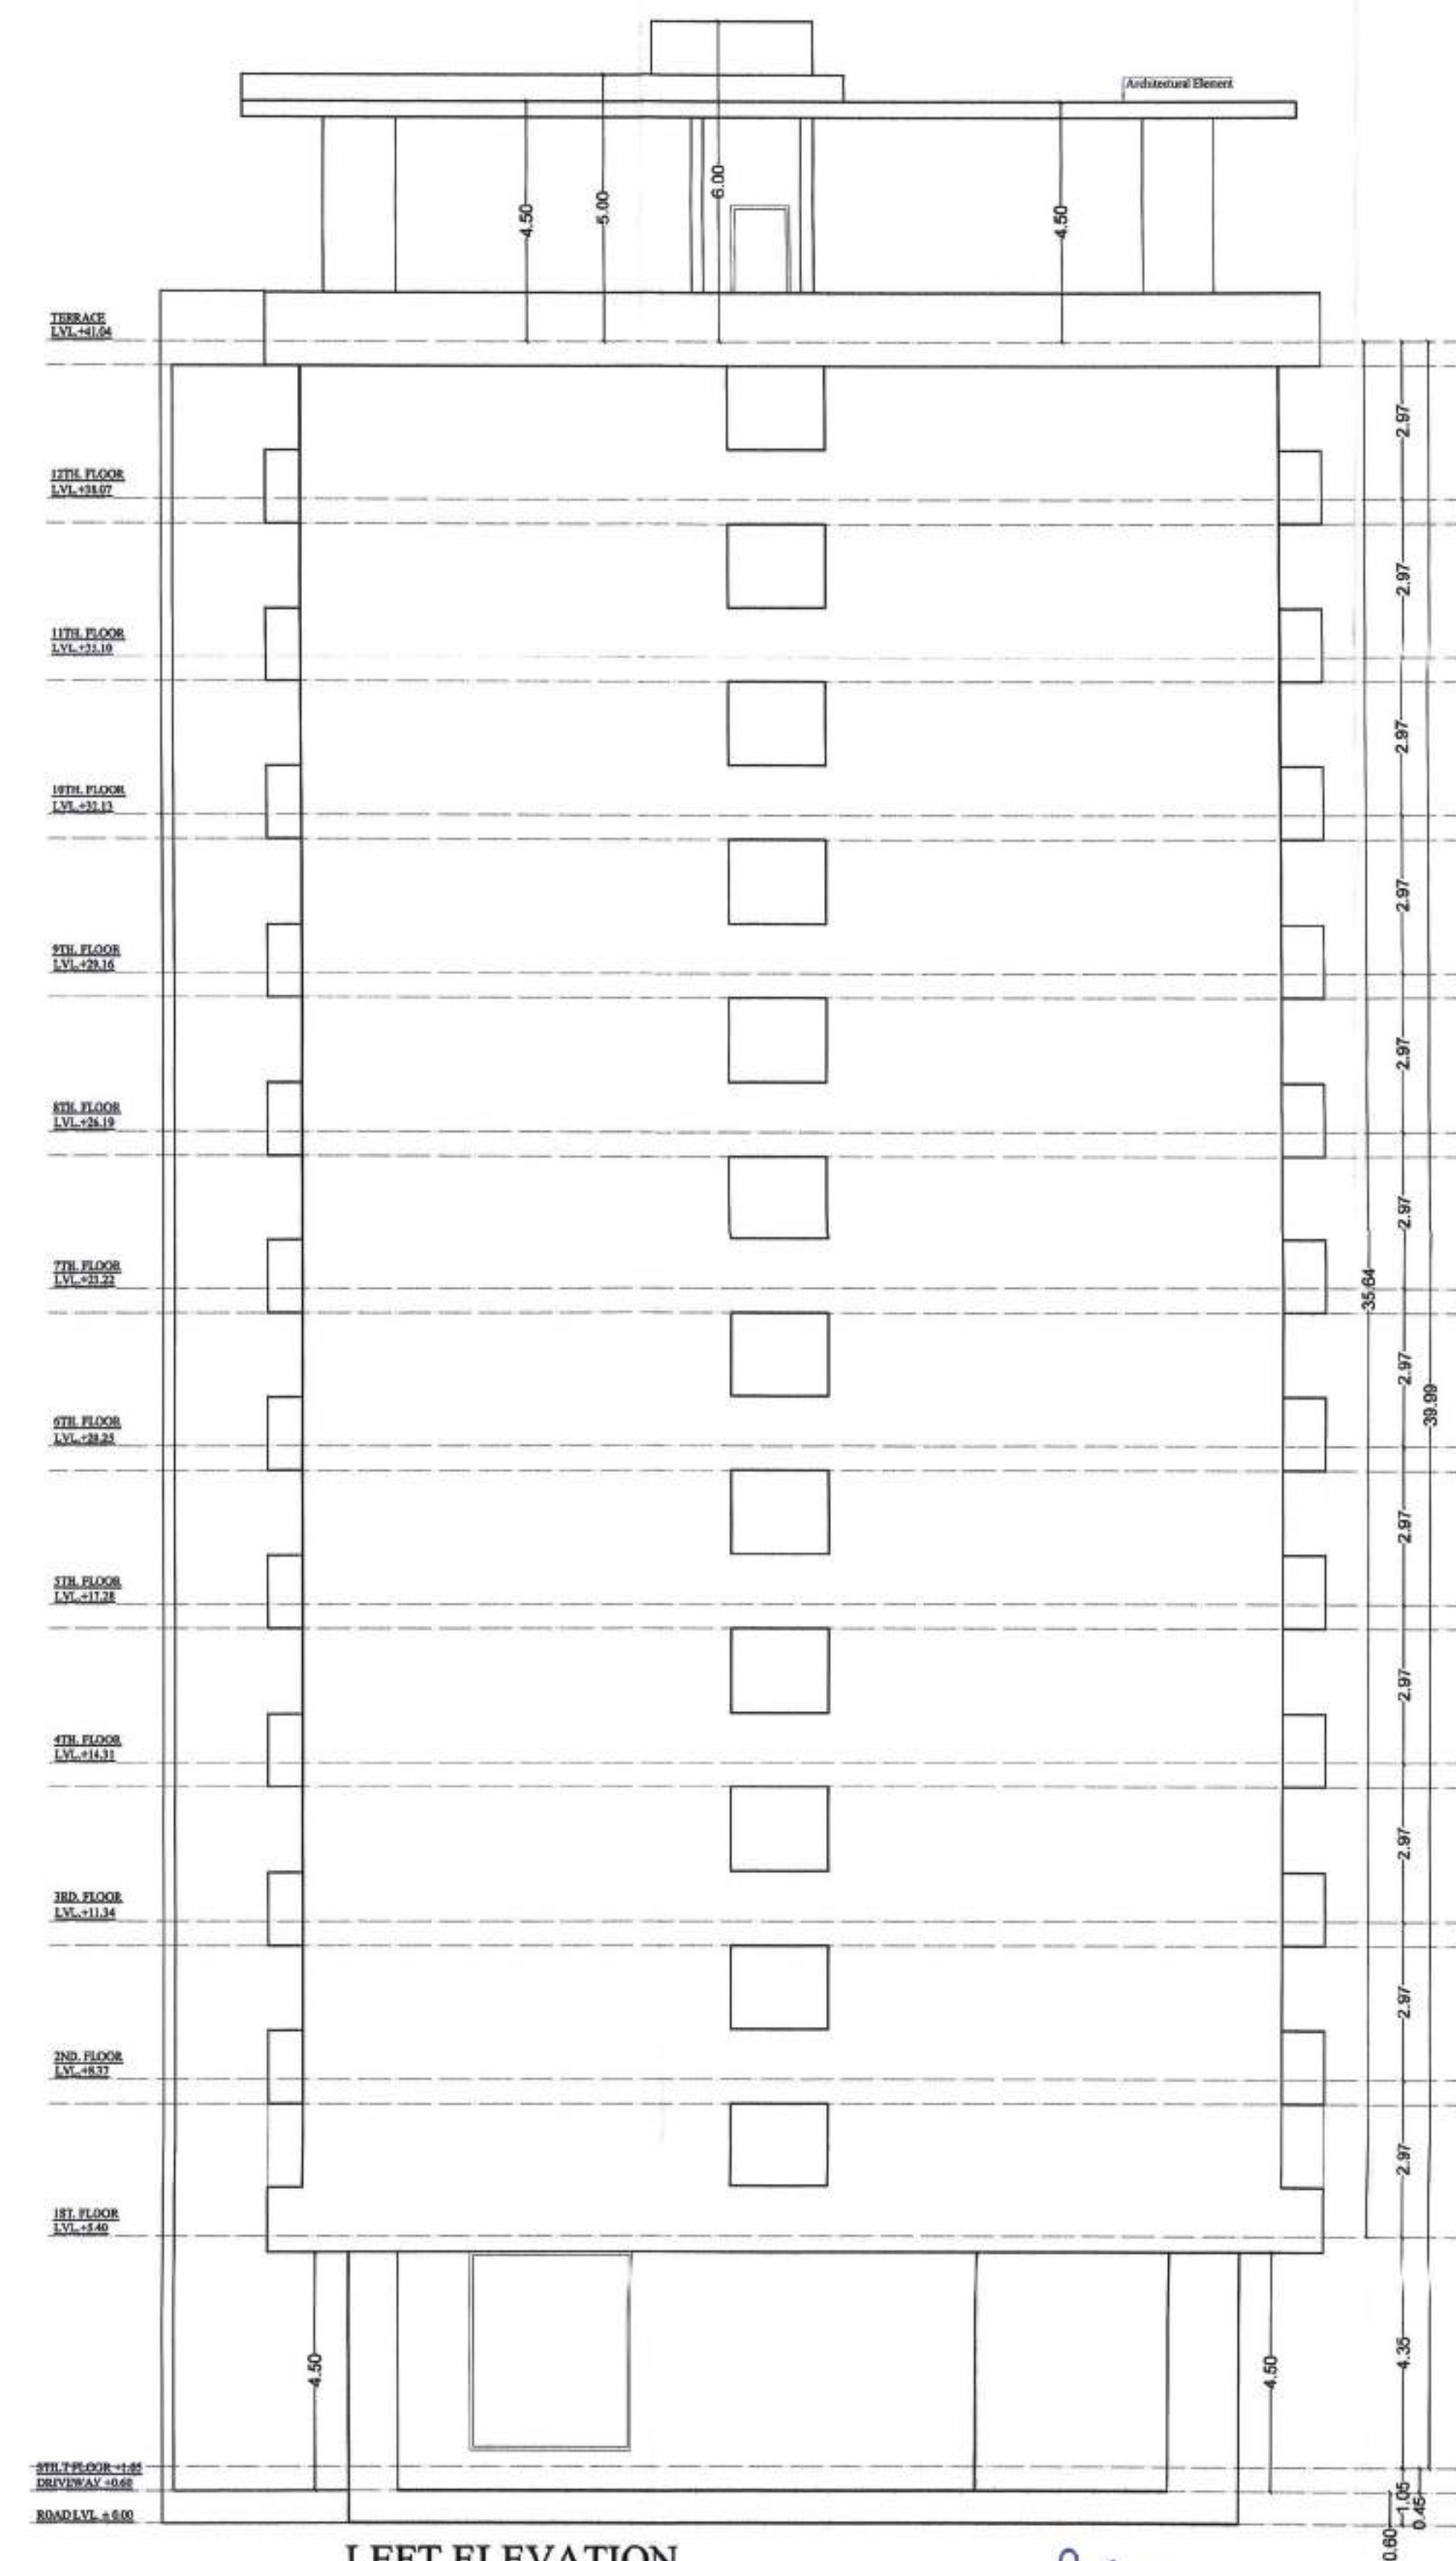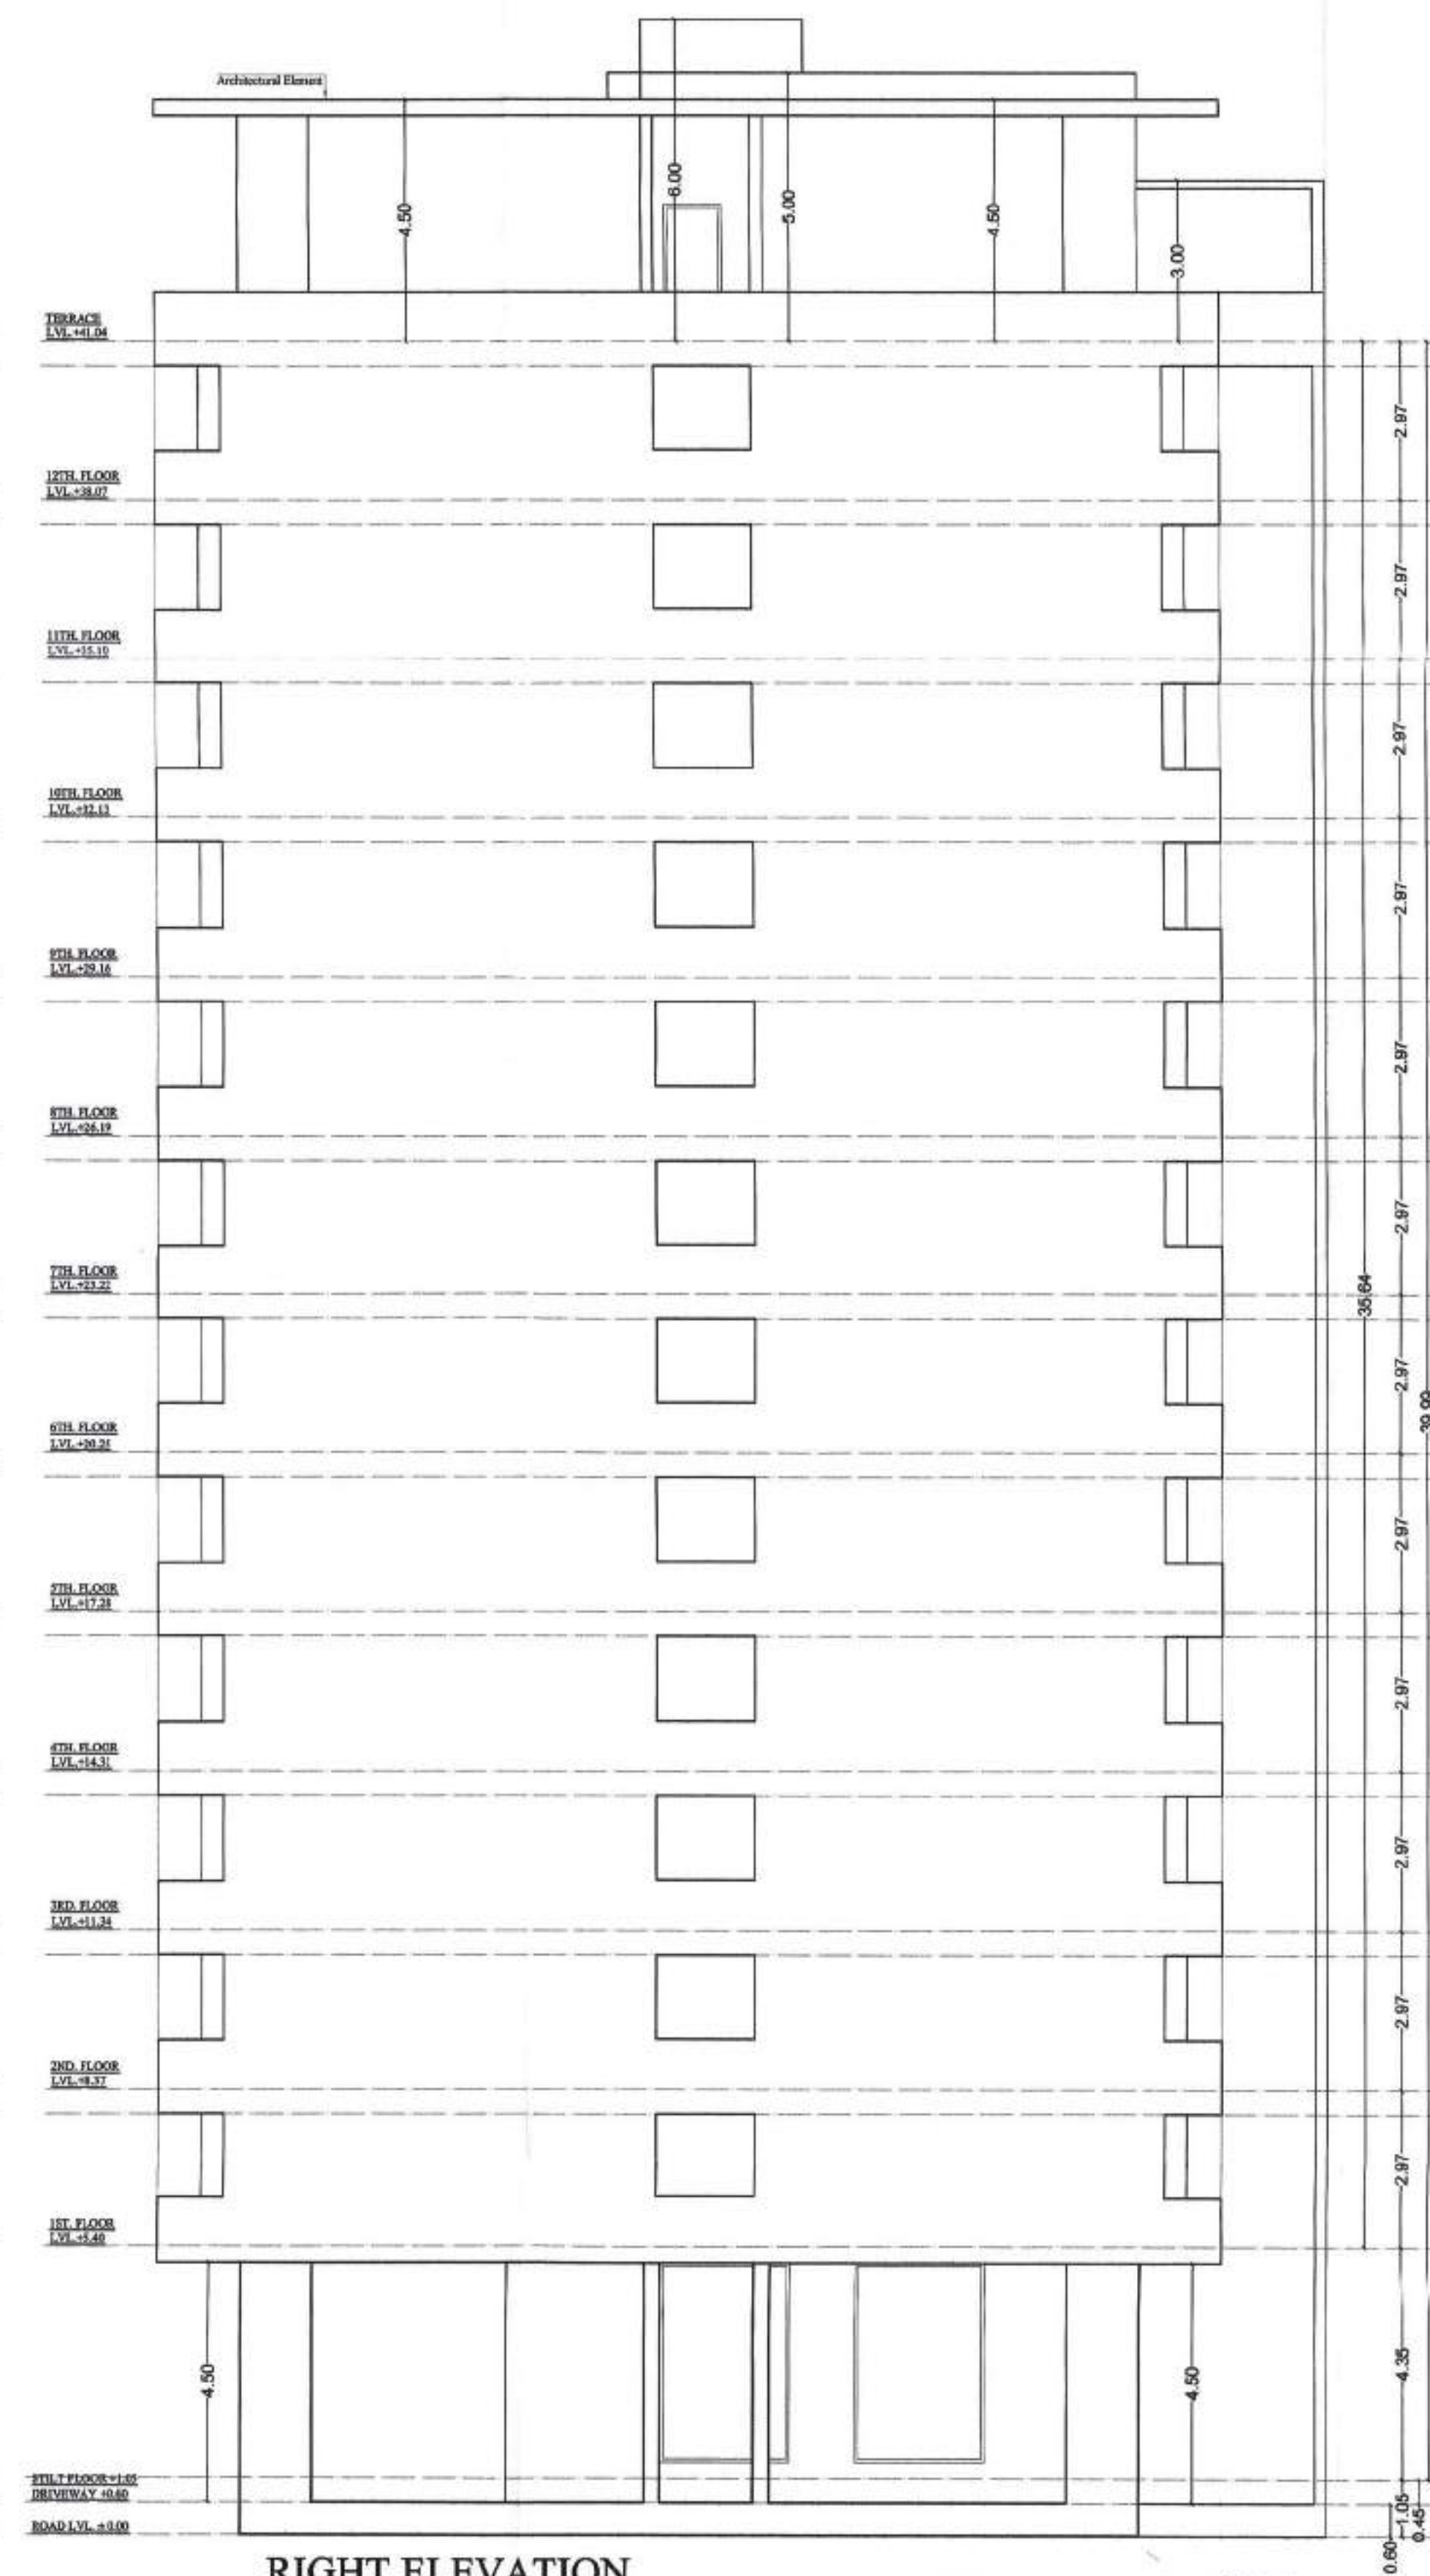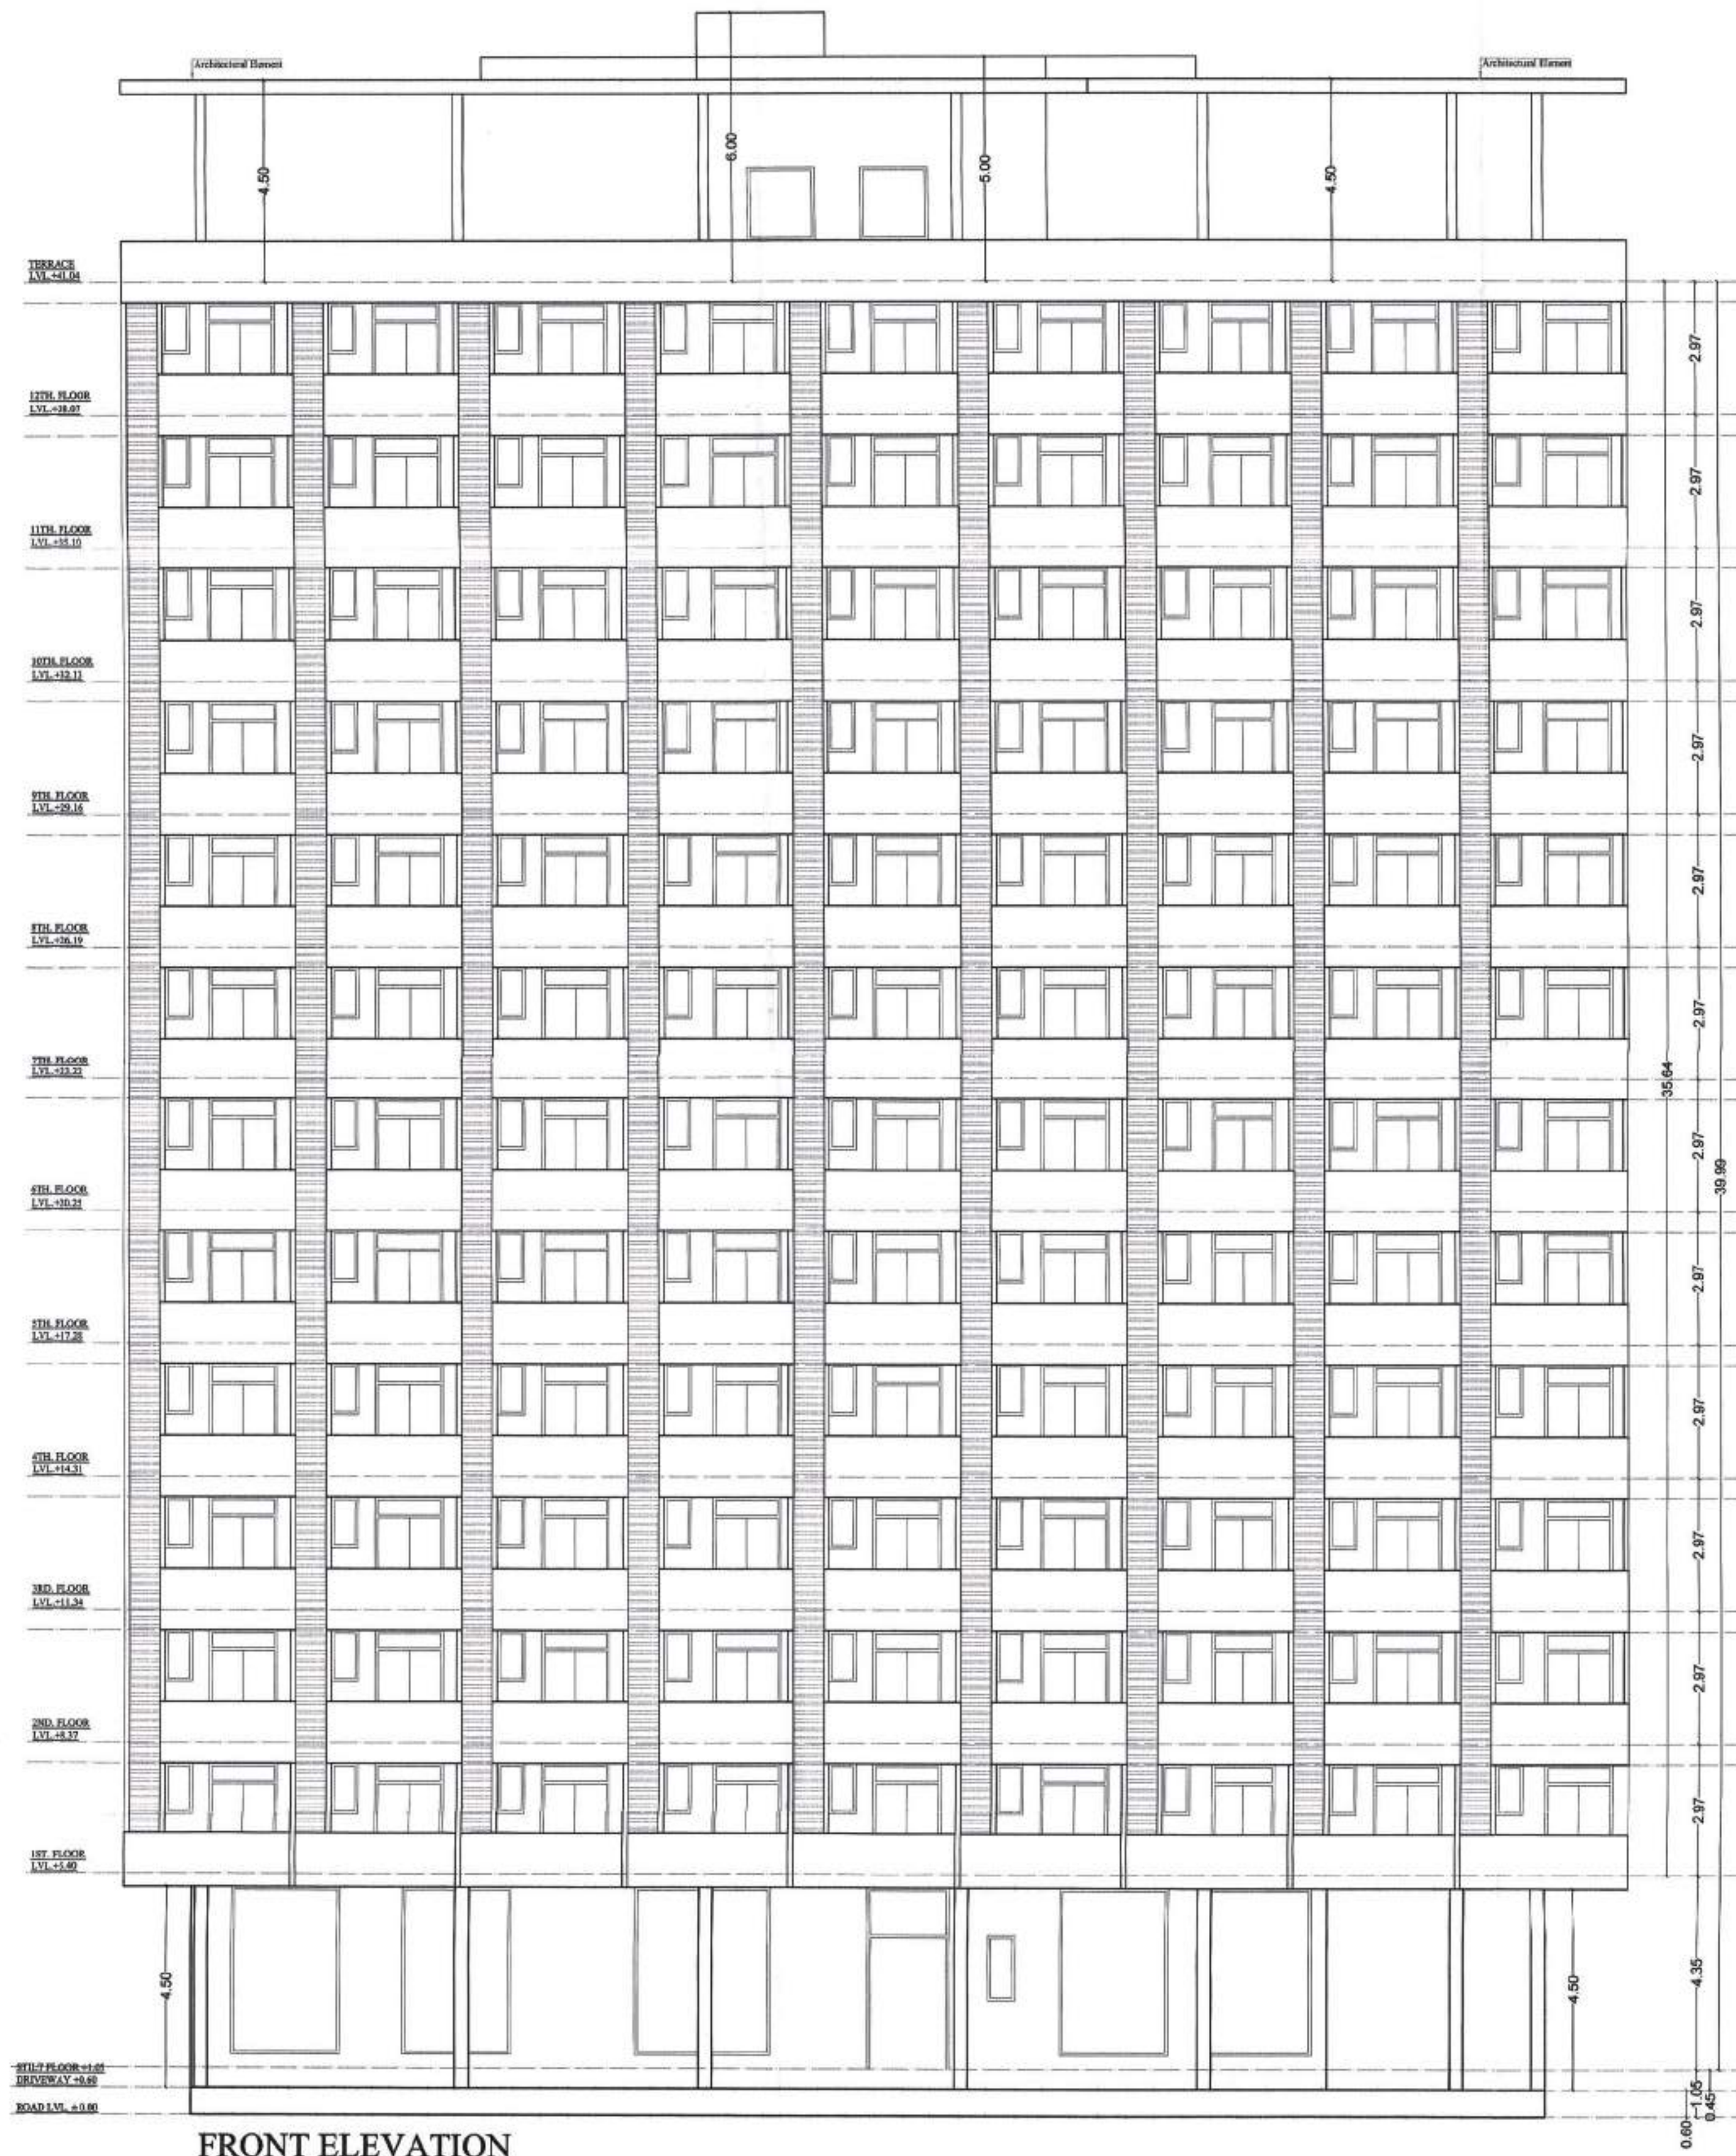

पार्किंग क्षेत्र का उपयोग केवल पार्किंग हेतु किया जाएगा।

"जैसे किने ऐसे अनुमोदित मानचित्र में दर्शाये गये हैं कि जिन की संरचना (STRUCTURE) का पारित प्रमाण का ही होगा।"

Adequate Light and Ventilation to be Provided as per N. B. C. Norms.

इन मानचित्रों का उपयोग किसी भी भी संरचना में भू-स्थल के अति संरचना का प्रमाण पत्र-पत्रों मांग वास्तव में नहीं इससे किसी भी वास्तविक संरचना को उत्पन्न करने के लिए नहीं है।

खरीदक को इन से विकसित व्यक्तियों के लिए विशेष सुविधा का प्रमाण नियमानुसार दिया जाये।

सौर ऊर्जा से पानी गरम करने का प्रणालीनुसार प्रदान किया जाये।

विशेष सेवा, बलवर्ती एवं जल, गल पिकास सेवाएं मेहानों विविध सेवाओं और इन्फ्रा के उपयोग के अनुसार होंगी।

THESE PLANS ARE VALID ONLY UPTO SEVEN YEARS FROM DATE OF ISSUE.

Rain Water Harvesting Units Shall be Provided as per Rules

अनुमोदित

प्रस्तुत किए गए 15 मीटर से अधिक ऊँचाई होने के कारण 15 मीटर से अधिक मीटरों पर निर्माण होने वाले से पूर्व पूर्ण अतिरिक्त प्रमाण पत्र (RCC) सेवा और एक वास्तविक प्रमाण पत्र (RCC) में संश्लेषित प्रमाण पत्र (RCC) प्रमाण पत्र की पानी की जांच होगी। अन्यथा यह स्वीकृति 15 मीटर ऊँचाई तक ही मान्य होगी।

उप नगर निरीक्षण
राजस्थान आवासन मण्डल
जयपुर

श्री 440
श्री 440
श्री 440

अतिरिक्त मुख्य नगर निरीक्षण
राजस्थान आवासन मण्डल
जयपुर

श्री 440
श्री 440
श्री 440

OWNER	
Vangshdeep Builders Pvt. Ltd.	
Director	
SCALE = 1:100	
PROJECT :- PROPOSED STUDIO APARTMENT AT PLOT NO. 5, COACHING HUB, PRATAP NAGAR, JAIPUR	
ARCHITECT :- SPACE GRID	
C-49, VIDYA APARTMENT, PARAS MARG, BAPU NAGAR, NEAR JANTA STORE CIRCLE, JAIPUR-302015 PH-09314918766, 0141-4005506 (O) Email- info.spacegrid@gmail.com	

SHRI KRISHNA
ARCHITECT
C-49/25451

जहाँ से का उच्छेद केव
पार्किंग से काया जायेगा।

"करी किये गये अनुकूलित मानचित्र
में दर्शाये गये मूल निर्माण की संरचना
(STRUCTURE) का पश्चिम प्रवेश
का ही होगा।"

Adequate Light and Ventilation
to be Provided as per N. B. C.
Norms.

इस मानचित्र का उपयोग किसी भी गति
अवस्था में/प्रकार के प्रति व्यक्ति या
समूह को नहीं करना चाहिए और यदि
इसके बिना का उपयोग सम्पन्धी अधिकारी
की प्रतिक्रिया होगी।

शारीरिक रूप से विकलांग व्यक्तियों के
लिए विशेष सुविधा का प्रावधान
निम्नानुसार किया जाये।

सौर ऊर्जा से पानी गरम करने का
निम्नानुसार प्रावधान किया जाये।

विद्युत सेवा, भागवती एवं जल, गैस विद्युत
सेवाएं नियमित तालिफत और और इन्फ्रस्ट्र
के उपस्था के अनुसार होगी।

THESE PLANS ARE VALID
ONLY UP TO SEVEN YEARS
FROM DATE OF ISSUE.

Rain Water Harvesting Units
Shall be Provided as per Rule#

अनुमोदित

इच्छित कम 15 मीटर से अधिक ऊँचाई होने
के कारण 15 मीटर से अधिक मीलों पर
निर्माण शुरू करने से पूर्व ठीक सीमा तक
अधिकतम ऊँचाई तक गैर गैर गैर गैर गैर
का (NOC) सेवा सेवा सेवा सेवा सेवा
का (NOC) सेवा सेवा सेवा सेवा सेवा
की कार्य अधिकतम सेवा सेवा सेवा सेवा
15 मीटर ऊँचाई से सेवा सेवा सेवा सेवा

Ran
17-11-23

उप नगर निगम
राजस्थान आवासन मंत्रालय
जयपुर

44/49
वरिष्ठ नगर निगम
राजस्थान आवासन मंत्रालय
जयपुर

30/08/23
अतिरिक्त मुख्य गैर निगम
राजस्थान आवासन मंत्रालय
जयपुर


OWNER	Vanshdeep Builders Pvt. Ltd.
Director	
SCALE = 1:100	
PROJECT :-	PROPOSED STUDIO APARTMENT AT PLOT NO. 5, COACHING HUB, PRATAP NAGAR, JAIPUR
ARCHITECT :-	SPACE GRID G-46, VIDYA APARTMENT PHASE MAR, BAPU NAGAR NEAR JANTA STORE CIRCLE, JAIPUR-302015 PH-09314918766, 0141-4005506 (O) Email- info.spacegrid@gmail.com

SHANKRISHAN
ARCHITECT
CA/912543


का मानचित्र का 36.4
दि 26-11-23 के द्वारा जारी किया गया।



REAR ELEVATION

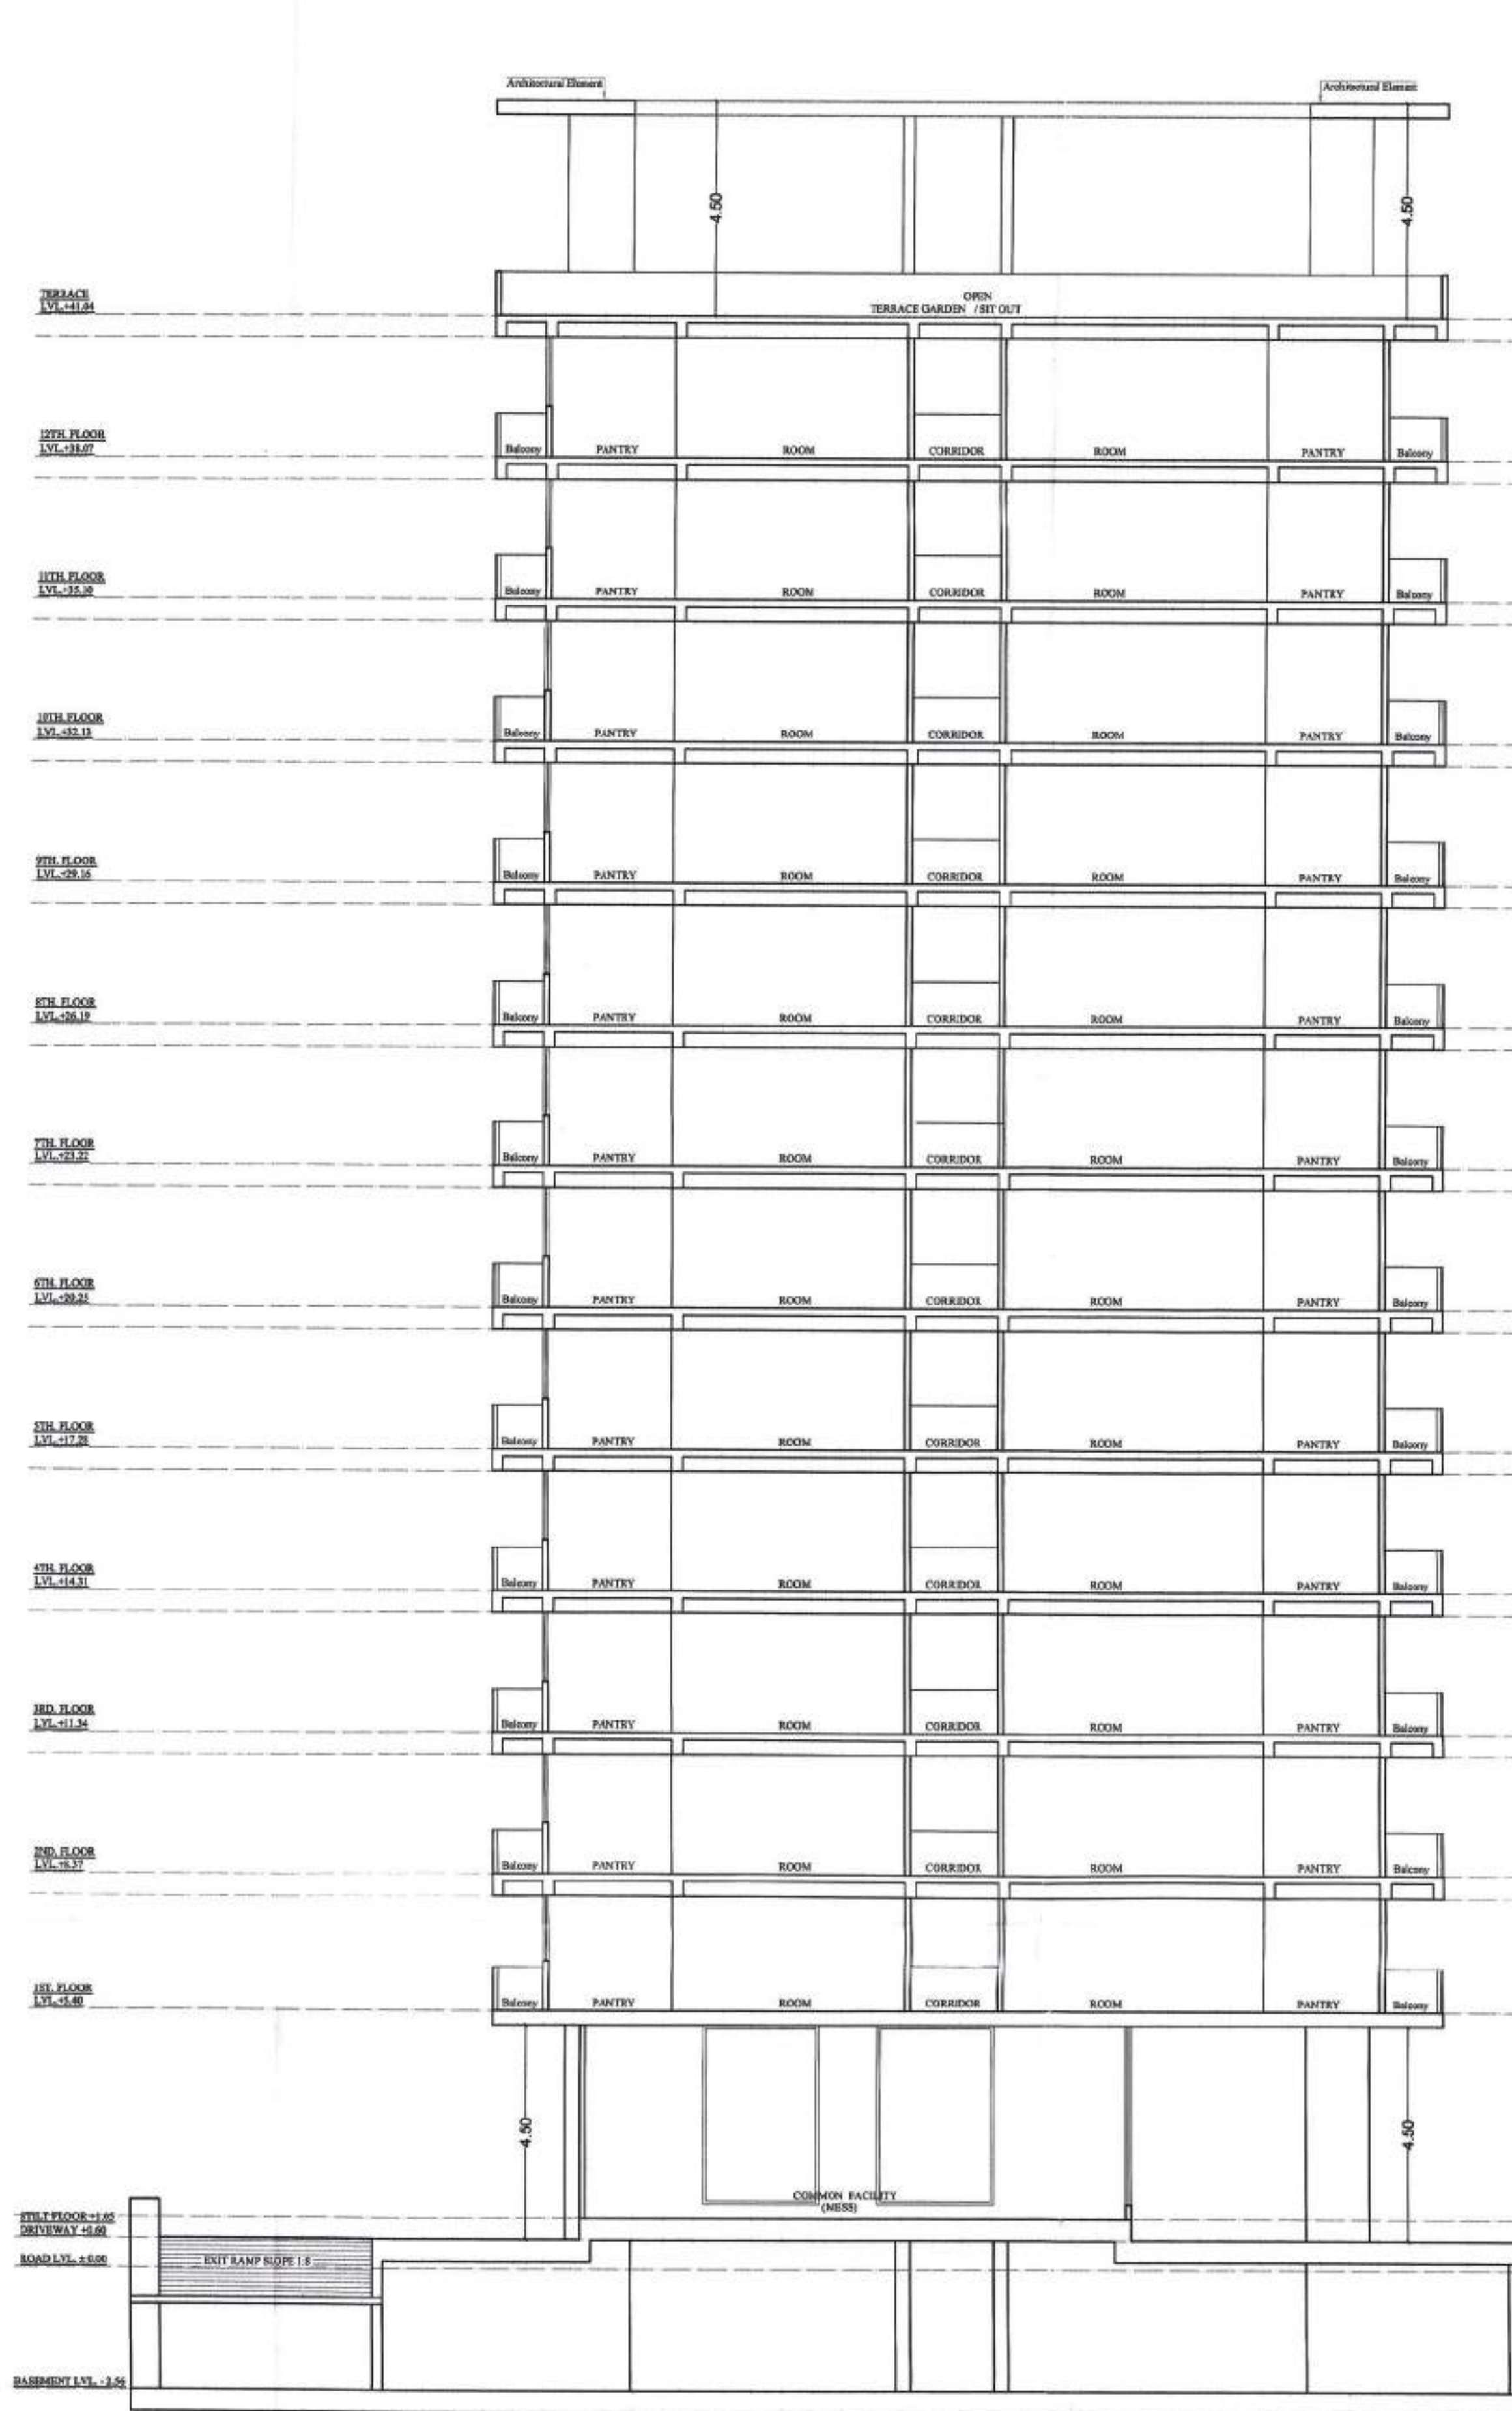

SECTION S2-S2

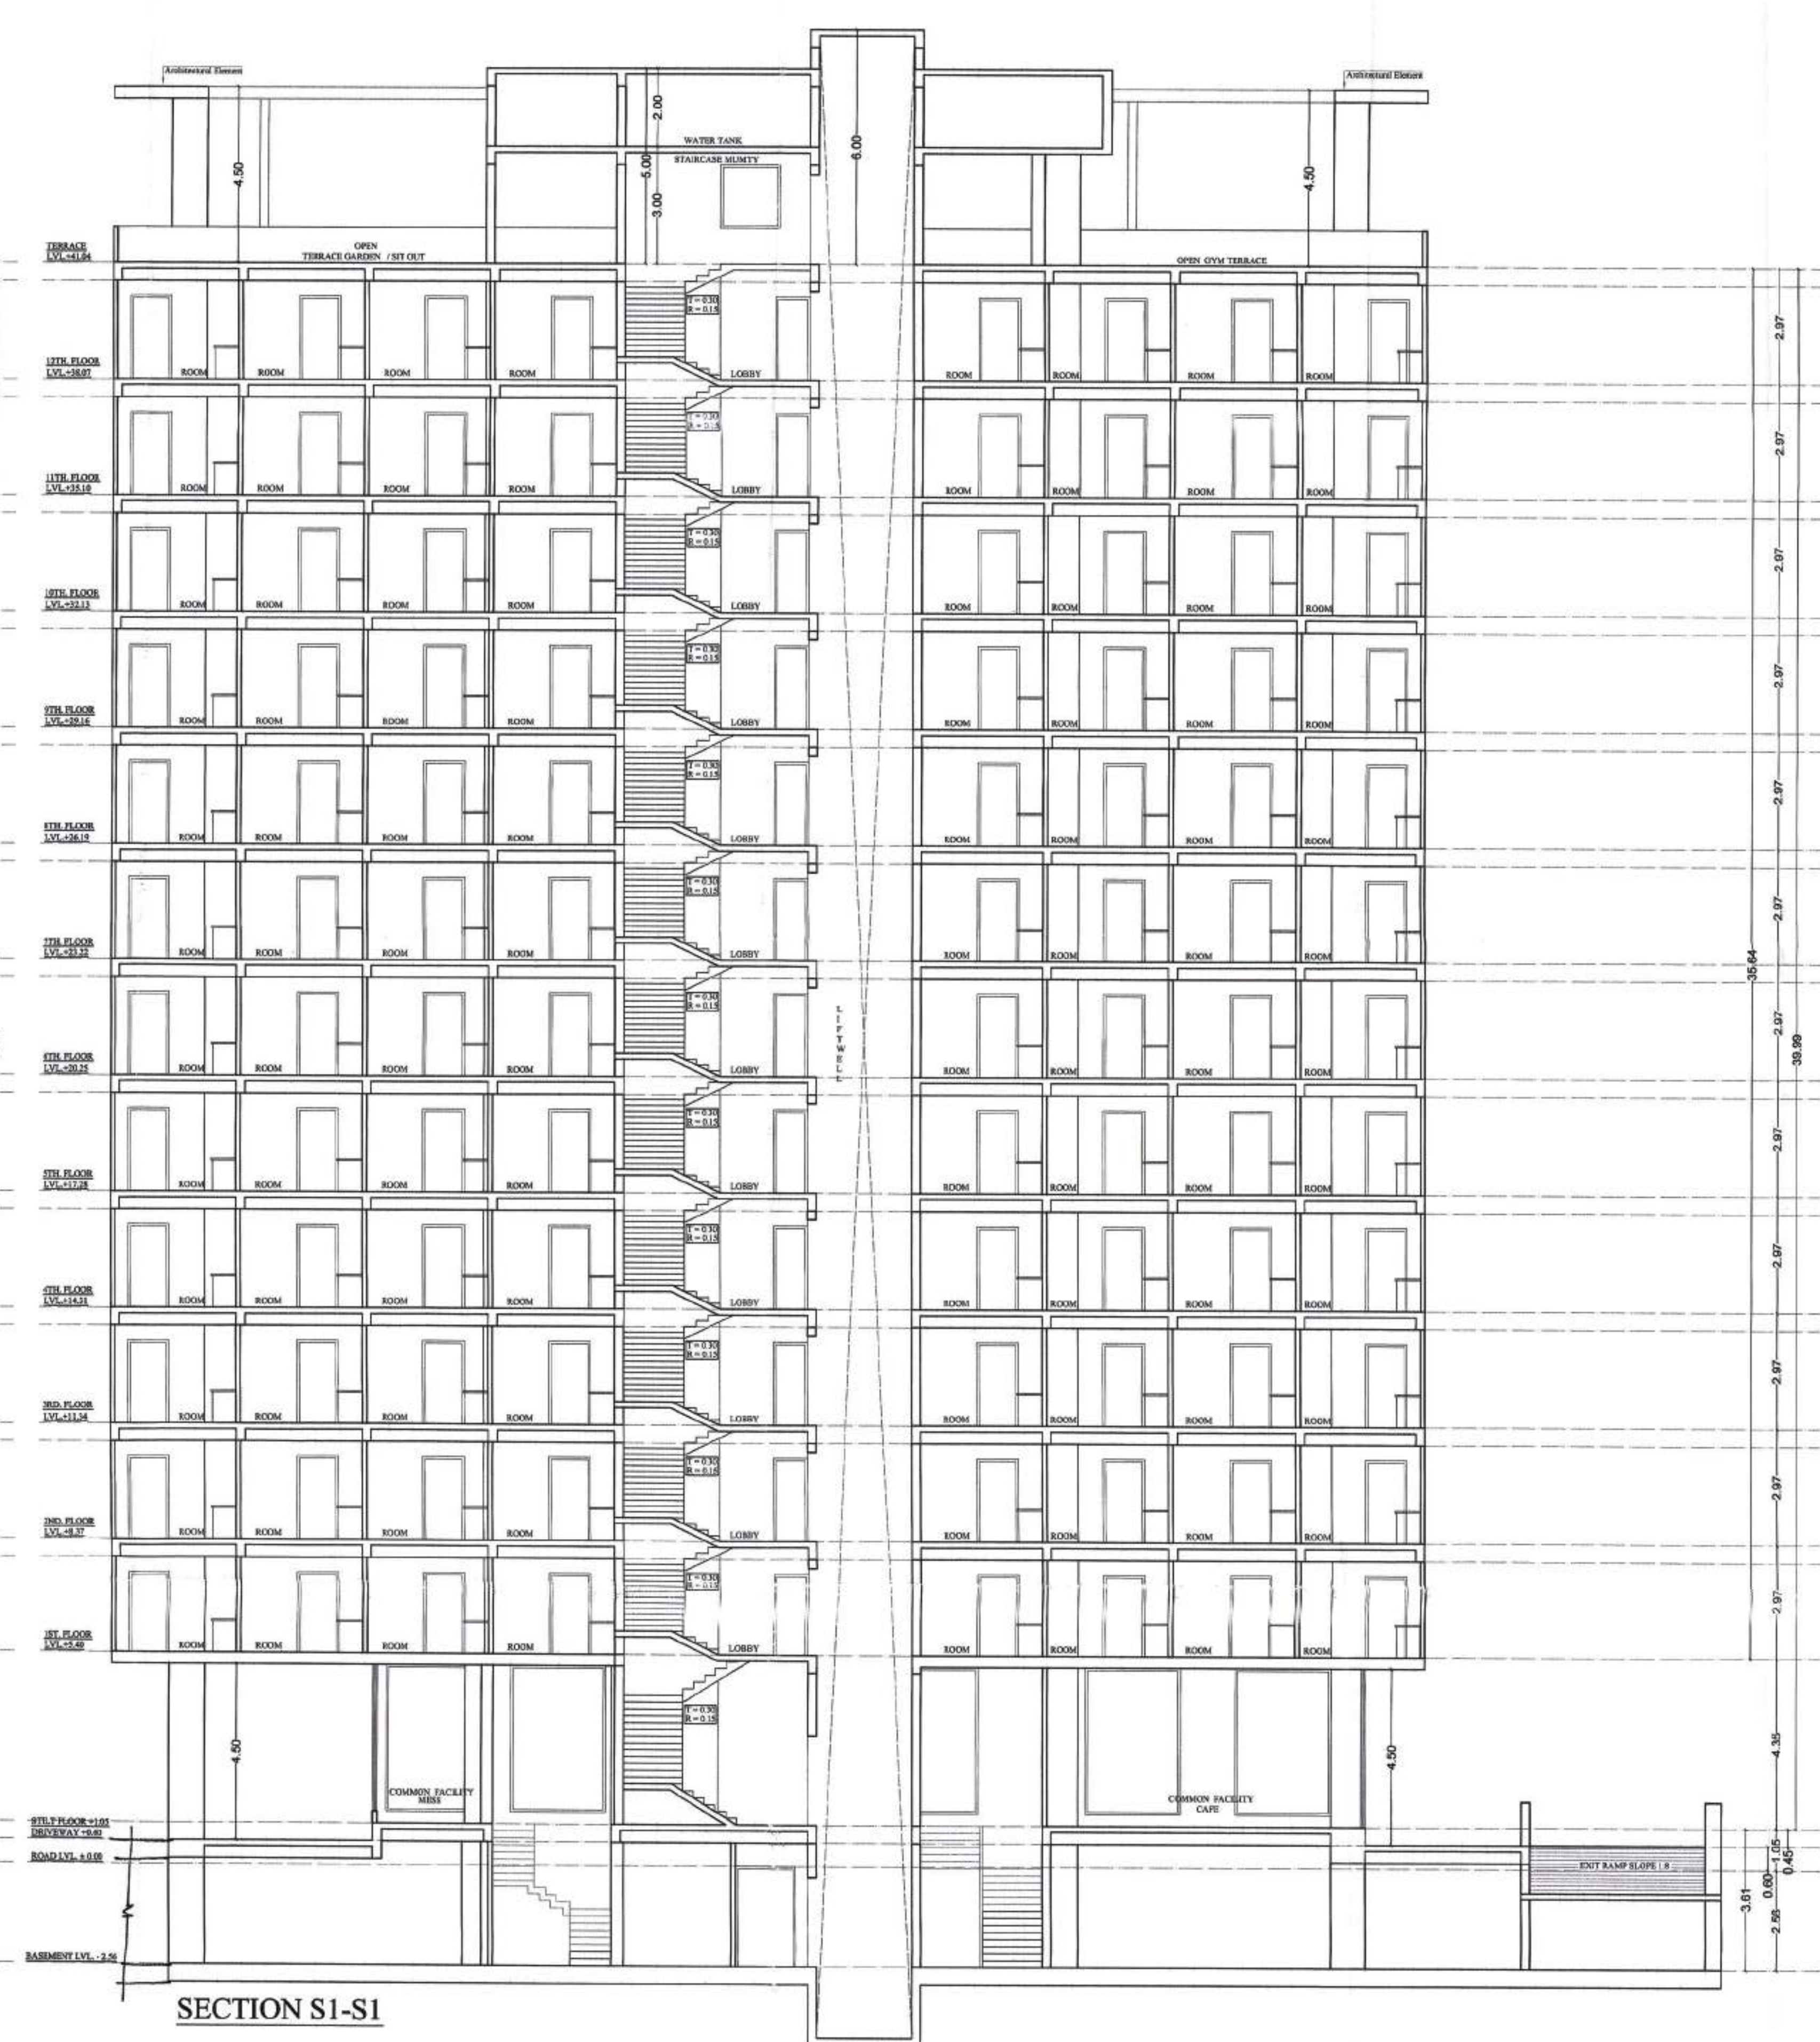

SECTION S1-S1



SPACE GRID ARCHITECTS

C-49, VIDYA APARTMENT, PARAS MARG, BAPU NAGAR, NEAR
JANTA STORE CIRCLE, JAIPUR-302015 PH-09314918766,
0141-4005506 (O) Email: -info.spacegrid@gmail.com

TO WHOMSOEVER IT MAY CONCERN

In reference to Project “**VISION 204**” situated at Plot No. 5, Coaching Hub, Pratap Nagar, Jaipur.

I, Shri Krishan, architect of the Project does solemnly declare that the open area in the project is as follows: -

	Area (in sqm)
Plot Area (A)	1713.59
Stilt Floor Area Without Projection (B)	519.93
Guard Room Area (C)	6.35
Total Open Area [A-(B+C)]	1187.31

SHRI KRISHAN
ARCHITECT
CA/99/25451