



जयपुर विकास प्राधिकरण, जयपुर

www.jda.urban.rajasthan.gov.in

क्रमांक: जचिप्रा/उपा./जोन-11/2024/डी-221

दिनांक: 24/1/24

श्री राजेश शर्मा पुत्र श्री गिरधारी लाल शर्मा
जरिये अधिकृत प्रतिनिधि मैसर्स मंगलम बिल्ड डवलपर्स लि.
पंजीकृत कार्यालय- 6th फ्लोर, अपेक्स मॉल,
लाल कोठी, टोंक रोड़, जयपुर।

विषय:-ग्राम महापुरा, तहसील सांगानेर में स्थित खसरा नम्बर 406, 407, 407/1, 2260/404
कुल कित्ता 4 कुल क्षेत्रफल 1.0500 हैक्ट. भूमि पर आवासीय योजना "मंगलम ग्राण्ट
सिटी विस्तार ब्लॉक ए (पार्ट- I)" का मानचित्र जारी करने बाबत।

उपरोक्त विषयान्तर्गत लेख है कि आप द्वारा ग्राम महापुरा, तहसील सांगानेर में स्थित खसरा
नम्बर 406, 407, 407/1, 2260/404 कुल कित्ता 4 कुल क्षेत्रफल 1.0500 हैक्ट. भूमि पर आवासीय
योजना "मंगलम ग्राण्ट सिटी विस्तार ब्लॉक ए (पार्ट- I)" का मानचित्र जारी करने हेतु आवेदन किया
गया है।

आप द्वारा प्रस्तुत दस्तावेजों के आधार पर ग्राम महापुरा, तहसील सांगानेर में स्थित खसरा
नम्बर 406, 407, 407/1, 2260/404 कुल कित्ता 4 कुल क्षेत्रफल 1.0500 हैक्ट. भूमि पर आवासीय
योजना "मंगलम ग्राण्ट सिटी विस्तार ब्लॉक ए (पार्ट- I)" का मानचित्र रिकॉर्ड शाखा में (डी.आर.जी.)
क्रमांक 1385/बी दिनांक 19.01.2024 पर दर्ज किया गया है।

अतः रिकॉर्ड शाखा में दर्ज किये जाने के पश्चात् योजना मानचित्र की प्रति संलग्न कर
प्रेषित है।

प्रति- योजना मानचित्र की छायाप्रति।

उपायुक्त, जयपुर-11
जयपुर विकास प्राधिकरण
जयपुर

J.D.A.

NORTH:-

NORTH



KEY PLAN:-

मास्टर विकास योजना 2026 के अनुसार भू उपयोग
भूखण्डों की निर्माण स्थिति :-

- आवासीय - 48
ई. डब्ल्यू.एस./एल. आई.जी.-09
खुर्दरा व्यवसायिक -12
- पूर्ण / आंशिक निर्मित भूखण्ड -
 - चार दीवारी निर्मित भूखण्ड -
 - खाली भूखण्ड -

कुल भूखण्ड -69

मौके के अनुसार योजना का भू उपयोग व तकनीकी विश्लेषण :-

नोट :- सेक्टर रोड एवं योजना की रोड पर स्थित कार्नेर
भूखण्डों का क्षेत्रफल नियमानुसार कम किया गया है।

SCHEME AREA ANALYSIS

क्रमांक (S.No.)	भू उपयोग (Land Utilization)	क्षेत्रफल (Sq.Mtr.)	प्रतिशत (%)
1.	आवासीय	4415.28	42.05%
2.	ई. डब्ल्यू.एस./एल. आई.जी. (10% AREA OF RESIDENTIAL)	447.39	04.26%
3.	खुर्दरा व्यवसायिक	48.00	00.46%
4.	व्यवसायिक	0.00	00.00%
5.	कुल (1+2+3+4)	4910.67	46.77%
6.	पार्क एवं खुला क्षेत्र	1066.40	10.16%
7.	सुविधा क्षेत्र	1057.20	10.07%
8.	PUBLIC UTILITY (Toilet)	10.00	00.09%
9.	MOB. TOWER	10.24	00.10%
10.	S.W.M (SOLID WASTE MANAGEMENT)	55.89	00.53%
11.	सड़क, LANE & PATHWAY	3389.60	32.28%
12.	कुल (5+6+7+8+9+10)	5589.33	53.23%
13.	कुल योजना क्षेत्र	10500.00	100.00%
14.	कुल खातेदार का क्षेत्र	(1.05 HECT.)	

KHASRA NO. 2260/404, 406, 407, 407/1
AT VILLAGE- MAHAPURA, TEH.- SANGANER, JAIPUR (RAJ.)

ARCHITECTURAL CONSULTANT:-

CADD SQUARE Consultancy
319 - 2nd Floor, Apex Mall, Lal kothi, Tonk Road, Jaipur (Raj.)
Tel : +91 141 4015808, Mob.- 96290-47373, 97845-90593
Email: caddsquare.jaipur@gmail.com, Web : www.caddsquare.com

NAME OF SOCIETY:-

NIJI KHATEDAR

NAME OF SCHEME:-

"MANGLAM'S" "GRAND CITY EXT. BLOCK A (PART-I)"

ZONE NO.-11

SECTOR NO.-

SCALE:- 1CM = 6.0M.

DRG. NO. CSC/22/235

J.E.N (ZONE-11)

AMIN (ZONE-11)

T.D.R (ZONE-11)

A.T.P. (ZONE-11)

D.C (ZONE-11)



JAIPUR DEVELOPMENT AUTHORITY, JAIPUR

PROPOSED LAY OUT MAP OF

"MANGLAM'S" GRAND CITY EXT. BLOCK A (PART - I)

AT VILLAGE- MAHAPURA, TEH.- SANGANER, JAIPUR (RAJ.)

SCALE : 1 : 600 OR (1" = 50' Feet)


NORTH



योजना के भूखण्डों की स्थिति :-

- आवासीय - 48
- ई. डब्ल्यू.एस./एल. आई.जी.-09
- खुर्दरा व्यवसायिक -12

कुल भूखण्ड -69

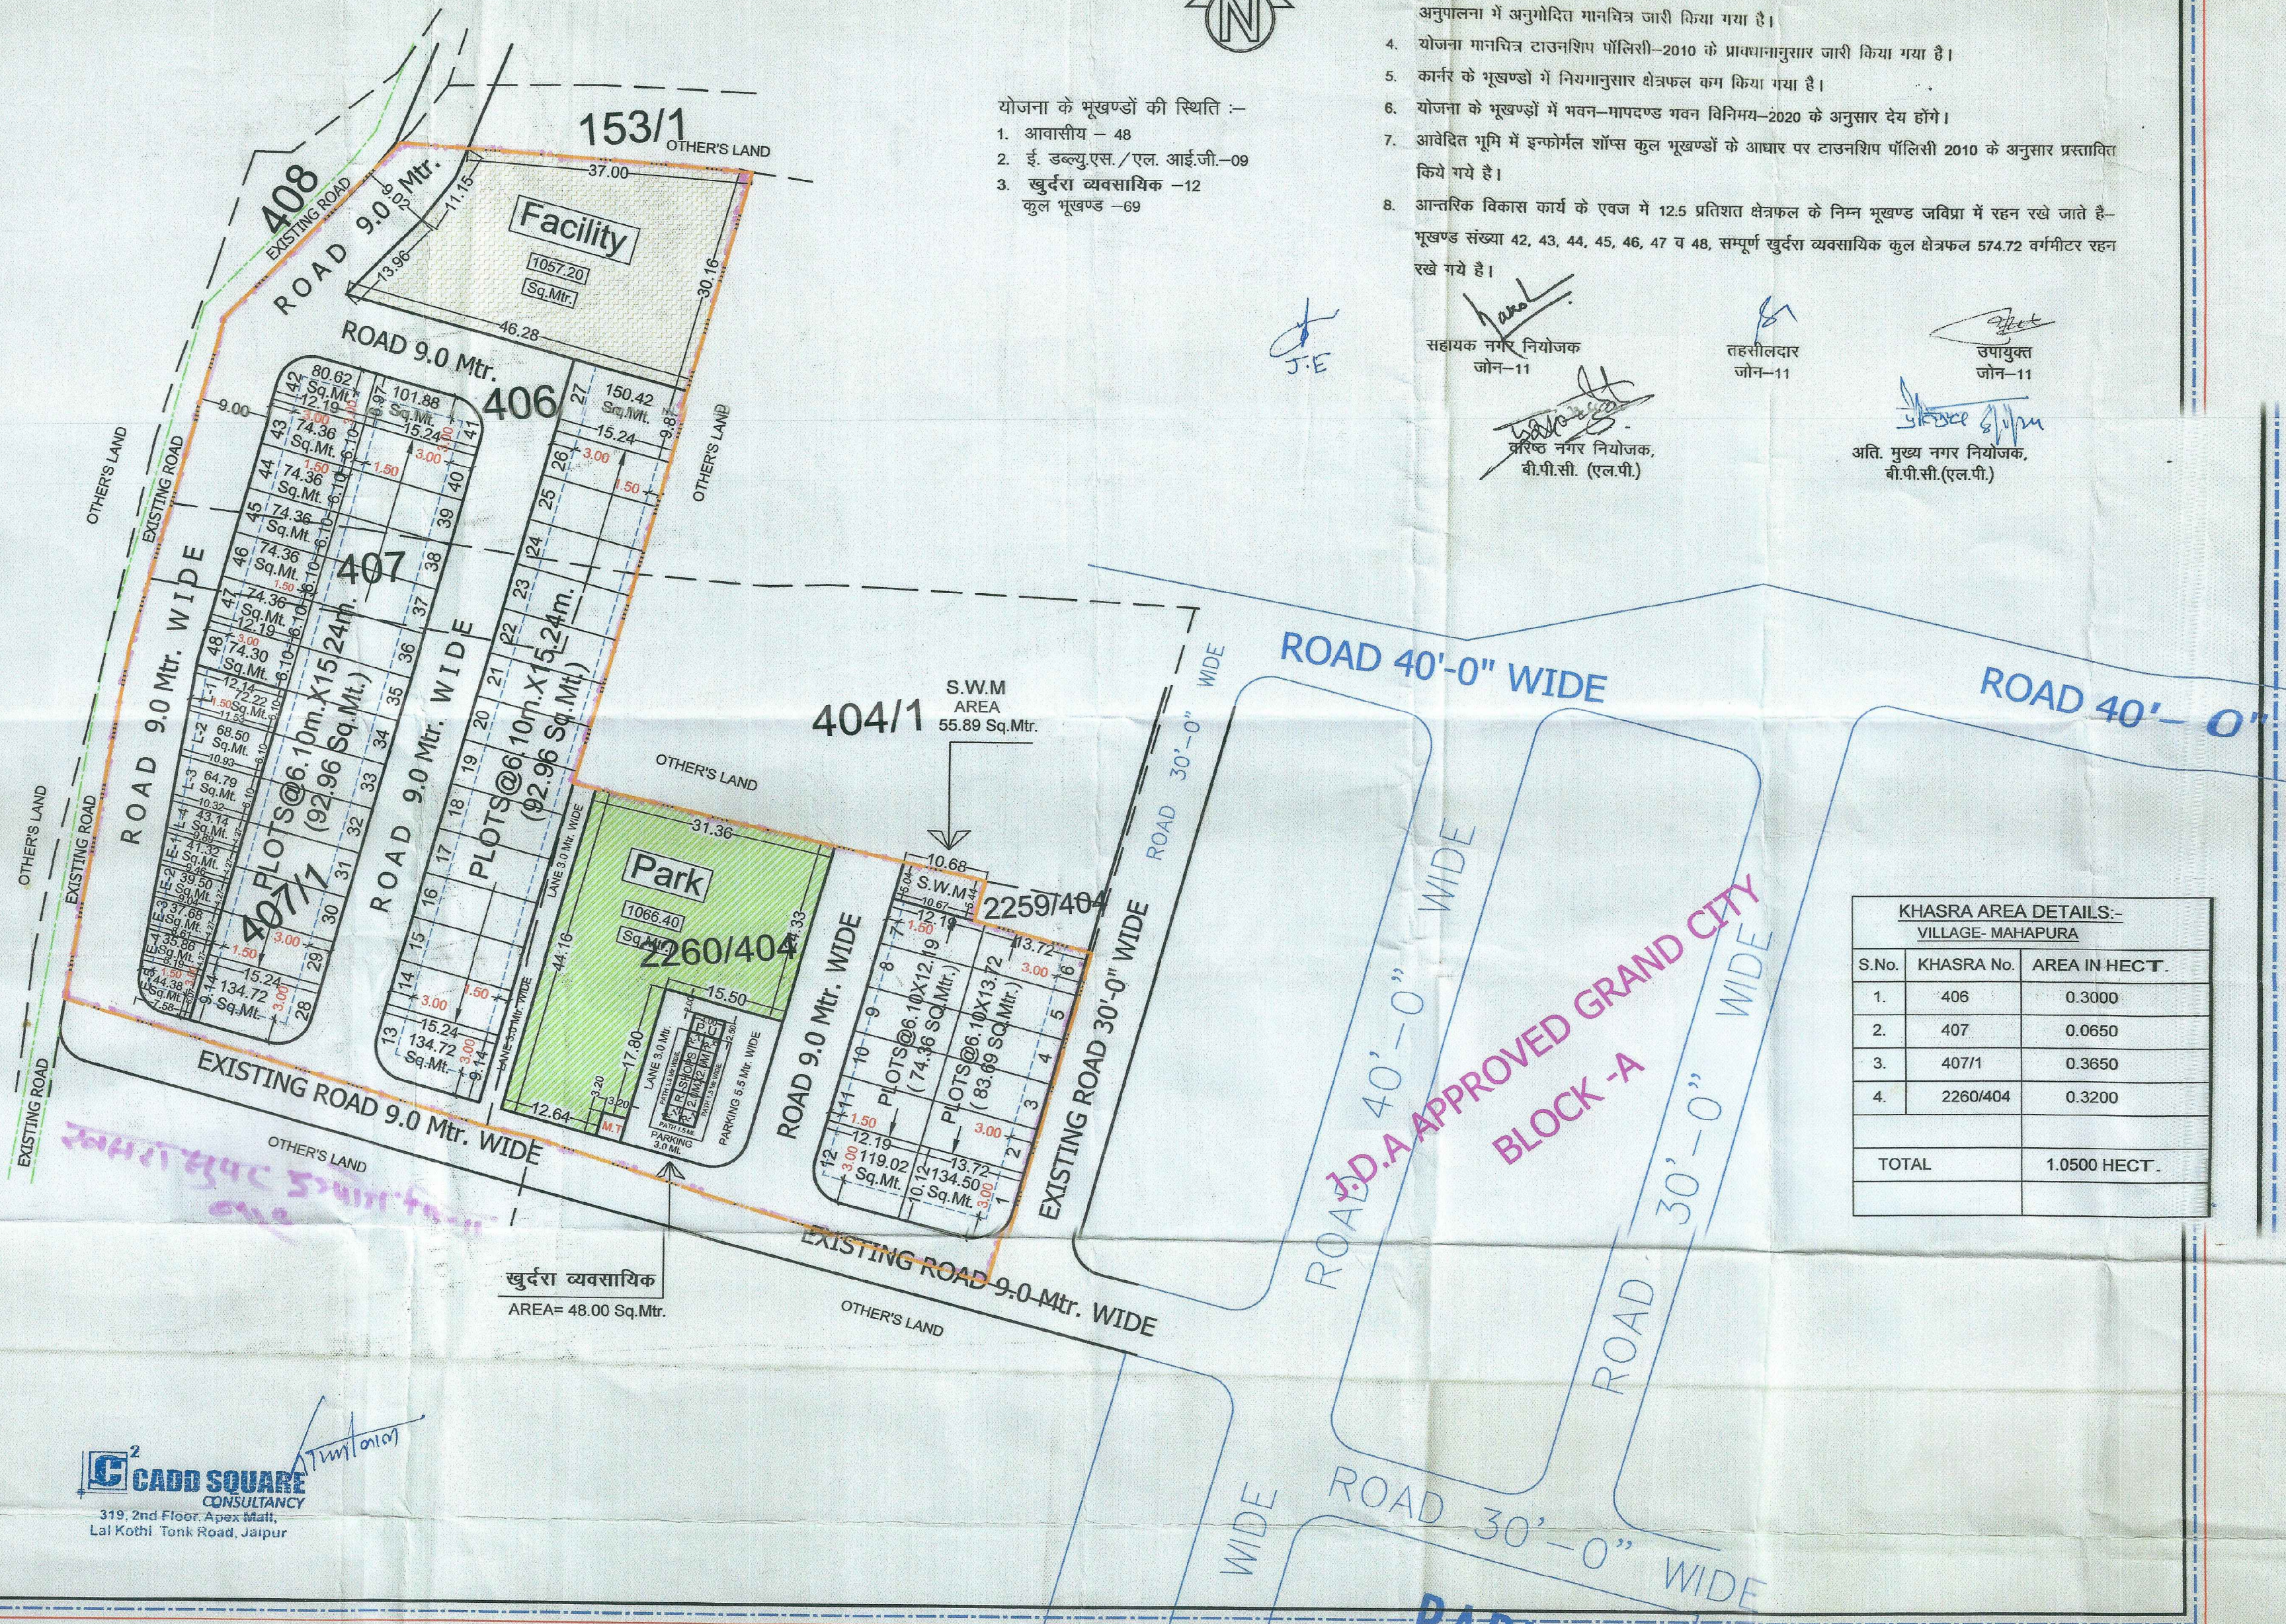

- योजना में सम्मिलित सभी खसरो की 90-ए का निर्णय दिनांक 28.03.2022 को पारित किया गया है।
- योजना की भूमि सभ्यता अधिनियम की धारा 90ए की कार्यवाही प्राधिकृत अधिकारी द्वारा एवं खसरा सौगा प्रमाणिकर अमीन द्वारा किया गया है।
- योजना का अनुमोदन बी.पी.सी (एल.पी) की 321वीं बैठक दिनांक 28.07.2022 को किया गया, जिसकी अनुपालना में अनुमोदित मानचित्र जारी किया गया है।
- योजना मानचित्र टाउनशिप पोलिसी-2010 के प्रावधानानुसार जारी किया गया है।
- कार्नेर के भूखण्डों में नियमानुसार क्षेत्रफल कम किया गया है।
- योजना के भूखण्डों में भवन-मापदण्ड भवन विनियम-2020 के अनुसार देय होंगे।
- आवेदित भूमि में इन्फोर्मल शॉपस कुल भूखण्डों के आधार पर टाउनशिप पोलिसी 2010 के अनुसार प्रस्तावित किये गये हैं।
- आन्तरिक विकास कार्य के एवज में 12.5 प्रतिशत क्षेत्रफल के निम्न भूखण्ड जविप्रा में रहन रखे जाते हैं- भूखण्ड संख्या 42, 43, 44, 45, 46, 47 व 48, सम्पूर्ण खुर्दरा व्यवसायिक कुल क्षेत्रफल 574.72 वर्गमीटर रहन रखे गये हैं।

सहायक नगर नियोजक
जोन-11तहसीलदार
जोन-11उपायुक्त
जोन-11सहायक नगर नियोजक,
बी.पी.सी. (एल.पी.)अति. मुख्य नगर नियोजक,
बी.पी.सी. (एल.पी.)KHASRA AREA DETAILS:-
VILLAGE- MAHAPURA

S.No.	KHASRA No.	AREA IN HECT.
1.	406	0.3000
2.	407	0.0650
3.	407/1	0.3650
4.	2260/404	0.3200
TOTAL		1.0500 HECT.